


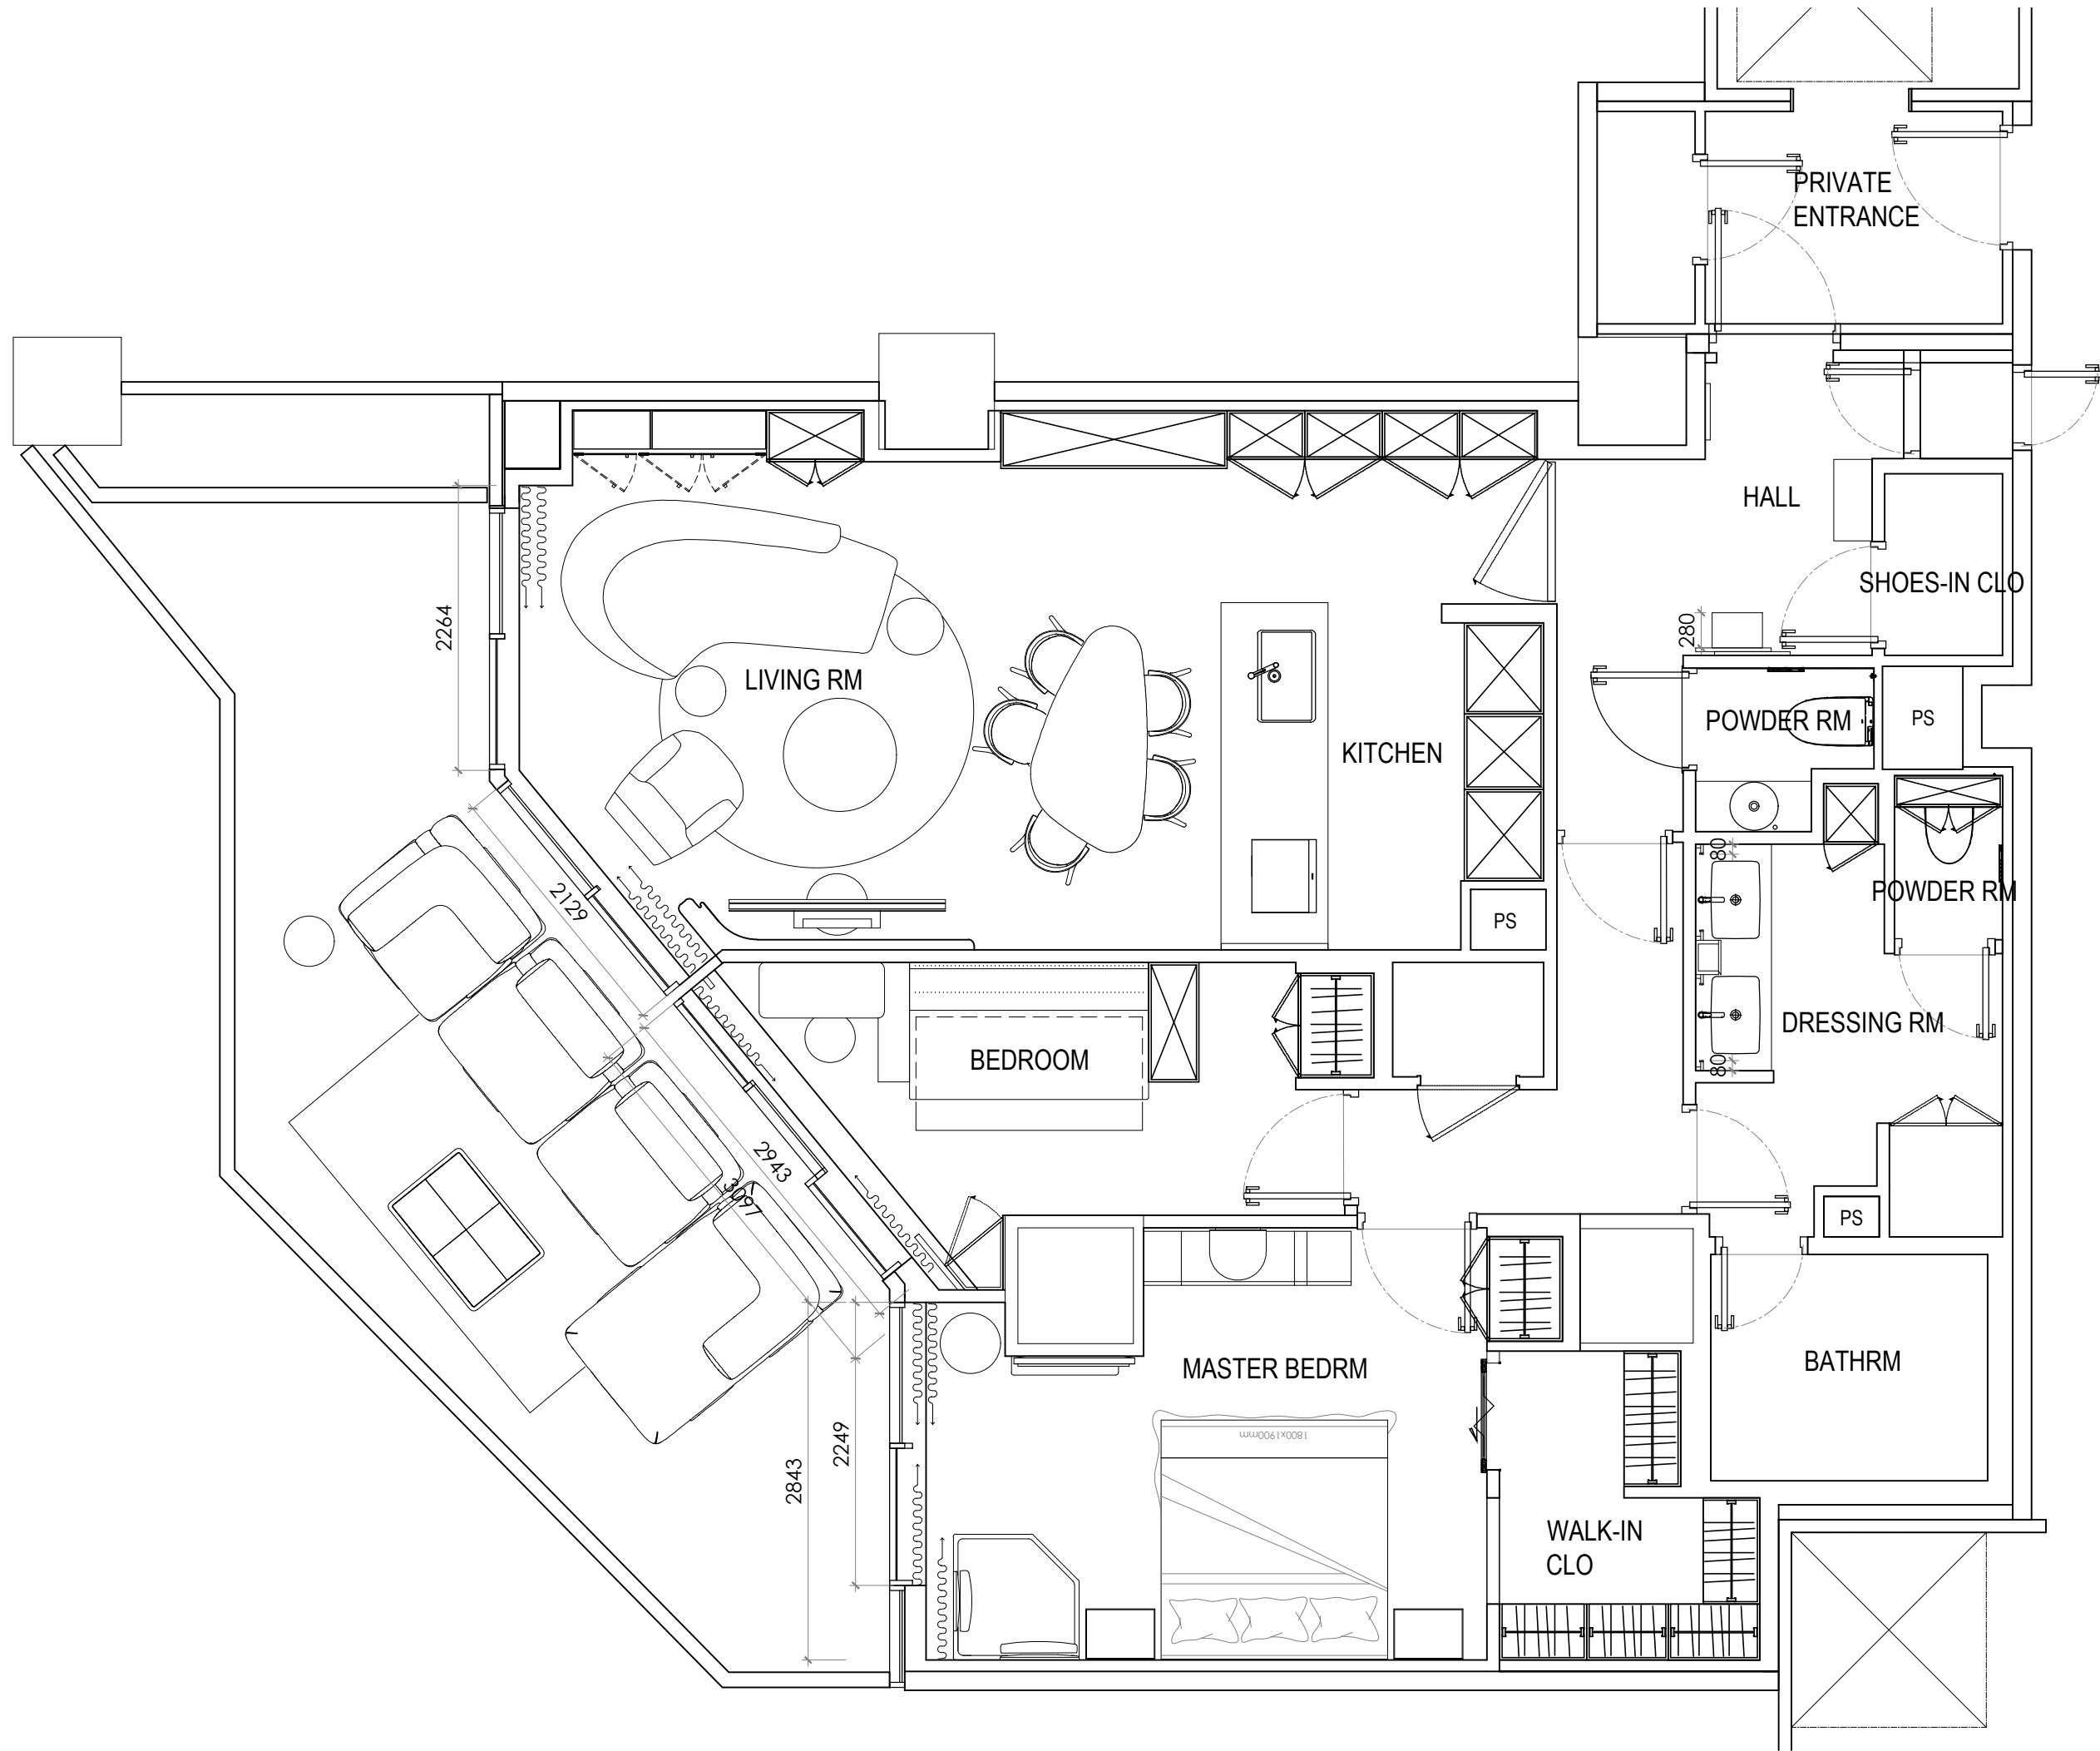

Revision

APPROVAL / 核准

設計者:	建築師:
業主:	

備註:

- 圖面標註尺寸僅供參考，施作均以現場放樣檢討之。
- 圖面標註尺寸、材料及文字敘述因版本不同之差異，均以出圖章簽認日期之最近為準。
- 電腦圖檔除由合約訂定外，均不得以任何方式外流。
- 圖面所示均為本公司所擁有之智慧財產，切勿以任何方式複製修改。



MULA DECO

▲ 3F, N.26, Ln.290, Guangfu S. Rd., Taipei.
☎ 886-2-2546-3258
☎ 886-2-2546-3257
✉ Guido@muladeco.com


Project / 案名

日本神宮案

Sheet Title / 圖名
507

平面配置圖

Date / 日期	Scale / 比例
4/20/2026	1/50cm
Designer / 設計	Approval / 核准
MONICA	
Job No / 業務編號	Drawn By / 繪圖
00000	GUIDO
Dwg No.	Page No.
P-01	01

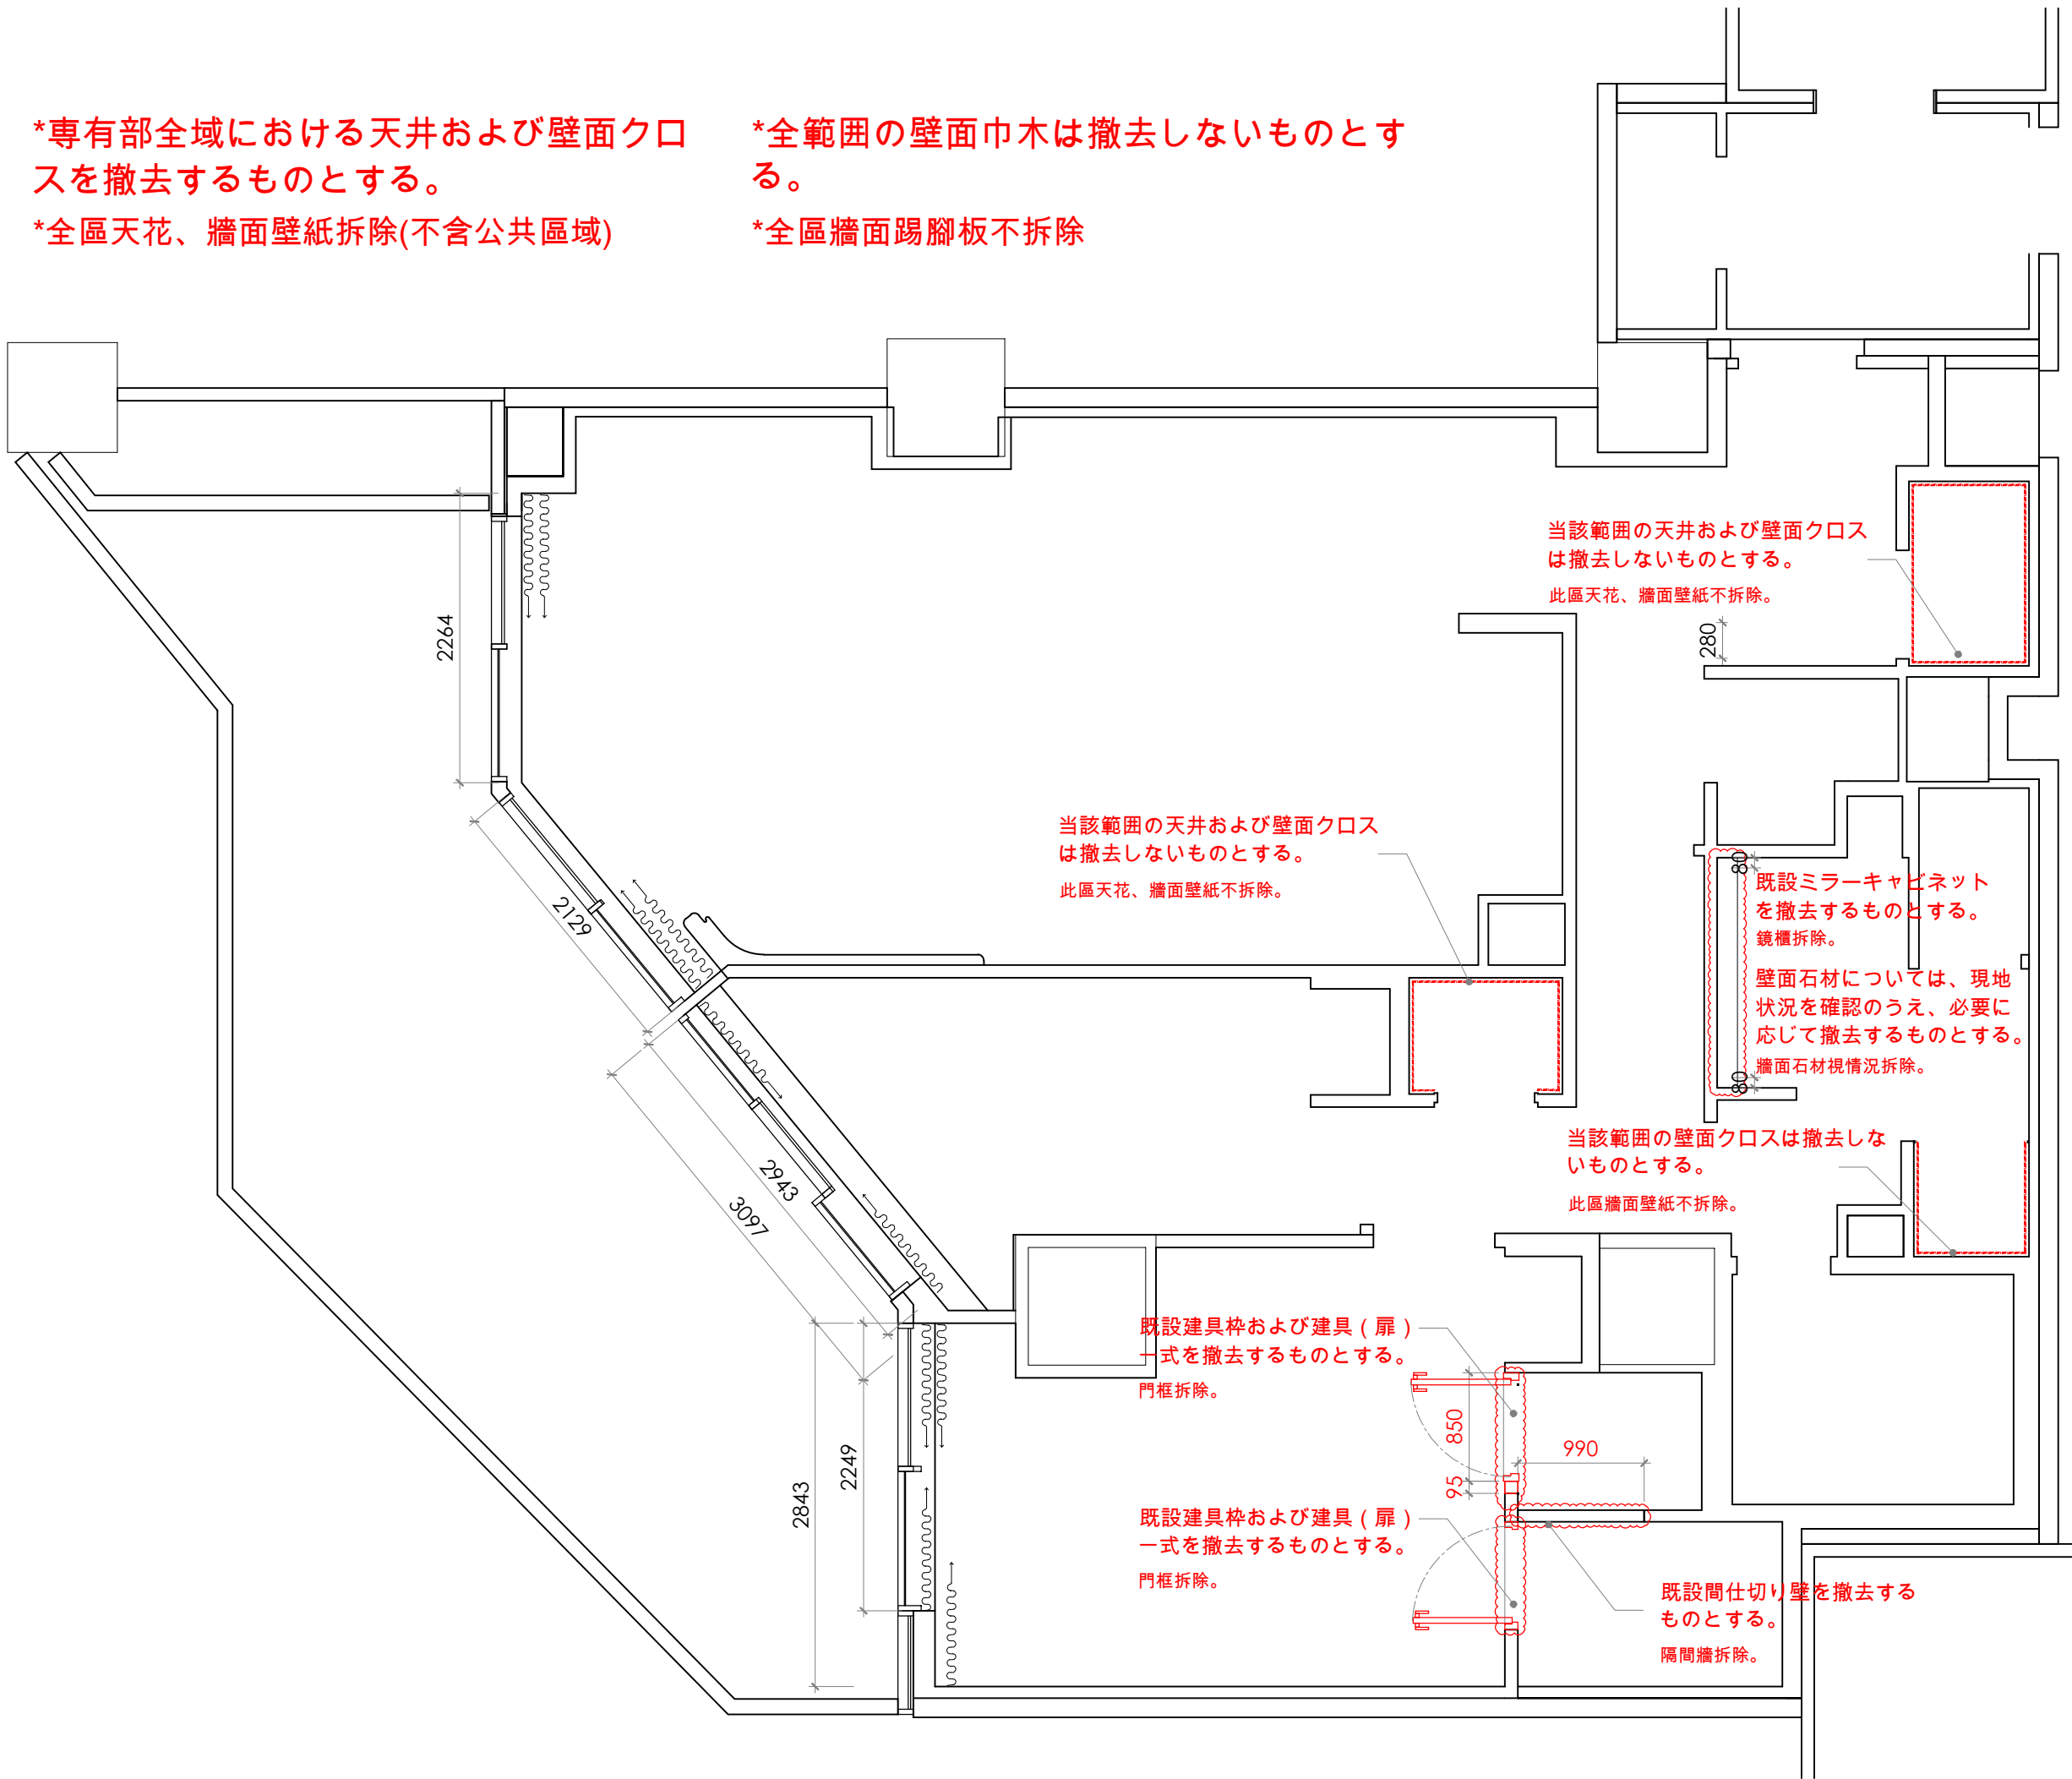

Revision

APPROVAL / 核准

設計者:	建築師:
業主:	

備註:

- a. 圖面標註尺寸僅供參考，施作均以現場放樣檢討之。
b. 圖面標註尺寸、材料及文字敘述因版本不同之差異，均以出圖章簽認日期之最近為準。
c. 電腦圖檔除由合約訂定外，均不得以任何方式外流。
d. 圖面所示均為本公司所擁有之智慧財產，切勿以任何方式複製修改。



MULA DECO

▲ 3F, N.26, Ln.290, Guangfu S. Rd., Taipei.
☎ 886-2-2546-3258
☎ 886-2-2546-3257
✉ Guido@muladeco.com

Project / 案名


日本神宮案

Sheet Title / 圖名
507

解体平面図

Date / 日期	Scale / 比例
4/20/2026	1/50cm
Designer / 設計	Approval / 核准
MONICA	
Job No / 業務編號	Drawn By / 繪圖
00000	GUIDO
Dwg No.	Page No.
P-02	02

牆 型 式	內 容	總 厚 度
	当該区画における天井および壁面クロスは撤去対象外とする。 隔間結構加强。	
	増設間仕切り壁は、既存間仕切り壁と同等の遮音性能とする。 増設隔間牆，同原隔間牆隔音等級。	
	増設木造間仕切り壁は、既存間仕切り壁と同等の性能とする。 増設隔間牆，同原隔間牆隔音等級。	

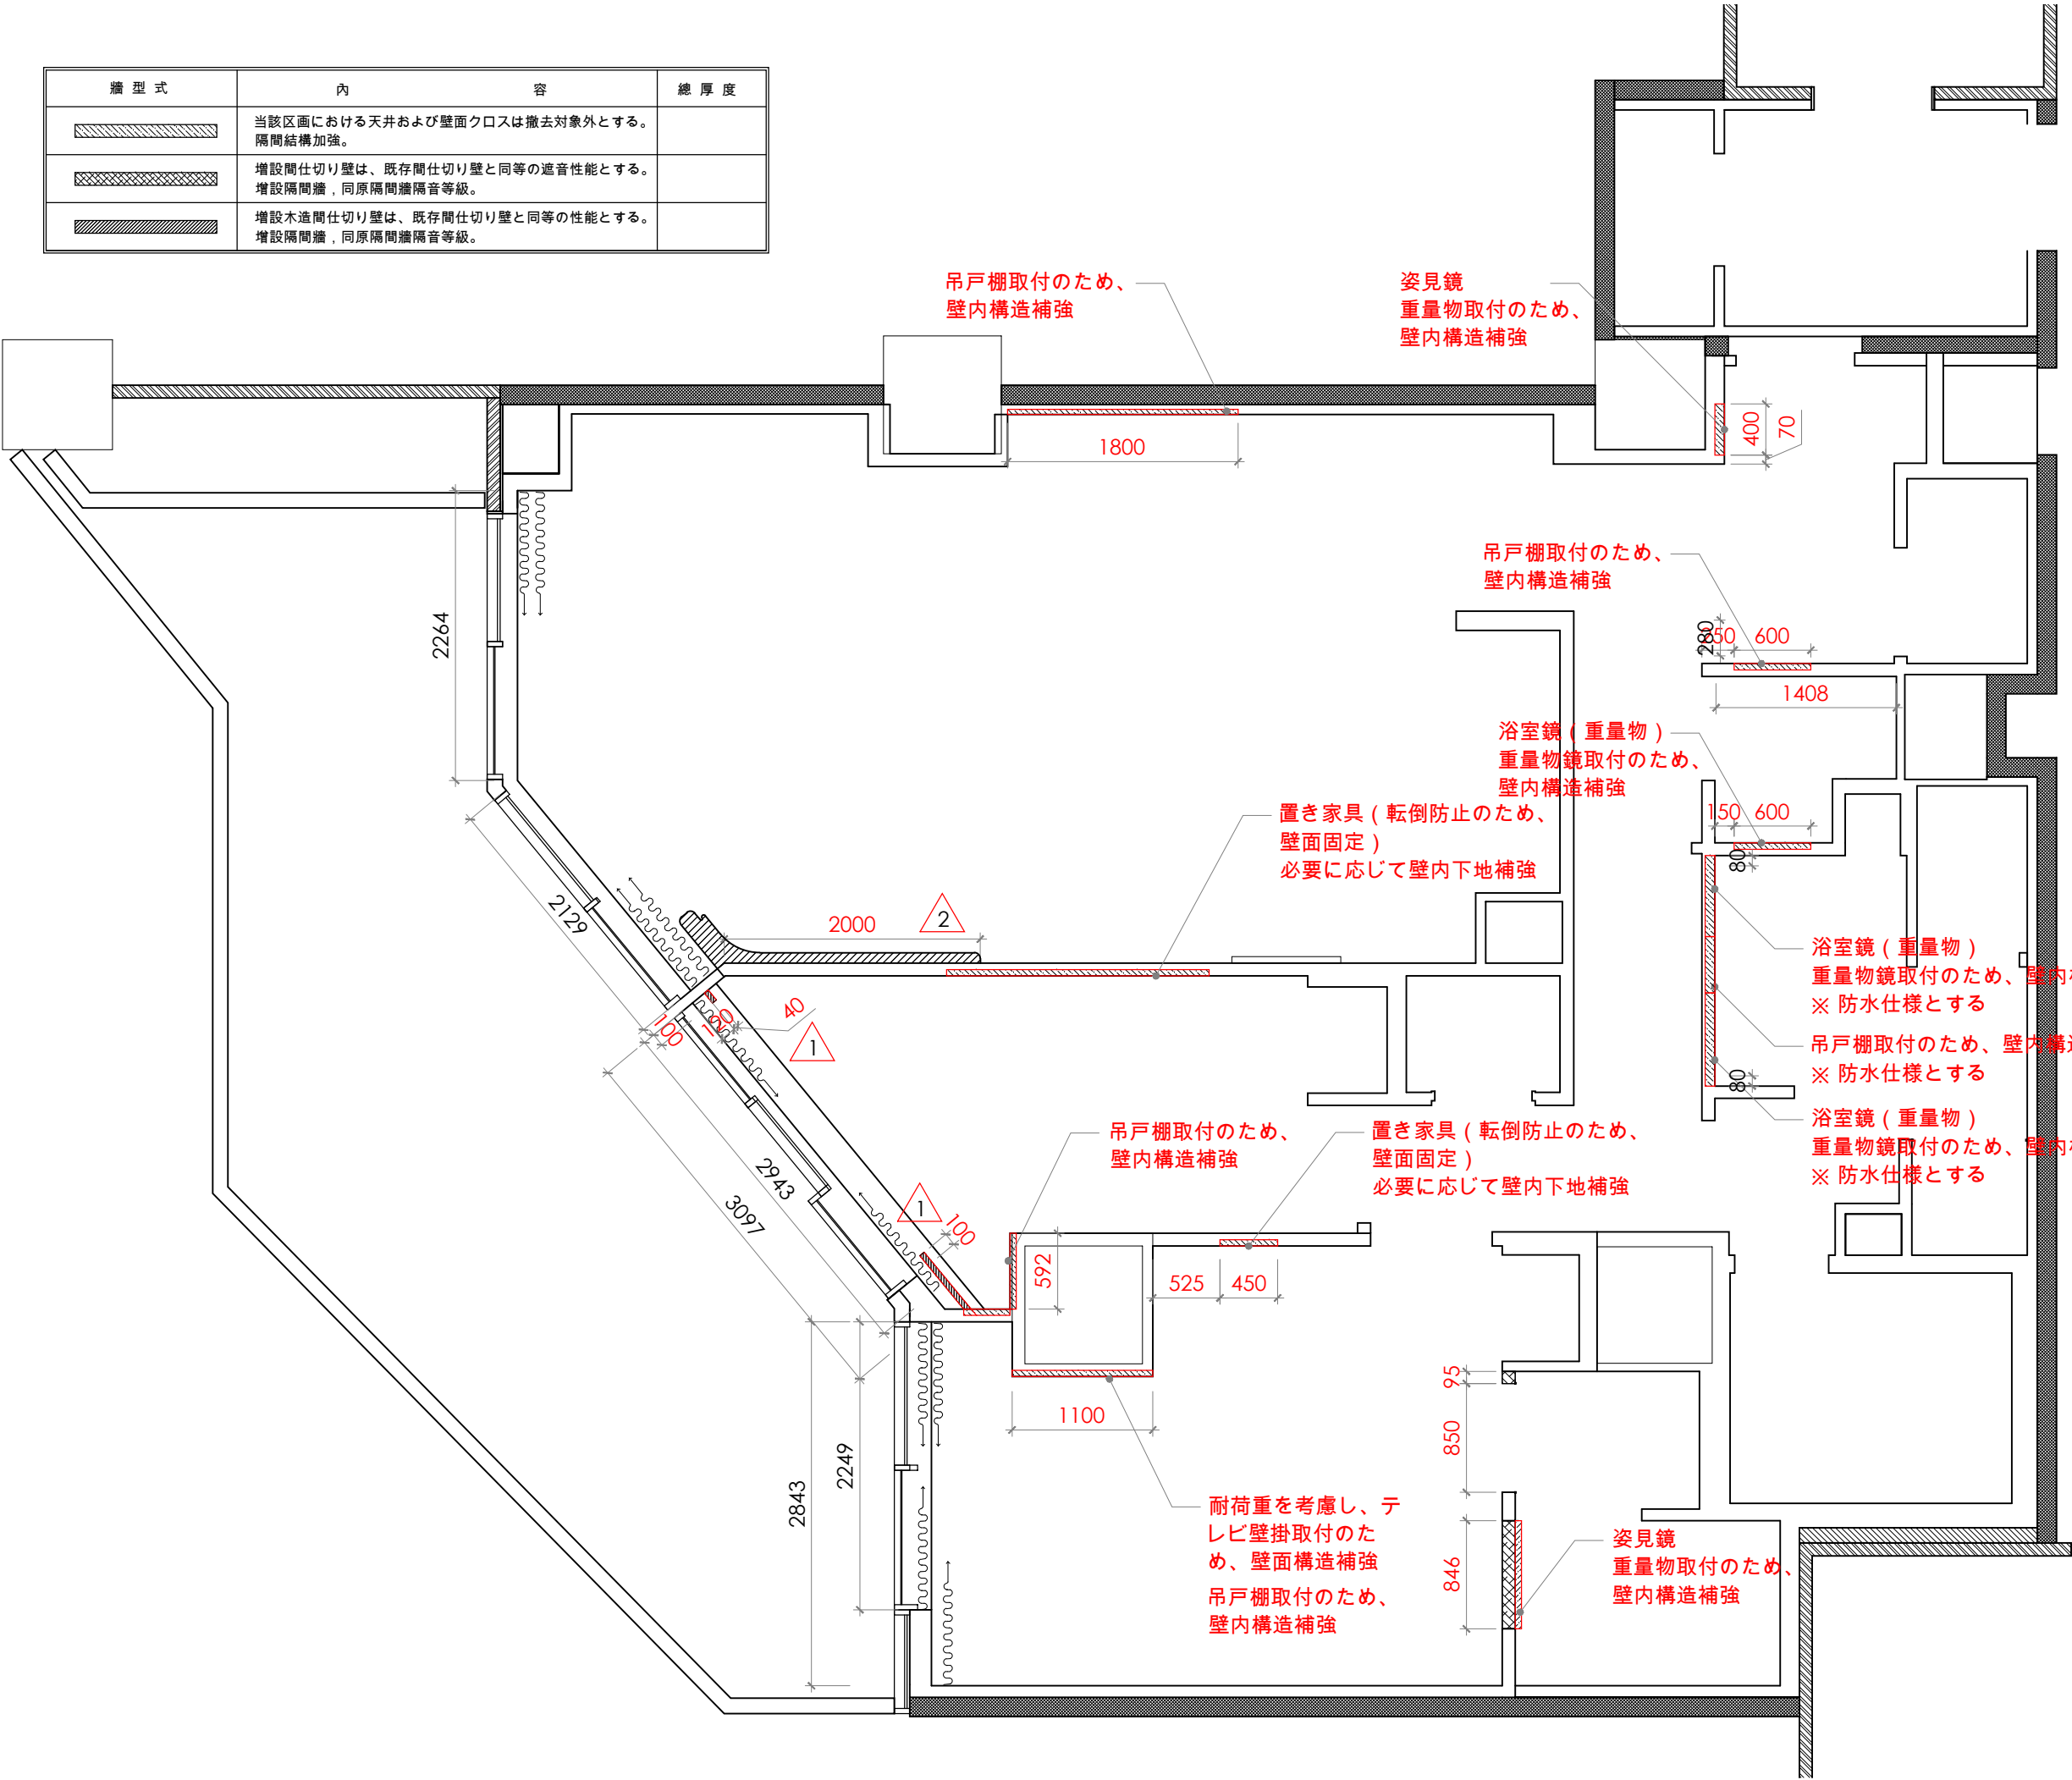

Revision	
圖面做以下修正：	
1. 隔間位置調整。	
2. 電視更改為落地式支架，電視牆修改。	
圖面修正内容は以下のとおり：	
1. 間仕切り位置を調整する。	
2. 電視改為落地式支架，並調整 / 修改電視牆面。	
APPROVAL / 核准	
設計者:	建築師:
業主:	

備註:

a. 圖面標註尺寸僅供參考，施作均以現場放樣檢討之。

b. 圖面標註尺寸、材料及文字敘述因版本不同之差異，均以出圖章簽認日期之最近為準。

c. 電腦圖檔除由合約訂定外，均不得以任何方式外流。

d. 圖面所示均為本公司所擁有之智慧財產，切勿以任何方式複製修改。



MULA DECO

▲ 3F, N.26, Ln.290, Guangfu S. Rd., Taipei.
☎ 886-2-2546-3258
☎ 886-2-2546-3257
✉ Guido@muladeco.com

Project / 案名	
日本神宮案	
Sheet Title / 圖名	
507 間仕切り詳細寸法図	
Date / 日期	Scale / 比例
4/20/2026	1/50cm
Designer / 設計	Approval / 核准
MONICA	
Job No / 業務編號	Drawn By / 繪圖
00000	GUIDO
Dwg No.	Page No.
P-03	03

[illegible]


Date / 日期	Scale / 比例
4/20/2026	1/50cm
Designer / 設計	Approval / 核准
MONICA	
Job No / 案號編號	Drawn By / 繪圖
00000	GUIDO
Dwg No.	Page No.
P-05	05

編號	圖示	説明	尺寸	光源	備 註
L1	㊦	ダウンライト			
L2	㊦	ダウンライト (小型)			
L3	㊦	照 明 器 具 取 付 位 置 (引 掛 シーリング)			
L4	㊦	ブラケット 照 明			
L5	-----	間接照明			
L6	-----	調光対応間接照明		LEDテープ 位相制御 (TRIAC) 調光	
L7	㊦	屋外用ボールライト			

*照明器具関連設備は、照明器具仕様書に基づき、最終確認を行うこと。

*照明器具の電源はすべて110Vとする。

*図面上に番号のない照明器具は、既設・設置済みの照明器具とする。

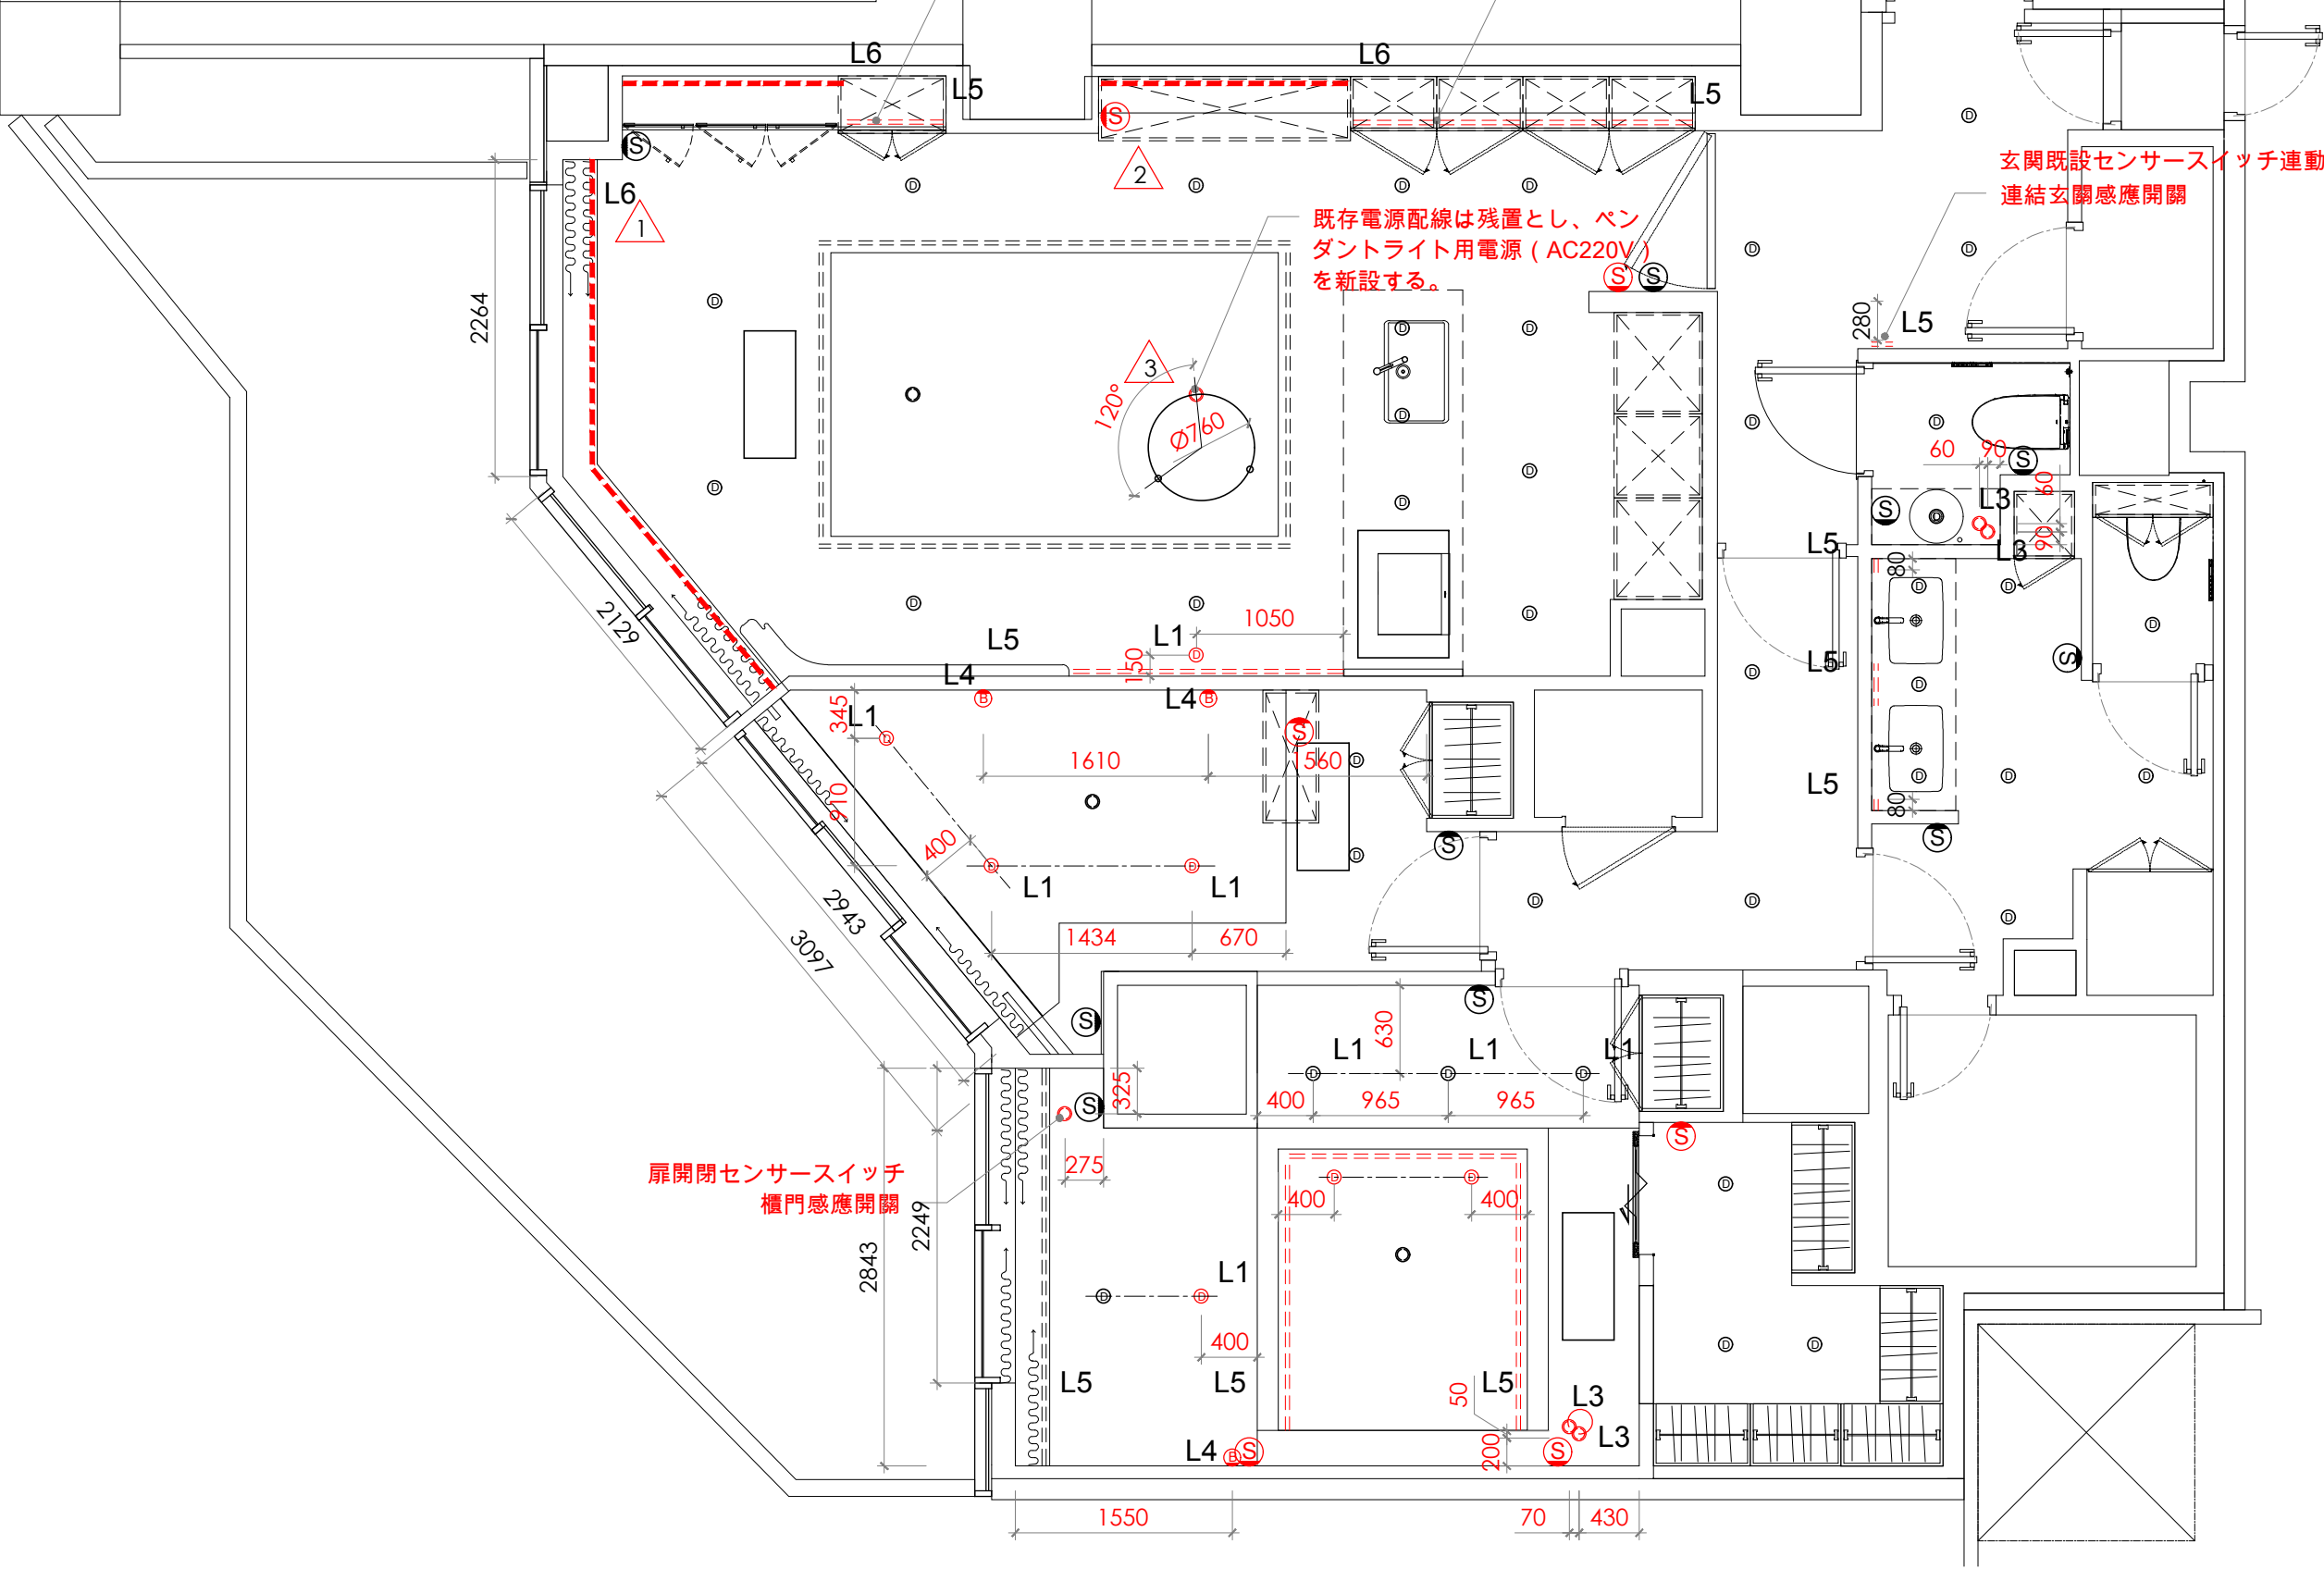

Revision	
圖面做以下修正:	
1. 新增窗簾盒間接照明。	
2. 迴路調整。	
3. 新增吊燈用電源 (AC220V) 。	
図面修正内容は以下のとおり:	
1.カーテンボックス間接照明の追加。	
2.回路の調整。	
3.ペンダントライト用電源 (AC220V) 新設。	
APPROVAL / 核准	
設計者:	建築師:
業主:	

備註:

a. 圖面標註尺寸僅供參考，施作均以現場放樣檢討之。

b. 圖面標註尺寸、材料及文字敘述因版本不同之差異，均以出圖章簽認日期之最近為準。

c. 電腦圖檔除由合約訂定外，均不得以任何方式外流。

d. 圖面所示均為本公司所擁有之智慧財產，切勿以任何方式複製修改。

MULA DECO

▲ 3F, N.26, Ln.290, Guangfu S. Rd., Taipei.

☎ 886-2-2546-3258


☎ 886-2-2546-3257

✉ Guido@muladeco.com

Project / 案名	
日本神宮案	
Sheet Title / 圖名	
507 照明器具平面配置図	
Date / 日期	Scale / 比例
4/20/2026	1/50cm
Designer / 設計	Approval / 核准
MONICA	
Job No / 業務編號	Drawn By / 繪圖
00000	GUIDO
Dwg No.	Page No.
P-06	06

圖例	說 明	數量	圖例	說 明	數量
①	コンセント (1口)		㊸	テレビ・LAN・電話コンセント	
②	コンセント (2口)		㊹	インターホン (副親機)	
⑬	アース付コンセント (1口)		㊺	HDMIコンセント	
⑭	アース付コンセント (2口)		㊻	LANコンセント	
㊴	床面コンセント (110V・ニロコンセント)		㊼	調光装置 (親機)	
㊽	テレビコンセント		㊾	調光装置 (子機)	
備註					
1.コンセントおよび照明器具出線口の詳細な位置・寸法・高さは、内装図にて確認すること。 3.すべての壁面コンセントは、特別に高さ表示のあるものを除き、現場の壁面スイッチと同一高さとする。 3.すべての壁面スイッチは、特別に高さ表示のあるものを除き、現場の壁面スイッチと同一高さとする。 4.所有配管・線均由平頂天花配置。 5.影音視聽系統所需弱電設備，由影音視聽系統廠商規劃後提供圖面予業主審核。					

圖例	說 明	數量	圖例	說 明	數量
①	單孔插座		㊸	電視、通訊插座組合	
②	雙孔插座		㊹	對講機 (副主機)	
⑬	單孔接地插座		㊺	HDMI插座	
⑭	雙孔接地插座		㊻	網路插座	
㊴	110V地面插座		㊼	調光裝置 (主機)	
㊽	電視插座組合		㊾	調光裝置 (子機)	
備註					
1.插座、燈具出線口詳細位置尺寸、高度詳裝修圖。 3.所有壁面插座，除特別標示高度者之外，一律與現場壁面開關同高度。 3.所有壁面開關，除特別標示高度者之外，一律與現場壁面開關同高度。 4.所有配管、線均由平頂天花配置。 5.影音視聽系統所需弱電設備，由影音視聽系統廠商規劃後提供圖面予業主審核。					

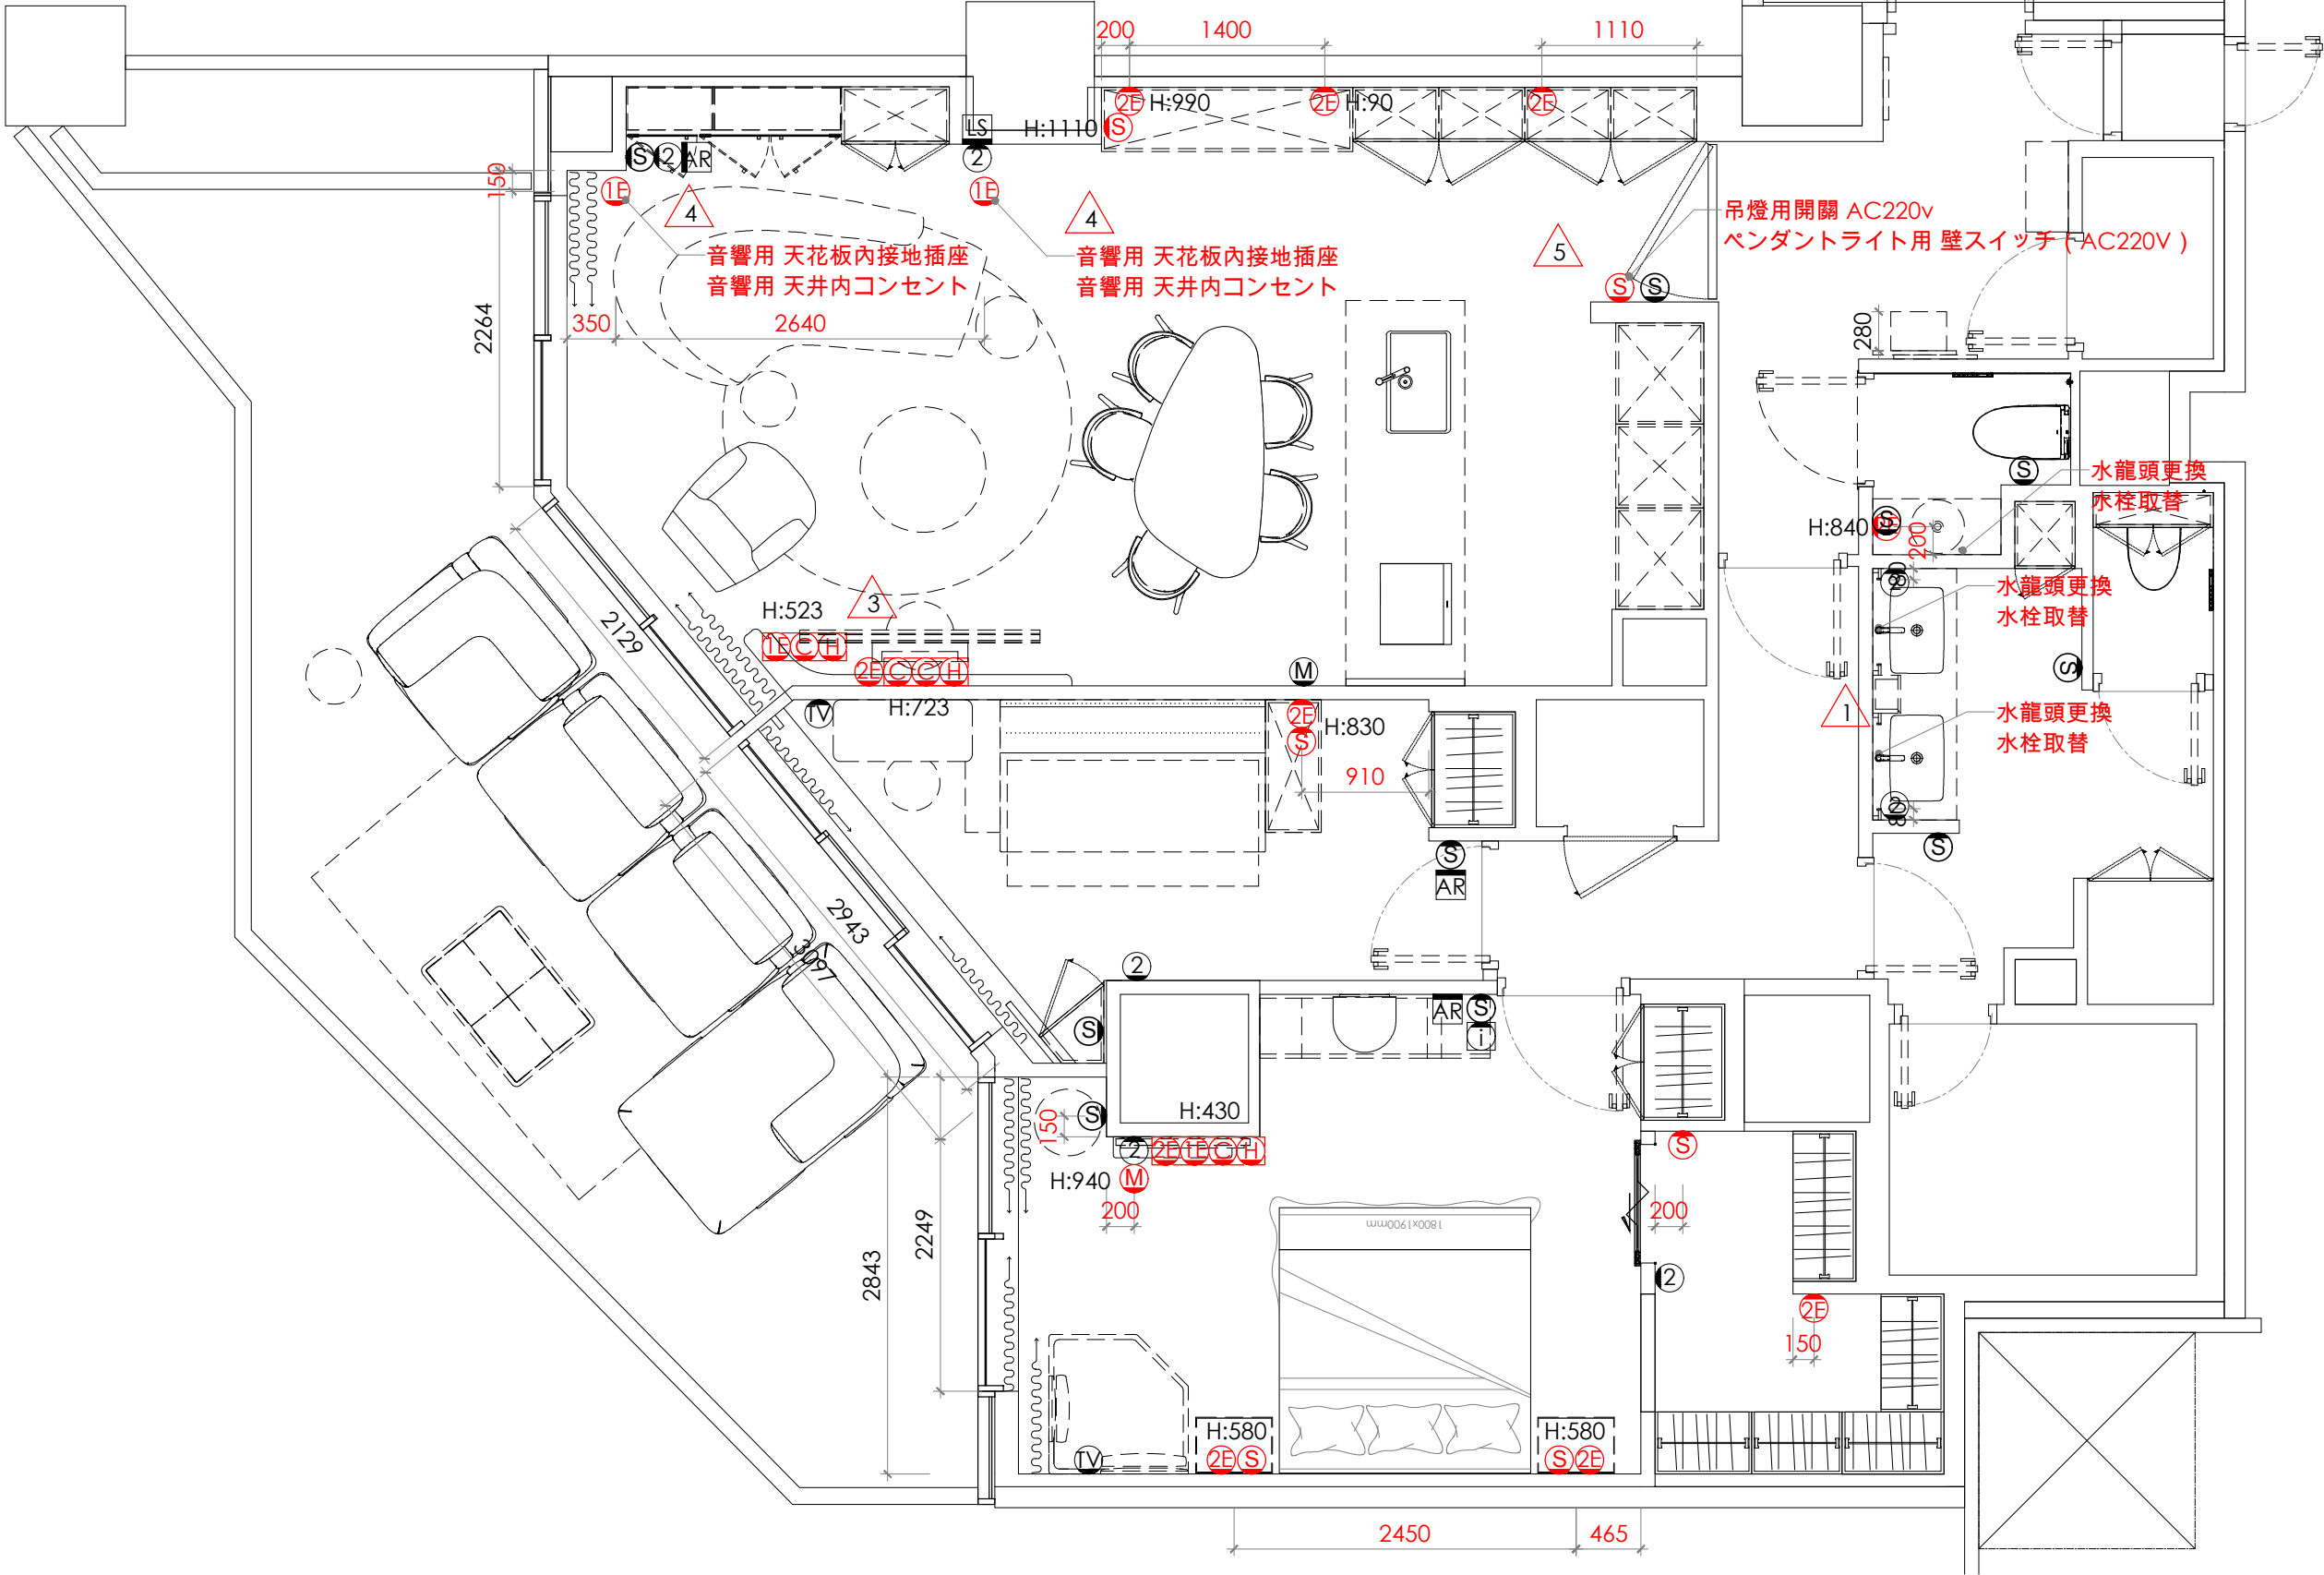

Revision

圖面做以下修正:

- 1.新增水龍頭更換。
- 2.未特別標示之壁面開關、插座設定高度。
- 3.插座配置調整。
- 4.音響用 天花板內接地插座。

図面修正内容は以下のとおり:

- 1.水栓交換の追加。
- 2.特別に高さを示さない壁面スイッチ・コンセントの設置高さを決定する。
- 3.コンセント配置の調整。
- 4.音響用 天井内コンセント。

- 5.ペンダントライト用 壁スイッチ (AC220V)。

APPROVAL/核准

設計者:	建築師:
業主:	

備註:

- a. 圖面標註尺寸僅供參考，施作均以現場放樣檢討之。
- b. 圖面標註尺寸、材料及文字敘述因版本不同之差異，均以出圖章簽認日期之最近為準。
- c. 電腦圖檔除由合約訂定外，均不得以任何方式外流。
- d. 圖面所示均為本公司所擁有之智慧財產，切勿以任何方式複製修改。



MULA DECO

▲ 3F, N.26, Ln.290, Guangfu S. Rd., Taipei.
☎ 886-2-2546-3258
✉ 886-2-2546-3257
E Guido@muladeco.com

Project / 案名


日本神宮案

Sheet Title / 圖名

507

弱電設備平面配置図

Date / 日期	Scale / 比例
4/20/2026	1/50cm
Designer / 設計	Approval / 核准
MONICA	
Job No / 業務編號	Drawn By / 繪圖
00000	GUIDO
Dwg No.	Page No.
P-08	08

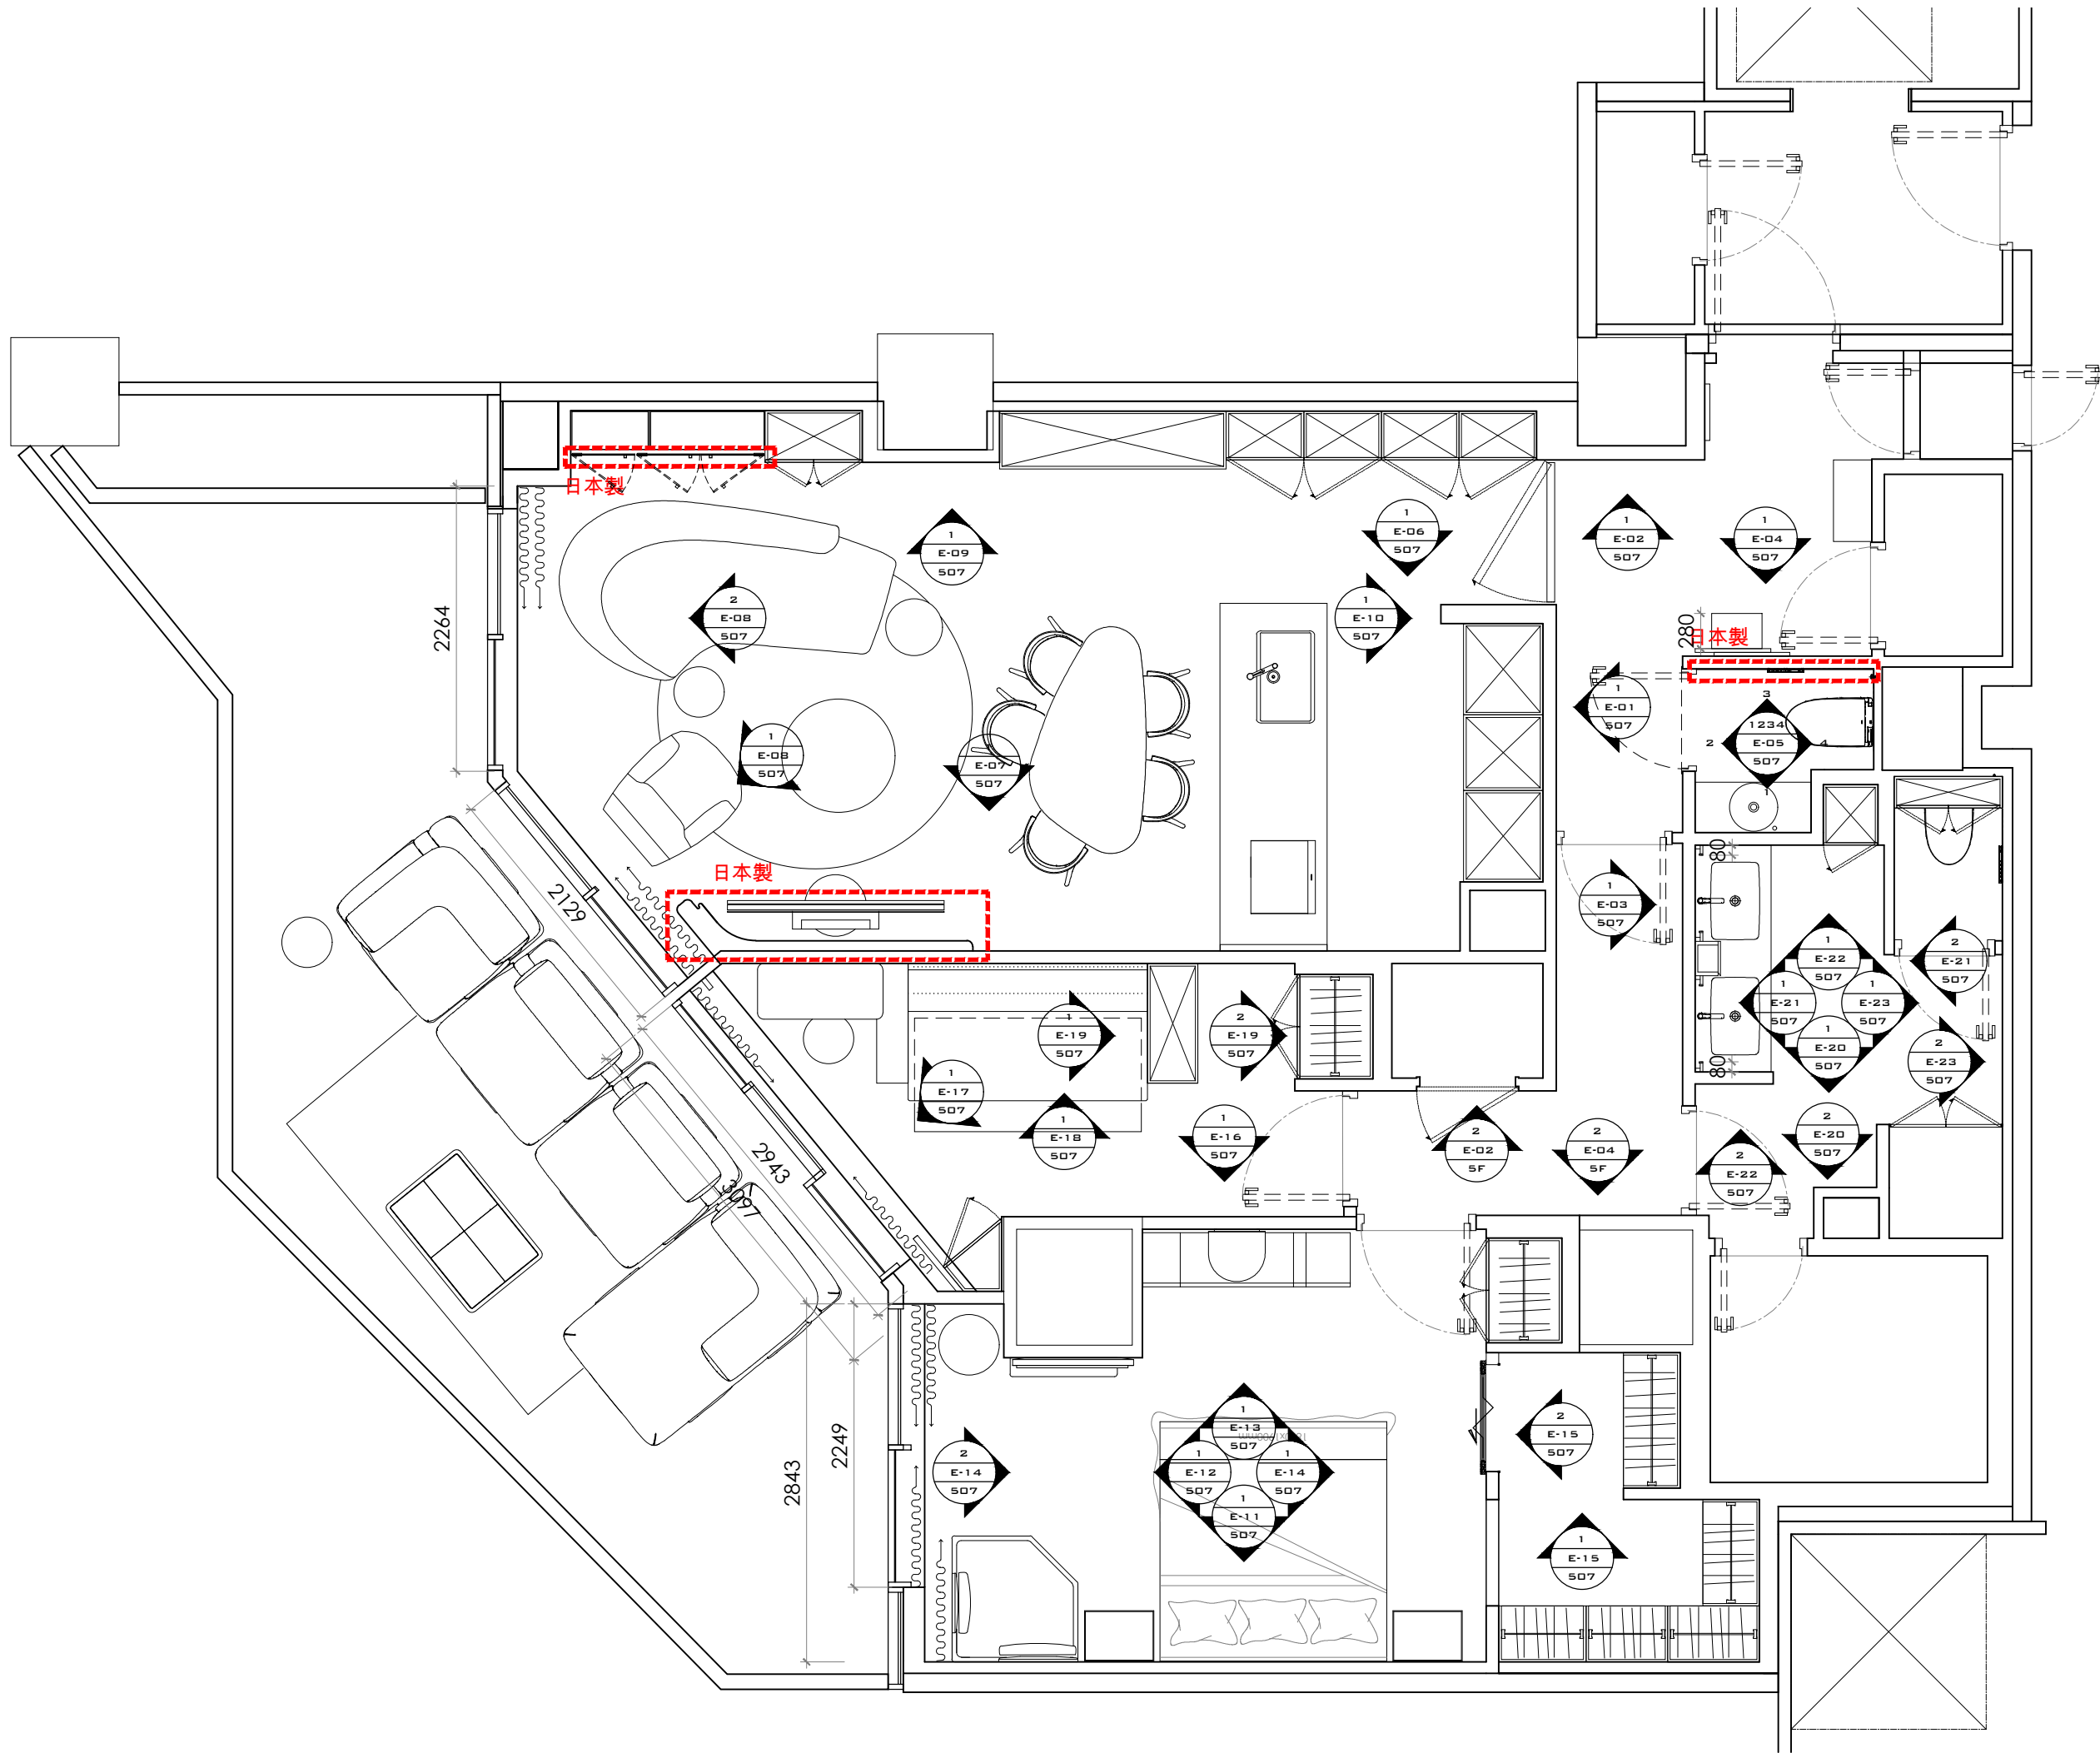

Revision

APPROVAL / 核准

設計者:	建築師:
業主:	

備註:

- 圖面標註尺寸僅供參考，施作均以現場放樣檢討之。
- 圖面標註尺寸、材料及文字敘述因版本不同之差異，均以出圖章簽認日期之最近為準。
- 電腦圖檔除由合約訂定外，均不得以任何方式外流。
- 圖面所示均為本公司所擁有之智慧財產，切勿以任何方式複製修改。



MULA DECO

▲ 3F, N.26, Ln.290, Guangfu S. Rd., Taipei.
T 886-2-2546-3258
F 886-2-2546-3257
E Guido@muladeco.com

Project / 案名

日本神宮案

Sheet Title / 圖名
507

立面索引圖

Date / 日期	Scale / 比例
4/20/2026	1/50cm
Designer / 設計	Approval / 核准
MONICA	
Job No / 業務編號	Drawn By / 繪圖
00000	GUIDO

Dwg No.

Page No.

P-10

10