



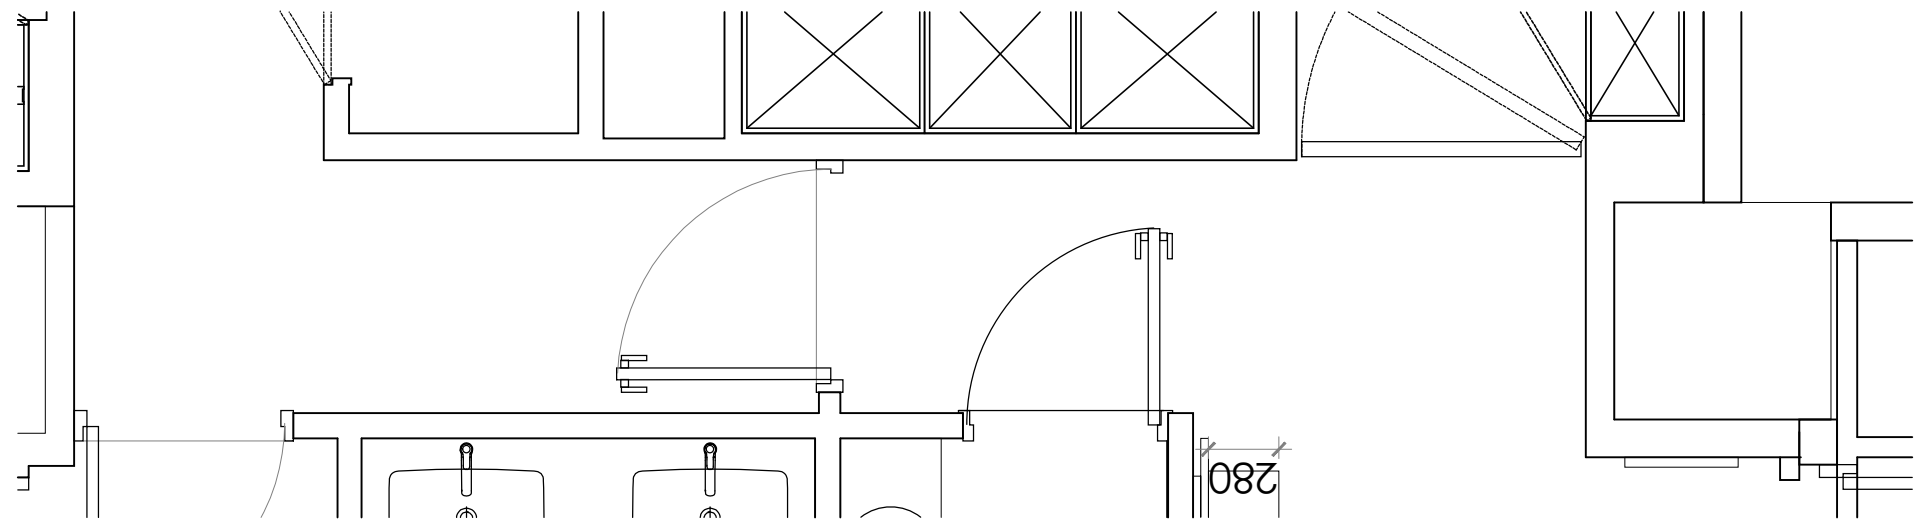

△CH 2205mm

▼FL ±0 mm
▲FL -50 mm

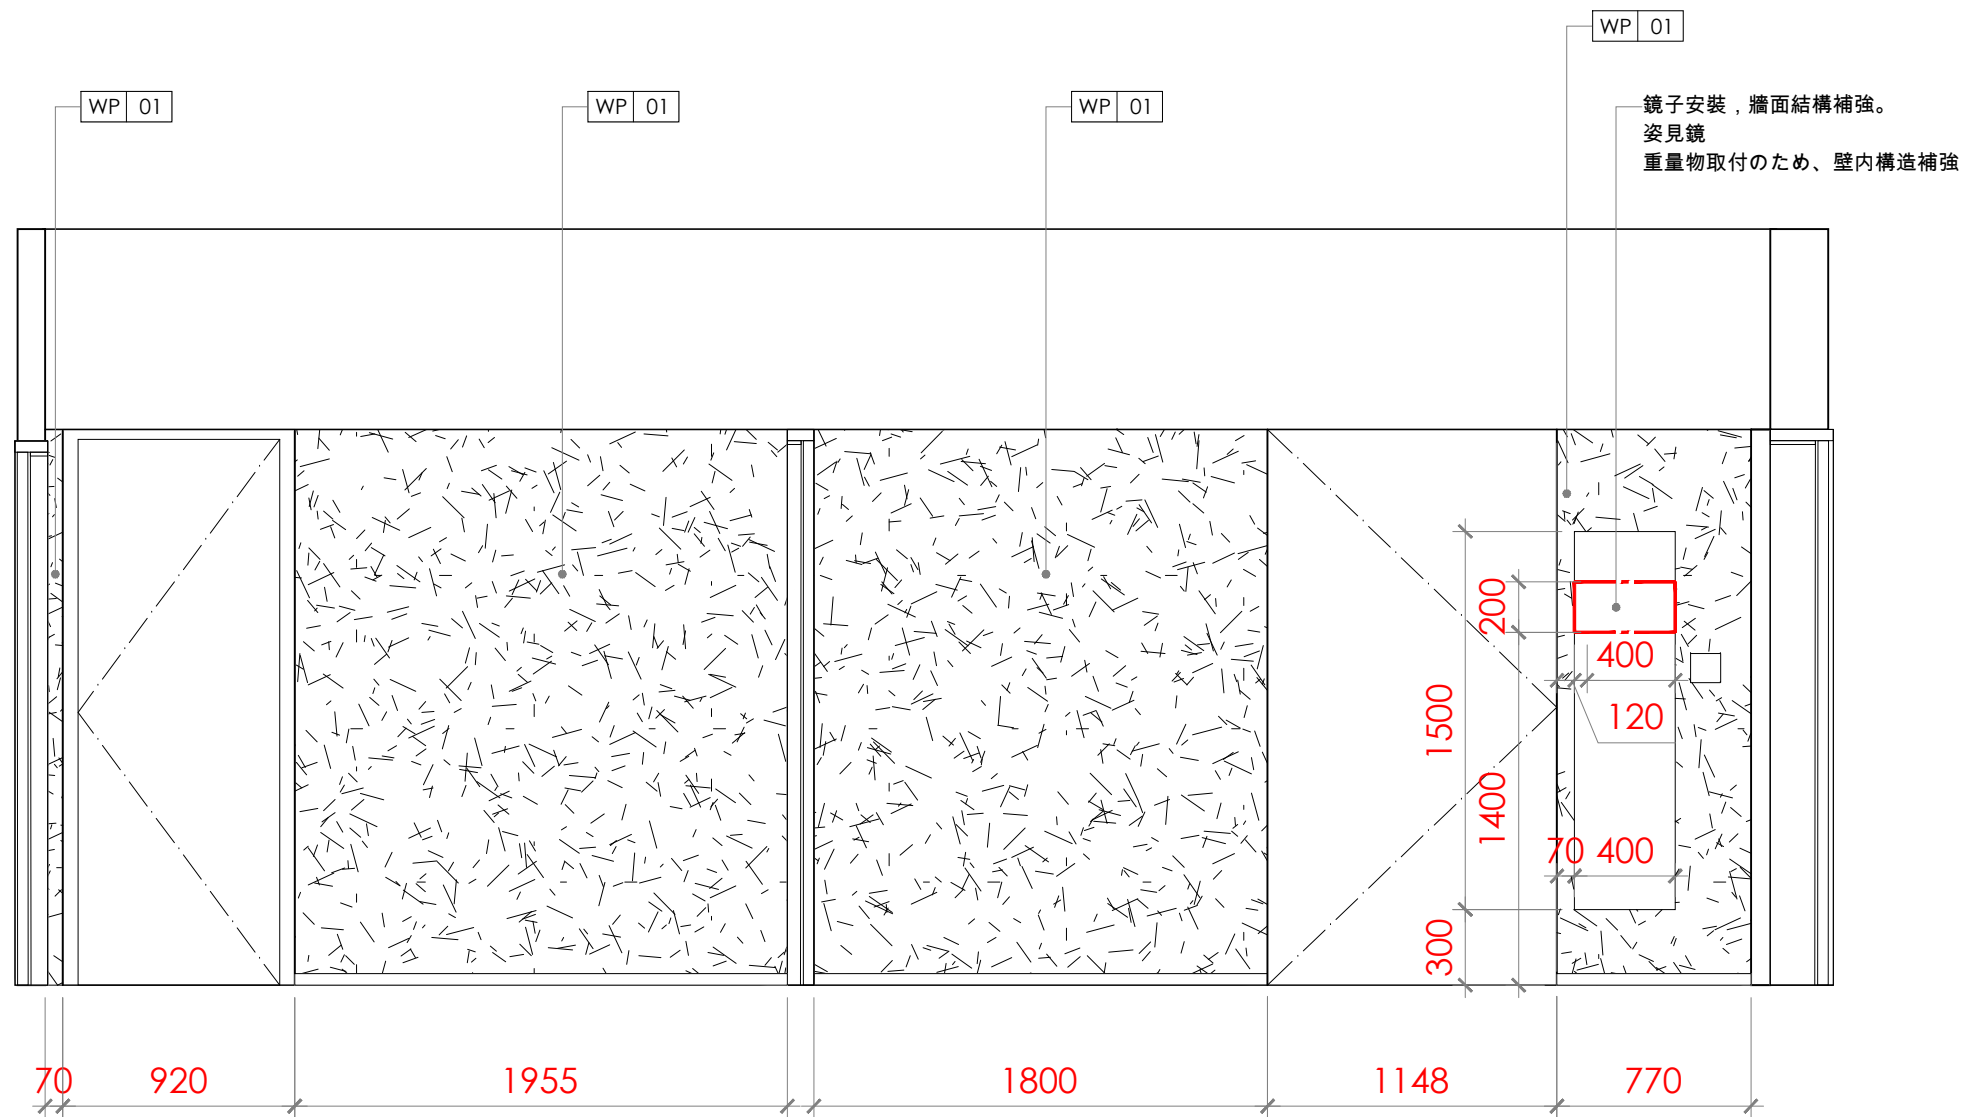

1
E-01

ELEVATION

Scale=1:30

Revision

APPROVAL/核准

設計者:	建築師:
業主:	

備註:

- 圖面標註尺寸僅供參考，施作均以現場放樣檢討之。
- 圖面標註尺寸、材料及文字敘述因版本不同之差異，均以出圖章簽認日期之最近為準。
- 電腦圖檔除由合約訂定外，均不得以任何方式外流。
- 圖面所示均為本公司所擁有之智慧財產，切勿以任何方式複製修改。



MULA DECO

▲ 3F, N.26, Ln.290, Guangfu S. Rd., Taipei.
☎ 886-2-2546-3258
☎ 886-2-2546-3257
✉ Guido@muladeco.com

Project / 案名

日本神宮案



Sheet Title / 圖名
507

立面圖

Date / 日期	Scale / 比例
3/25/2026	1/30cm
Designer / 設計	Approval / 核准
MONICA LIN	
Job No / 業務編號	Drawn By / 繪圖
00000	GUIDO
Dwg No.	Page No.


E-01

11

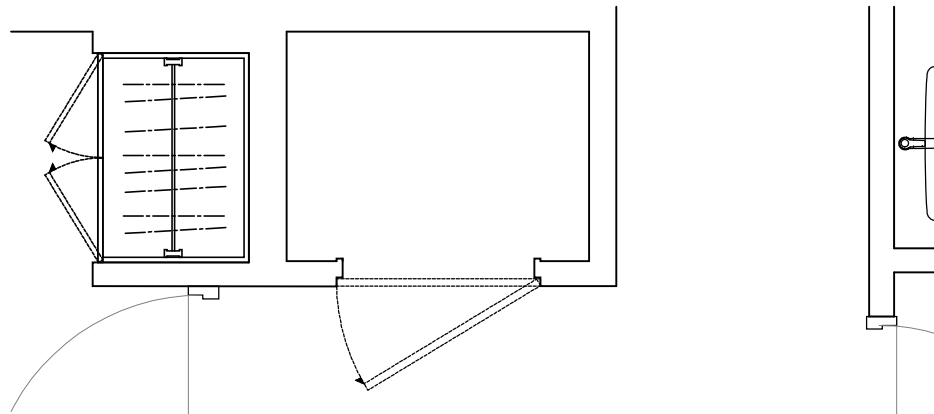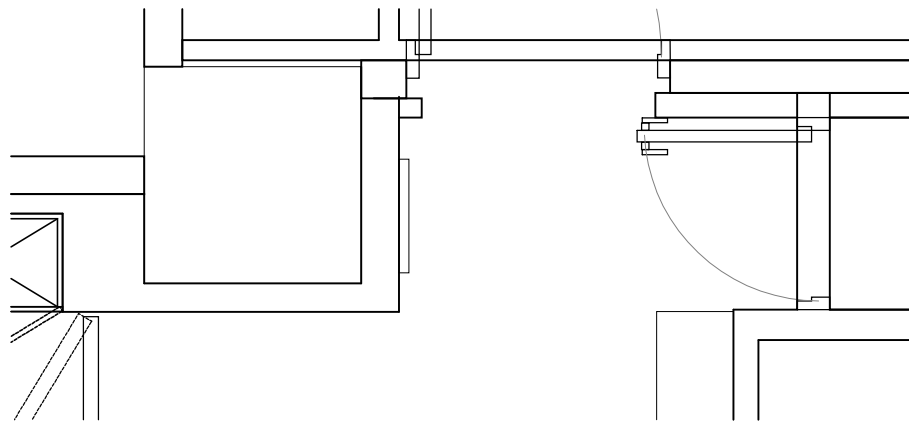

△CH 2205mm


▼FL ±0 mm
▲FL -50 mm

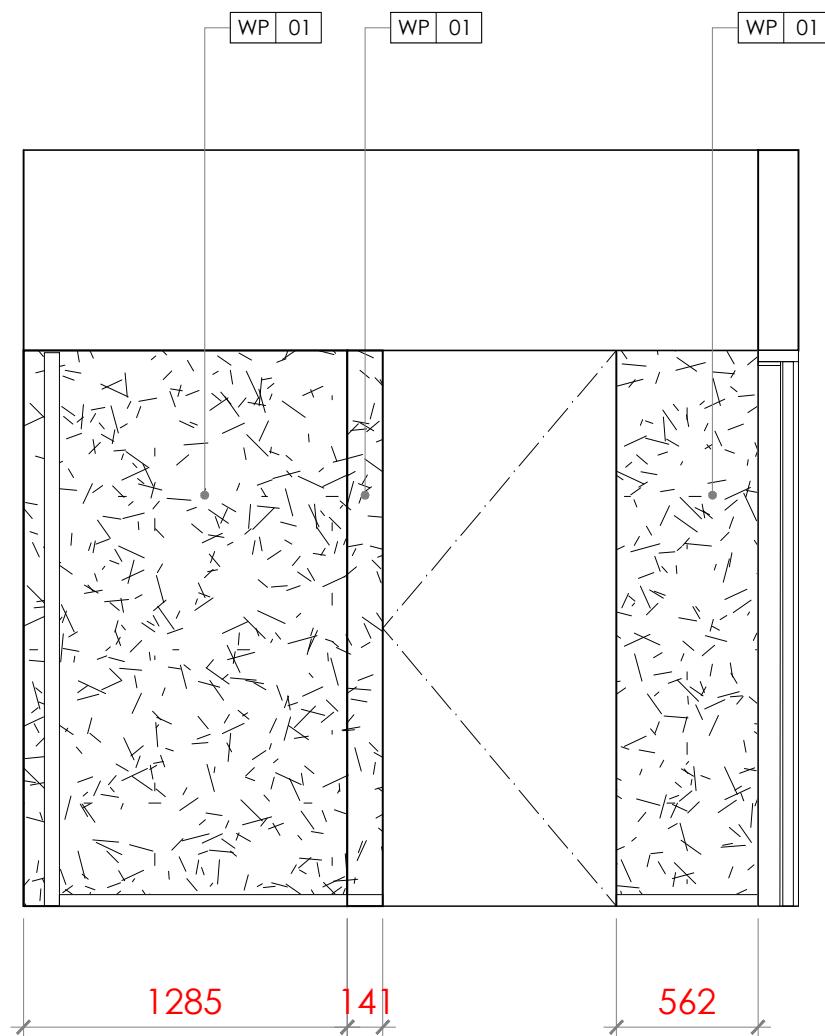

1
E-02

ELEVATION

Scale=1:30

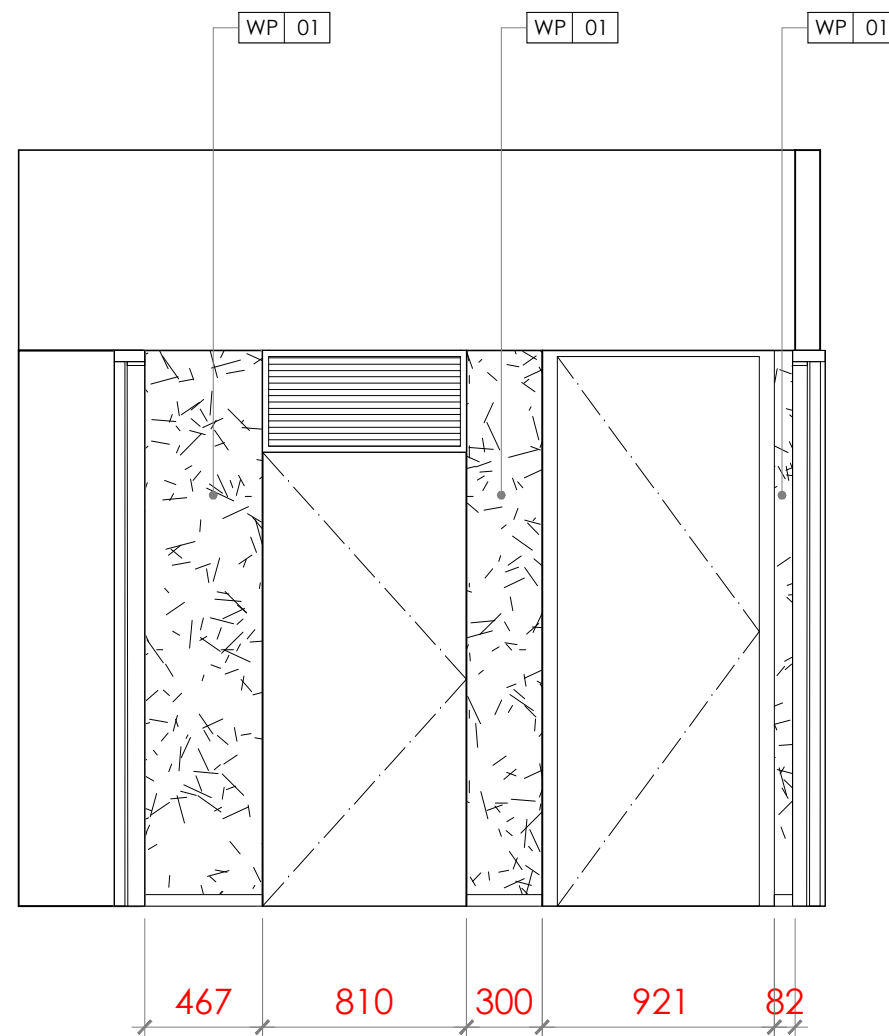

2
E-02

ELEVATION

Scale=1:30

Revision

APPROVAL/核准

設計者:	建築師:
業主:	

備註:

- 圖面標註尺寸僅供參考，施作均以現場放樣檢討之。
- 圖面標註尺寸、材料及文字敘述因版本不同之差異，均以出圖章簽認日期之最近為準。
- 電腦圖檔除由合約訂定外，均不得以任何方式外流。
- 圖面所示均為本公司所擁有之智慧財產，切勿以任何方式複製修改。



MULA DECO

▲ 3F, N.26, Ln.290, Guangfu S. Rd., Taipei.
☎ 886-2-2546-3258
☎ 886-2-2546-3257
✉ Guido@muladeco.com

Project / 案名

日本神宮案



Sheet Title / 圖名
507

立面圖

Date / 日期	Scale / 比例
3/25/2026	1/30cm
Designer / 設計	Approval / 核准
MONICA LIN	
Job No / 業務編號	Drawn By / 繪圖
00000	GUIDO
Dwg No.	Page No.

E-02

12

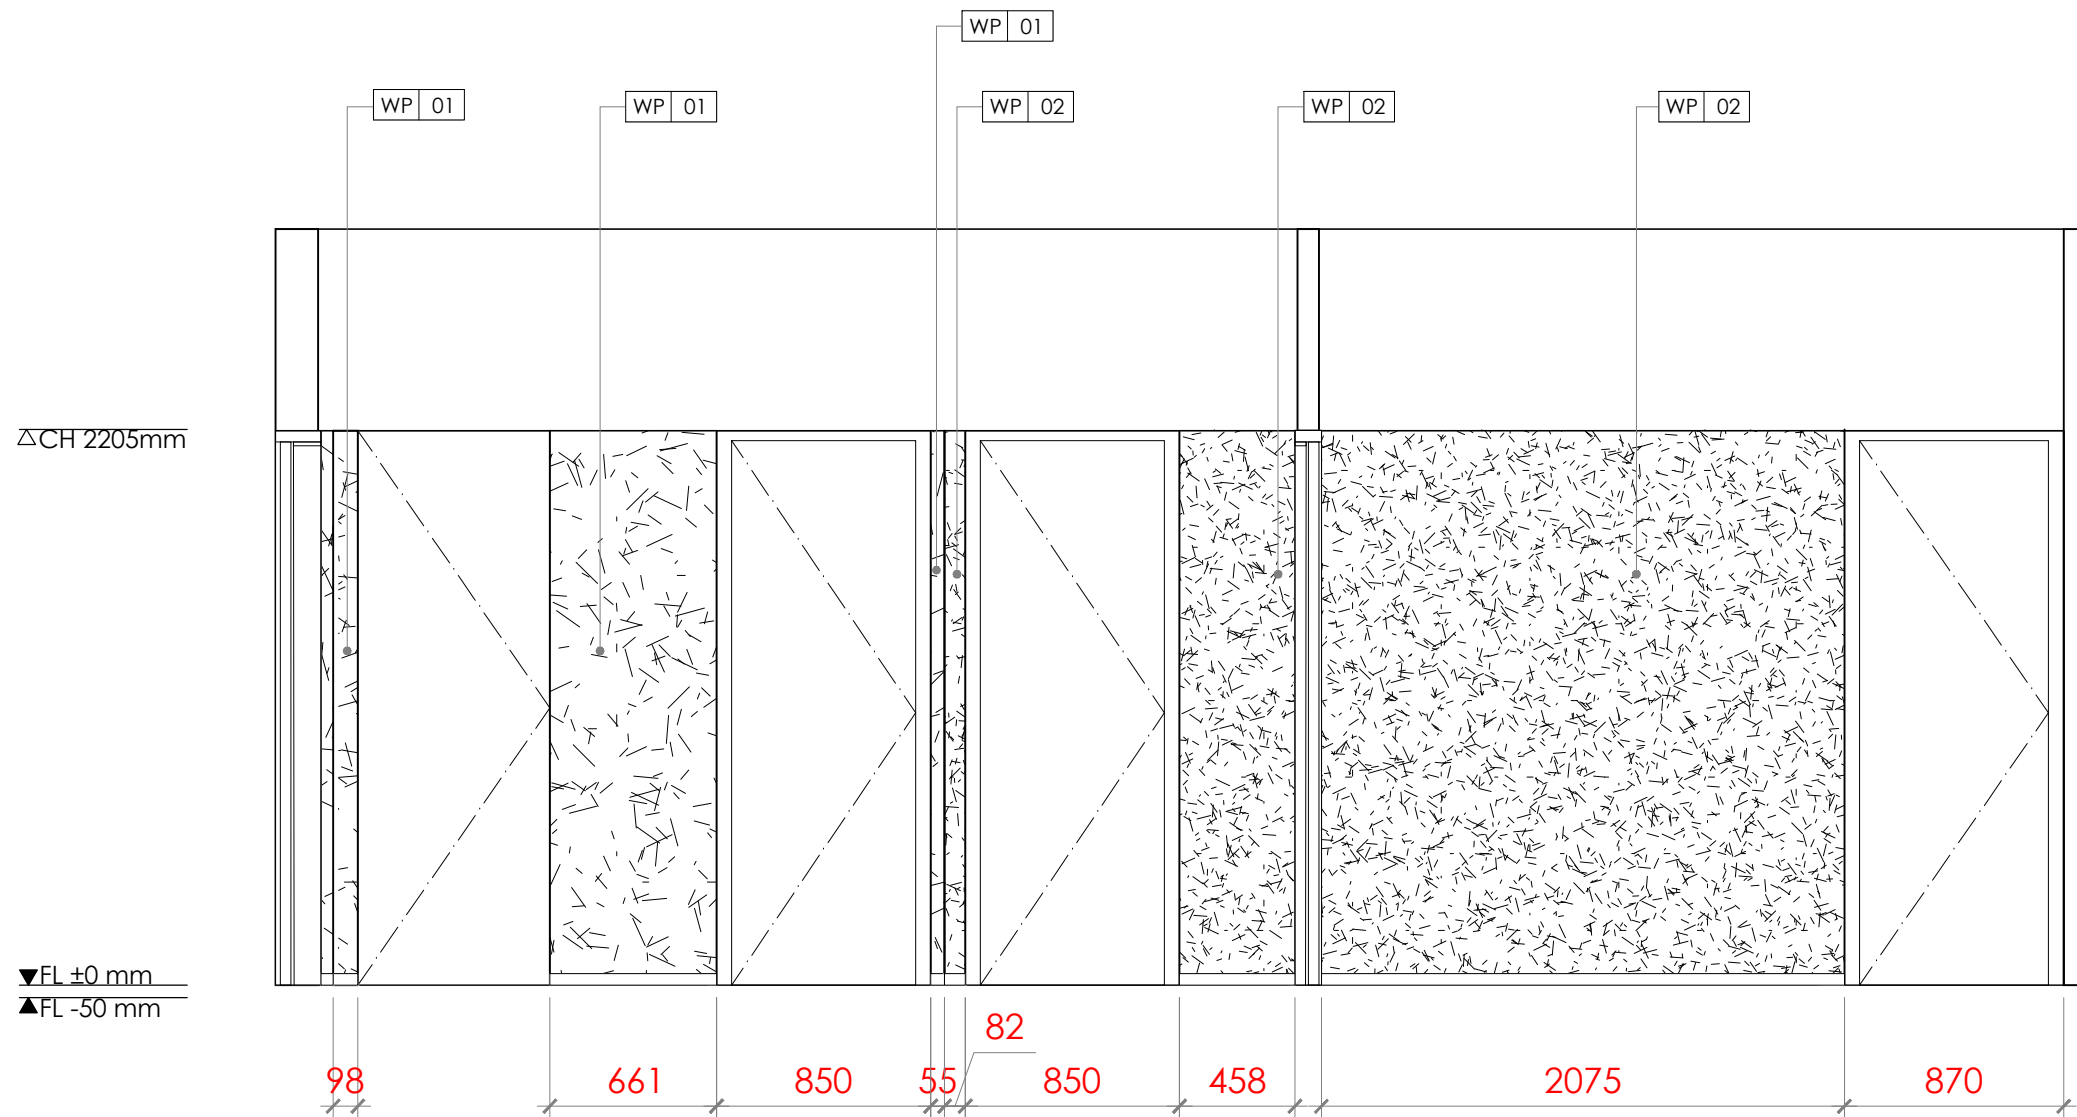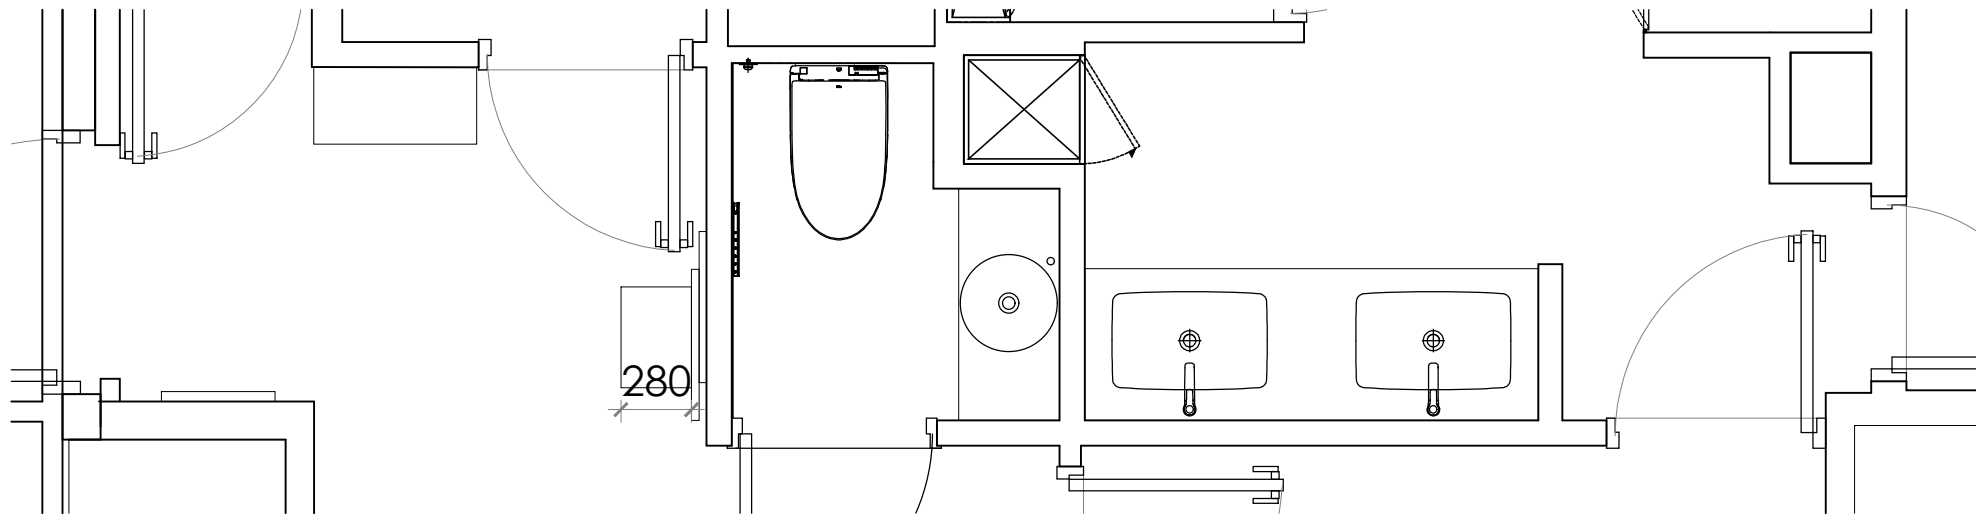

1
E-03

ELEVATION

Scale=1:30

Revision

APPROVAL / 核准

設計者:	建築師:
業主:	

備註:

- 圖面標註尺寸僅供參考，施作均以現場放樣檢討之。
- 圖面標註尺寸、材料及文字敘述因版本不同之差異，均以出圖章簽認日期之最近為準。
- 電腦圖檔除由合約訂定外，均不得以任何方式外流。
- 圖面所示均為本公司所擁有之智慧財產，切勿以任何方式複製修改。



MULA DECO

▲ 3F, N.26, Ln.290, Guangfu S. Rd., Taipei.
☎ 886-2-2546-3258
☎ 886-2-2546-3257
✉ Guido@muladeco.com

Project / 案名

日本神宮案



Sheet Title / 圖名
507

立面圖

Date / 日期	Scale / 比例
3/25/2026	1/30cm
Designer / 設計	Approval / 核准
MONICA LIN	
Job No / 業務編號	Drawn By / 繪圖
00000	GUIDO
Dwg No.	Page No.



E-03

13

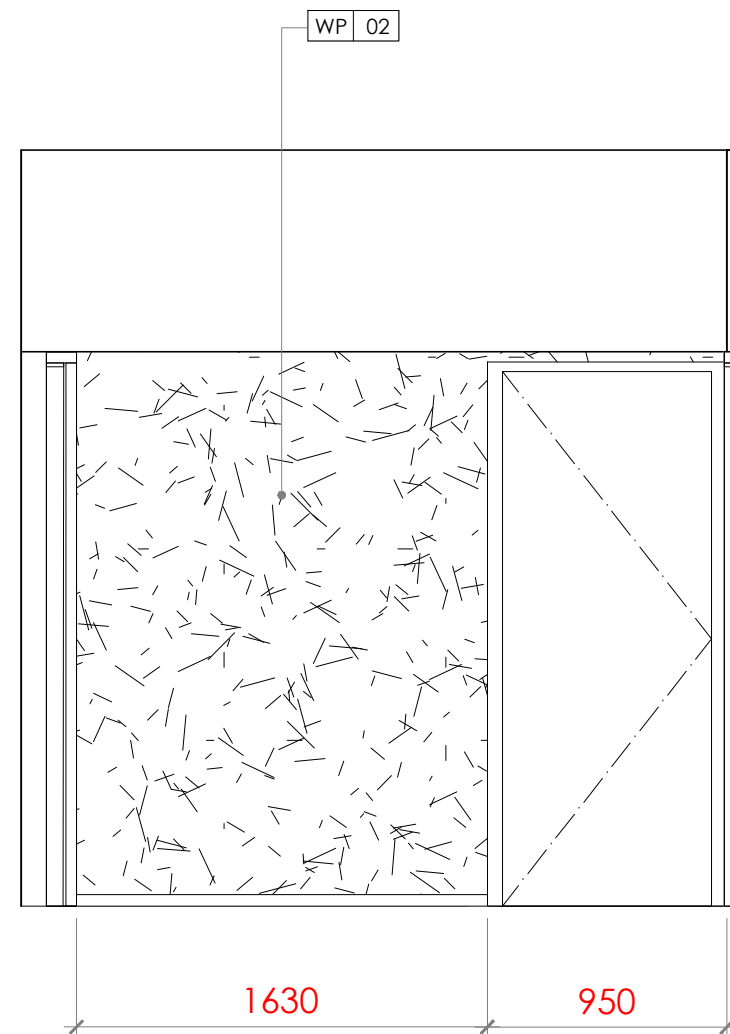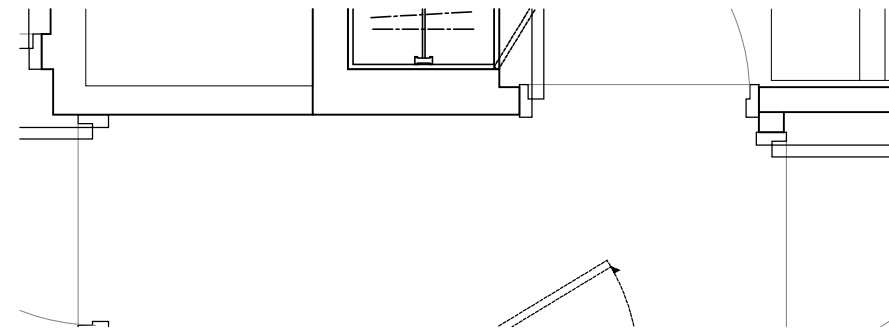

2 ELEVATION
E-04 Scale=1:30

Dwg No.	Page No.
E-04	14

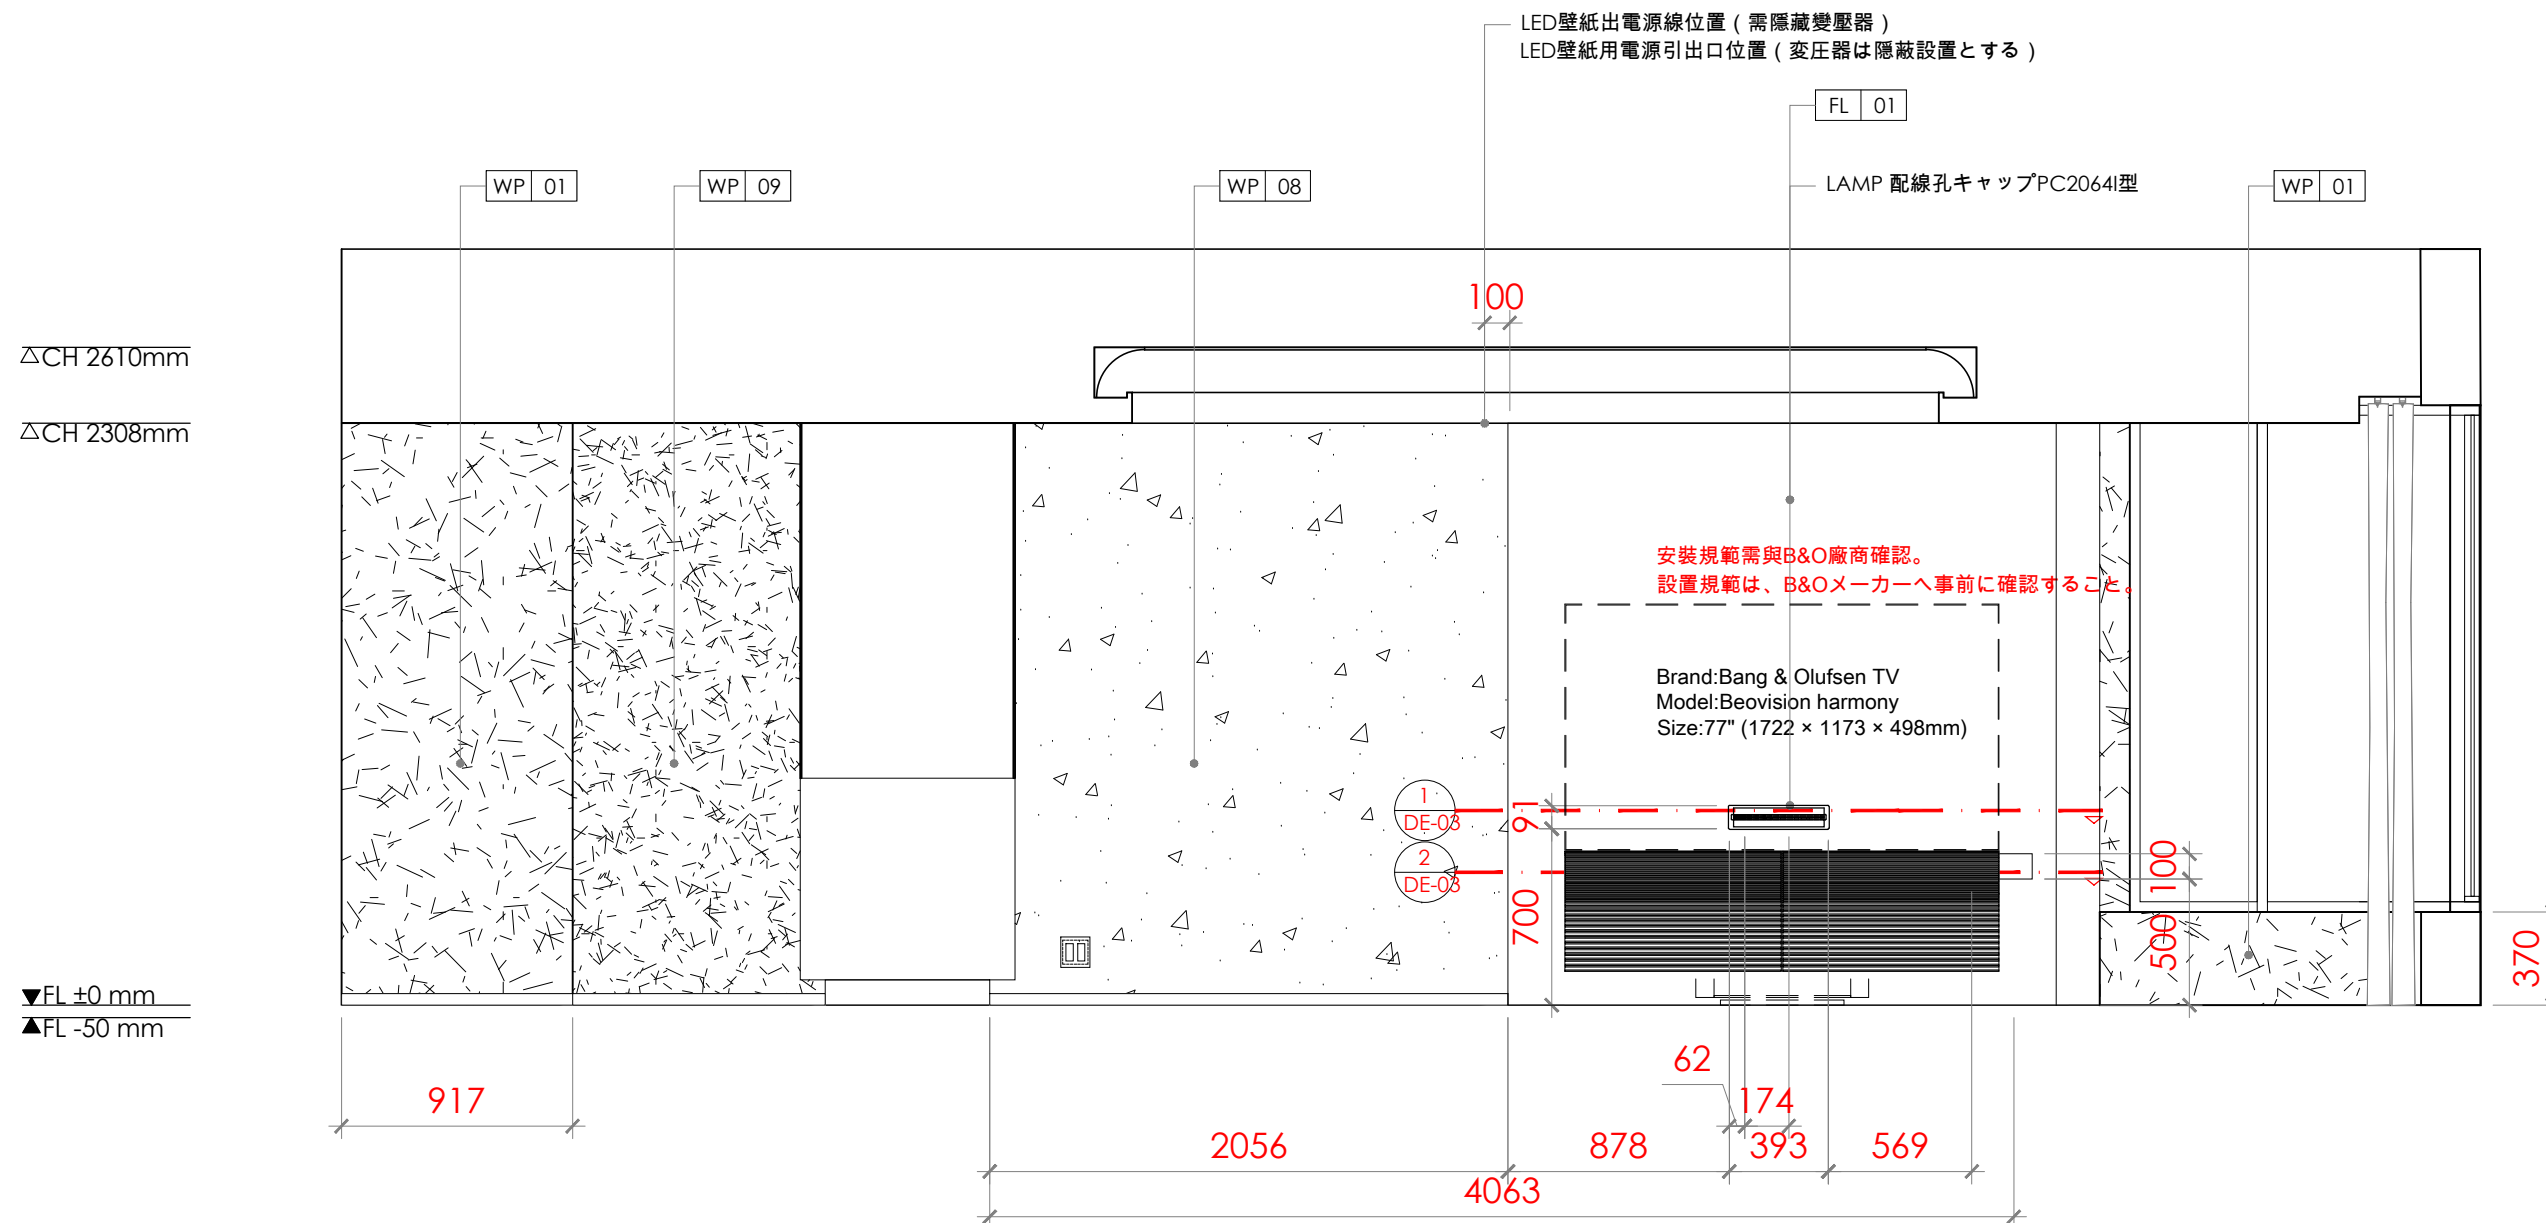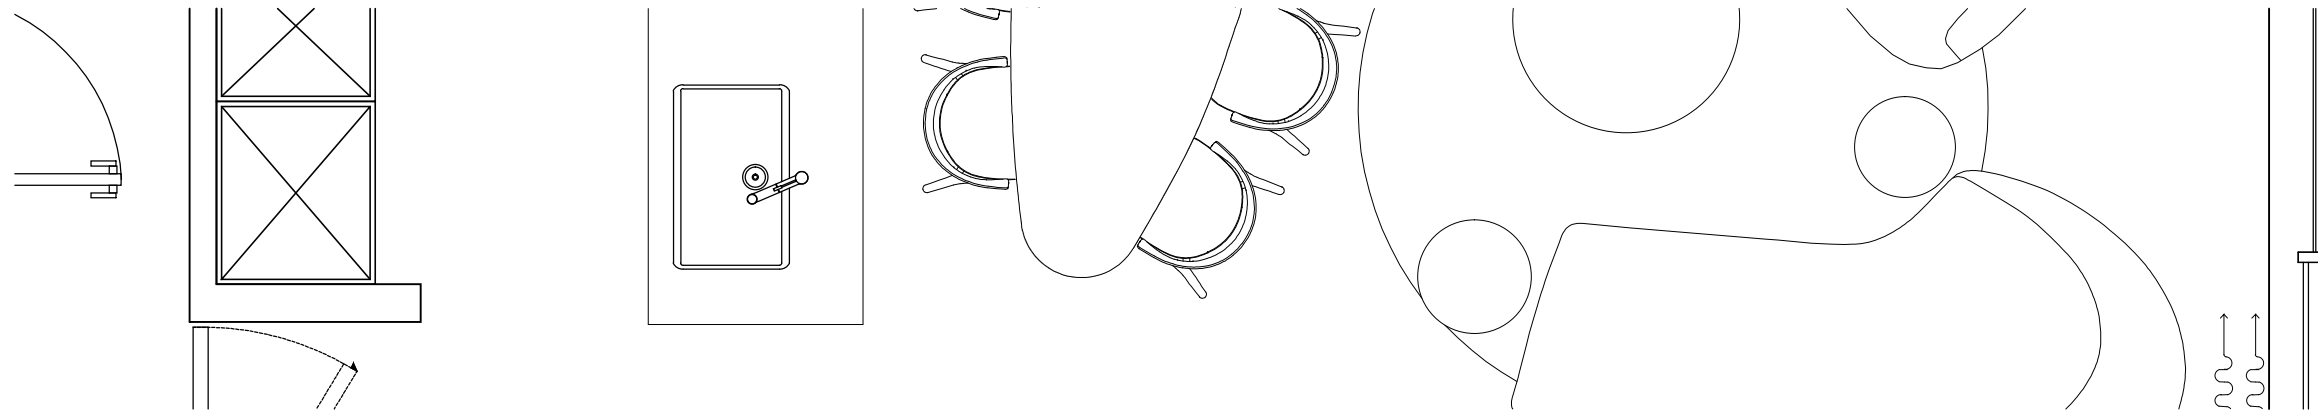

1
E-06

ELEVATION

Scale=1:30

Revision

APPROVAL/核准

設計者:	建築師:
業主:	

備註:

- 圖面標註尺寸僅供參考，施作均以現場放樣檢討之。
- 圖面標註尺寸、材料及文字敘述因版本不同之差異，均以出圖章簽認日期之最近為準。
- 電腦圖檔除由合約訂定外，均不得以任何方式外流。
- 圖面所示均為本公司所擁有之智慧財產，切勿以任何方式複製修改。



MULA DECO

▲ 3F, N.26, Ln.290, Guangfu S. Rd., Taipei.
☎ 886-2-2546-3258
☎ 886-2-2546-3257
✉ Guido@muladeco.com

Project / 案名

日本神宮案


Sheet Title / 圖名
507

立面圖

Date / 日期	Scale / 比例
3/25/2026	1/30cm
Designer / 設計	Approval / 核准
MONICA LIN	
Job No / 業務編號	Drawn By / 繪圖
00000	GUIDO
Dwg No.	Page No.

E-06


16

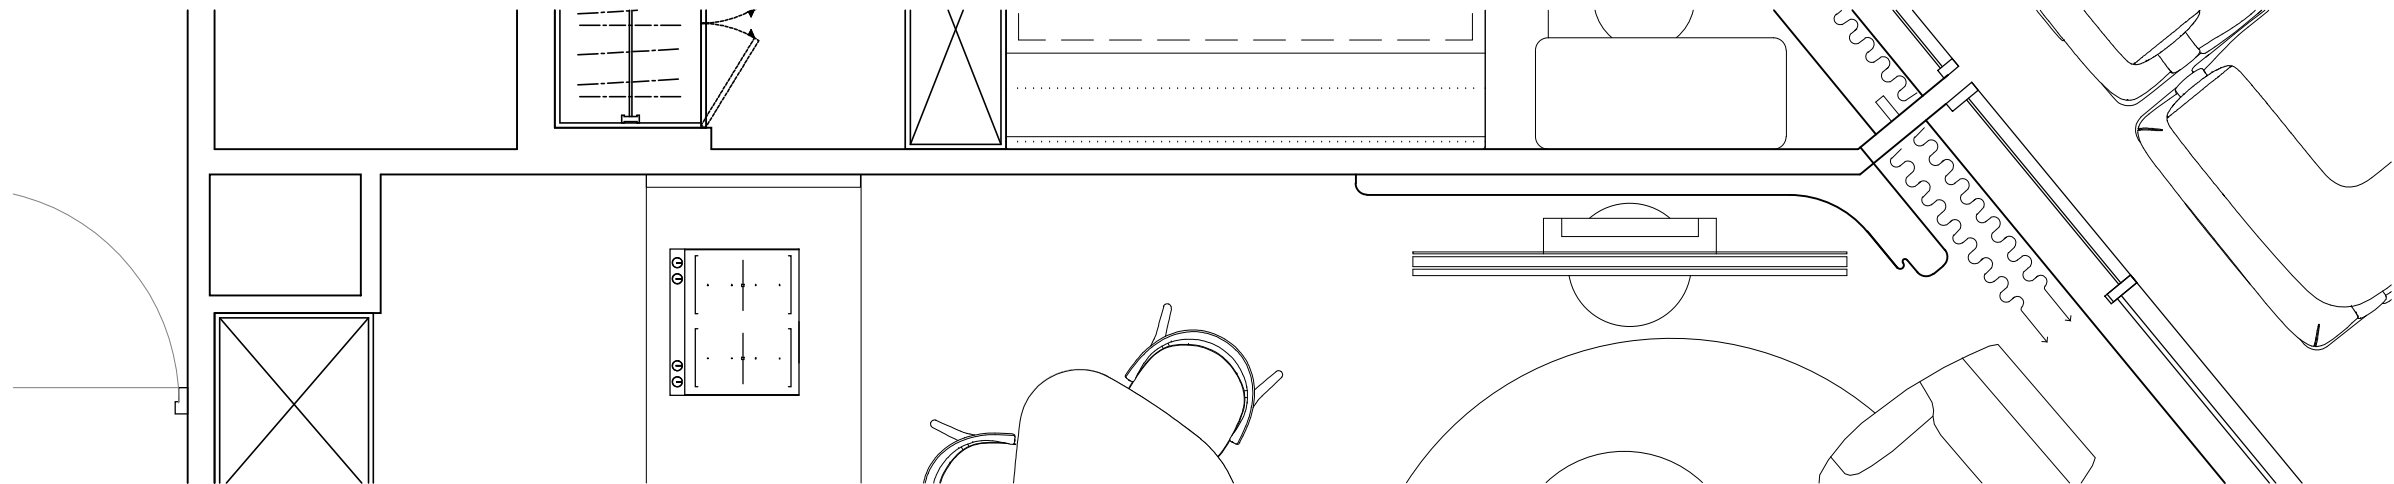

△CH 2610mm

△CH 2308mm

▼FL ±0 mm
▲FL -50 mm

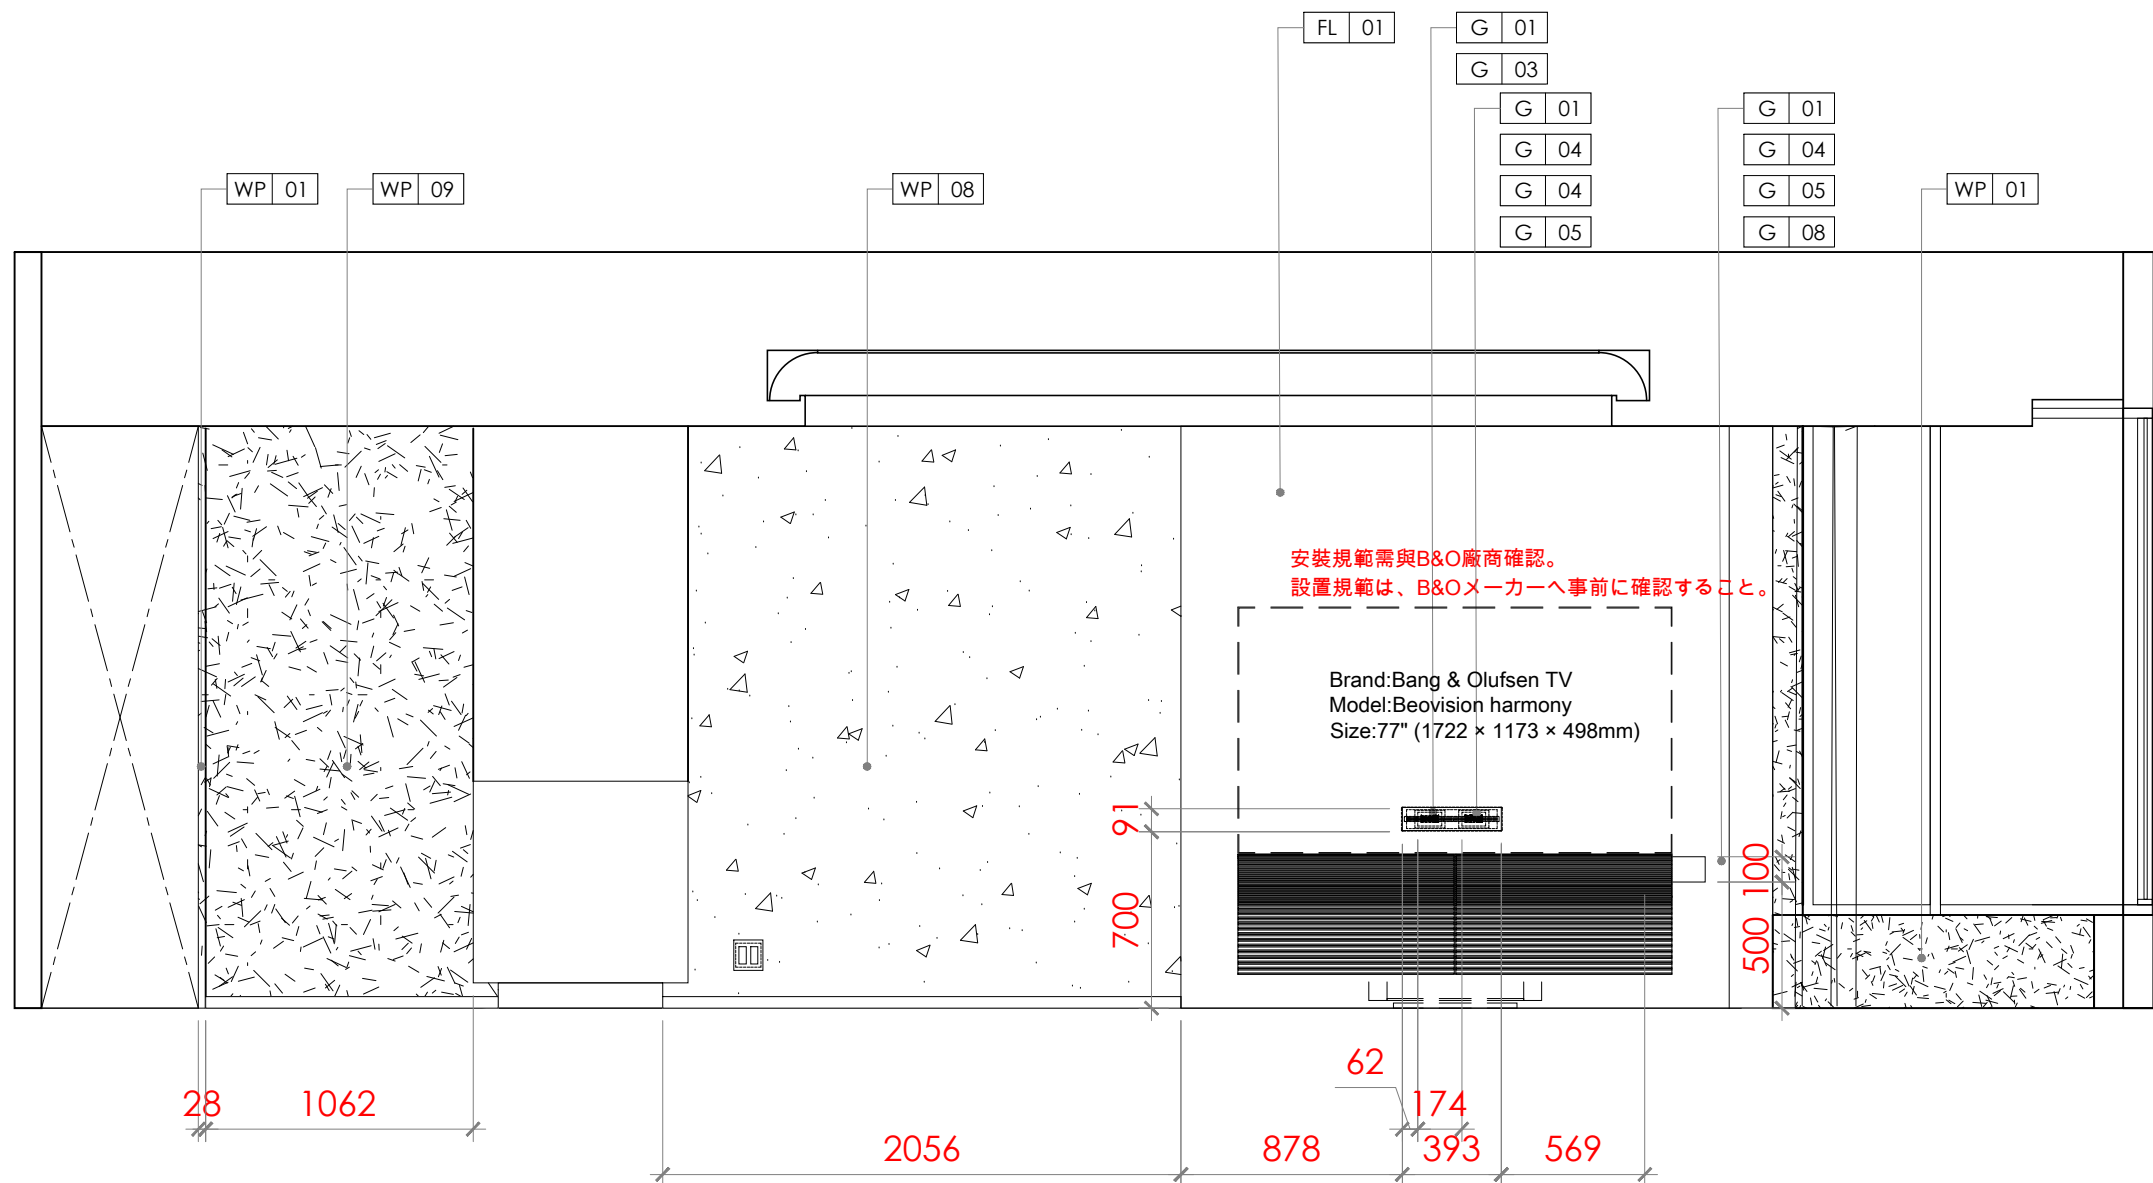

1
E-07

ELEVATION

Scale=1:30

Revision

APPROVAL/核准

設計者:	建築師:
業主:	

備註:
a. 圖面標註尺寸僅供參考，施作均以現場放樣檢討之。
b. 圖面標註尺寸、材料及文字敘述因版本不同之差異，均以出圖章簽認日期之最近為準。
c. 電腦圖檔除由合約訂定外，均不得以任何方式外流。
d. 圖面所示均為本公司所擁有之智慧財產，切勿以任何方式複製修改。



MULA DECO

▲ 3F, N.26, Ln.290, Guangfu S. Rd., Taipei.
☎ 886-2-2546-3258
☎ 886-2-2546-3257
✉ Guido@muladeco.com

Project / 案名

日本神宮案



Sheet Title / 圖名
507

立面圖

Date / 日期	Scale / 比例
3/25/2026	1/30cm
Designer / 設計	Approval / 核准
MONICA LIN	
Job No / 業務編號	Drawn By / 繪圖
00000	GUIDO
Dwg No.	Page No.

E-07

17

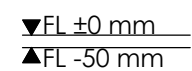
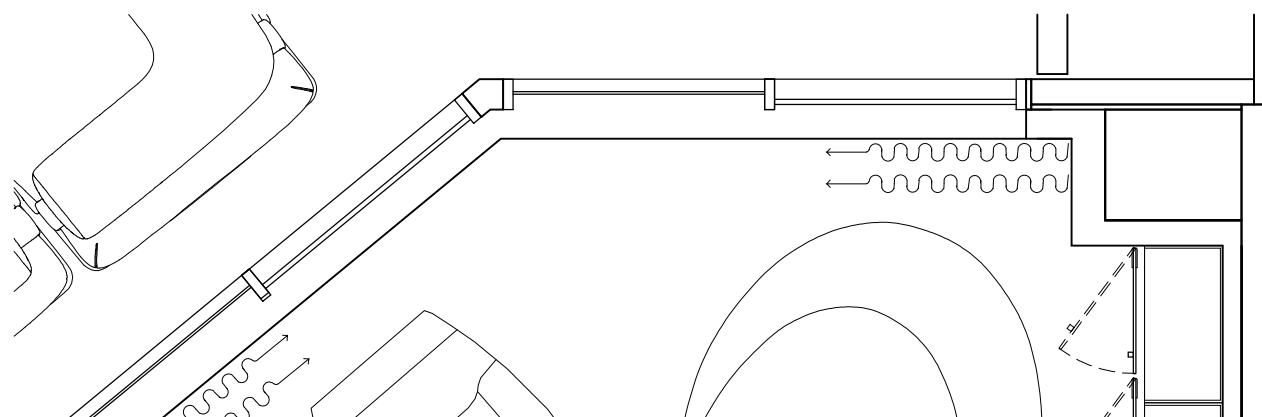


Scale=1:30



Scale=1:30

E-08 18

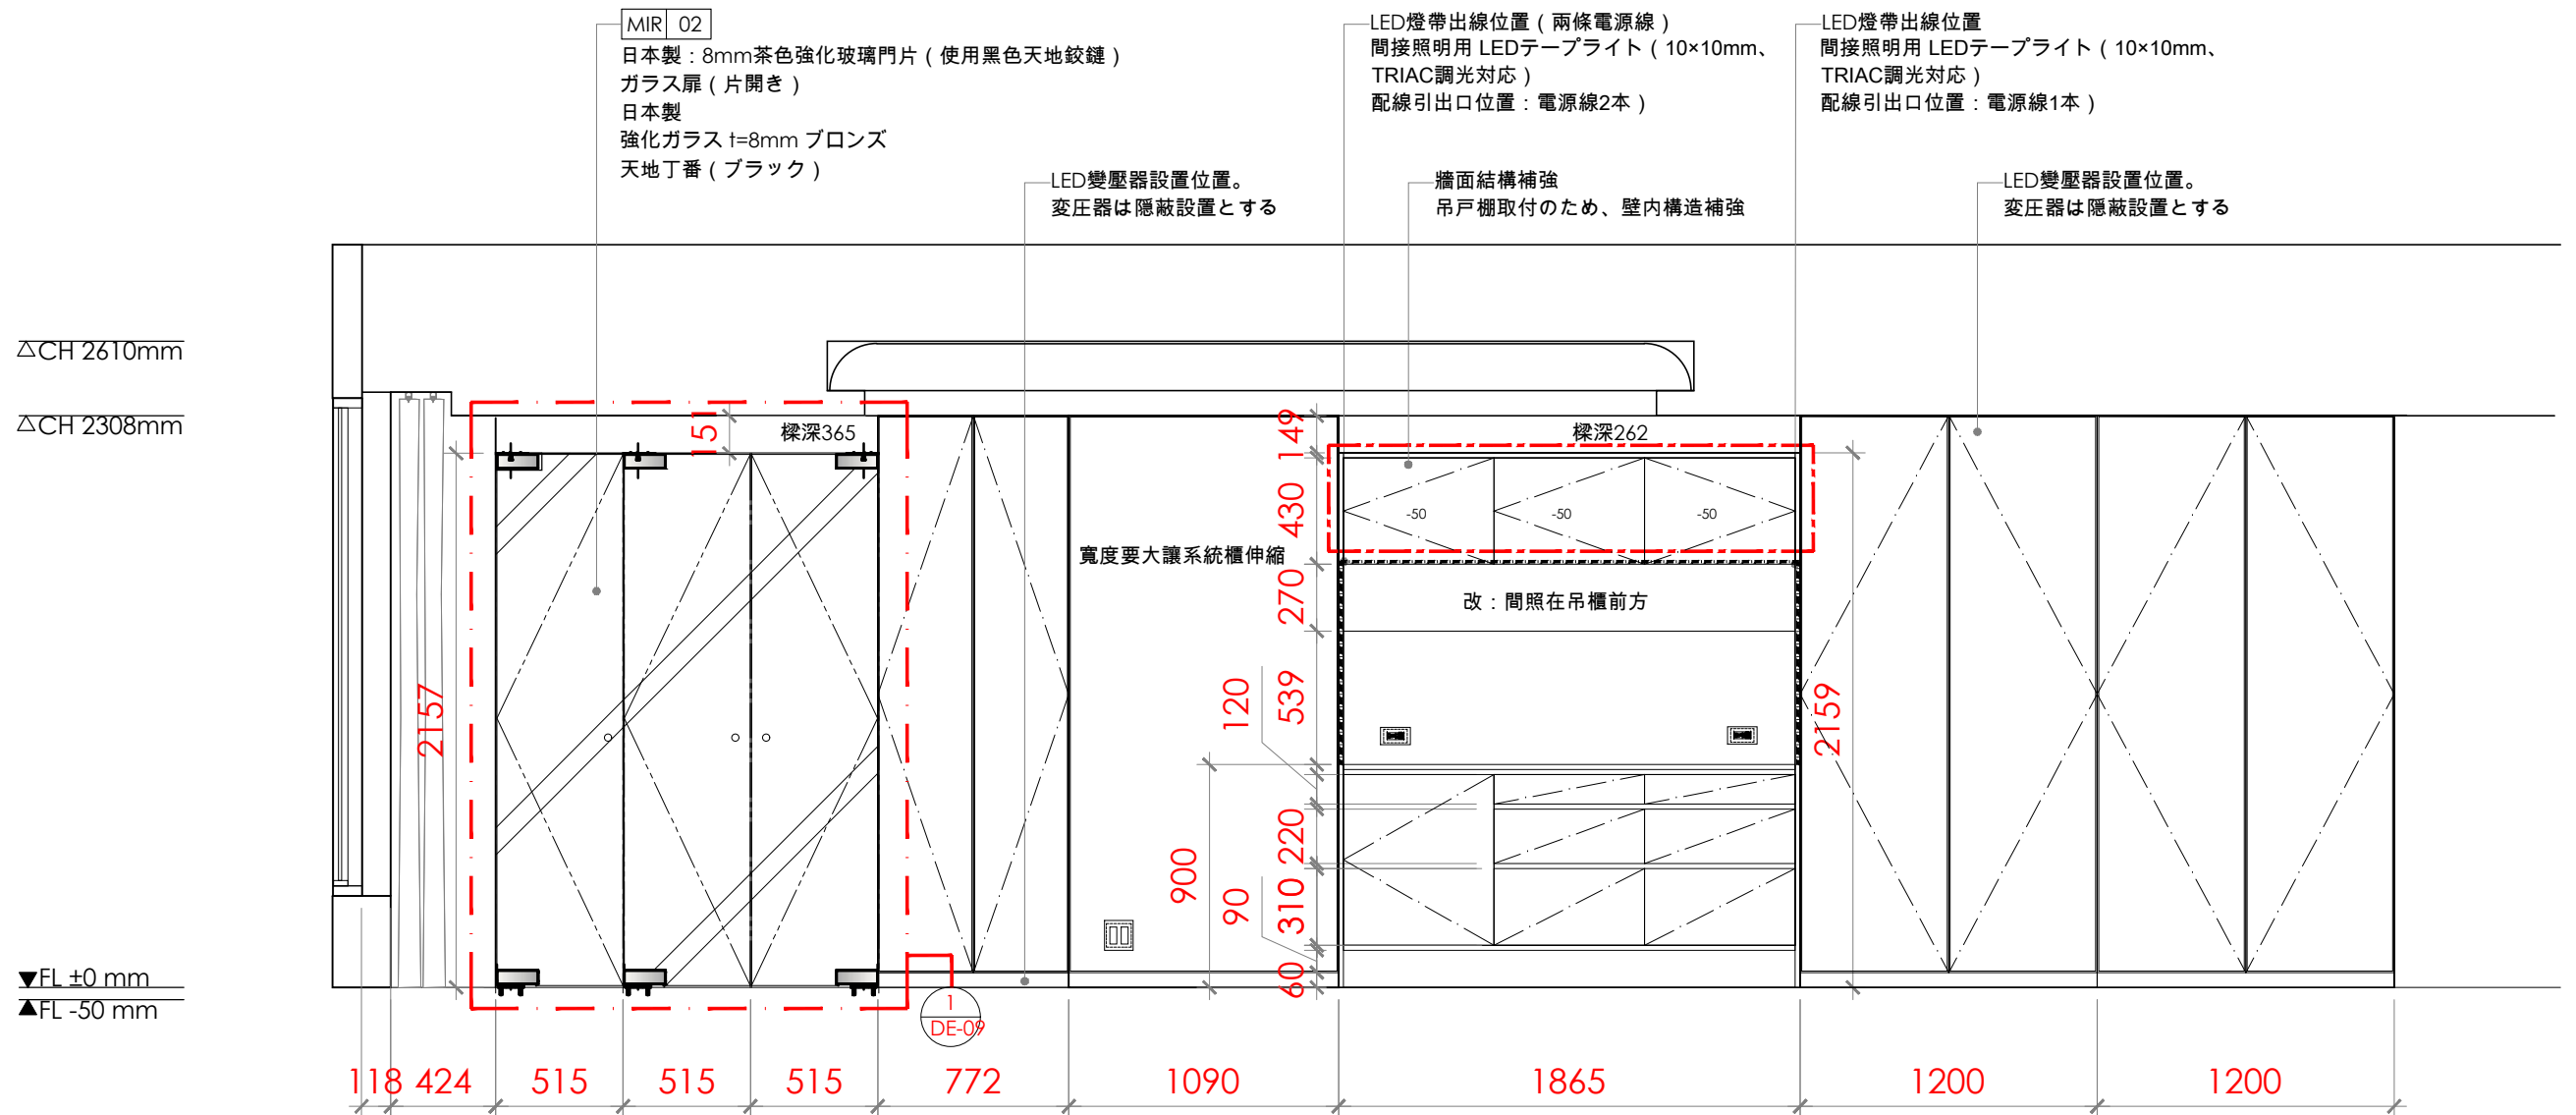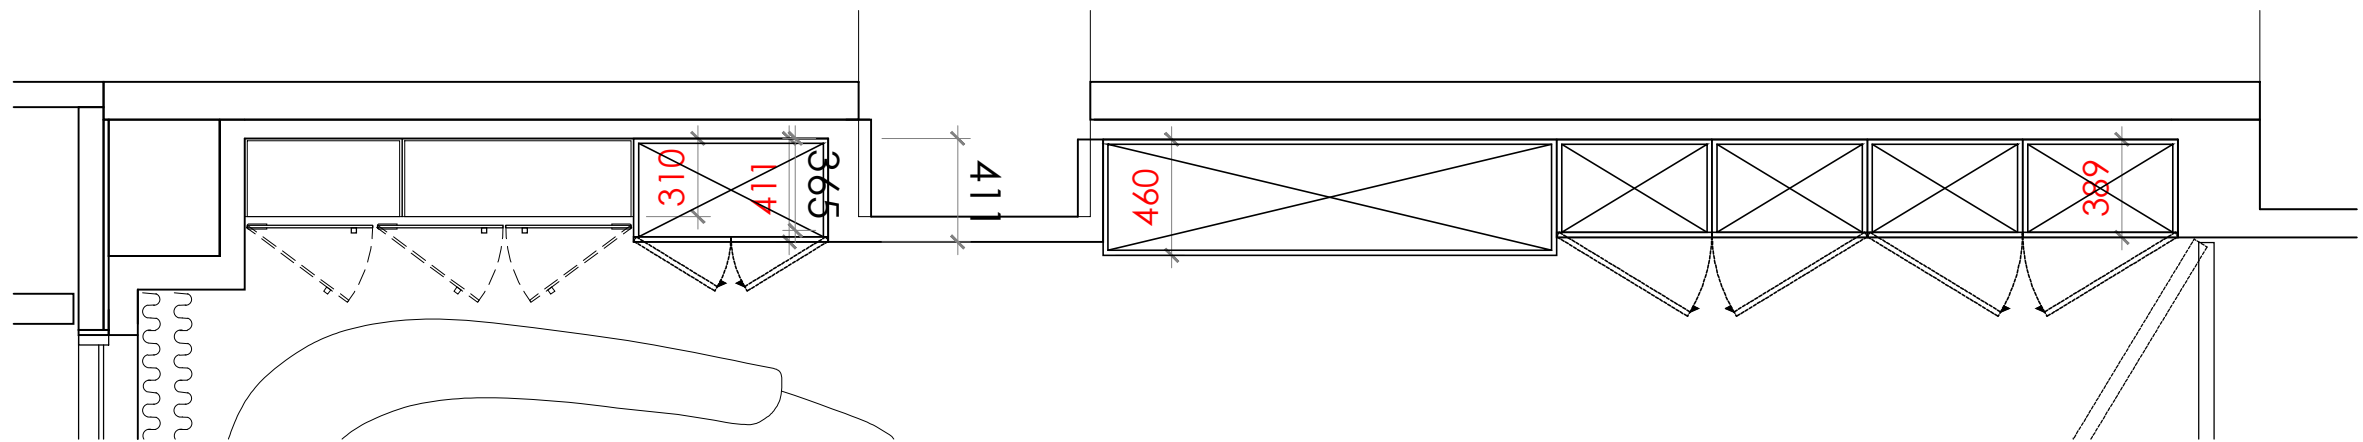

1
E-09

ELEVATION

Scale=1:30

Revision

APPROVAL/核准

設計者:	建築師:
業主:	

備註:

- 圖面標註尺寸僅供參考，施作均以現場放樣檢討之。
- 圖面標註尺寸、材料及文字敘述因版本不同之差異，均以出圖章簽認日期之最近為準。
- 電腦圖檔除由合約訂定外，均不得以任何方式外流。
- 圖面所示均為本公司所擁有之智慧財產，切勿以任何方式複製修改。



MULA DECO

▲ 3F, N.26, Ln.290, Guangfu S. Rd., Taipei.
☎ 886-2-2546-3258
☎ 886-2-2546-3257
✉ Guido@muladeco.com

Project / 案名

日本神宮案


Sheet Title / 圖名
507

立面圖

Date / 日期	Scale / 比例
3/25/2026	1/30cm
Designer / 設計	Approval / 核准
MONICA LIN	
Job No / 業務編號	Drawn By / 繪圖
00000	GUIDO
Dwg No.	Page No.

E-09

19

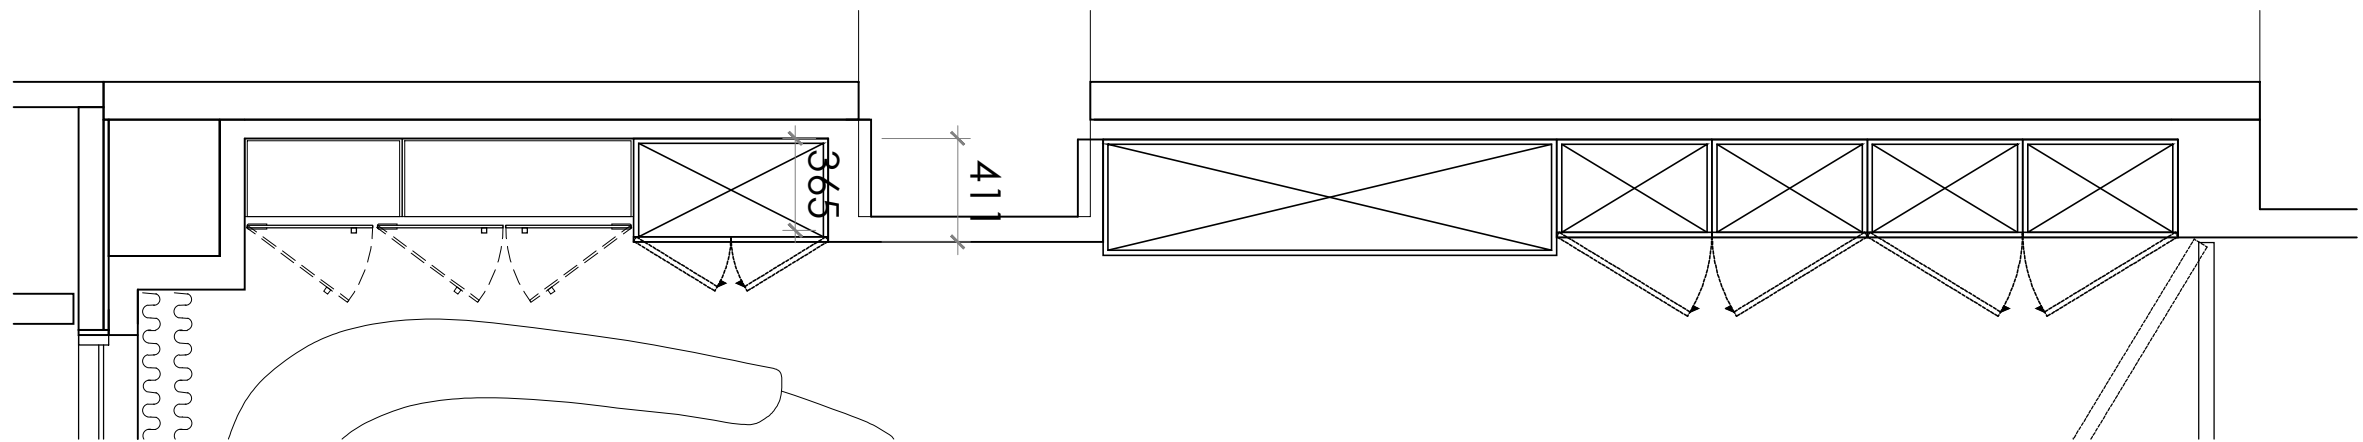

LED燈帶出線位置(燈帶台灣配置)
間接照明用 LEDテープライト (10×10mm、TRIAC調光対応)
配線引出口位置：電源線2本) 台灣製

WP 06

LED燈帶出線位置
間接照明用 LEDテープライト (アルミチャンネル
付：10×10mm、配線引出口位置：電源線1本)

LED燈帶出線位置 (兩條電源線)
間接照明用 LEDテープライト (10×10mm)
配線引出口位置：電源線2本)

LED變壓器設置位置。
変圧器は隠蔽設置とする

LED燈帶出線位置 (兩條電源線)
間接照明用 LEDテープライト
(10×10mm)
配線引出口位置：電源線2本)

A：安定器は、収納上部のオレンジ範囲に設置可能です。
当該部分の板材は可動式とする想定です。


A：安定器可設置於櫃體上方橘色區域，
該處板材將設計為可活動式。

△CH 2610mm

△CH 2308mm

▼FL ±0 mm

▲FL -50 mm

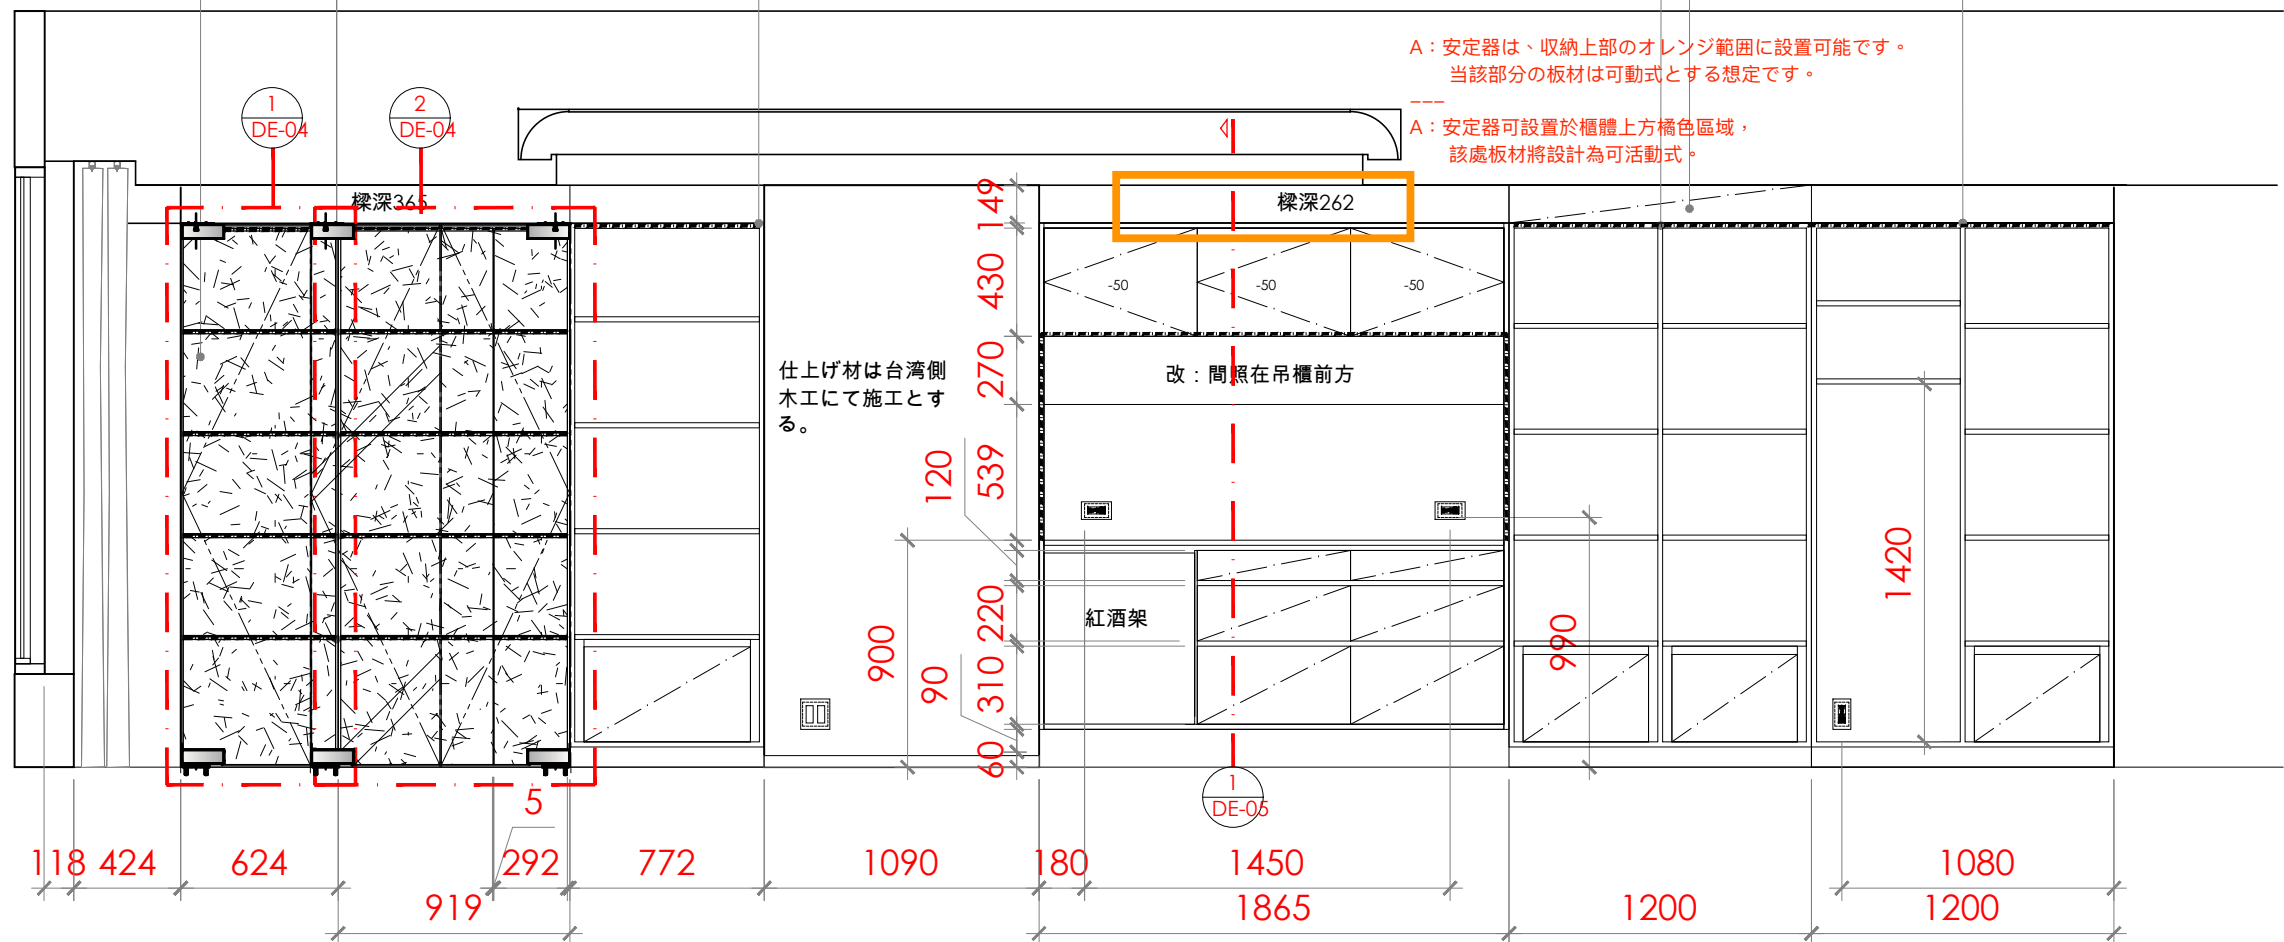

1
E-09

ELEVATION

Scale=1:30

Revision

APPROVAL/核准

設計者:	建築師:
業主:	

備註:

- 圖面標註尺寸僅供參考，施作均以現場放樣檢討之。
- 圖面標註尺寸、材料及文字敘述因版本不同之差異，均以出圖章簽認日期之最近為準。
- 電腦圖檔除由合約訂定外，均不得以何方式外流。
- 圖面所示均為本公司所擁有之智慧財產，切勿以任何方式複製修改。



MULA DECO

▲ 3F, N.26, Ln.290, Guangfu S. Rd., Taipei.
☎ 886-2-2546-3258
☎ 886-2-2546-3257
✉ Guido@mulatedeco.com

Project / 案名

日本神宮案


Sheet Title / 圖名
507

立面圖

Date / 日期	Scale / 比例
3/25/2026	1/30cm
Designer / 設計	Approval / 核准
MONICA LIN	
Job No / 業務編號	Drawn By / 繪圖
00000	GUIDO
Dwg No.	Page No.

E-09

19

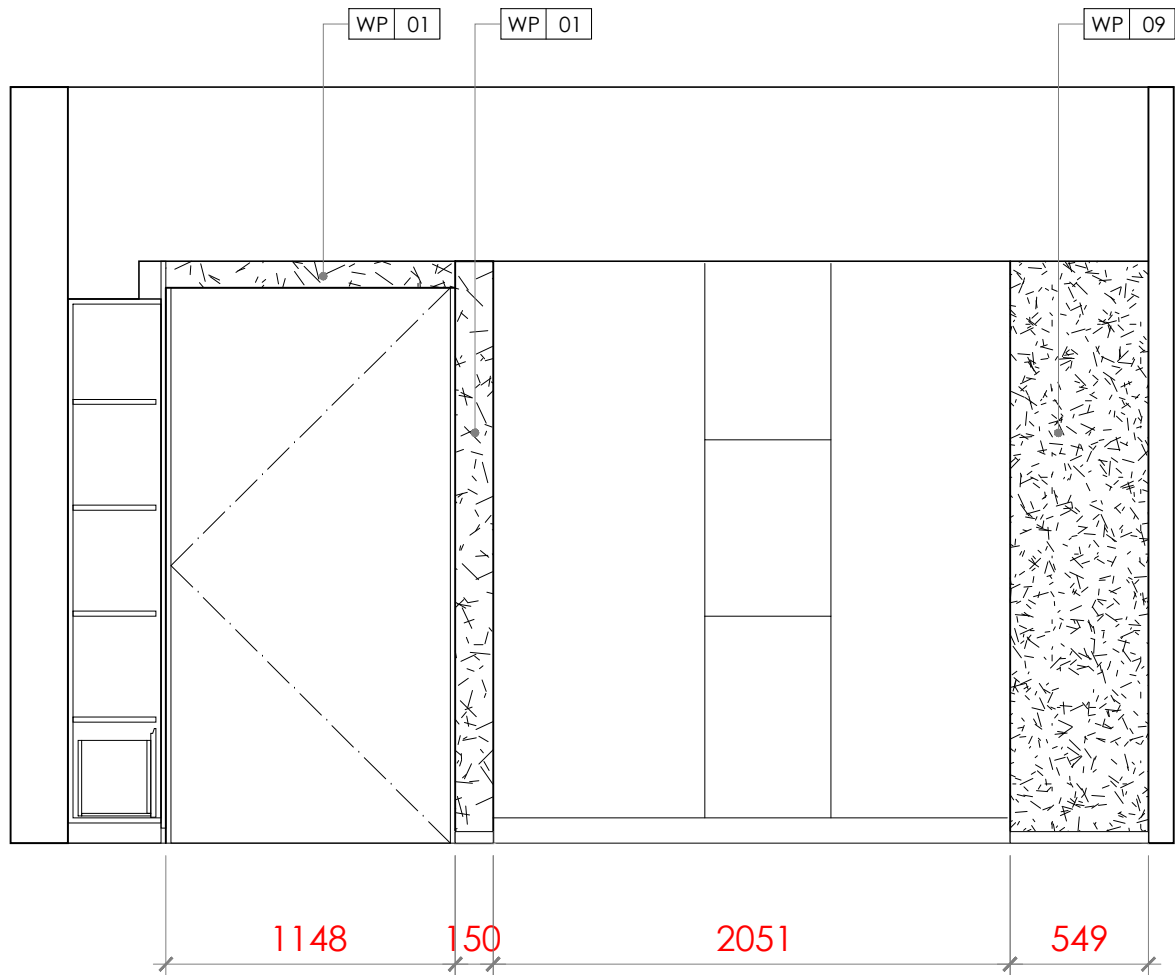

▼FL ±0 mm
▲FL -50 mm

[illegible]



MULA DECO
A 3F, N.26, Ln.290, Guangfu S. Rd., Taipei.
T 886-2-2546-3258
F 886-2-2546-3257
E Guido@mula deco.com

Project / 案名

Sheet Title / 圖名
507

立面圖

Date / 日期	Scale / 比例
3/25/2026	1/30cm
Designer / 設計	Approval / 核准
MONICA LIN	
Job No / 案卷編號	Drawn By / 繪圖
00000	GUIDO
Dwg No.	Page No.
E-10	20

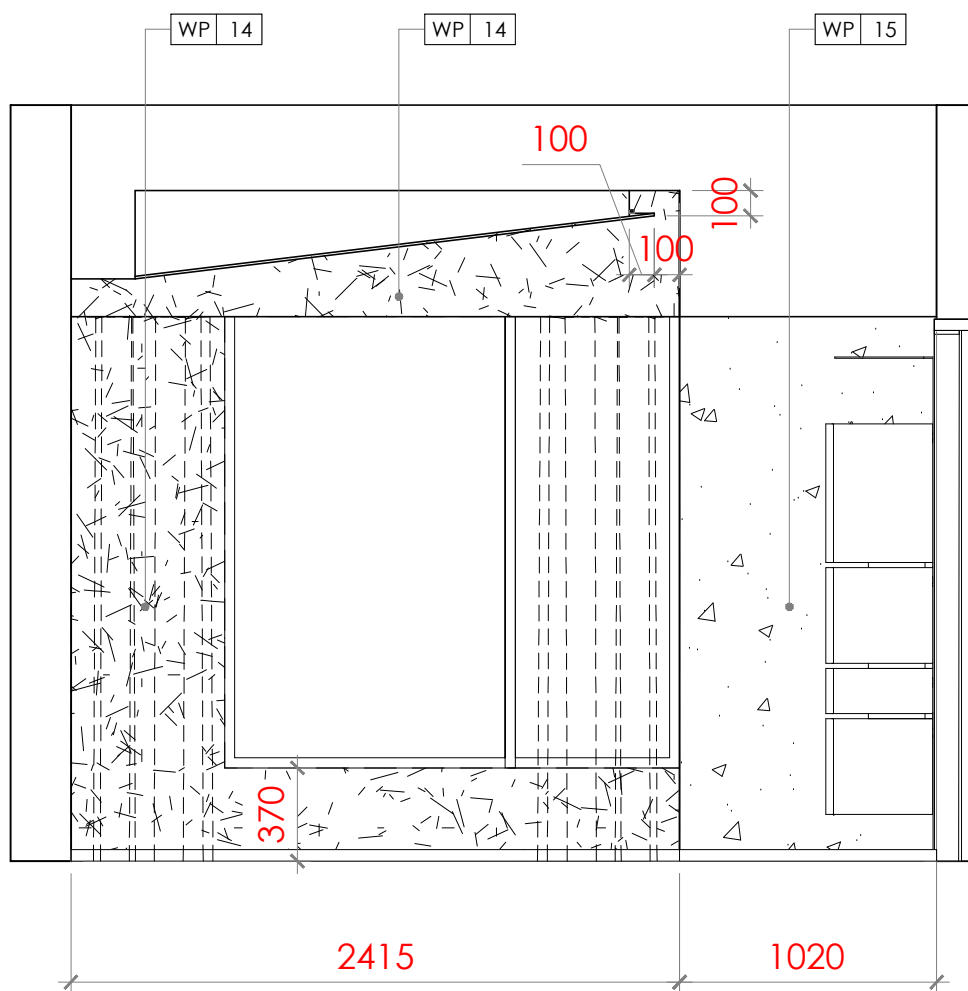

▼FL ±0 mm
▲FL -50 mm

[illegible]

Project / 案名


日本神宮案

Sheet Title / 圖名

507

立面圖

E-12 22

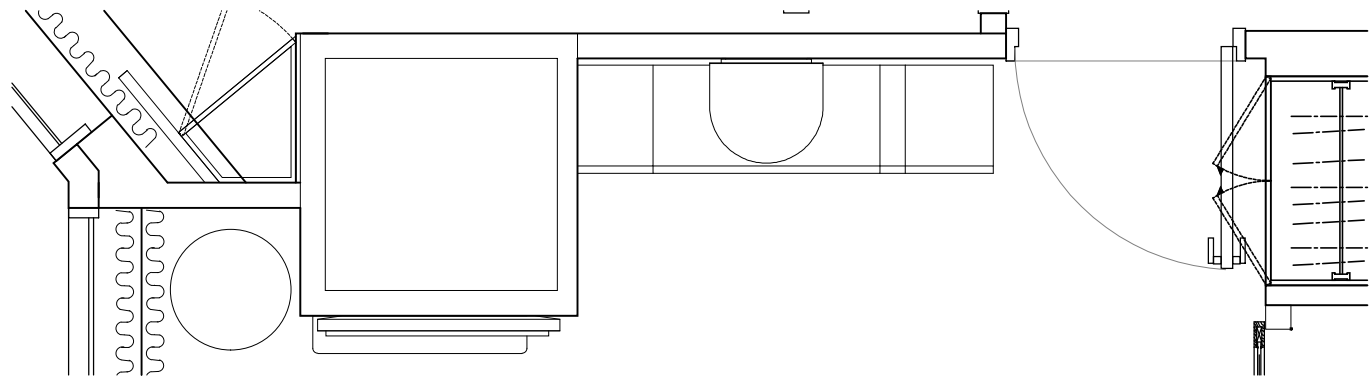

48V型 4K有機ELテレビ LG OLED evo AI C5
Size:1071 x 618 x 47 mm

手臂式壁掛架 MOUNTUP MU0062 43.5 x 26.6 x 3.3cm
アーム式壁掛け金具 - MOUNTUP MU0062 43.5 x 26.6 x 3.3cm

需有管道聯通至電視後方，以配置線路。
テレビ背面まで配管を通し、配線を確保すること。

テレビ壁掛（可動式）

耐荷重を考慮し、テレビ壁掛取付のため、
壁内構造補強
吊戸棚取付のため、
壁内構造補強

置き家具（転倒防止のため、壁面固定）
必要に応じて
壁内下地補強

WP 14

WP 14

WP 14

WP 14

WP 15


△CH 2660mm

△CH 2310mm

△CH 2160mm

▼FL ±0 mm

▲FL -50 mm

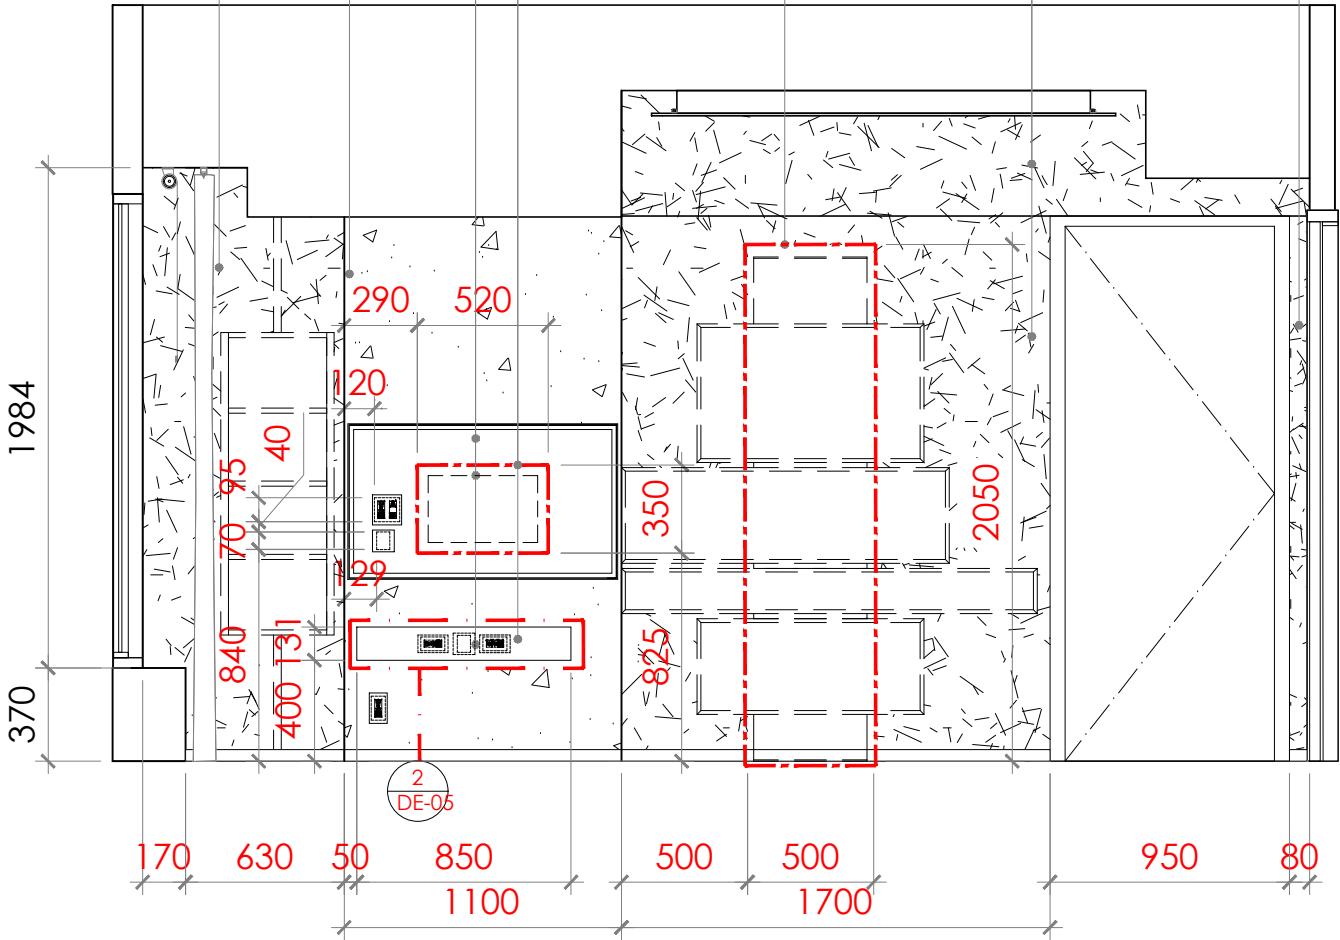

1
E-13

ELEVATION

Scale=1:30

Revision

APPROVAL/核准

設計者:	建築師:
業主:	

備註:

- 圖面標註尺寸僅供參考，施作均以現場放樣檢討之。
- 圖面標註尺寸、材料及文字敘述因版本不同之差異，均以出圖章簽認日期之最近為準。
- 電腦圖檔除由合約訂定外，均不得以任何方式外流。
- 圖面所示均為本公司所擁有之智慧財產，切勿以任何方式複製修改。



MULA DECO

▲ 3F, N.26, Ln.290, Guangfu S. Rd., Taipei.
☎ 886-2-2546-3258
☎ 886-2-2546-3257
✉ Guido@muladeco.com

Project / 案名

日本神宮案


Sheet Title / 圖名
507

立面圖

Date / 日期	Scale / 比例
3/25/2026	1/30cm
Designer / 設計	Approval / 核准
MONICA LIN	
Job No / 業務編號	Drawn By / 繪圖
00000	GUIDO
Dwg No.	Page No.

E-13

23

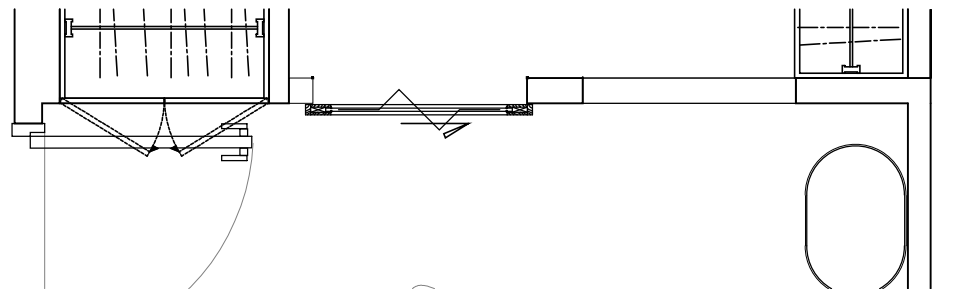


△CH 2660mm

△CH 2310mm


△CH 2160mm

▼FL ±0 mm

▲FL -50 mm

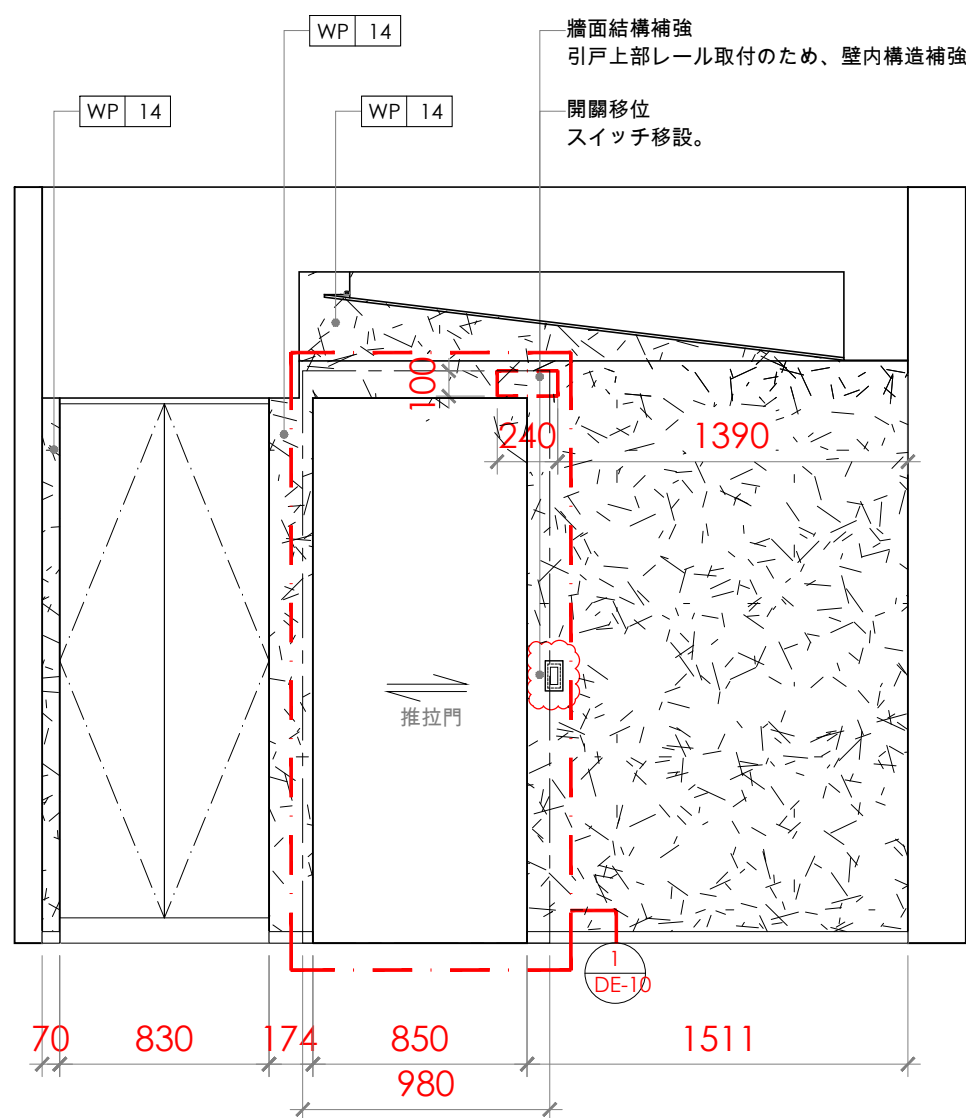

1 ELEVATION Scale=1:30

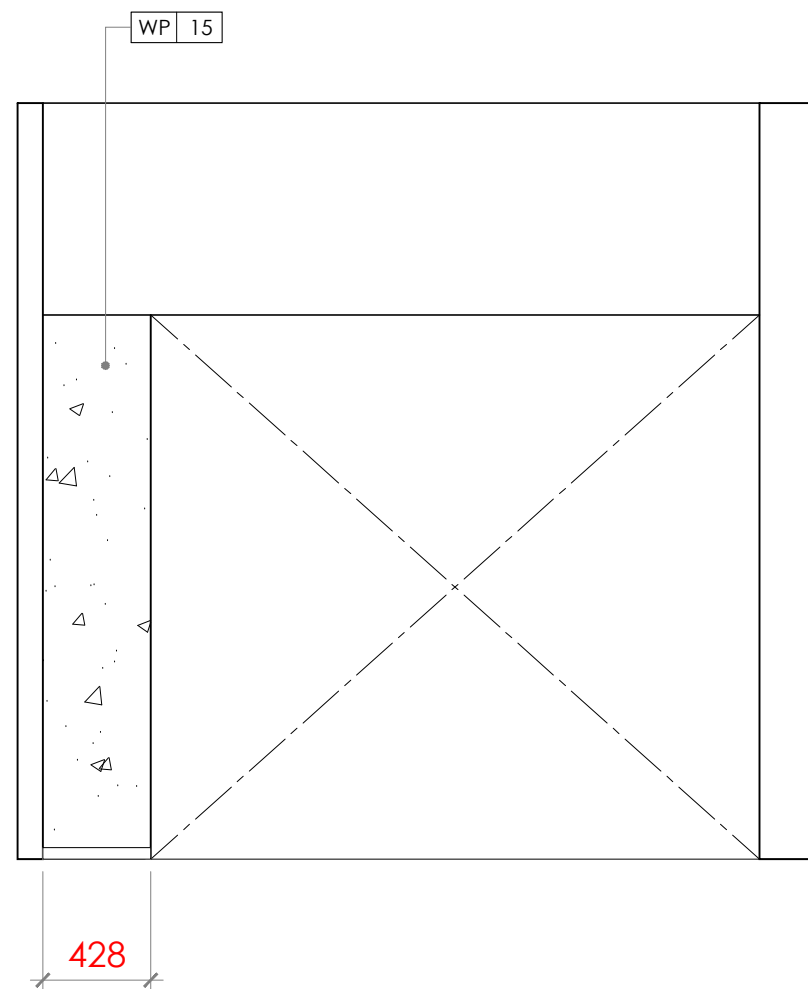

2 ELEVATION Scale=1:30

Revision

APPROVAL/核准

設計者:	建築師:
業主:	

備註:

- 圖面標註尺寸僅供參考，施作均以現場放樣檢討之。
- 圖面標註尺寸、材料及文字敘述因版本不同之差異，均以圖章簽認日期之最近為準。
- 電腦圖檔除由合約訂定外，均不得以任何方式外流。
- 圖面所示均為本公司所擁有之智慧財產，切勿以任何方式複製修改。



MULA DECO

▲ 3F, N.26, Ln.290, Guangfu S. Rd., Taipei.
☎ 886-2-2546-3258
☎ 886-2-2546-3257
✉ Guido@muladeco.com

Project / 案名

日本神宮案


Sheet Title / 圖名
507

立面圖

Date / 日期	Scale / 比例
3/25/2026	1/30cm
Designer / 設計	Approval / 核准
MONICA LIN	
Job No / 業務編號	Drawn By / 繪圖
00000	GUIDO
Dwg No.	Page No.

E-14

24


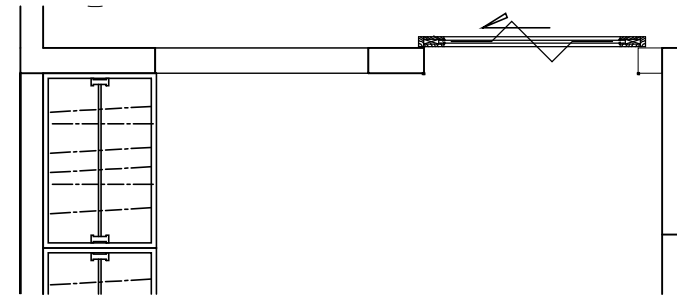


コーナ一用 3mm 見切り材

WP	13
----	----

Scale=1:30

25

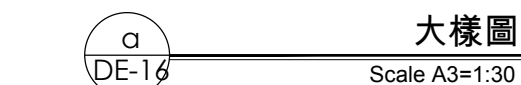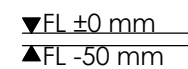

Scale=1:30

APPROVAL/核准	
設計者:	建築師:
業主:	

備註:

- a. 圖面標註尺寸僅供參考，施作均以現場放樣檢討之。
- b. 圖面標註尺寸、材料及文字敘述因版本不同之差異，均以出圖章簽認日期之最近為準。
- c. 電腦圖檔除由合約訂定外，均不得以任何方式外流。
- d. 圖面所示均為本公司所擁有之智慧財產，切勿以任何方式複製修改。




Project / 案名

日本神宮案

Sheet Title / 圖名
507

立面圖


E-16 26

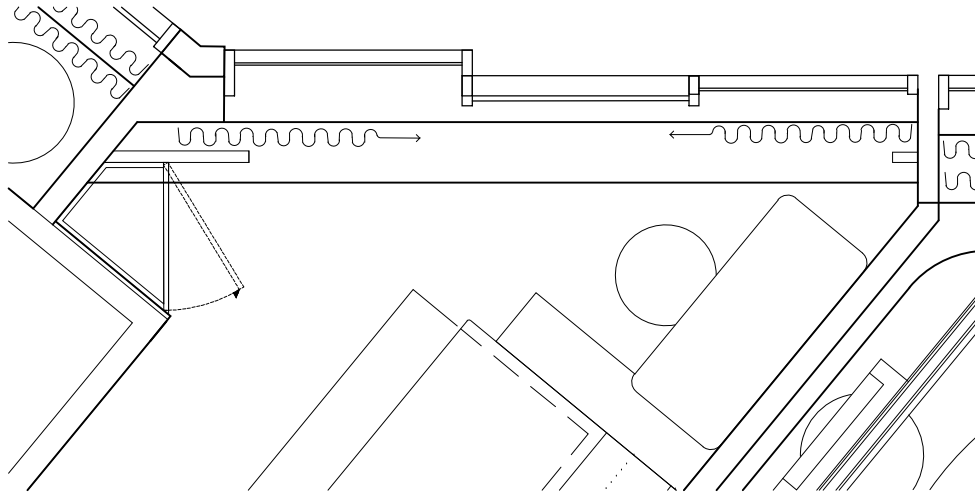

△CH 2614mm

△CH 2312mm

▼FL ±0 mm
▲FL -50 mm

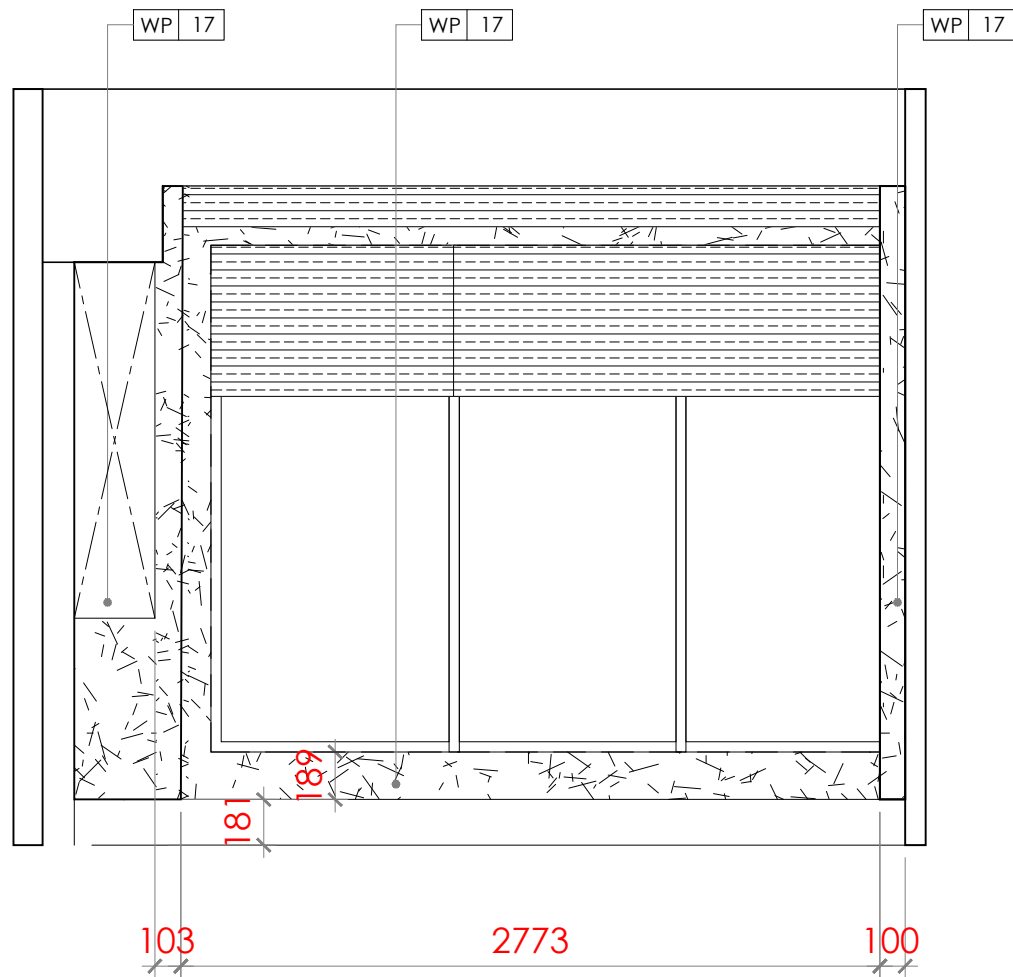

1
E-17

ELEVATION

Scale=1:30

Revision

APPROVAL/核准

設計者:	建築師:
業主:	

備註:

- 圖面標註尺寸僅供參考，施作均以現場放樣檢討之。
- 圖面標註尺寸、材料及文字敘述因版本不同之差異，均以出圖章簽認日期之最近為準。
- 電腦圖檔除由合約訂定外，均不得以任何方式外流。
- 圖面所示均為本公司所擁有之智慧財產，切勿以任何方式複製修改。



MULA DECO

▲ 3F, N.26, Ln.290, Guangfu S. Rd., Taipei.
☎ 886-2-2546-3258
☎ 886-2-2546-3257
✉ Guido@muladeco.com

Project / 案名

日本神宮案



Sheet Title / 圖名
507

立面圖

Date / 日期	Scale / 比例
3/25/2026	1/30cm
Designer / 設計	Approval / 核准
MONICA LIN	
Job No / 業務編號	Drawn By / 繪圖
00000	GUIDO
Dwg No.	Page No.

E-17

27

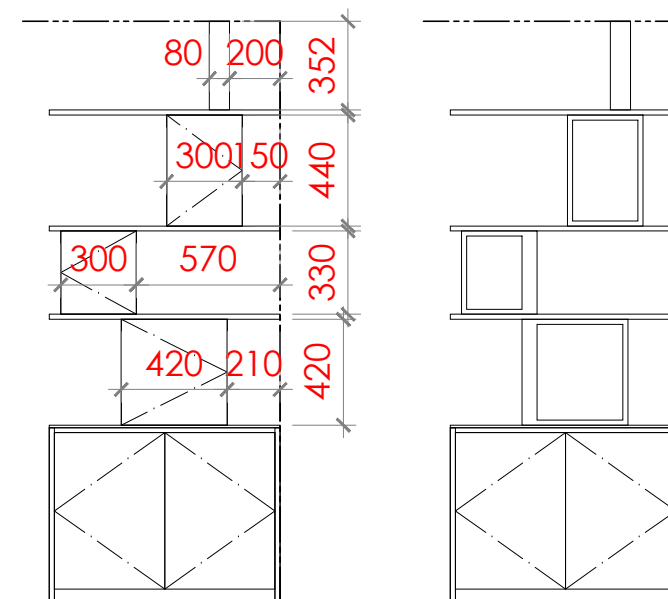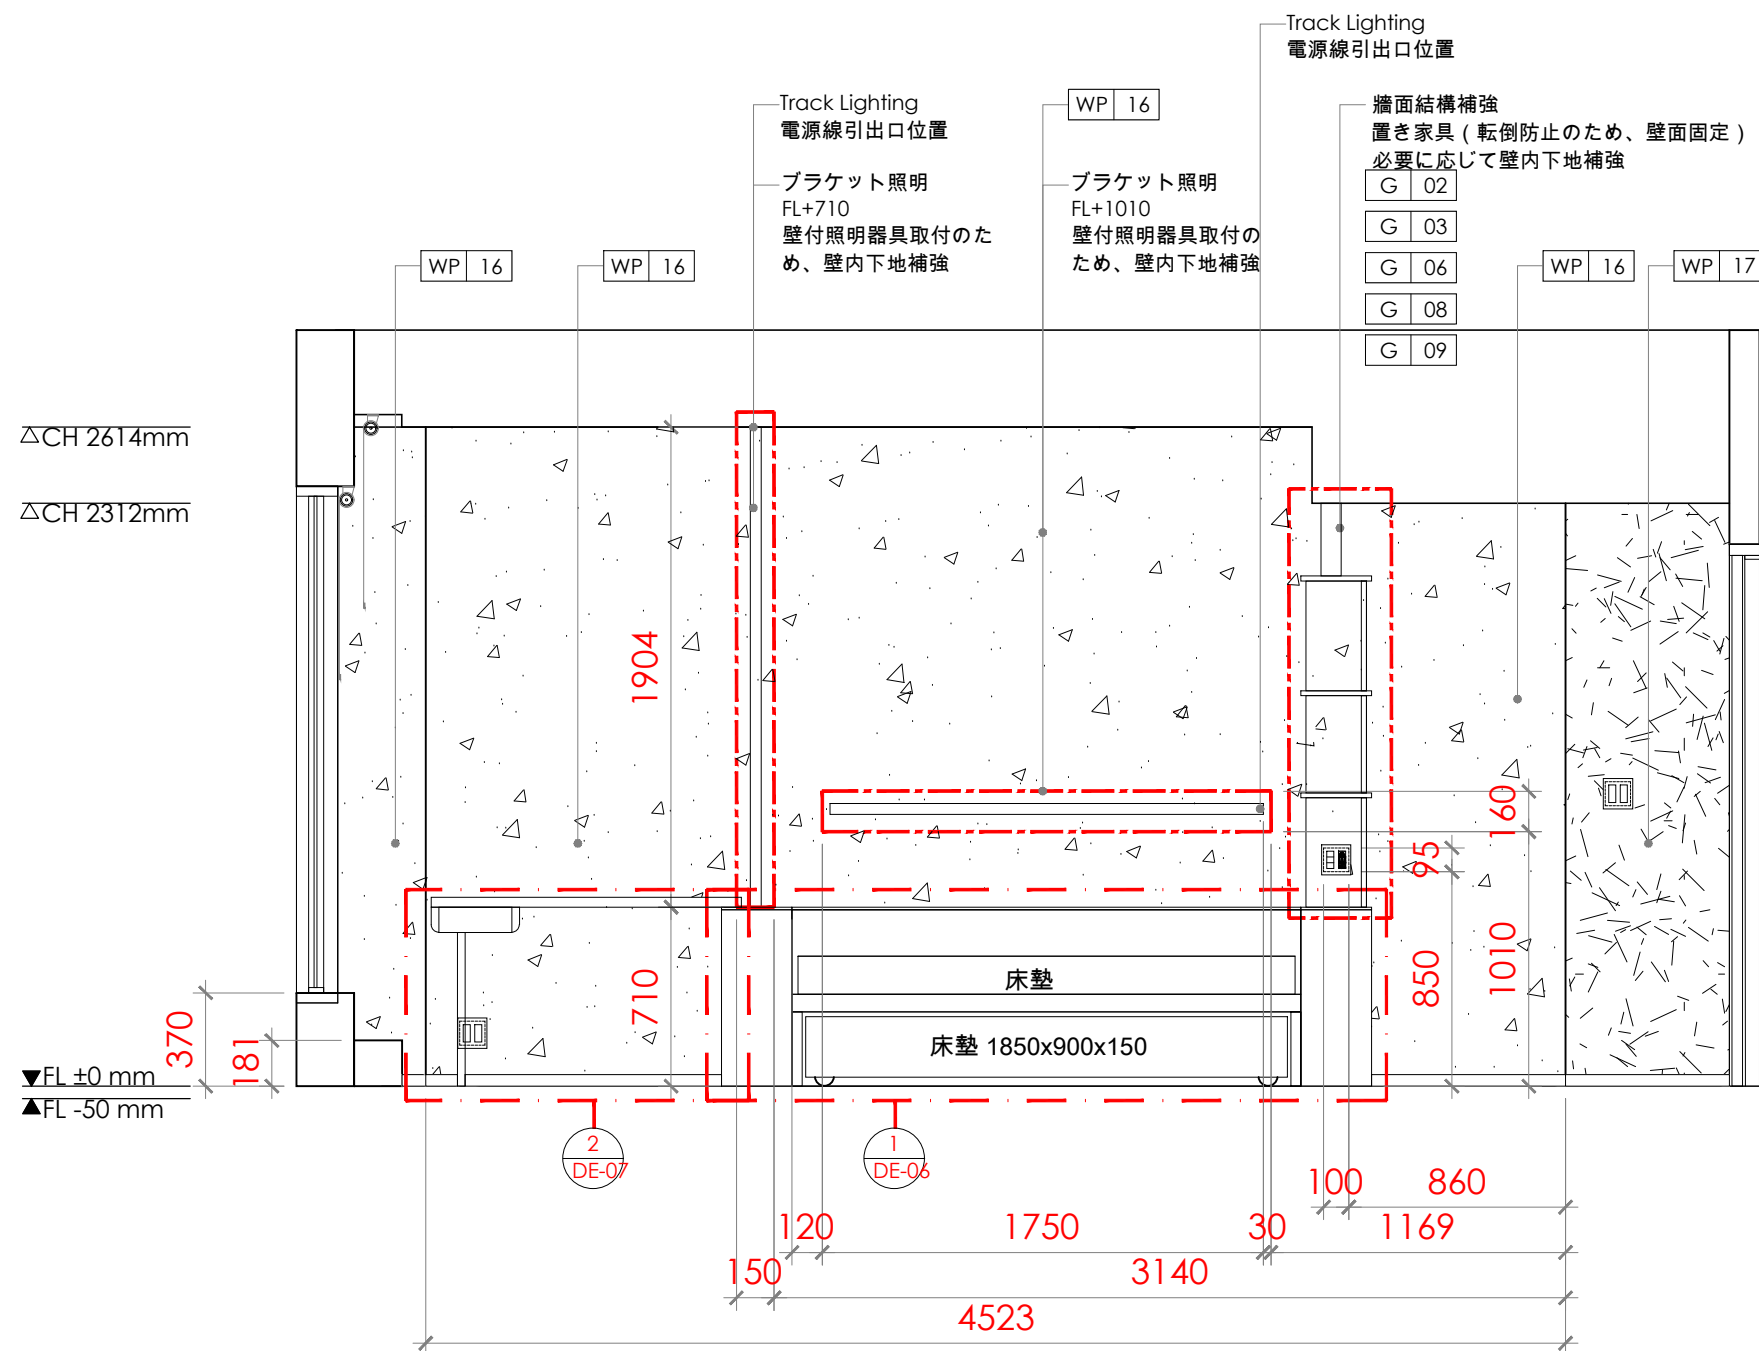

1 ELEVATION
E-18 Scale=1:30

Revision

APPROVAL/核准

設計者:	建築師:
業主:	

備註:

- a. 圖面標註尺寸僅供參考，施作均以現場放樣檢討之。
- b. 圖面標註尺寸、材料及文字敘述因版本不同之差異，均以圖章簽認日期之最近為準。
- c. 電腦圖檔除由合約訂定外，均不得以任何方式外流。
- d. 圖面所示均為本公司所擁有之智慧財產，切勿以任何方式複製修改。



MULA DECO

A 3F, N.26, Ln.290, Guangfu S. Rd., Taipei.
T 886-2-2546-3258
F 886-2-2546-3257
E Guido@muladeco.com

Project / 案名

日本神宮案



Sheet Title / 圖名
507

立面圖

Date / 日期	Scale / 比例
3/25/2026	1/30cm
Designer / 設計	Approval / 核准
MONICA LIN	
Job No / 業務編號	Drawn By / 繪圖
00000	GUIDO
Dwn No	Page No

E-18

28

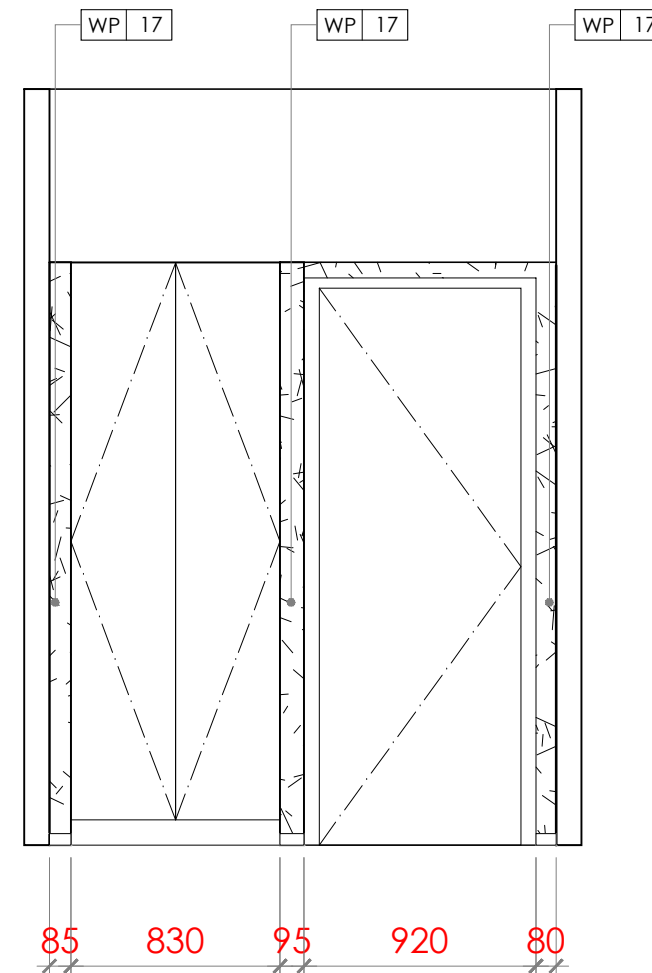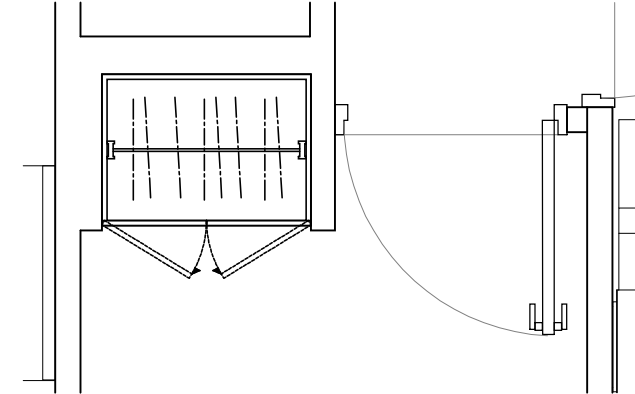

2 ELEVATION
E-19 Scale=1:30

Revision

設計者:	建築師:
業主:	

備註:





- ①.圖面標註尺寸僅供參考，施作均以現場放樣檢討之。
- ②.圖面標註尺寸、材料及文字敘述因版本不同之差異，均以出圖章簽認日期之最近為準。
- ③.電腦圖檔除由合約訂定外，均不得以任何方式外流。
- ④.圖面所有均為本公司所擁有之智慧財產，切勿以任何方式複製修改。



日本神宮案

立面圖

Date / 日期	Scale / 比例
3/25/2026	1/30cm
Designer / 設計	Approval / 核准
MONICA LIN	
Job No / 業務編號	Drawn By / 繪圖
00000	GUIDO
Dwg No.	Page No.
E-19	29

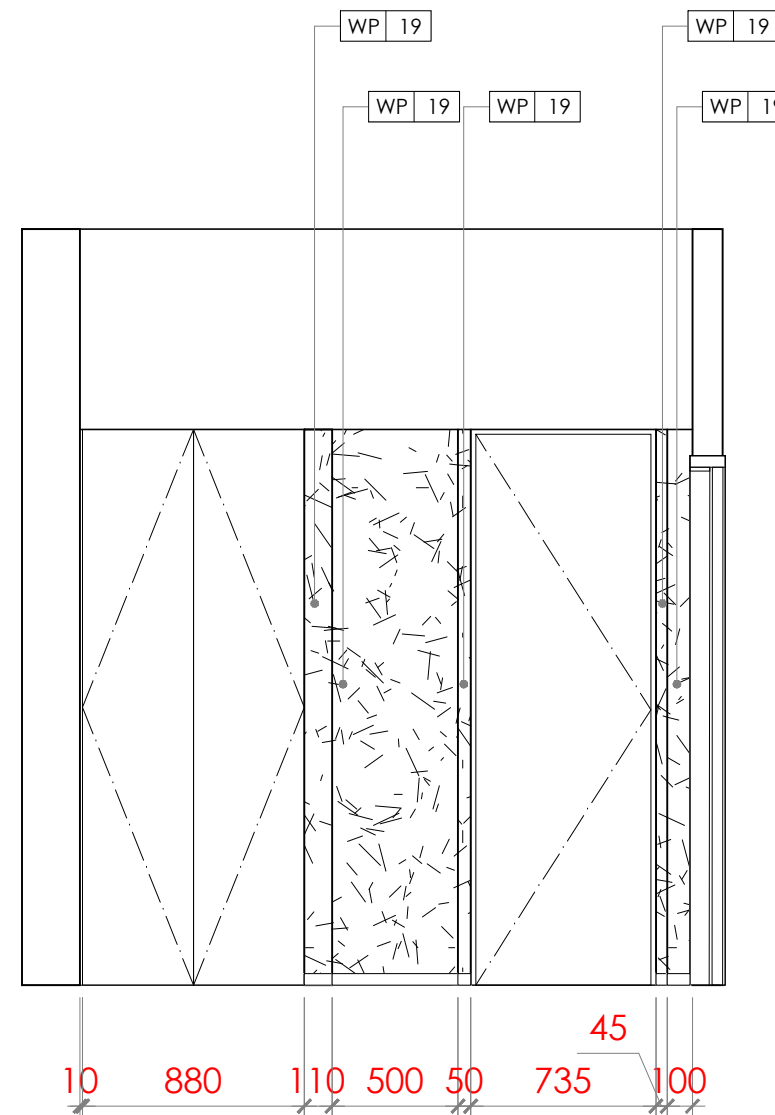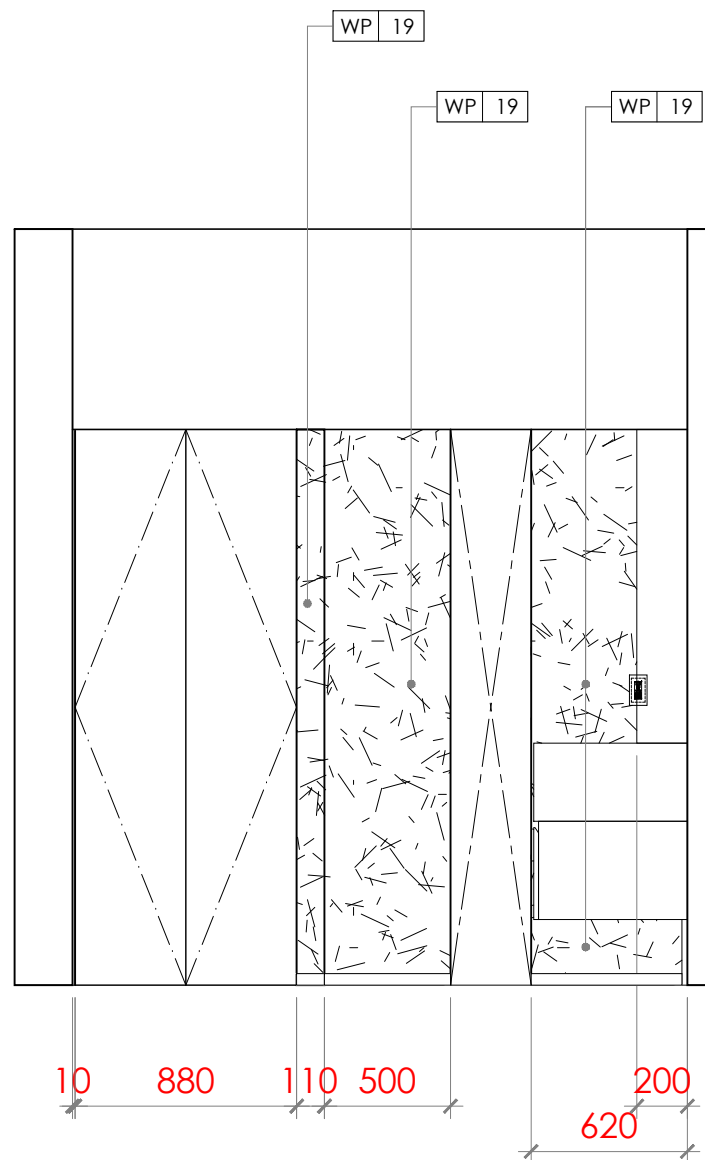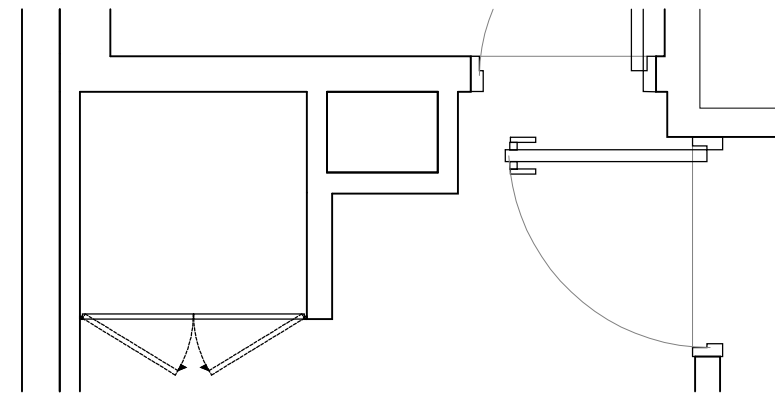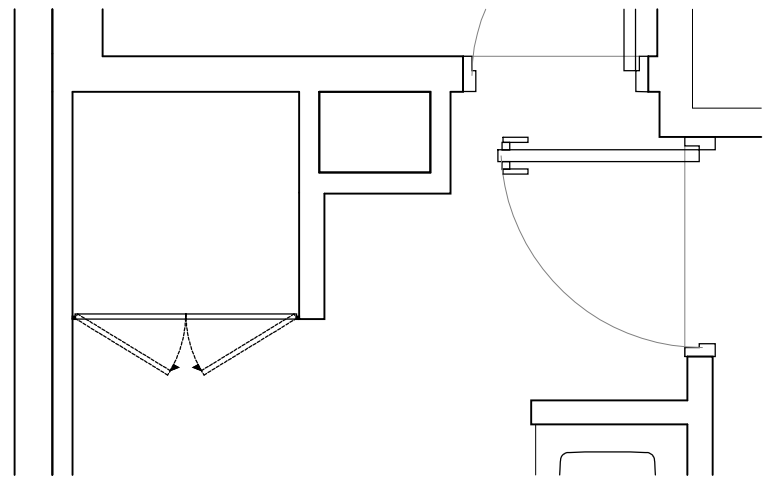

△CH 2205mm

▼FL ±0 mm
▲FL -50 mm

1 ELEVATION
E-20
Scale=1:30

2 ELEVATION
E-20
Scale=1:30

Revision

APPROVAL/核准	
設計者:	建築師:
業主:	

備註:

a. 圖面標註尺寸僅供參考，施作均以現場放樣檢討之。

b. 圖面標註尺寸、材料及文字敘述因版本不同之差異，均以出圖章簽認日期之最近為準。

c. 電腦圖檔除由合約訂定外，均不得以任何方式外流。

d. 圖面所示均為本公司所擁有之智慧財產，切勿以任何方式複製修改。

M

MULA DECO

▲ 3F, N.26, Ln.290, Guangfu S. Rd., Taipei.
☎ 886-2-2546-3258
✉ 886-2-2546-3257
E Guido@muladeco.com

Project / 案名



日本神宮案

Sheet Title / 圖名

507


立面圖

Date / 日期	Scale / 比例
3/25/2026	1/30cm
Designer / 設計	Approval / 核准
MONICA LIN	
Job No / 業務編號	Drawn By / 繪圖
00000	GUIDO
Dwg No.	Page No.
E-20	30

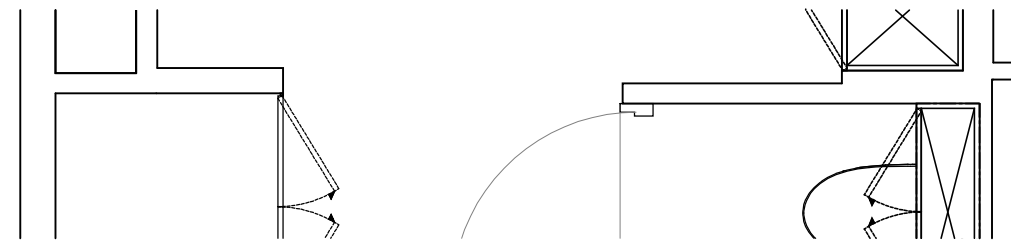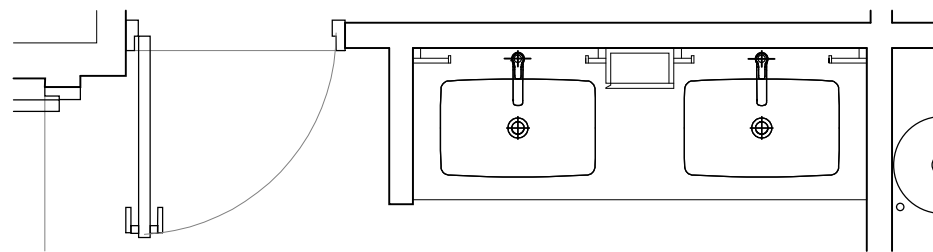


△CH 2205mm

▼FL ±0 mm
▲FL -50 mm

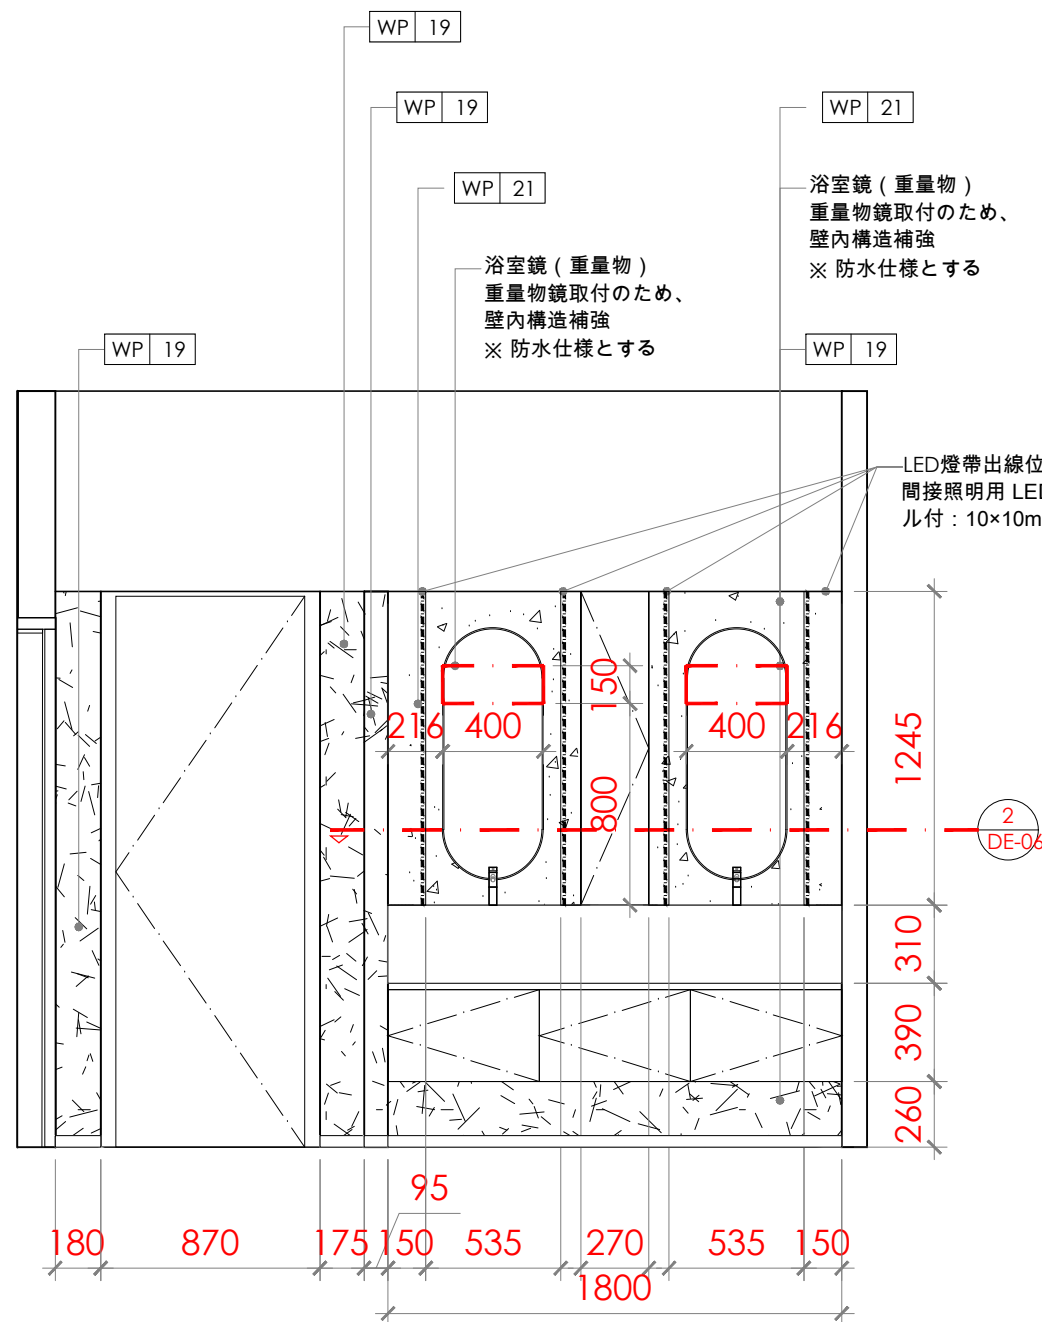

1 E-21 ELEVATION Scale=1:30

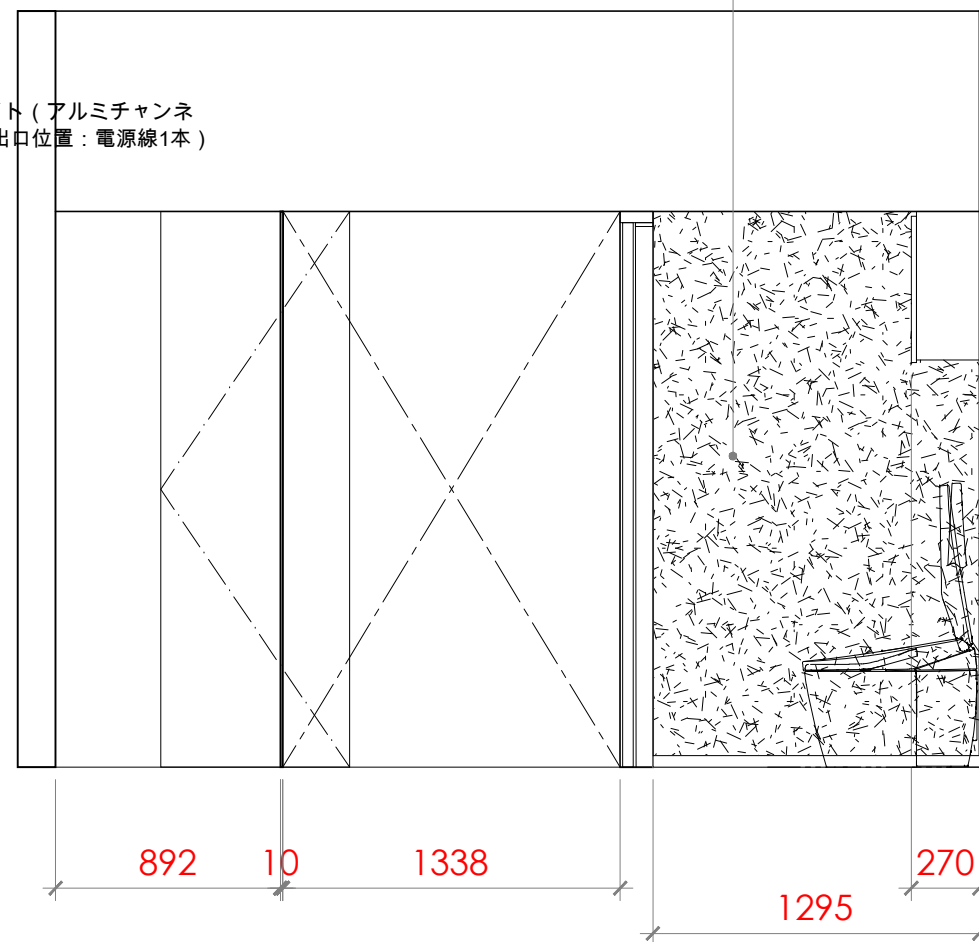

2 E-21 ELEVATION Scale=1:30

Revision

APPROVAL/核准

設計者:	建築師:
業主:	

備註:

- 圖面標註尺寸僅供參考，施作均以現場放樣檢討之。
- 圖面標註尺寸、材料及文字敘述因版本不同之差異，均以出圖章簽認日期之最近為準。
- 電腦圖檔除由合約訂定外，均不得以何方式外流。
- 圖面所示均為本公司所擁有之智慧財產，切勿以任何方式複製修改。



MULA DECO

▲ 3F, N.26, Ln.290, Guangfu S. Rd., Taipei.
☎ 886-2-2546-3258
☎ 886-2-2546-3257
✉ Guido@mulatedeco.com

Project / 案名

日本神宮案



Sheet Title / 圖名
507

立面圖

Date / 日期	Scale / 比例
3/25/2026	1/30cm
Designer / 設計	Approval / 核准
MONICA LIN	
Job No / 業務編號	Drawn By / 繪圖
00000	GUIDO
Dwg No.	Page No.

E-21

31

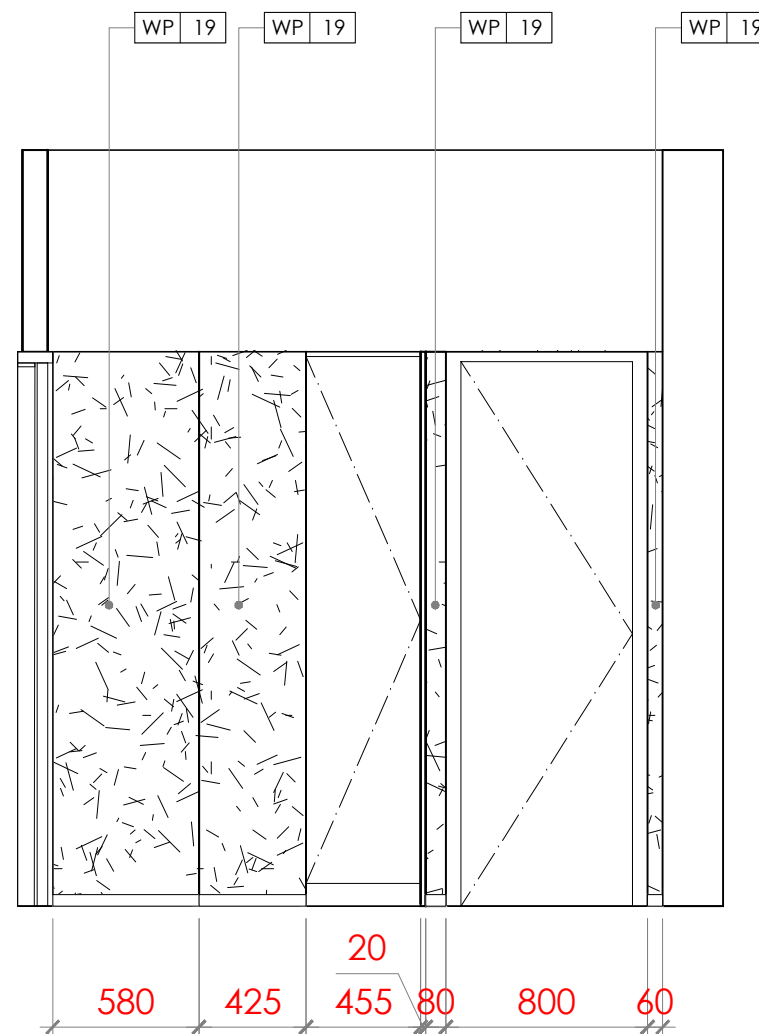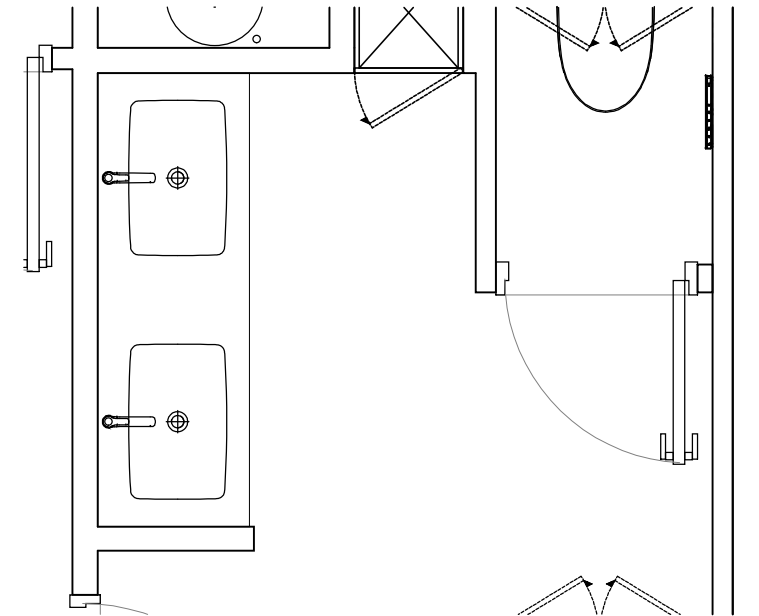

Scale=1:30

Scale=1:30

[illegible]

設計者:	建築師:
業主:	

- g. 圖面標註尺寸僅供參考，施作均以現場放樣檢討之。
- h. 圖面標註尺寸、材料及文字敘述因版本不同之差異，均以出圖章簽認日期之最近為準。
- i. 電腦圖檔除由合約訂定外，均不得以任何方式外流。
- j. 圖面所示均為本公司所擁有之智慧財產，切勿以任何方式複製修改。






日本神宮案

立面圖

Date / 日期	Scale / 比例
3/25/2026	1/30cm
Designer / 設計	Approval / 核准
MONICA LIN	
Job No / 業務編號	Drawn By / 繪圖
00000	GUIDO
Dwg No.	Page No.

32

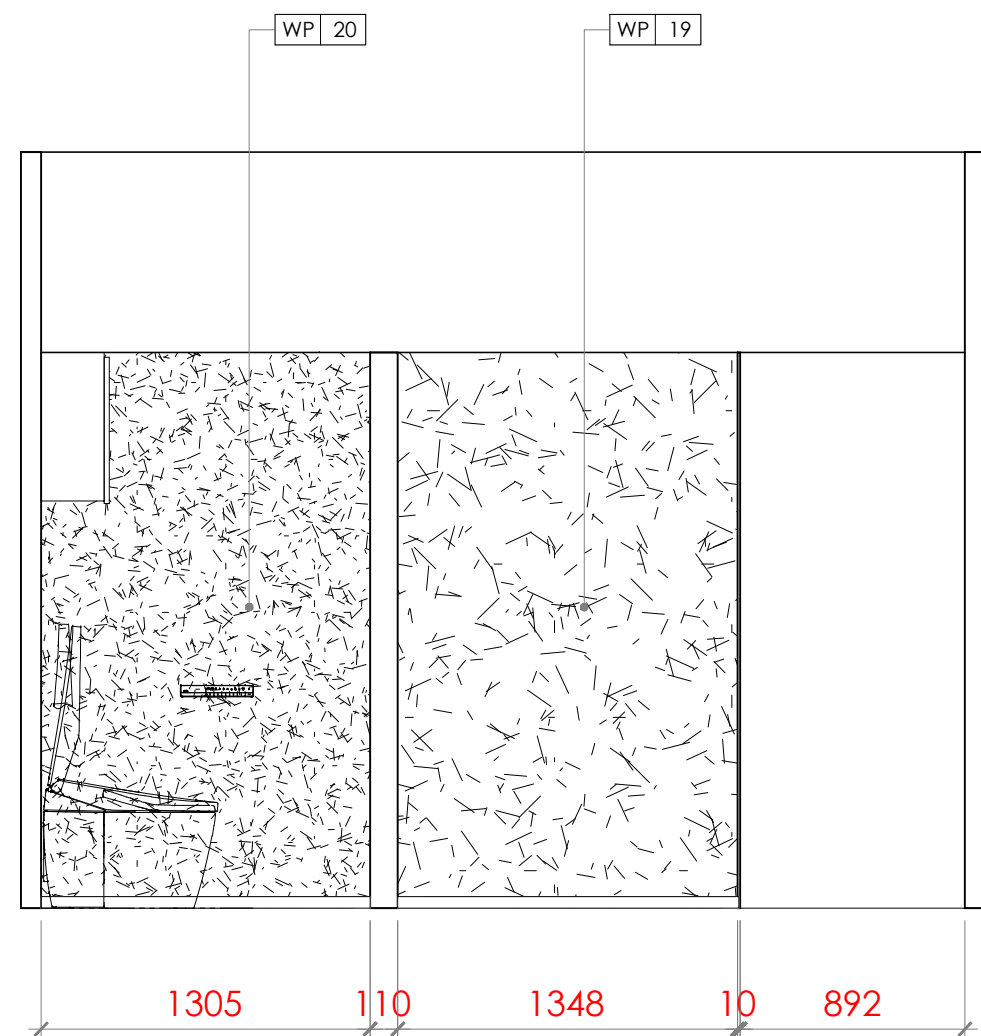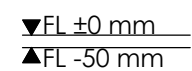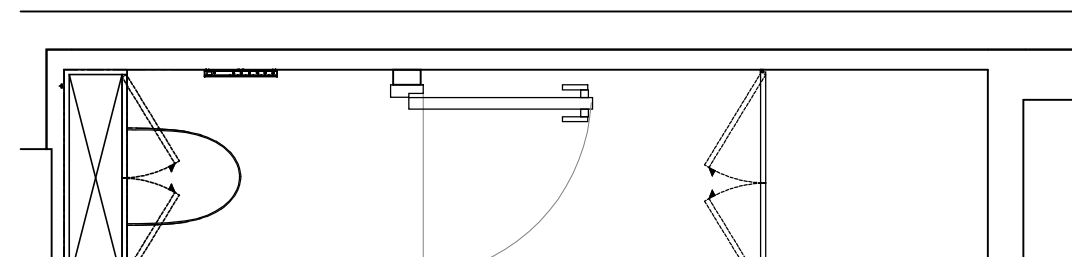

2 ELEVATION
E-23 Scale=1:30

[illegible]

設計者:	建築師:
業主:	

- a. 圖面標註尺寸僅供參考，施作均以現場放樣檢討之。
- b. 圖面標註尺寸、材料及文字敘述因版本不同之差異，均以出圖章簽認日期之最近為準。
- c. 電腦圖檔除由合約訂定外，均不得以任何方式外流。
- d. 圖面所示均為本公司所擁有之智慧財產，切勿以任何方式複製修改。



A 3F, N.26, Ln.290, Guangfu S. Rd., Taipei.
T 886-2-2546-3258
F 886-2-2546-3257
E Guido@muladeco.com

Project / 案名

日本神宮案


Sheet Title / 圖名
507

立面圖


Date / 日期	Scale / 比例
3/25/2026	1/30cm
Designer / 設計	Approval / 核准
MONICA LIN	
Job No / 案卷編號	Drawn By / 繪圖
00000	GUIDO
Dwg No.	Page No.
E-23	33

E-23


33

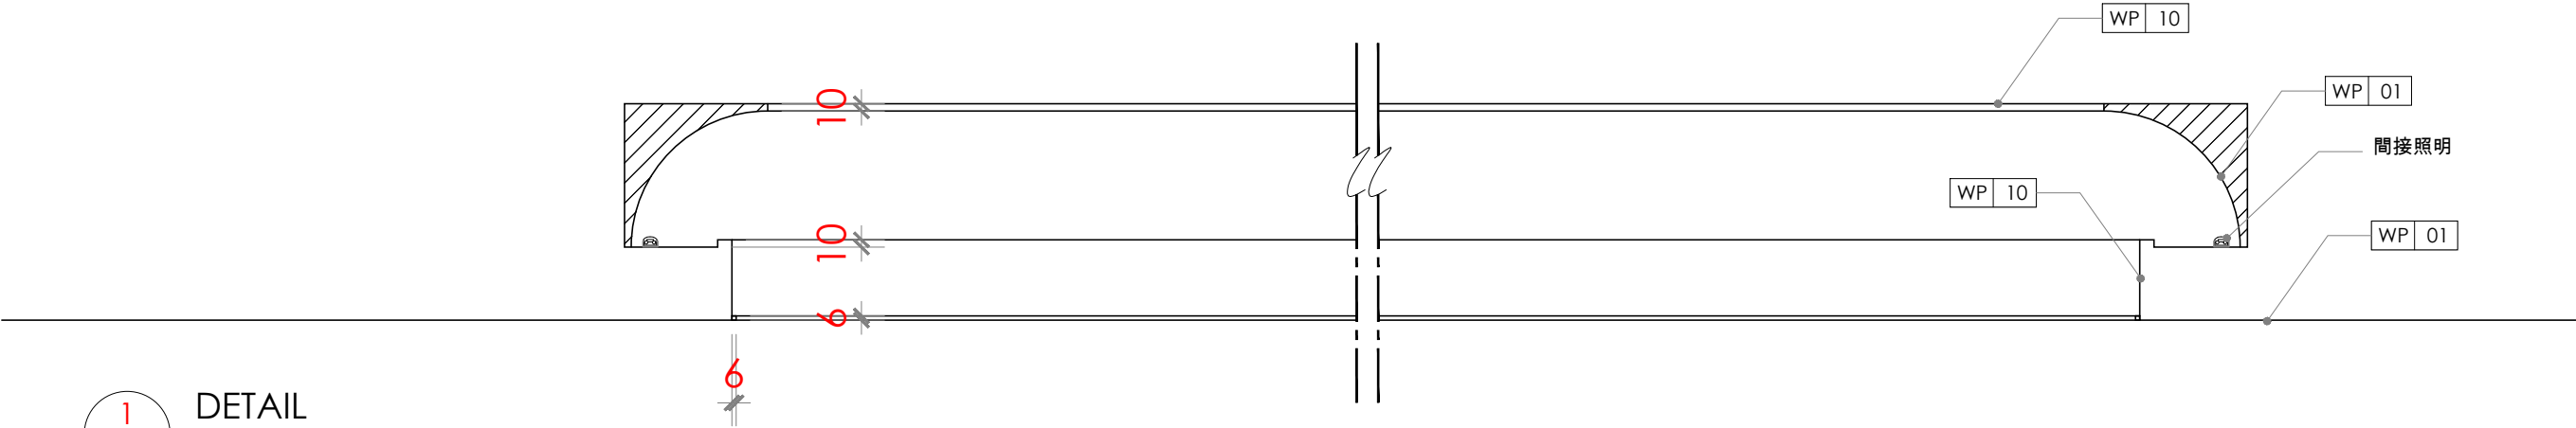

1
DETAIL
DE-01
S 1:10

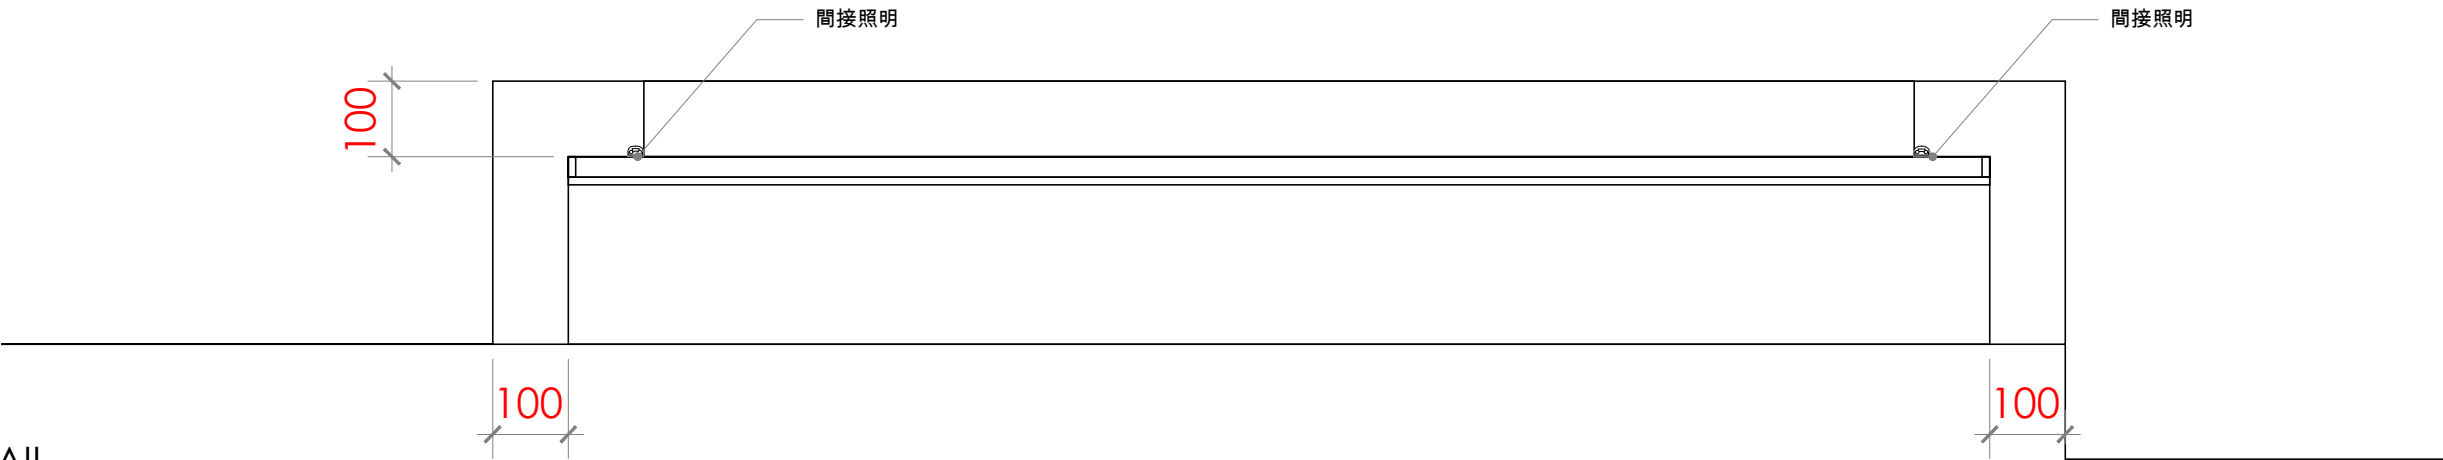

2
DETAIL
DE-01
S 1:10

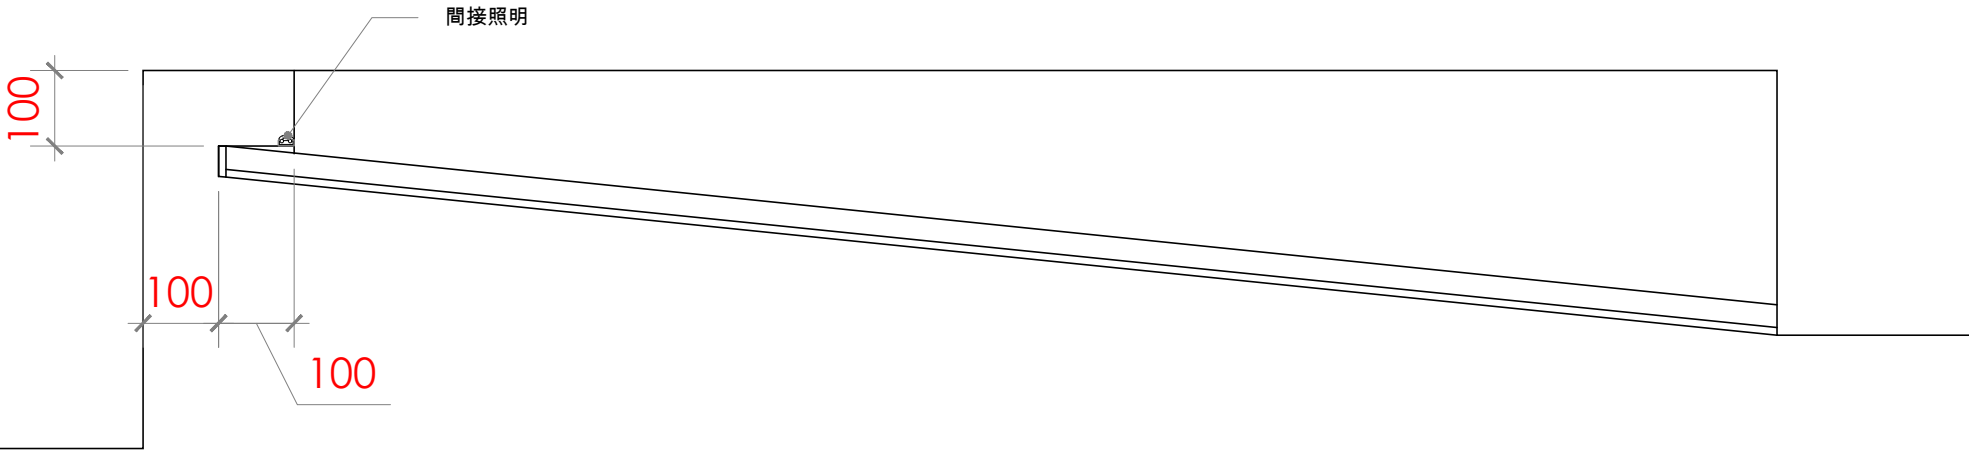

3
DETAIL
DE-01
S 1:10

Revision

APPROVAL/核准	
設計者:	建築師:
業主:	

備註:
a. 圖面標註尺寸僅供參考，施作均以現場放樣檢討之。
b. 圖面標註尺寸、材料及文字敘述因版本不同之差異，均以出圖章簽認日期之最近為準。
c. 電腦圖檔除由合約訂定外，均不得以任何方式外流。
d. 圖面所示均為本公司所擁有之智慧財產，切勿以任何方式複製修改。


MULA DECO
A 3F, N.26, Ln.290, Guangfu S. Rd., Taipei.
T 886-2-2546-3258
F 886-2-2546-3257
E Guido@muladeco.com





Project / 案名





日本神宮案

Sheet Title / 圖名
507

大樣圖

Date / 日期	Scale / 比例
3/25/2026	1/10cm
Designer / 設計	Approval / 核准
MONICA LIN	
Job No / 業務編號	Drawn By / 繪圖
00000	GUIDO
Dwg No.	Page No.
DE-01	34

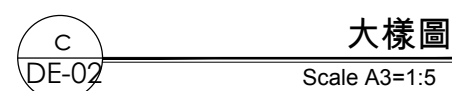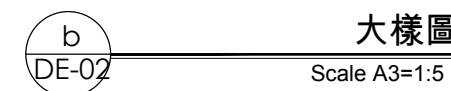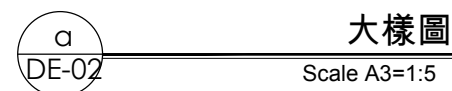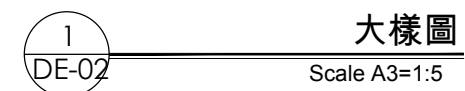

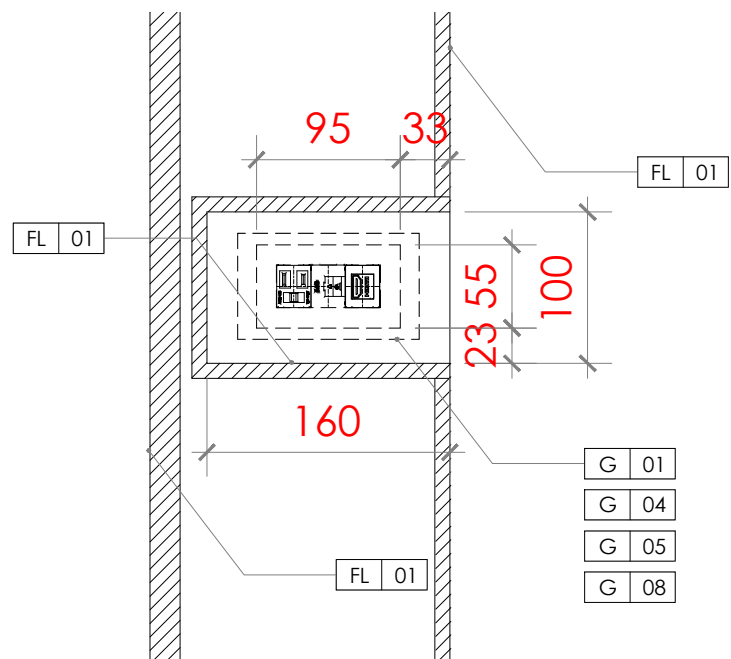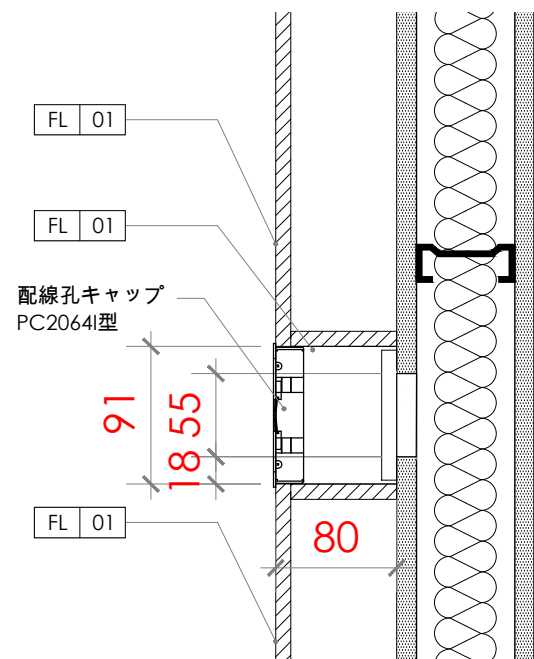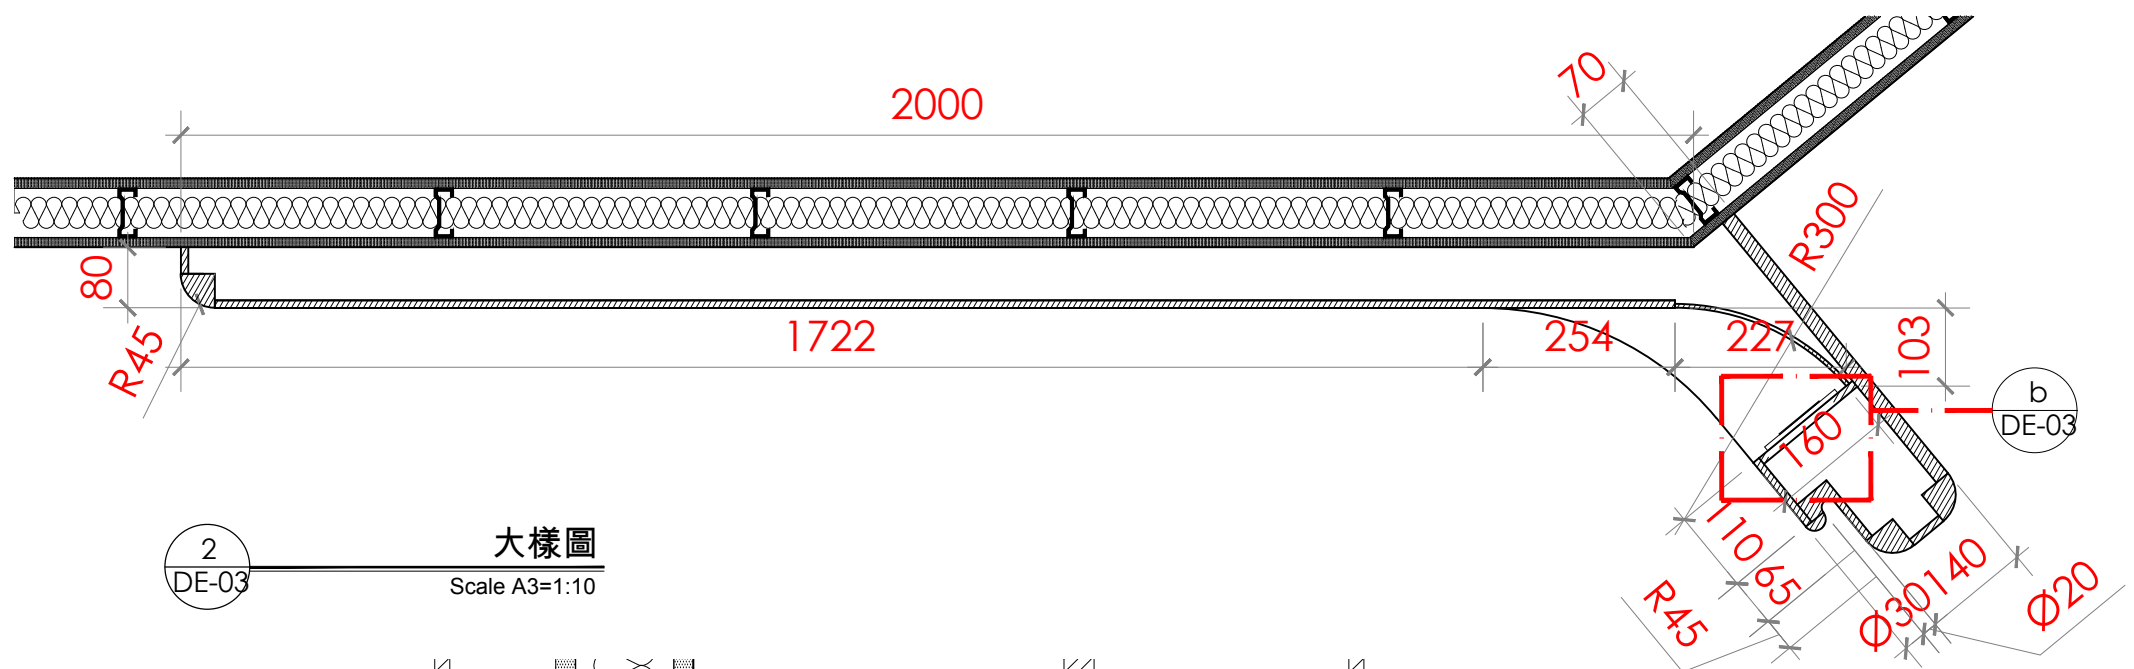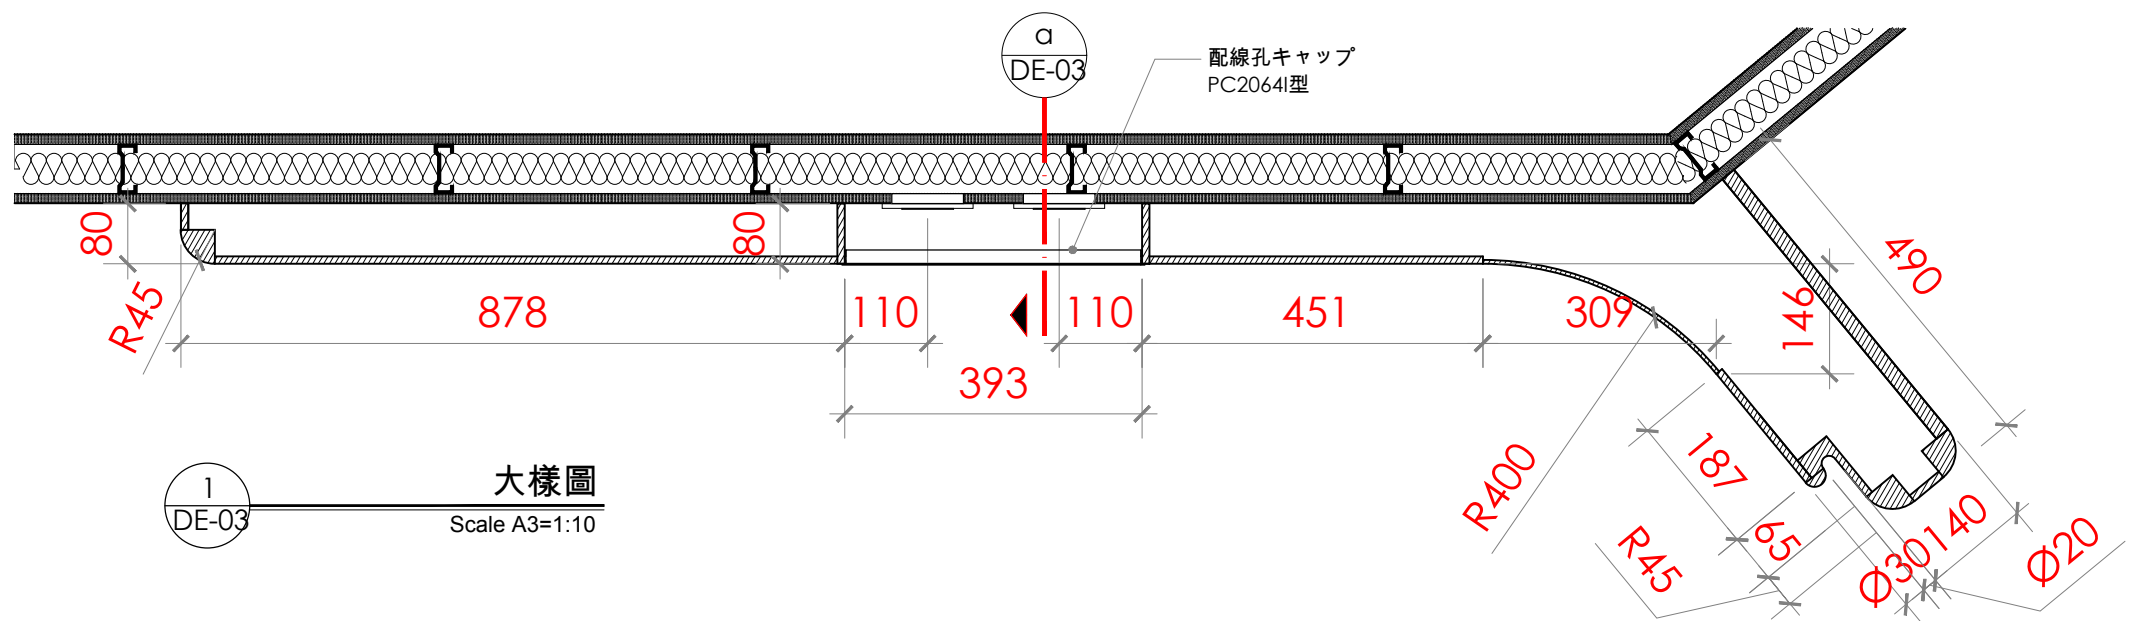

Revision

APPROVAL / 核准

設計者:	建築師:
業主:	

備註:

- a. 圖面標註尺寸僅供參考，施作均以現場放樣檢討之。
b. 圖面標註尺寸、材料及文字敘述因版本不同之差異，均以出圖章簽認日期之最近為準。
c. 電腦圖檔除由合約訂定外，均不得以何方式外流。
d. 圖面所示均為本公司所擁有之智慧財產，切勿以任何方式複製修改。



MULA DECO

▲ 3F, N.26, Ln.290, Guangfu S. Rd., Taipei.
☎ 886-2-2546-3258
☎ 886-2-2546-3257
✉ Guido@muladeco.com

Project / 案名

日本神宮案

Sheet Title / 圖名
507





大樣圖

Date / 日期	Scale / 比例
3/25/2026	1/10cm
Designer / 設計	Approval / 核准
MONICA LIN	
Job No / 業務編號	Drawn By / 繪圖
00000	GUIDO
Dwg No.	Page No.
DE-03	36




大様圖
Scale A3=1:2

[illegible]

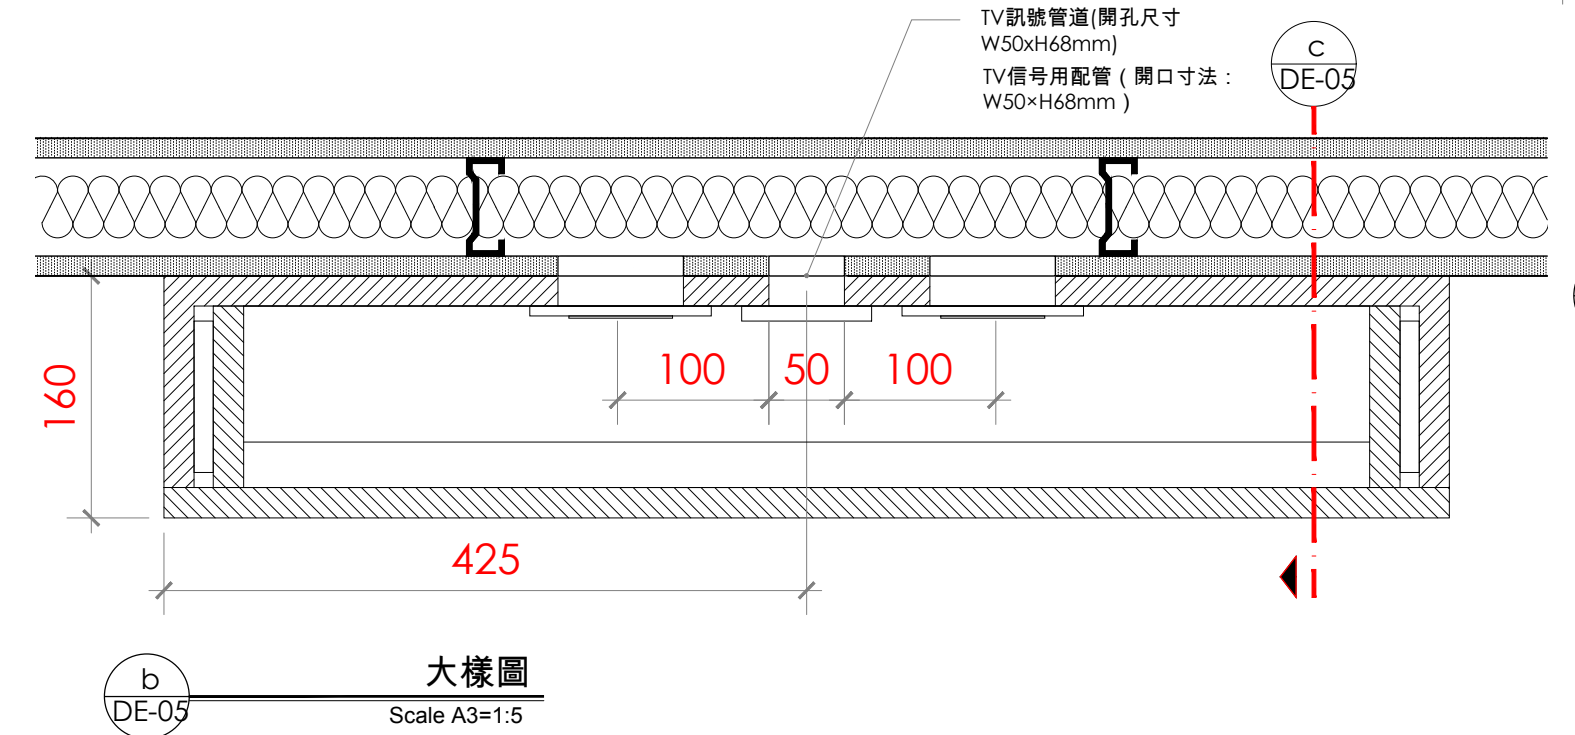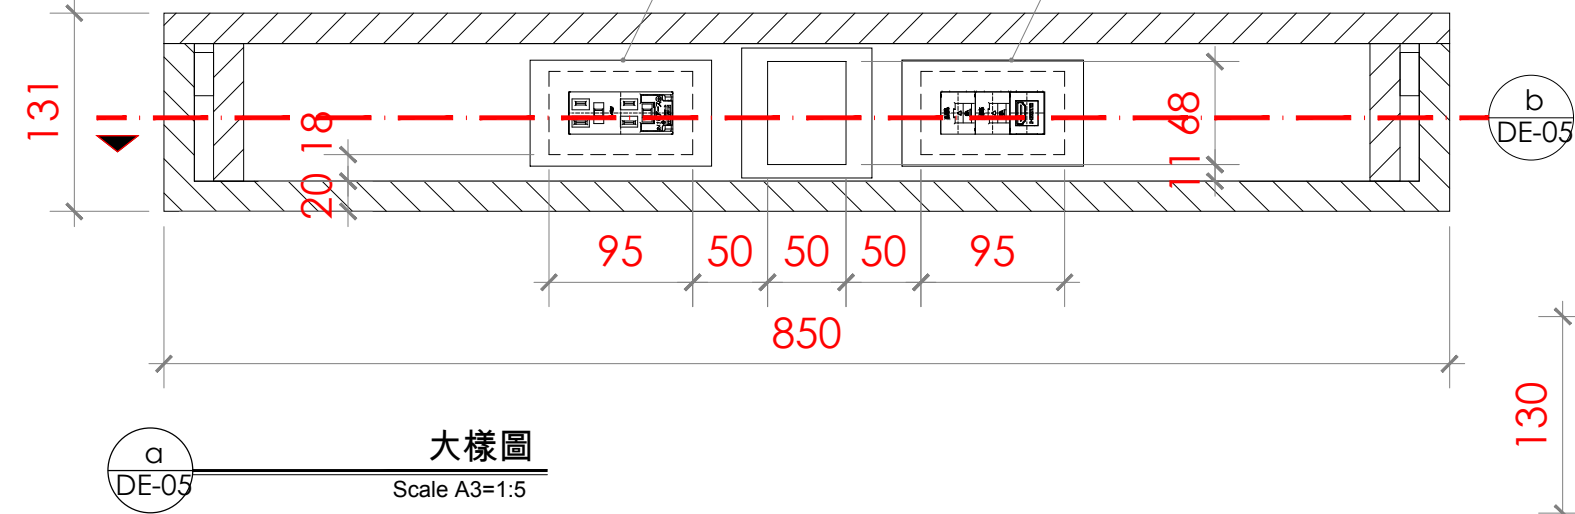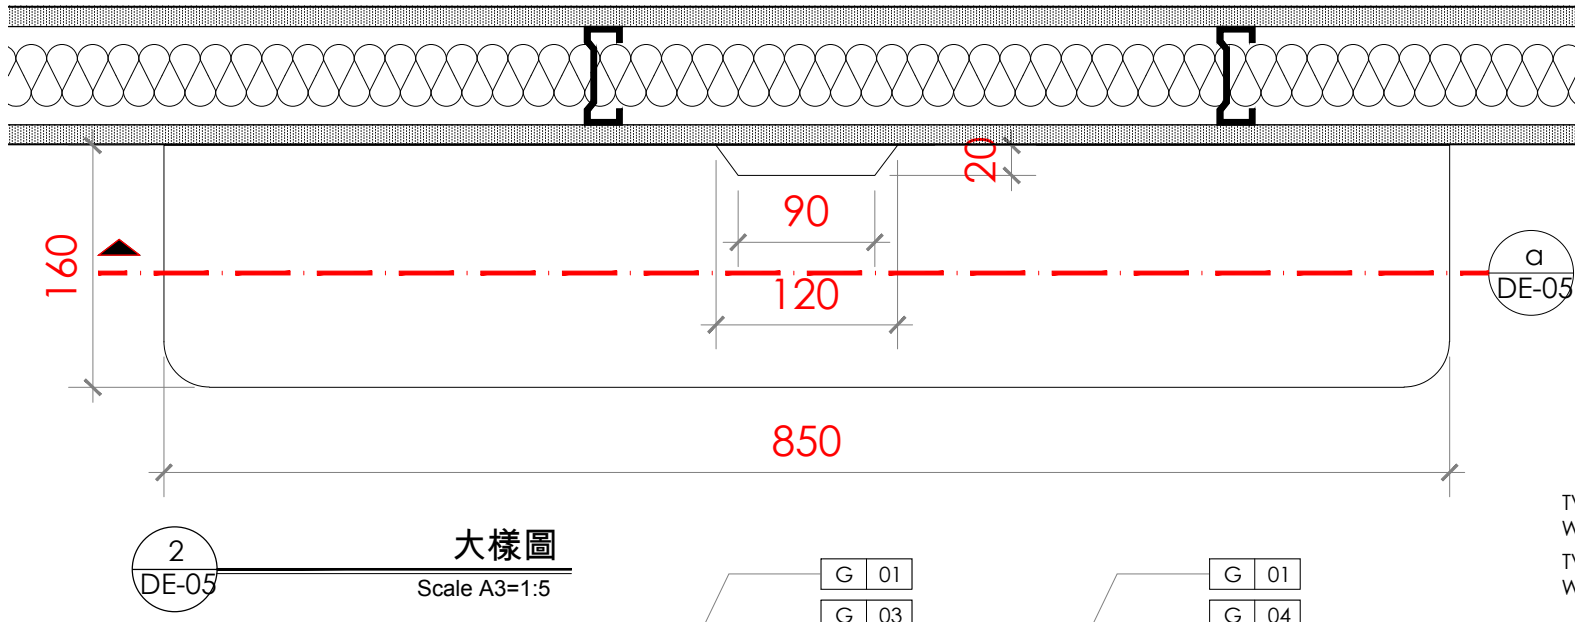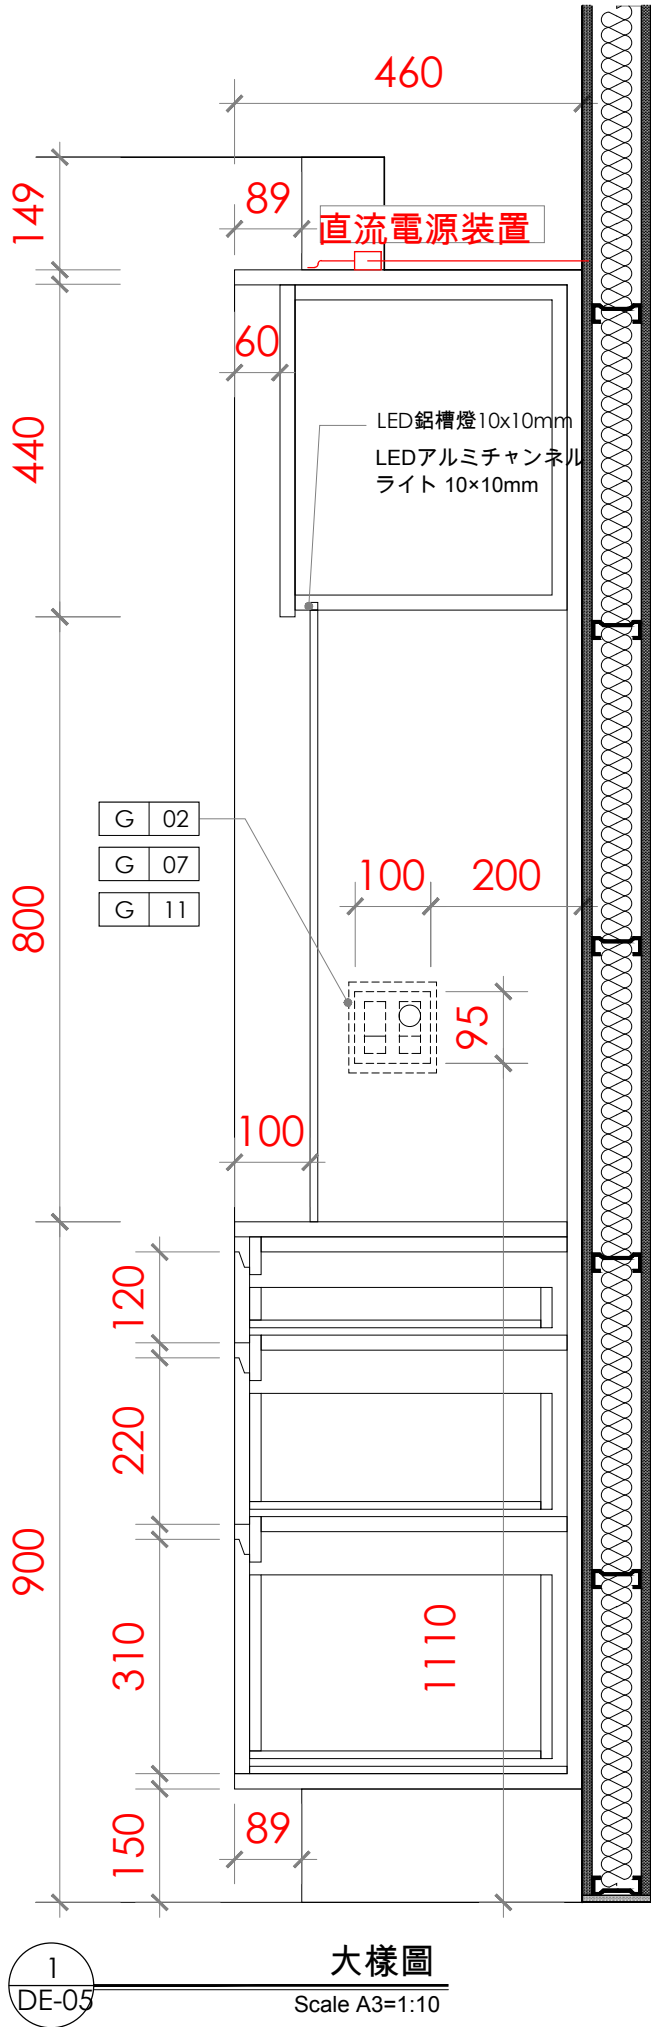

TV 訊號管道 (開孔尺寸
W50xH68mm)
TV 信号用配管 (開口寸法:
W50xH68mm)

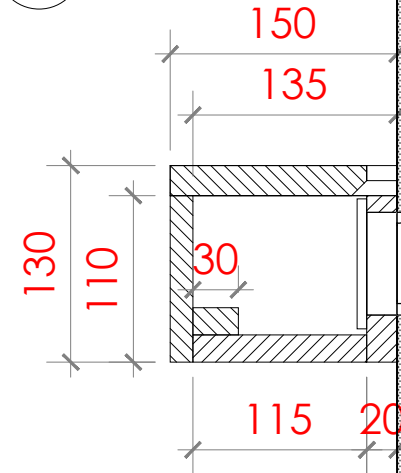

c
DE-05

大様圖
Scale A3=1:5

Revision	

APPROVAL / 核准	
設計者:	建築師:
業主:	

備註:

a. 圖面標註尺寸僅供參考，施作均以現場放樣檢討之。

b. 圖面標註尺寸、材料及文字敘述因版本不同之差異，均以出圖章簽認日期之最近為準。

c. 電腦圖檔除由合約訂定外，均不得以任何方式外流。


d. 圖面所示均為本公司所擁有之智慧財產，切勿以任何方式複製修改。


MULA DECO


▲ 3F, N.26, Ln.290, Guangfu S. Rd., Taipei.
☎ 886-2-2546-3258
☎ 886-2-2546-3257
✉ Guido@muladeco.com

Project / 案名	
日本神宮案	
Sheet Title / 圖名	
507	
大様圖	

Date / 日期	Scale / 比例
3/25/2026	1/10cm
Designer / 設計	Approval / 核准
MONICA LIN	
Job No / 業務編號	Drawn By / 繪圖
00000	GUIDO
Dwg No.	Page No.
DE-05	38

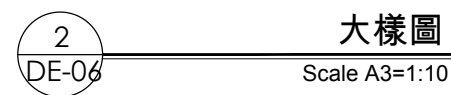


Date / 日期	Scale / 比例
3/25/2026	1/10cm
Designer / 設計	Approval / 核准
MONICA LIN	
Job No / 案卷編號	Drawn By / 繪圖
00000	GUIDO
Dwg No.	Page No.
DE-06	39

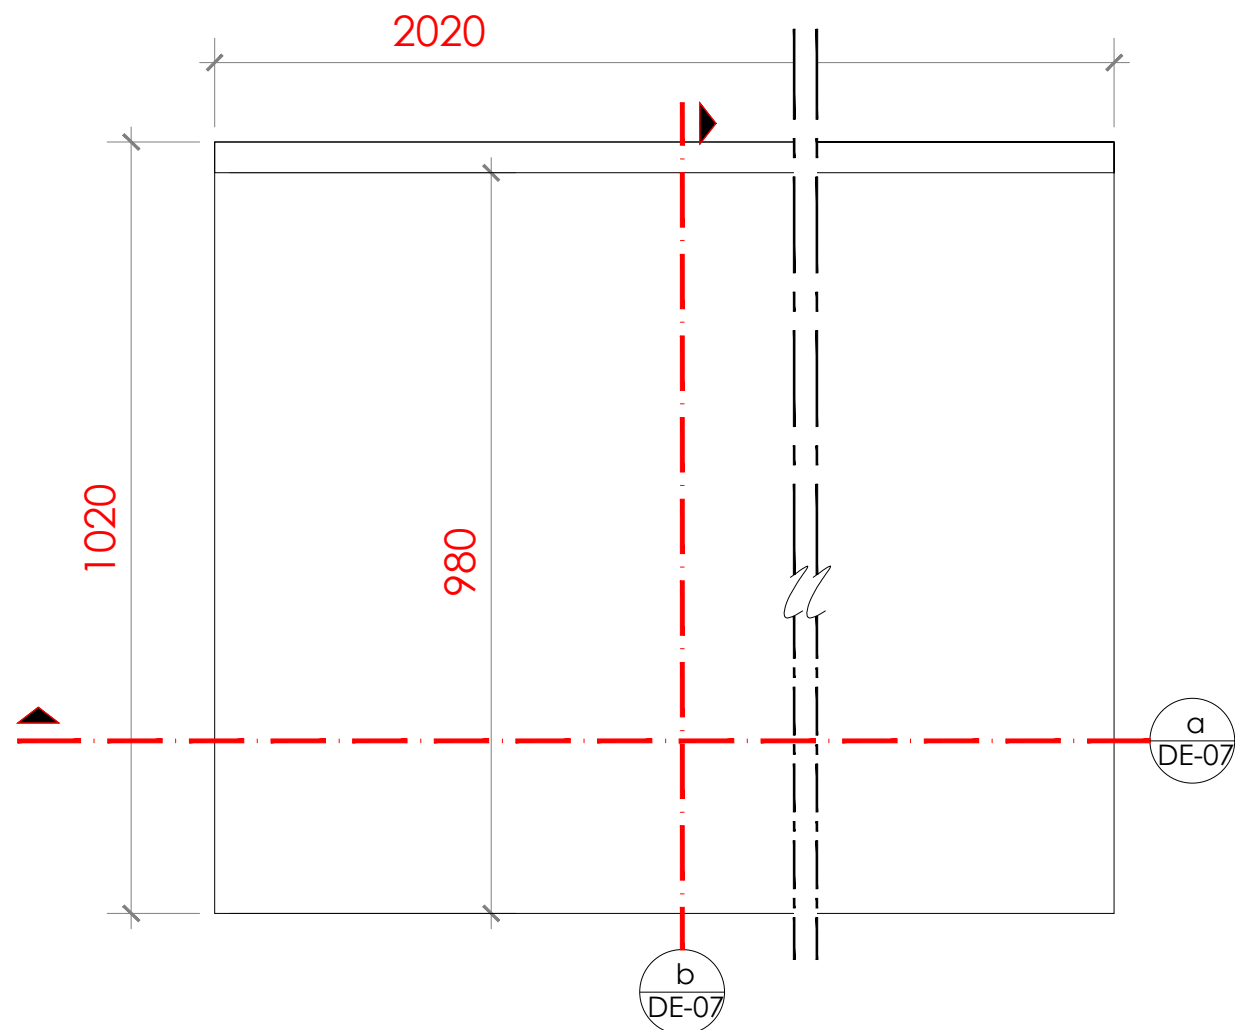


1
DE-07

大樣圖
Scale A3=1:10

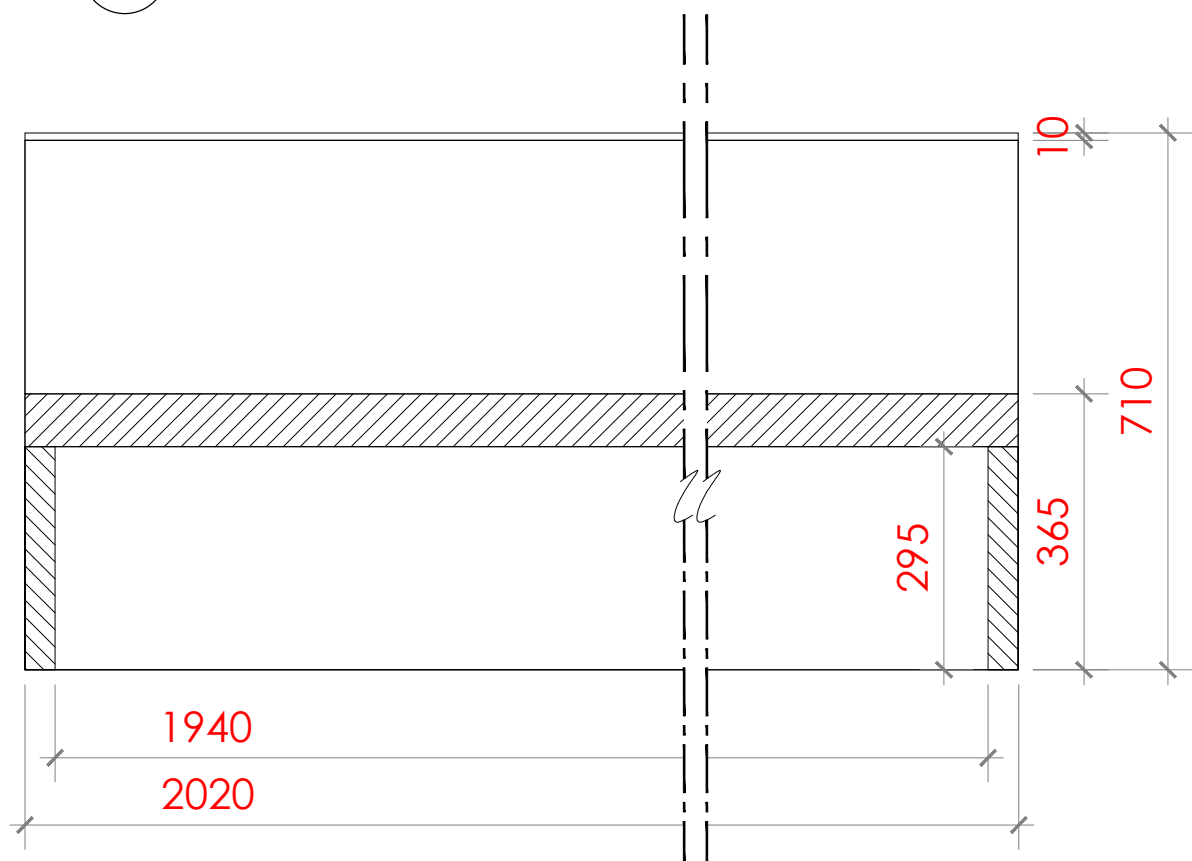


a
DE-07

大樣圖
Scale A3=1:10

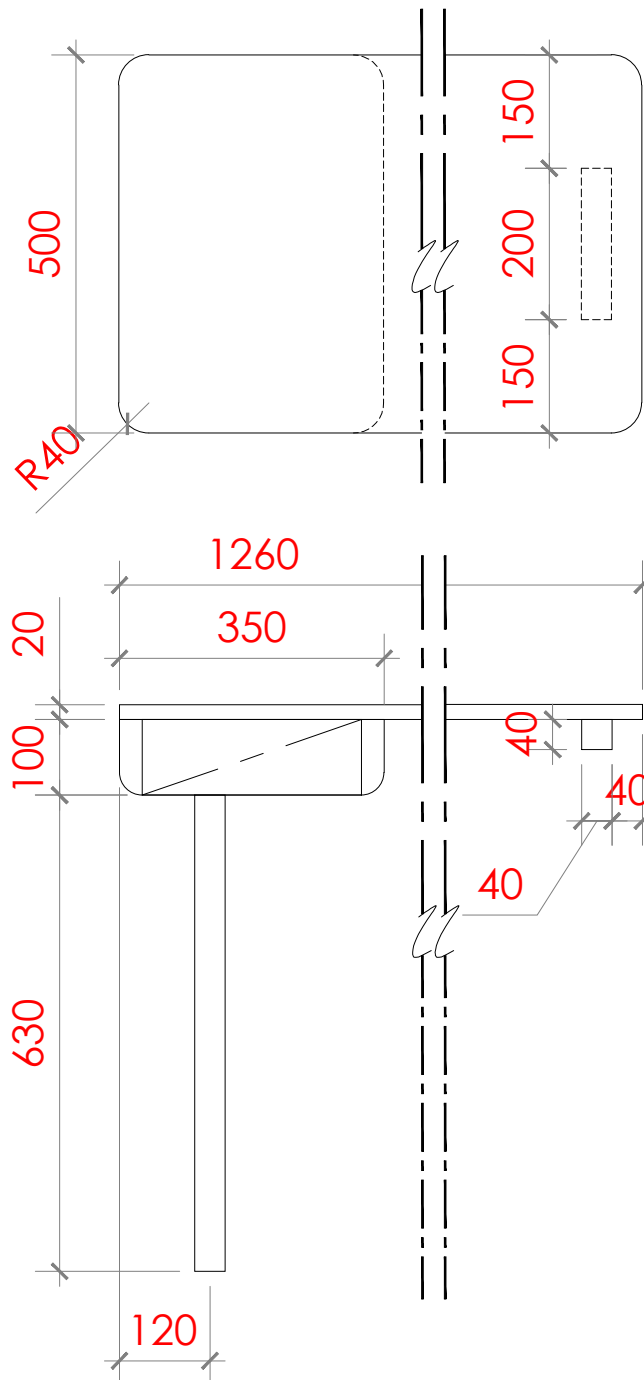


2
DE-07

大樣圖
Scale A3=1:10

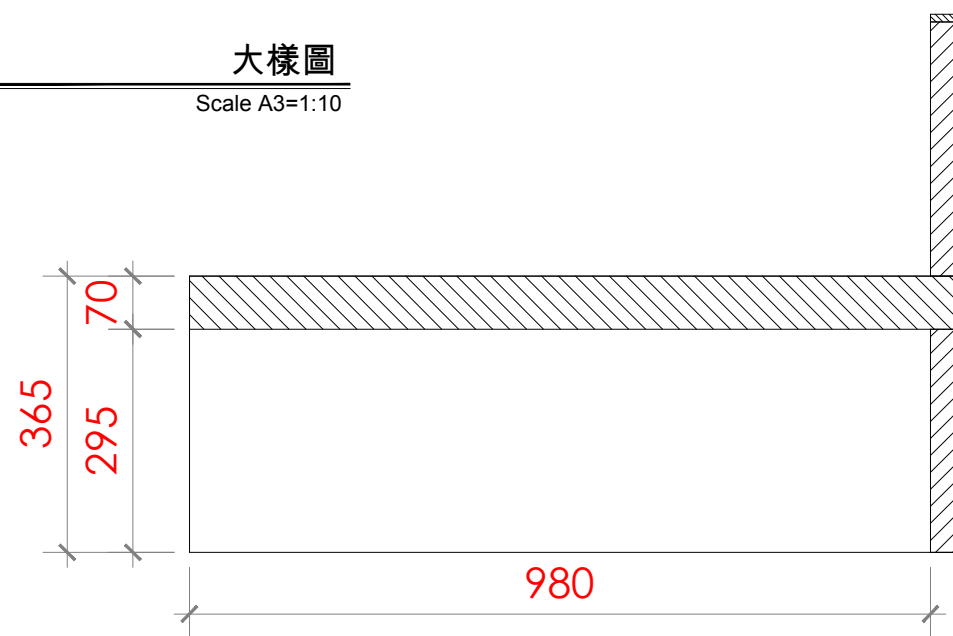

b
DE-07

大樣圖
Scale A3=1:10

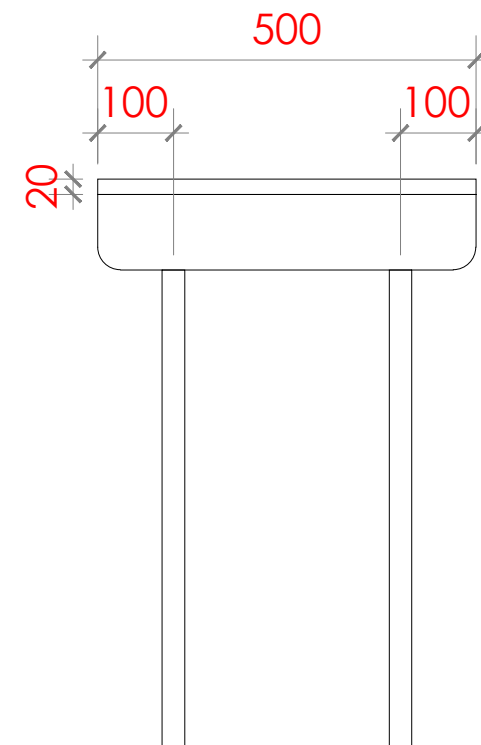

Revision

APPROVAL / 核准

設計者:	建築師:
業主:	

備註:

- a. 圖面標註尺寸僅供參考，施作均以現場放樣檢討之。
- b. 圖面標註尺寸、材料及文字敘述因版本不同之差異，均以出圖章簽認日期之最近為準。
- c. 電腦圖檔除由合約訂定外，均不得以任何方式外流。
- d. 圖面所示均為本公司所擁有之智慧財產，切勿以任何方式複製修改。



MULA DECO

▲ 3F, N.26, Ln.290, Guangfu S. Rd., Taipei.
☎ 886-2-2546-3258
✉ 886-2-2546-3257
E Guido@muladeco.com


Project / 案名

日本神宮案


Sheet Title / 圖名
507

立面圖


Date / 日期	Scale / 比例
3/25/2026	1/10cm
Designer / 設計	Approval / 核准
MONICA LIN	
Job No / 業務編號	Drawn By / 繪圖
00000	GUIDO
Dwg No.	Page No.
DE-07	40

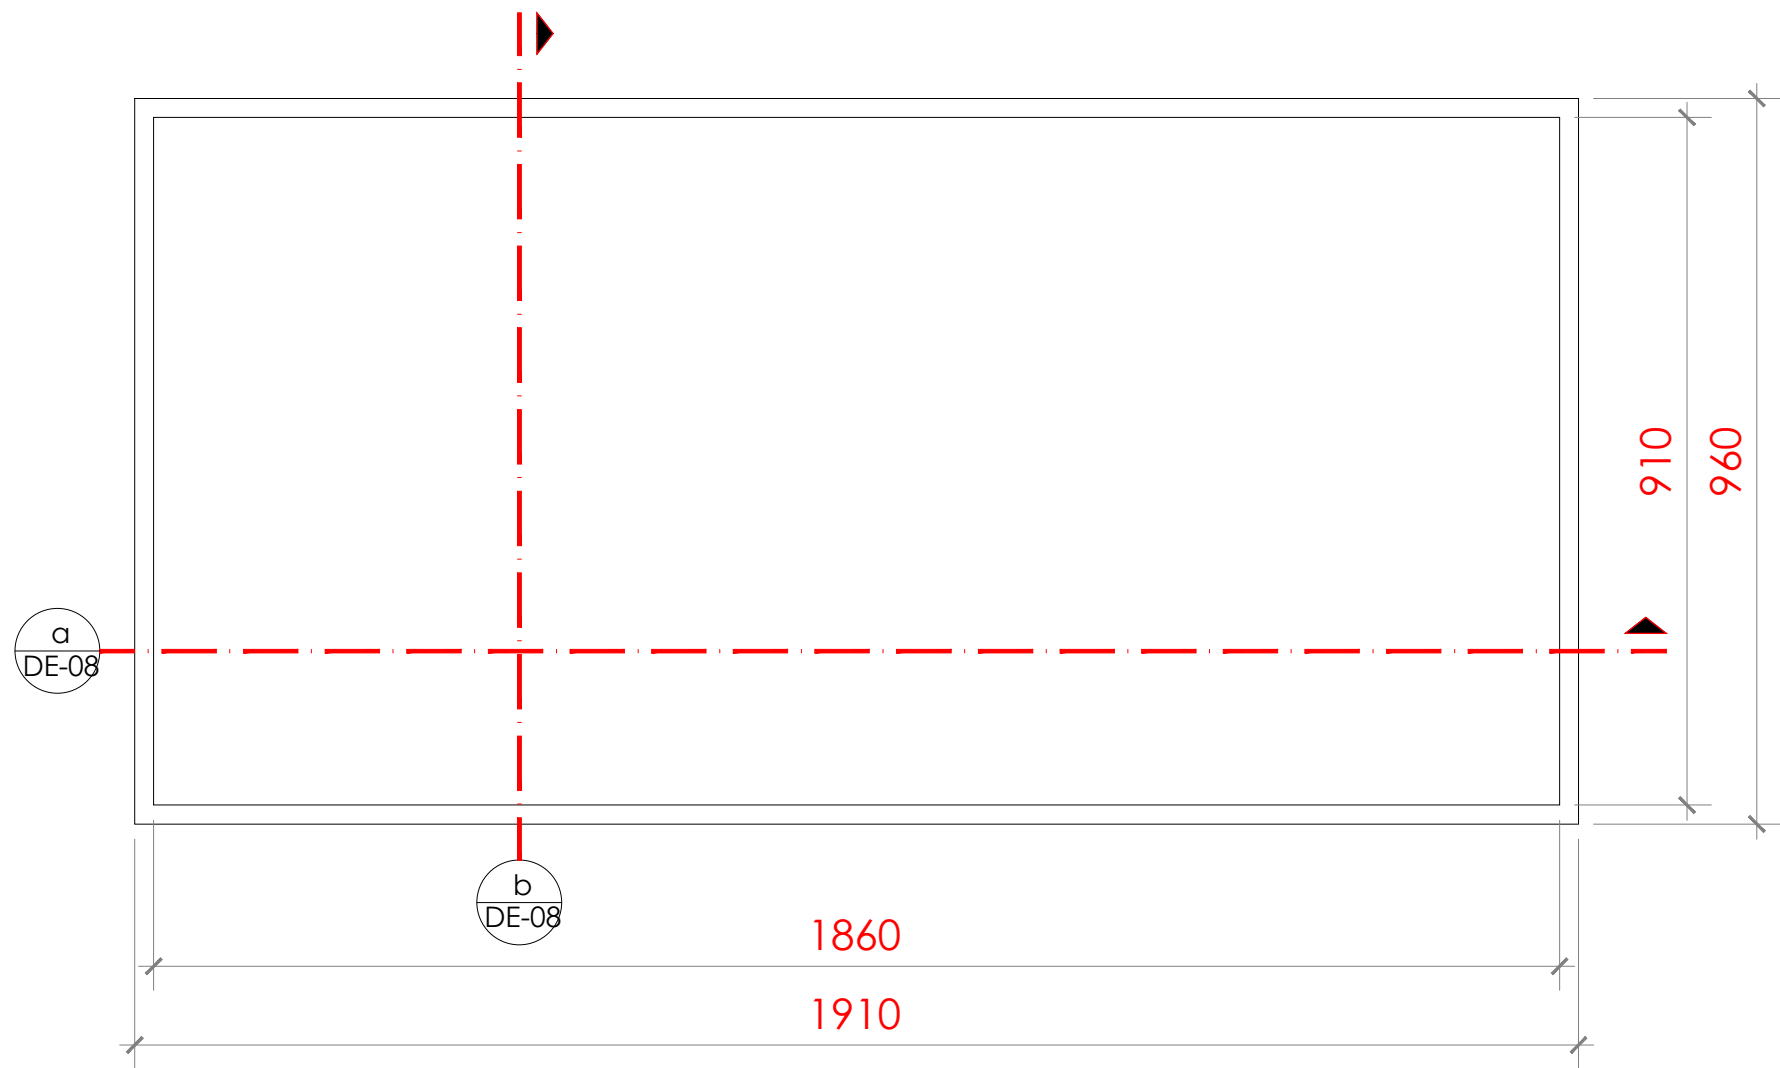

1
DE-08
大樣圖
Scale A3=1:10

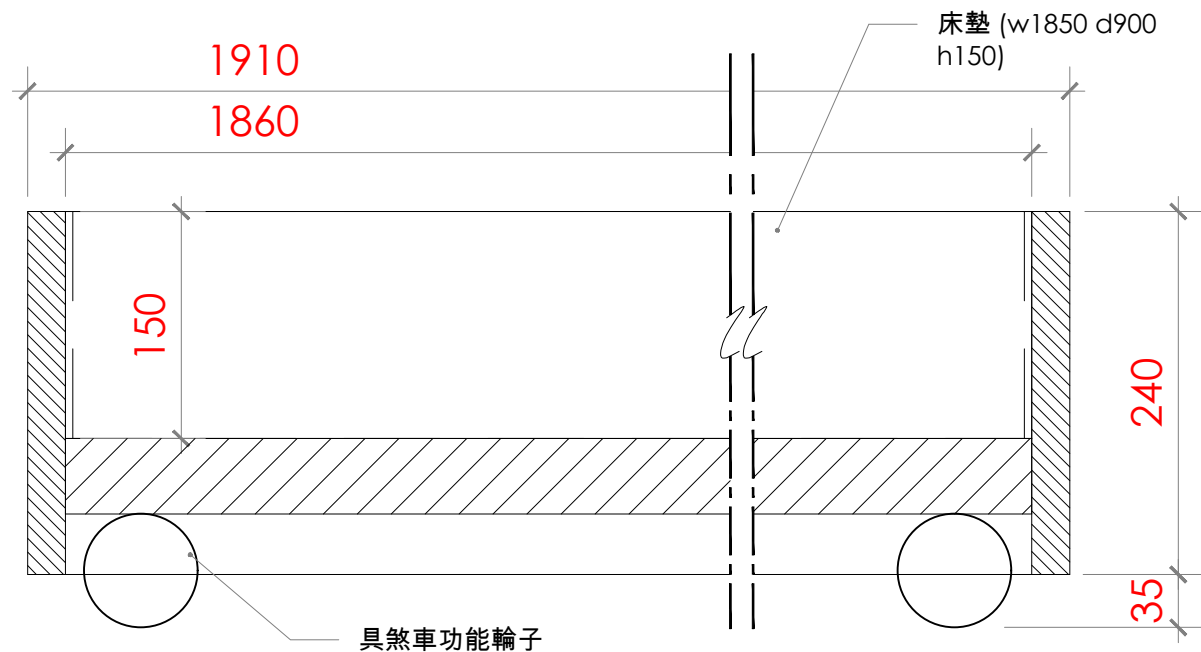

a
DE-08
大樣圖
Scale A3=1:5

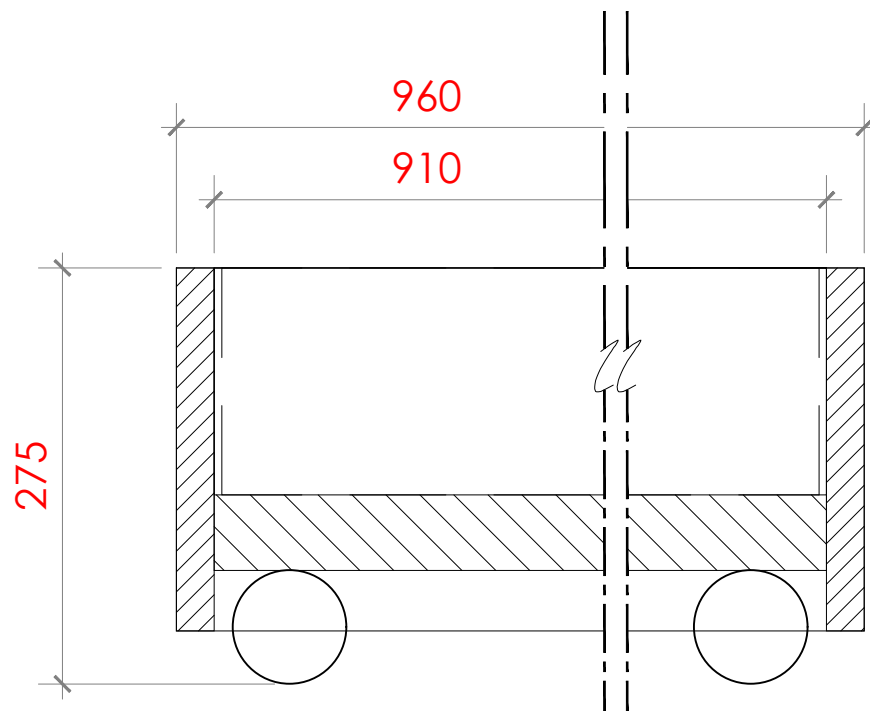

b
DE-08
大樣圖
Scale A3=1:5

Revision	
APPROVAL/核准	
設計者:	建築師:
業主:	

備註:
a. 圖面標註尺寸僅供參考，施作均以現場放樣檢討之。
b. 圖面標註尺寸、材料及文字敘述因版本不同之差異，均以出圖章簽認日期之最近為準。
c. 電腦圖檔除由合約訂定外，均不得以任何方式外流。
d. 圖面所示均為本公司所擁有之智慧財產，切勿以任何方式複製修改。



MULA DECO

▲ 3F, N.26, Ln.290, Guangfu S. Rd., Taipei.
☎ 886-2-2546-3258
✉ 886-2-2546-3257
E Guido@muladeco.com


Project / 案名

日本神宮案

Sheet Title / 圖名
507

立面圖

Date / 日期	Scale / 比例
3/25/2026	1/10cm
Designer / 設計	Approval / 核准
MONICA LIN	
Job No / 業務編號	Drawn By / 繪圖
00000	GUIDO
Dwg No.	Page No.
DE-08	41

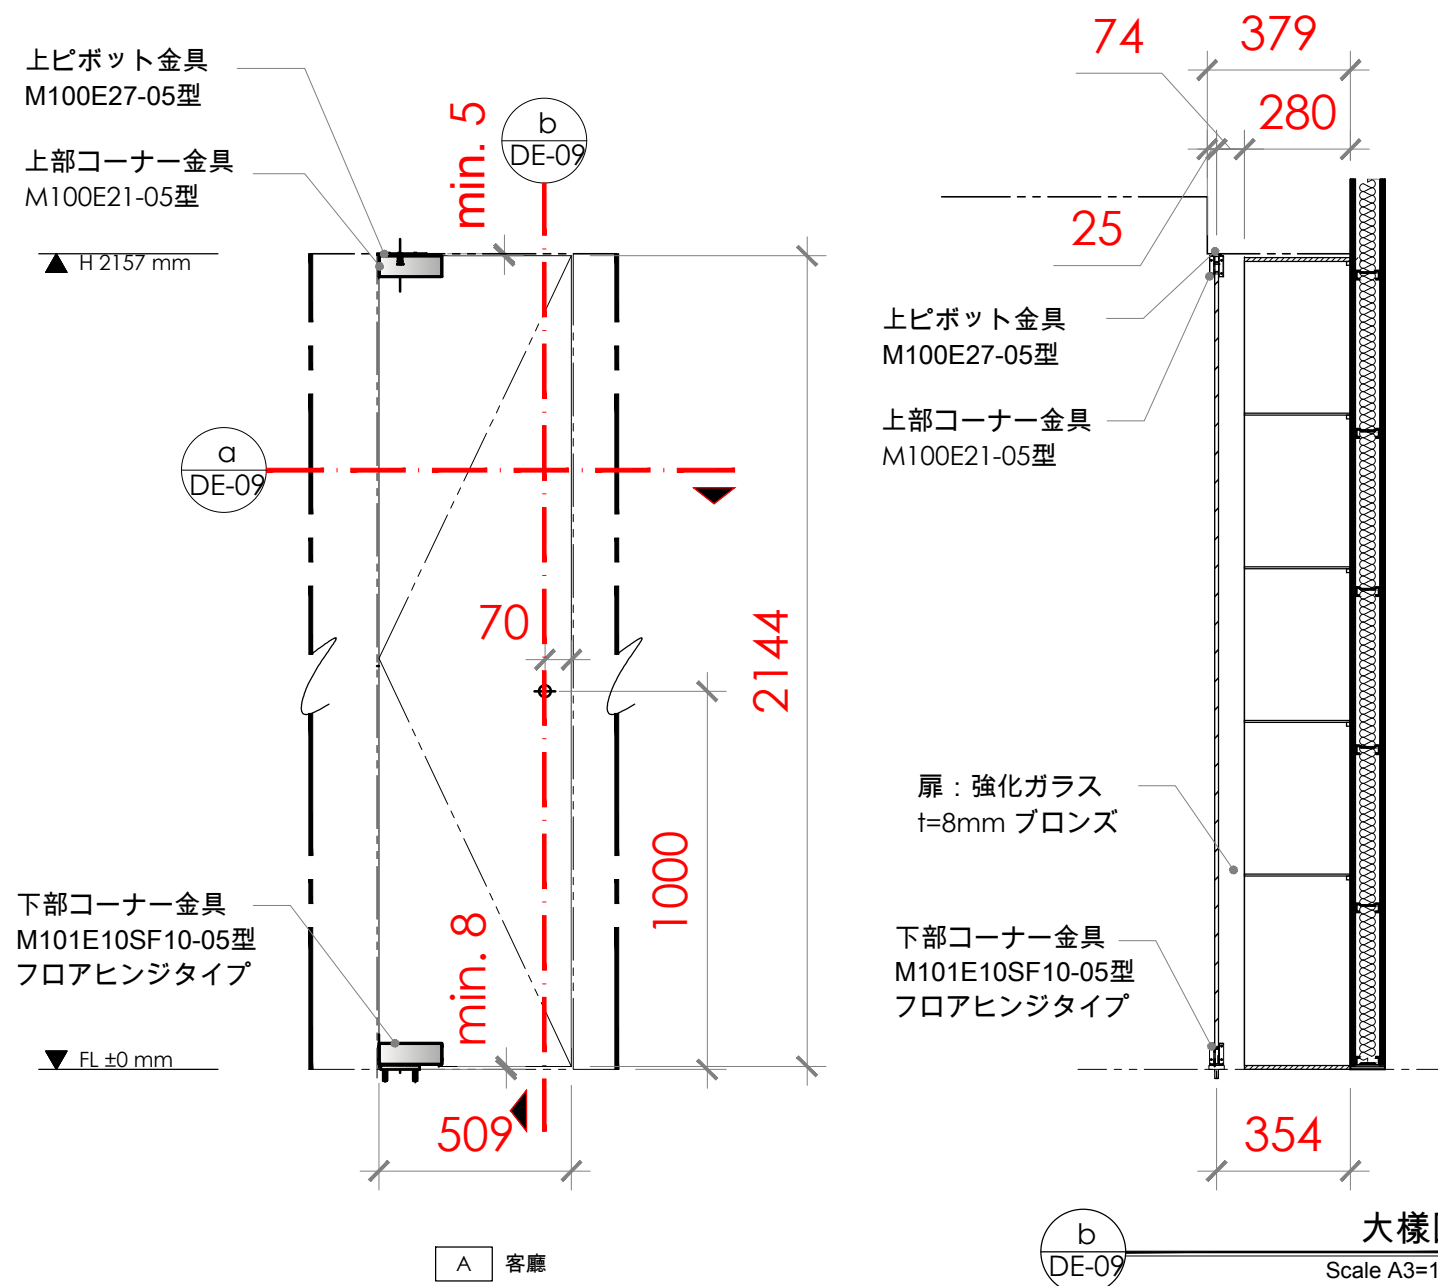[illegible]

備註:

- a. 圖面標註尺寸僅供參考，施作均以現場放樣檢討之。
- b. 圖面標註尺寸、材料及文字敘述因版本不同之差異，均以出圖章簽認日期之最近為準。
- c. 電腦圖檔除由合約訂定外，均不得以任何方式外流。
- d. 圖面所示均為本公司所擁有之智慧財產，切勿以任何方式複製修改。



MULA DECO

A 3F, N.26, Ln.290, Guangfu S. Rd., Taipei.
T 886-2-2546-3258
F 886-2-2546-3257
E Guido@muladeco.com


Project / 案名

日本神宮案

Sheet Title / 圖名
507

立面圖

Date / 日期	Scale / 比例
3/25/2026	1/20cm
Designer / 設計	Approval / 核准
MONICA LIN	
Job No / 業務編號	Drawn By / 繪圖
00000	GUIDO
Dwg No.	Page No.
DE-09	42

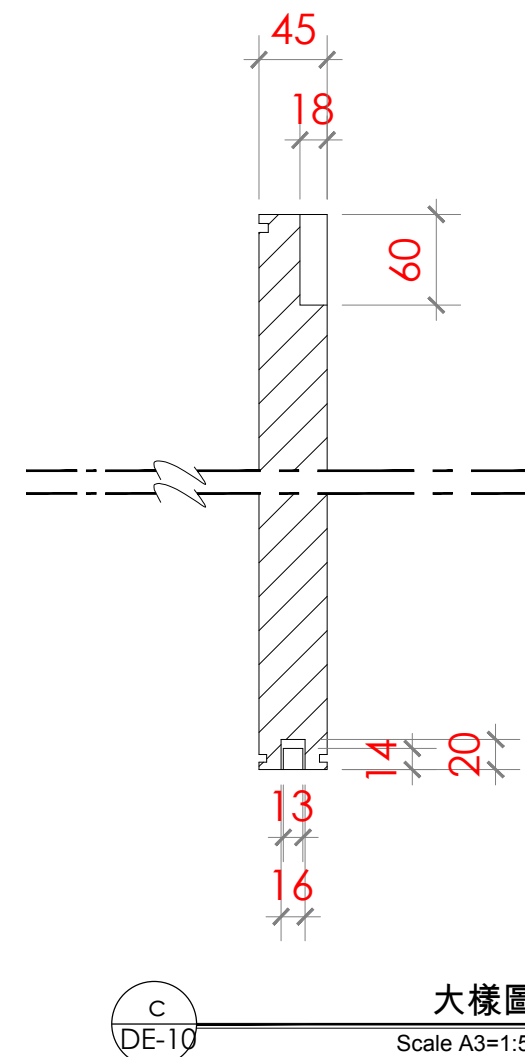

Date / 日期	Scale / 比例
3/25/2026	1/20cm
Designer / 設計	Approval / 核准
MONICA LIN	
Job No / 專案編號	Drawn By / 繪圖
00000	GUIDO
Dwg No.	Page No.
DE-10	43



DETAIL



S 1:3


MULA DECO
A 3F, N.26, Ln.290, Guangfu S. Rd., Taipei.
T 886-2-2546-3258
F 886-2-2546-3257
E Guido@mula deco.com

日本神宮案

立面圖

Date / 日期	Scale / 比例
3/25/2026	1/5cm
Designer / 設計	Approval / 核准
MONICA LIN	
Job No / 案卷編號	Drawn By / 繪圖
00000	GUIDO
Dwg No.	Page No.

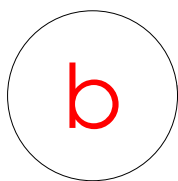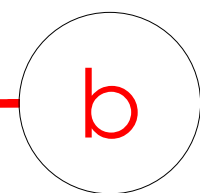

S 1:3

01