


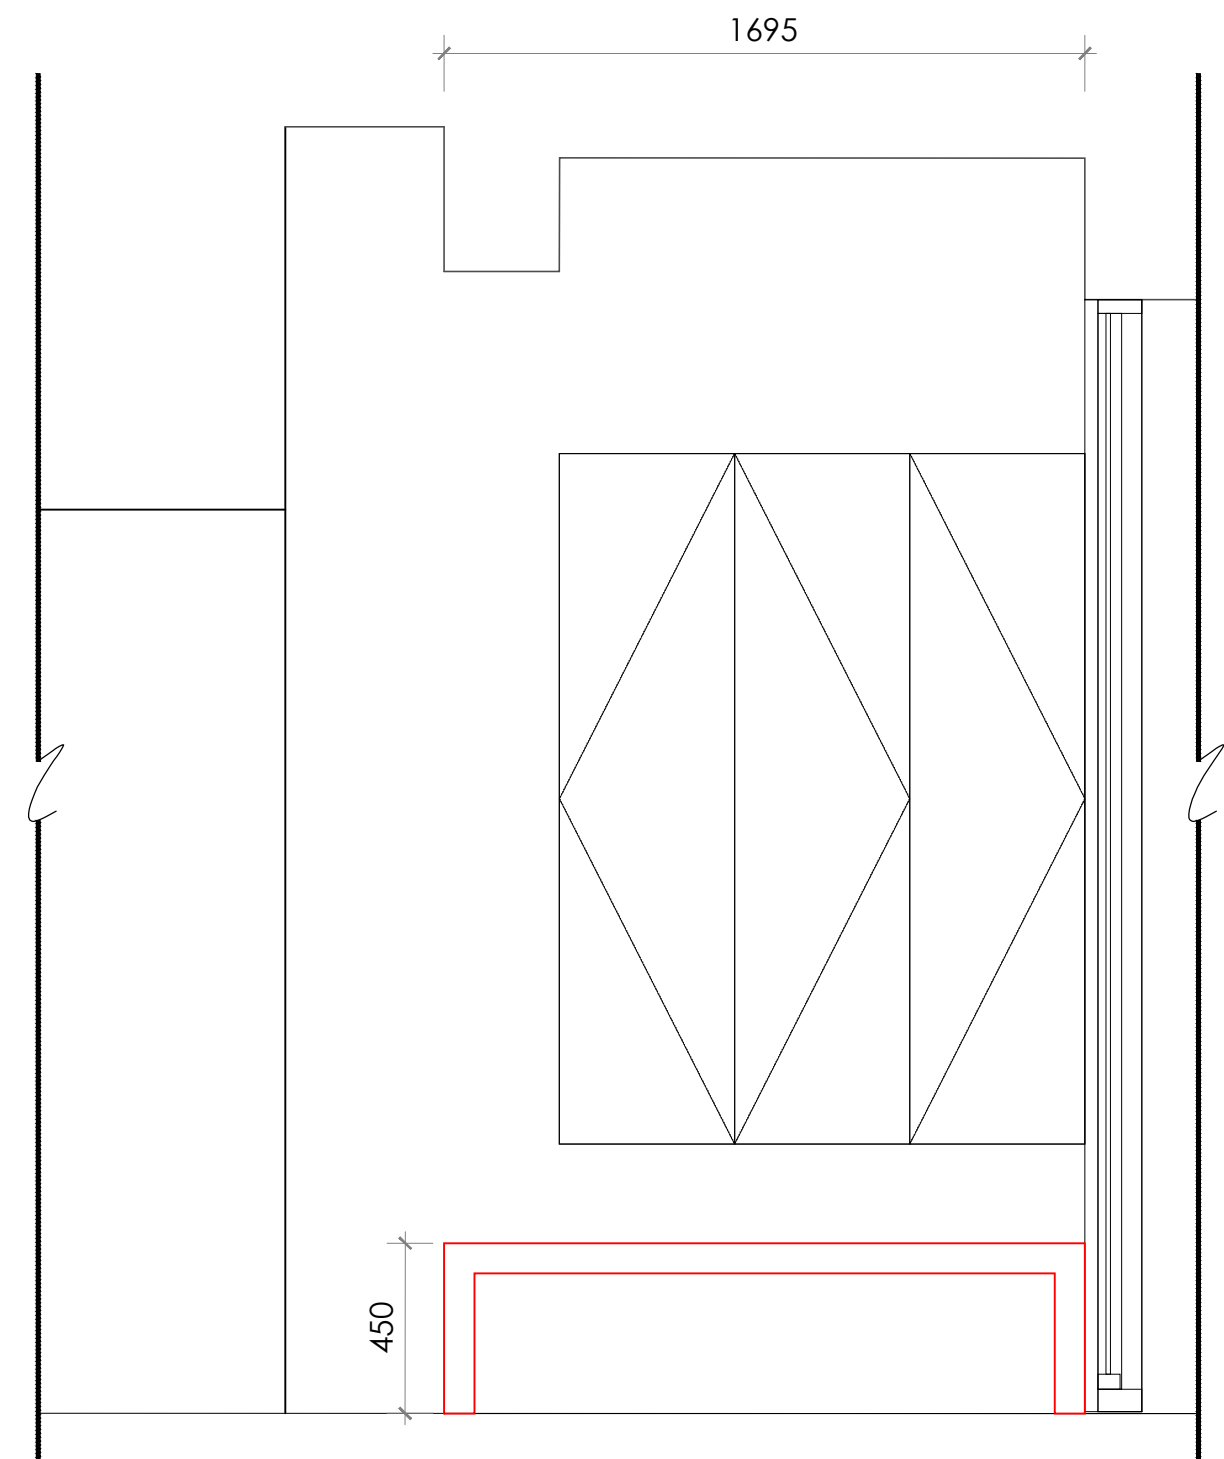

Revision

[illegible]

APPROVAL/核准

設計者:	建築師:
業主:	

葡註:

- g. 圖面標註尺寸僅供參考，施作均以現場放樣檢討之。
- h. 圖面標註尺寸、材料及文字敘述因版本不同之差異，均以出圖章簽認日期之最近為準。
- i. 電腦圖檔除由合約訂定外，均不得以任何方式外流。
- j. 圖面所示均為本公司所擁有之智慧財產，切勿以任何方式複製修改。



MULA DECO

A 3F, N.26, Ln.290, Guanfu S. Rd., Taipei.

T 886-2-2546-3258

F 886-2-2546-3257

E Guido@muladeco.com

Project / 案名

林口雲品薇閣姚宅

Sheet Title / 圖名

1F

大門鞋櫃


Date / 日期	Scale / 比例
8/10/2026	1/20MM
Designer / 設計	Approval / 核准
MONICA LIN	
Job No / 業務編號	Drawn By / 繪圖
80000	GUIDO
Dwn No	Page No

Dwg No

Page No.

DWG NO


PAGE

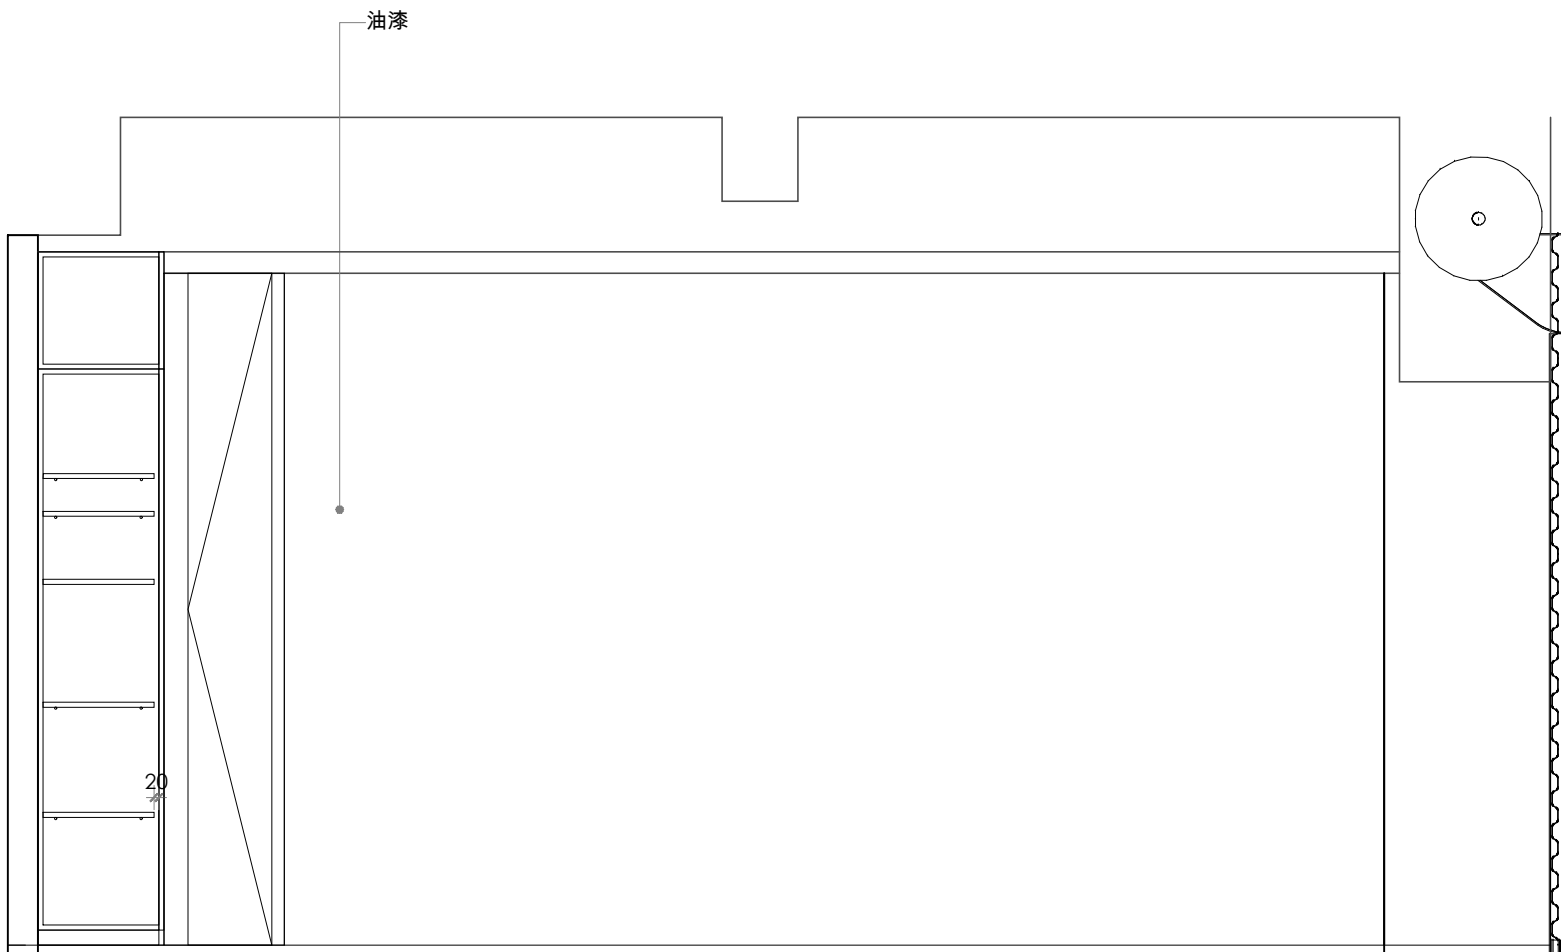

▲CH 2750mm
▲CH 2665mm

Scale=1:30


71

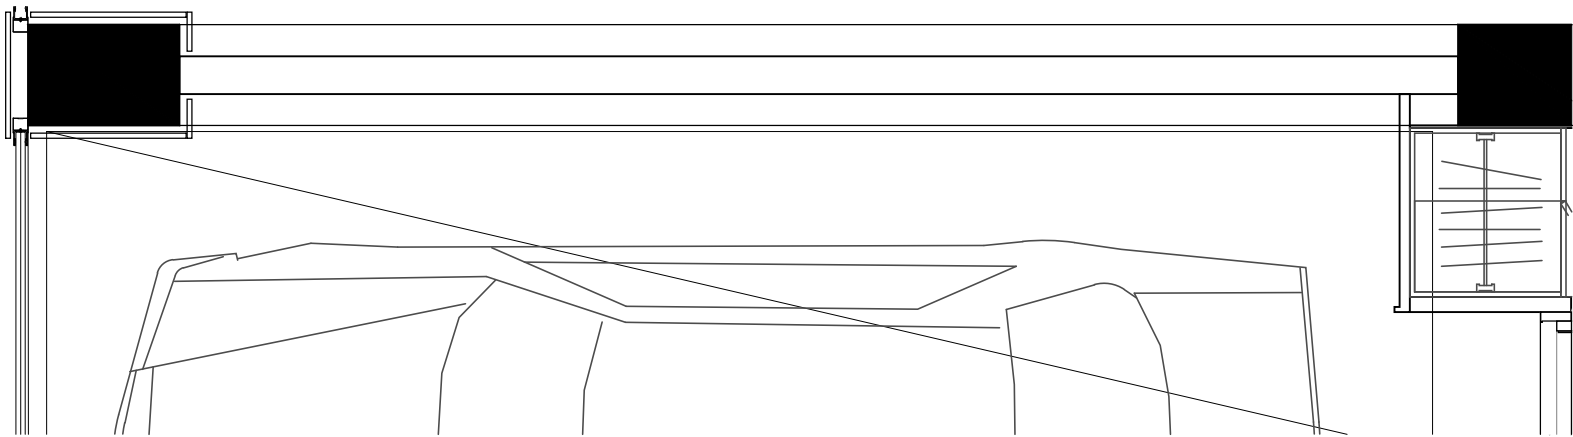

▲CH 3340mm

▲CH 2750mm
▲CH 2665mm

▼FL ±0 mm
▲FL -50 mm

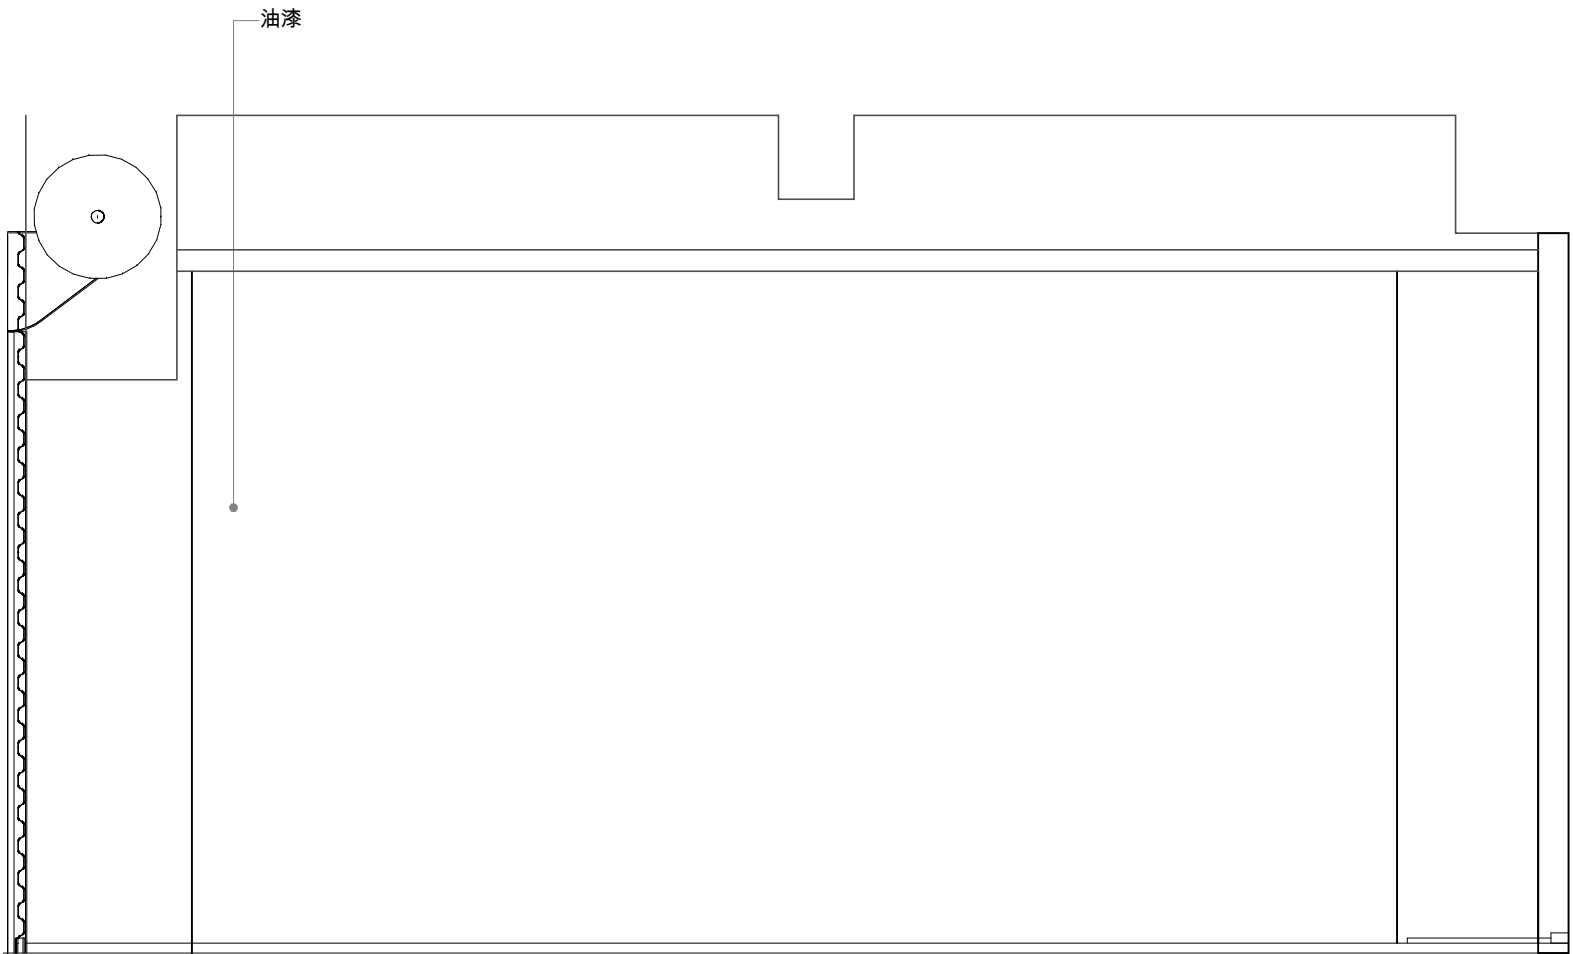

1
E-02

ELEVATION

Scale=1:30

Revision

APPROVAL/核准

設計者:	建築師:
業主:	

備註:

- a. 圖面標註尺寸僅供參考，施作均以現場放樣檢討之。
- b. 圖面標註尺寸、材料及文字敘述因版本不同之差異，均以出圖章簽認日期之最近為準。
- c. 電腦圖檔除由合約訂定外，均不得以任何方式外流。
- d. 圖面所示均為本公司所擁有之智慧財產，切勿以任何方式複製修改。



MULA DECO

▲ 3F, N.26, Ln.290, Guangfu S. Rd., Taipei.
☎ 886-2-2546-3258
☎ 886-2-2546-3257
✉ Guido@muladeco.com

Project / 案名

林口雲品薇閣姚宅

Sheet Title / 圖名



B1F

立面圖

Date / 日期	Scale / 比例
8/10/2026	1/30cm
Designer / 設計	Approval / 核准
MONICA LIN	
Job No / 業務編號	Drawn By / 繪圖
00000	GUIDO
Dwg No.	Page No.

E-02

72

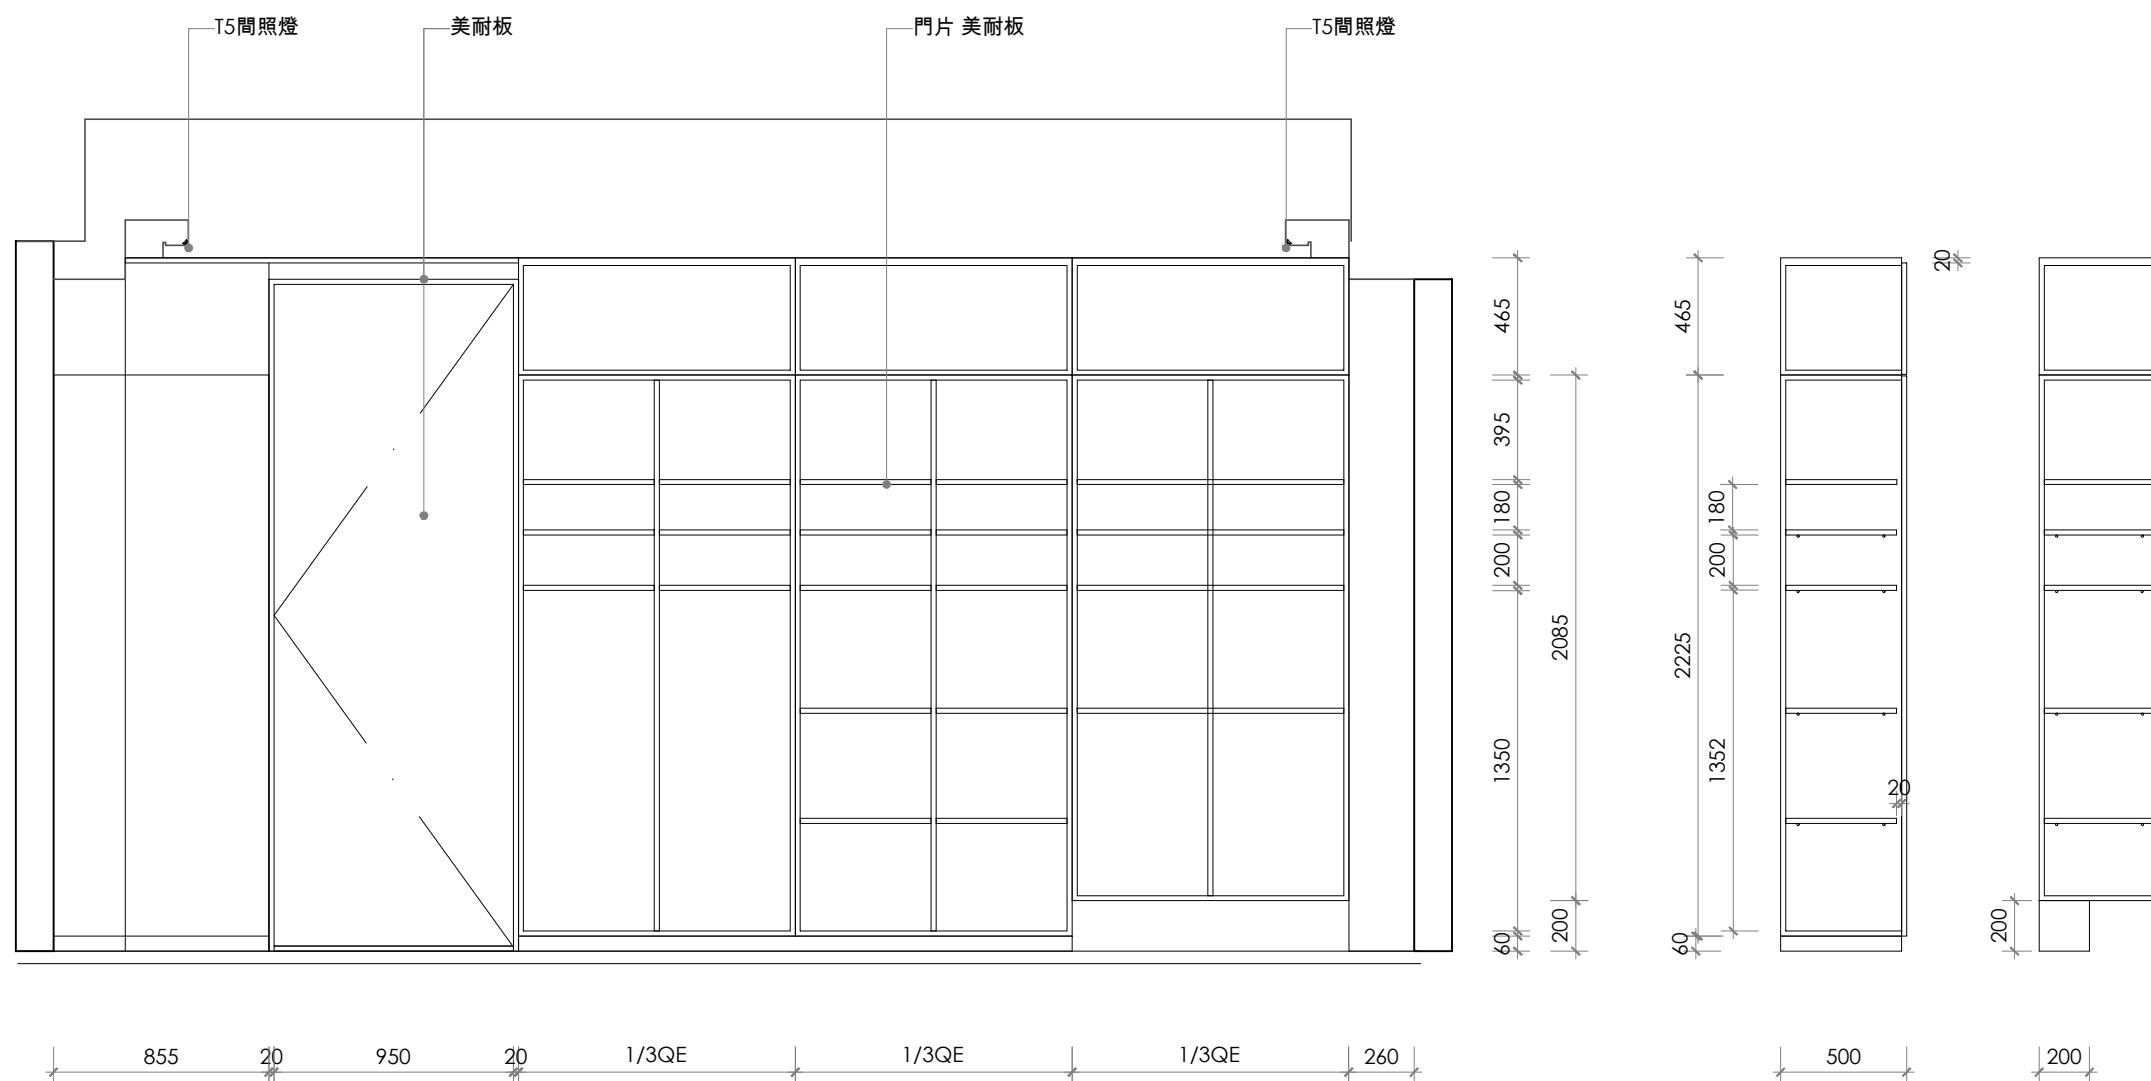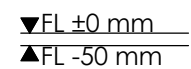

1
E-03

ELEVATION

Scale=1:30

[illegible]

備註:

- a. 圖面標註尺寸僅供參考，施作均以現場放樣檢校之。
- b. 圖面標註尺寸、材料及文字敘述因版本不同之差異，均以出圖章簽認日期之最近為準。
- c. 電腦圖檔除由合約訂定外，均不得以任何方式外洩。
- d. 圖面所示均為本公司所擁有之智慧財產，切勿以任何方式複製修改。



MULA DECO

A 3F, N.26, Ln.290, Guangfu S. Rd., Taipei.
T 886-2-2546-3258
F 886-2-2546-3257
E Guido@muladeco.com

Project / 案名

林口雲品薇閣姚宅


Sheet Title / 圖名
B1F

立面圖

Date / 日期	Scale / 比例
8/10/2026	1/30cm
Designer / 設計	Approval / 核准
MONICA LIN	
Job No / 業務編號	Drawn By / 繪圖
00000	GUIDO
Dwg No.	Page No.

E-03


74

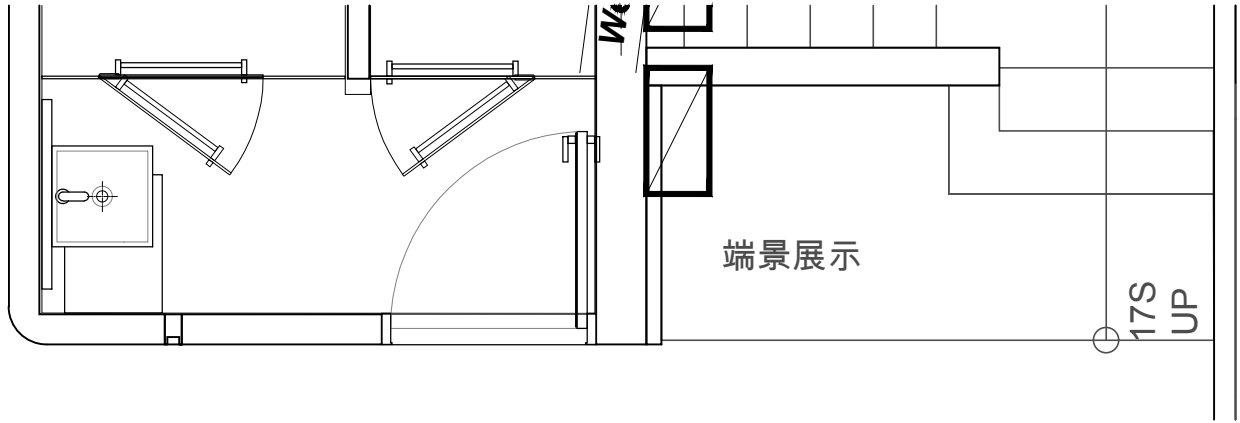

▲CH 3340mm

▲CH 2750mm
▲CH 2665mm

▼FL ±0 mm
▲FL -50 mm

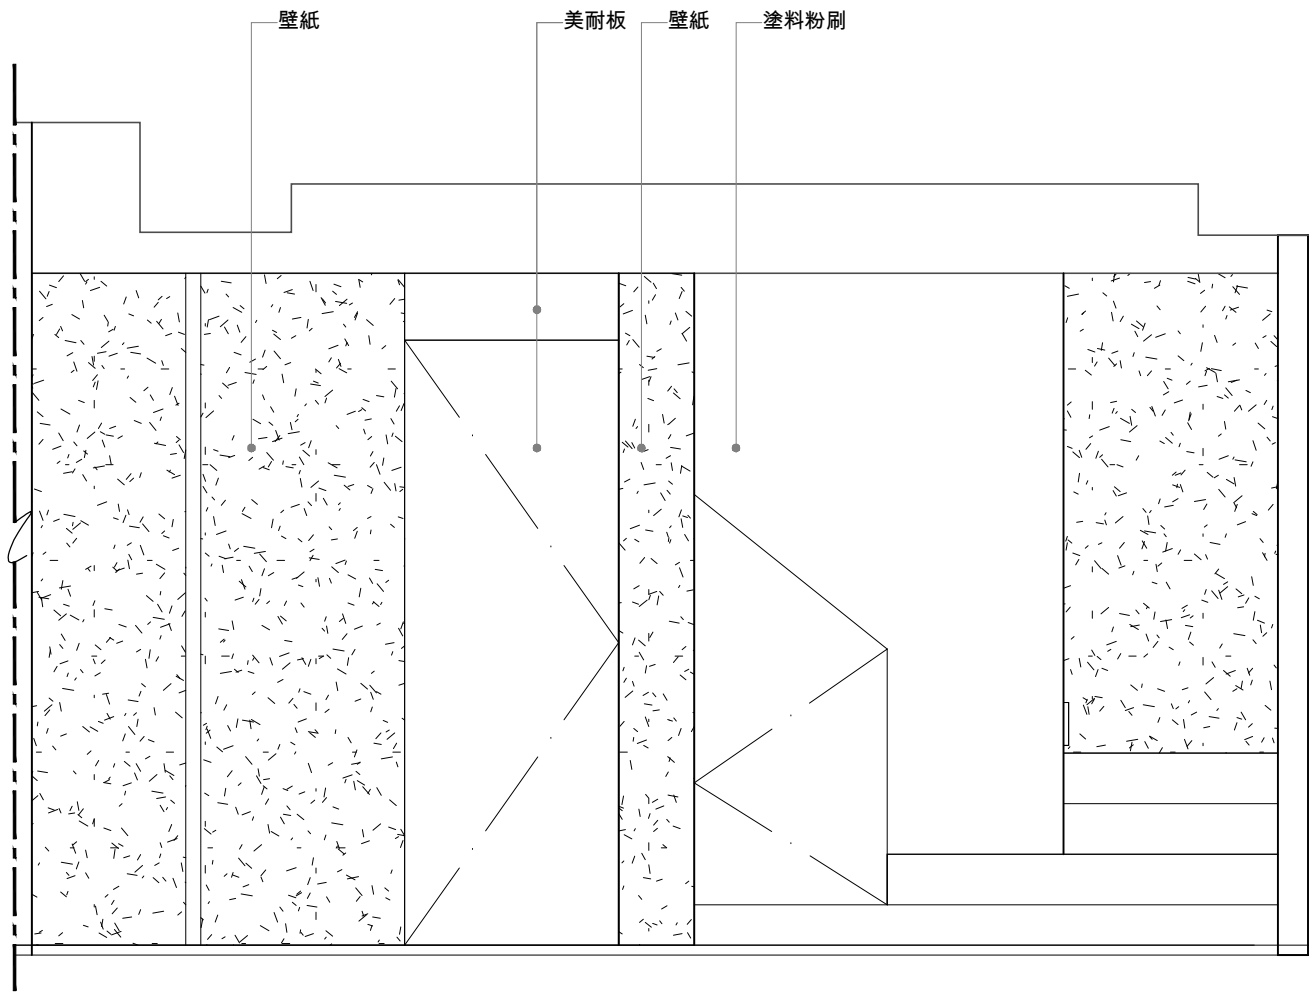

1
E-04

ELEVATION

Scale=1:30

Revision

APPROVAL/核准

設計者:	建築師:
業主:	

備註:

- 圖面標註尺寸僅供參考，施作均以現場放樣檢討之。
- 圖面標註尺寸、材料及文字敘述因版本不同之差異，均以圖章簽認日期之最近為準。
- 電腦圖檔除由合約訂定外，均不得以任何方式外流。
- 圖面所示均為本公司所擁有之智慧財產，切勿以任何方式複製修改。



MULA DECO

▲ 3F, N.26, Ln.290, Guangfu S. Rd., Taipei.
☎ 886-2-2546-3258
☎ 886-2-2546-3257
✉ Guido@muladeco.com

Project / 案名

林口雲品薇閣姚宅


Sheet Title / 圖名
B1F

立面圖

Date / 日期	Scale / 比例
8/10/2026	1/30cm
Designer / 設計	Approval / 核准
MONICA LIN	
Job No / 業務編號	Drawn By / 繪圖
00000	GUIDO
Dwg No.	Page No.

E-04


75

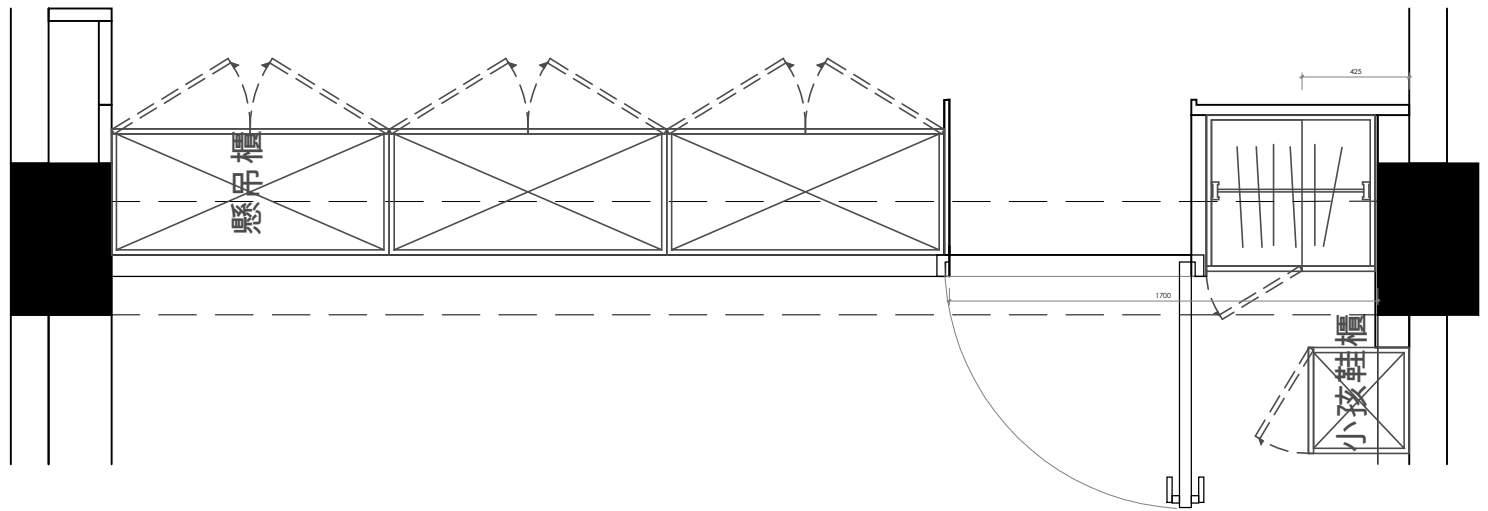

▲CH 3340mm

▲CH 2750mm
▲CH 2665mm

▼FL ±0 mm
▲FL -50 mm

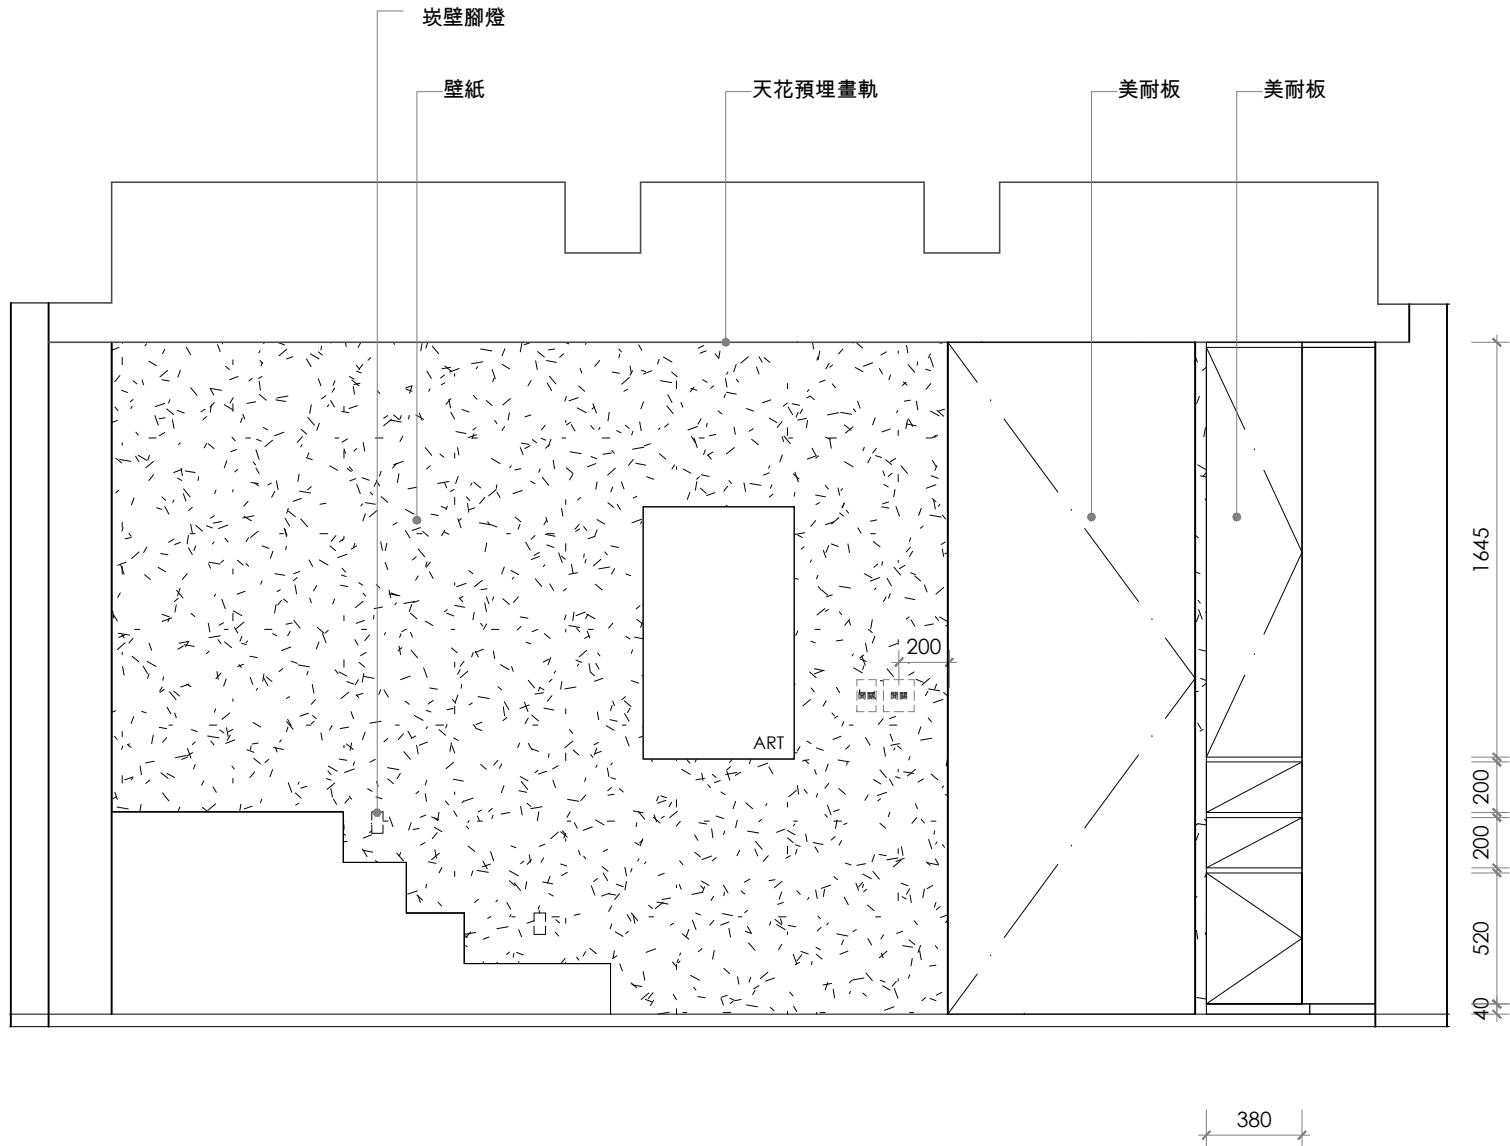

1
E-05

ELEVATION

Scale=1:30

Revision

APPROVAL/核准

設計者:	建築師:
業主:	

備註:

- 圖面標註尺寸僅供參考，施作均以現場放樣檢討之。
- 圖面標註尺寸、材料及文字敘述因版本不同之差異，均以出圖章簽認日期之最近為準。
- 電腦圖檔除由合約訂定外，均不得以何方式外流。
- 圖面所示均為本公司所擁有之智慧財產，切勿以任何方式複製修改。



MULA DECO

▲ 3F, N.26, Ln.290, Guangfu S. Rd., Taipei.
☎ 886-2-2546-3258
☎ 886-2-2546-3257
✉ Guido@muladeco.com

Project / 案名

林口雲品薇閣姚宅



Sheet Title / 圖名
B1F

立面圖

Date / 日期	Scale / 比例
8/10/2026	1/30cm
Designer / 設計	Approval / 核准
MONICA LIN	
Job No / 業務編號	Drawn By / 繪圖
00000	GUIDO
Dwg No.	Page No.

E-05

76

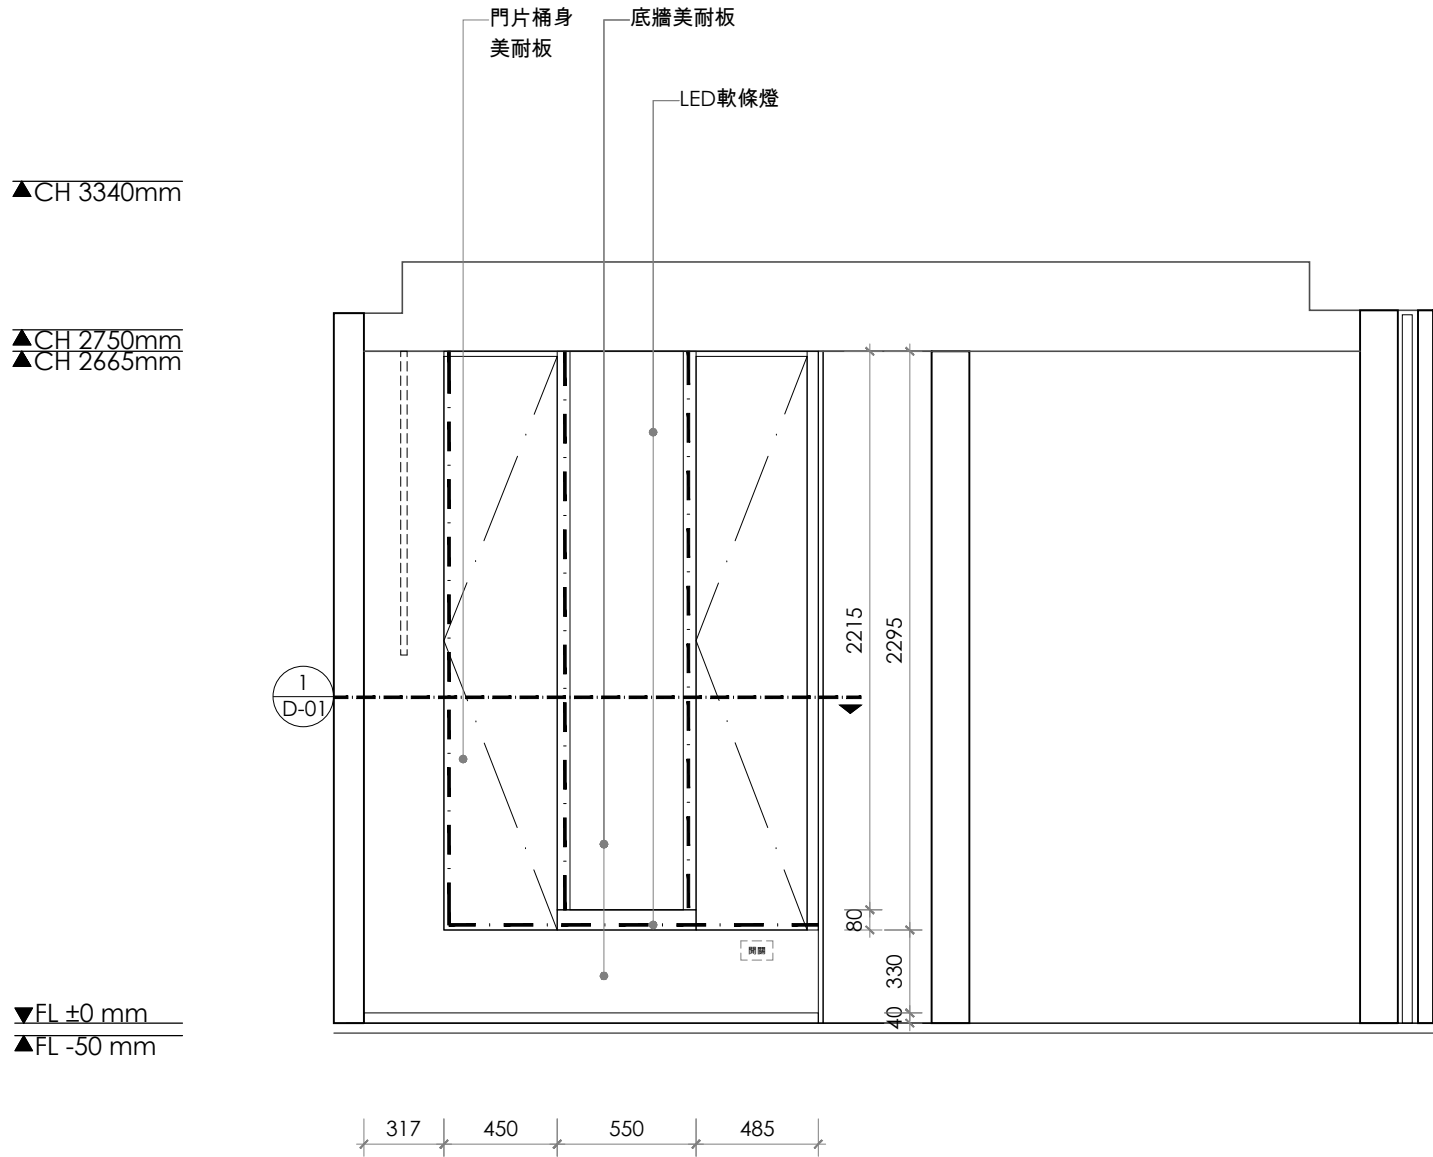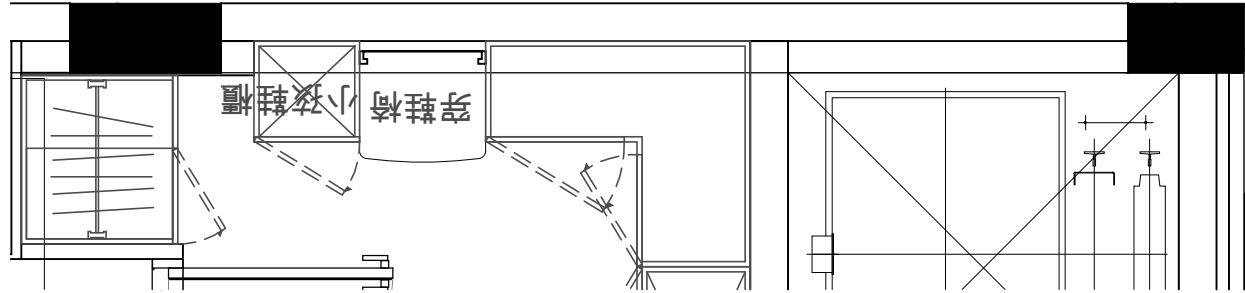

1
E-06

ELEVATION

Scale=1:30

Revision

APPROVAL/核准

設計者:	建築師:
業主:	

備註:

- 圖面標註尺寸僅供參考，施作均以現場放樣檢討之。
- 圖面標註尺寸、材料及文字敘述因版本不同之差異，均以圖章簽認日期之最近為準。
- 電腦圖檔除由合約訂定外，均不得以任何方式外流。
- 圖面所示均為本公司所擁有之智慧財產，切勿以任何方式複製修改。



MULA DECO

▲ 3F, N.26, Ln.290, Guangfu S. Rd., Taipei.
☎ 886-2-2546-3258
☎ 886-2-2546-3257
✉ Guido@muladeco.com

Project / 案名

林口雲品薇閣姚宅


Sheet Title / 圖名
B1F

立面圖

Date / 日期	Scale / 比例
8/10/2026	1/30cm
Designer / 設計	Approval / 核准
MONICA LIN	
Job No / 業務編號	Drawn By / 繪圖
00000	GUIDO
Dwg No.	Page No.

E-06

77

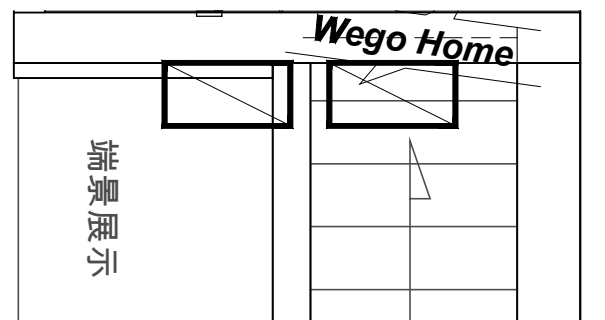

▲CH 2750mm
▲CH 2665mm

1
E-07

Scale=1:30

Revision




設計者:	建築師:
業主:	

- a. 圖面標註尺寸僅供參考，施作均以現場放樣檢討之。
- b. 圖面標註尺寸、材料及文字敘述因版本不同之差異，均以圖章簽認日期之最近為準。
- c. 電腦圖檔除由合約訂定外，均不得以任何方式外流。
- d. 圖面所示均為本公司所擁有之智慧財產，切勿以任何方式複製修改。



立面圖

Date / 日期	Scale / 比例
8/10/2026	1/30cm
Designer / 設計	Approval / 核准
MONICA LIN	
Job No / 業務編號	Drawn By / 繪圖
00000	GUIDO
Dwg No.	Page No.
E-07	78

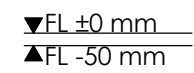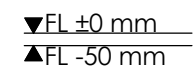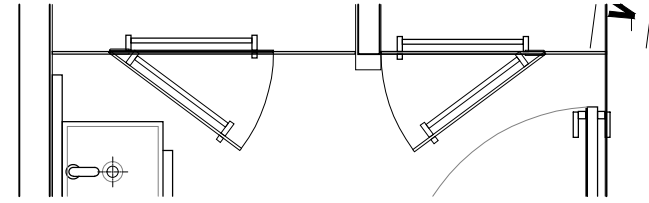[illegible]

設計者:	建築師:
業主:	

3. 圖面標註尺寸僅供參考，施作均以現場放樣檢討之。



4. 圖面標註尺寸、材料及文字敘述因版本不同之差異，均以出圖章簽認日期之圖章為準。

5. 電腦圖檔除由合約訂定外，均不得以任何方式外流。

6. 圖面所示均為本公司所擁有之智慧財產，切勿以任何方式複製修改。





Date / 日期	Scale / 比例
8/10/2026	1/30cm
Designer / 設計	Approval / 核准
MONICA LIN	
Job No / 業務編號	Drawn By / 繪圖
00000	GUIDO
Dwg No.	Page No.
E-08	79

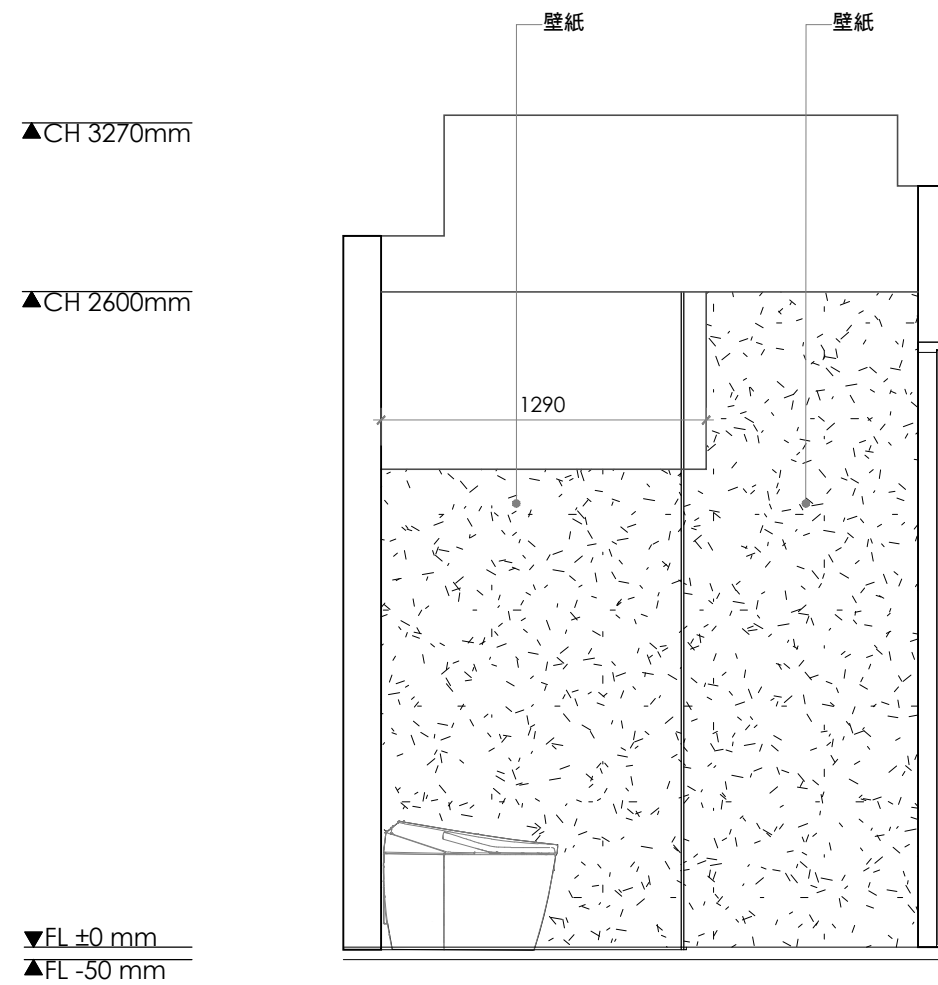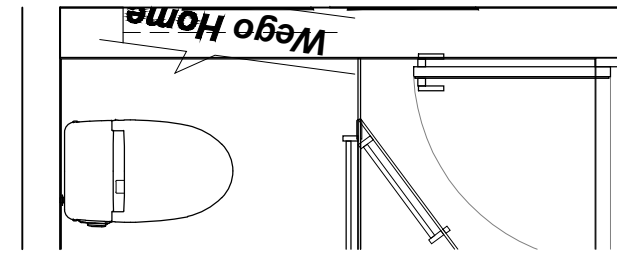

Scale=1:30

E-09 80

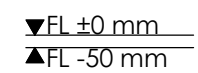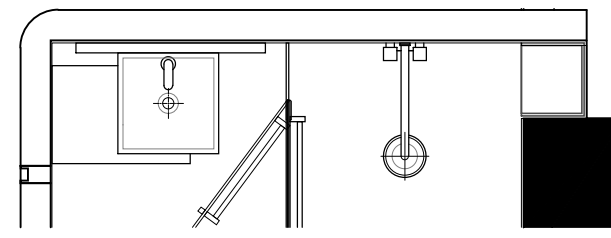

2 ELEVATION
E-10 Scale=1:30

[illegible]

設計者:	建築師:
業主:	

備註:

- ①.圖面標註尺寸僅供參考，施作均以現場放樣檢討之。
- ②.圖面標註尺寸、材料及文字敘述因版本不同之差異，均以出圖章簽認日期之最近為準。
- ③.電腦圖檔除由合約訂定外，均不得以任何方式外流。
- ④.圖面所示均為本公司所擁有之智慧財產，切勿以任何方式複製修改。



MULA DECO
A 3F, N.26, Ln.290, Guangfu S. Rd., Taipei.
T 886-2-2546-3258
F 886-2-2546-3257
E Guido@muladeco.com

Project / 案名


林口雲品薇閣姚宅

Sheet Title / 圖名
B1F

立面圖

Date / 日期	Scale / 比例
8/10/2026	1/30cm
Designer / 設計	Approval / 核准
MONICA LIN	
Job No / 案牘編號	Drawn By / 繪圖
00000	GUIDO
Dwg No.	Page No.

E-10 81

 

投影機

—led鋁槽燈

—led壁紙出電源

▲CH 3340mm

▲CH 2750mm
▲CH 2665mm




600 | 1100

006

▼FL ±0 mm

▲FL -50 mm

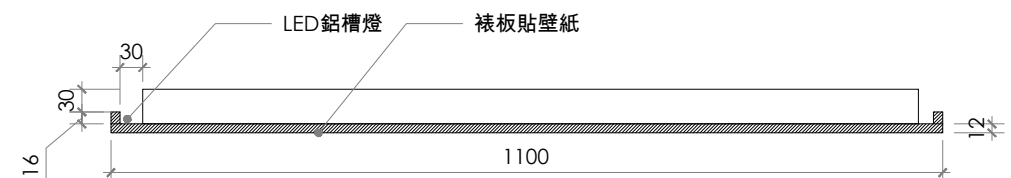

DETAIL

S 1:10

C

1
E-11

ELEVATION

Scale=1:30

Revision

APPROVAL/核准	
設計者:	建築師:
業主:	

備註:

- 4. 圖面標註尺寸僅供參考，施作均以現場放樣檢討之。
- 5. 圖面標註尺寸、材料及文字敘述因版本不同之差異，均以出圖章簽認日期之最近為準。
- 6. 電腦圖檔除由合約訂定外，均不得以任何方式外流。
- 7. 圖面所示均為本公司所擁有之智慧財產，切勿以任何方式複製修改。



MULA DECO

A 3F, N.26, Ln.290, Guangfu S. Rd., Taipei.

T 886-2-2546-3258

F 886-2-2546-3257

E Guido@muladeco.com

Project / 案名

林口雲品薇閣姚宅


Sheet Title / 圖名
B1F

立面圖

Date / 日期	Scale / 比例
8/10/2026	1/30cm
Designer / 設計	Approval / 核准
MONICA LIN	
Job No / 案卷編號	Drawn By / 繪圖
00000	GUIDO
Dwn No	Page No

E-11


32

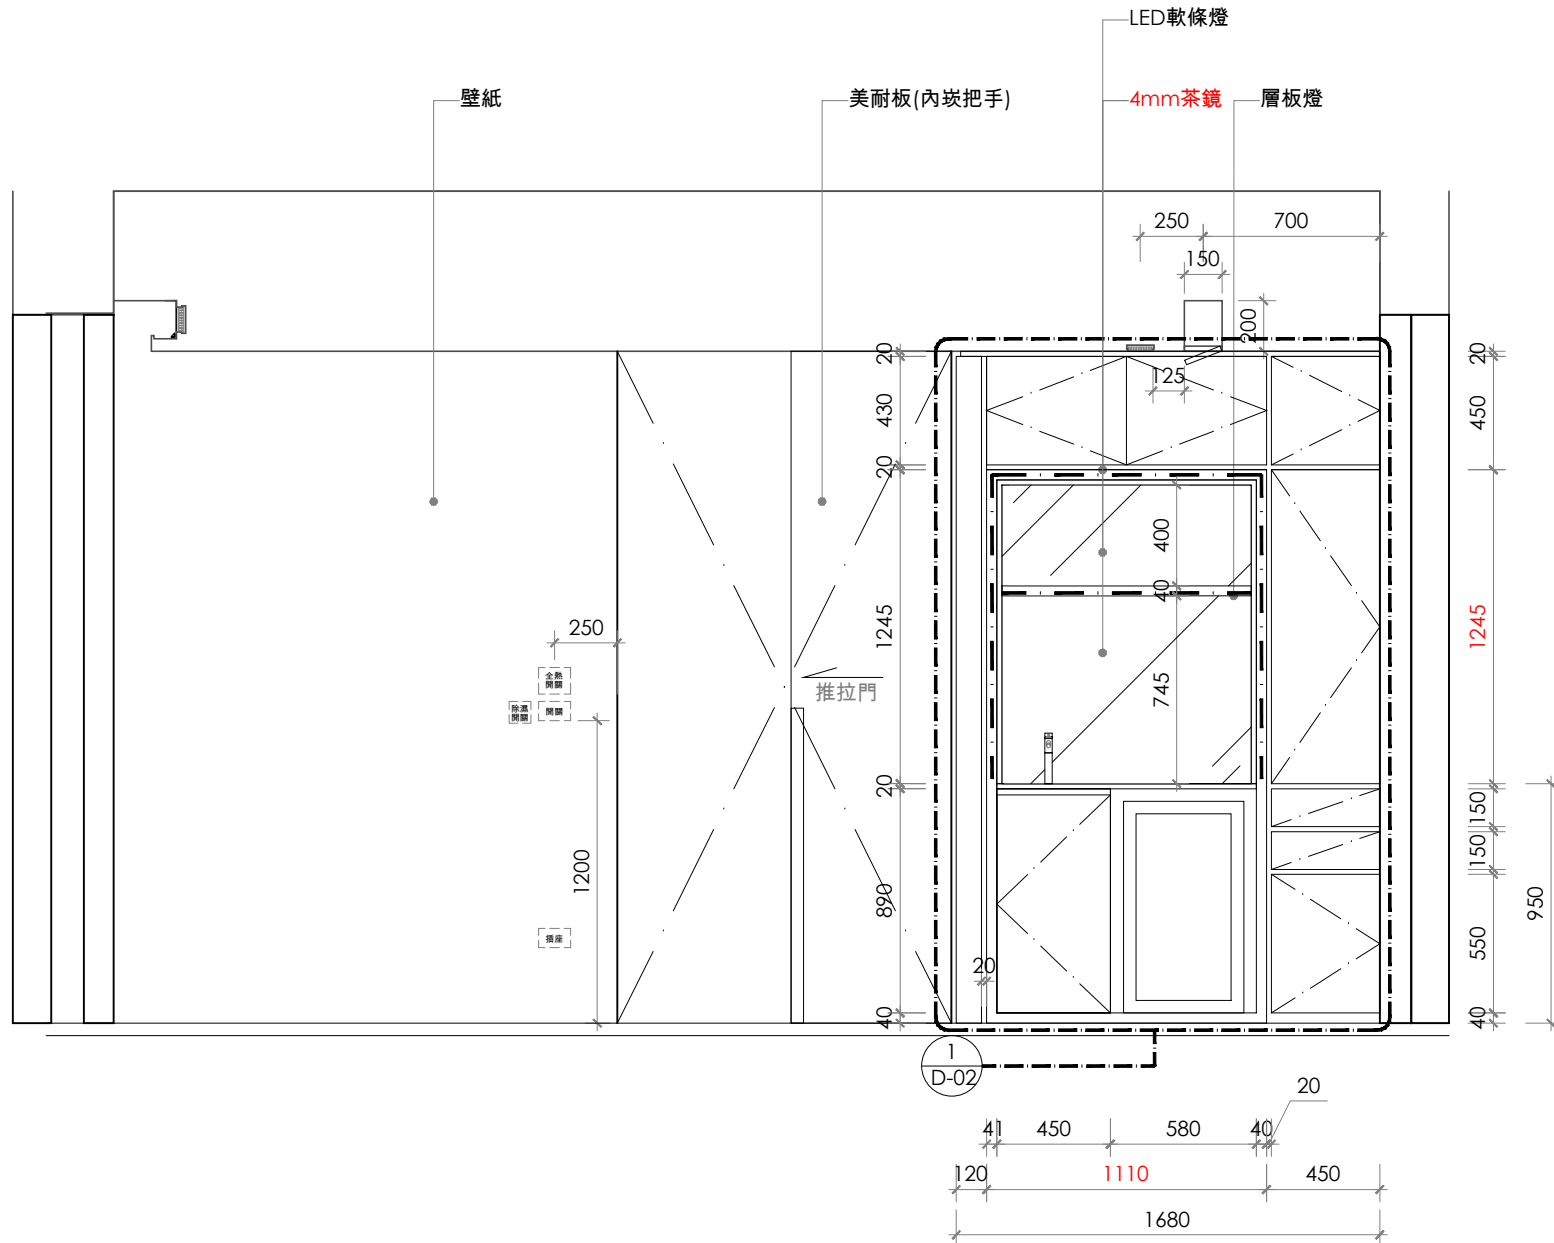

▼FL ±0 mm
▲FL -50 mm

Scale=1:30

E-12 83

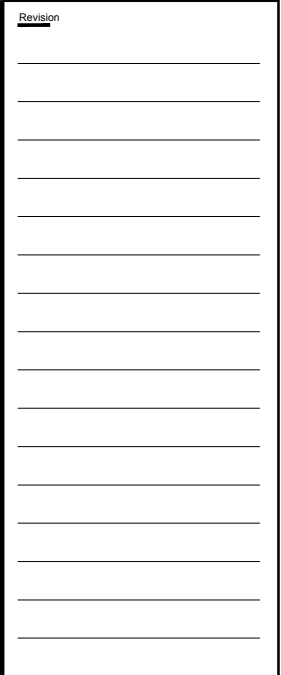

APPROVAL/核准

設計者:	建築師:
業主:	

葡註:

- 3. 圖面標註尺寸僅供參考，施作均以現場放樣檢討之。
- 4. 圖面標註尺寸、材料及文字敘述因版本不同之差異，均以出圖章簽認日期之最近為準。
- 5. 電腦圖檔除由合約訂定外，均不得以任何方式外流。
- 6. 圖面所示均為本公司所擁有之智慧財產，切勿以任何方式複製修改。



MULA DECO

A 3F, N.26, Ln.290, Guangfu S. Rd., Taipei.
T 886-2-2546-3258
F 886-2-2546-3257
E Guido@muladeco.com



Project / 案名

林口雲品薇閣姚宅

Sheet Title / 圖名
B1F

立面圖


Date / 日期	Scale / 比例
8/10/2026	1/30cm
Designer / 設計	Approval / 核准
MONICA LIN	
Job No / 業務編號	Drawn By / 繪圖
00000	GUIDO
Dwg No.	Page No.
E-12	84

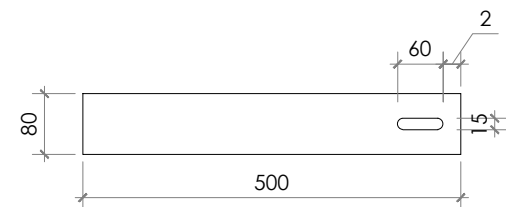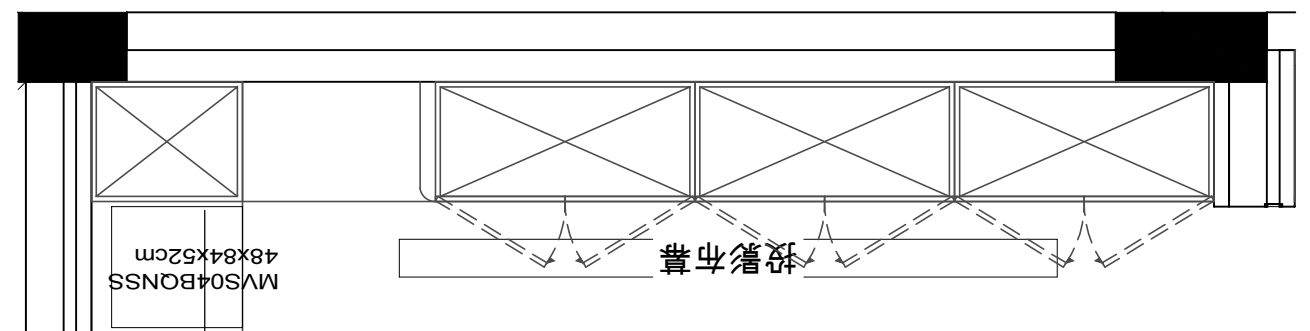

▲CH 3340mm

▲CH 2750mm
▲CH 2665mm


▼FL ±0 mm
▲FL -50 mm

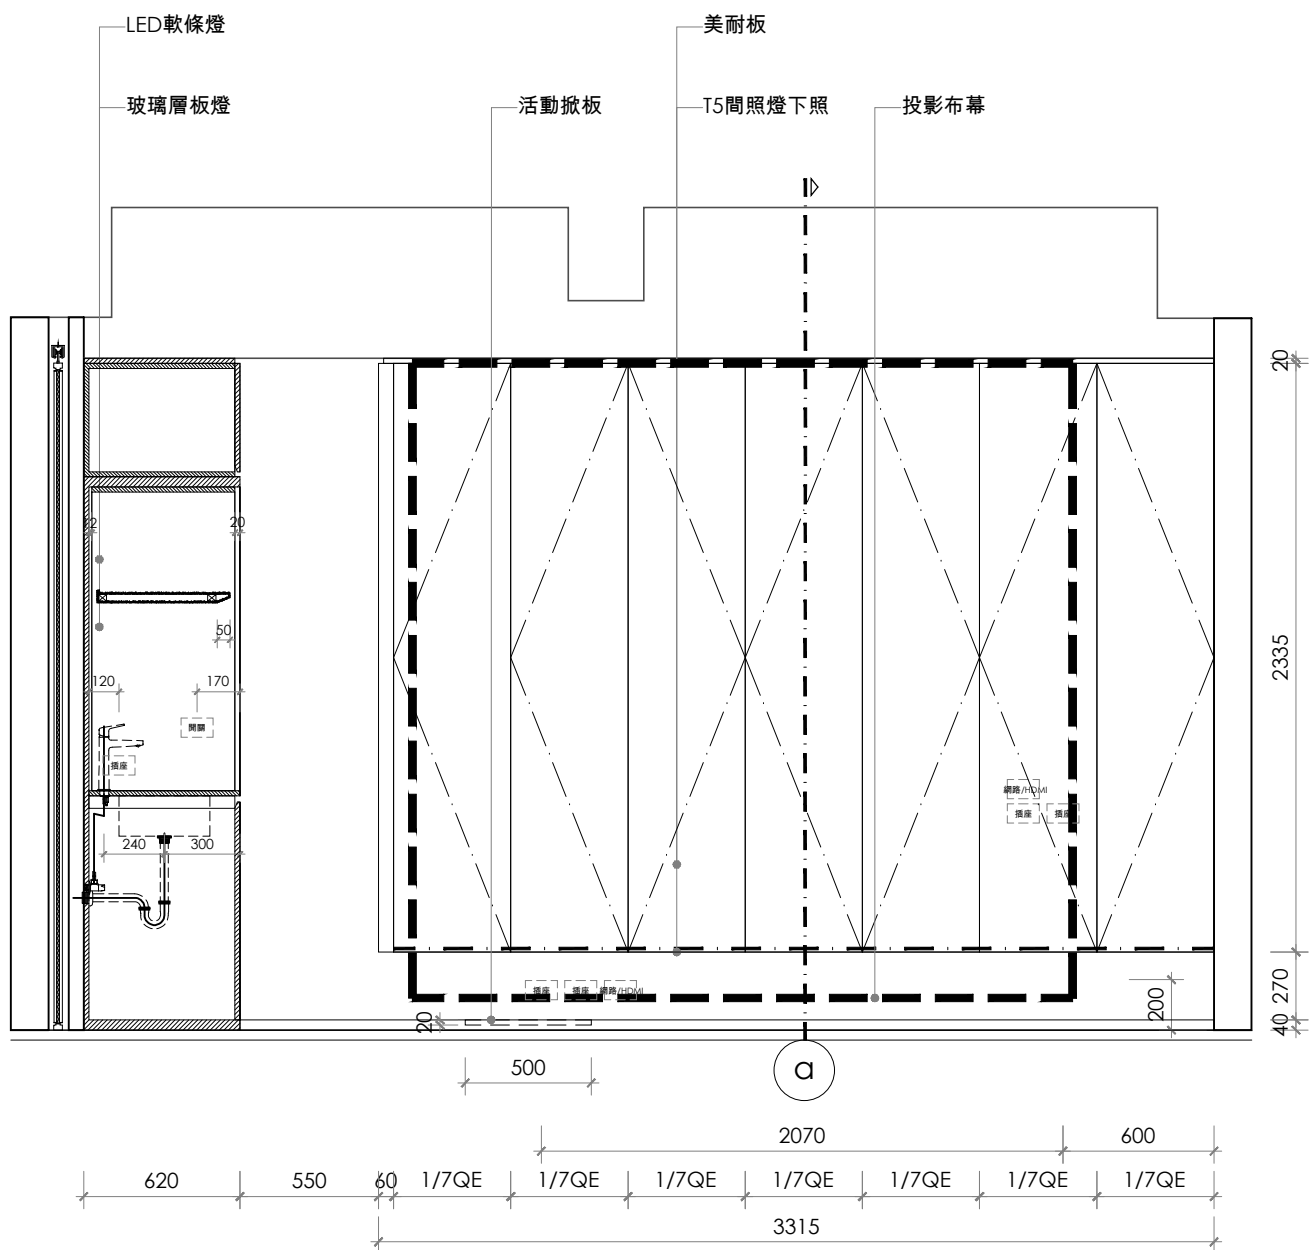

1
E-13

ELEVATION

Scale=1:30

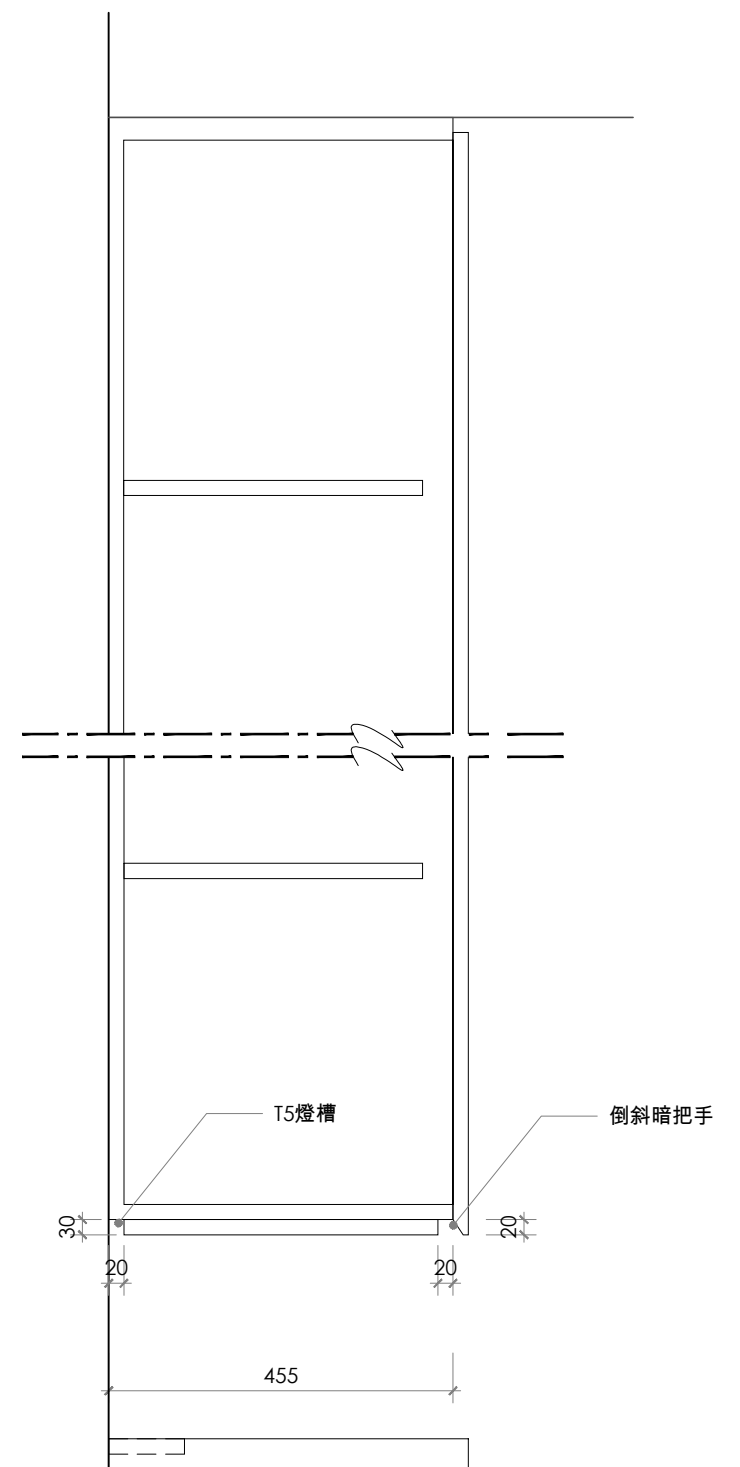

a

DETAIL

S 1:10

Revision

APPROVAL/核准

設計者:	建築師:
業主:	

備註:

- 圖面標註尺寸僅供參考，施作均以現場放樣檢討之。
- 圖面標註尺寸、材料及文字敘述因版本不同之差異，均以圖章簽認日期之最近為準。
- 電腦圖檔除由合約訂定外，均不得以任何方式外流。
- 圖面所示均為本公司所擁有之智慧財產，切勿以任何方式複製修改。



MULA DECO

▲ 3F, N.26, Ln.290, Guangfu S. Rd., Taipei.
☎ 886-2-2546-3258
☎ 886-2-2546-3257
✉ Guido@muladeco.com

Project / 案名

林口雲品薇閣姚宅

Sheet Title / 圖名


B1F

立面圖

Date / 日期	Scale / 比例
8/10/2026	1/30cm
Designer / 設計	Approval / 核准
MONICA LIN	
Job No / 業務編號	Drawn By / 繪圖
00000	GUIDO
Dwg No.	Page No.

E-13

85

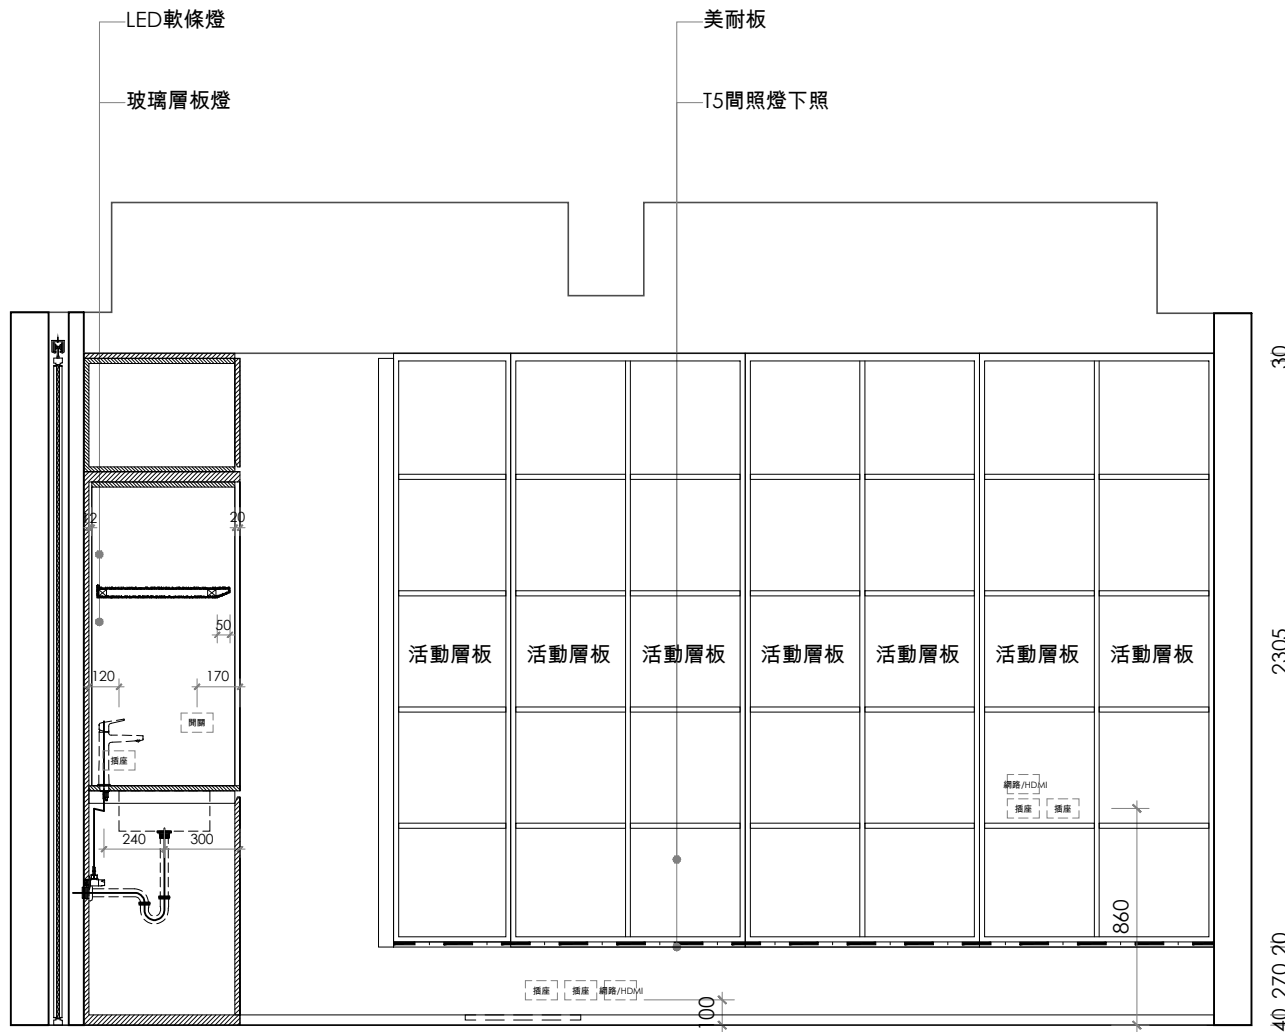

▲CH 2750mm
▲CH 2665mm

Timeline diagram for the 2019-2020 period. The timeline starts at 60, followed by a segment of 465. After a gap, there are three segments of $\frac{1}{3}QE$ separated by gaps. The total duration is 3315. The timeline ends with a segment of 2070, followed by a gap, and then a segment of 600.

●圖面標註尺寸僅供參考，施作均以現場放樣檢討之。



●圖面標註尺寸、材料及文字敘述因版本不同之差異，均以出圖章簽日期之最近為準。


●電腦圖檔除由合約訂定外，均不得以任何方式外流。

●圖面所示均為本公司所擁有之智慧財產，切勿以任何方式複製修改。




36

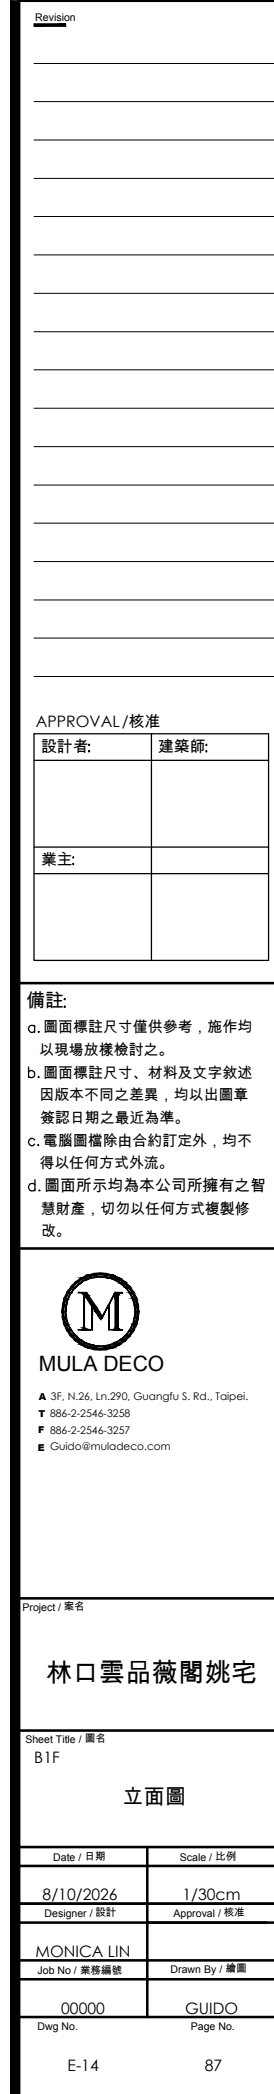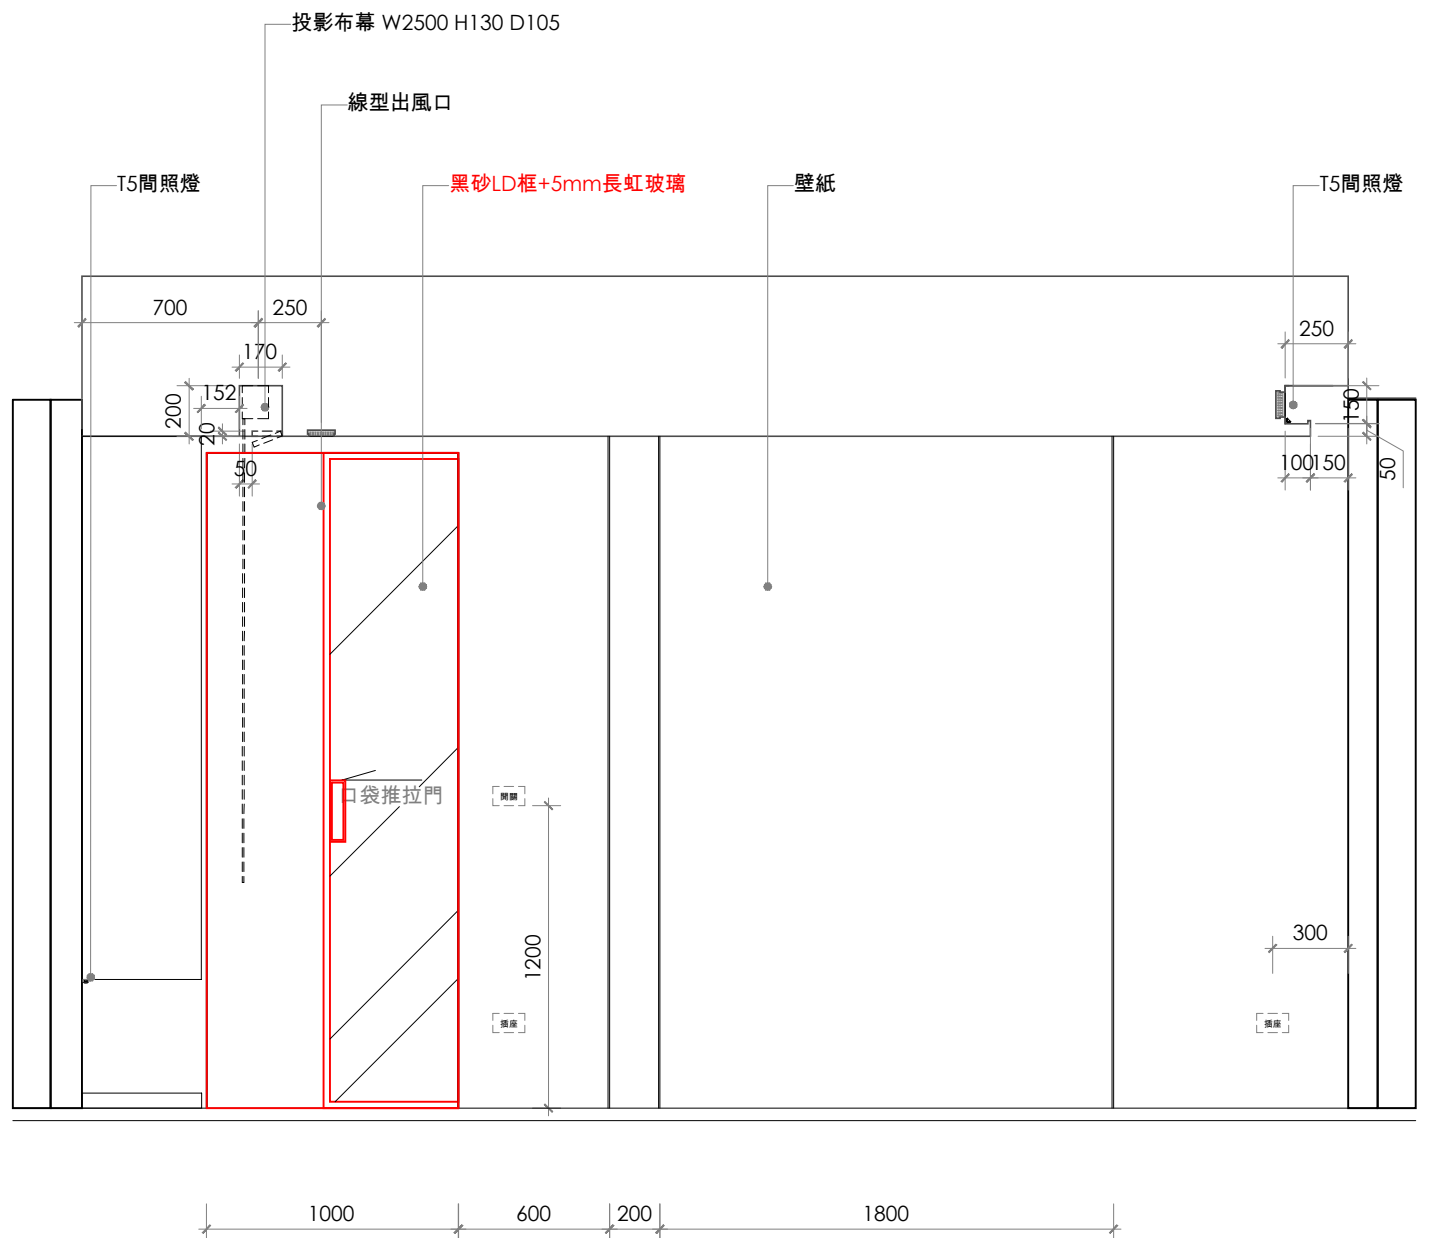

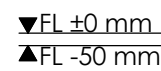

Scale=1:30

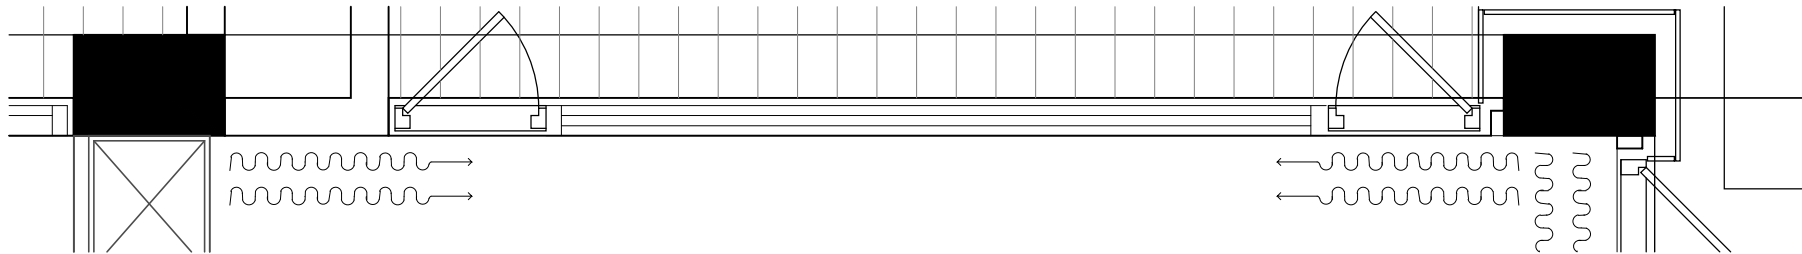


▲CH 3381mm

▲CH 2920mm

▲CH 2740mm

▼FL ±0 mm

▲FL -50 mm

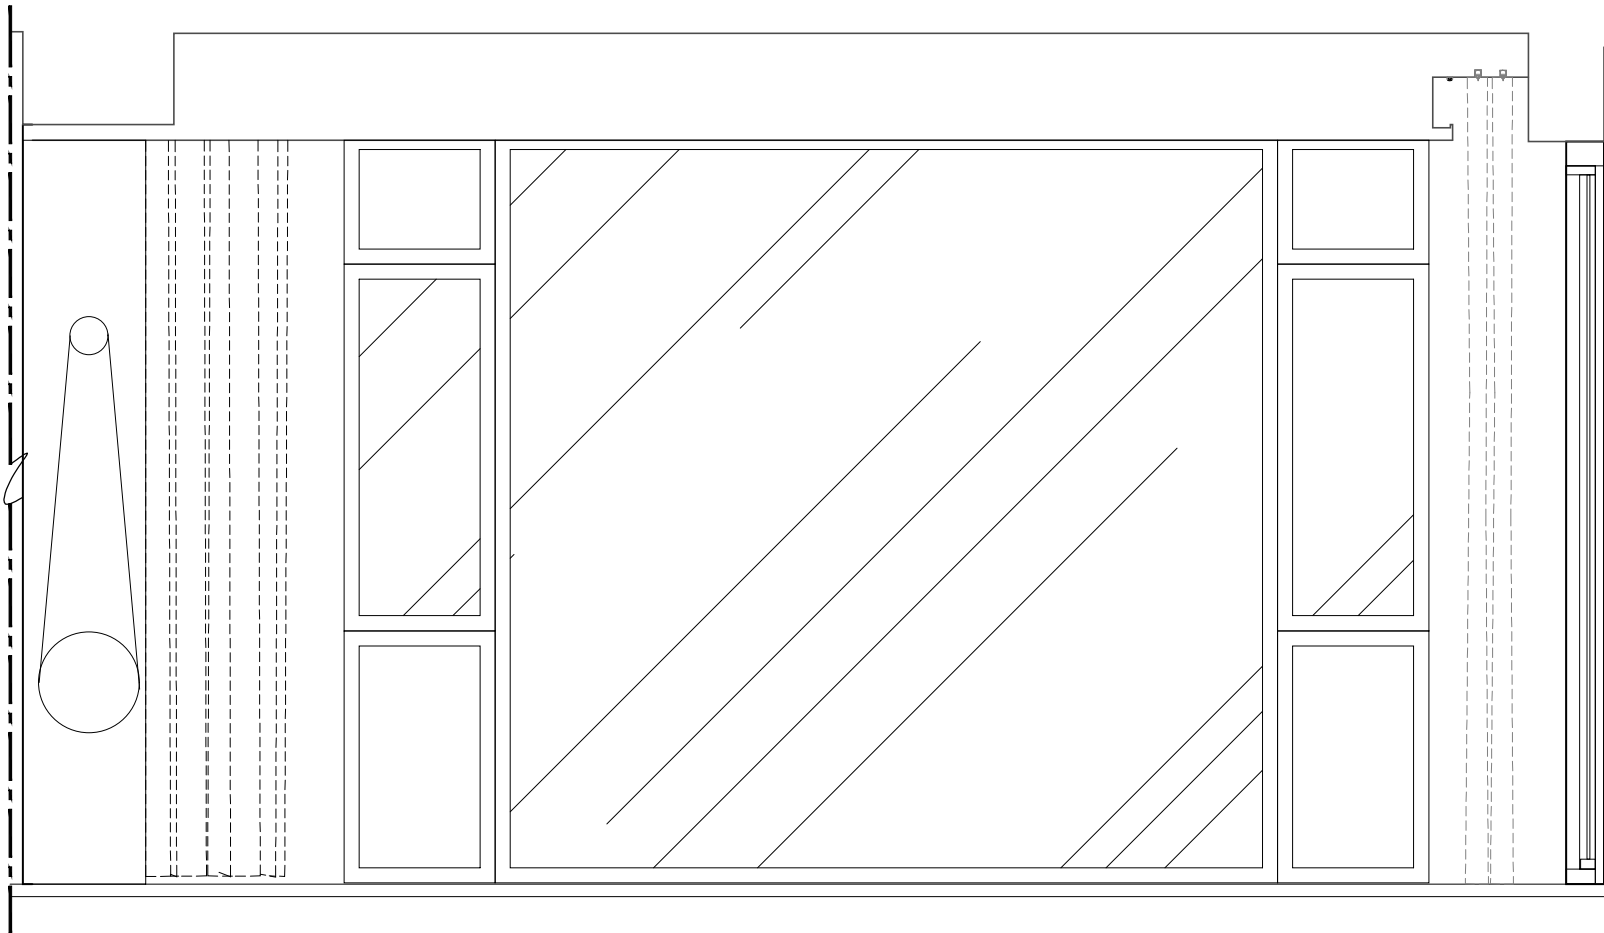

1
E-16

ELEVATION

Scale=1:30

Revision

APPROVAL/核准

設計者:	建築師:
業主:	

備註:

- a. 圖面標註尺寸僅供參考，施作均以現場放樣檢討之。
- b. 圖面標註尺寸、材料及文字敘述因版本不同之差異，均以出圖章簽認日期之最近為準。
- c. 電腦圖檔除由合約訂定外，均不得以任何方式外流。
- d. 圖面所示均為本公司所擁有之智慧財產，切勿以任何方式複製修改。



MULA DECO

▲ 3F, N.26, Ln.290, Guangfu S. Rd., Taipei.
☎ 886-2-2546-3258
✉ 886-2-2546-3257
E Guido@muladeco.com

Project / 案名

林口雲品薇閣姚宅

Sheet Title / 圖名


1F

立面圖

Date / 日期	Scale / 比例
8/10/2026	1/30cm
Designer / 設計	Approval / 核准
MONICA LIN	
Job No / 業務編號	Drawn By / 繪圖
00000	GUIDO
Dwg No.	Page No.

E-16

89

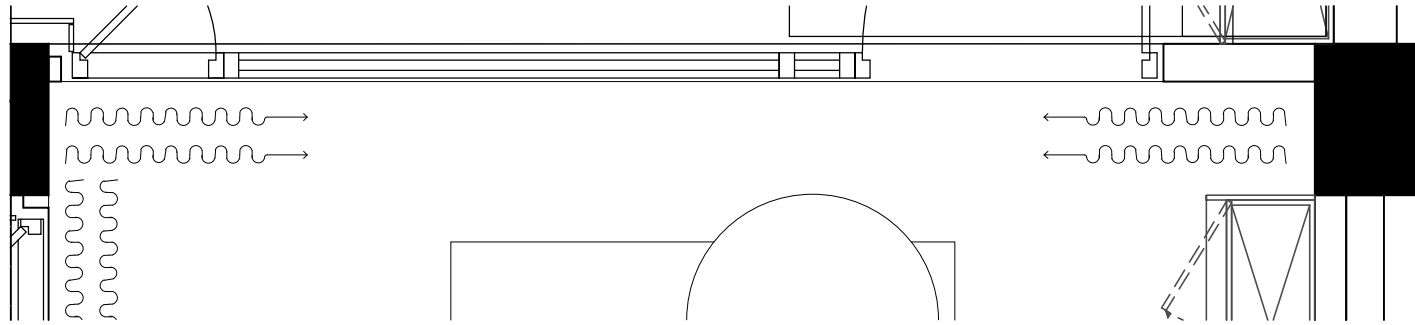

▲CH 3381mm


▲CH 2920mm

▲CH 2740mm

▼FL ±0 mm

▲FL -50 mm

LED軟條燈

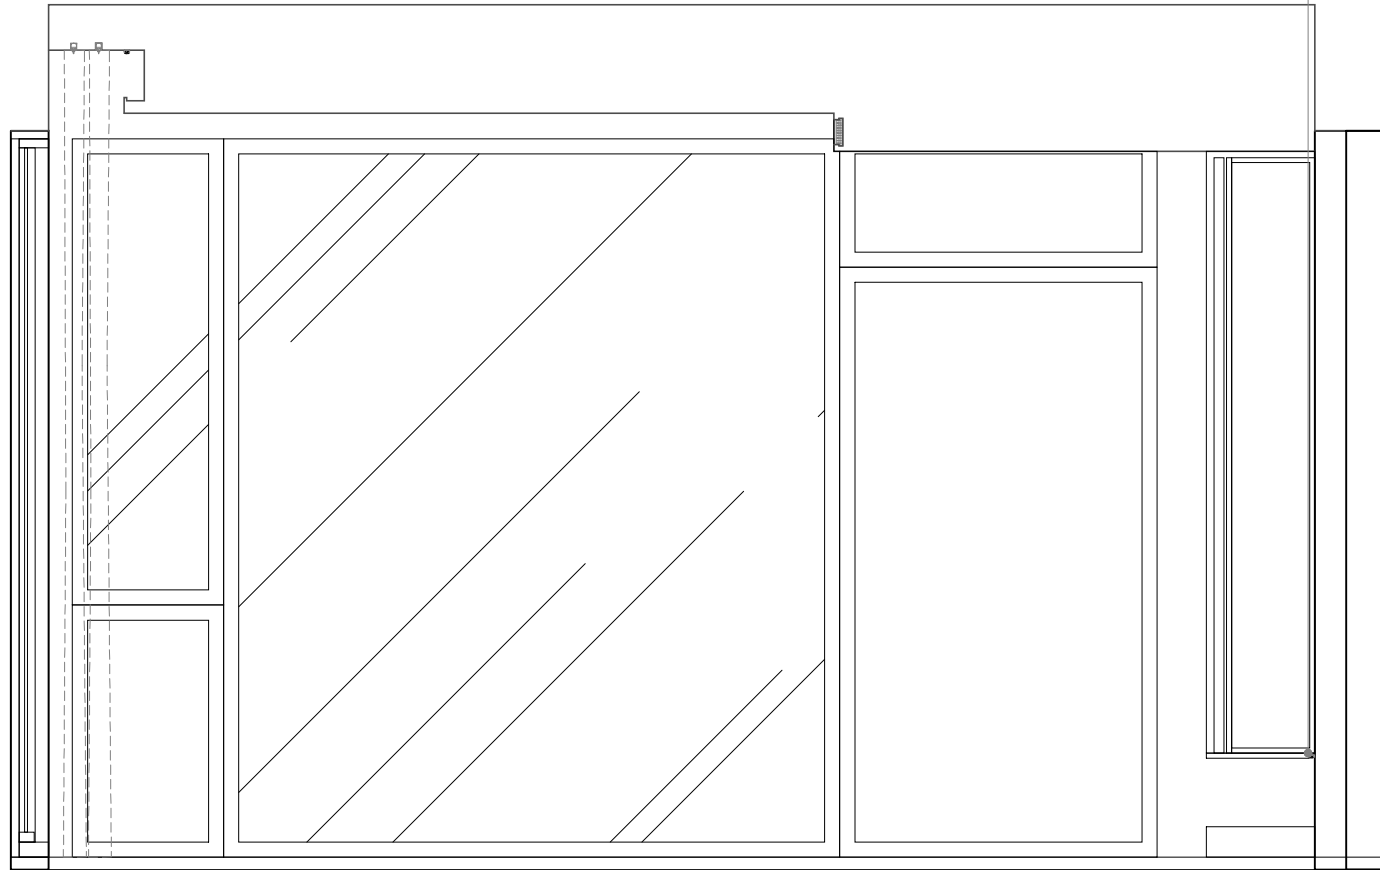

1
E-17

ELEVATION

Scale=1:30

Revision

APPROVAL/核准

設計者:	建築師:
業主:	

備註:

- a. 圖面標註尺寸僅供參考，施作均以現場放樣檢討之。
- b. 圖面標註尺寸、材料及文字敘述因版本不同之差異，均以出圖章簽認日期之最近為準。
- c. 電腦圖檔除由合約訂定外，均不得以任何方式外流。
- d. 圖面所示均為本公司所擁有之智慧財產，切勿以任何方式複製修改。



MULA DECO

▲ 3F, N.26, Ln.290, Guangfu S. Rd., Taipei.
☎ 886-2-2546-3258
☎ 886-2-2546-3257
✉ Guido@muladeco.com

Project / 案名

林口雲品薇閣姚宅

Sheet Title / 圖名



1F

立面圖

Date / 日期	Scale / 比例
8/10/2026	1/30cm
Designer / 設計	Approval / 核准
MONICA LIN	
Job No / 業務編號	Drawn By / 繪圖
00000	GUIDO
Dwg No.	Page No.

E-17

90

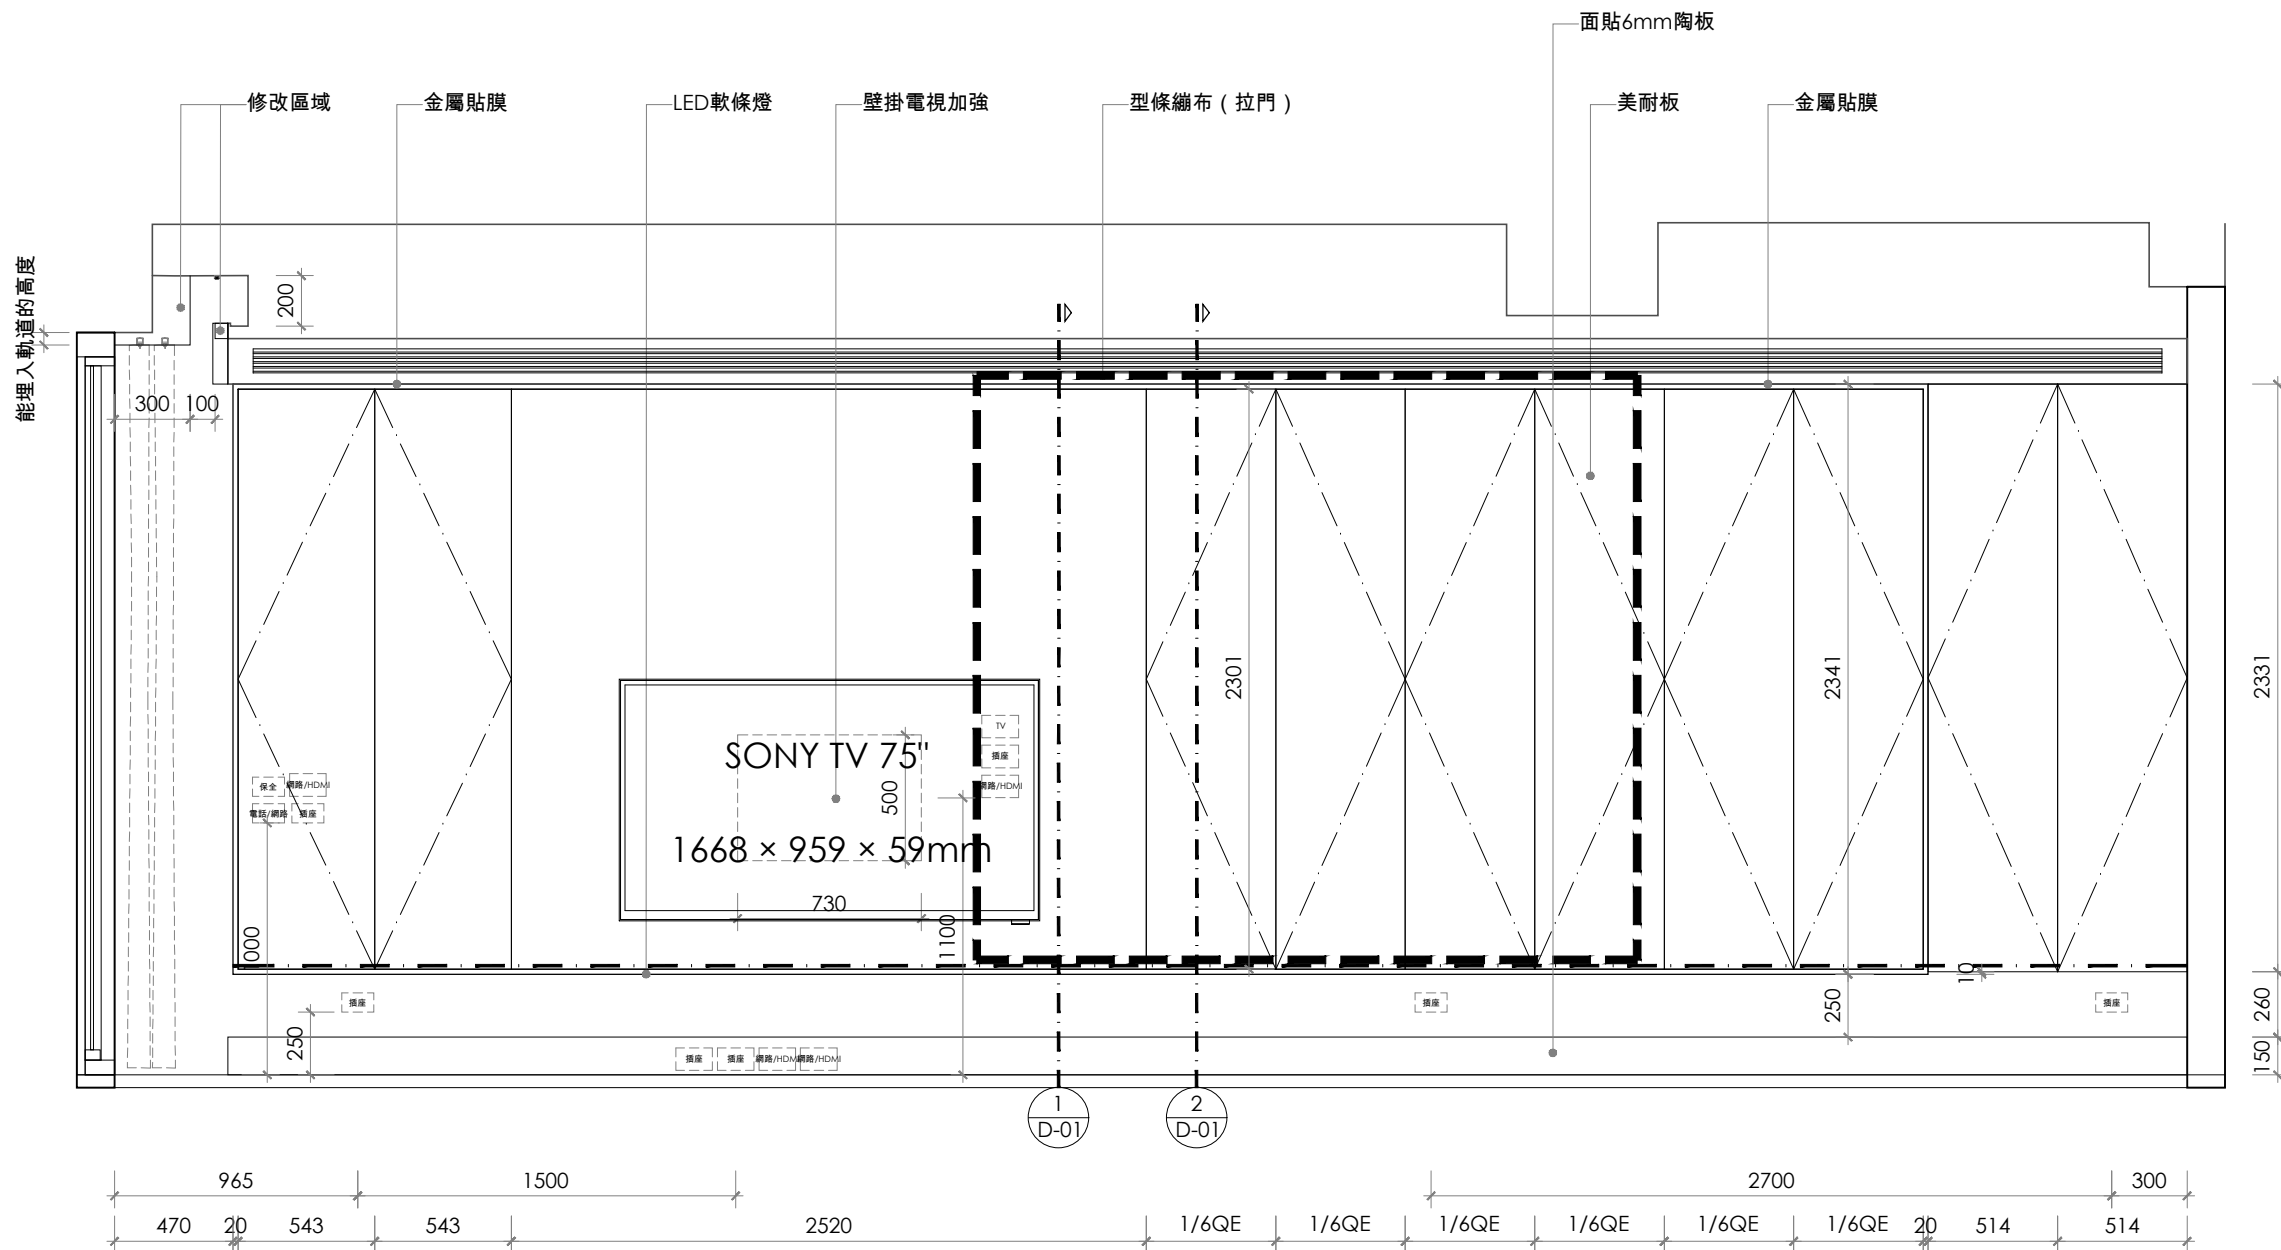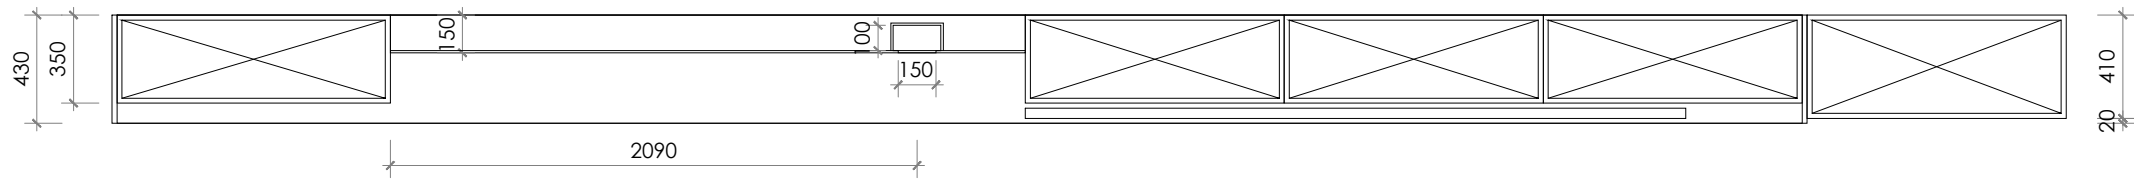

1
E-18

ELEVATION

Scale=1:30

Revision

APPROVAL/核准

設計者:	建築師:
業主:	

備註:

- 圖面標註尺寸僅供參考，施作均以現場放樣檢討之。
- 圖面標註尺寸、材料及文字敘述因版本不同之差異，均以出圖章簽認日期之最近為準。
- 電腦圖檔除由合約訂定外，均不得以任何方式外流。
- 圖面所示均為本公司所擁有之智慧財產，切勿以任何方式複製修改。



MULA DECO

▲ 3F, N.26, Ln.290, Guangfu S. Rd., Taipei.
☎ 886-2-2546-3258
☎ 886-2-2546-3257
✉ Guido@muladeco.com

Project / 案名

林口雲品薇閣姚宅

Sheet Title / 圖名
1F

立面圖

Date / 日期	Scale / 比例
8/10/2026	1/30cm
Designer / 設計	Approval / 核准
MONICA LIN	
Job No / 業務編號	Drawn By / 繪圖
00000	GUIDO
Dwg No.	Page No.
E-18	91

▲FL -50 mm

設計者:	建築師:
業主:	

葡註:

- 圖面標註尺寸僅供參考，施作均以現場放樣檢討之。
- 圖面標註尺寸、材料及文字敘述因版本不同之差異，均以出圖章簽認日期之最近為準。
- 電腦圖檔除由合約訂定外，均不得以任何方式外流。
- 圖面所示均為本公司所擁有之智慧財產，切勿以任何方式複製修改。



MULA DECO

A 3F, N.26, Ln.290, Guangfu S. Rd., Taipei.

T 886-2-2546-3258
F 884-2-2544-3257

E Guido@muladeco.com


Project / 案名

林口雲品薇閣姚宅

Sheet Title / 圖名

立面圖


Date / 日期	Scale / 比例
8/10/2026	1/30cm
Designer / 設計	Approval / 核准
MONICA LIN	
Job No / 業務編號	Drawn By / 繪圖
00000	GUIDO
Dwn No	Page No

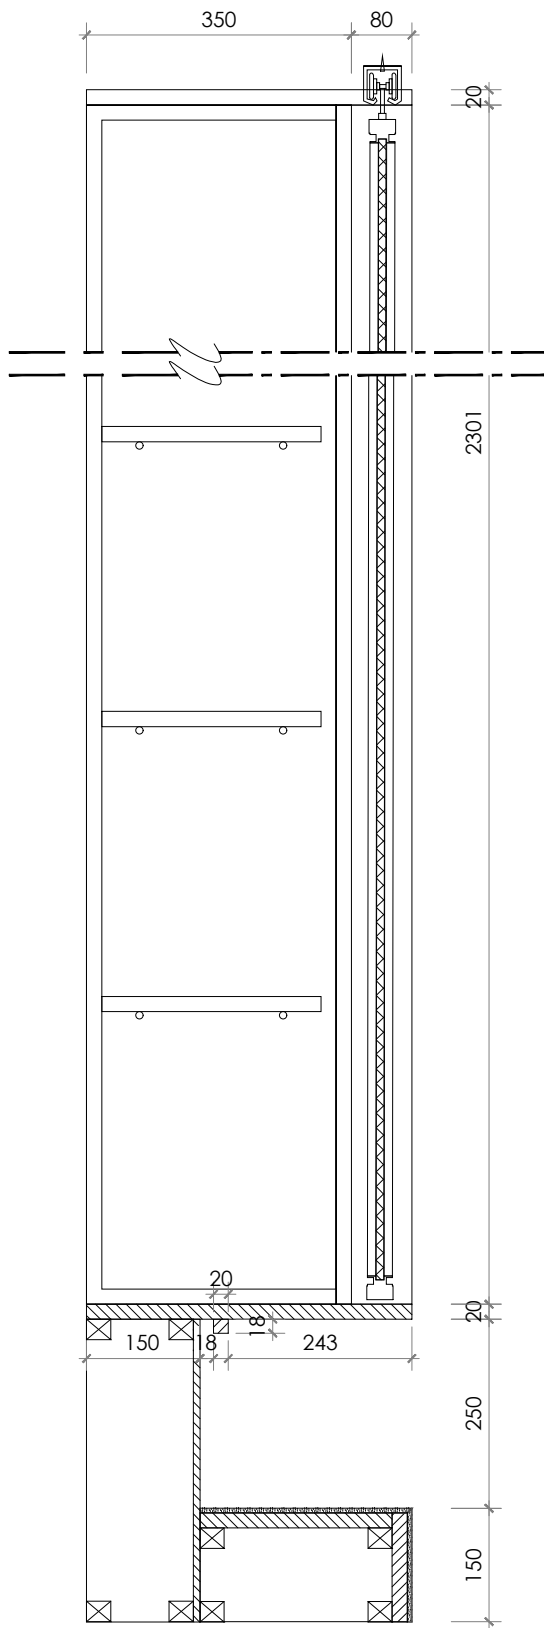

1
D-01

DETAIL



S 1:10

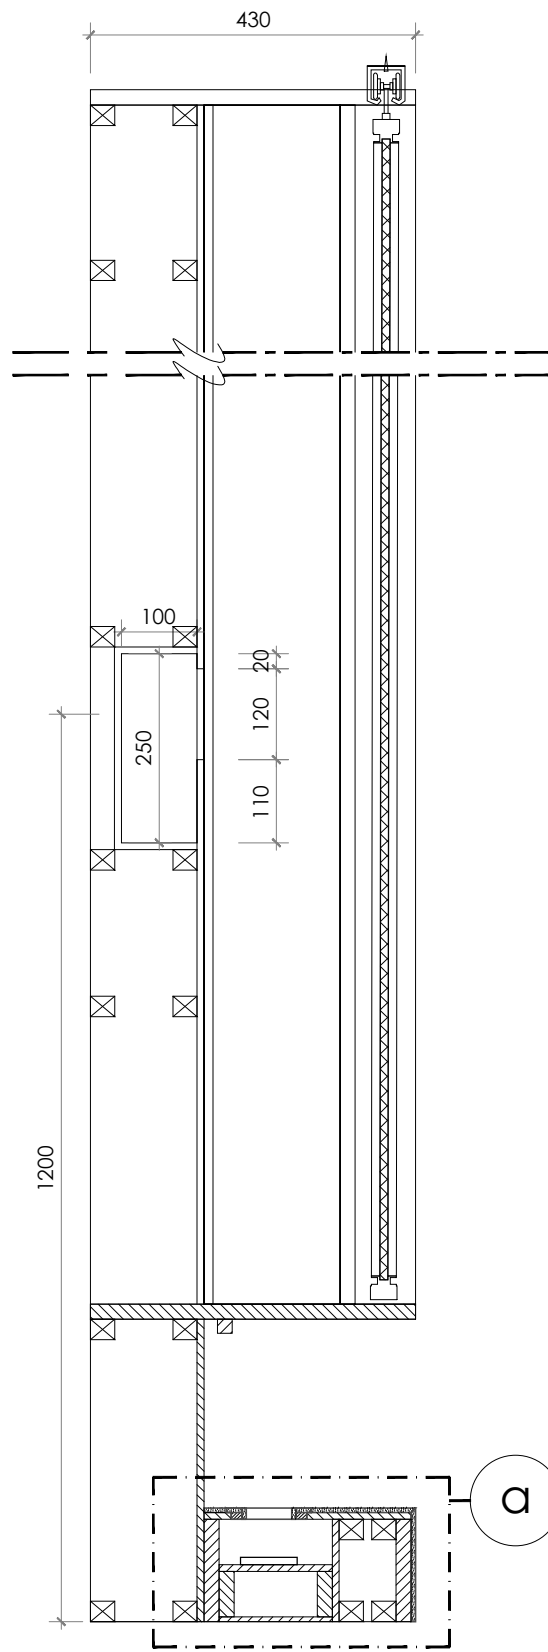

2
D-01

DETAIL


S 1:10

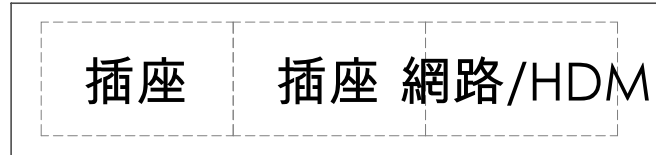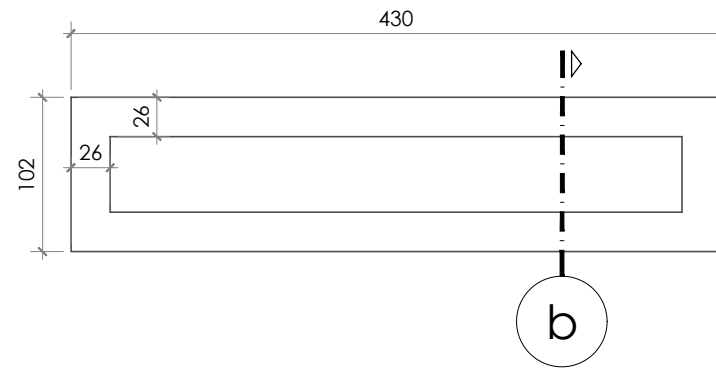

3
D-01

DETAIL


S 1:5

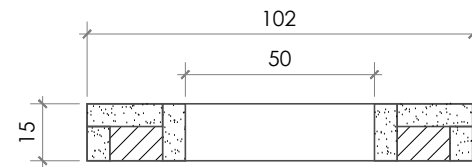

b

DETAIL

S 1:2

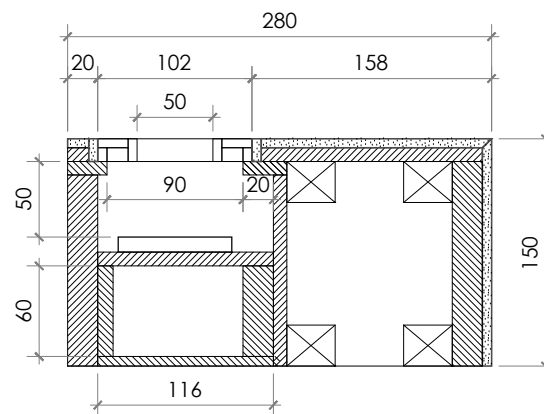

a

DETAIL

S 1:5

Revision

APPROVAL/核准

設計者:	建築師:
業主:	

備註:

- 圖面標註尺寸僅供參考，施作均以現場放樣檢討之。
- 圖面標註尺寸、材料及文字敘述因版本不同之差異，均以出圖章簽認日期之最近為準。
- 電腦圖檔除由合約訂定外，均不得以任何方式外流。
- 圖面所示均為本公司所擁有之智慧財產，切勿以任何方式複製修改。



MULA DECO

▲ 3F, N.26, Ln.290, Guangfu S. Rd., Taipei.
☎ 886-2-2546-3258
☎ 886-2-2546-3257
✉ Guido@muladeco.com

Project / 案名

林口雲品薇閣姚宅

Sheet Title / 圖名



1F

立面圖

Date / 日期	Scale / 比例
8/10/2026	1/30cm
Designer / 設計	Approval / 核准
MONICA LIN	
Job No / 業務編號	Drawn By / 繪圖
00000	GUIDO
Dwg No.	Page No.

E-18

93

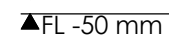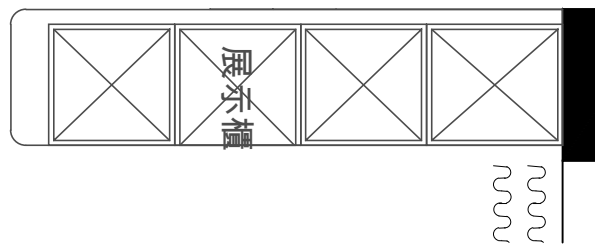

Scale=1:30

A 3F, N.26, Ln.290, Guangfu S. Rd., Taipei.
T 886-2-2546-3258
F 886-2-2546-3257
E Guido@muladeco.com




Project / 案名

林口雲品薇閣姚宅

Sheet Title / 圖名
1F

立面圖

E-19

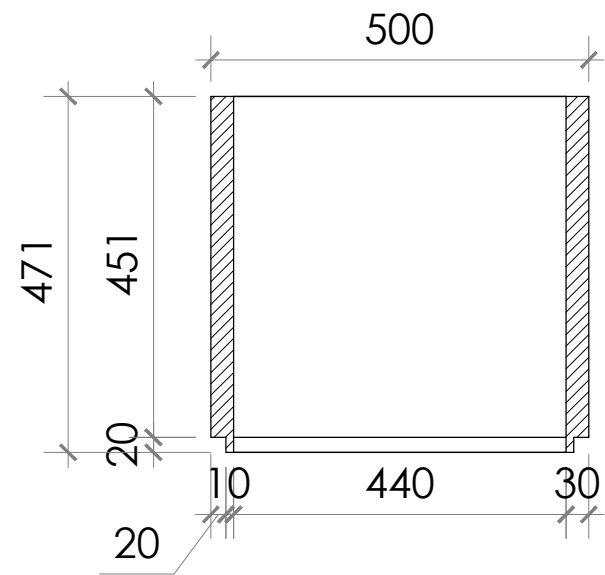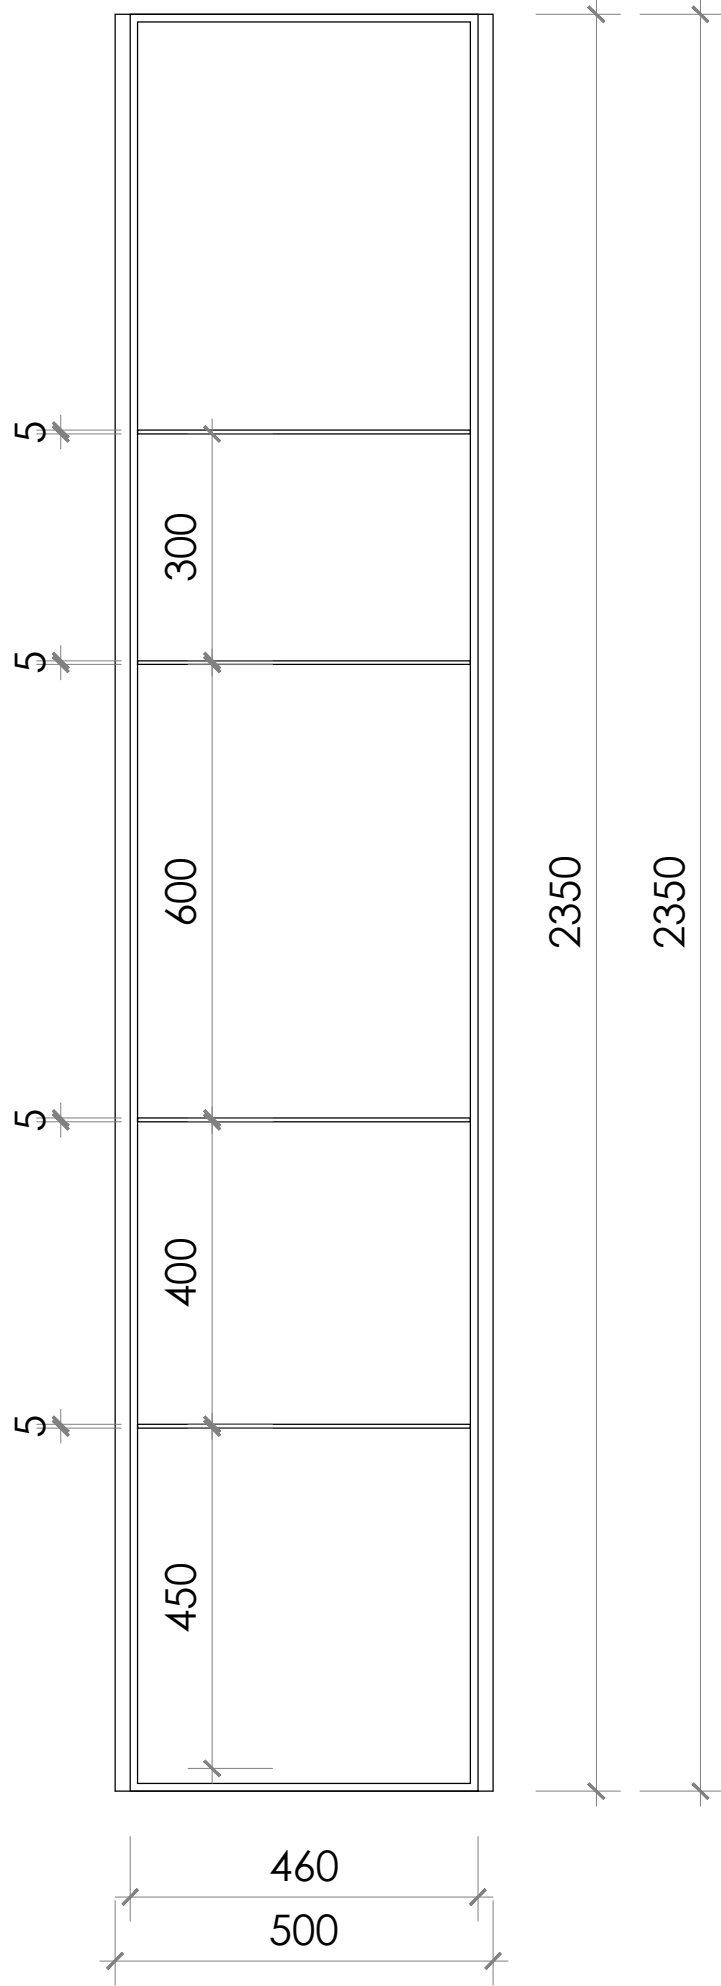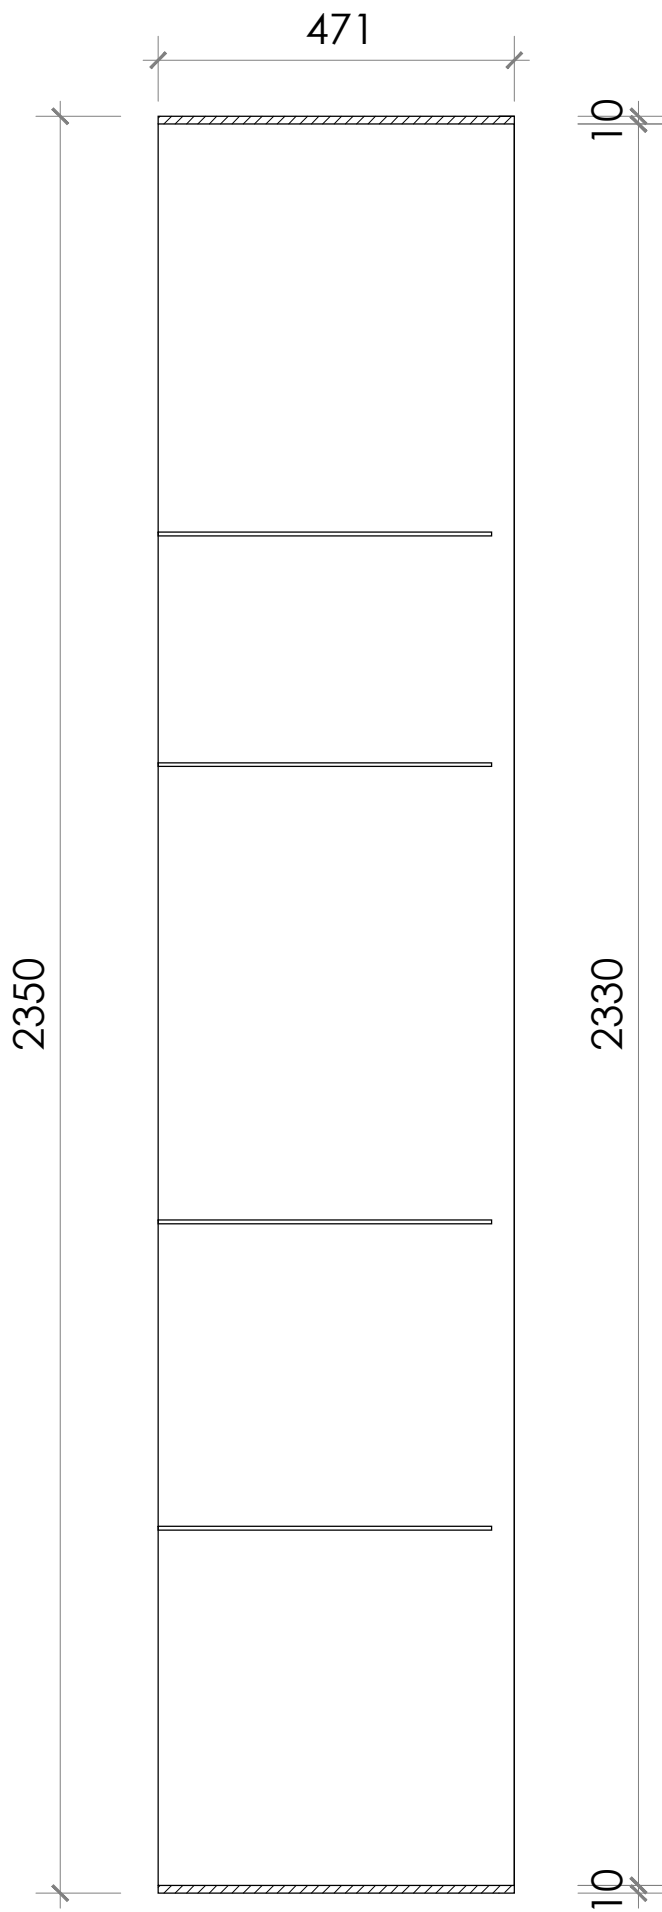

Revision

APPROVAL/核准

設計者:	建築師:
業主:	

備註:

a. 圖面標註尺寸僅供參考，施作均以現場放樣檢討之。

b. 圖面標註尺寸、材料及文字敘述因版本不同之差異，均以出圖章簽認日期之最近為準。

c. 電腦圖檔除由合約訂定外，均不得以任何方式外流。

d. 圖面所示均為本公司所擁有之智慧財產，切勿以任何方式複製修改。

M

MULA DECO

▲ 3F, N.26, Ln.290, Guangfu S. Rd., Taipei.

☎ 886-2-2546-3258

☎ 886-2-2546-3257

✉ Guido@muladeco.com

Project / 案名


林口雲品薇閣姚宅

Sheet Title / 圖名

1F

細部大樣圖



Date / 日期	Scale / 比例
8/10/2026	1/10cm
Designer / 設計	Approval / 核准
MONICA LIN	
Job No / 業務編號	Drawn By / 繪圖
00000	GUIDO
Dwg No.	Page No.
E-19	96

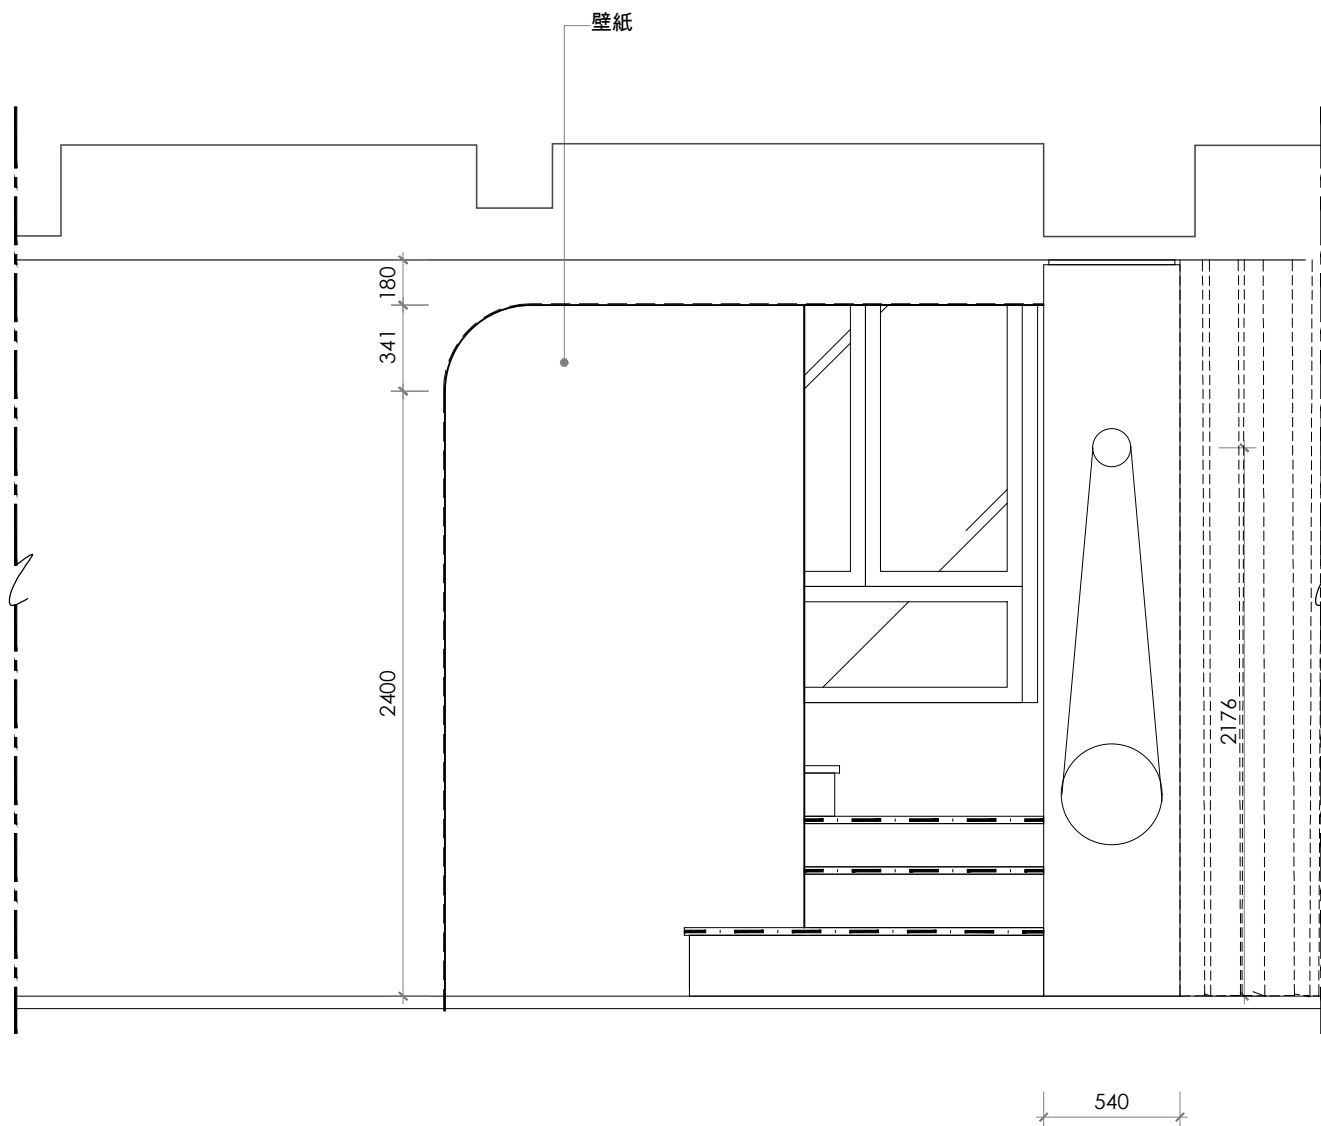

▲FL -50 mm

Scale=1:30

7

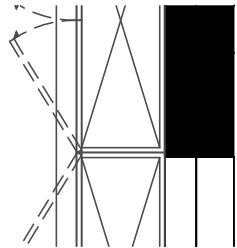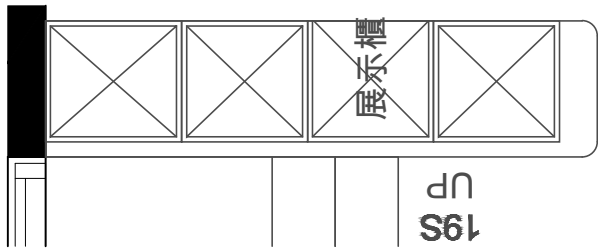


▲CH 3381mm

▲CH 2920mm

▲CH 2740mm

▼FL ±0 mm

▲FL -50 mm

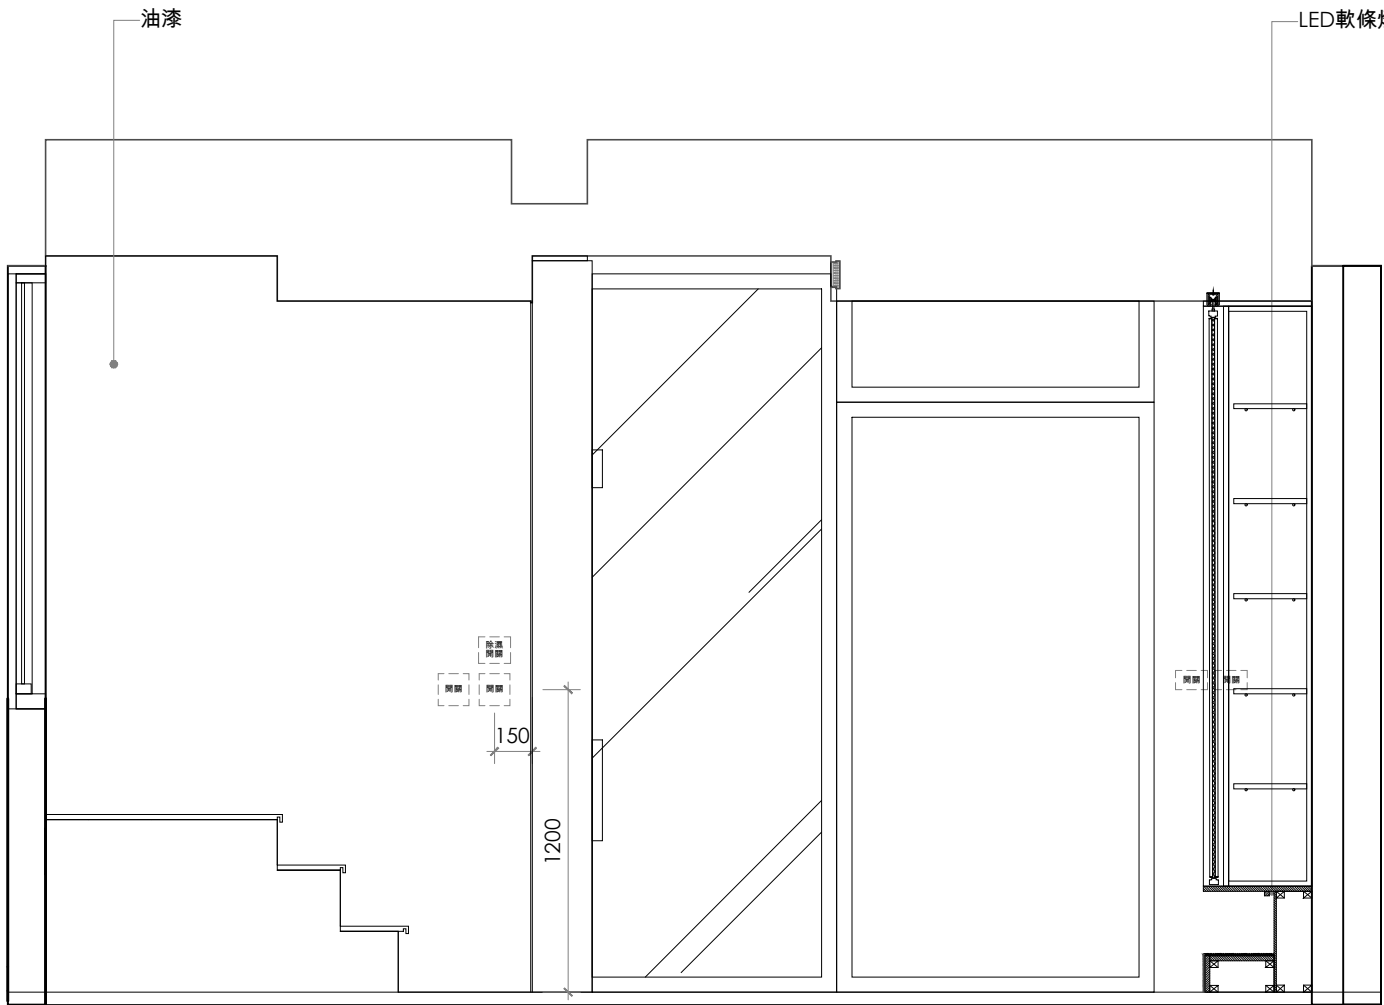

1
E-21

ELEVATION

Scale=1:30

Revision

APPROVAL/核准

設計者:	建築師:
業主:	

備註:

- 圖面標註尺寸僅供參考，施作均以現場放樣檢討之。
- 圖面標註尺寸、材料及文字敘述因版本不同之差異，均以出圖章簽認日期之最近為準。
- 電腦圖檔除由合約訂定外，均不得以任何方式外流。
- 圖面所示均為本公司所擁有之智慧財產，切勿以任何方式複製修改。



MULA DECO

▲ 3F, N.26, Ln.290, Guangfu S. Rd., Taipei.
☎ 886-2-2546-3258
☎ 886-2-2546-3257
✉ Guido@muladeco.com

Project / 案名

林口雲品薇閣姚宅


Sheet Title / 圖名
1F

立面圖

Date / 日期	Scale / 比例
8/10/2026	1/30cm
Designer / 設計	Approval / 核准
MONICA LIN	
Job No / 業務編號	Drawn By / 繪圖
00000	GUIDO
Dwg No.	Page No.

E-21

98

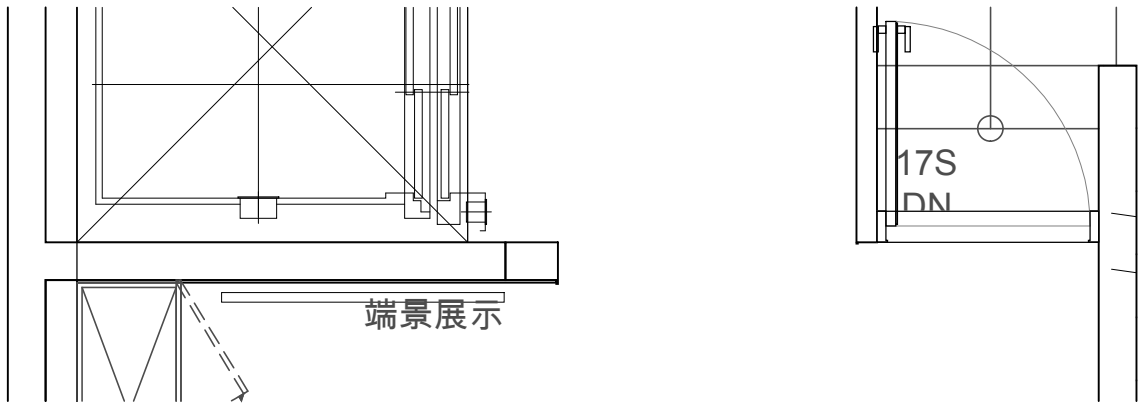


▲CH 3381mm

▲CH 2920mm

▲CH 2740mm

▼FL ±0 mm

▲FL -50 mm

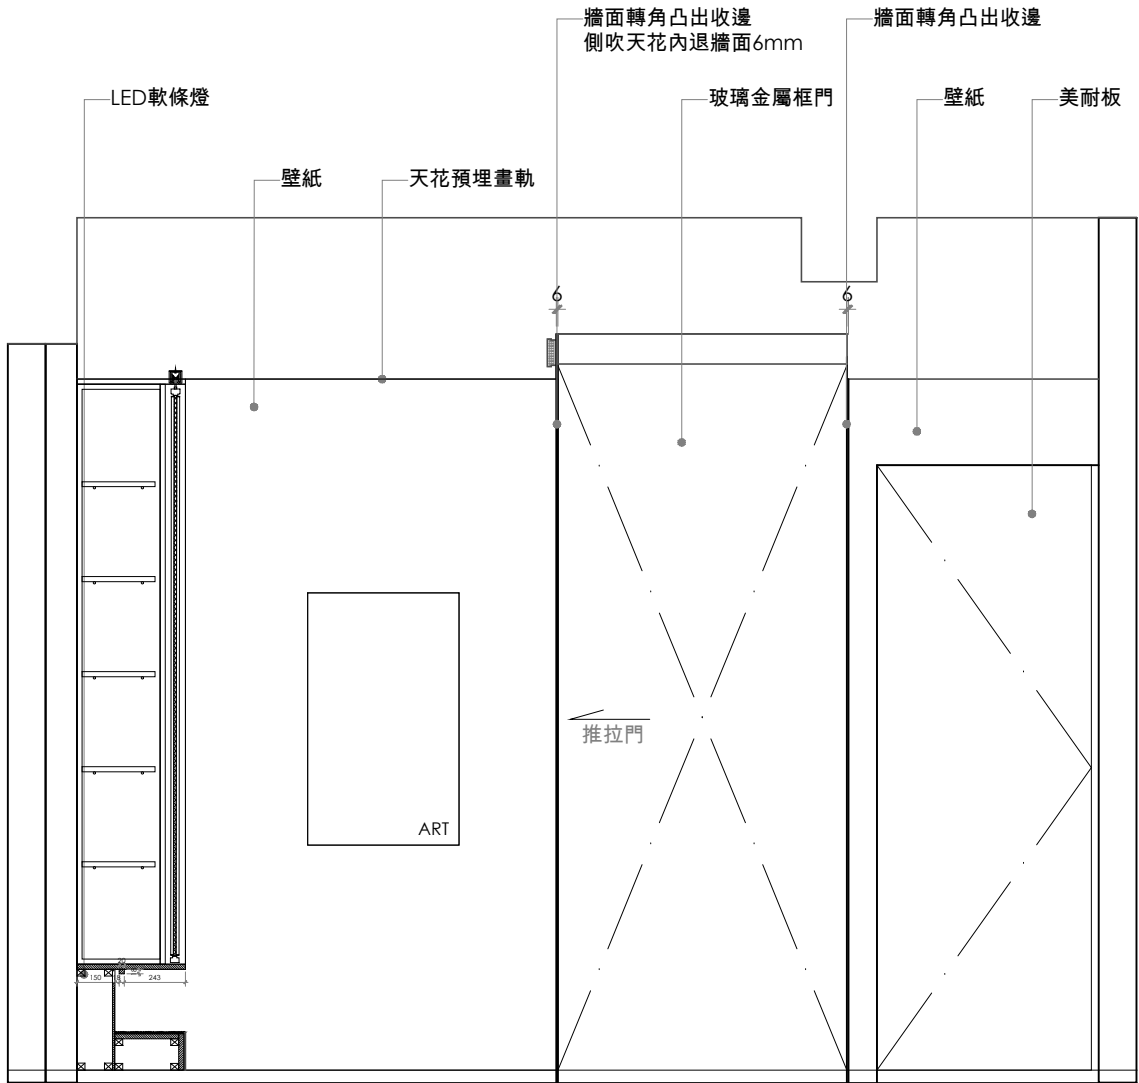

1
E-22

ELEVATION

Scale=1:30

Revision

APPROVAL/核准

設計者:	建築師:
業主:	

備註:

- 圖面標註尺寸僅供參考，施作均以現場放樣檢討之。
- 圖面標註尺寸、材料及文字敘述因版本不同之差異，均以出圖章簽認日期之最近為準。
- 電腦圖檔除由合約訂定外，均不得以任何方式外流。
- 圖面所示均為本公司所擁有之智慧財產，切勿以任何方式複製修改。



MULA DECO

▲ 3F, N.26, Ln.290, Guangfu S. Rd., Taipei.
☎ 886-2-2546-3258
☎ 886-2-2546-3257
✉ Guido@muladeco.com

Project / 案名

林口雲品薇閣姚宅


Sheet Title / 圖名
1F

立面圖

Date / 日期	Scale / 比例
8/10/2026	1/30cm
Designer / 設計	Approval / 核准
MONICA LIN	
Job No / 業務編號	Drawn By / 繪圖
00000	GUIDO
Dwg No.	Page No.

E-22

99

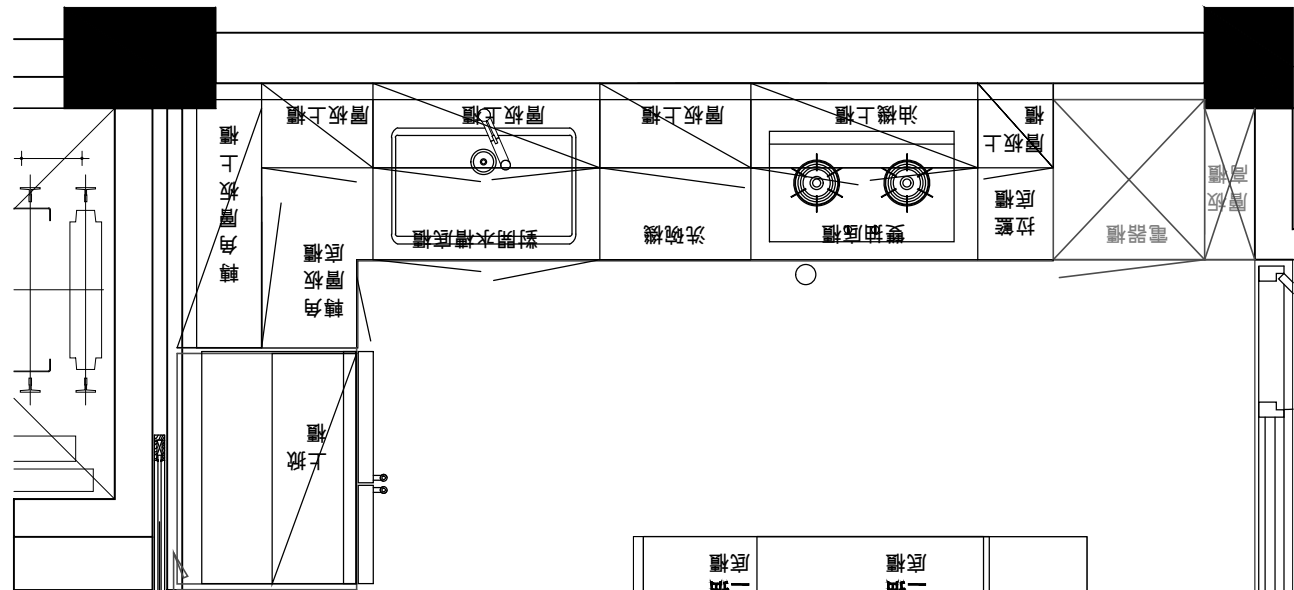


▲CH 3381mm

▲CH 2805mm

▲CH 2350mm

▼FL ±0 mm

▲FL -50 mm

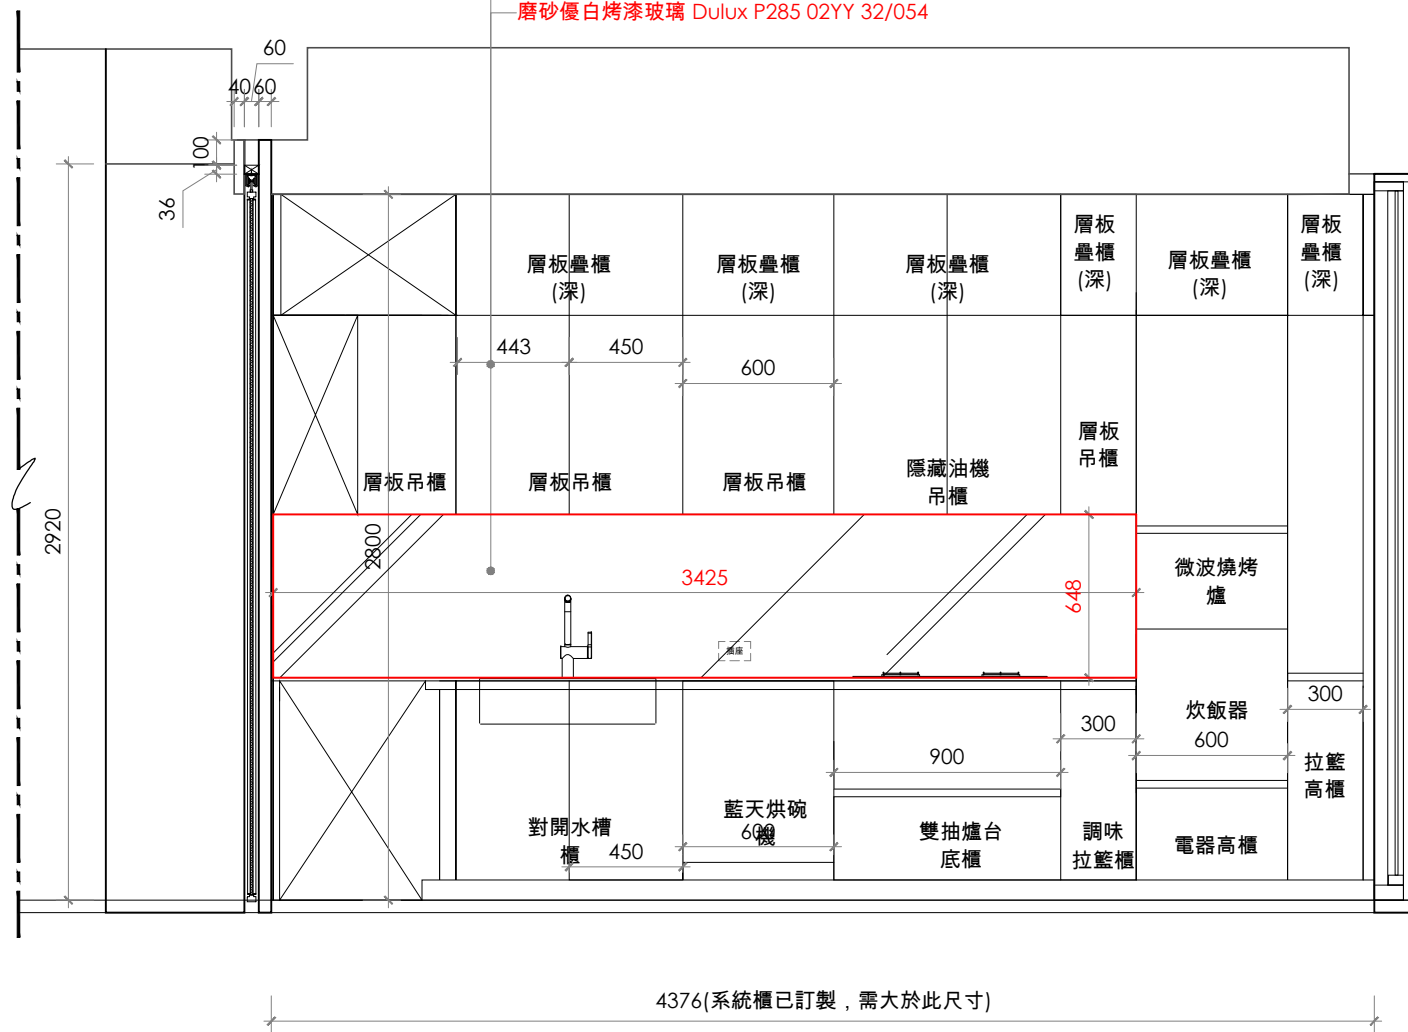

1
E-25

ELEVATION

Scale=1:30

Revision

APPROVAL/核准

設計者:	建築師:
業主:	

備註:

- 圖面標註尺寸僅供參考，施作均以現場放樣檢討之。
- 圖面標註尺寸、材料及文字敘述因版本不同之差異，均以出圖章簽認日期之最近為準。
- 電腦圖檔除由合約訂定外，均不得以任何方式外流。
- 圖面所示均為本公司所擁有之智慧財產，切勿以任何方式複製修改。



MULA DECO

▲ 3F, N.26, Ln.290, Guangfu S. Rd., Taipei.
☎ 886-2-2546-3258
✉ 886-2-2546-3257
E Guido@muladeco.com

Project / 案名

林口雲品薇閣姚宅

Sheet Title / 圖名



1F

立面圖

Date / 日期	Scale / 比例
8/10/2026	1/30cm
Designer / 設計	Approval / 核准
MONICA LIN	
Job No / 業務編號	Drawn By / 繪圖
00000	GUIDO
Dwg No.	Page No.

E-25

102

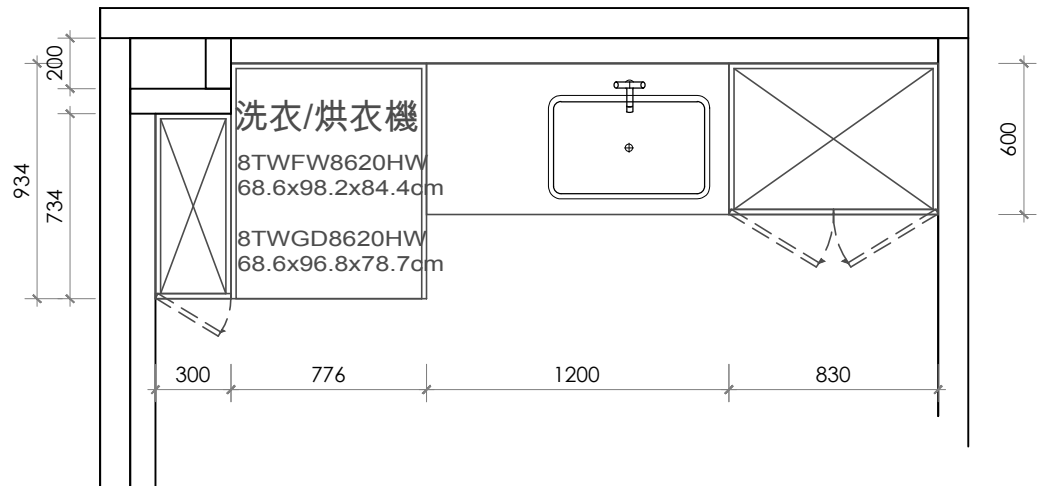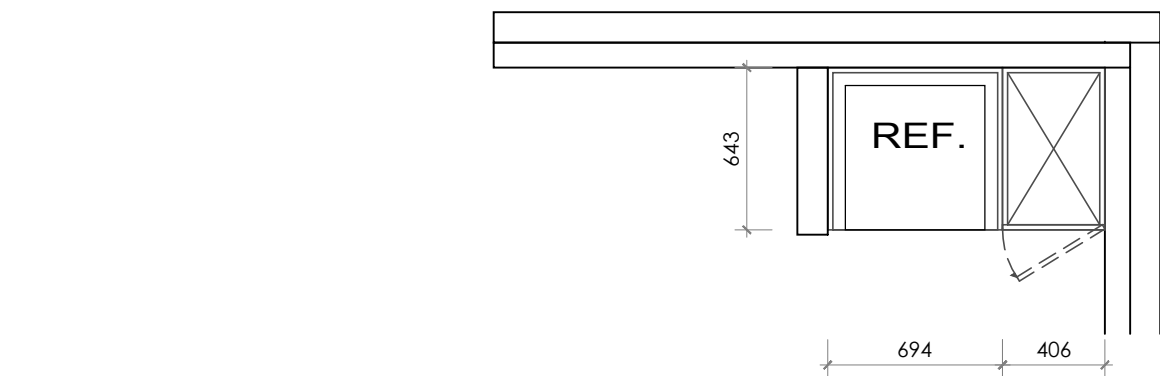



▲CH 3381mm

▲CH 2920mm

▲CH 2740mm

▼FL ±0 mm

▲FL -50 mm

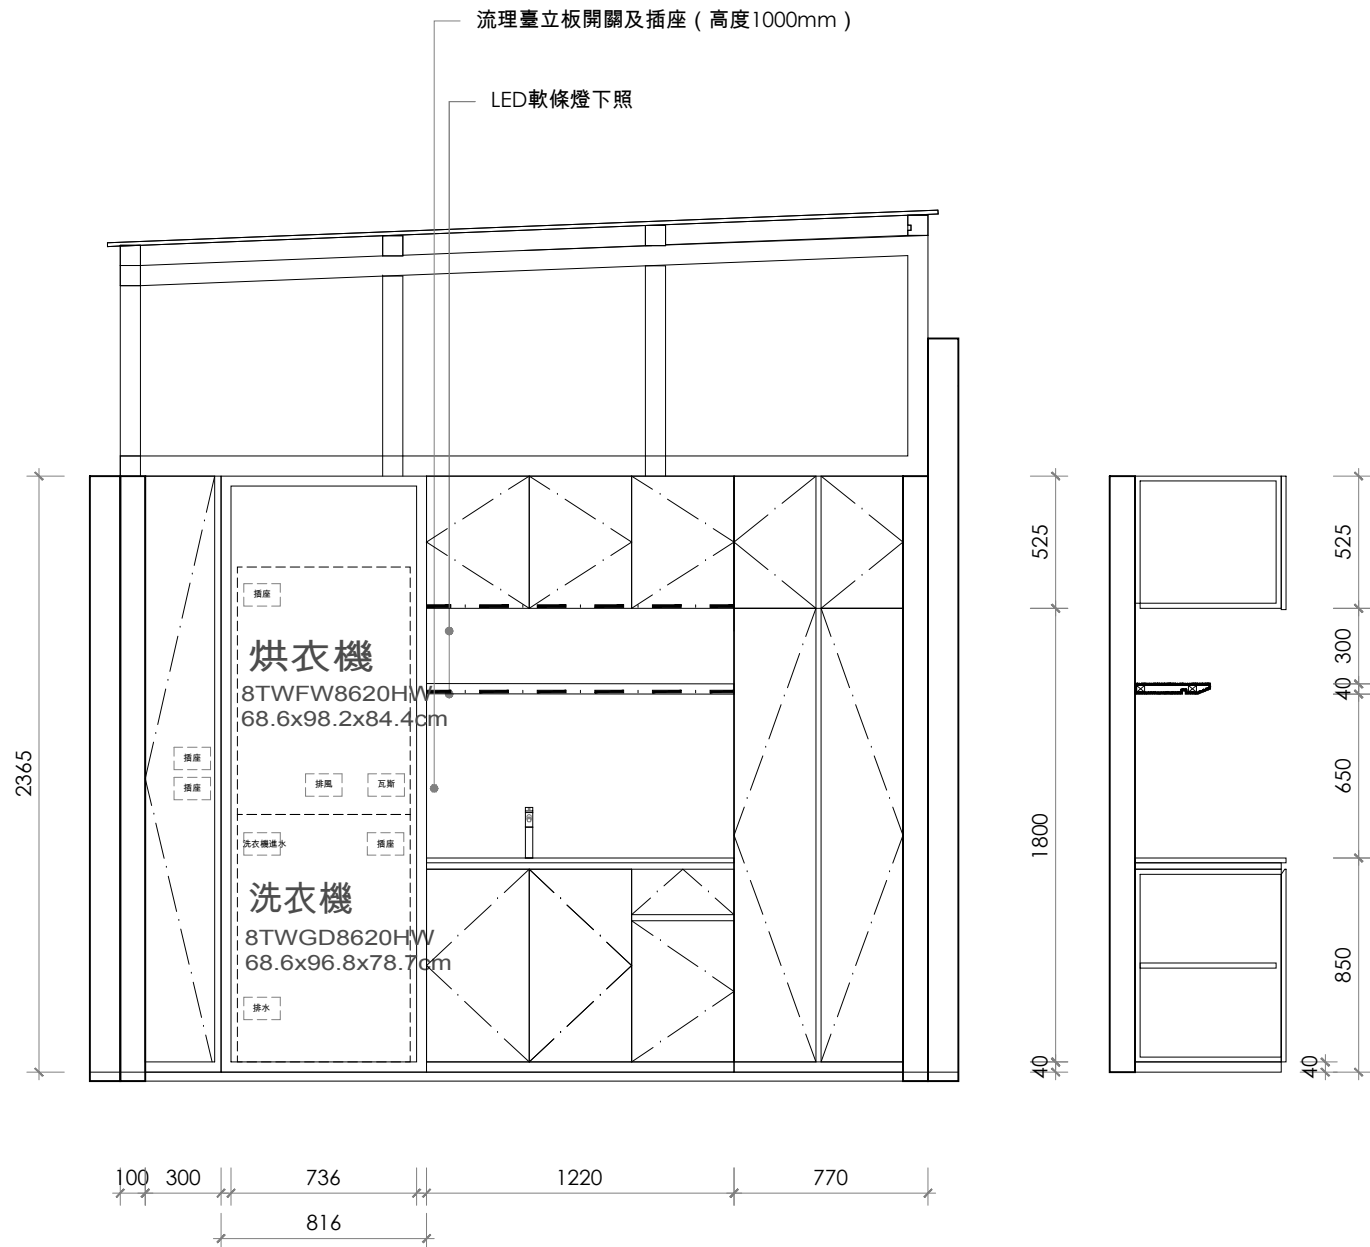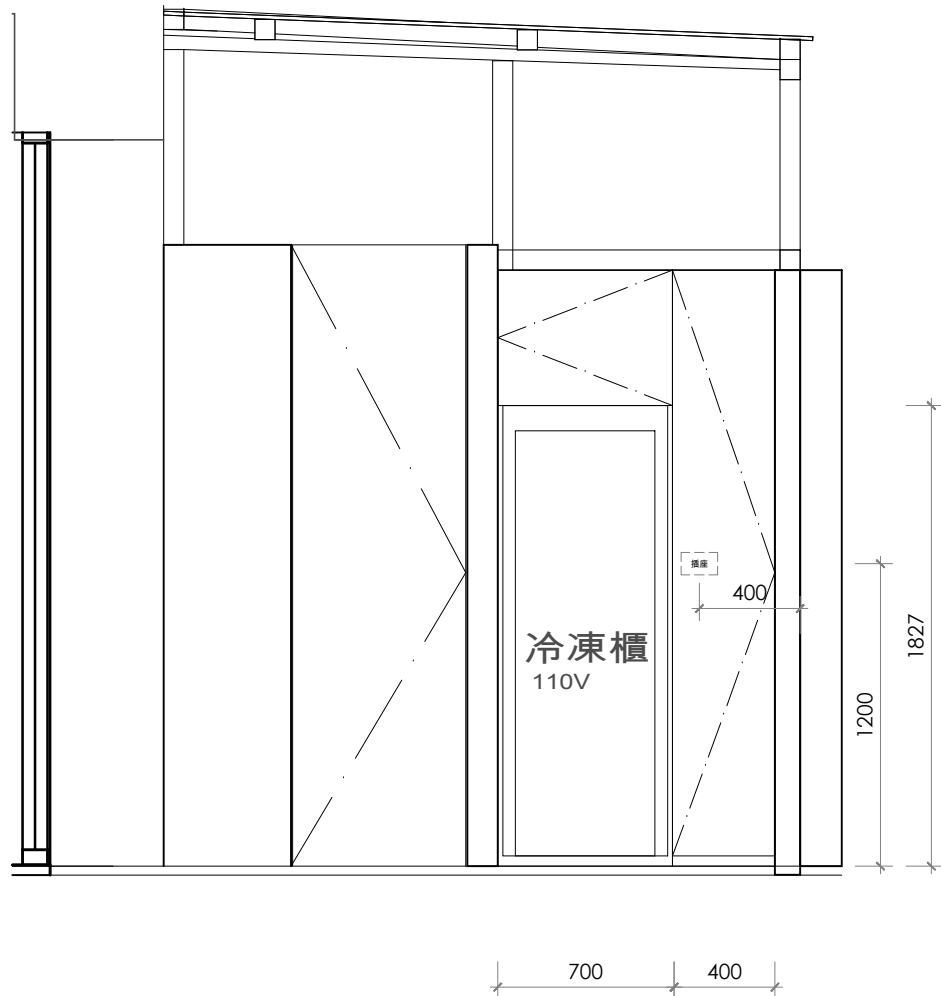

1 ELEVATION Scale=1:30 E-26

2 ELEVATION Scale=1:30 E-26

Revision

APPROVAL/核准

設計者:	建築師:
業主:	

備註:

- 圖面標註尺寸僅供參考，施作均以現場放樣檢討之。
- 圖面標註尺寸、材料及文字敘述因版本不同之差異，均以出圖章簽認日期之最近為準。
- 電腦圖檔除由合約訂定外，均不得以任何方式外流。
- 圖面所示均為本公司所擁有之智慧財產，切勿以任何方式複製修改。

M MULA DECO

3F, N.26, Ln.290, Guangfu S. Rd., Taipei.
886-2-2546-3258
886-2-2546-3257
Guido@muladeco.com


Project / 案名

林口雲品薇閣姚宅

Sheet Title / 圖名
1F

立面圖

Date / 日期	Scale / 比例
8/10/2026	1/30cm
Designer / 設計	Approval / 核准
MONICA LIN	
Job No / 業務編號	Drawn By / 繪圖
00000	GUIDO
Dwg No.	Page No.
E-26	103


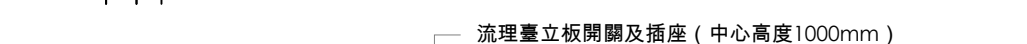


ELEVATION

ELEVATION

E-26 104



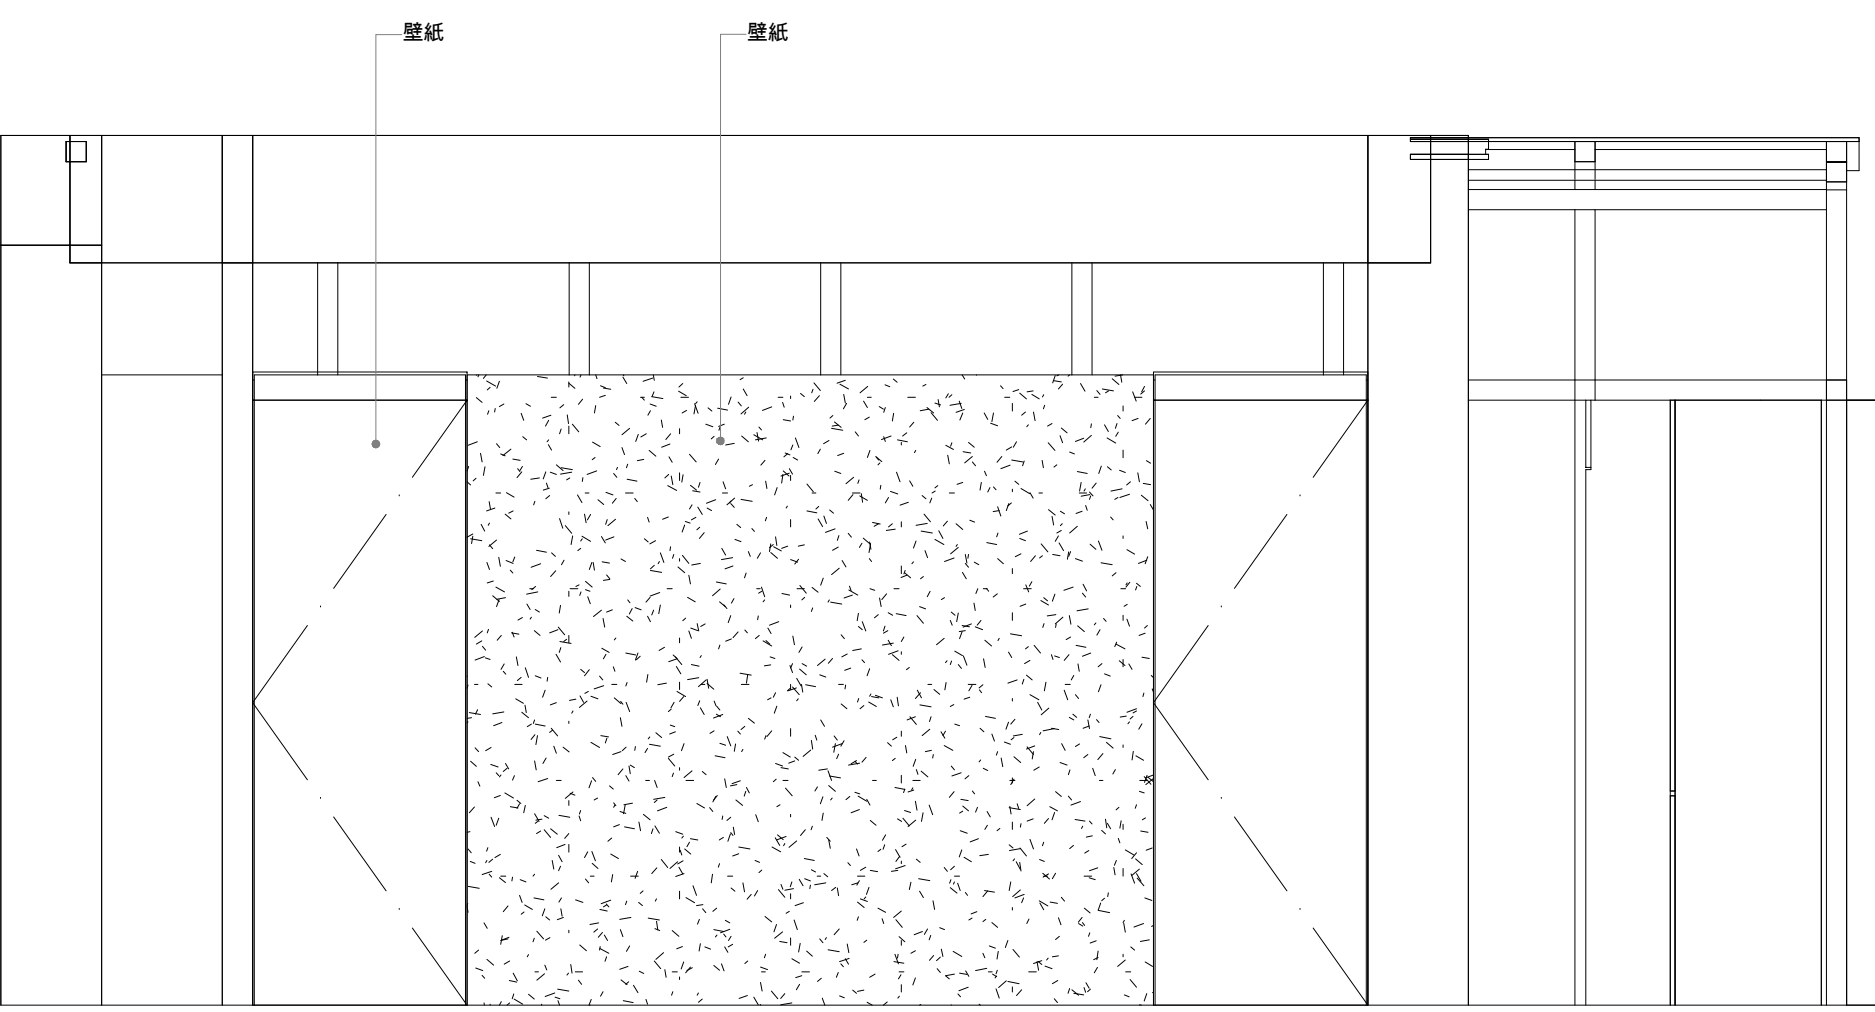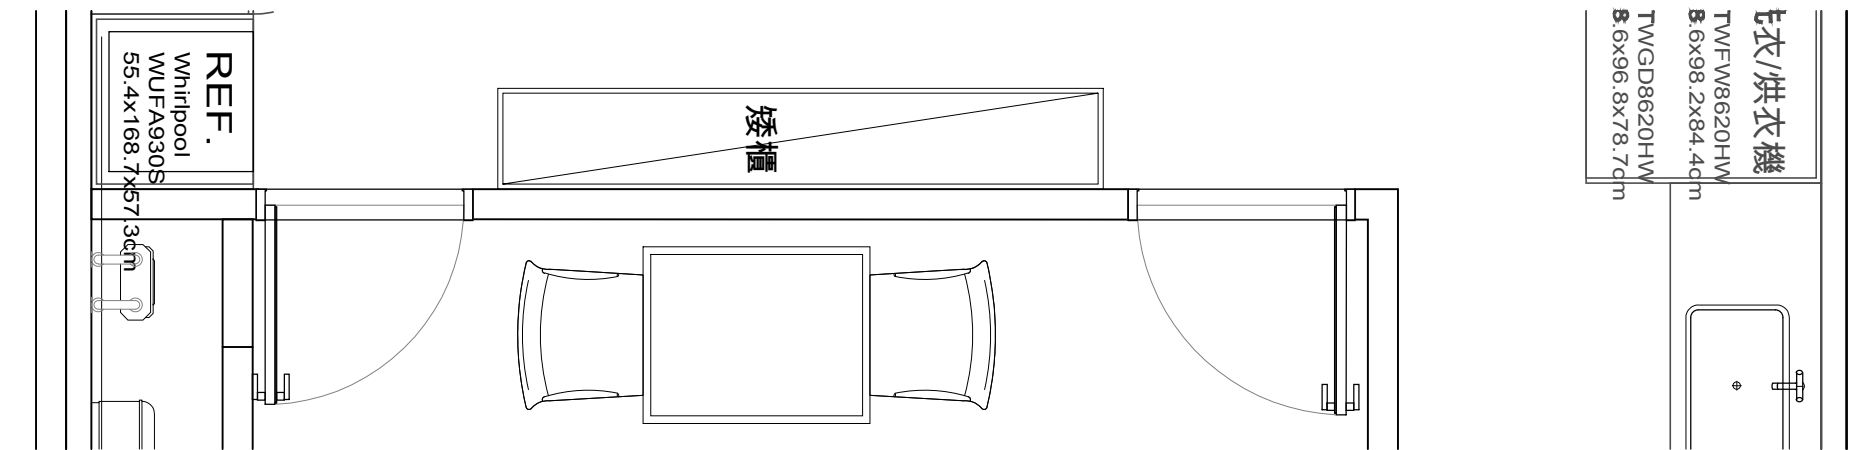

▲CH 3381mm

▲CH 2920mm

▲CH 2740mm

▼FL ±0 mm

▲FL -50 mm

1
E-28

ELEVATION

Scale=1:30

Revision

APPROVAL / 核准

設計者:	建築師:
業主:	

備註:

- a. 圖面標註尺寸僅供參考，施作均以現場放樣檢討之。
- b. 圖面標註尺寸、材料及文字敘述因版本不同之差異，均以圖章簽認日期之最近為準。
- c. 電腦圖檔除由合約訂定外，均不得以任何方式外流。
- d. 圖面所示均為本公司所擁有之智慧財產，切勿以任何方式複製修改。



MULA DECO

▲ 3F, N.26, Ln.290, Guangfu S. Rd., Taipei.
☎ 886-2-2546-3258
☎ 886-2-2546-3257
✉ Guido@muladeco.com

Project / 案名

林口雲品薇閣姚宅


Sheet Title / 圖名
1F

立面圖

Date / 日期	Scale / 比例
8/10/2026	1/30cm
Designer / 設計	Approval / 核准
MONICA LIN	
Job No / 業務編號	Drawn By / 繪圖
00000	GUIDO
Dwg No.	Page No.

E-28

106

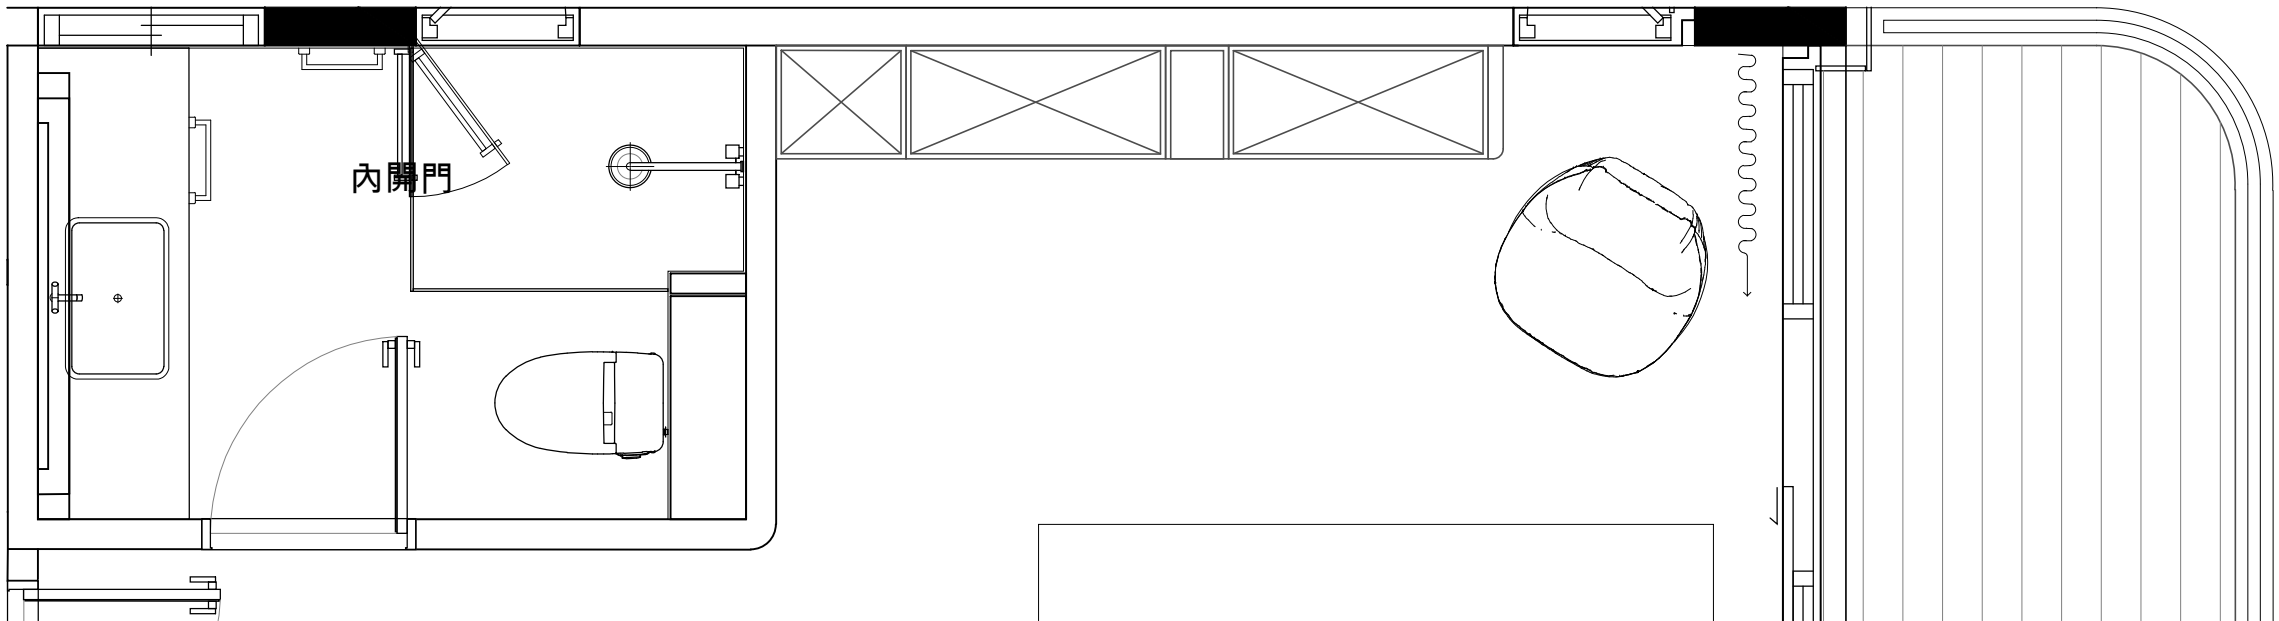


▲CH 2902mm

▲CH 2502mm

▲CH 2252mm

▼FL ±0 mm
▲FL -50 mm

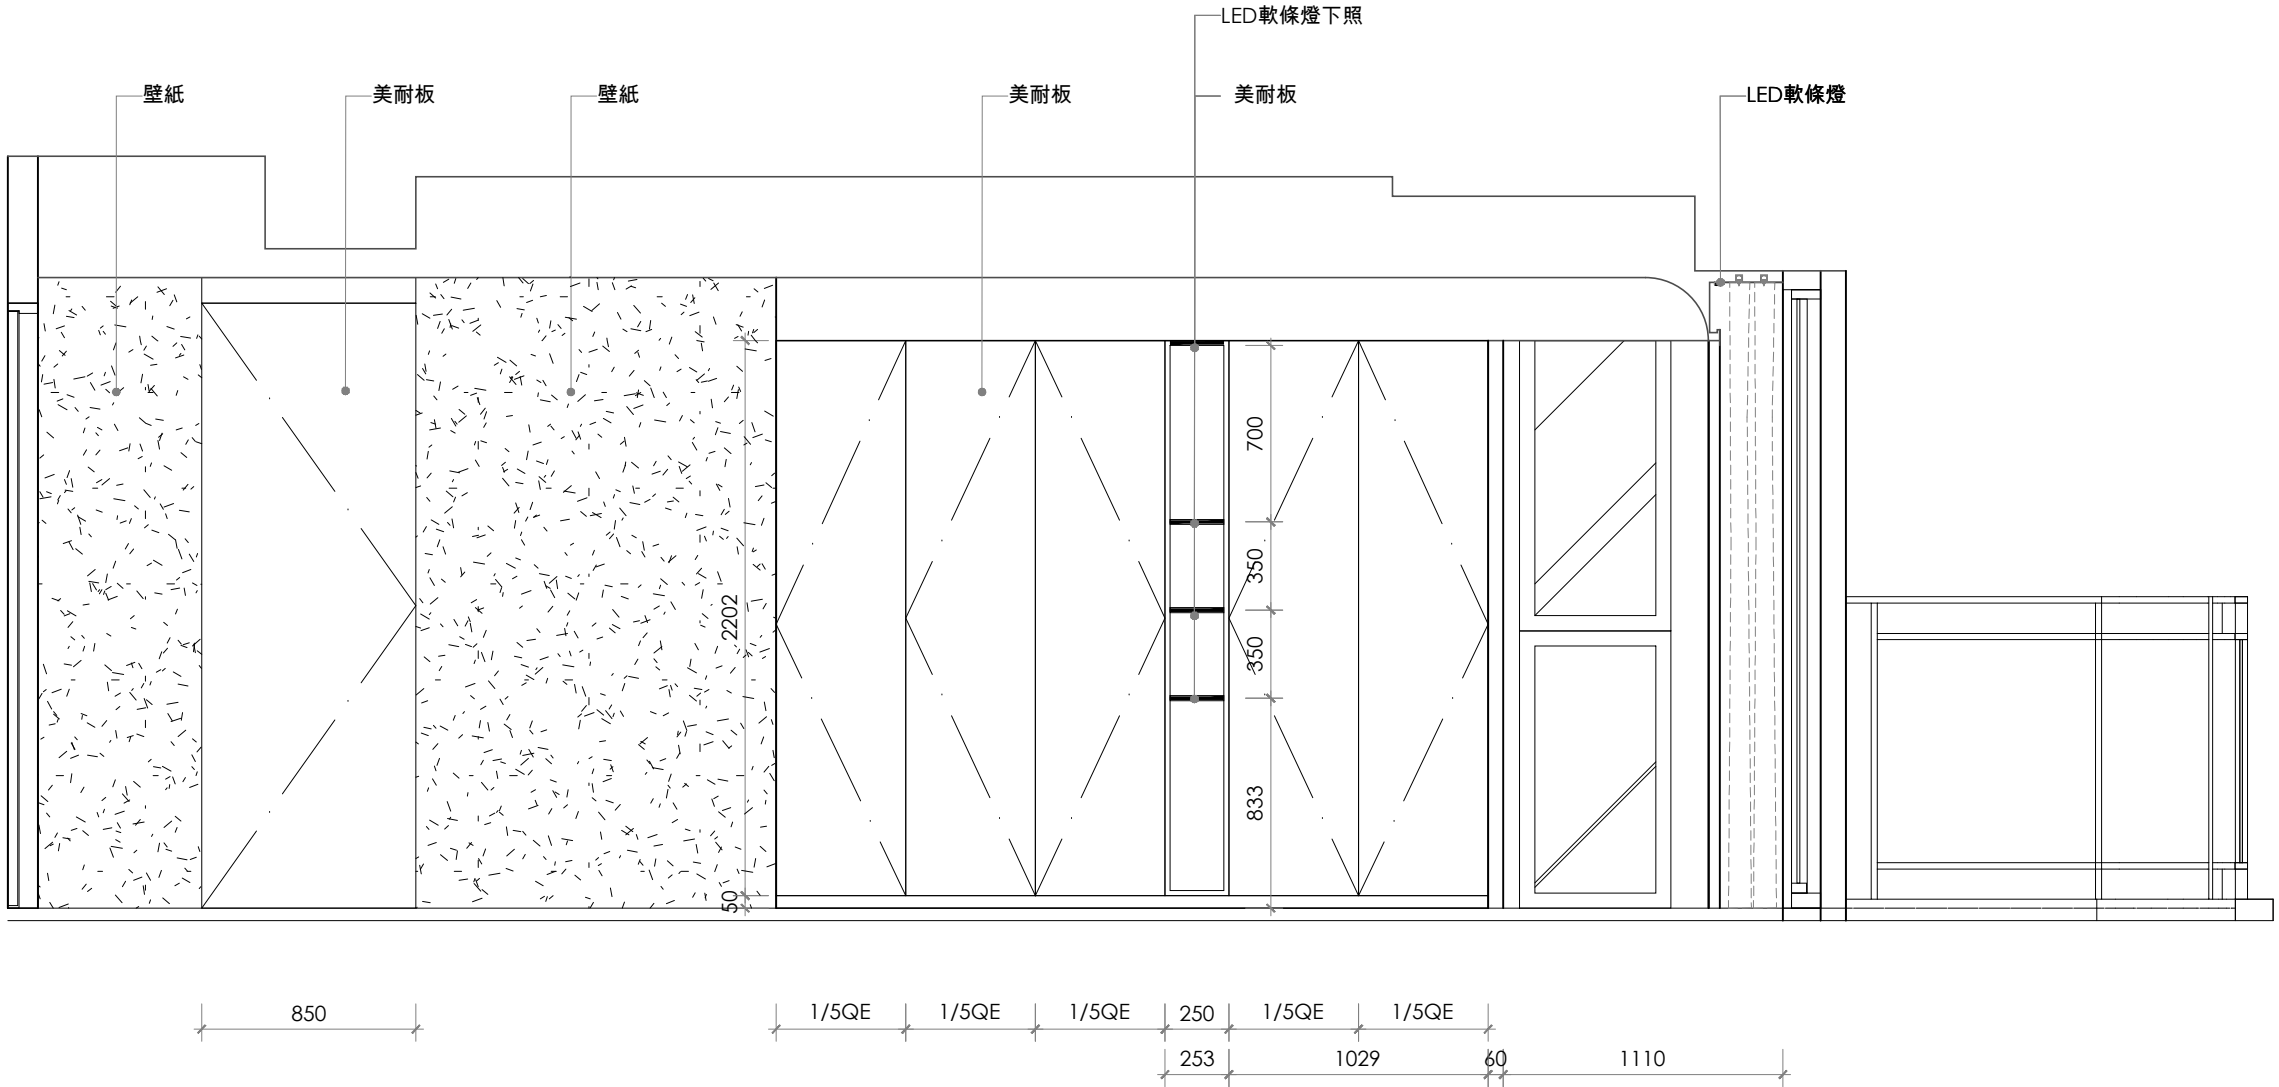

1
E-29

ELEVATION

Scale=1:30

Revision

APPROVAL/核准

設計者:	建築師:
業主:	

備註:
a. 圖面標註尺寸僅供參考，施作均以現場放樣檢討之。
b. 圖面標註尺寸、材料及文字敘述因版本不同之差異，均以出圖章簽認日期之最近為準。
c. 電腦圖檔除由合約訂定外，均不得以任何方式外流。
d. 圖面所示均為本公司所擁有之智慧財產，切勿以任何方式複製修改。

M
MULA DECO
▲ 3F, N.26, Ln.290, Guangfu S. Rd., Taipei.
☎ 886-2-2546-3258
✉ Guido@muladeco.com

Project / 案名



林口雲品薇閣姚宅

Sheet Title / 圖名
2F

立面圖

Date / 日期	Scale / 比例
8/10/2026	1/30cm
Designer / 設計	Approval / 核准
MONICA LIN	
Job No / 業務編號	Drawn By / 繪圖
00000	GUIDO
Dwg No.	Page No.

E-29 107

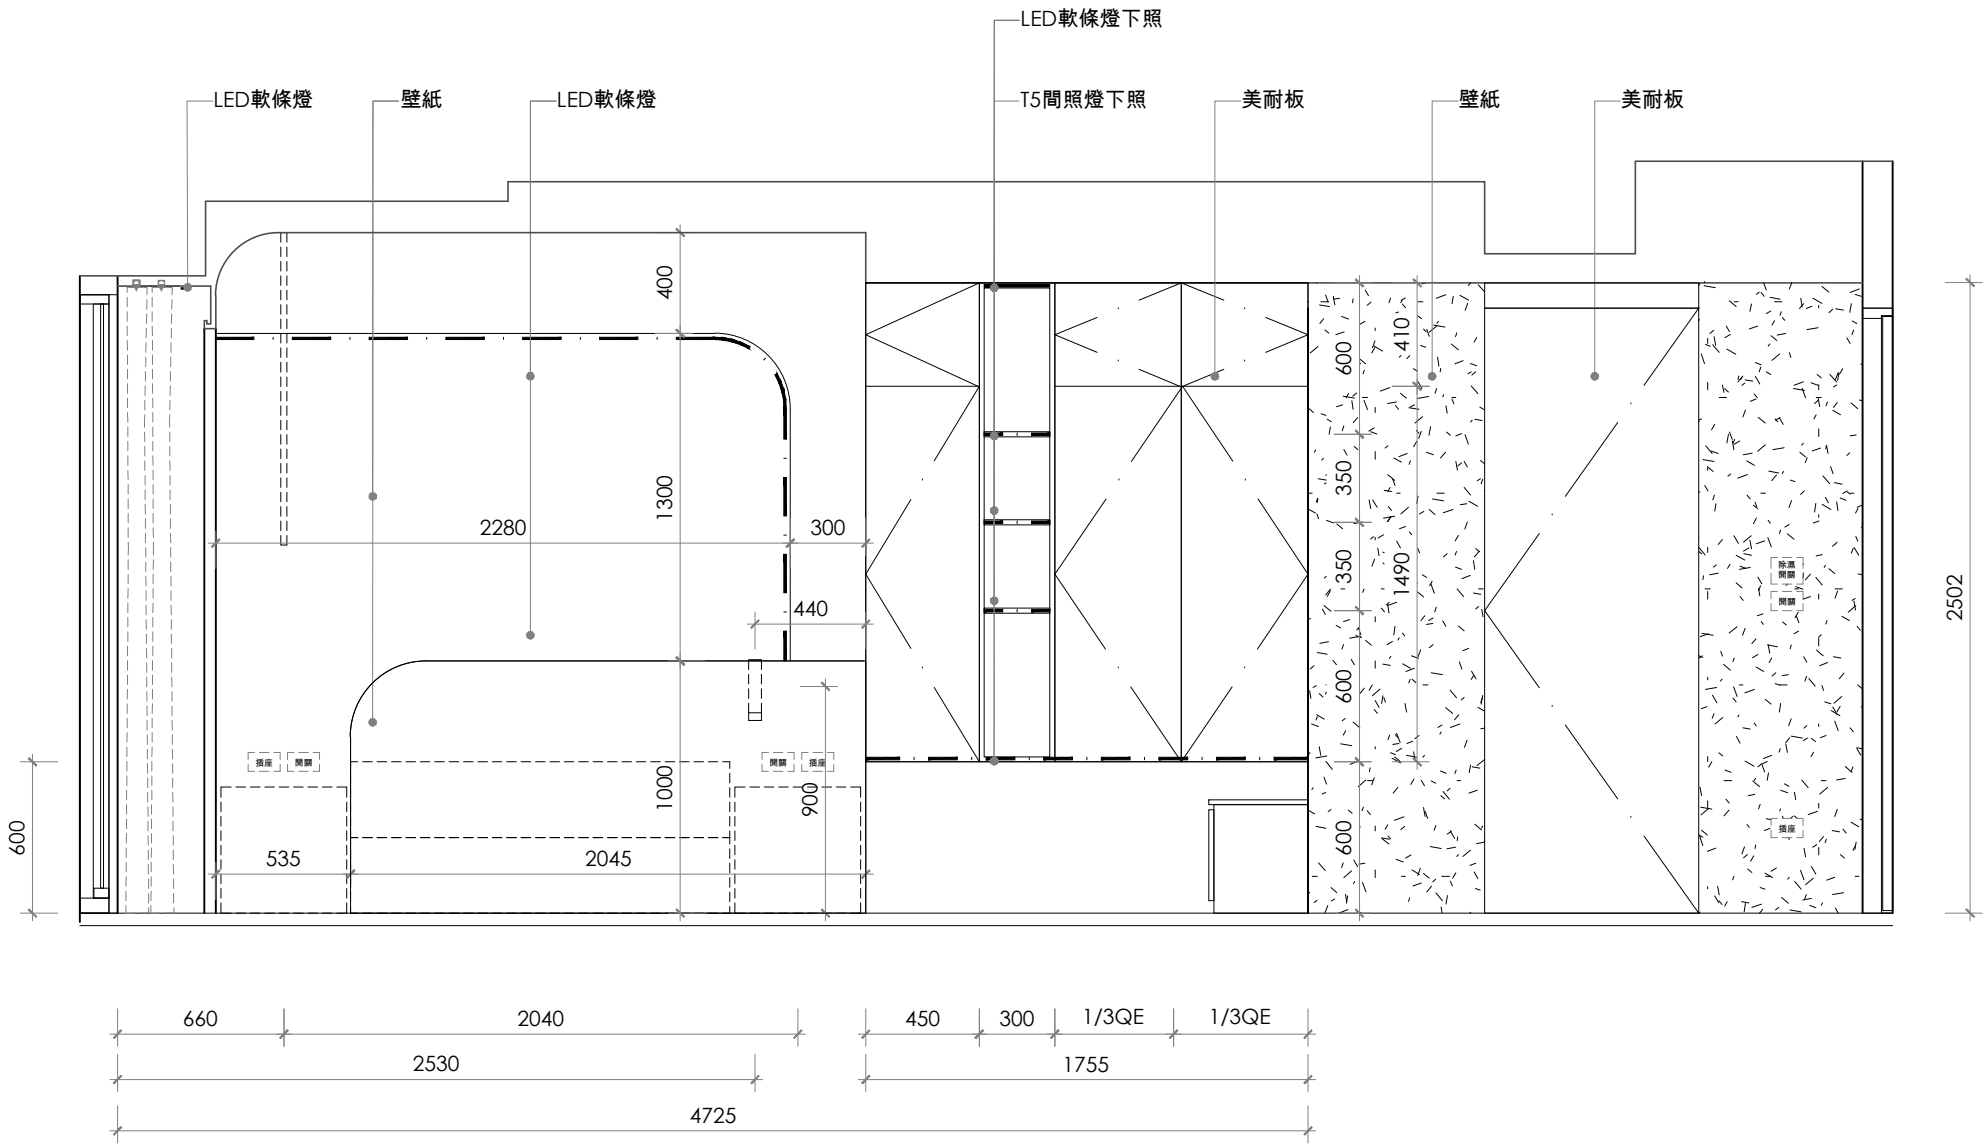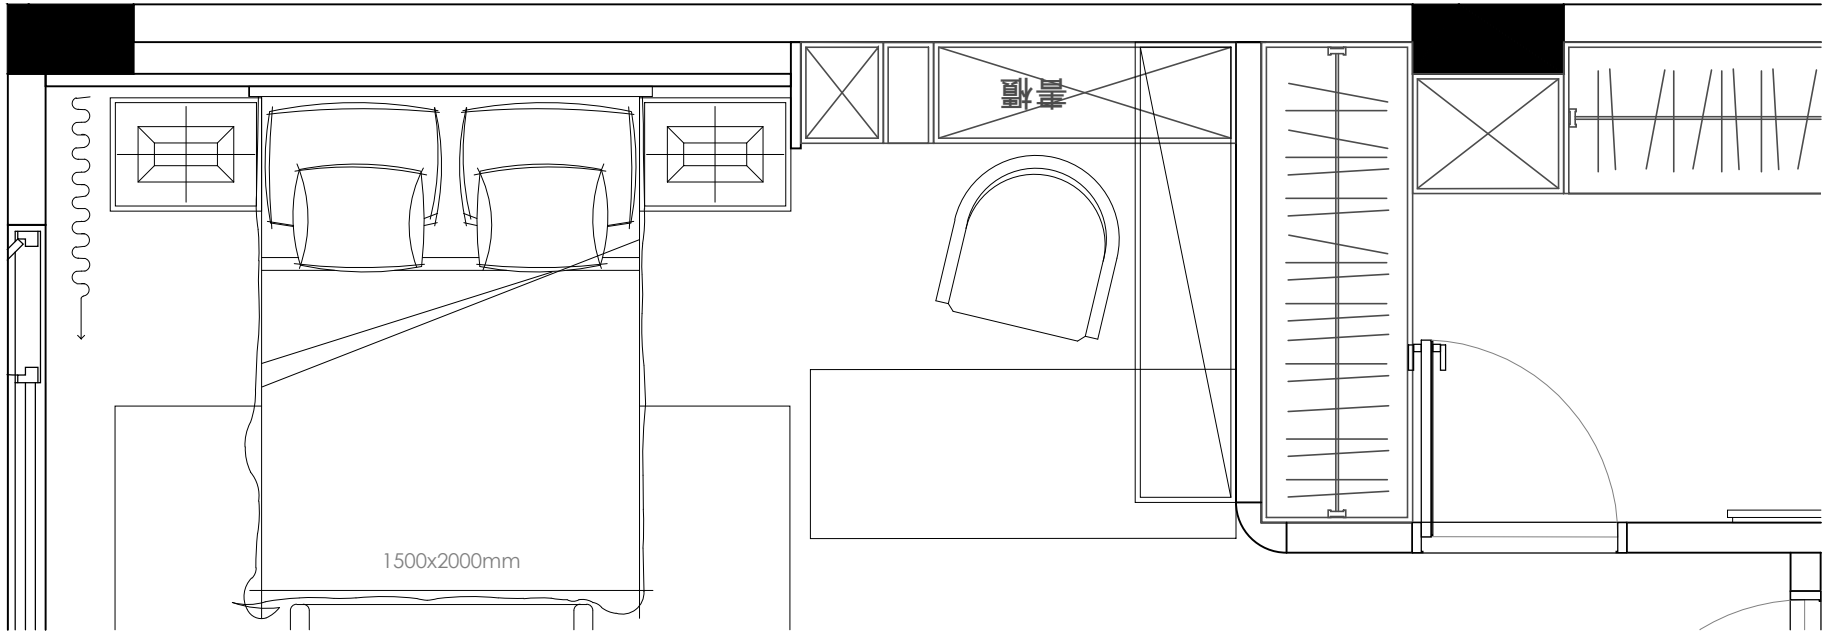

1
E-30

ELEVATION

Scale=1:30

Revision

APPROVAL/核准

設計者:	建築師:
業主:	

備註:

- 圖面標註尺寸僅供參考，施作均以現場放樣檢討之。
- 圖面標註尺寸、材料及文字敘述因版本不同之差異，均以出圖章簽認日期之最近為準。
- 電腦圖檔除由合約訂定外，均不得以任何方式外流。
- 圖面所示均為本公司所擁有之智慧財產，切勿以任何方式複製修改。



MULA DECO

▲ 3F, N.26, Ln.290, Guangfu S. Rd., Taipei.
☎ 886-2-2546-3258
☎ 886-2-2546-3257
✉ Guido@muladeco.com

Project / 案名


林口雲品薇閣姚宅

Sheet Title / 圖名

2F

立面圖

Date / 日期	Scale / 比例
8/10/2026	1/30cm
Designer / 設計	Approval / 核准
MONICA LIN	
Job No / 業務編號	Drawn By / 繪圖
00000	GUIDO
Dwg No.	Page No.
E-30	108


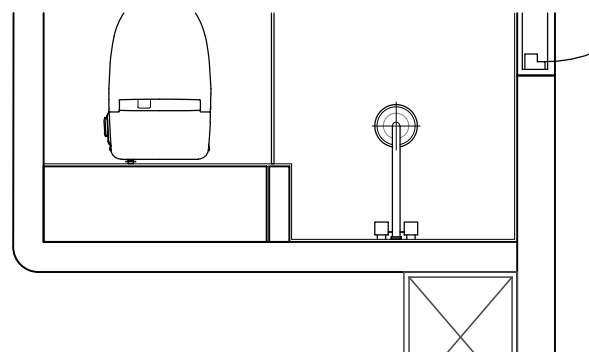


▲CH 2252mm

1
E-31

Scale=1:30

109

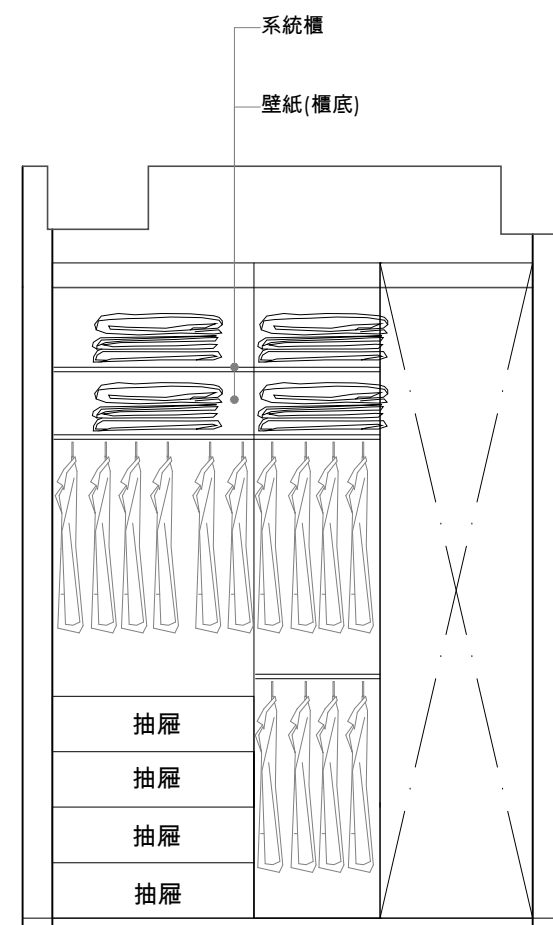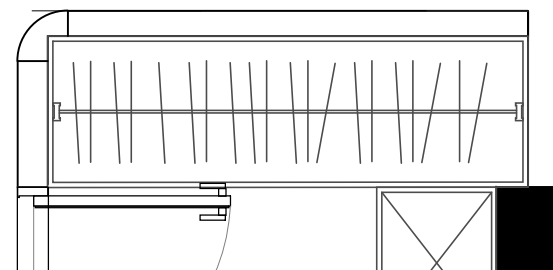

Revision

APPROVAL/核准

APPROVAL/核准	
設計者:	建築師:
業主:	

備註:

- a. 圖面標註尺寸僅供參考，施作均以現場放樣檢討之。
- b. 圖面標註尺寸、材料及文字敘述因版本不同之差異，均以圖章簽認日期之最近為準。
- c. 電腦圖檔除由合約訂定外，均不得以任何方式外流。
- d. 圖面所示均為本公司所擁有之智慧財產，切勿以任何方式複製修改。



MULA DECO

A 3F, N.26, Ln.290, Guangfu S. Rd., Taipei.
T 886-2-2546-3258
F 886-2-2546-3257
E Guido@muladeco.com

Project / 案名

林口雲品薇閣姚宅

Sheet Title / 圖名
2F



100

立面圖

Date / 日期	Scale / 比例
8/10/2026	1/30cm
Designer / 設計	Approval / 核准
MONICA LIN	
Job No / 業務編號	Drawn By / 繪圖
00000	GUIDO
Dwg No.	Page No.



E-32

11C

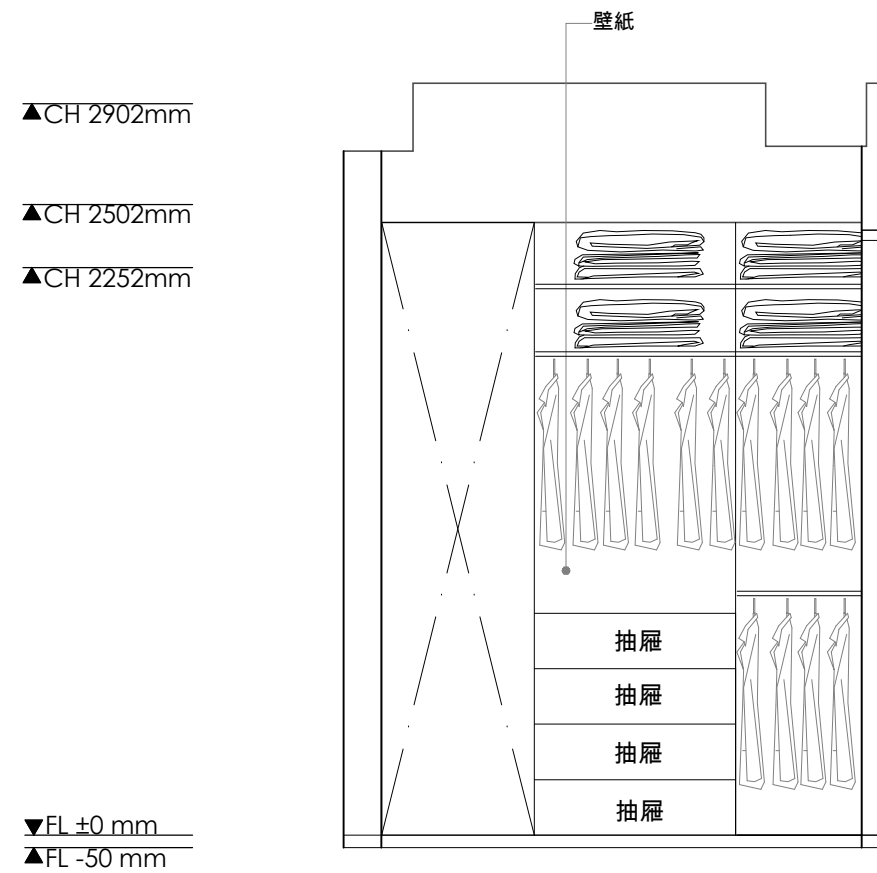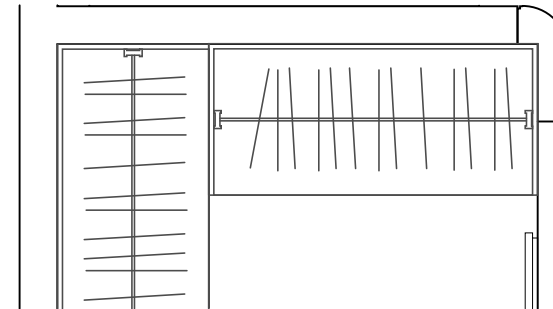

2 ELEVATION
E-33 Scale=1:30

Date / 日期	Scale / 比例
8/10/2026	1/30cm
Designer / 設計	Approval / 核准
MONICA LIN	
Job No / 業務編號	Drawn By / 繪圖
00000	GUIDO
Dwg No.	Page No.
E-33	111

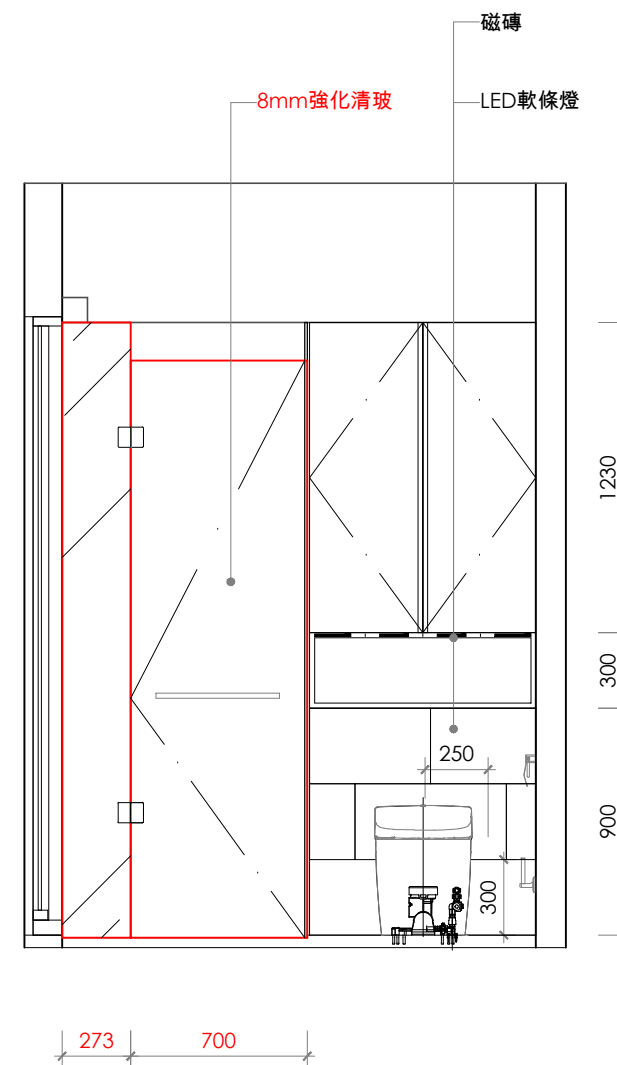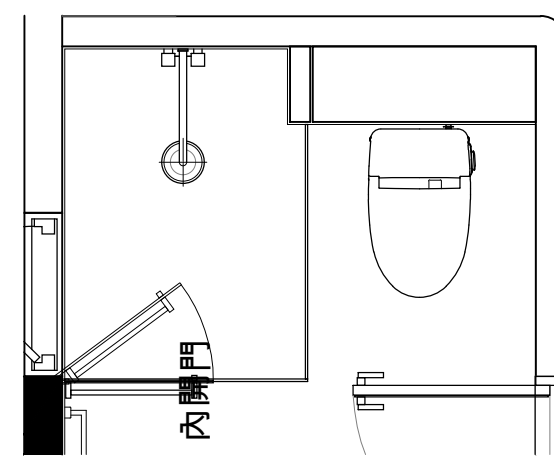

2 ELEVATION
E-34 Scale=1:30

附註:





- ①圖面標註尺寸僅供參考，施作均以現場放樣尺寸為準。
- ②圖面標註尺寸、材料及文字敘述因版本不同之差異，均以圖章簽認日期之最近為準。
- ③電腦圖檔除由合約訂定外，均不得以何方式外流。
- ④圖面所示均為本公司所擁有之智慧財產，切勿以任何方式複製修改。


MULA DECO
A 3F, N.26, Ln.290, Guanglu S. Rd., Taipei.
T 886-2-2546-3258
F 886-2-2546-3257
E Guido@mula deco.com

林口雲品薇閣姚宅

Sheet Title / 圖名
2F
立面圖

Date / 日期	Scale / 比例
8/10/2026	1/30cm
Designer / 設計	Approval / 核准
MONICA LIN	
Job No. / 業務編號	Drawn By / 繪圖
00000	GUIDO
Dwg No.	Page No.
E-34	112

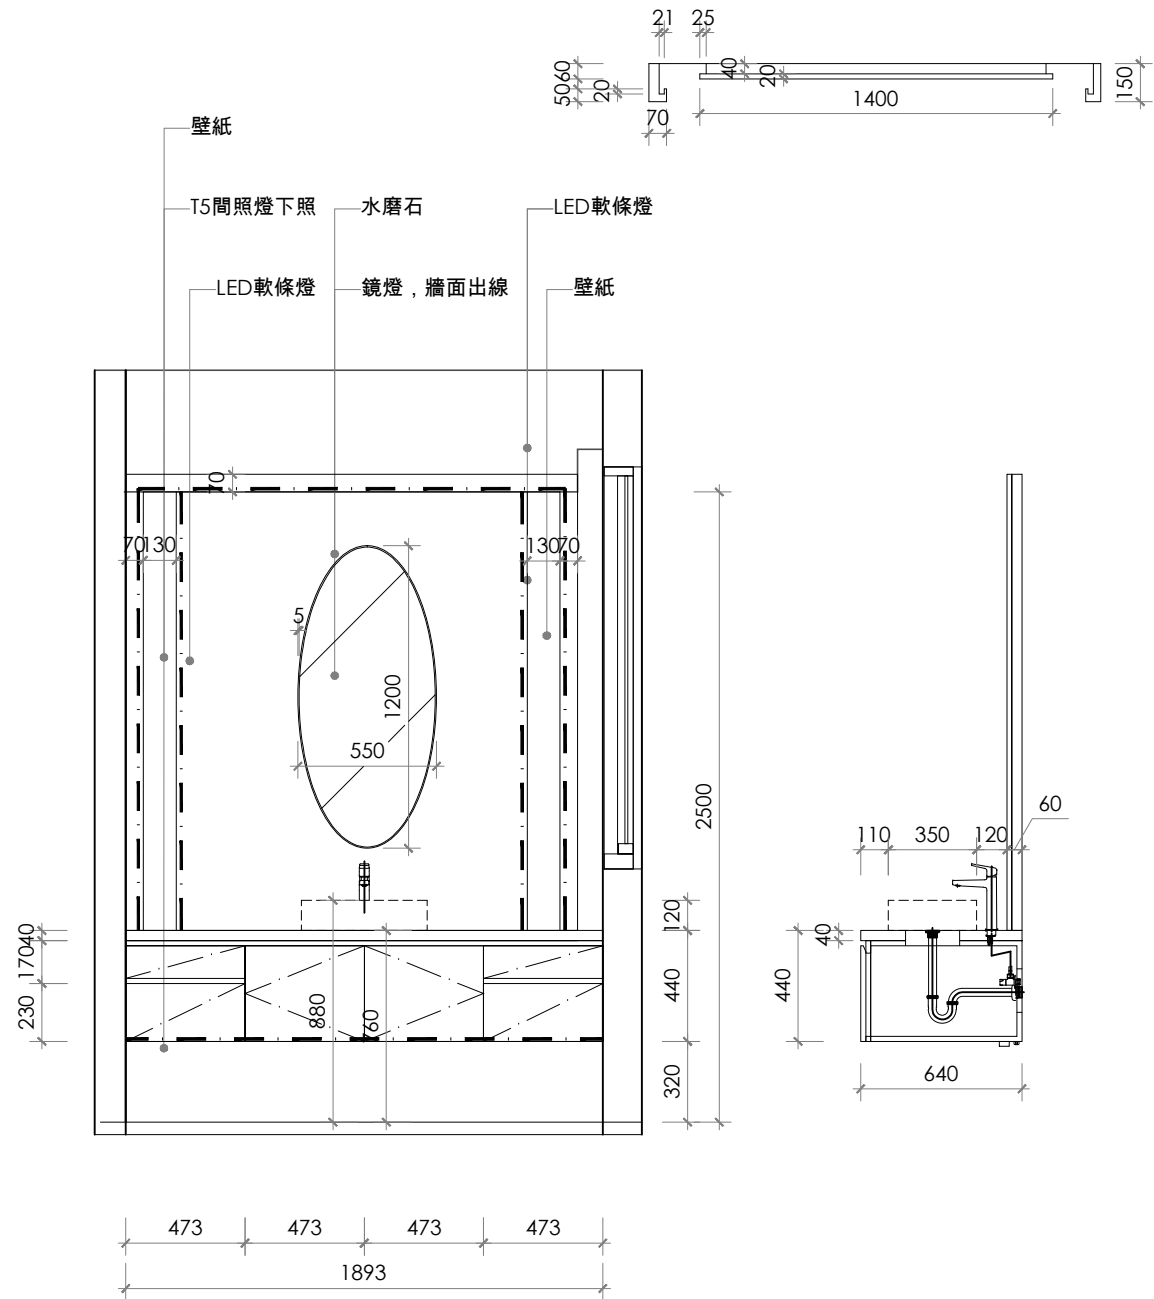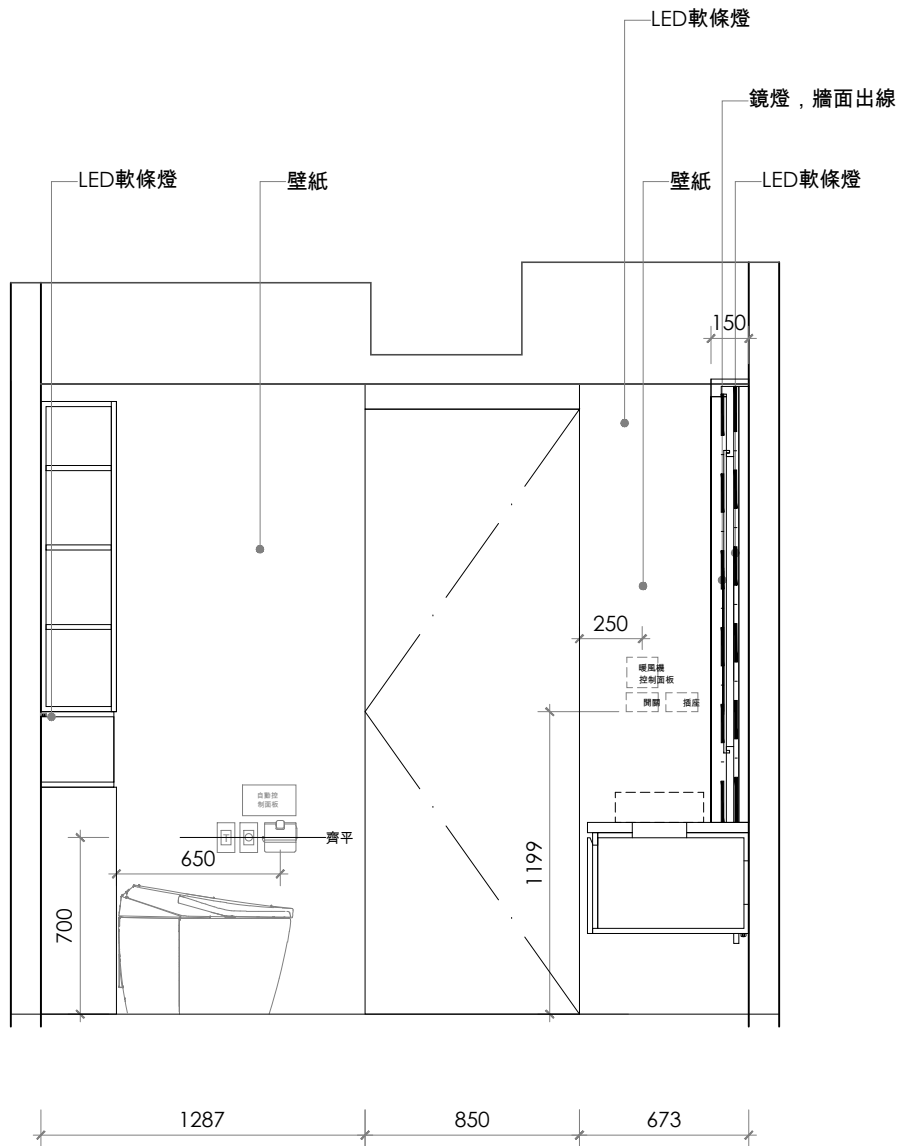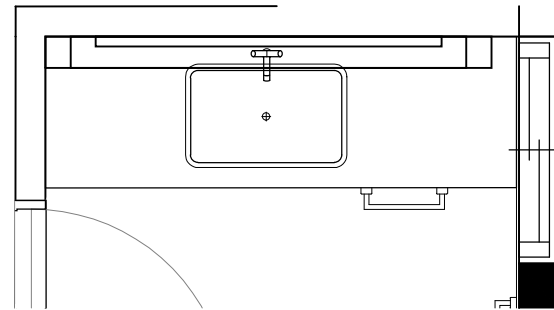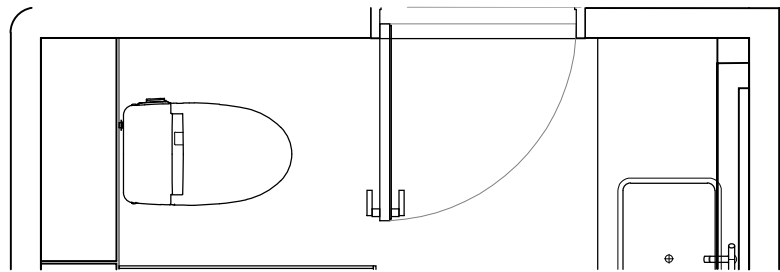

1 ELEVATION
E-35
Scale=1:30

2 ELEVATION
E-35
Scale=1:30

Revision

APPROVAL/核准

設計者:	建築師:
業主:	

備註:

- 圖面標註尺寸僅供參考，施作均以現場放樣檢討之。
- 圖面標註尺寸、材料及文字敘述因版本不同之差異，均以出圖章簽認日期之最近為準。
- 電腦圖檔除由合約訂定外，均不得以任何方式外流。
- 圖面所示均為本公司所擁有之智慧財產，切勿以任何方式複製修改。



MULA DECO

▲ 3F, N.26, Ln.290, Guangfu S. Rd., Taipei.
☎ 886-2-2546-3258
☎ 886-2-2546-3257
✉ Guido@muladeco.com

Project / 案名

林口雲品薇閣姚宅


Sheet Title / 圖名
2F

立面圖

Date / 日期	Scale / 比例
8/10/2026	1/30cm
Designer / 設計	Approval / 核准
MONICA LIN	
Job No / 業務編號	Drawn By / 繪圖
00000	GUIDO
Dwg No.	Page No.

E-35


113

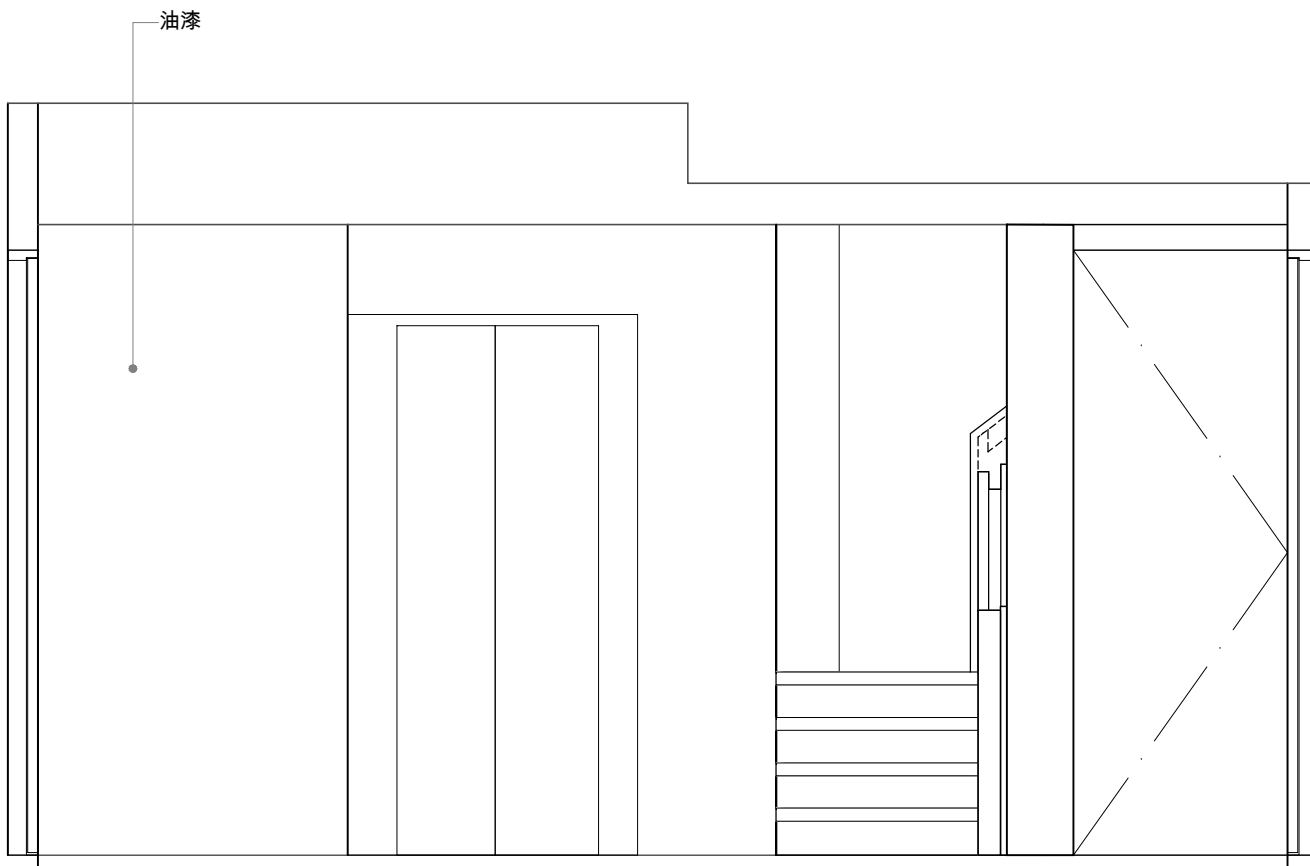

▼FL ±0 mm
▲FL -50 mm

Scale=1:30

E-37 115

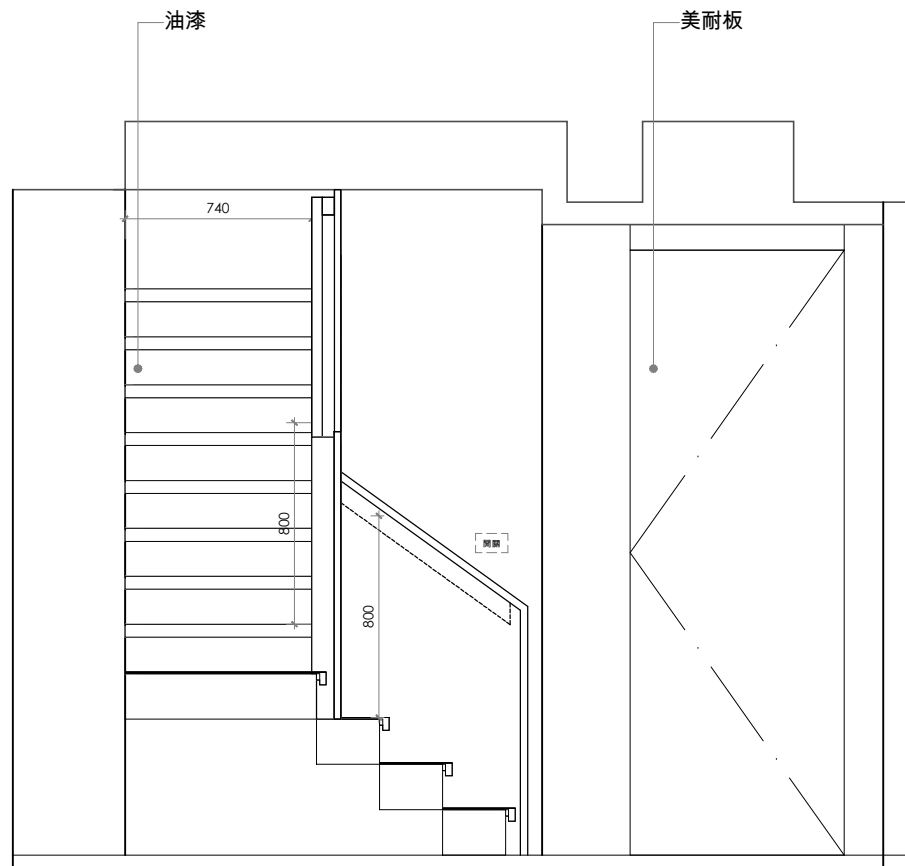

▼FL ±0 mm
▲FL -50 mm

[illegible]

MULA DECO

A 3F, N.26, Ln.290, Guangfu S. Rd., Taipei.
T 886-2-2546-3258
F 886-2-2546-3257
E Guido@mula deco.com

Date / 日期	Scale / 比例
8/10/2026	1/30cm
Designer / 設計	Approval / 核准
MONICA LIN	
Job No / 業務編號	Drawn By / 繪圖
00000	GUIDO
Dwg No.	Page No.
E-38	116

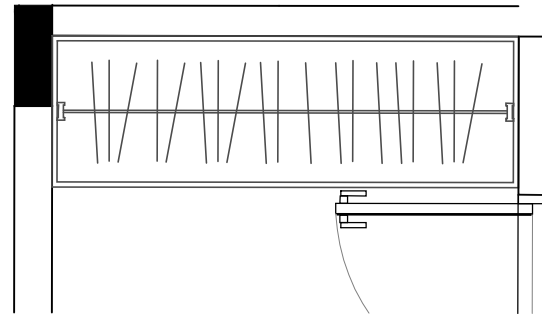
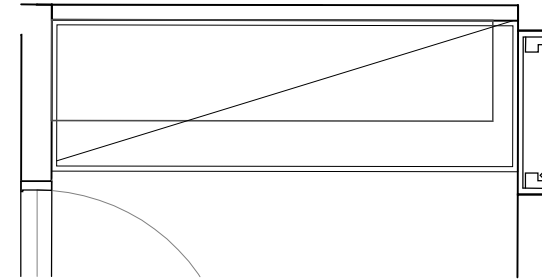






Diagram illustrating the components of a cabinet structure:

- 美耐板 (門片) (Melamine board (Door panel))
- 樂活板 (桶身) (Living board (Cabinet body))
- 活動層板櫃 (Activity shelf cabinet)

Scale=1:30

E-39 117

E-40 118

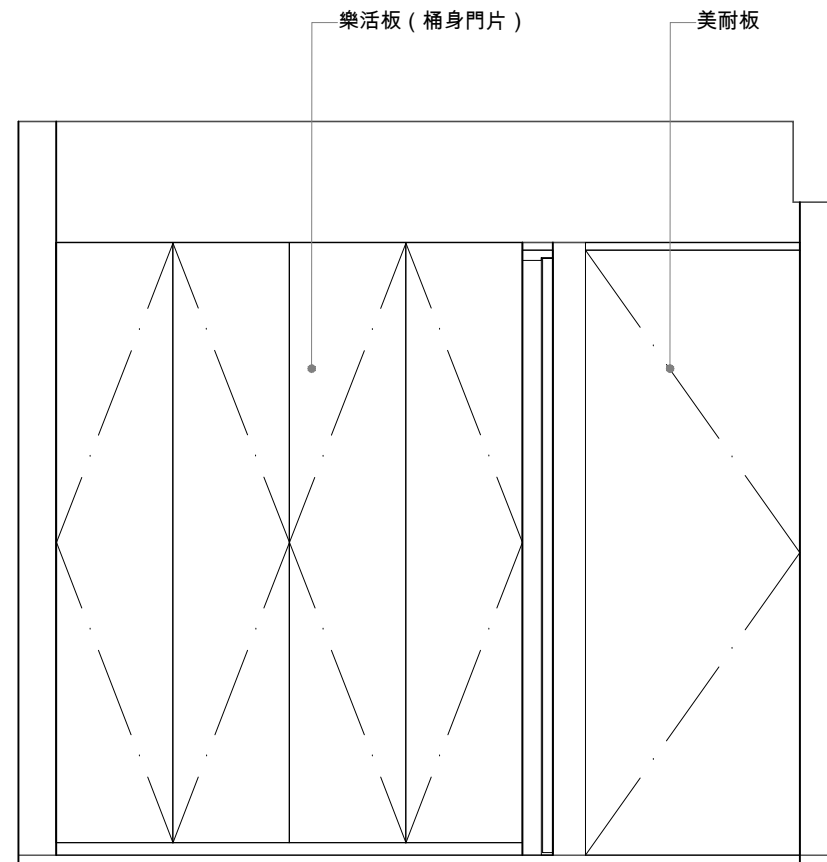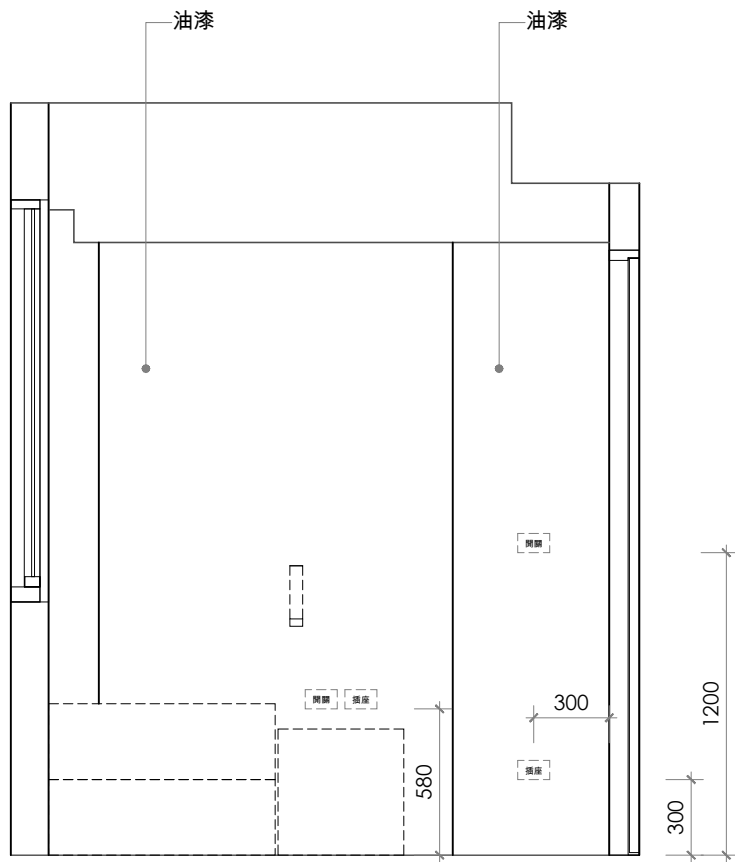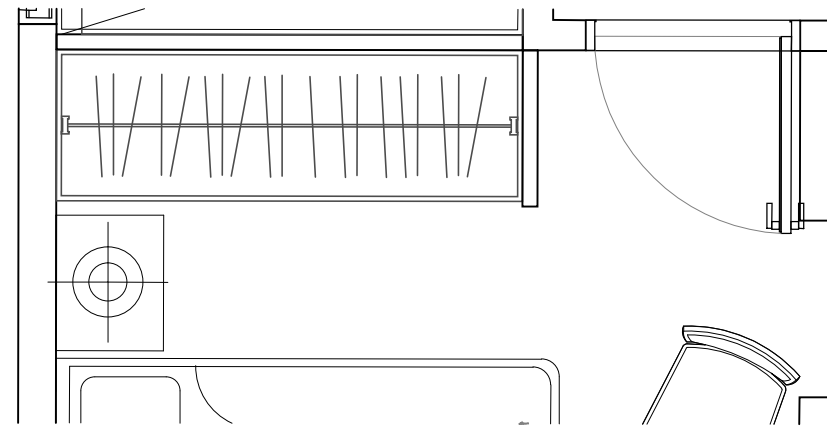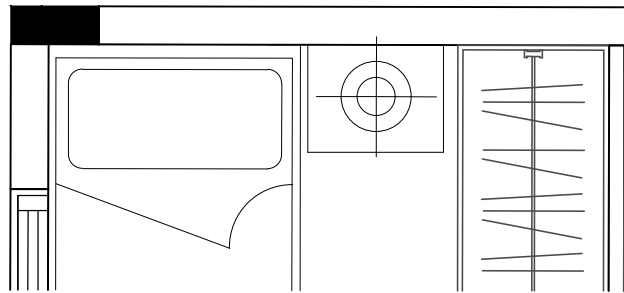

▲CH 2983mm

▲CH 2500mm

▼FL ±0 mm

▲FL -50 mm

▲CH 2983mm

▲CH 2500mm

▼FL ±0 mm

▲FL -50 mm

1
E-41

ELEVATION

Scale=1:30

2
E-41

ELEVATION

Scale=1:30

Revision

APPROVAL/核准

設計者:	建築師:
業主:	

備註:

- 圖面標註尺寸僅供參考，施作均以現場放樣檢討之。
- 圖面標註尺寸、材料及文字敘述因版本不同之差異，均以出圖章簽認日期之最近為準。
- 電腦圖檔除由合約訂定外，均不得以任何方式外流。
- 圖面所示均為本公司所擁有之智慧財產，切勿以任何方式複製修改。



MULA DECO

▲ 3F, N.26, Ln.290, Guangfu S. Rd., Taipei.
☎ 886-2-2546-3258
☎ 886-2-2546-3257
✉ Guido@muladeco.com

Project / 案名

林口雲品薇閣姚宅



Sheet Title / 圖名
2F

立面圖

Date / 日期	Scale / 比例
8/10/2026	1/30cm
Designer / 設計	Approval / 核准
MONICA LIN	
Job No / 業務編號	Drawn By / 繪圖
00000	GUIDO
Dwg No.	Page No.

E-41

119

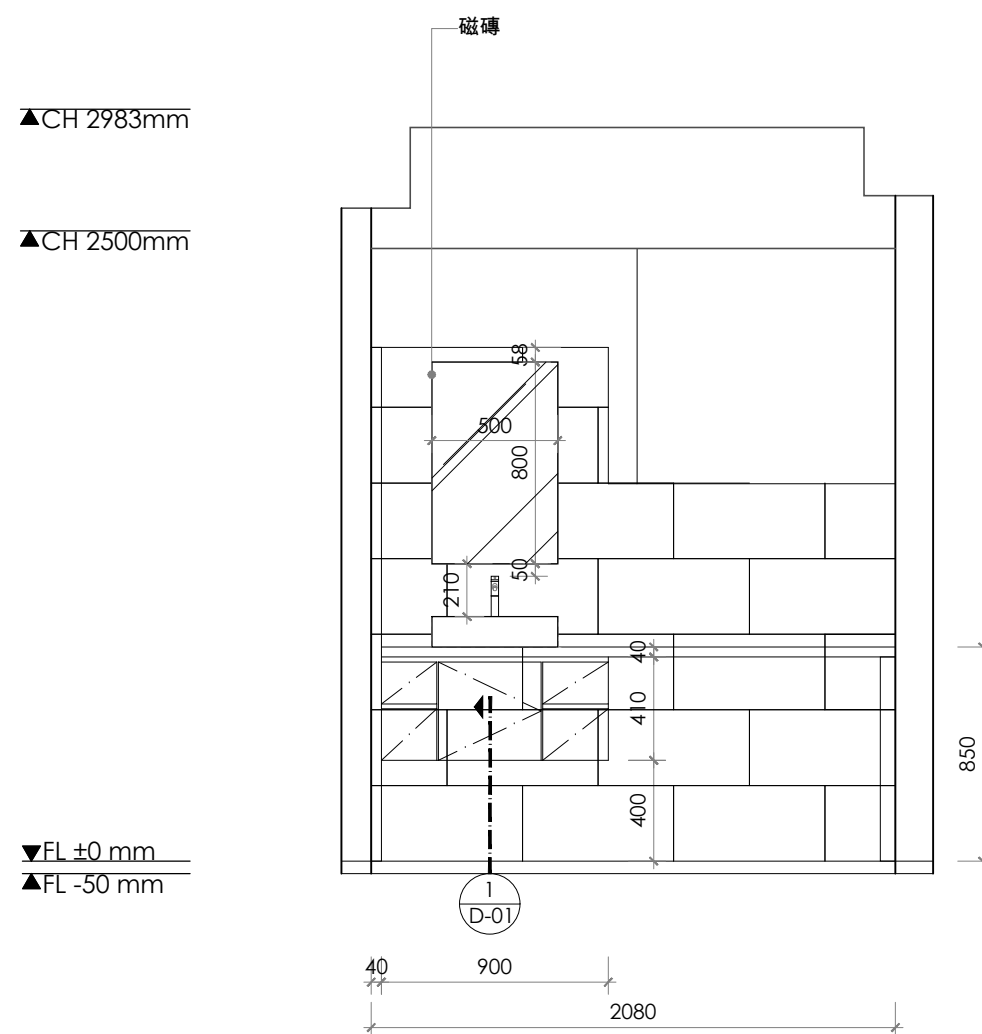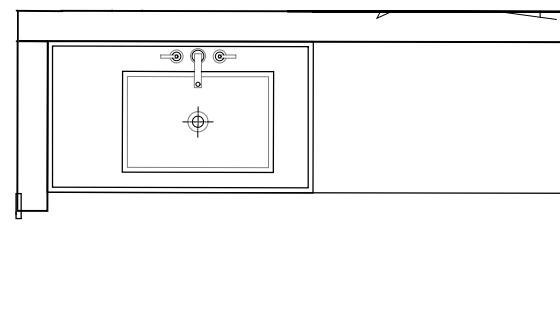

1
E-42

ELEVATION

Scale=1:30

Revision

APPROVAL/核准

設計者:	建築師:
業主:	

備註:

- a. 圖面標註尺寸僅供參考，施作均以現場放樣檢討之。
- b. 圖面標註尺寸、材料及文字敘述因版本不同之差異，均以圖章簽認日期之最近為準。
- c. 電腦圖檔除由合約訂定外，均不得以任何方式外流。
- d. 圖面所示均為本公司所擁有之智慧財產，切勿以任何方式複製修改。



MULA DECO

A 3F, N.26, Ln.290, Guangfu S. Rd., Taipei.
T 886-2-2546-3258
F 886-2-2546-3257
E Guido@muladeco.com


Project / 案名

林口雲品薇閣姚宅

Sheet Title / 圖名
2F

立面圖


Date / 日期	Scale / 比例
8/10/2026	1/30cm
Designer / 設計	Approval / 核准
MONICA LIN	
Job No / 業務編號	Drawn By / 繪圖
00000	GUIDO
Dwg No.	Page No.
E-42	120

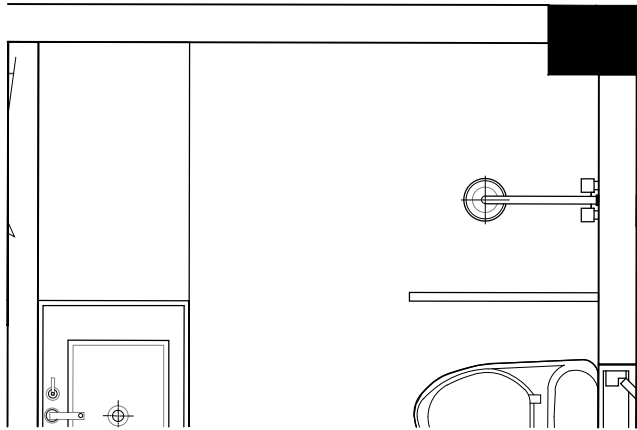

▲CH 2983mm

▲CH 2500mm

▼FL ±0 mm
▲FL -50 mm

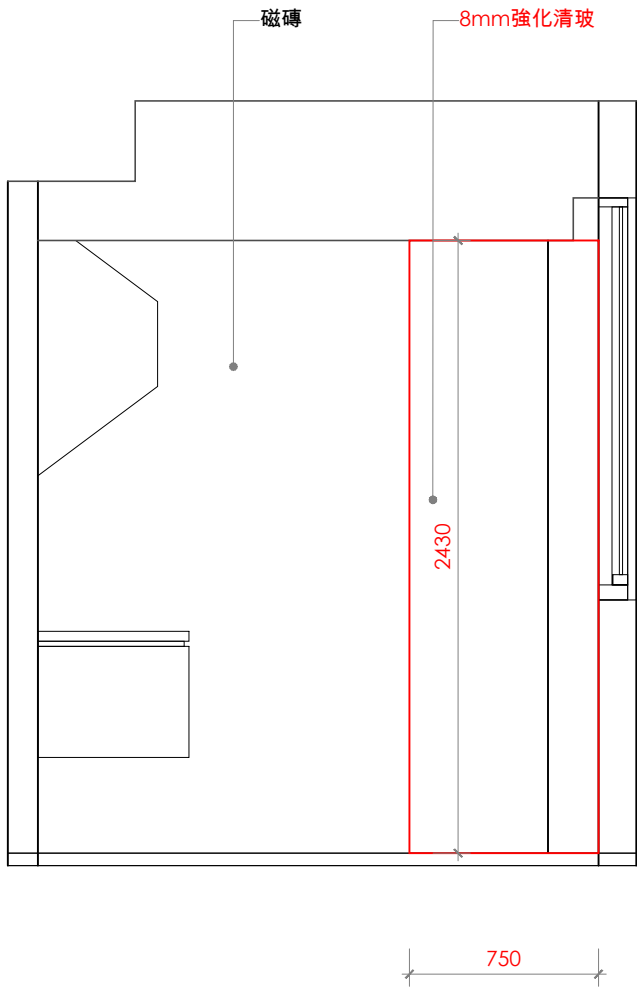

1
E-43

ELEVATION

Scale=1:30

Revision	
APPROVAL/核准	
設計者:	建築師:
業主:	


備註:
a. 圖面標註尺寸僅供參考，施作均以現場放樣檢討之。
b. 圖面標註尺寸、材料及文字敘述因版本不同之差異，均以出圖章簽認日期之最近為準。
c. 電腦圖檔除由合約訂定外，均不得以任何方式外流。
d. 圖面所示均為本公司所擁有之智慧財產，切勿以任何方式複製修改。



MULA DECO
▲ 3F, N.26, Ln.290, Guangfu S. Rd., Taipei.
☎ 886-2-2546-3258
✉ 886-2-2546-3257
E Guido@muladeco.com

Project / 案名	
林口雲品薇閣姚宅	
Sheet Title / 圖名	
2F 立面圖	
Date / 日期	Scale / 比例
8/10/2026	1/30cm
Designer / 設計	Approval / 核准
MONICA LIN	
Job No / 業務編號	Drawn By / 繪圖
00000	GUIDO
Dwg No.	Page No.
E-43	121

▼FL ±0 mm
▲FL -50 mm

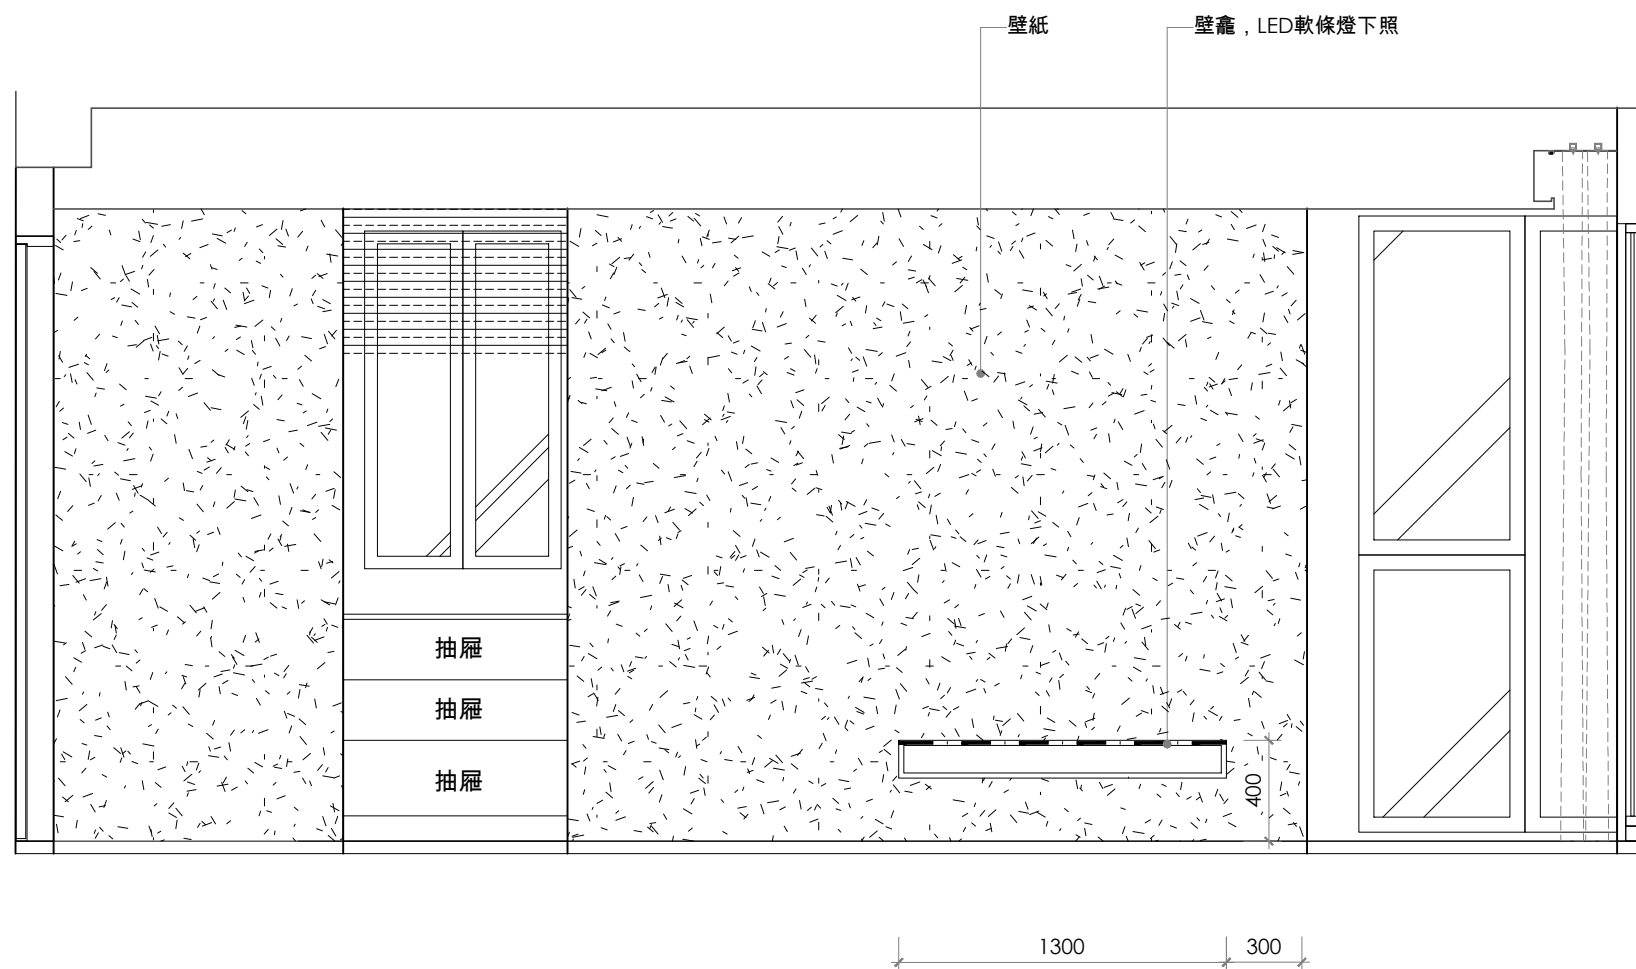

1
E-44

ELEVATION

Scale=1:30

Revision

APPROVAL/核准

設計者:	建築師:
業主:	

備註:

- a. 圖面標註尺寸僅供參考，施作均以現場放樣檢討之。
- b. 圖面標註尺寸、材料及文字敘述因版本不同之差異，均以出圖章簽認日期之最近為準。
- c. 電腦圖檔除由合約訂定外，均不得以任何方式外流。
- d. 圖面所示均為本公司所擁有之智慧財產，切勿以任何方式複製修改。



MULA DECO

A 3F, N.26, Ln.290, Guangfu S. Rd., Taipei.
T 886-2-2546-3258
F 886-2-2546-3257
E Guido@muladeco.com

Project / 案名

林口雲品薇閣姚宅


Sheet Title / 圖名
3F

立面圖

Date / 日期	Scale / 比例
8/10/2026	1/30cm
Designer / 設計	Approval / 核准
MONICA LIN	
Job No / 業務編號	Drawn By / 繪圖
00000	GUIDO
Dwg No	Page No

E-44


122

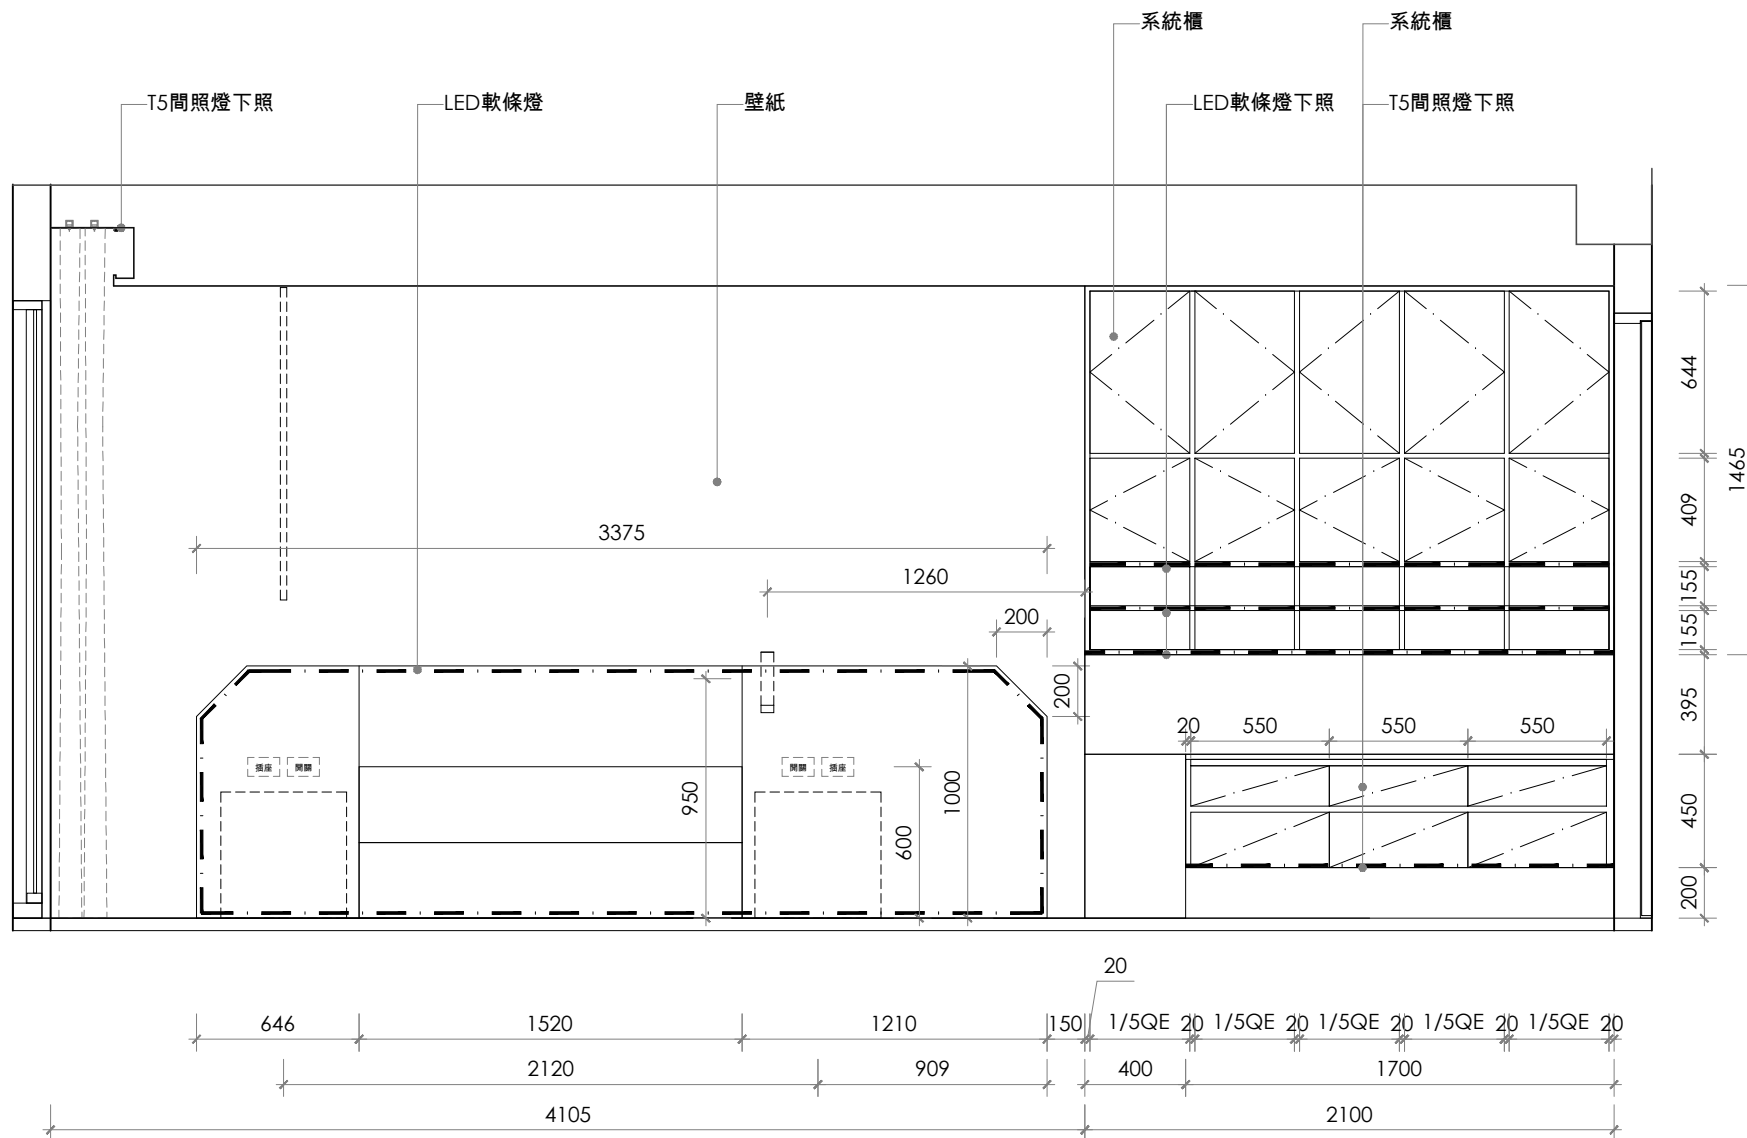

▼FL ±0 mm
▲FL -50 mm

Scale=1:30

E-45 123

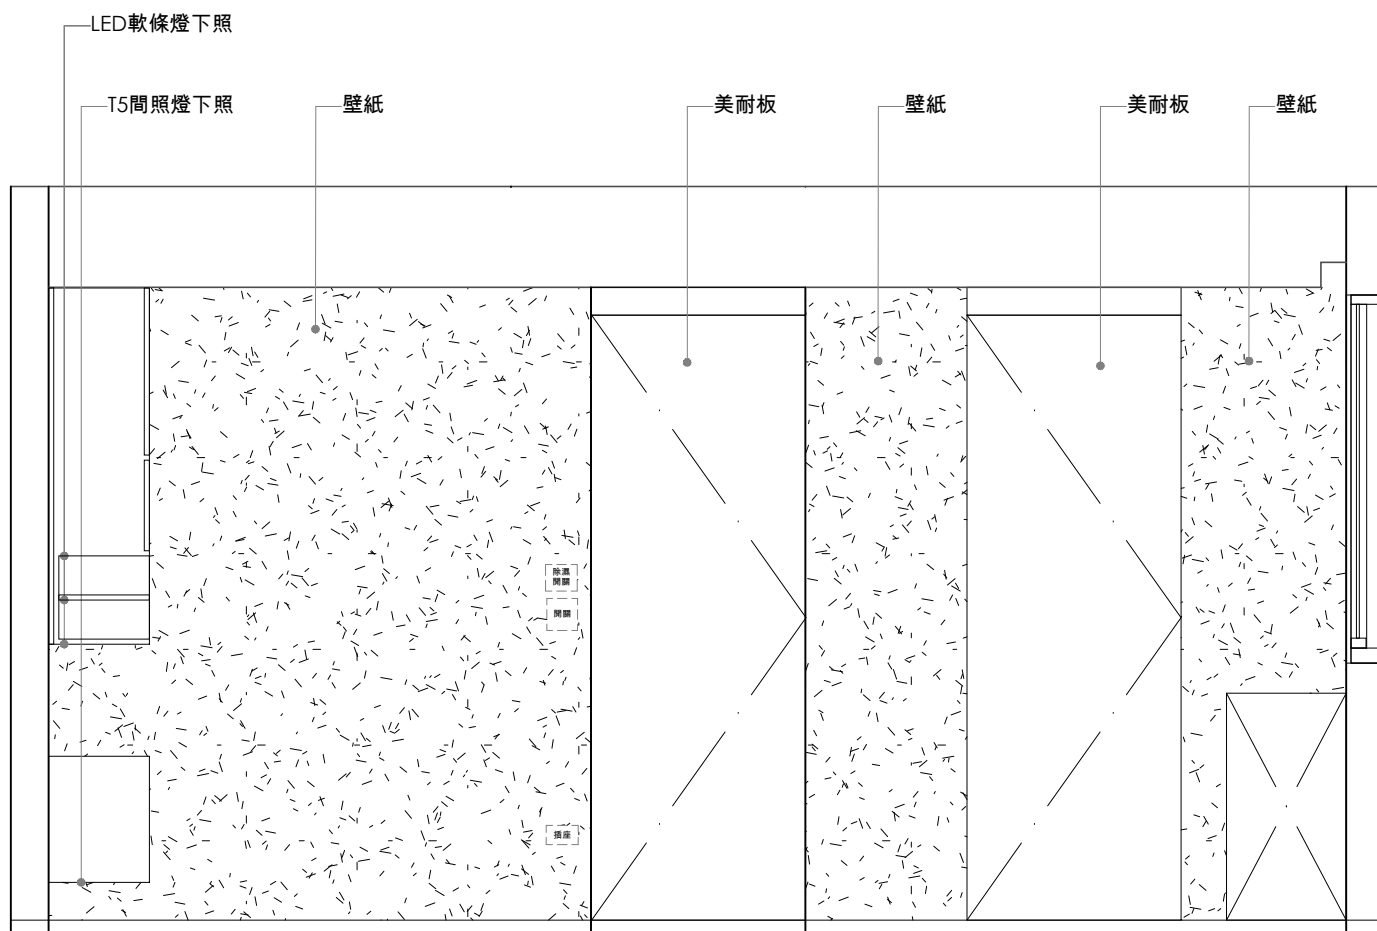


▼FL ±0 mm
▲FL -50 mm

1
E-46

Scale=1:30



E-46 124

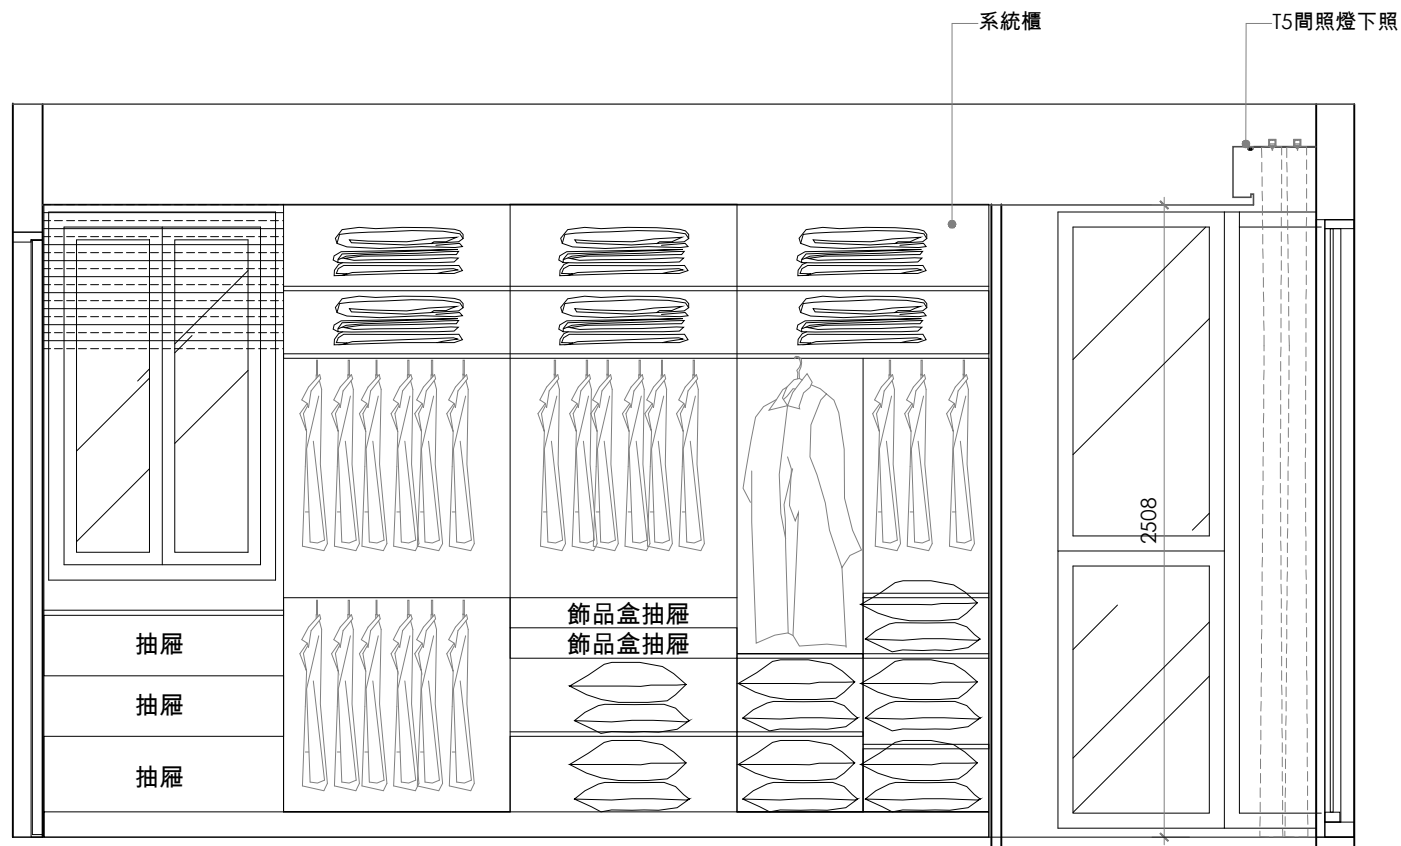

▼FL ±0 mm
▲FL -50 mm

Scale=1:30

125

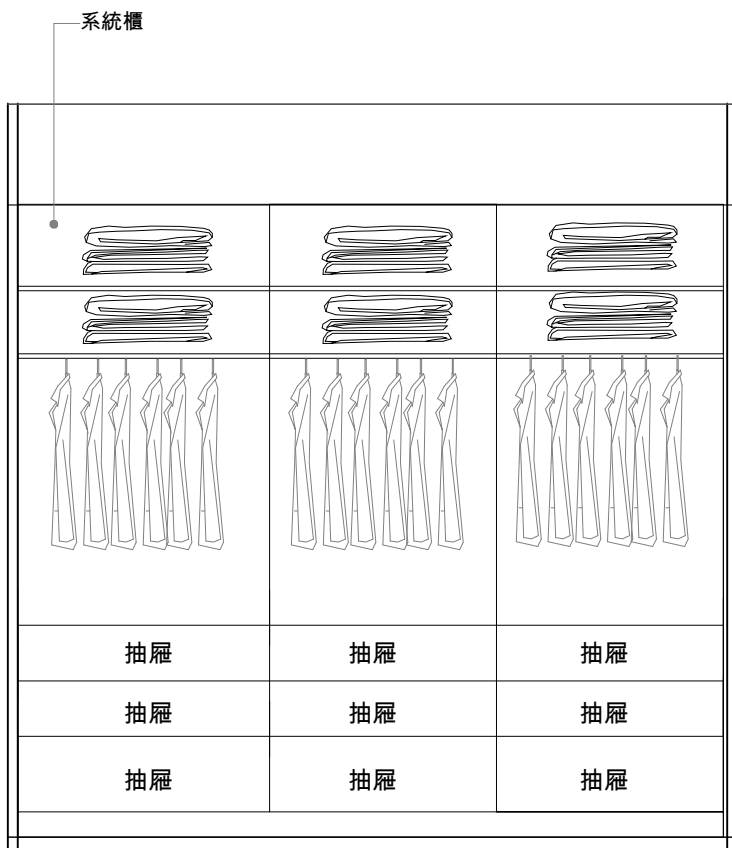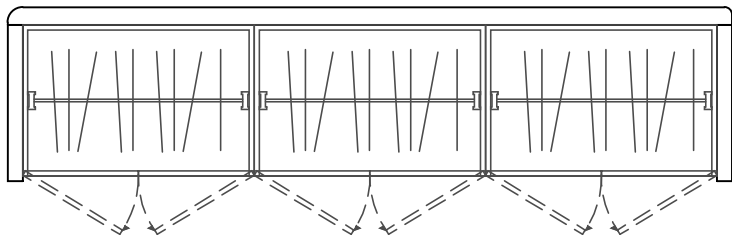

▲CH 2908mm

▲CH 2510mm

▼FL ±0 mm
▲FL -50 mm

840

1
E-48

ELEVATION

Scale=1:30


Revision	
APPROVAL/核准	
設計者:	建築師:
業主:	

備註:
a. 圖面標註尺寸僅供參考，施作均以現場放樣檢討之。
b. 圖面標註尺寸、材料及文字敘述因版本不同之差異，均以出圖章簽認日期之最近為準。
c. 電腦圖檔除由合約訂定外，均不得以任何方式外流。
d. 圖面所示均為本公司所擁有之智慧財產，切勿以任何方式複製修改。





MULA DECO
▲ 3F, N.26, Ln.290, Guangfu S. Rd., Taipei.
☎ 886-2-2546-3258
☎ 886-2-2546-3257
✉ Guido@muladeco.com

Project / 案名	
林口雲品薇閣姚宅	
Sheet Title / 圖名	
3F 立面圖	
Date / 日期	Scale / 比例
8/10/2026	1/30cm
Designer / 設計	Approval / 核准
MONICA LIN	
Job No / 業務編號	Drawn By / 繪圖
00000	GUIDO
Dwg No.	Page No.
E-48	126

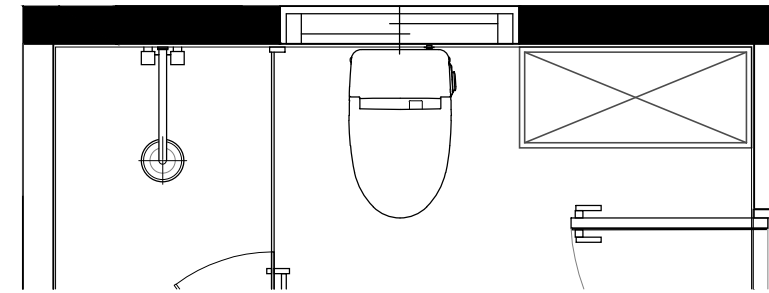

Scale=1:30

E-49 127

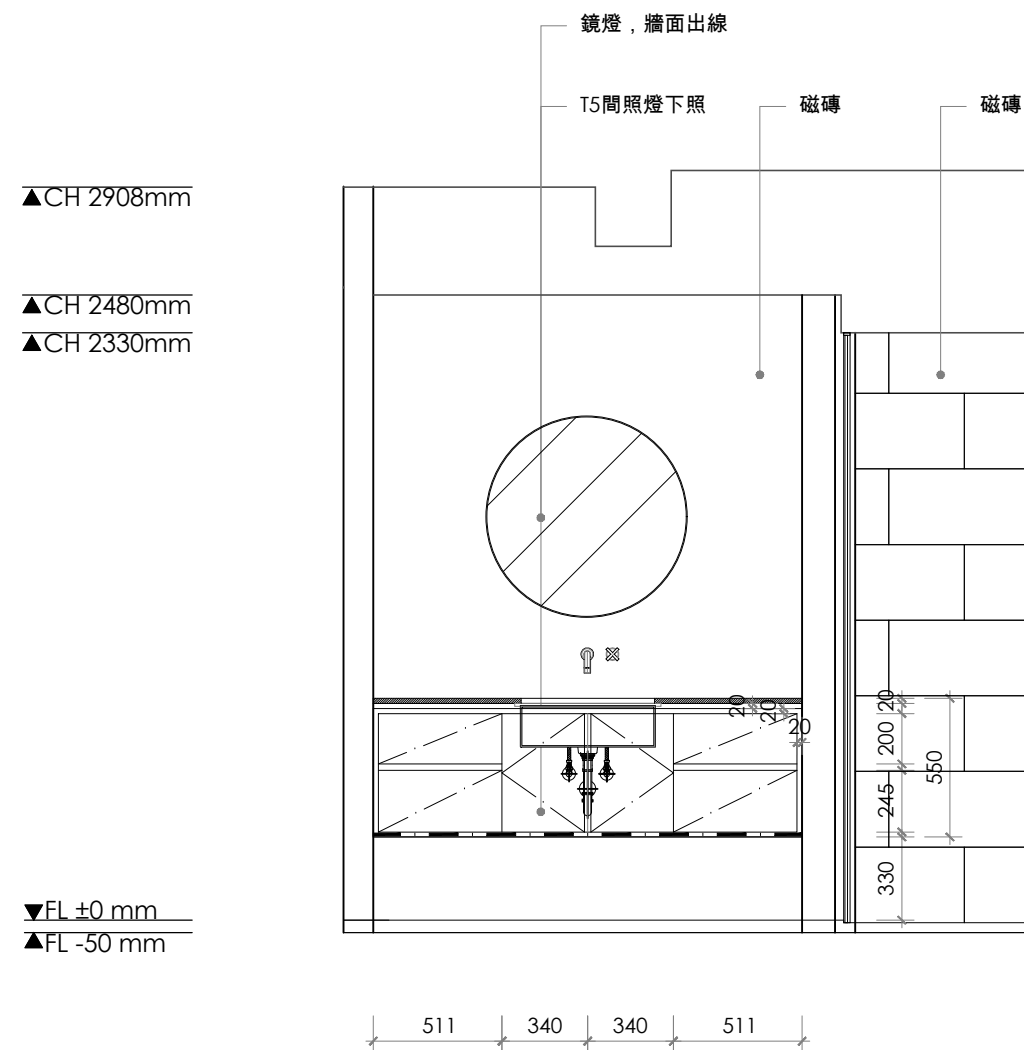
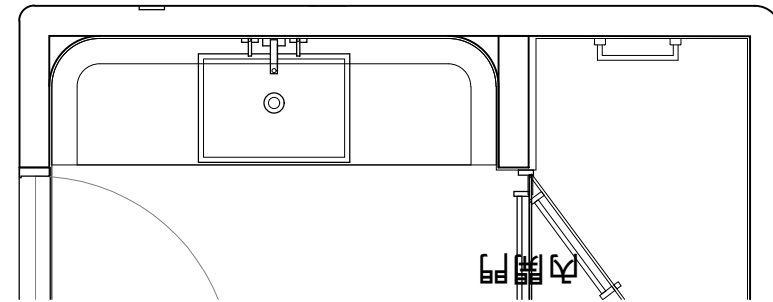


▲FL -50 mm

▲FL -50 mm

Scale=1:30

F-50 128

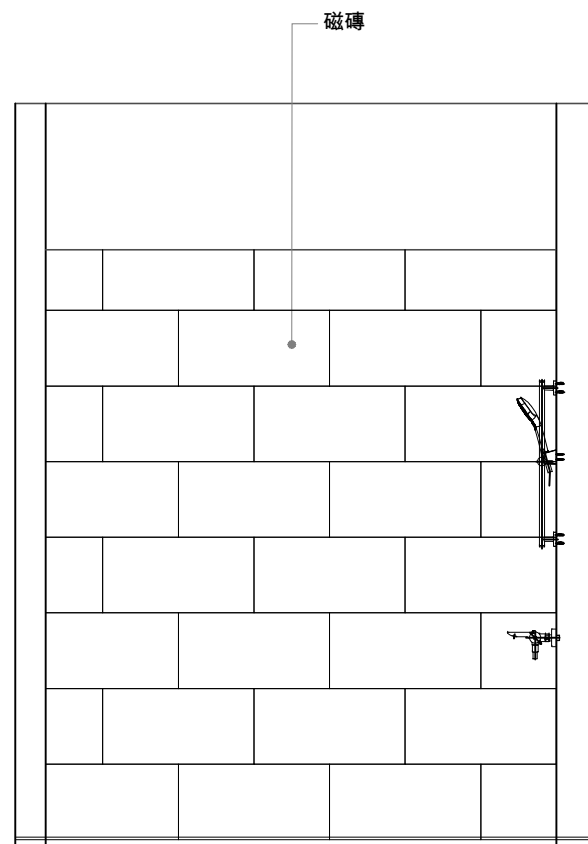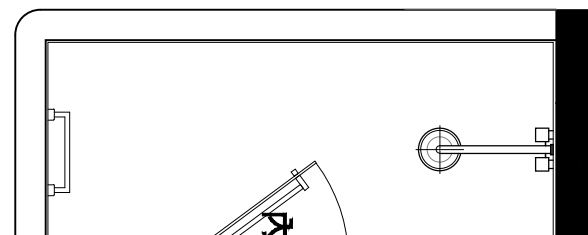

Scale=1:30

APPROVAL/核准	
設計者:	建築師:
業主:	

備註:

- a. 圖面標註尺寸僅供參考，施作均以現場放樣檢討之。
- b. 圖面標註尺寸、材料及文字敘述因版本不同之差異，均以圖章簽認日期之最近為準。
- c. 電腦圖檔除由合約訂定外，均不得以任何方式外流。
- d. 圖面所示均為本公司所擁有之智慧財產，切勿以任何方式複製修改。




Project / 案名

林口雲品薇閣姚宅

Sheet Title / 圖名
3F

立面圖

E-51 129

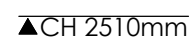


▼FL ±0 mm
▲FL -50 mm



ELEVATION

Scale=1:30

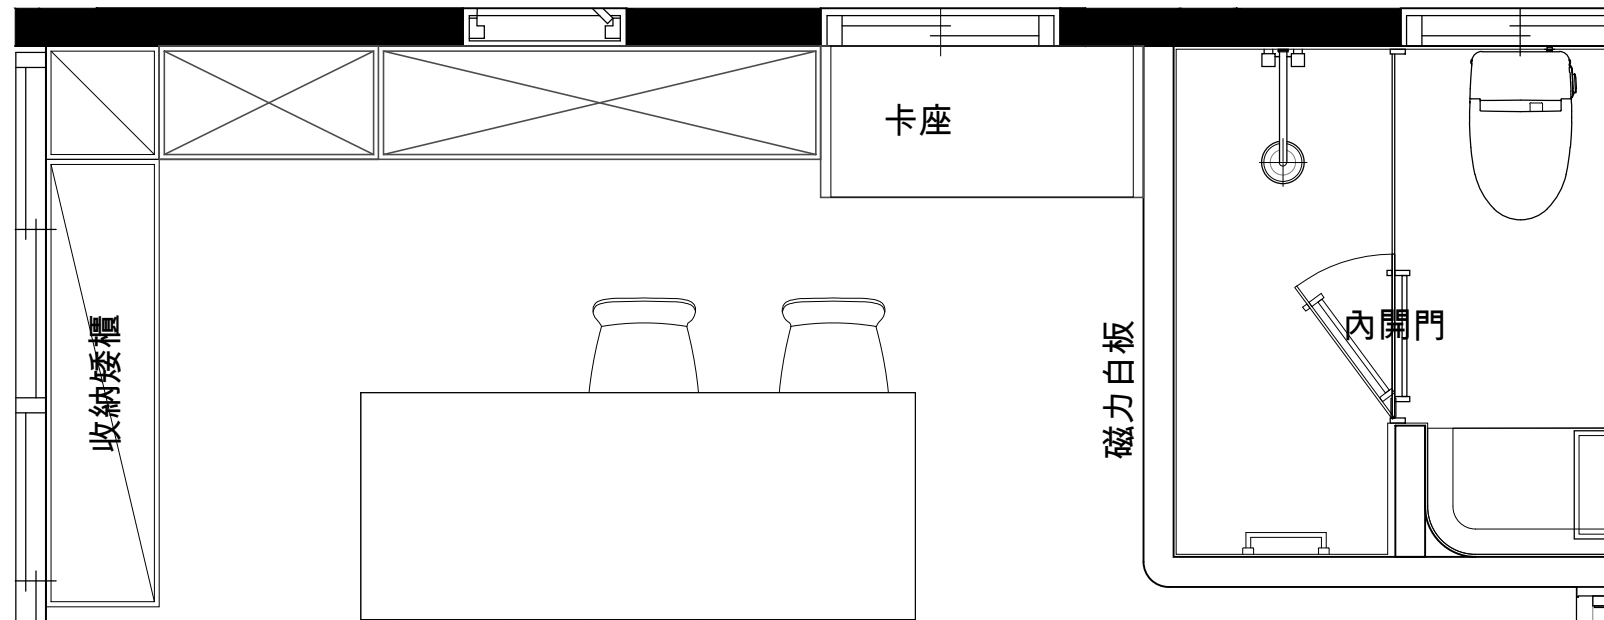

Revision

APPROVAL/核准

設計者:

建築師:

業主:

葡註:

圖面標註尺寸僅供參考，施作均以現場放樣檢討之。

圖面標註尺寸、材料及文字敘述因版本不同之差異，均以出圖蓋章簽日期之最近為準。

電腦圖檔除由合約訂定外，均不得以任何方式外流。

圖面所示均為本公司所擁有之智慧財產，切勿以任何方式複製修改。



MULA DECO

A 3F, N.26, Ln.290, Guangfu S. Rd., Taipei.
T 886-2-2546-3258
F 886-2-2546-3257
E Guido@muladeco.com

Project / 案名

林口雲品薇閣姚宅

Sheet Title / 圖名
3F


立面圖

Date / 日期	Scale / 比例
8/10/2026	1/30cm
Designer / 設計	Approval / 核准
MONICA LIN	
Job No / 案號編號	Drawn By / 繪圖
00000	GUIDO
Dwg No.	Page No.
E-52	130

E-52

30



32

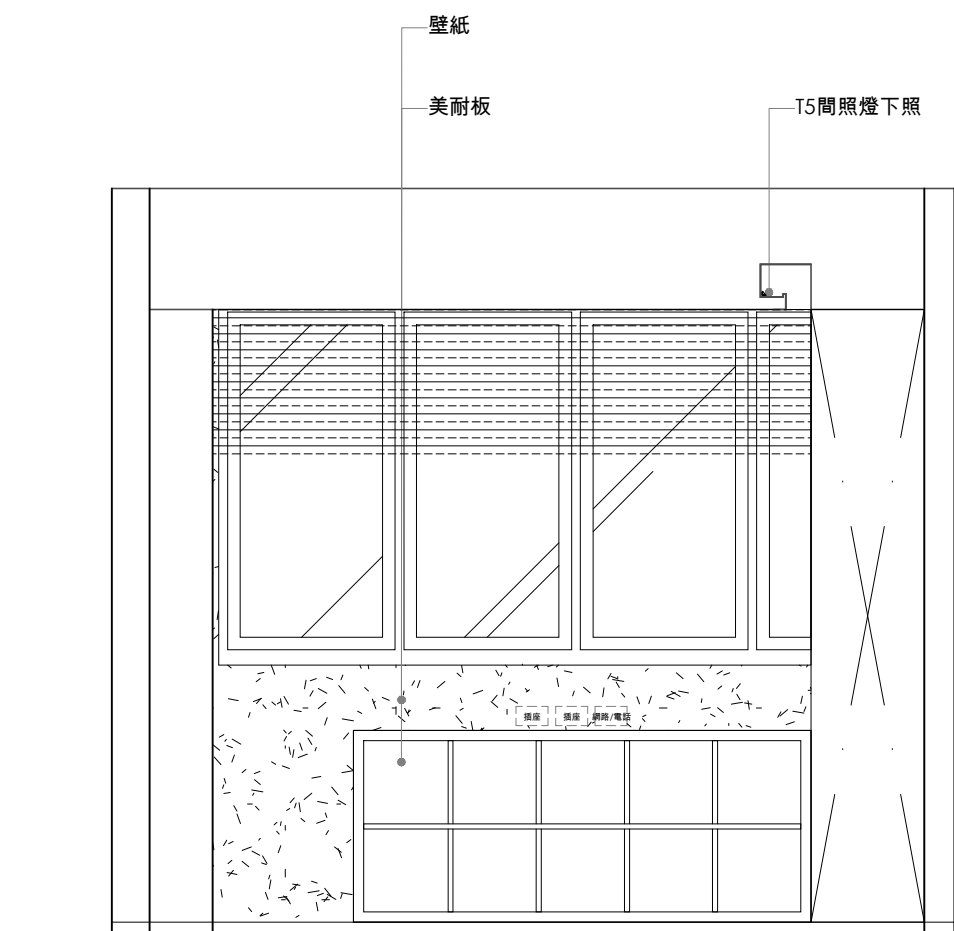

▼FL ±0 mm
▲FL -50 mm

Scale=1:30

133

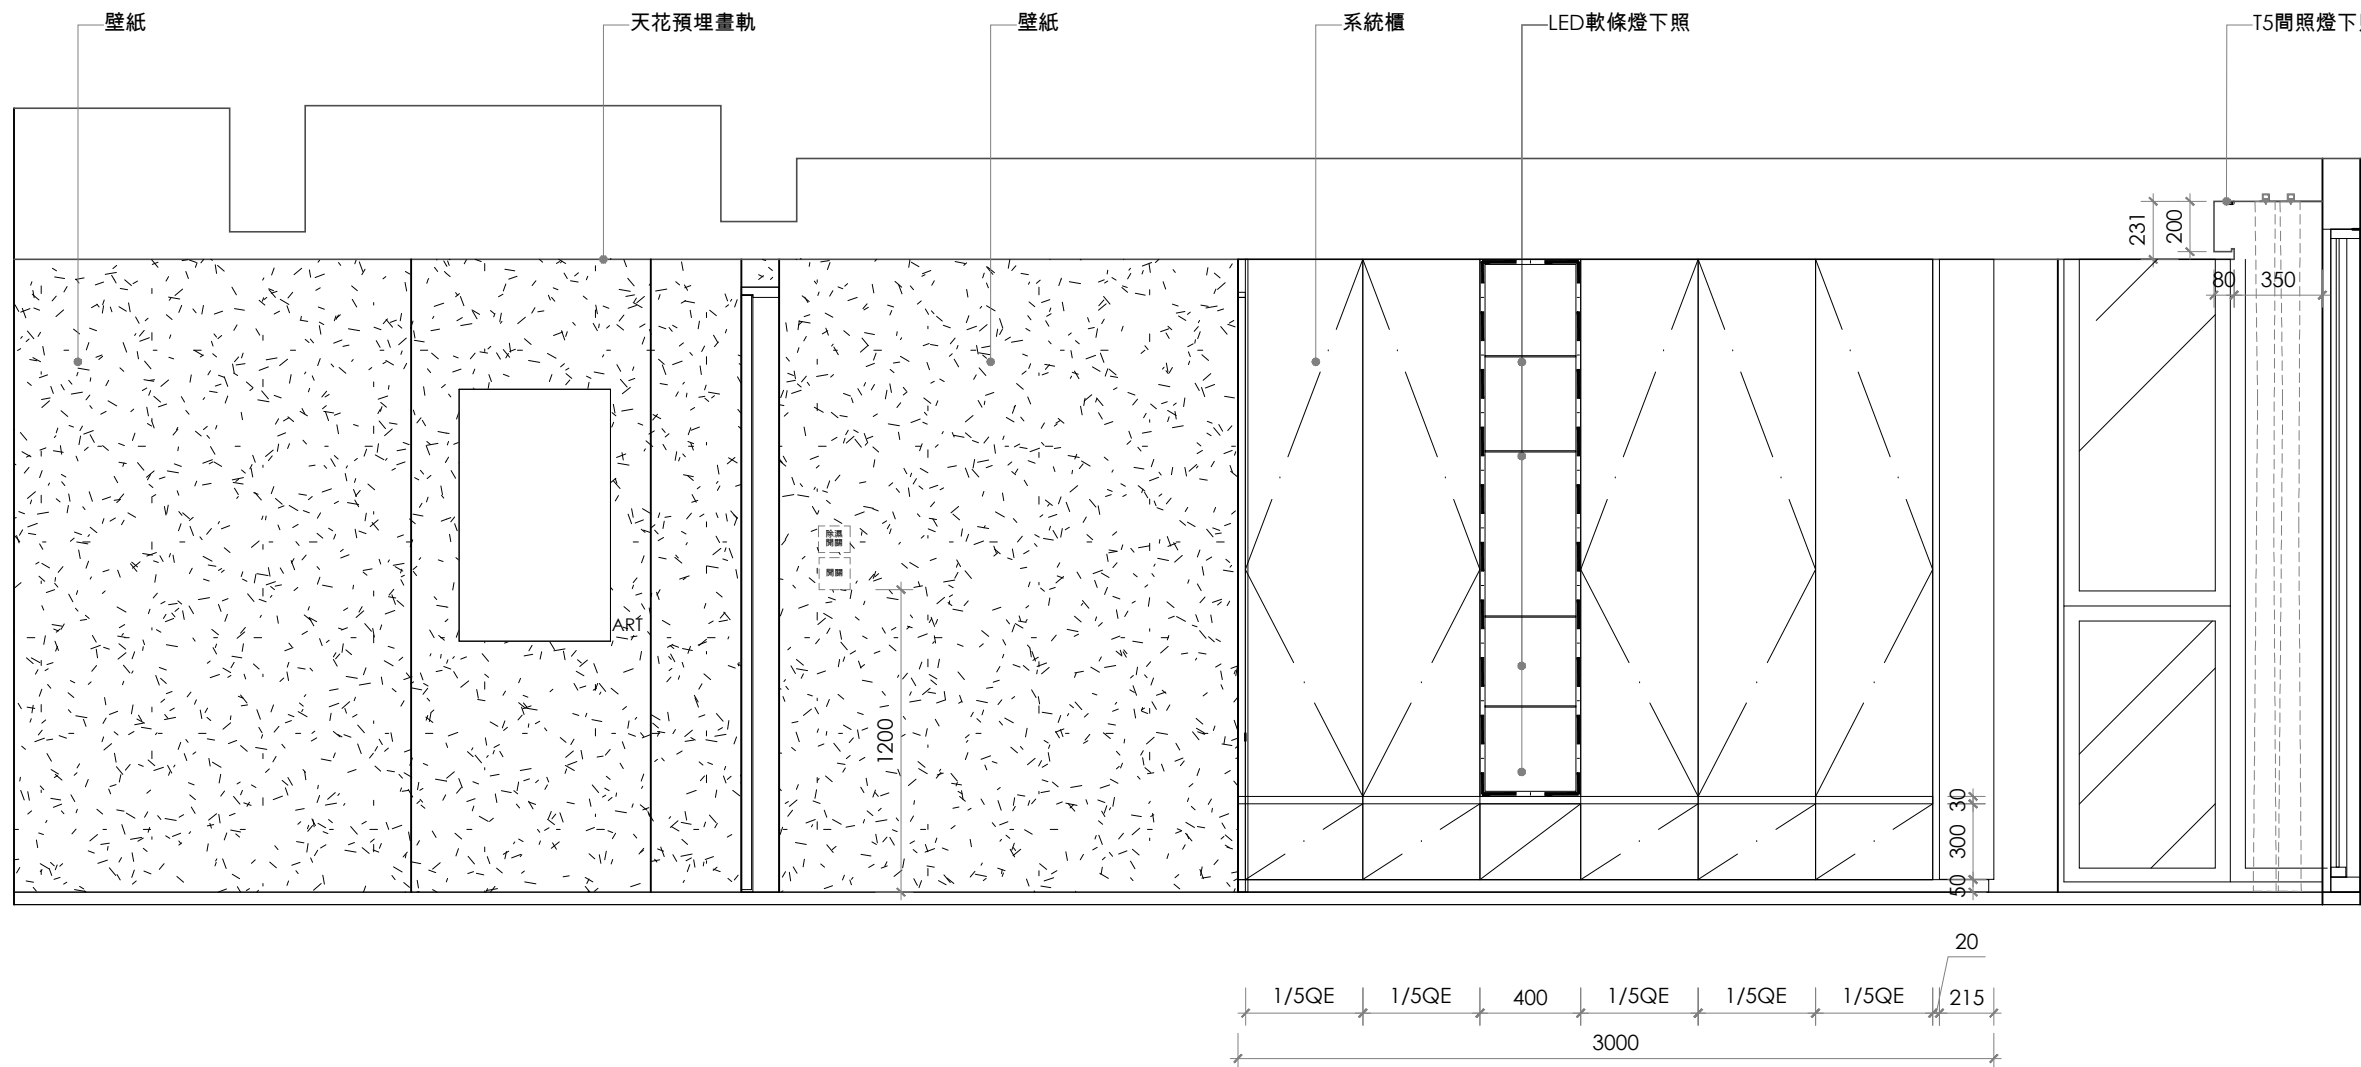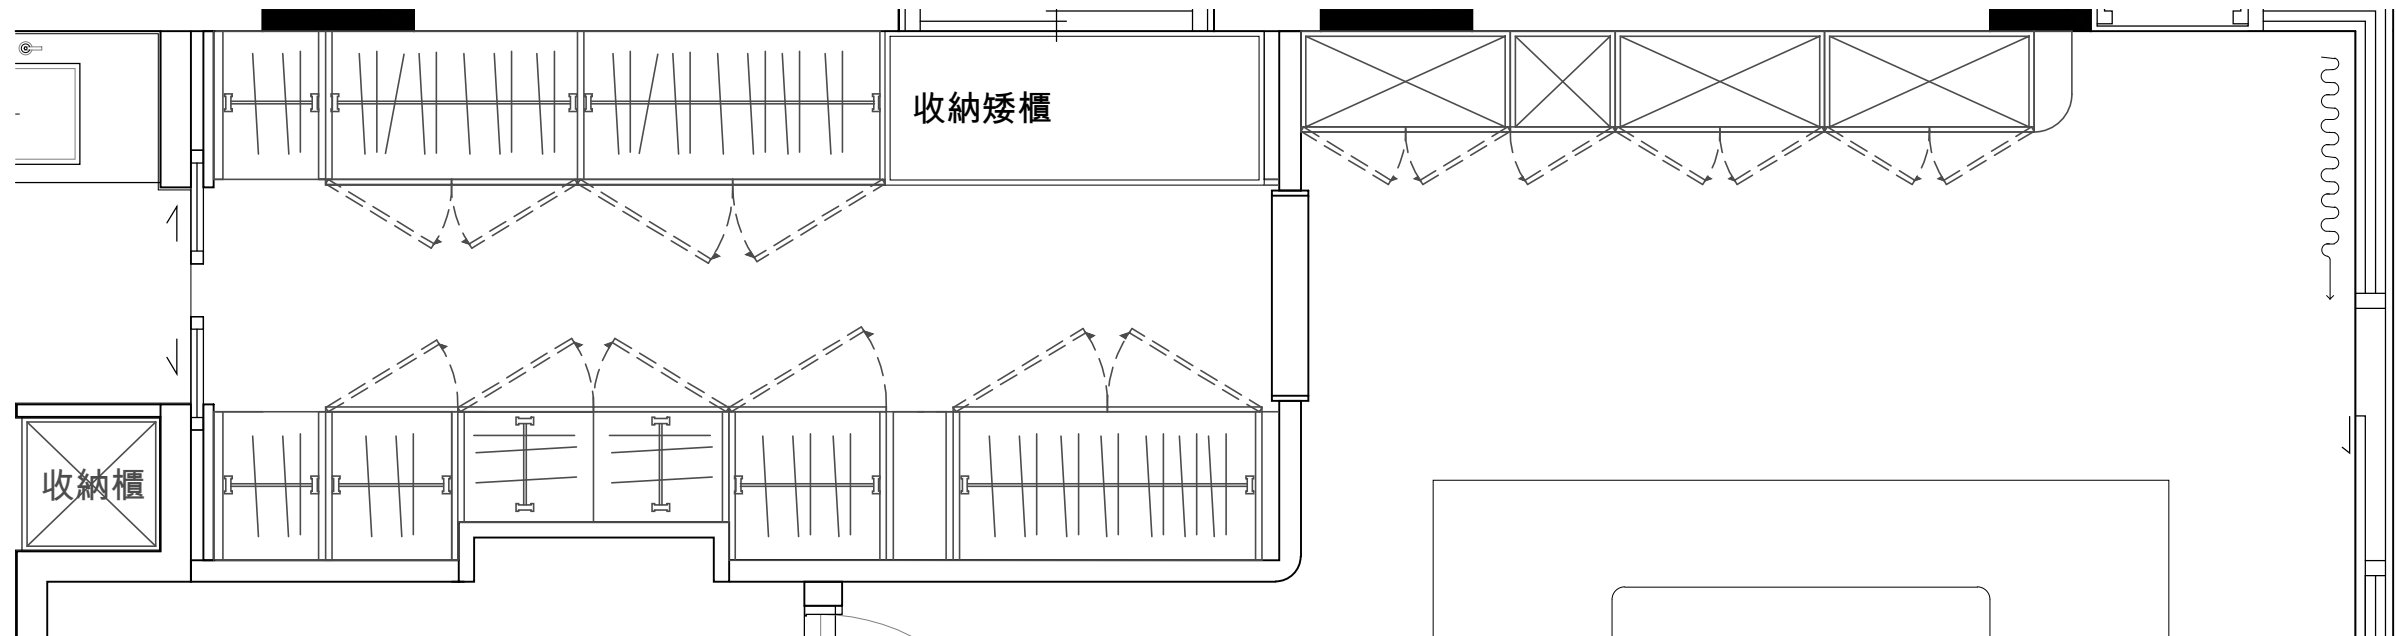

▲CH 3120mm

▲CH 2910mm

▲CH 2510mm

▲CH 2430mm

▼FL ±0 mm

▲FL -50 mm

1
E-56

ELEVATION

Scale=1:30

Revision

APPROVAL/核准

設計者:	建築師:
業主:	

備註:

- 圖面標註尺寸僅供參考，施作均以現場放樣檢討之。
- 圖面標註尺寸、材料及文字敘述因版本不同之差異，均以出圖章簽認日期之最近為準。
- 電腦圖檔除由合約訂定外，均不得以任何方式外流。
- 圖面所示均為本公司所擁有之智慧財產，切勿以任何方式複製修改。



MULA DECO

▲ 3F, N.26, Ln.290, Guangfu S. Rd., Taipei.
☎ 886-2-2546-3258
☎ 886-2-2546-3257
✉ Guido@muladeco.com

Project / 案名

林口雲品薇閣姚宅


Sheet Title / 圖名
4F

立面圖

Date / 日期	Scale / 比例
8/10/2026	1/30cm
Designer / 設計	Approval / 核准
MONICA LIN	
Job No / 業務編號	Drawn By / 繪圖
00000	GUIDO
Dwg No.	Page No.

E-56

134

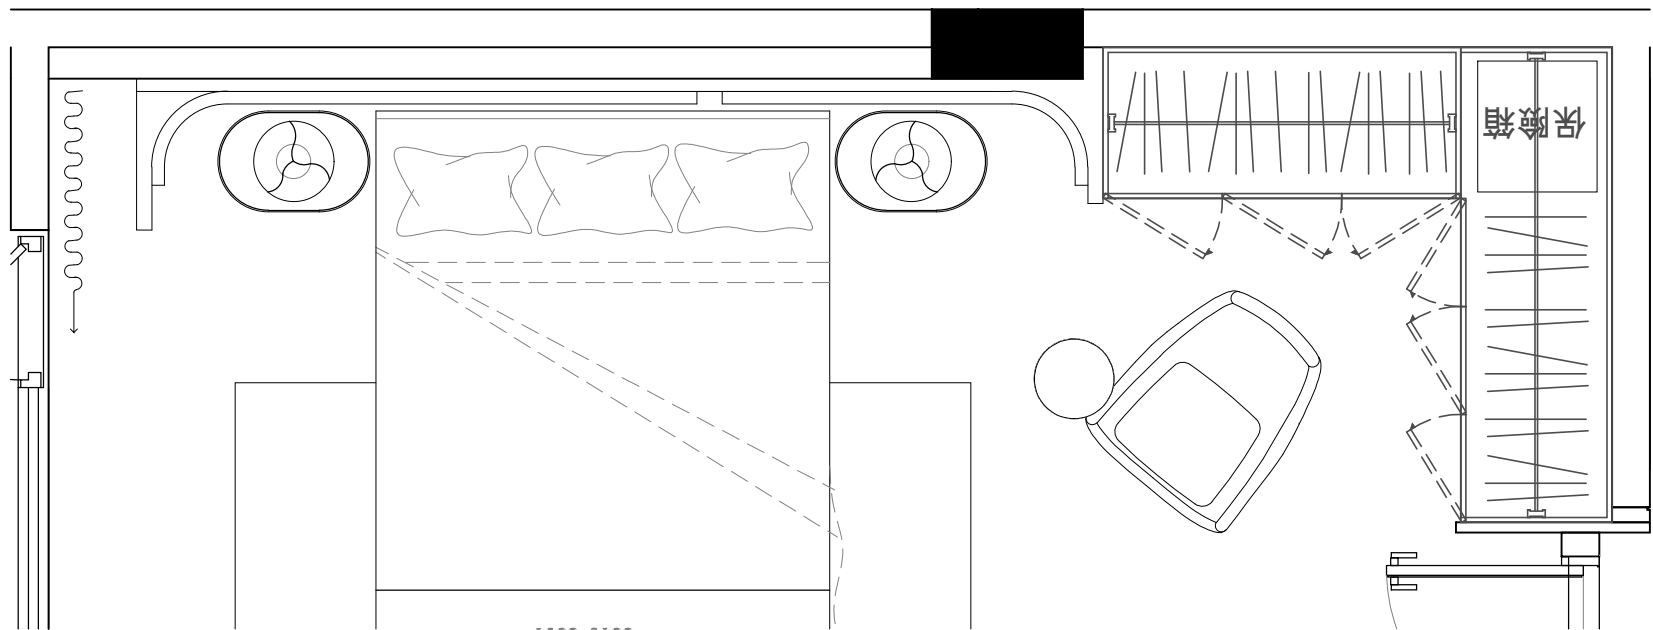

▲CH 3120mm



▲CH 2910mm

▲CH 2510mm

▲CH 2430mm

▼FL ±0 mm

▲FL -50 mm

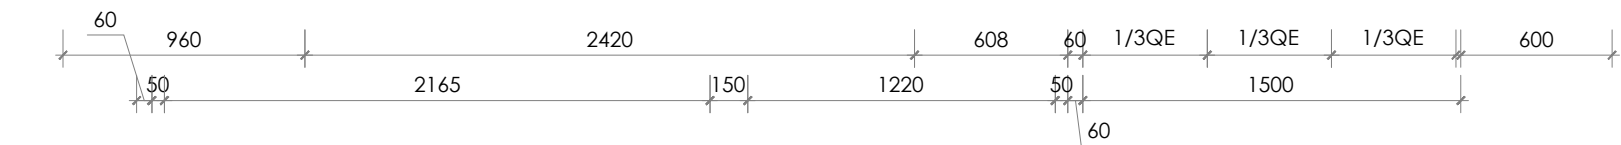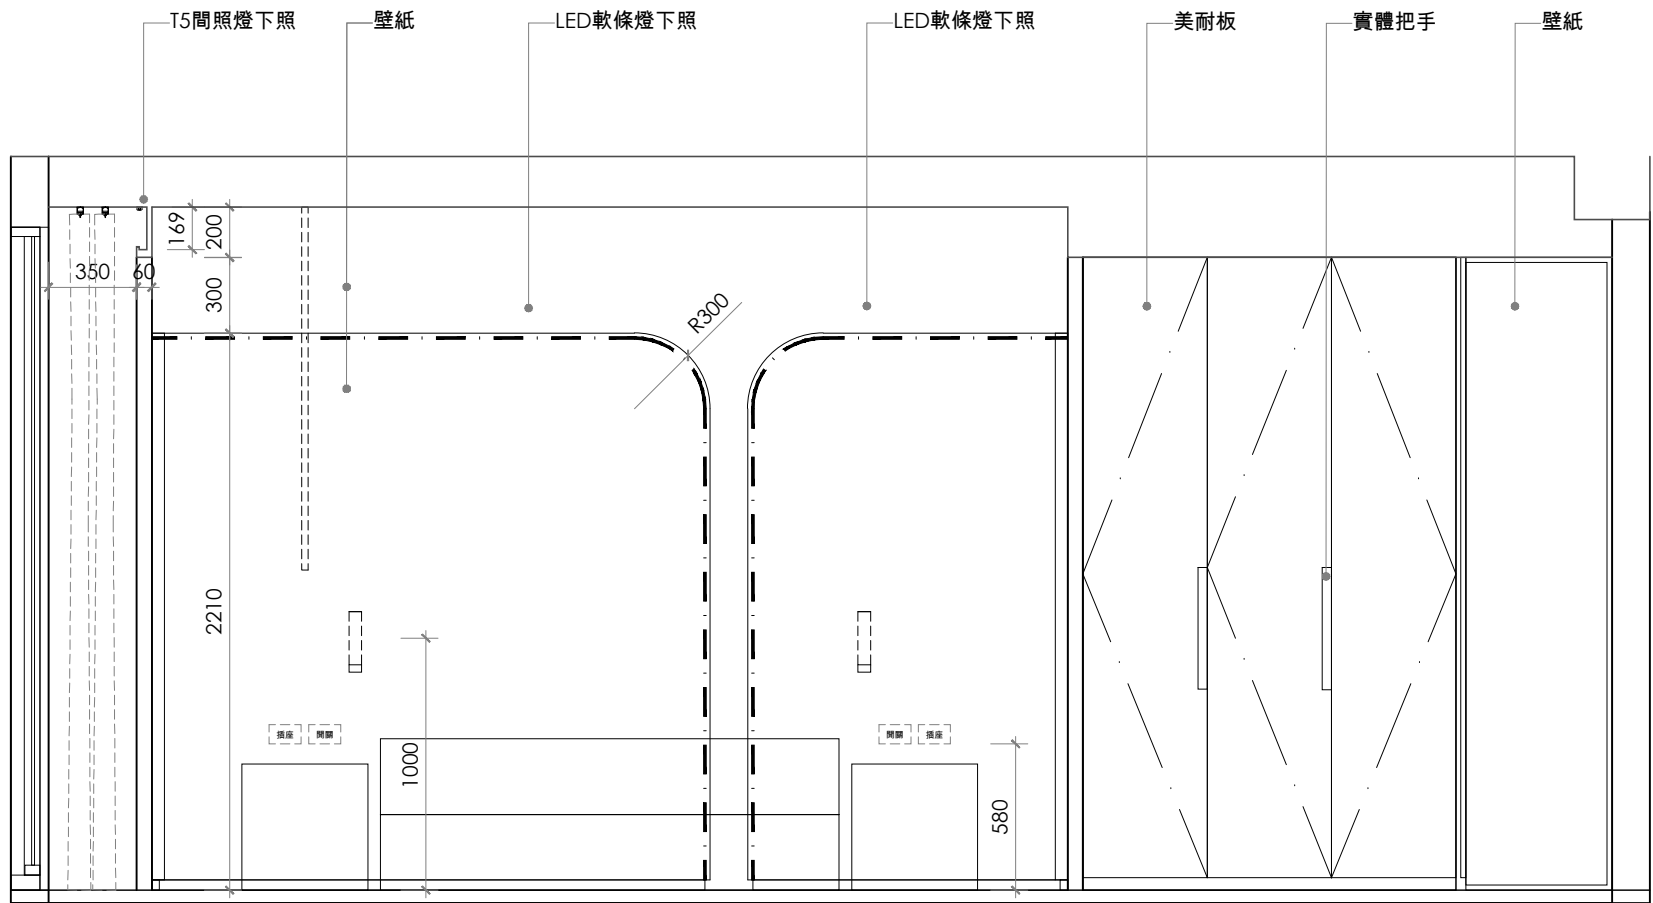

1
E-57

ELEVATION

Scale=1:30

Revision

APPROVAL/核准

設計者:	建築師:
業主:	

備註:

- 圖面標註尺寸僅供參考，施作均以現場放樣檢討之。
- 圖面標註尺寸、材料及文字敘述因版本不同之差異，均以出圖章簽認日期之最近為準。
- 電腦圖檔除由合約訂定外，均不得以任何方式外流。
- 圖面所示均為本公司所擁有之智慧財產，切勿以任何方式複製修改。



MULA DECO

▲ 3F, N.26, Ln.290, Guangfu S. Rd., Taipei.
☎ 886-2-2546-3258
☎ 886-2-2546-3257
✉ Guido@muladeco.com

Project / 案名

林口雲品薇閣姚宅



Sheet Title / 圖名
4F

立面圖

Date / 日期	Scale / 比例
8/10/2026	1/30cm
Designer / 設計	Approval / 核准
MONICA LIN	
Job No / 業務編號	Drawn By / 繪圖
00000	GUIDO
Dwg No.	Page No.

E-57

135

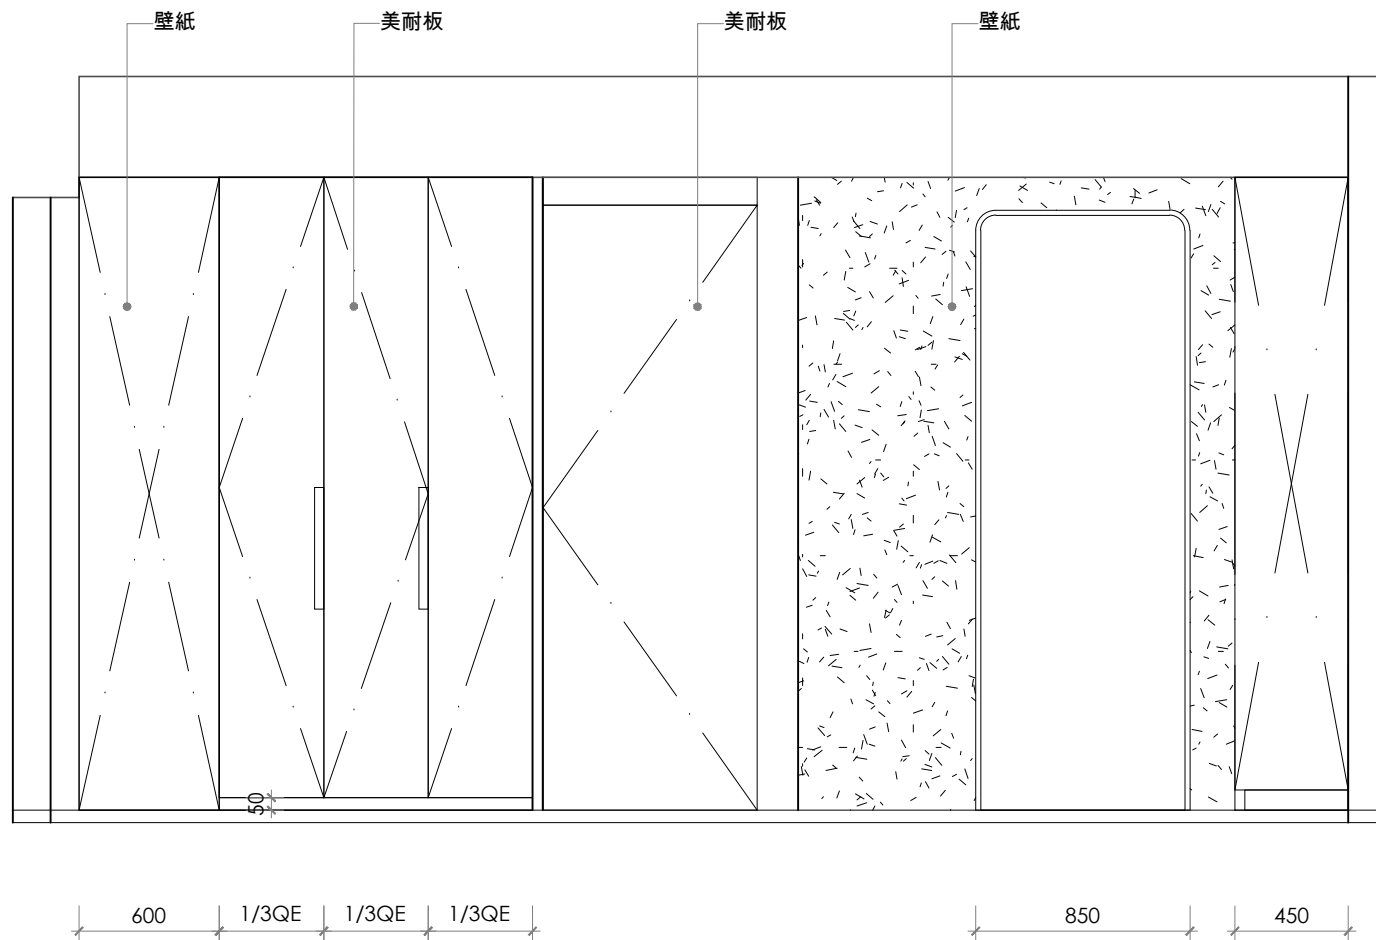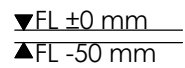

1
E-58

ELEVATION

Scale=1:30

[illegible]

APPROVAL/核准

設計者:	建築師:
業主:	

葡註:

- 圖面標註尺寸僅供參考，施作均以現場放樣檢討之。
- 圖面標註尺寸、材料及文字敘述因版本不同之差異，均以出圖章簽認日期之最近為準。
- 電腦圖檔除由合約訂定外，均不得以任何方式外流。
- 圖面所示均為本公司所擁有之智慧財產，切勿以任何方式複製修改。



MULA DECO

A 3F, N.26, Ln.290, Guangfu S. Rd., Taipei.
T 886-2-2546-3258
F 886-2-2546-3257
E Guido@muladeco.com

Project / 案名

林口雲品薇閣姚宅


Sheet Title / 圖名
4F

立面圖

Date / 日期	Scale / 比例
8/10/2026	1/30cm
Designer / 設計	Approval / 核准
MONICA LIN	
Job No / 業務編號	Drawn By / 繪圖
00000	GUIDO
Dwg No.	Page No.
E-58	136

E-58


36

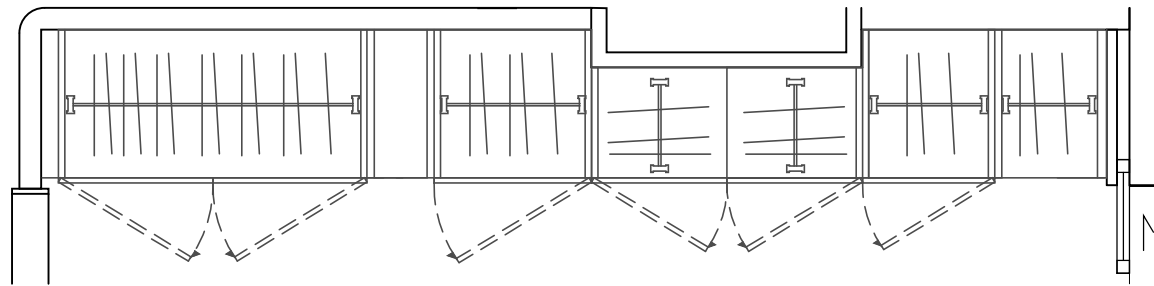

▲CH 3120mm
▲CH 2910mm

▲CH 2510mm
▲CH 2430mm

▼FL ±0 mm
▲FL -50 mm

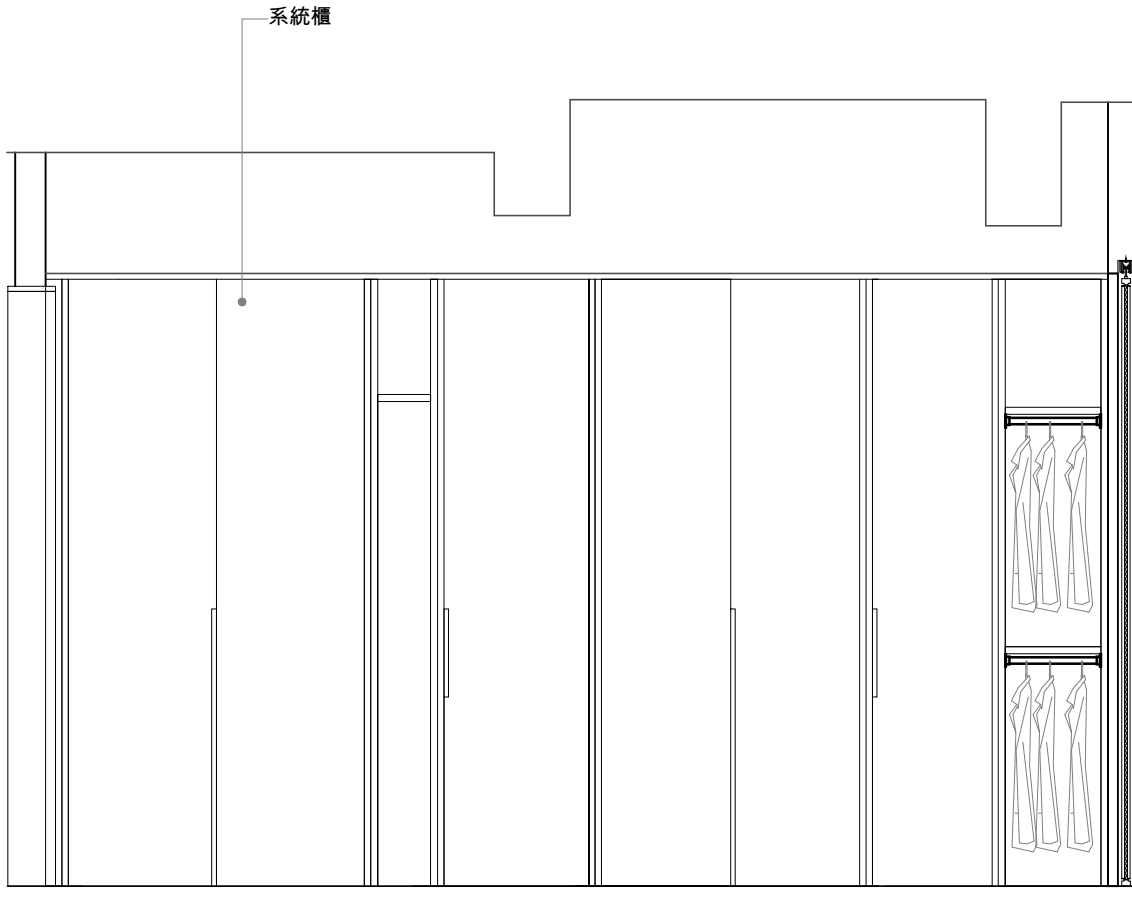

1
E-60

ELEVATION

Scale=1:30

Revision

APPROVAL/核准

設計者:	建築師:
業主:	

備註:

- a. 圖面標註尺寸僅供參考，施作均以現場放樣檢討之。
- b. 圖面標註尺寸、材料及文字敘述因版本不同之差異，均以出圖章簽認日期之最近為準。
- c. 電腦圖檔除由合約訂定外，均不得以任何方式外流。
- d. 圖面所示均為本公司所擁有之智慧財產，切勿以任何方式複製修改。



MULA DECO

▲ 3F, N.26, Ln.290, Guangfu S. Rd., Taipei.
☎ 886-2-2546-3258
✉ 886-2-2546-3257
E Guido@muladeco.com

Project / 案名

林口雲品薇閣姚宅



Sheet Title / 圖名
4F

立面圖

Date / 日期	Scale / 比例
8/10/2026	1/30cm
Designer / 設計	Approval / 核准
MONICA LIN	
Job No / 業務編號	Drawn By / 繪圖
00000	GUIDO
Dwg No.	Page No.

E-60

138

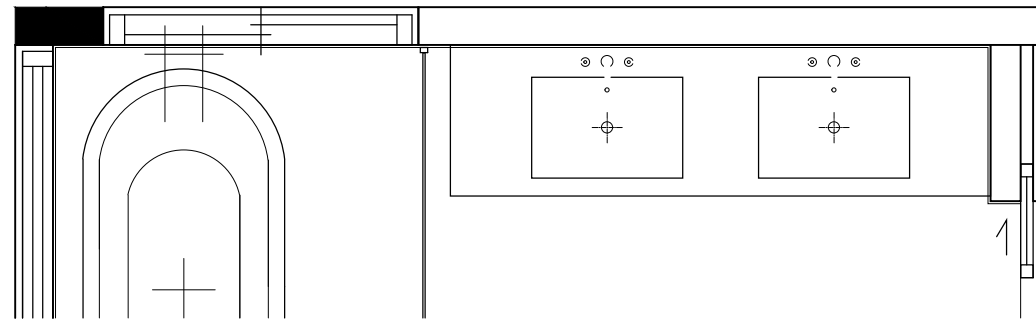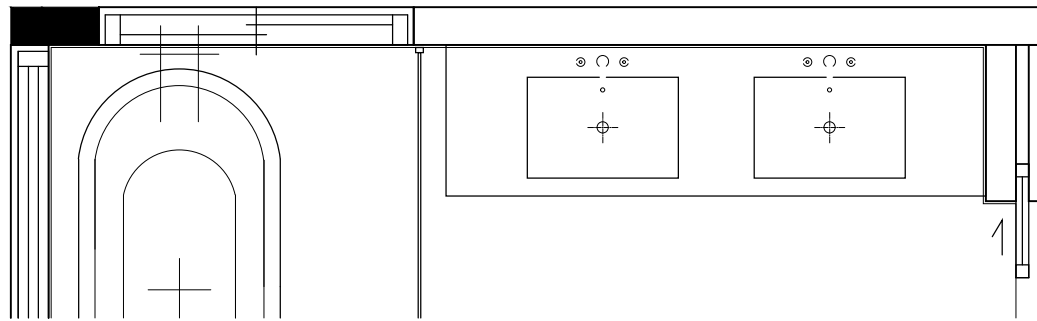

▲CH 3120mm



▲CH 2910mm

▲CH 2510mm

▲CH 2430mm

▼FL ±0 mm

▲FL -50 mm

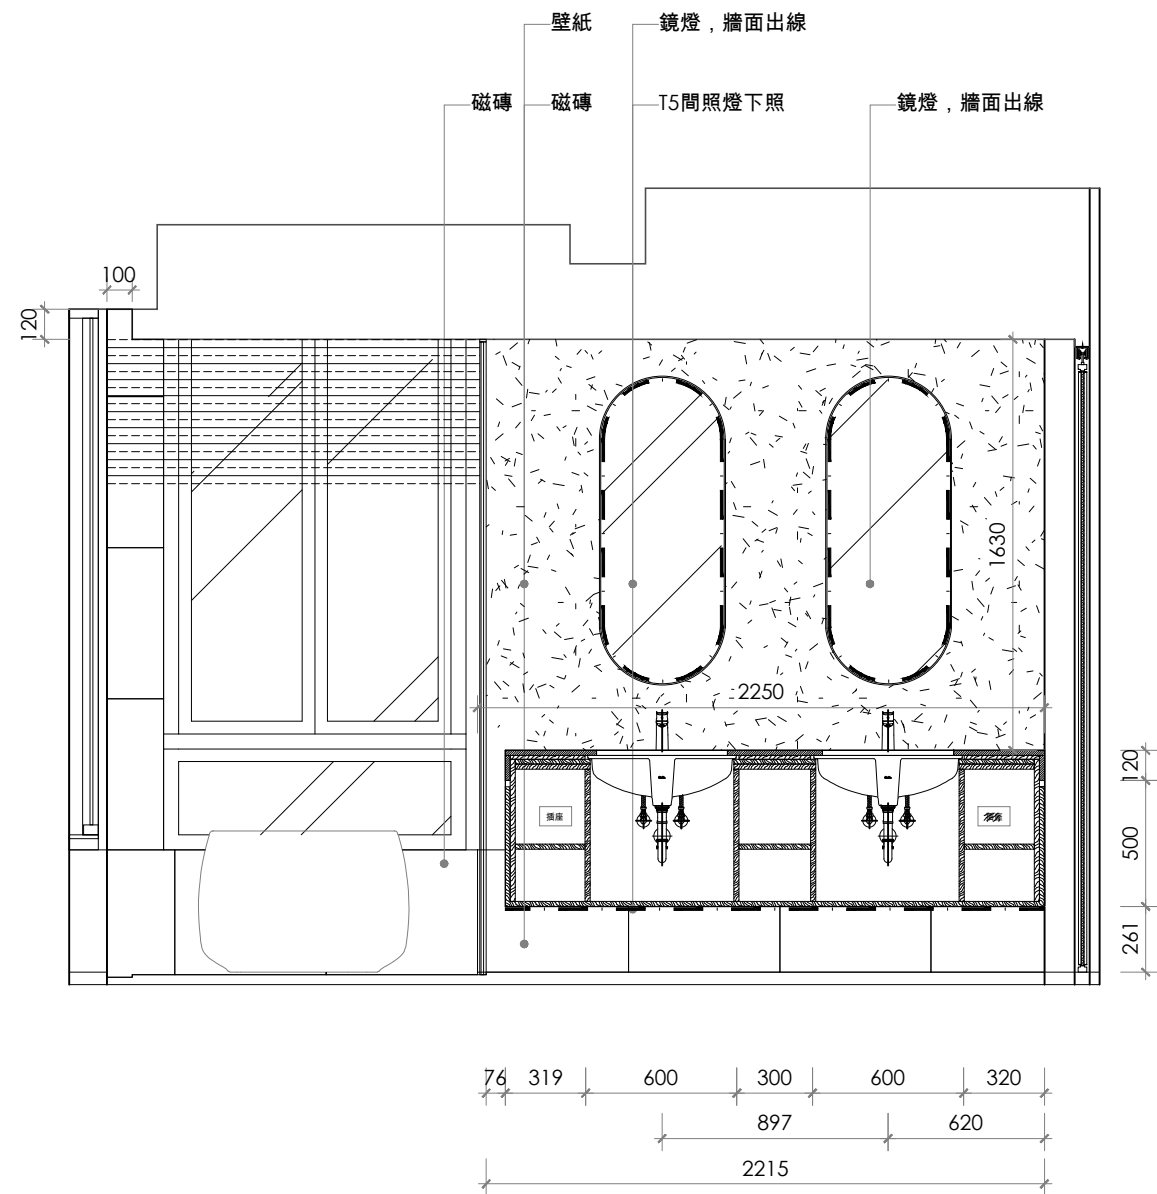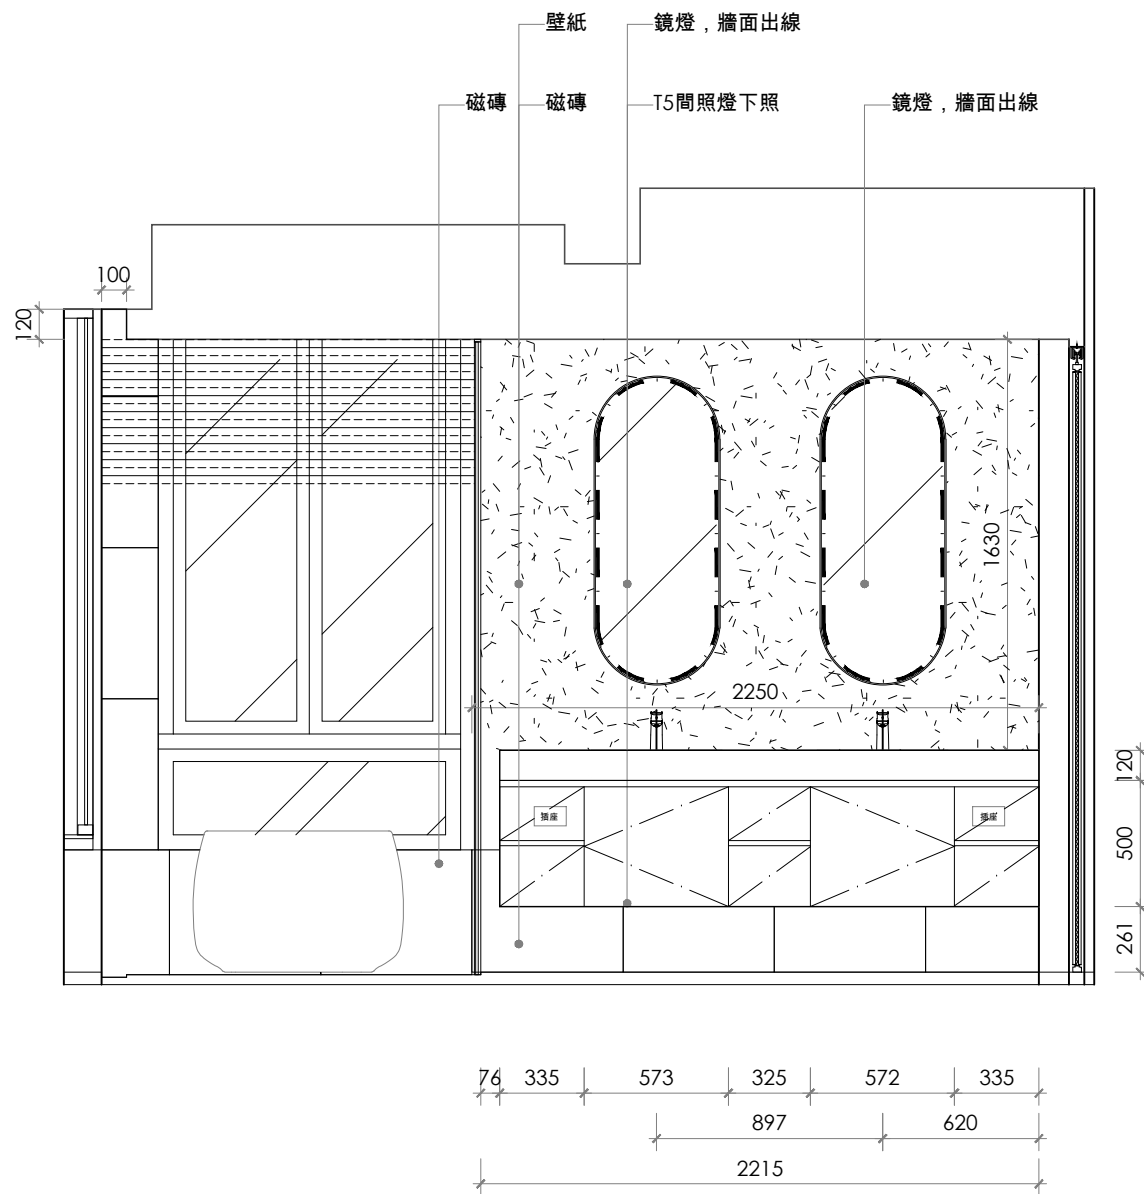

1
E-61

ELEVATION

Scale=1:30

Revision

APPROVAL/核准

設計者:	建築師:
業主:	

備註:

- 圖面標註尺寸僅供參考, 施作均以現場放樣檢討之。
- 圖面標註尺寸、材料及文字敘述因版本不同之差異, 均以出圖章簽認日期之最近為準。
- 電腦圖檔除由合約訂定外, 均不得以何方式外流。
- 圖面所示均為本公司所擁有之智慧財產, 切勿以任何方式複製修改。



MULA DECO

▲ 3F, N.26, Ln.290, Guangfu S. Rd., Taipei.
☎ 886-2-2546-3258
☎ 886-2-2546-3257
✉ Guido@muladeco.com



Project / 案名

林口雲品薇閣姚宅

Sheet Title / 圖名
4F

立面圖


Date / 日期	Scale / 比例
8/10/2026	1/30cm
Designer / 設計	Approval / 核准
MONICA LIN	
Job No / 業務編號	Drawn By / 繪圖
00000	GUIDO
Dwg No.	Page No.
E-61	139

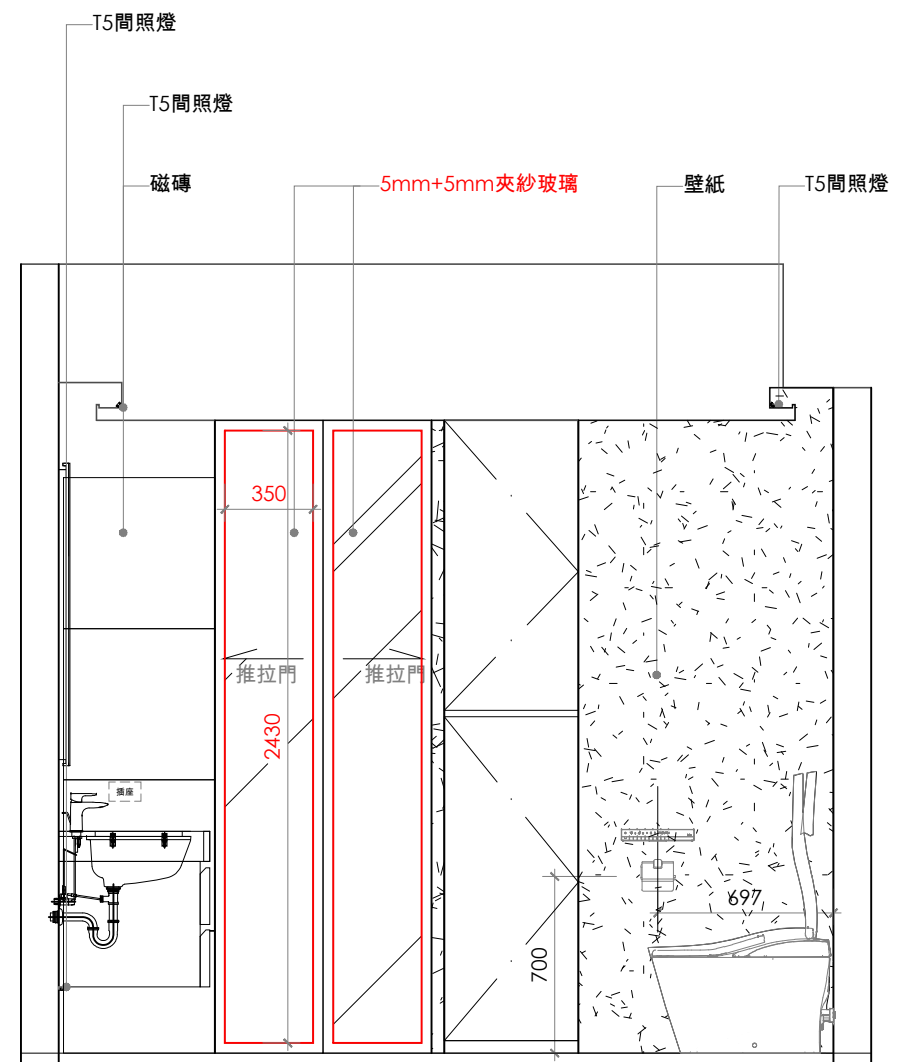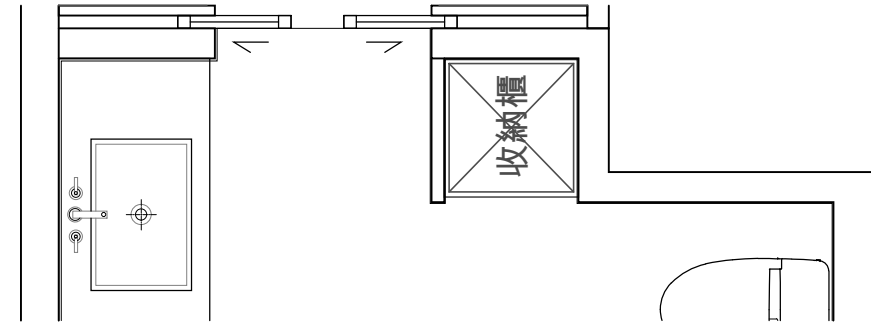

▼FL ±0 mm
▲FL -50 mm



Scale=1:30

Date / 日期	Scale / 比例
8/10/2026	1/30cm
Designer / 設計	Approval / 核准
MONICA LIN	
Job No / 業務編號	Drawn By / 繪圖
00000	GUIDO
Dwg No.	Page No.
E-62	140

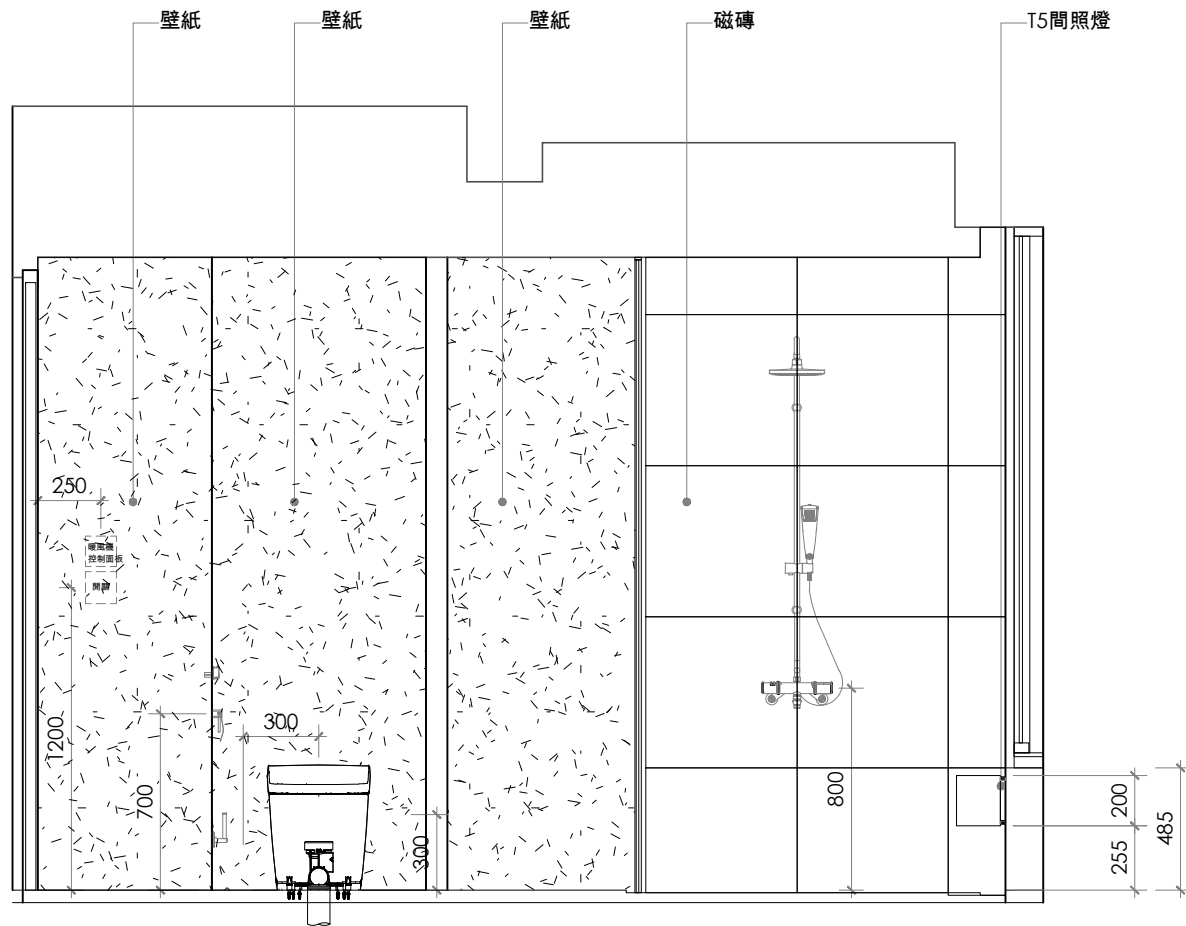

▼FL ±0 mm
▲FL -50 mm

Scale=1:30

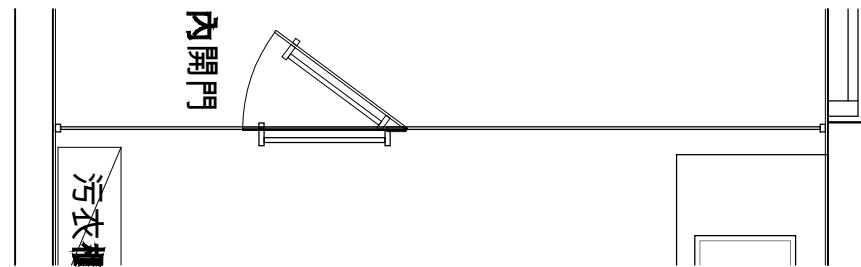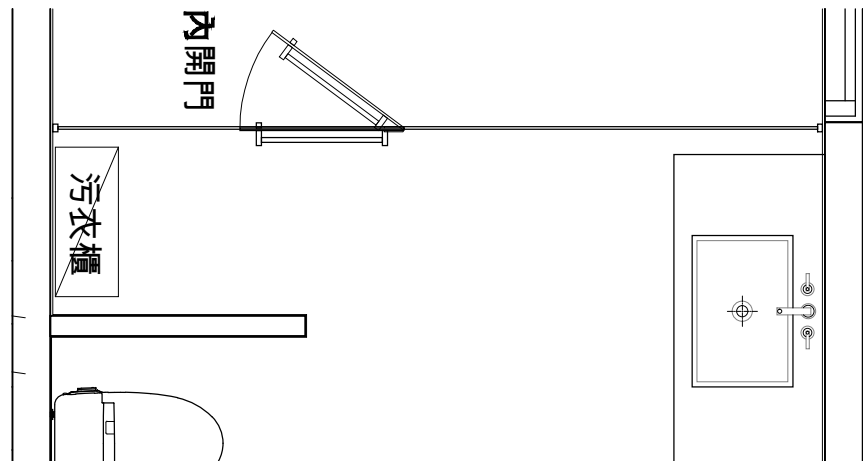

▲CH 3120mm


▲CH 2910mm

▲CH 2510mm

▲CH 2430mm

▼FL ±0 mm

▲FL -50 mm

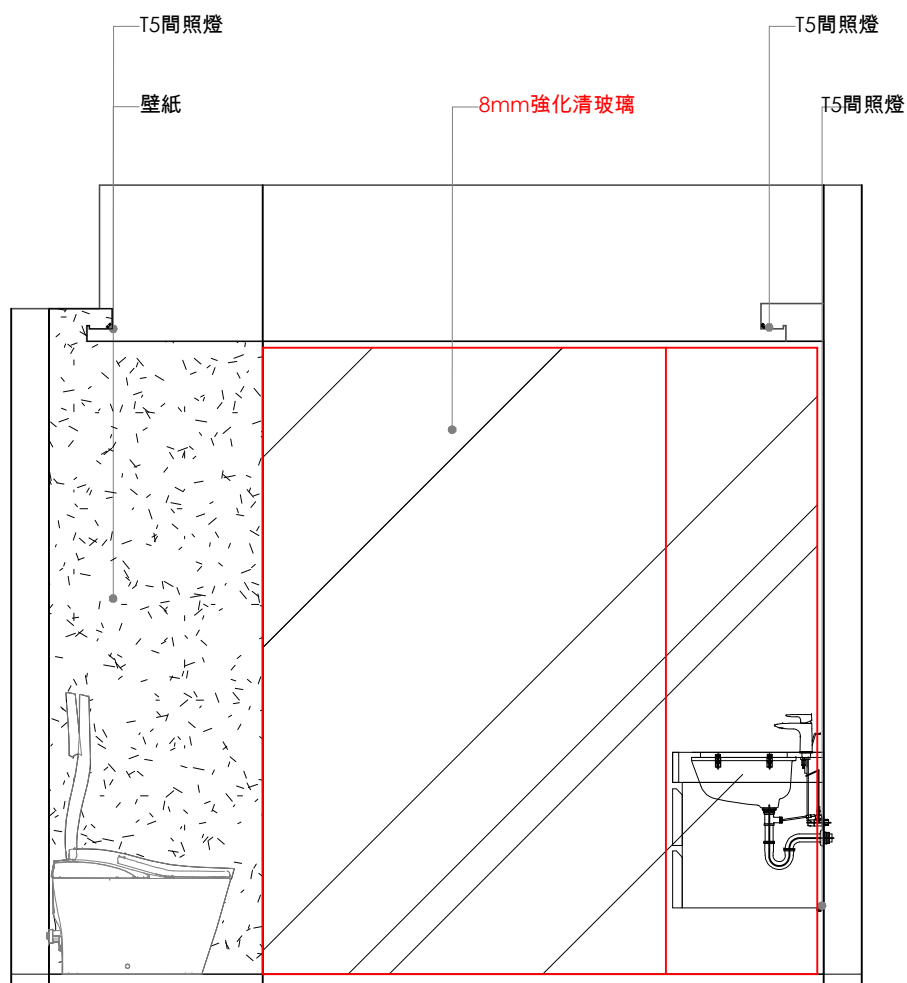

▲CH 3120mm



▲CH 2910mm

▲CH 2510mm

▲CH 2430mm

▼FL ±0 mm

▲FL -50 mm

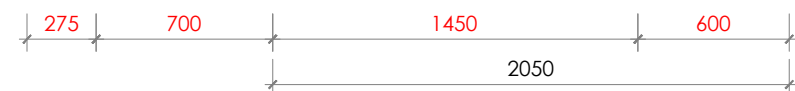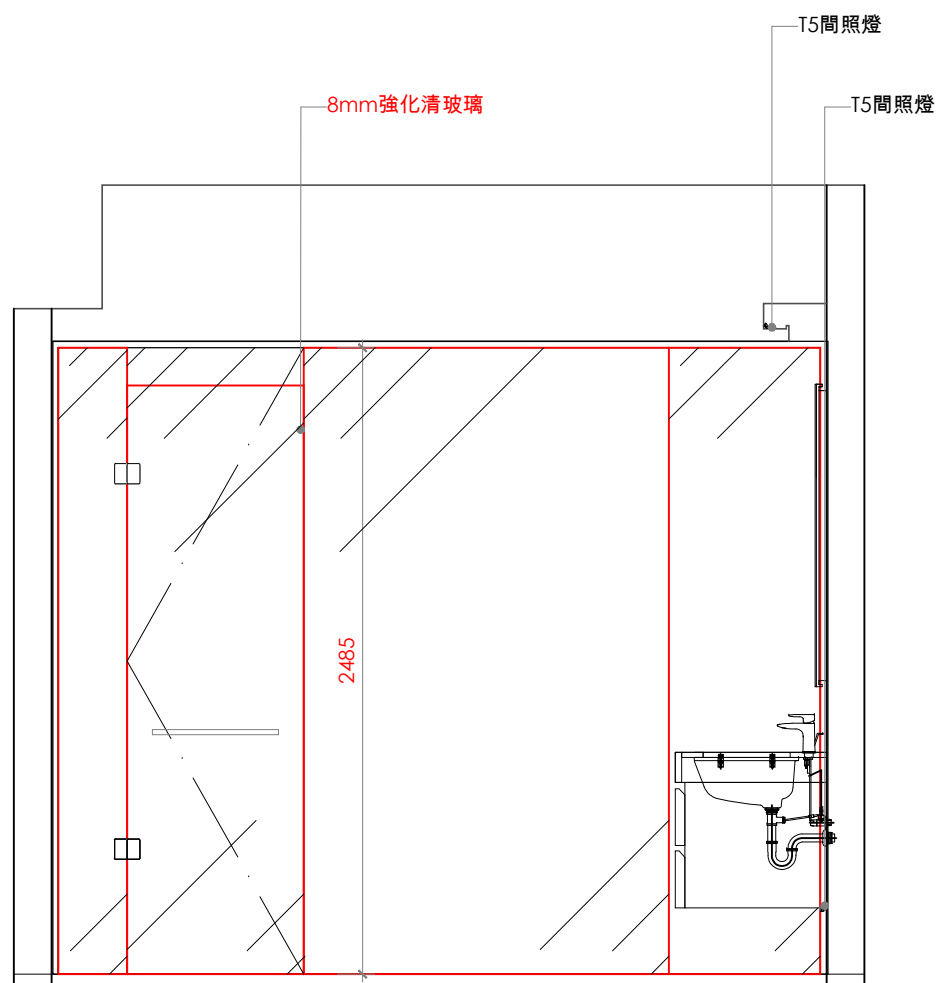

1
E-64

ELEVATION

Scale=1:30

Revision

APPROVAL / 核准

設計者:	建築師:
業主:	

備註:

- 圖面標註尺寸僅供參考，施作均以現場放樣檢討之。
- 圖面標註尺寸、材料及文字敘述因版本不同之差異，均以出圖章簽認日期之最近為準。
- 電腦圖檔除由合約訂定外，均不得以其他方式外流。
- 圖面所示均為本公司所擁有之智慧財產，切勿以任何方式複製修改。



MULA DECO

▲ 3F, N.26, Ln.290, Guangfu S. Rd., Taipei.
☎ 886-2-2546-3258
☎ 886-2-2546-3257
✉ Guido@muladeco.com

Project / 案名

林口雲品薇閣姚宅


Sheet Title / 圖名
4F

立面圖

Date / 日期	Scale / 比例
8/10/2026	1/30cm
Designer / 設計	Approval / 核准
MONICA LIN	
Job No / 業務編號	Drawn By / 繪圖
00000	GUIDO
Dwg No.	Page No.

E-64

142

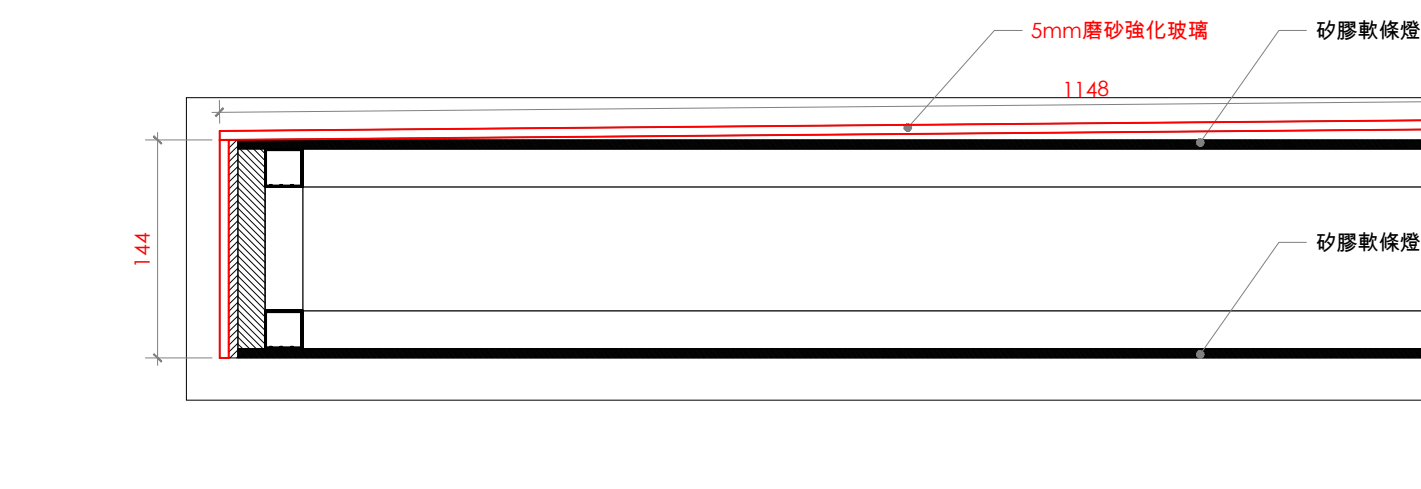


b DETAIL S 1:5


▲CH 3120mm
▲CH 2910mm

▲CH 2510mm
▲CH 2430mm



▼FL ±0 mm
▲FL -50 mm

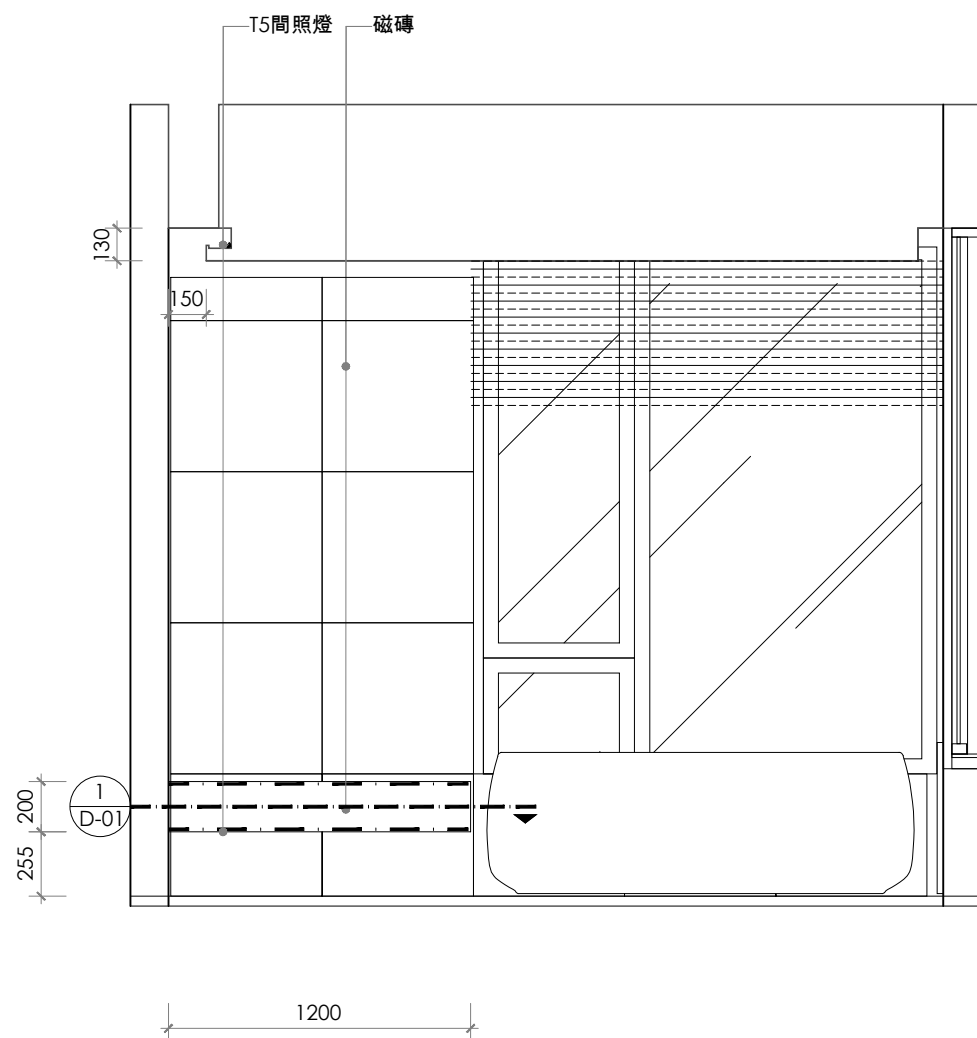

1 ELEVATION Scale=1:30 E-65

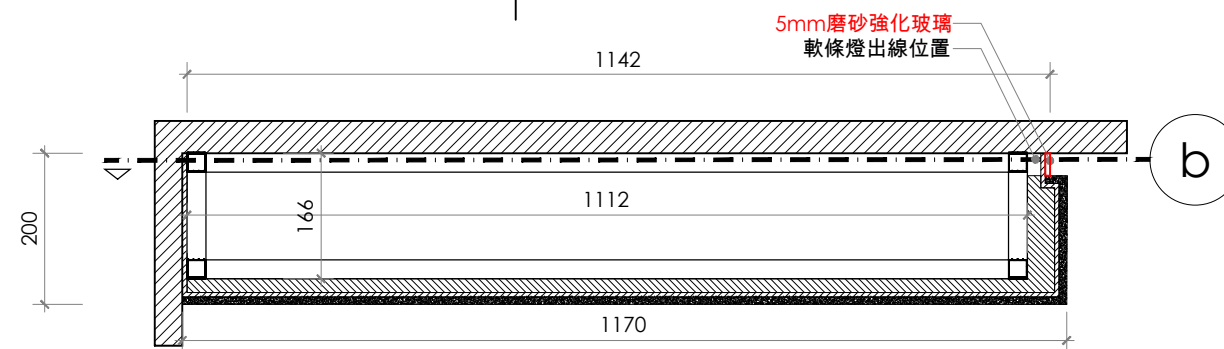

1 DETAIL S 1:10 D-01

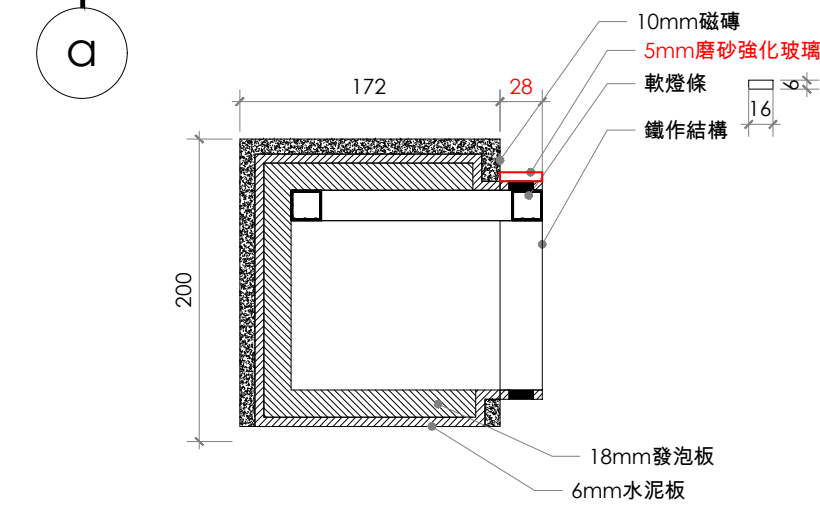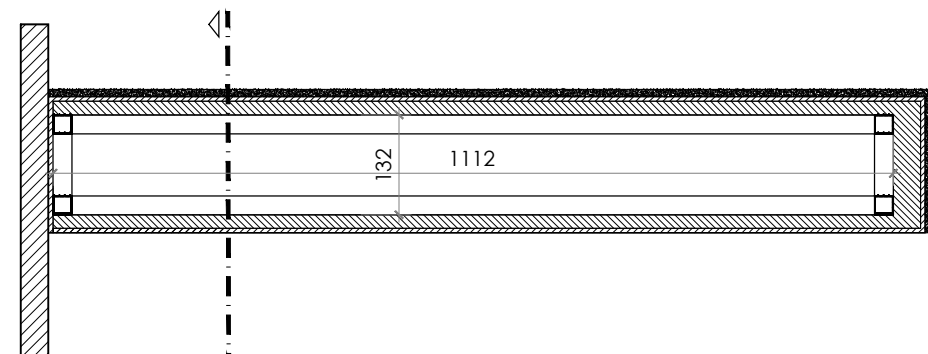

a DETAIL S 1:5

Revision

APPROVAL/核准

設計者:	建築師:
業主:	

備註:

- 圖面標註尺寸僅供參考，施作均以現場放樣檢討之。
- 圖面標註尺寸、材料及文字敘述因版本不同之差異，均以出圖章簽認日期之最近為準。
- 電腦圖檔除由合約訂定外，均不得以任何方式外流。
- 圖面所示均為本公司所擁有之智慧財產，切勿以任何方式複製修改。



MULA DECO

▲ 3F, N.26, Ln.290, Guangfu S. Rd., Taipei.
☎ 886-2-2546-3258
☎ 886-2-2546-3257
✉ Guido@muladeco.com


Project / 案名

林口雲品薇閣姚宅

Sheet Title / 圖名
4F

立面圖

Date / 日期	Scale / 比例
8/10/2026	1/30cm
Designer / 設計	Approval / 核准
MONICA LIN	
Job No / 業務編號	Drawn By / 繪圖
00000	GUIDO
Dwg No.	Page No.
E-65	143

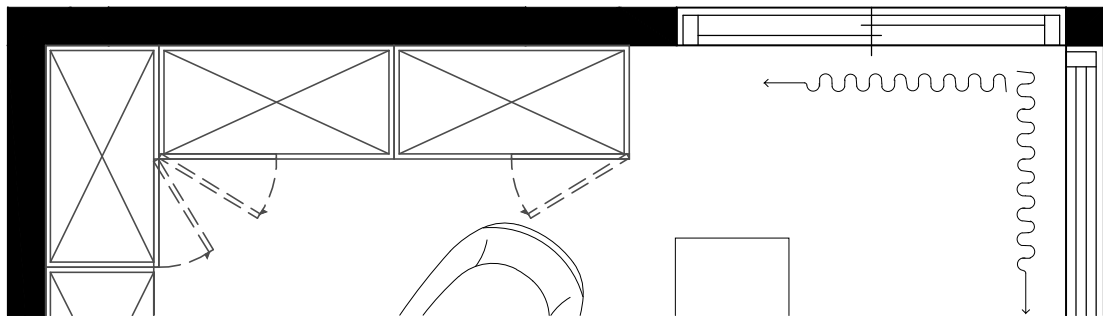



▲CH 2720mm

▲CH 2470mm

▲CH 2320mm

▼FL ±0 mm

▲FL -50 mm

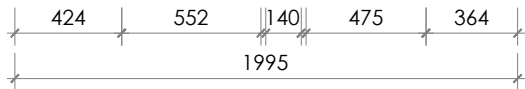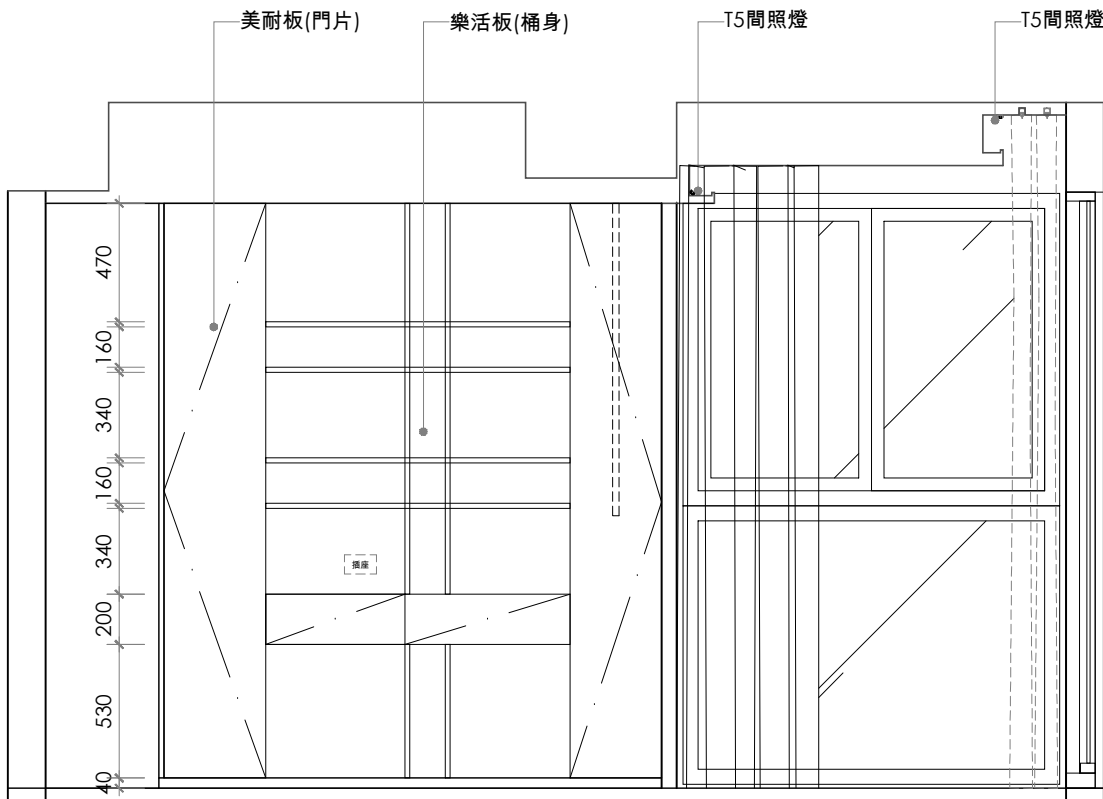

1
E-66

ELEVATION

Scale=1:30

Revision

APPROVAL/核准

設計者:	建築師:
業主:	

備註:

- a. 圖面標註尺寸僅供參考，施作均以現場放樣檢討之。
- b. 圖面標註尺寸、材料及文字敘述因版本不同之差異，均以出圖章簽認日期之最近為準。
- c. 電腦圖檔除由合約訂定外，均不得以任何方式外流。
- d. 圖面所示均為本公司所擁有之智慧財產，切勿以任何方式複製修改。



MULA DECO

▲ 3F, N.26, Ln.290, Guangfu S. Rd., Taipei.
☎ 886-2-2546-3258
☎ 886-2-2546-3257
✉ Guido@muladeco.com

Project / 案名

林口雲品薇閣姚宅


Sheet Title / 圖名
PIF

立面圖

Date / 日期	Scale / 比例
8/10/2026	1/30cm
Designer / 設計	Approval / 核准
MONICA LIN	
Job No / 業務編號	Drawn By / 繪圖
00000	GUIDO
Dwg No.	Page No.

E-66


144

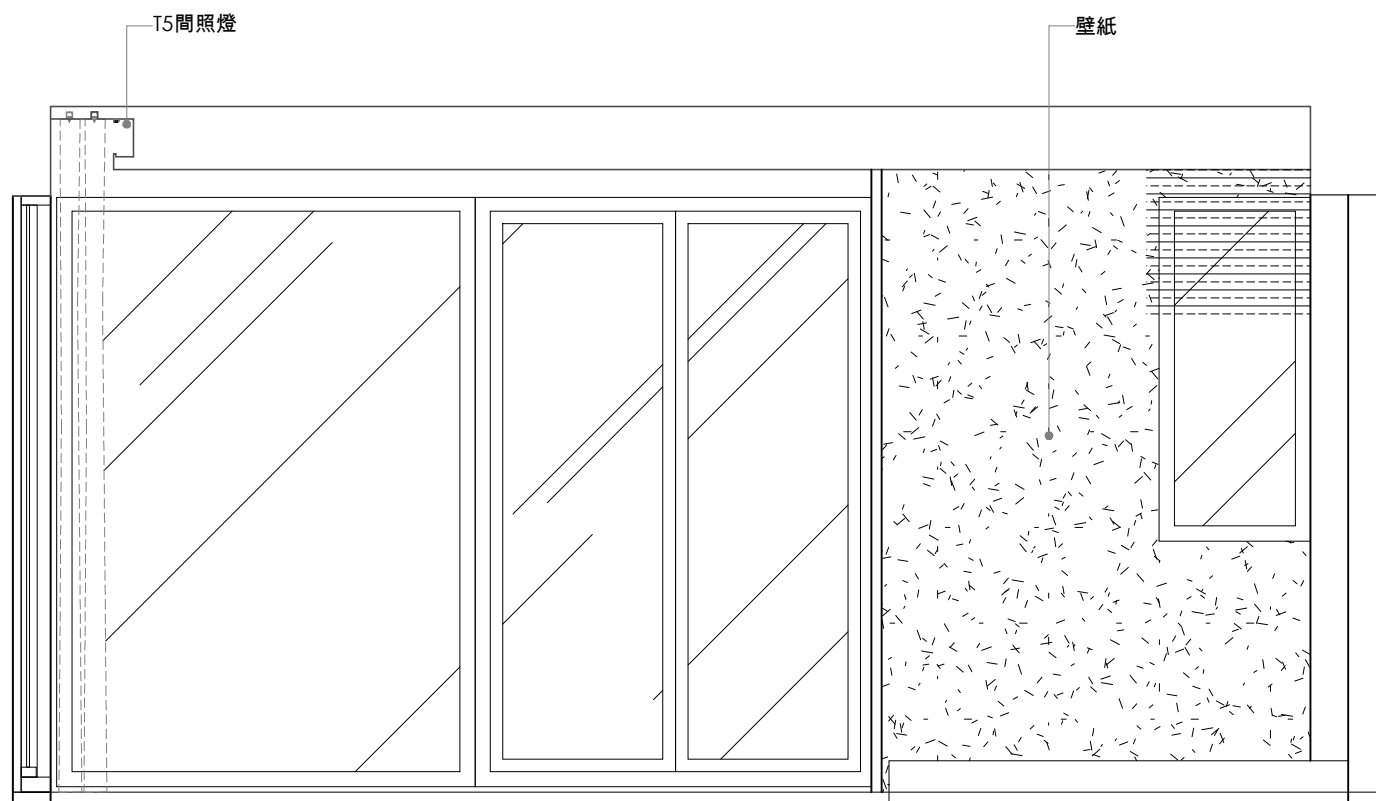

▲FL -50 mm

Scale=1:30

145

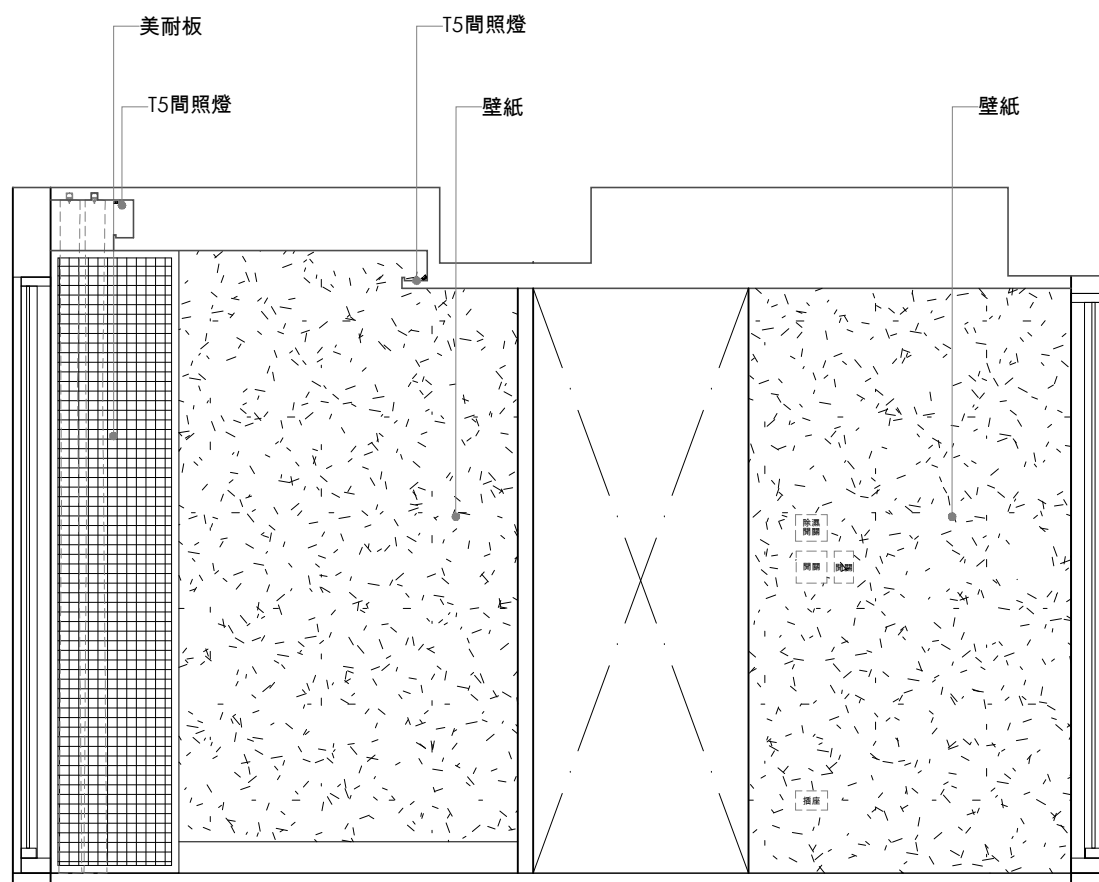


▲FL -50 mm

1
E-68

Scale=1:30

E-68 146

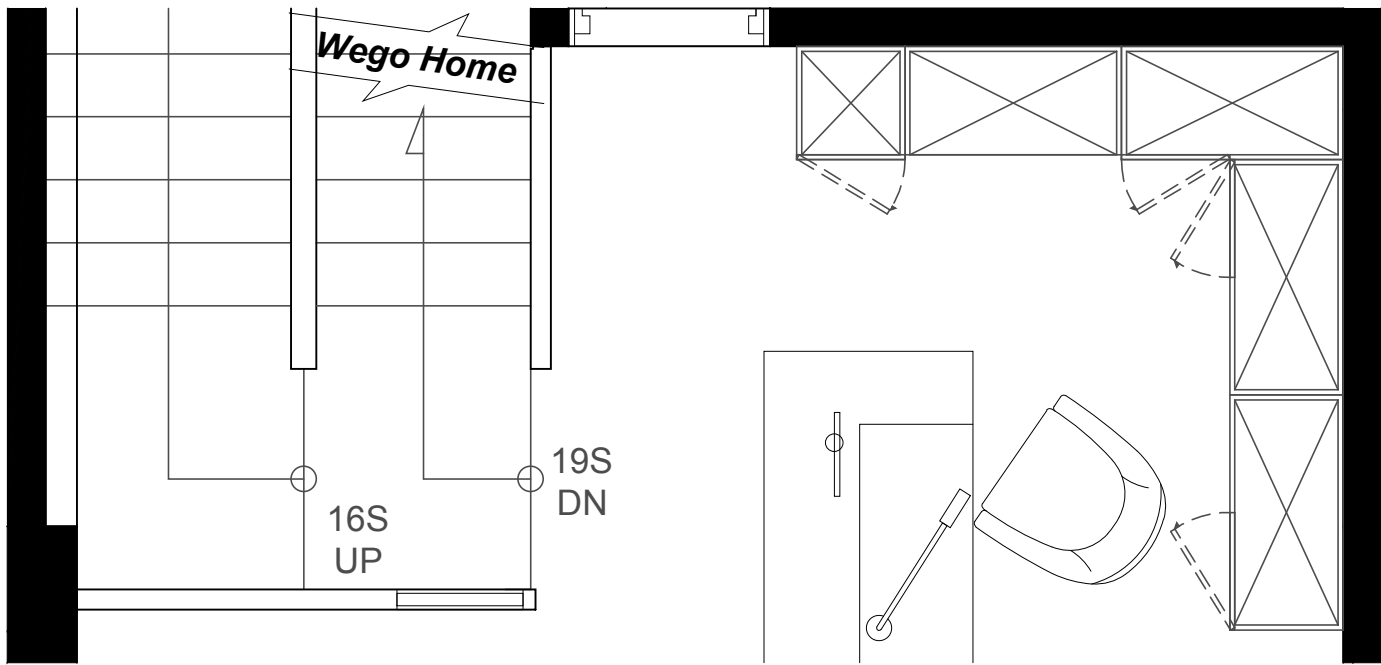




▲CH 2720mm

▲CH 2470mm

▲CH 2320mm

▼FL ±0 mm

▲FL -50 mm

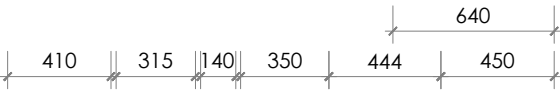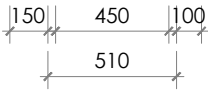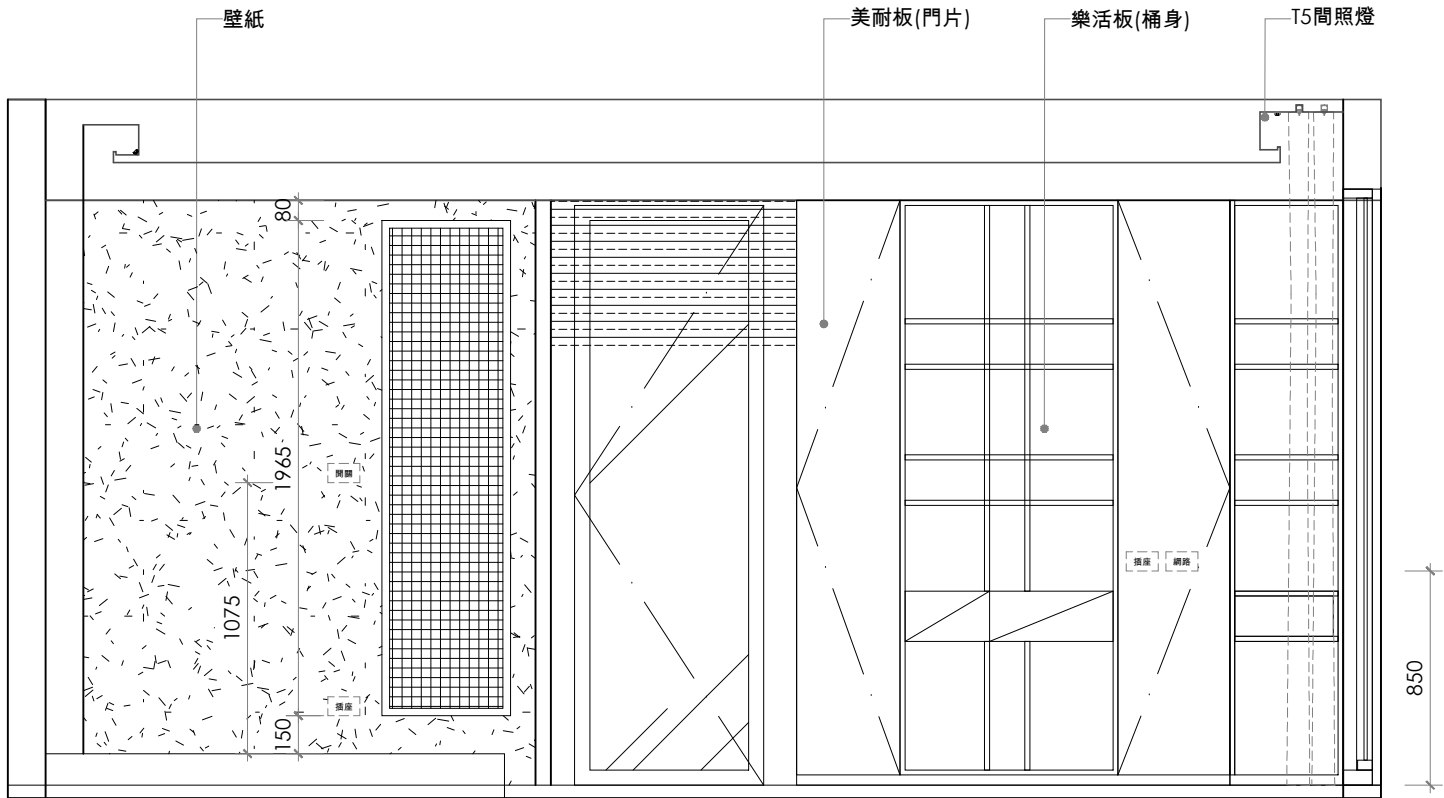

1
E-69

ELEVATION

Scale=1:30

Revision

APPROVAL/核准

設計者:	建築師:
業主:	

備註:

- a. 圖面標註尺寸僅供參考，施作均以現場放樣檢討之。
- b. 圖面標註尺寸、材料及文字敘述因版本不同之差異，均以出圖章簽認日期之最近為準。
- c. 電腦圖檔除由合約訂定外，均不得以任何方式外流。
- d. 圖面所示均為本公司所擁有之智慧財產，切勿以任何方式複製修改。



MULA DECO

▲ 3F, N.26, Ln.290, Guangfu S. Rd., Taipei.
☎ 886-2-2546-3258
☎ 886-2-2546-3257
✉ Guido@muladeco.com


Project / 案名

林口雲品薇閣姚宅

Sheet Title / 圖名
P1F

立面圖

Date / 日期	Scale / 比例
8/10/2026	1/30cm
Designer / 設計	Approval / 核准
MONICA LIN	
Job No / 業務編號	Drawn By / 繪圖
00000	GUIDO
Dwg No.	Page No.

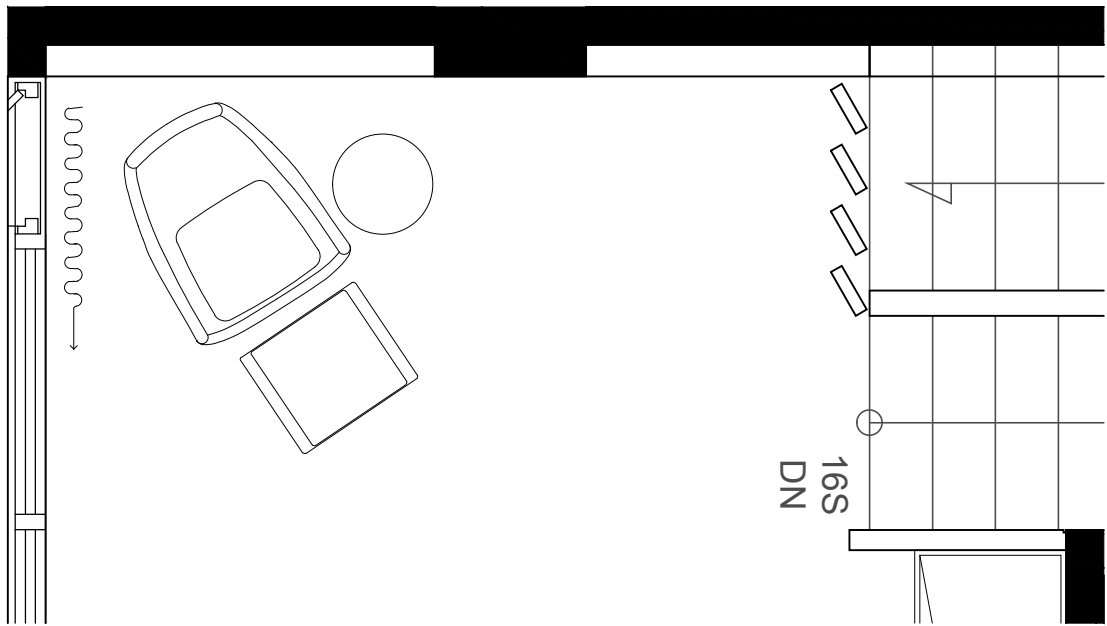


▲CH 2720mm

▲CH 2470mm

▲CH 2320mm

▼FL ±0 mm

▲FL -50 mm

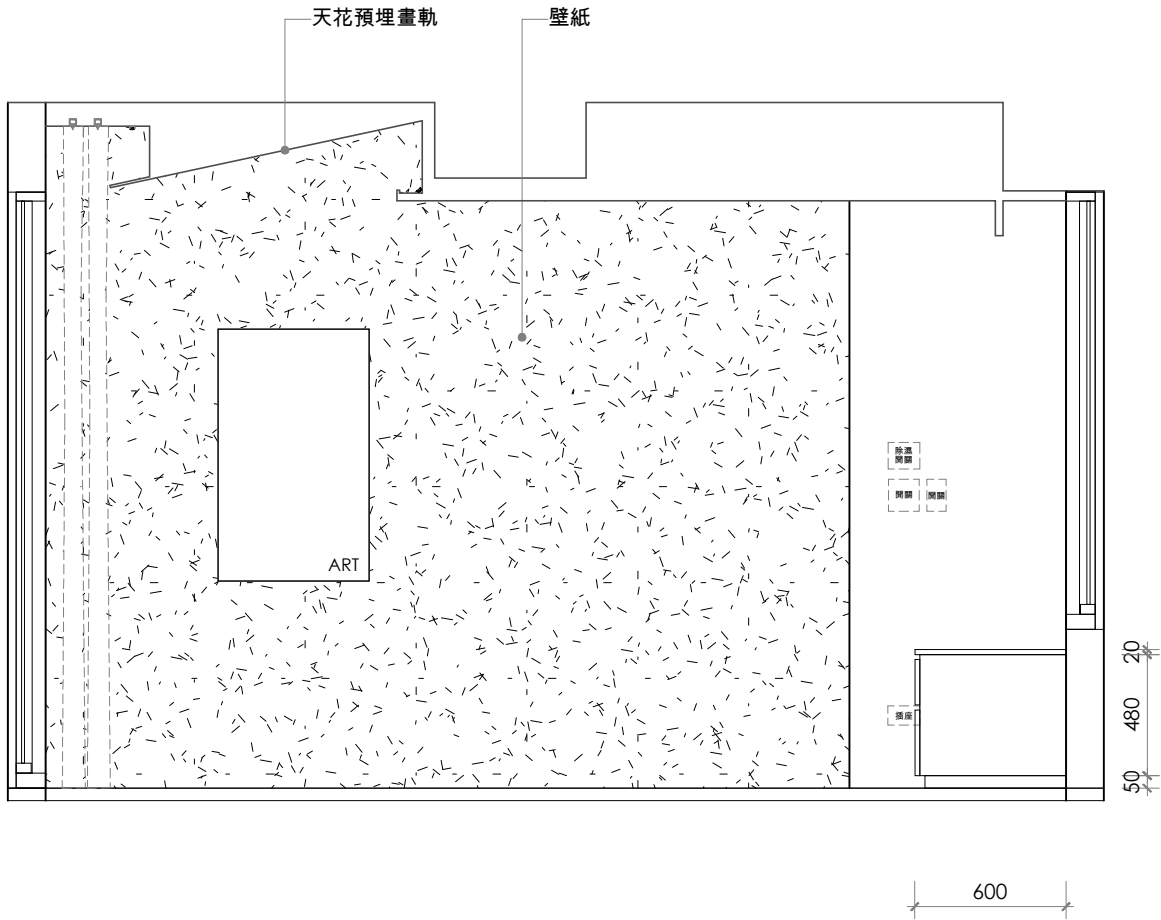

1
E-71

ELEVATION

Scale=1:30

Revision

APPROVAL/核准

設計者:	建築師:
業主:	

備註:

- 圖面標註尺寸僅供參考，施作均以現場放樣檢討之。
- 圖面標註尺寸、材料及文字敘述因版本不同之差異，均以出圖章簽認日期之最近為準。
- 電腦圖檔除由合約訂定外，均不得以任何方式外流。
- 圖面所示均為本公司所擁有之智慧財產，切勿以任何方式複製修改。



MULA DECO

▲ 3F, N.26, Ln.290, Guangfu S. Rd., Taipei.
☎ 886-2-2546-3258
☎ 886-2-2546-3257
✉ Guido@muladeco.com

Project / 案名

林口雲品薇閣姚宅


Sheet Title / 圖名
RF

立面圖

Date / 日期	Scale / 比例
8/10/2026	1/30cm
Designer / 設計	Approval / 核准
MONICA LIN	
Job No / 業務編號	Drawn By / 繪圖
00000	GUIDO
Dwg No.	Page No.

E-71

149

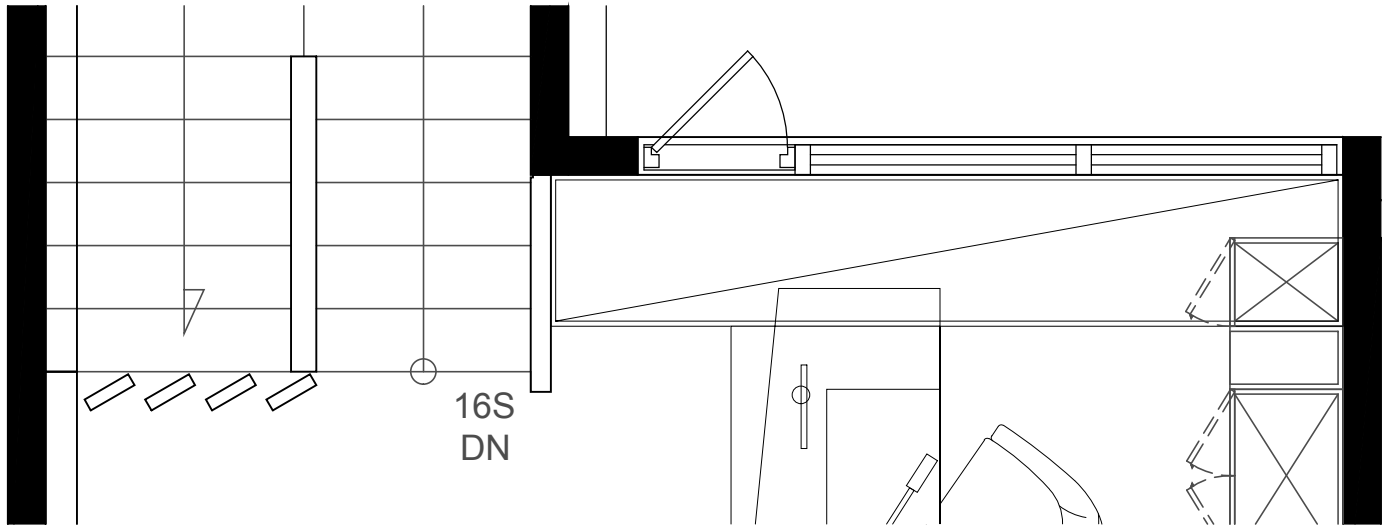



▲CH 2720mm

▲CH 2470mm

▲CH 2320mm

▼FL ±0 mm

▲FL -50 mm

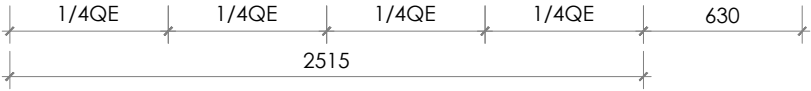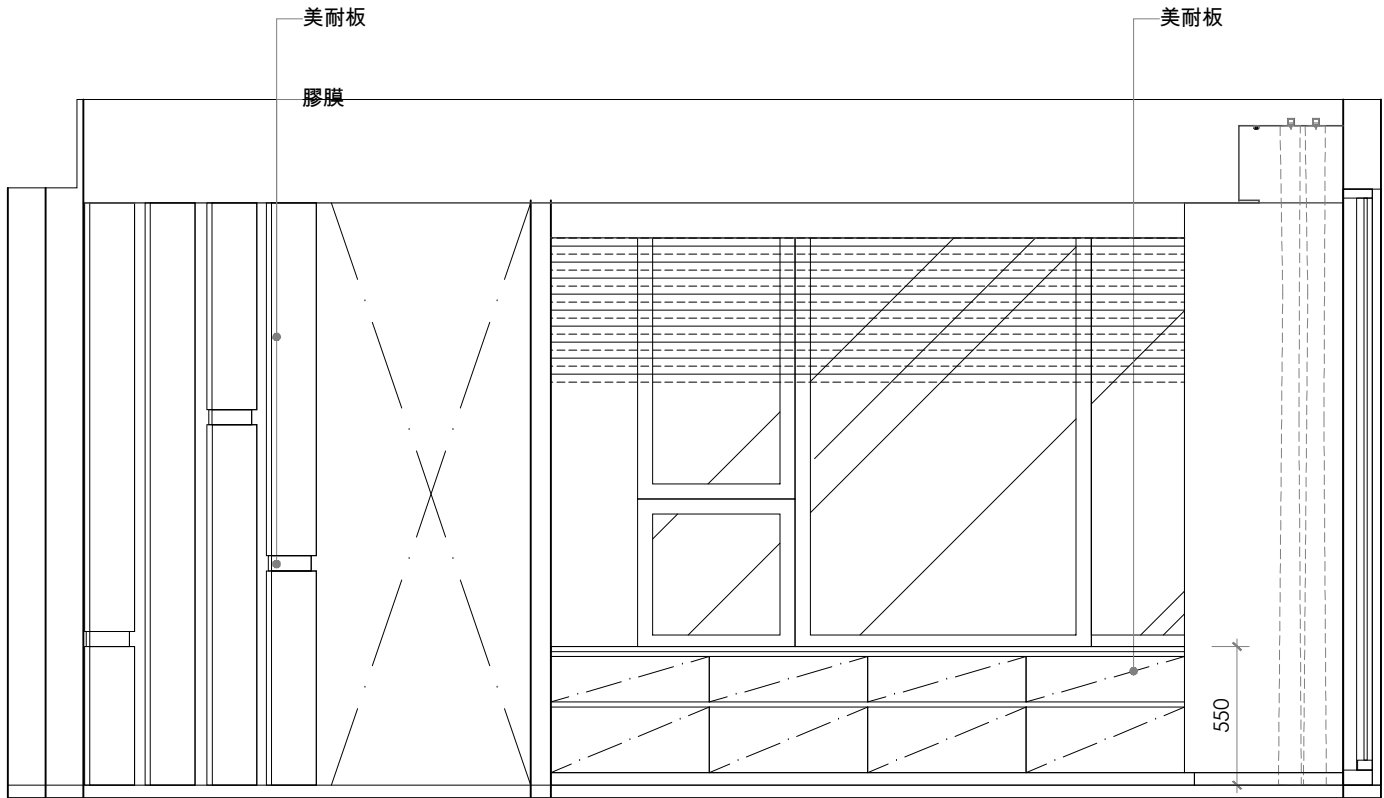

1
E-72

ELEVATION

Scale=1:30

Revision

APPROVAL/核准

設計者:	建築師:
業主:	

備註:

- a. 圖面標註尺寸僅供參考，施作均以現場放樣檢討之。
- b. 圖面標註尺寸、材料及文字敘述因版本不同之差異，均以出圖章簽認日期之最近為準。
- c. 電腦圖檔除由合約訂定外，均不得以任何方式外流。
- d. 圖面所示均為本公司所擁有之智慧財產，切勿以任何方式複製修改。



MULA DECO

▲ 3F, N.26, Ln.290, Guangfu S. Rd., Taipei.
☎ 886-2-2546-3258
☎ 886-2-2546-3257
✉ Guido@muladeco.com

Project / 案名

林口雲品薇閣姚宅

Sheet Title / 圖名






RF

立面圖



Date / 日期	Scale / 比例
8/10/2026	1/30cm
Designer / 設計	Approval / 核准
MONICA LIN	
Job No / 業務編號	Drawn By / 繪圖
00000	GUIDO
Dwg No.	Page No.

E-72

150

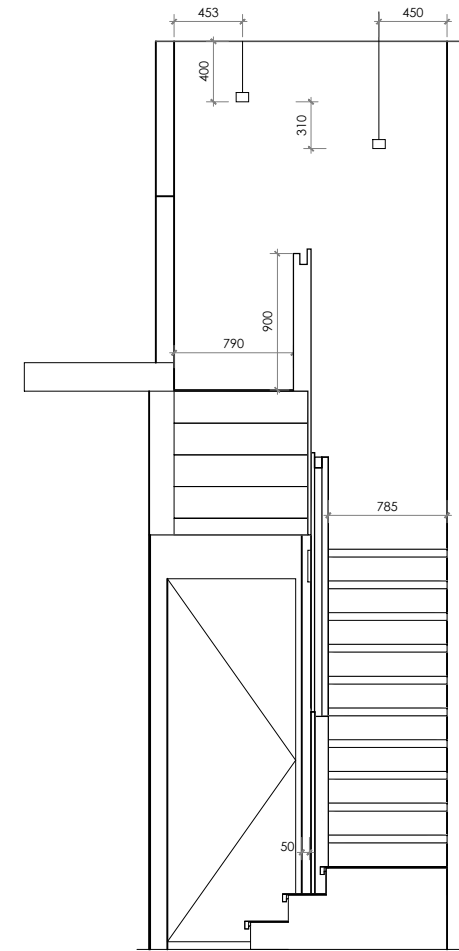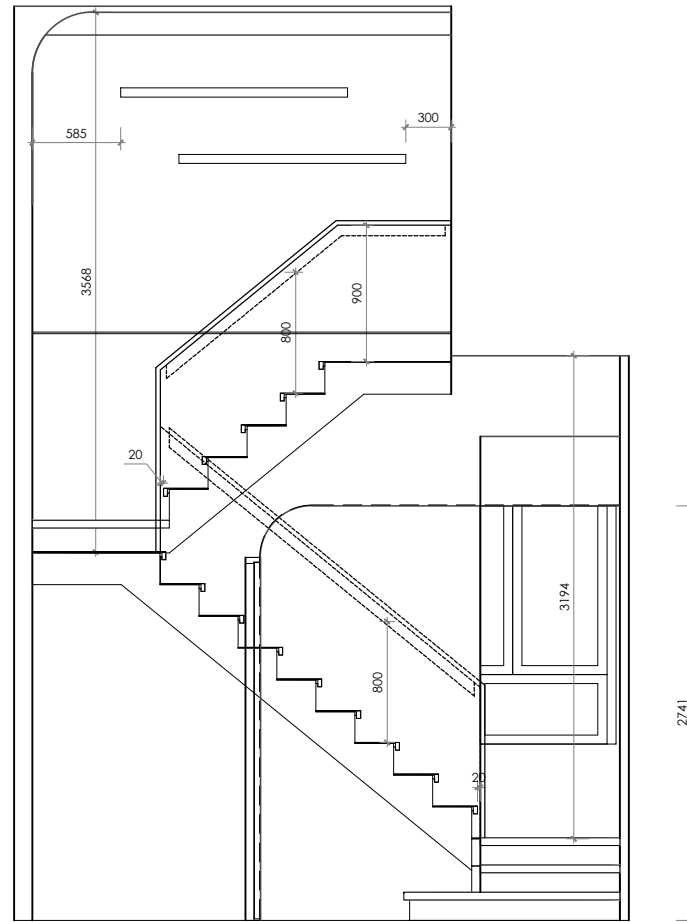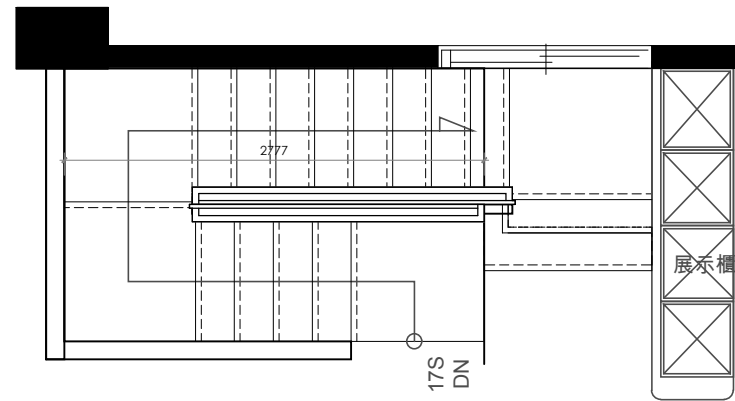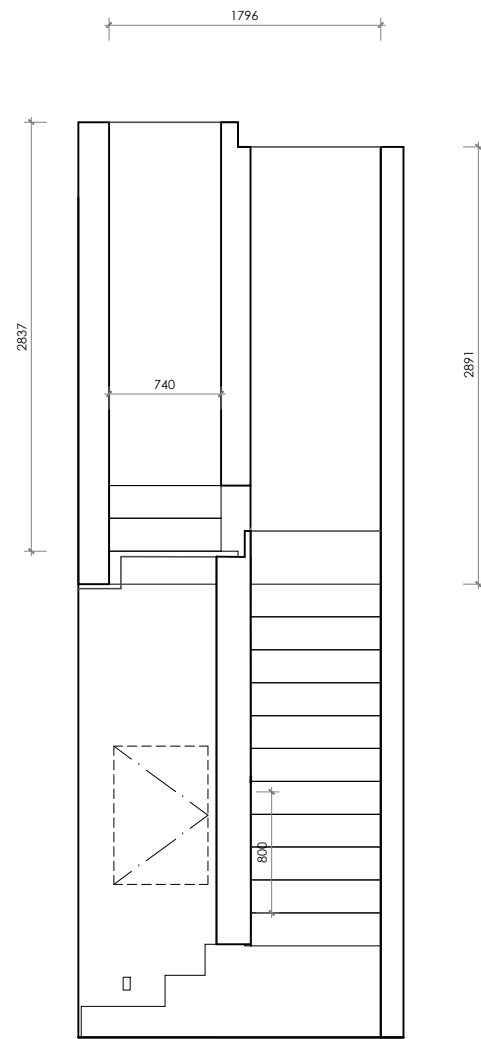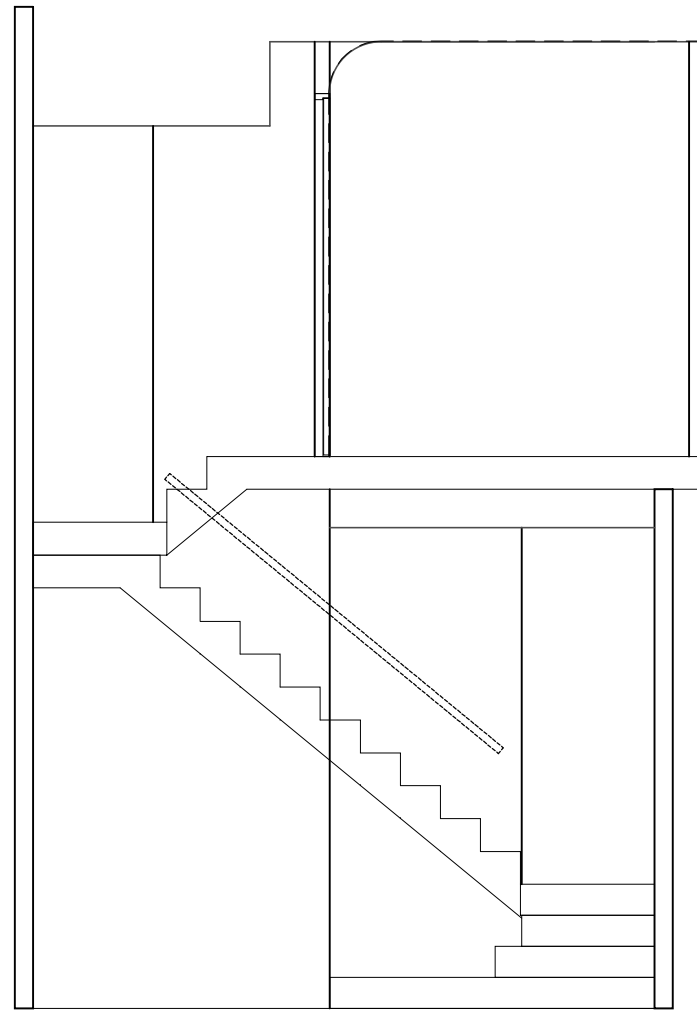

151

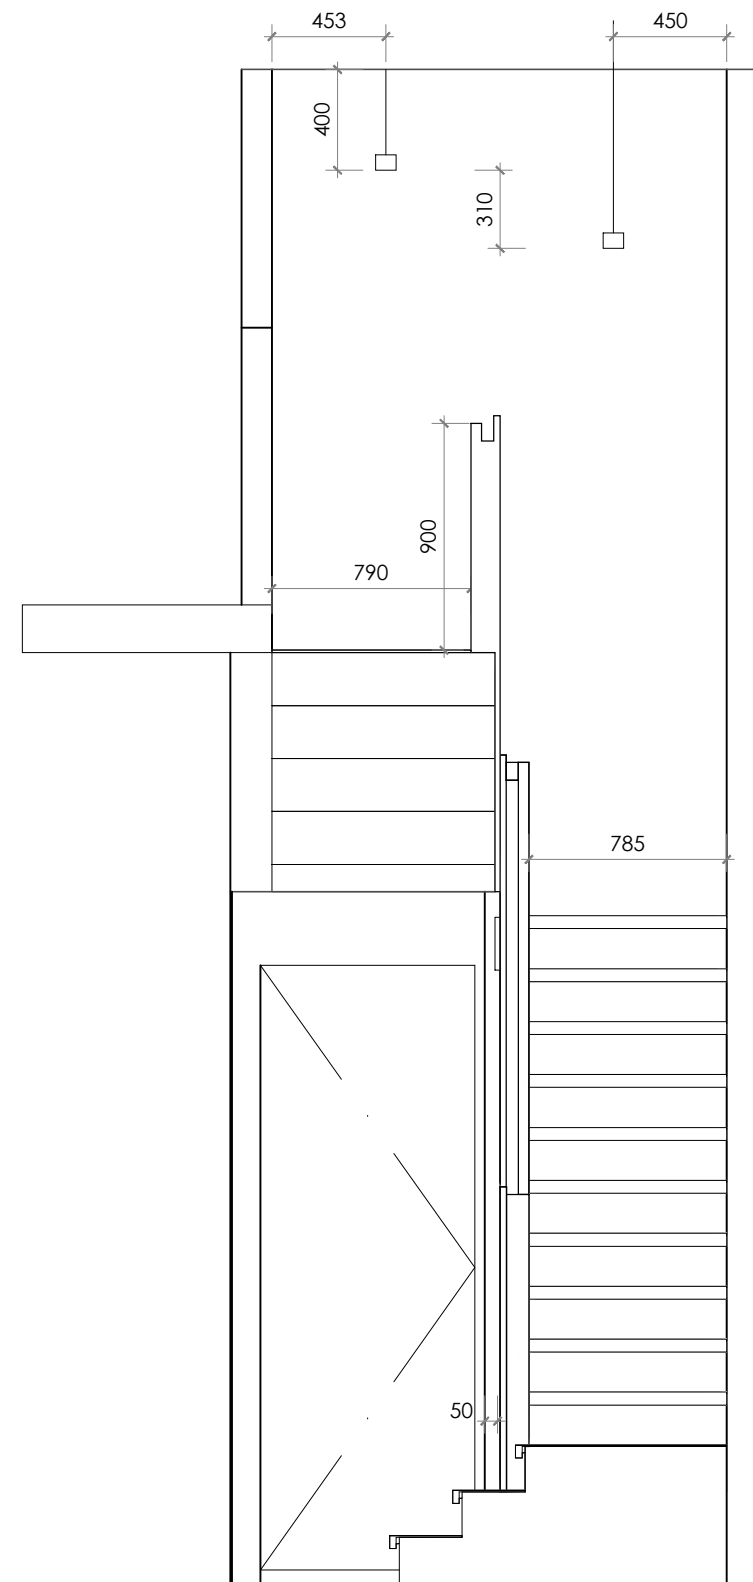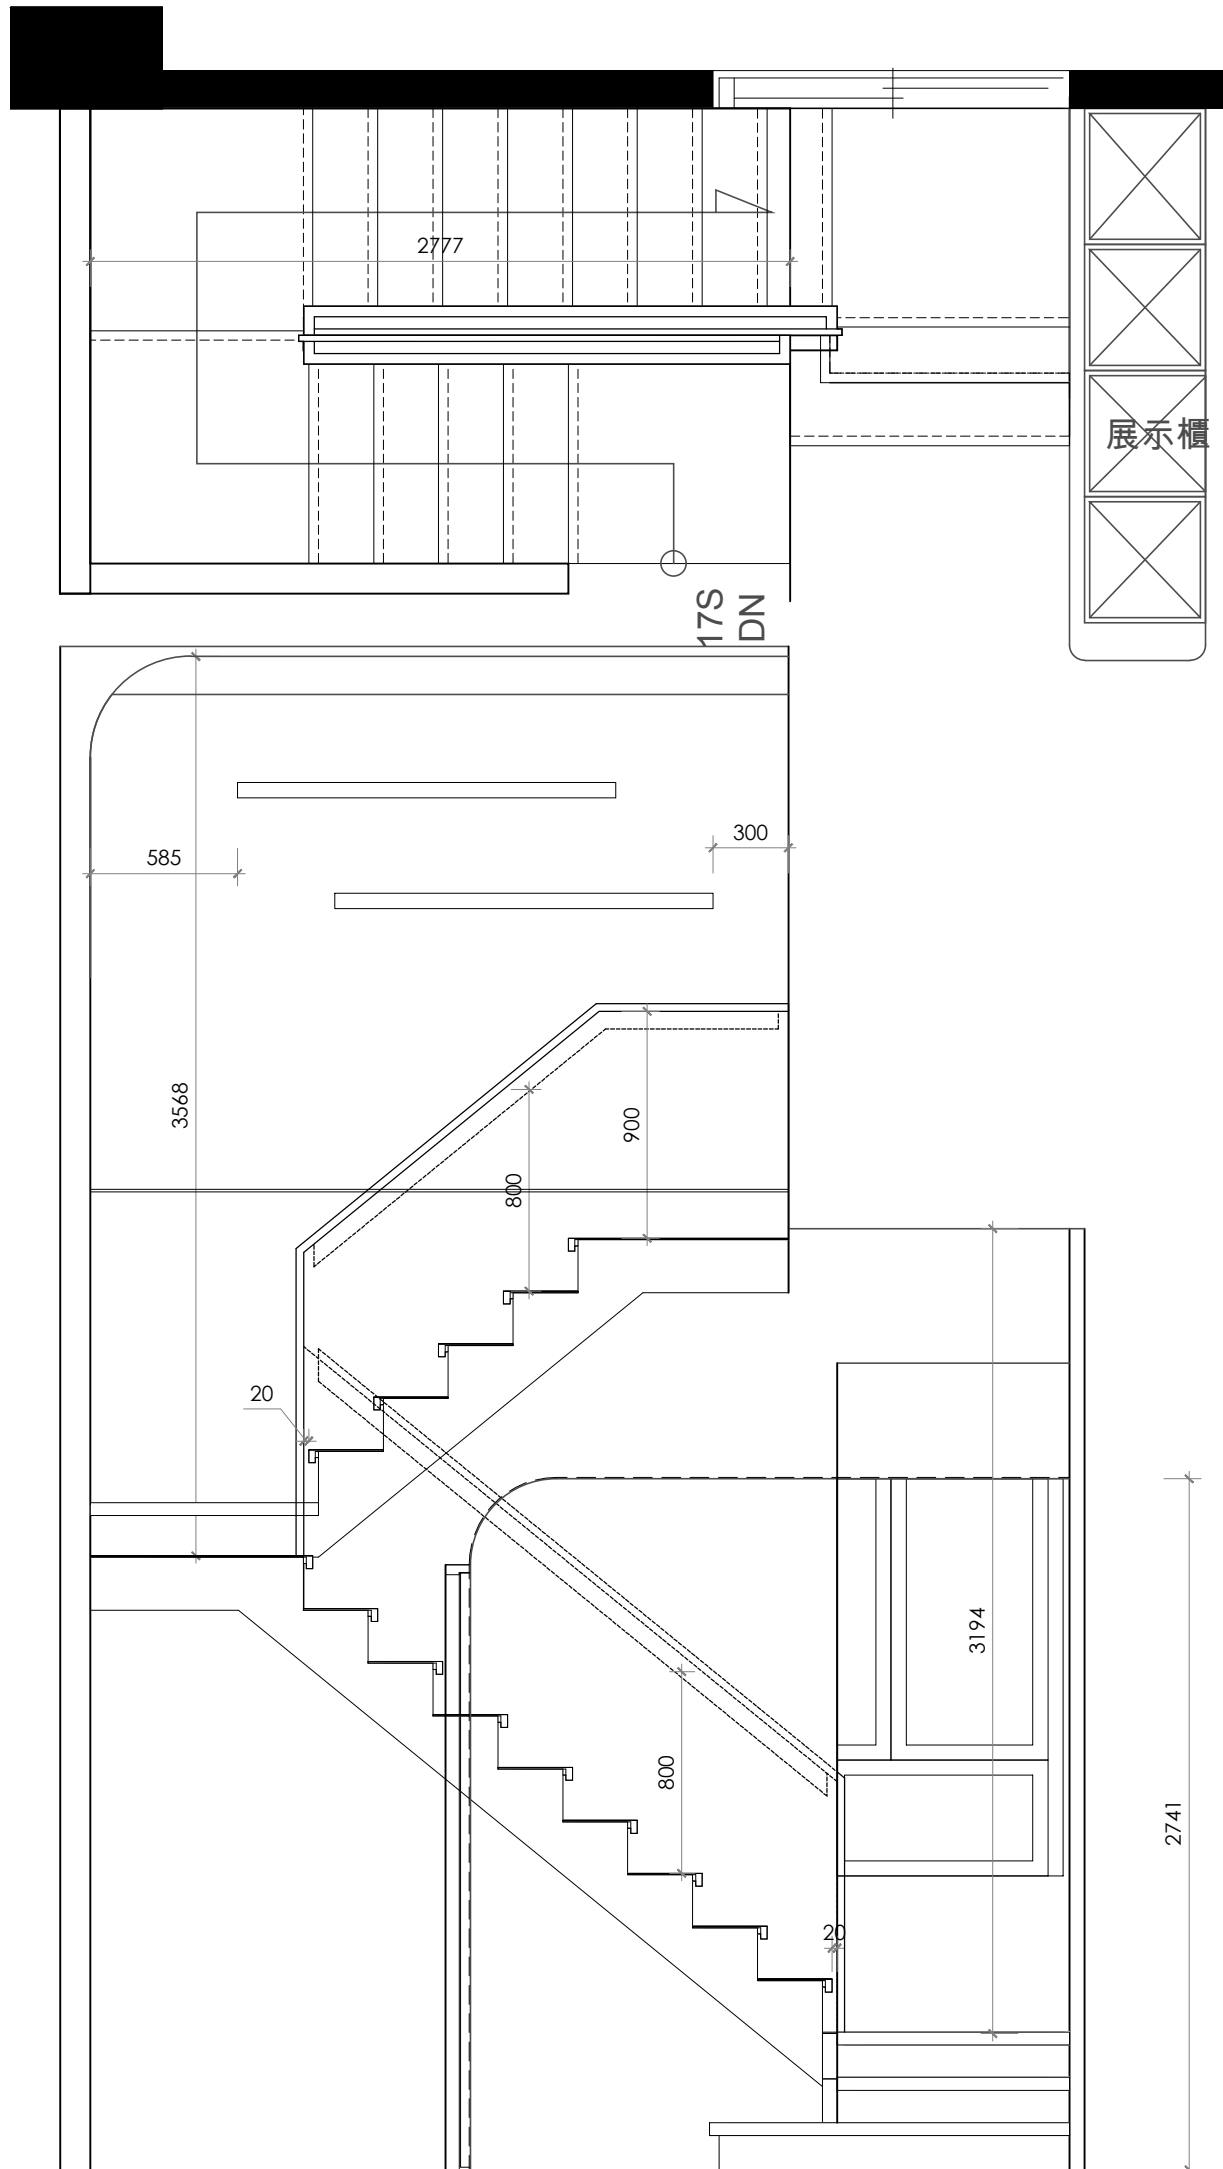

Revision

APPROVAL/核准

設計者:	建築師:
業主:	

請註:

- 圖面標註尺寸僅供參考，施作均以現場放樣檢討之。
- 圖面標註尺寸、材料及文字敘述因版本不同之差異，均以圖章簽註日期之最近為準。
- 電腦圖檔除由合約訂定外，均不得以任何方式外流。
- 圖面所示均為本公司所擁有之智慧財產，切勿以任何方式複製修改。



MULA DECO

A 3F, N.26, Ln.290, Guangfu S. Rd., Taipei.
T 886-2-2546-3258
F 886-2-2546-3257
E Guido@muladeco.com

Project / 案名

林口雲品薇閣姚宅

Sheet Title / 圖名


F-2F

立面圖

Date / 日期	Scale / 比例
8/10/2026	1/50cm
Designer / 設計	Approval / 核准
MONICA LIN	
Job No / 業務編號	Drawn By / 繪圖
00000	GUIDO

E-74

152

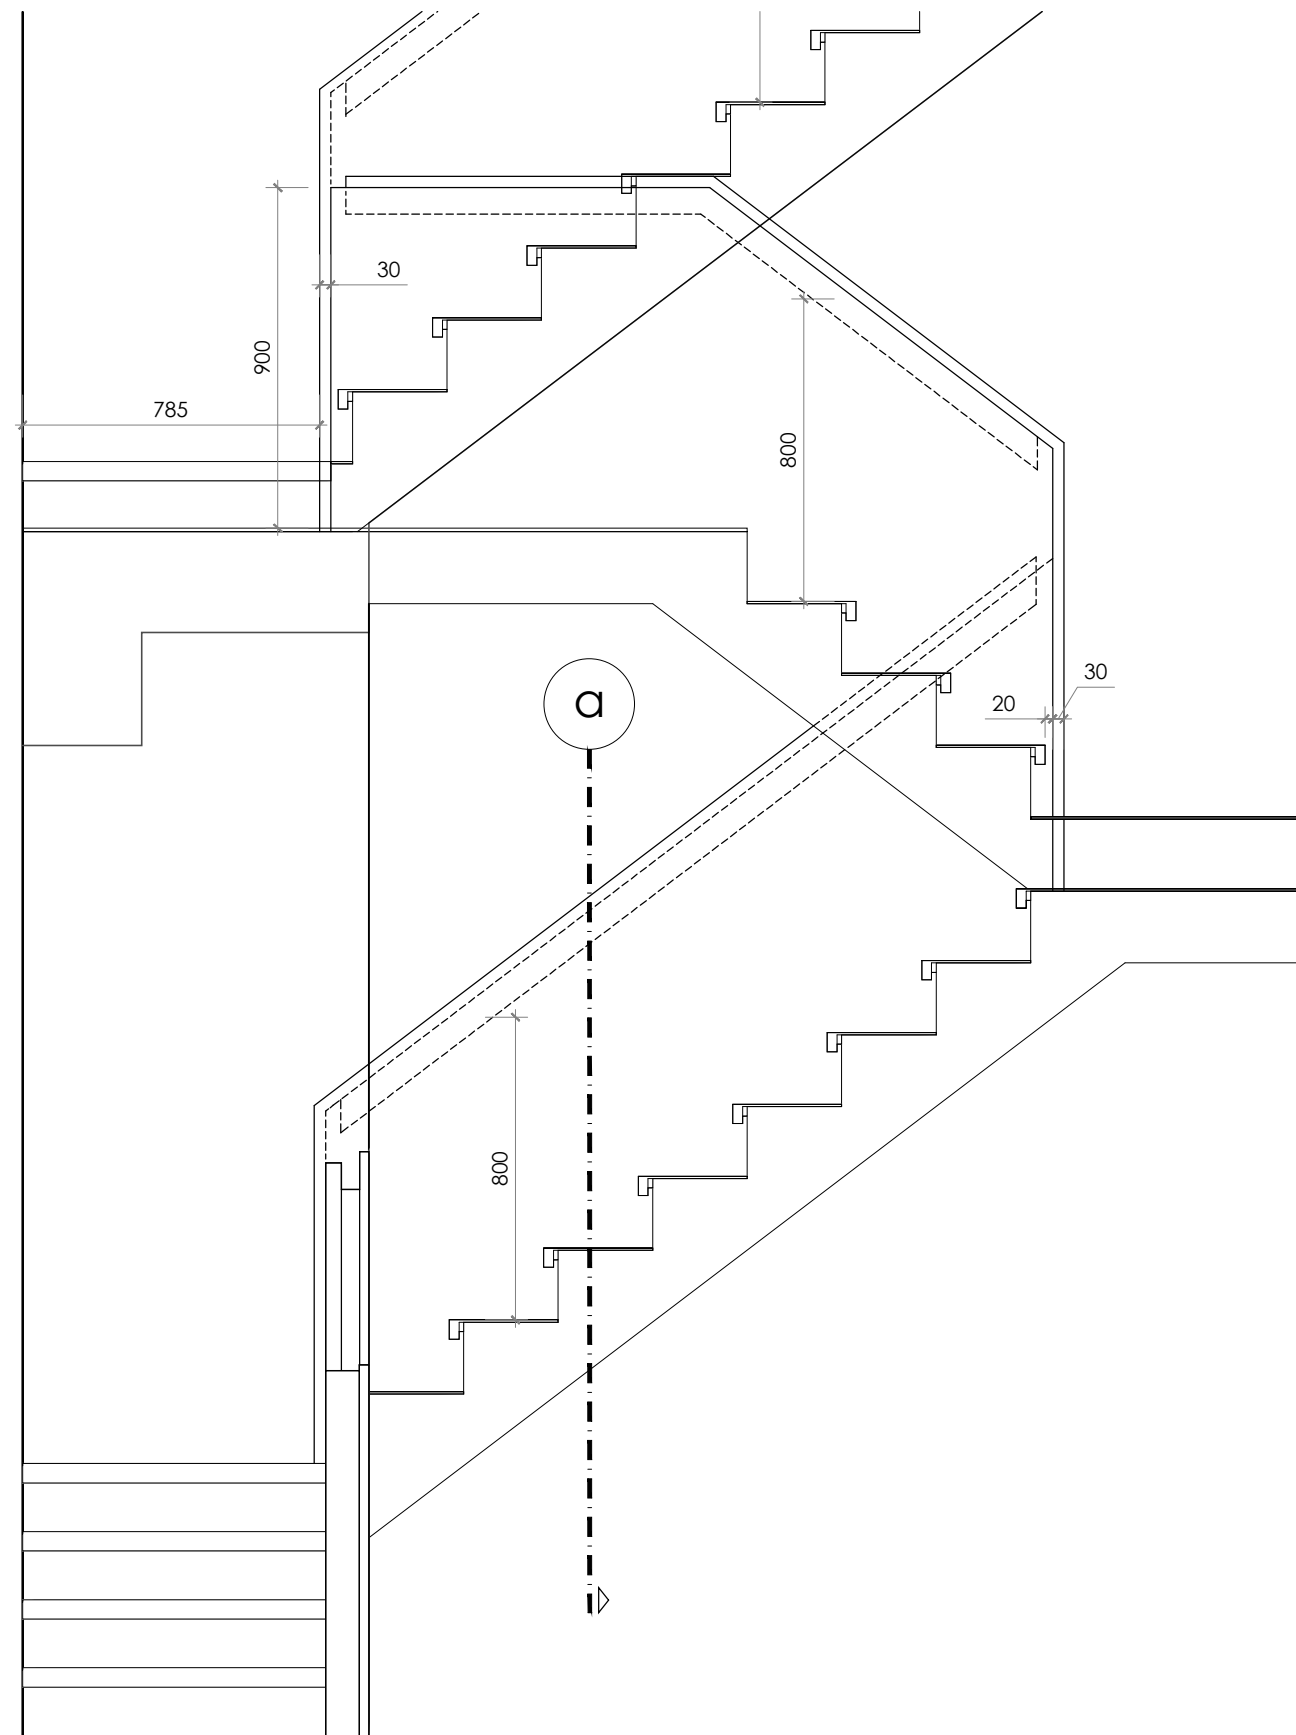

備註:

- 圖面標註尺寸僅供參考，施作均以現場放樣檢討之。
- 圖面標註尺寸、材料及文字敘述因版本不同之差異，均以出圖章簽認日期之最近為準。
- 電腦圖檔除由合約訂定外，均不得以何方式外洩。
- 圖面所示均為本公司所擁有之智慧財產，切勿以任何方式複製修改。




Project / 案名

林口雲品薇閣姚宅

Sheet Title / 圖名
2F-3F

立面圖

Date / 日期	Scale / 比例
8/10/2026	1/50cm
Designer / 設計	Approval / 核准
MONICA LIN	
Job No. / 業務編號	Drawn By / 繪圖
00000	GUIDO
Dwg No.	Page No.
E-75	153

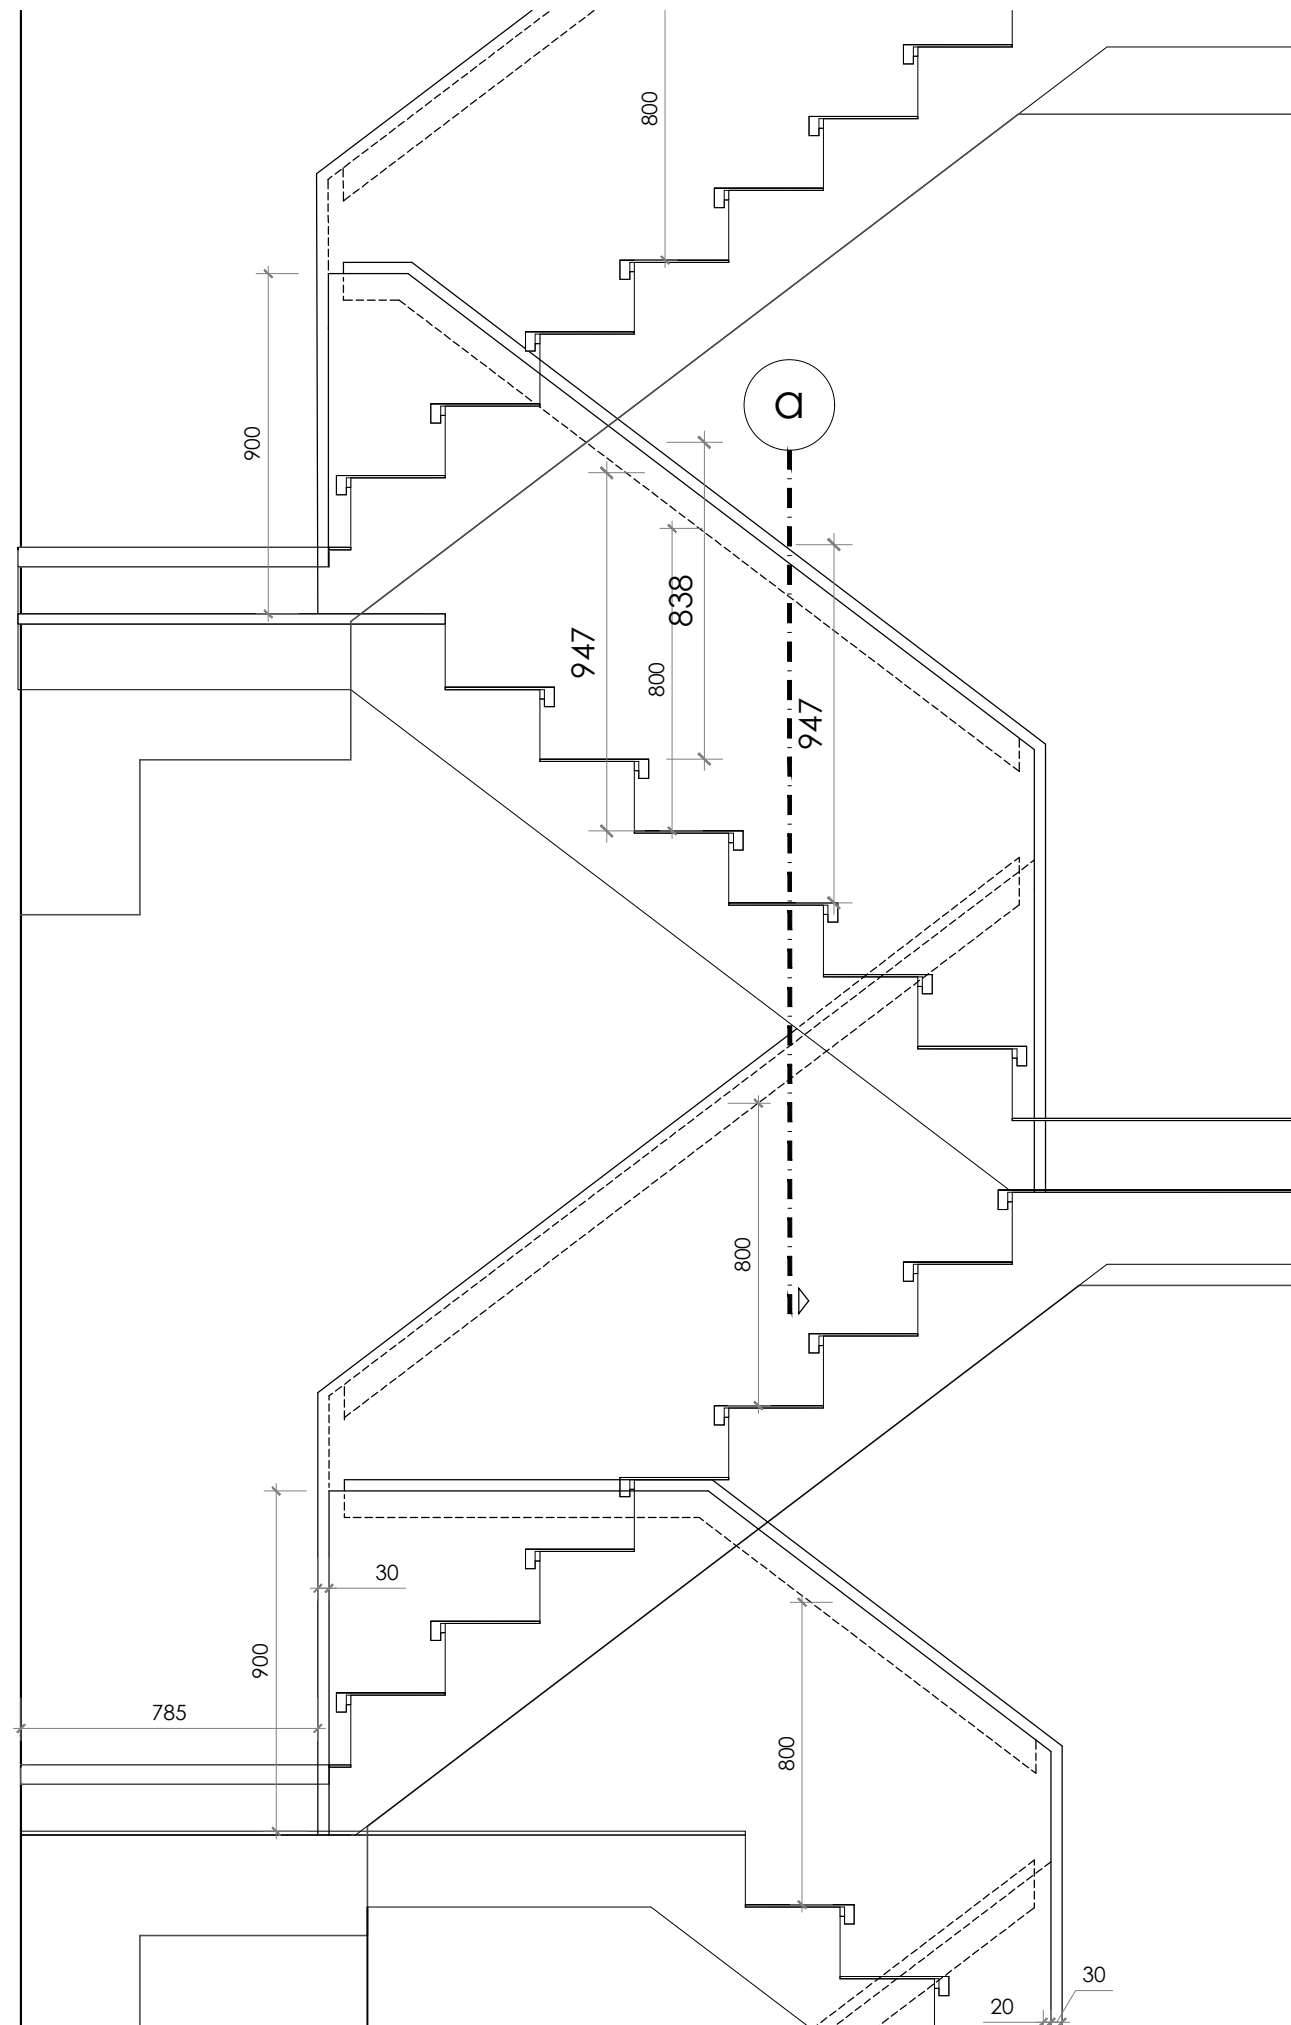

備註:

- a. 圖面標註尺寸僅供參考，施作均以現場放樣檢證之。
- b. 圖面標註尺寸、材料及文字敘述因版本不同之差異，均以出圖章簽認日期之最近為準。
- c. 電腦圖檔除由合約訂定外，均不得以任何方式外流。
- d. 圖面所示均為本公司所擁有之智慧財產，切勿以任何方式複製修改。




Project / 案名

林口雲品薇閣姚宅

Sheet Title / 圖名
3F-4F

立面圖

Date / 日期	Scale / 比例
8/10/2026	1/50cm
Designer / 設計	Approval / 核准
MONICA LIN	
Job No. / 業務編號	Drawn By / 繪圖
00000	GUIDO
Dwg No.	Page No.
E-76	154

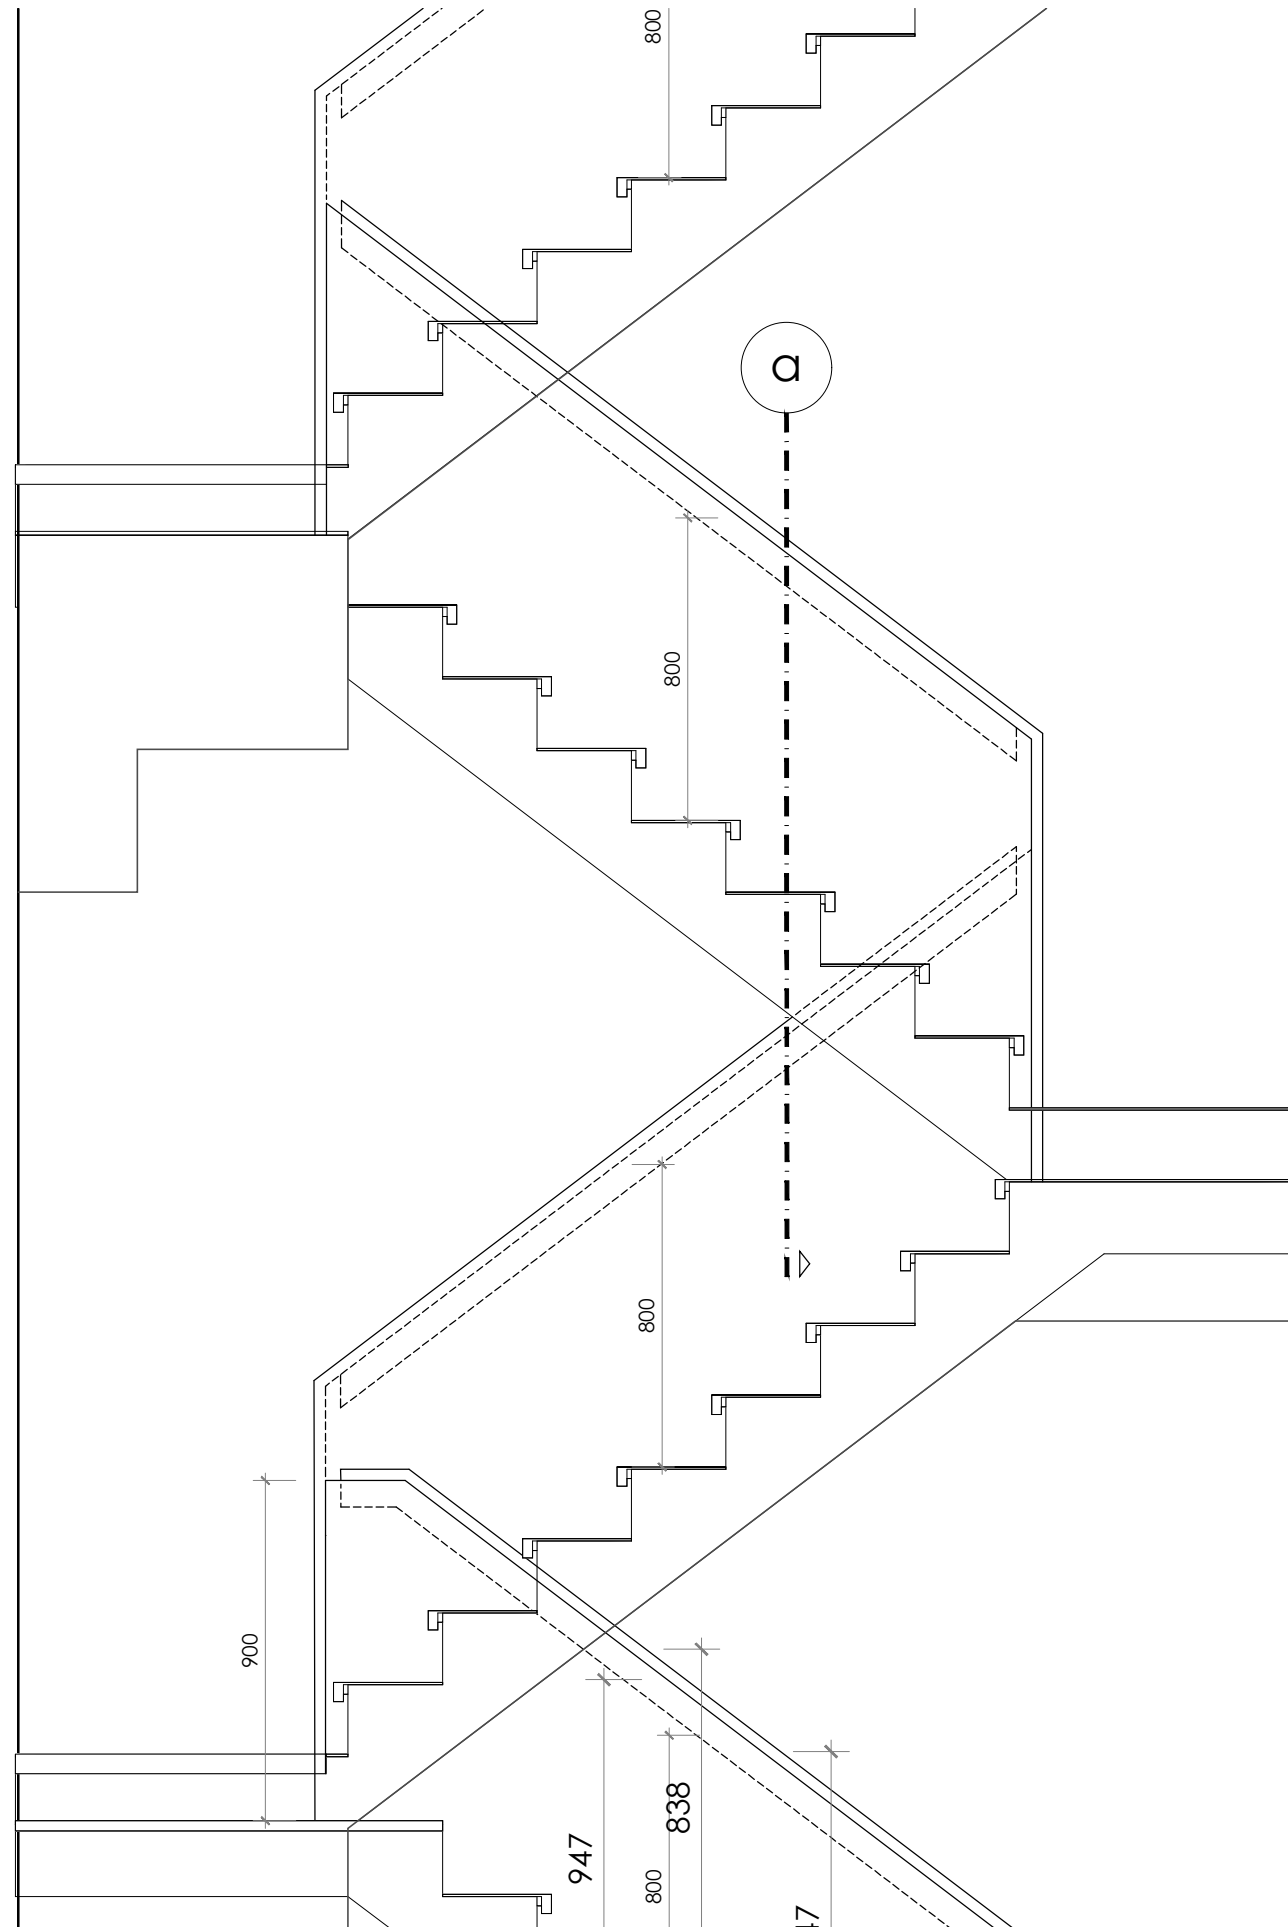



備註:


- a. 圖面標註尺寸僅供參考，施作均以現場放樣檢討之。
- b. 圖面標註尺寸、材料及文字敘述因版本不同之差異，均以出國章簽認日期之最近為準。
- c. 電腦圖權除由合約訂定外，均不得以任何方式外流。
- d. 圖面所示均為本公司所擁有之智慧財產，切勿以任何方式複製修改。

Project / 案名

林口雲品薇閣姚宅

Sheet Title / 圖名 4F-5F	
立面圖	
Date / 日期	Scale / 比例
8/10/2026	1/50cm
Designer / 設計	Approval / 核准
MONICA LIN	
Job No / 業務編號	Drawn By / 繪圖
00000	GUIDO
Dwg No.	Page No.
E-77	155

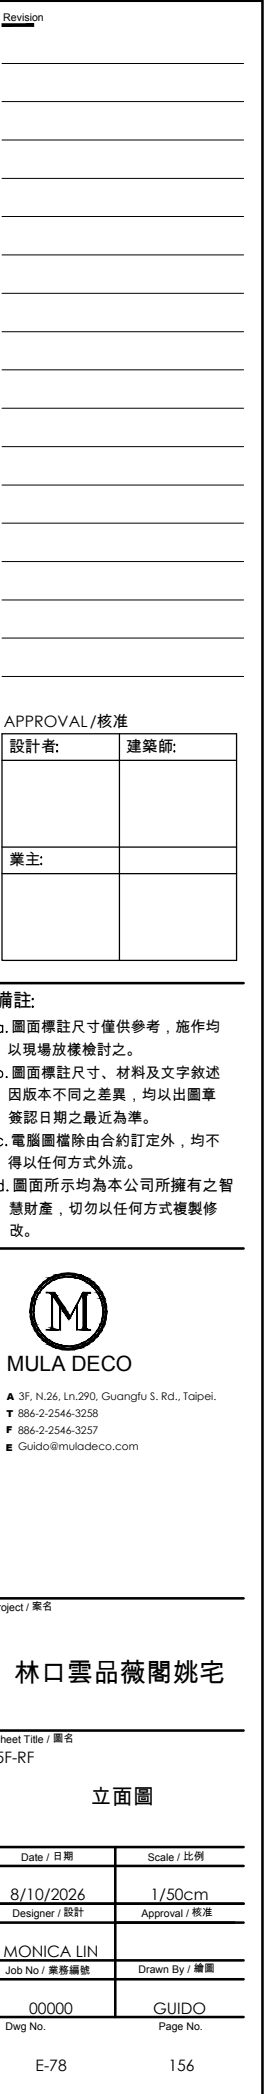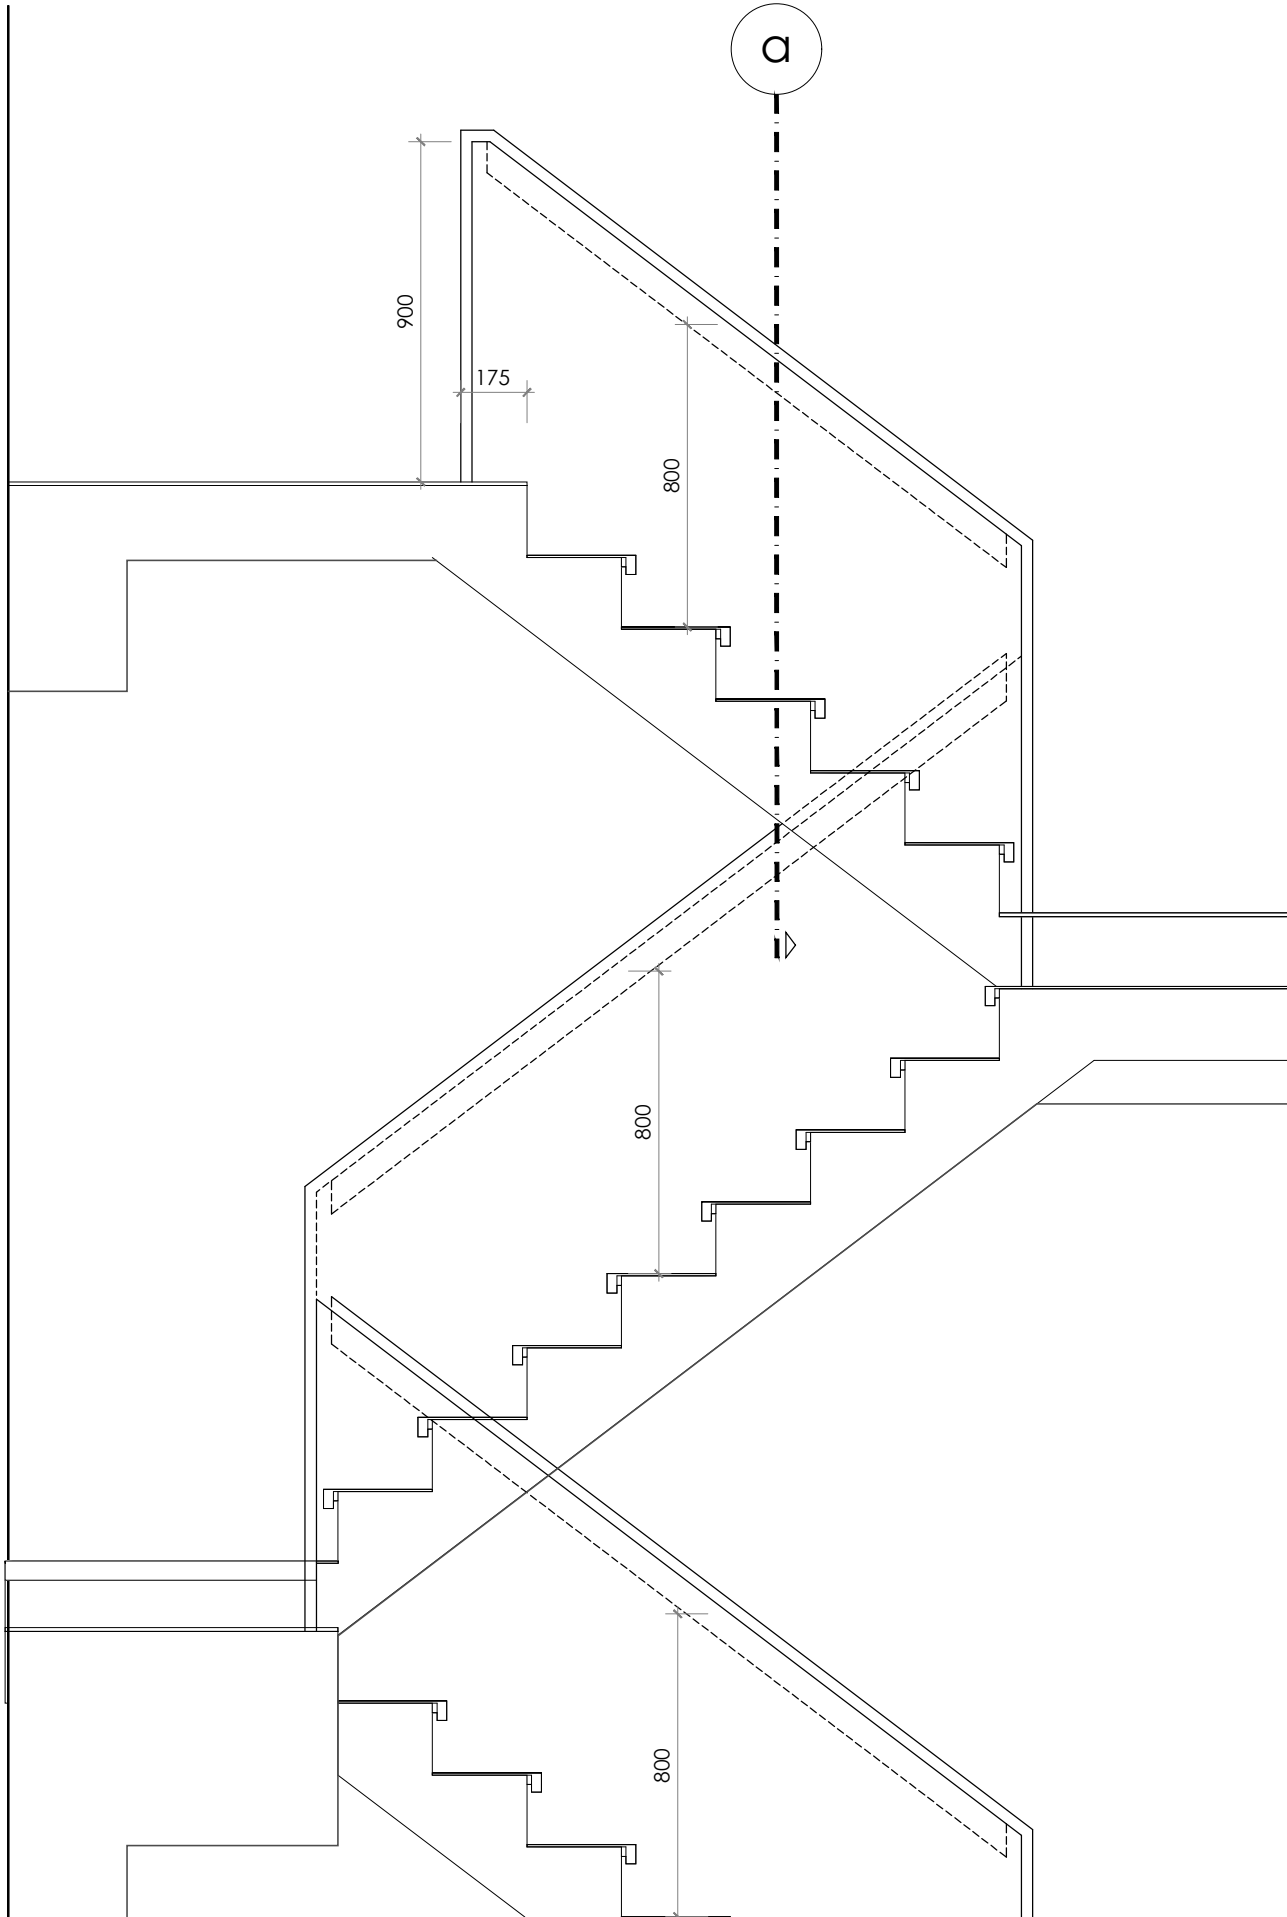

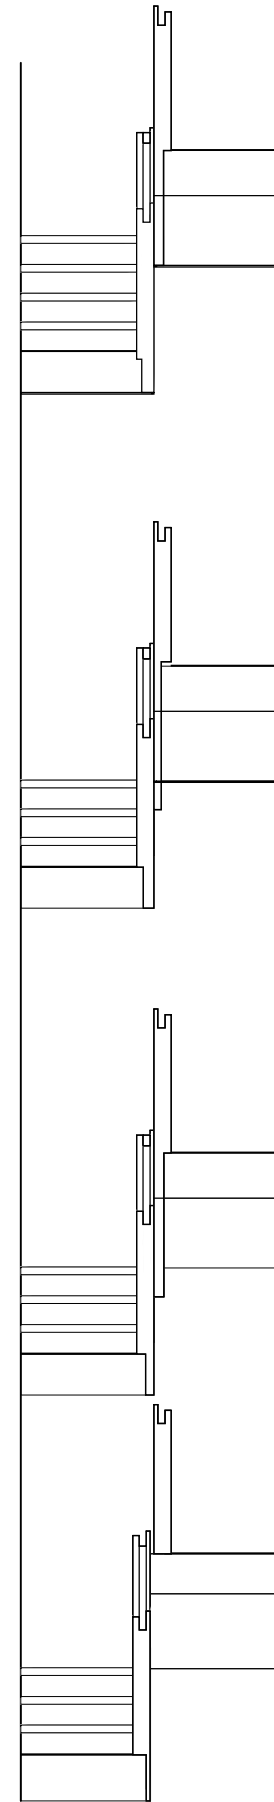

Revision	
APPROVAL /核准	
設計者:	建築師:
業主:	

備註:

- a. 圖面標註尺寸僅供參考，施作均以現場放樣檢討之。
- b. 圖面標註尺寸、材料及文字敘述因版本不同之差異，均以出圖章簽認日期之最近為準。
- c. 電腦圖檔除由合約訂定外，均不得以任何方式外流。
- d. 圖面所示均為本公司所擁有之智慧財產，切勿以任何方式複製修改。





MULA DECO

▲ 3F, N.26, Ln.290, Guangfu S. Rd., Taipei.
☎ 886-2-2546-3258
✉ 886-2-2546-3257
E Guido@mula deco.com

Project / 案名
林口雲品薇閣姚宅
Sheet Title / 圖名
2F-RF 立面圖

Date / 日期	Scale / 比例
8/10/2026	1/50cm
Designer / 設計	Approval / 核准
MONICA LIN	
Job No / 案務編號	Drawn By / 繪圖
00000	GUIDO
Dwg No.	Page No.
E-79	157

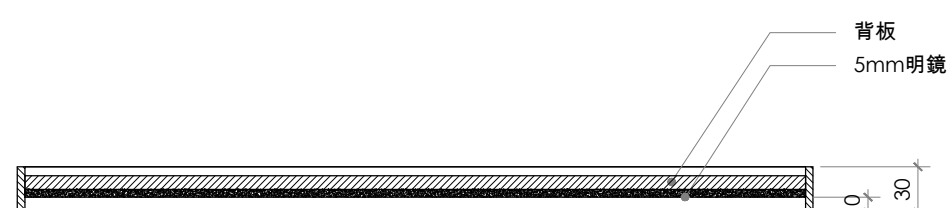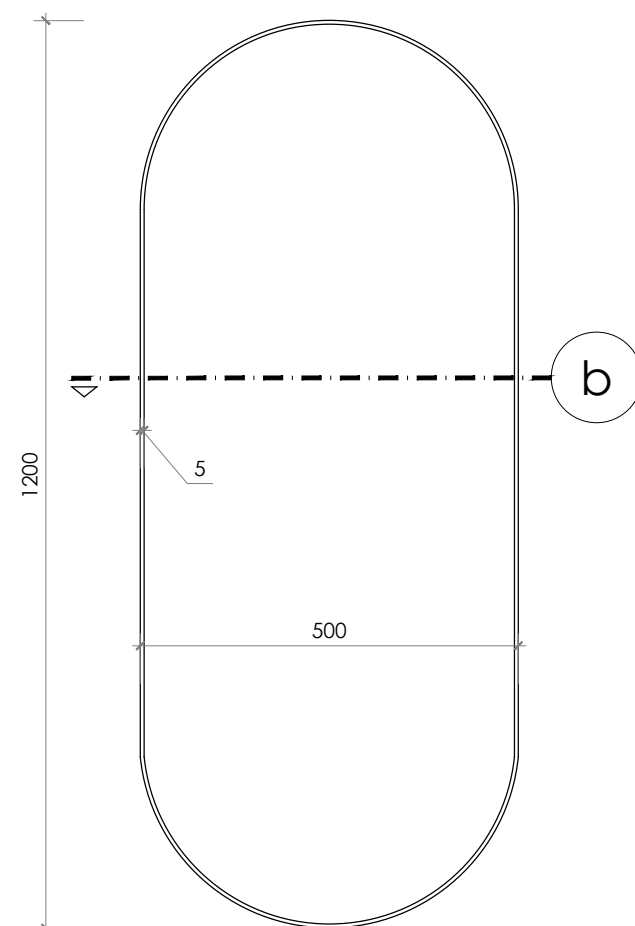

b DETAIL S 1:5

APPROVAL/核准	
設計者:	建築師:
業主:	

備註:

- a. 圖面標註尺寸僅供參考，施作均以現場放樣檢討之。
- b. 圖面標註尺寸、材料及文字敘述因版本不同之差異，均以出圖章簽認日期之最近為準。
- c. 電腦圖檔除由合約訂定外，均不得以任何方式外流。
- d. 圖面所示均為本公司所擁有之智慧財產，切勿以任何方式複製修改。






Project / 案名

林口雲品薇閣姚宅

Sheet Title / 圖名
B1
細部大樣圖

DE-01 158

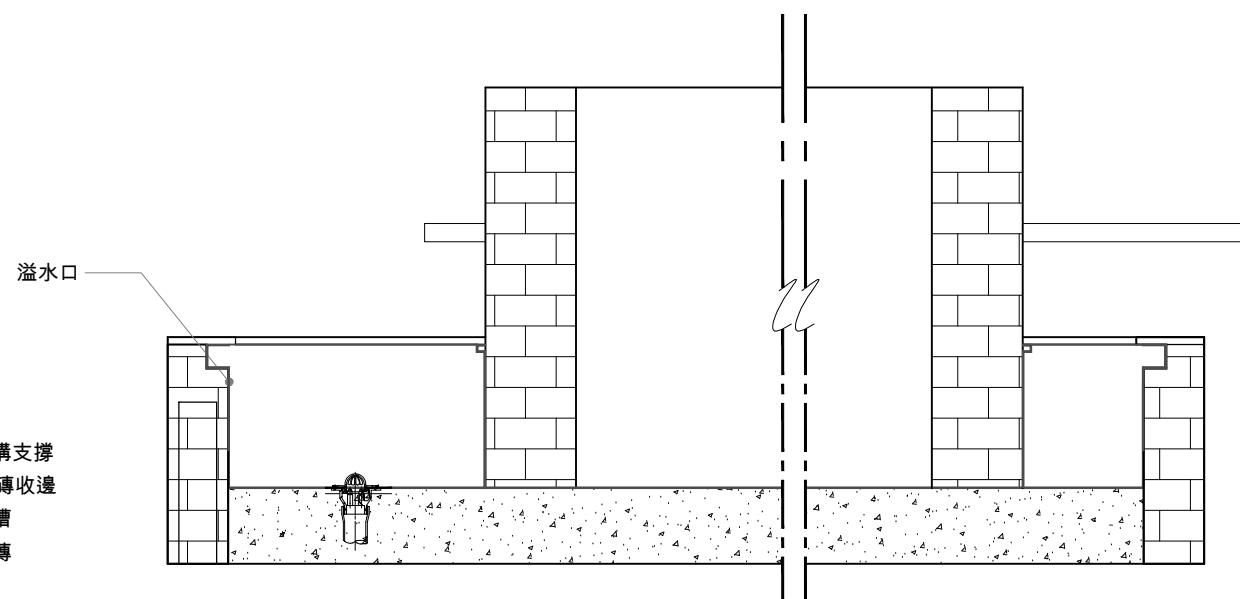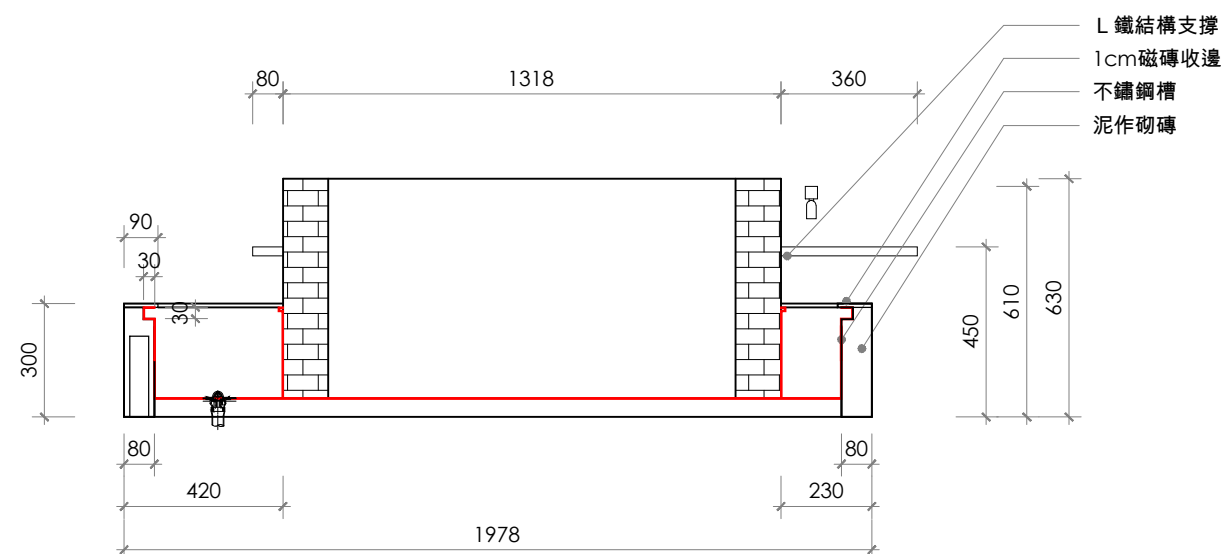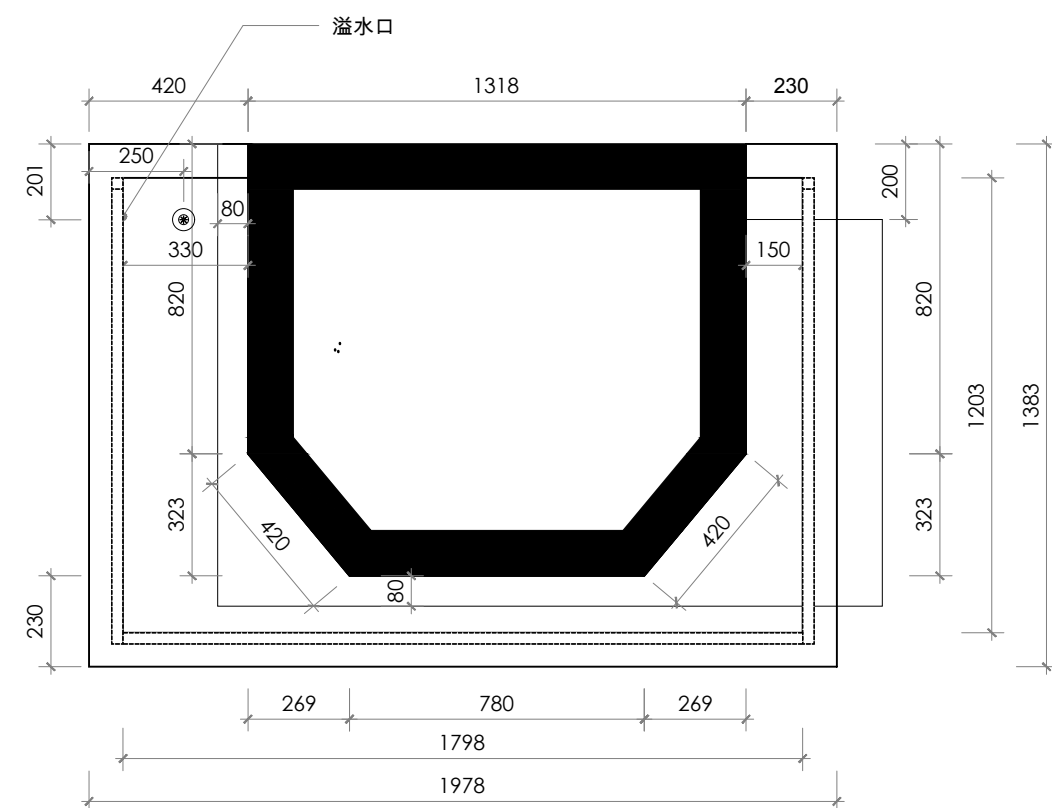

Revision

APPROVAL/核准

設計者:	建築師:
業主:	

備註:

- q. 圖面標註尺寸僅供參考，施作均以現場放樣檢討之。
- b. 圖面標註尺寸、材料及文字敘述因版本不同之差異，均以出圖章簽認日期之最近為準。
- c. 電腦圖檔除由合約訂定外，均不得以任何方式外流。
- d. 圖面所示均為本公司所擁有之智慧財產，切勿以任何方式複製修改。



MULA DECO

A 3F, N.26, Ln.290, Guangfu S. Rd., Taipei.
T 886-2-2546-3258
F 886-2-2546-3257
E Guido@muladeco.com

Project / 案名

林口雲品薇閣姚宅



Sheet Title / 圖名
1F

細部大樣圖

Date / 日期	Scale / 比例
8/10/2026	1/20cm
Designer / 設計	Approval / 核准
MONICA LIN	
Job No / 業務編號	Drawn By / 繪圖
00000	GUIDO

DE-02

159

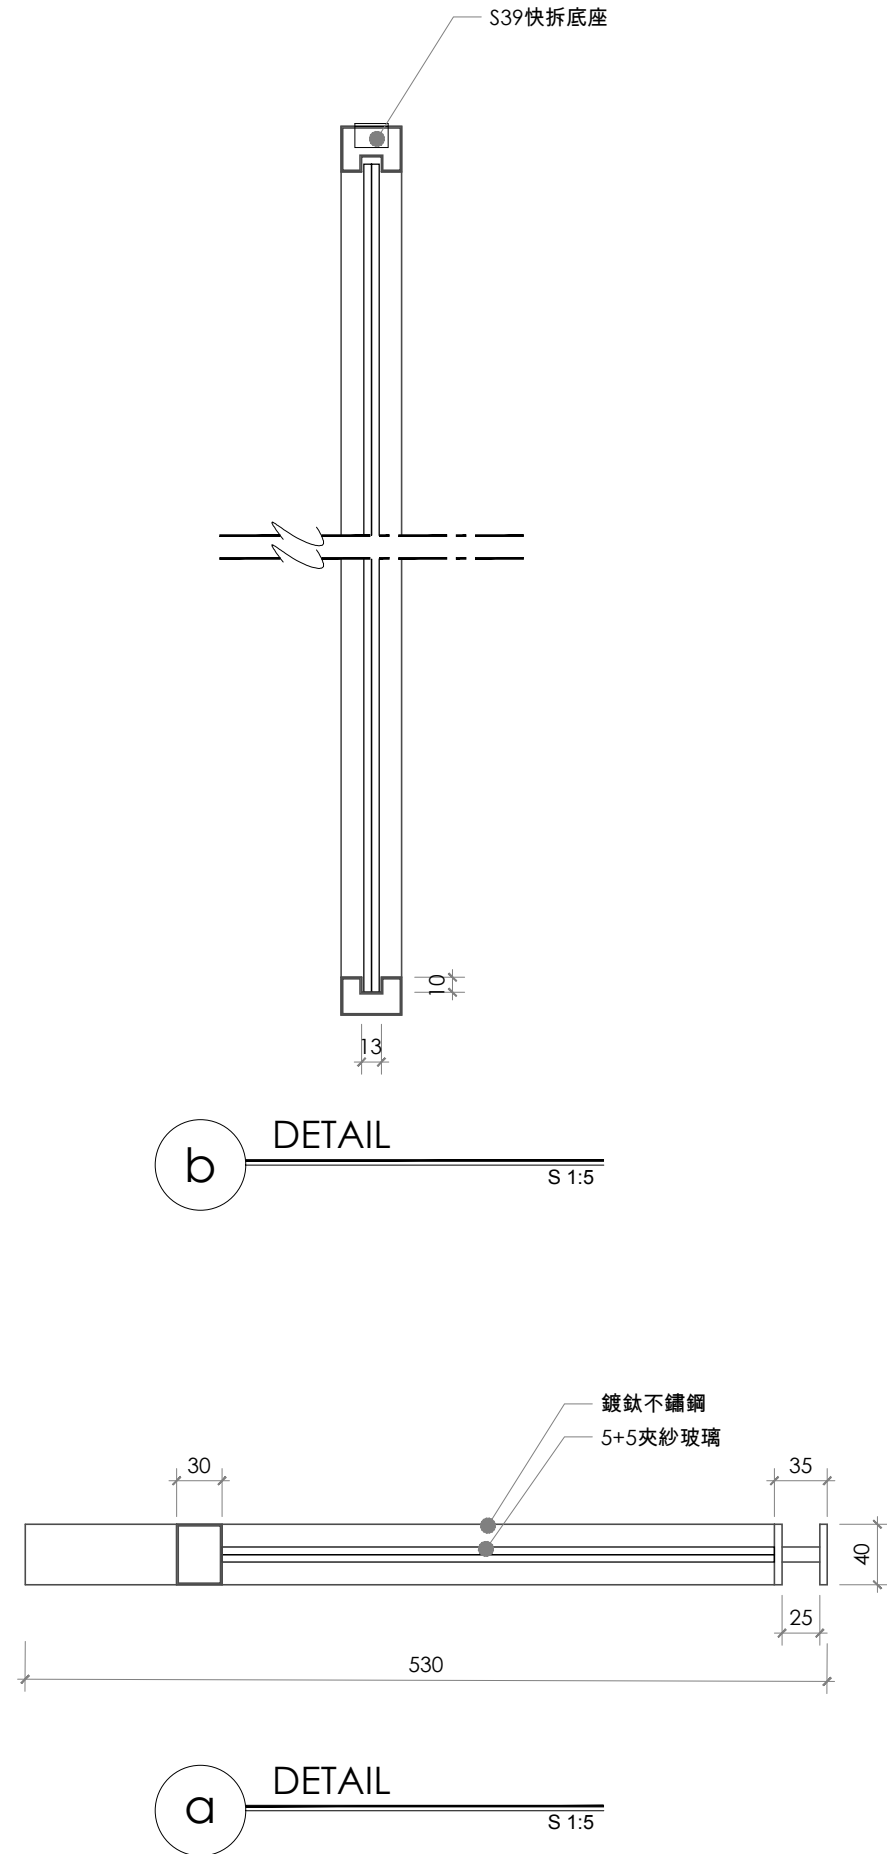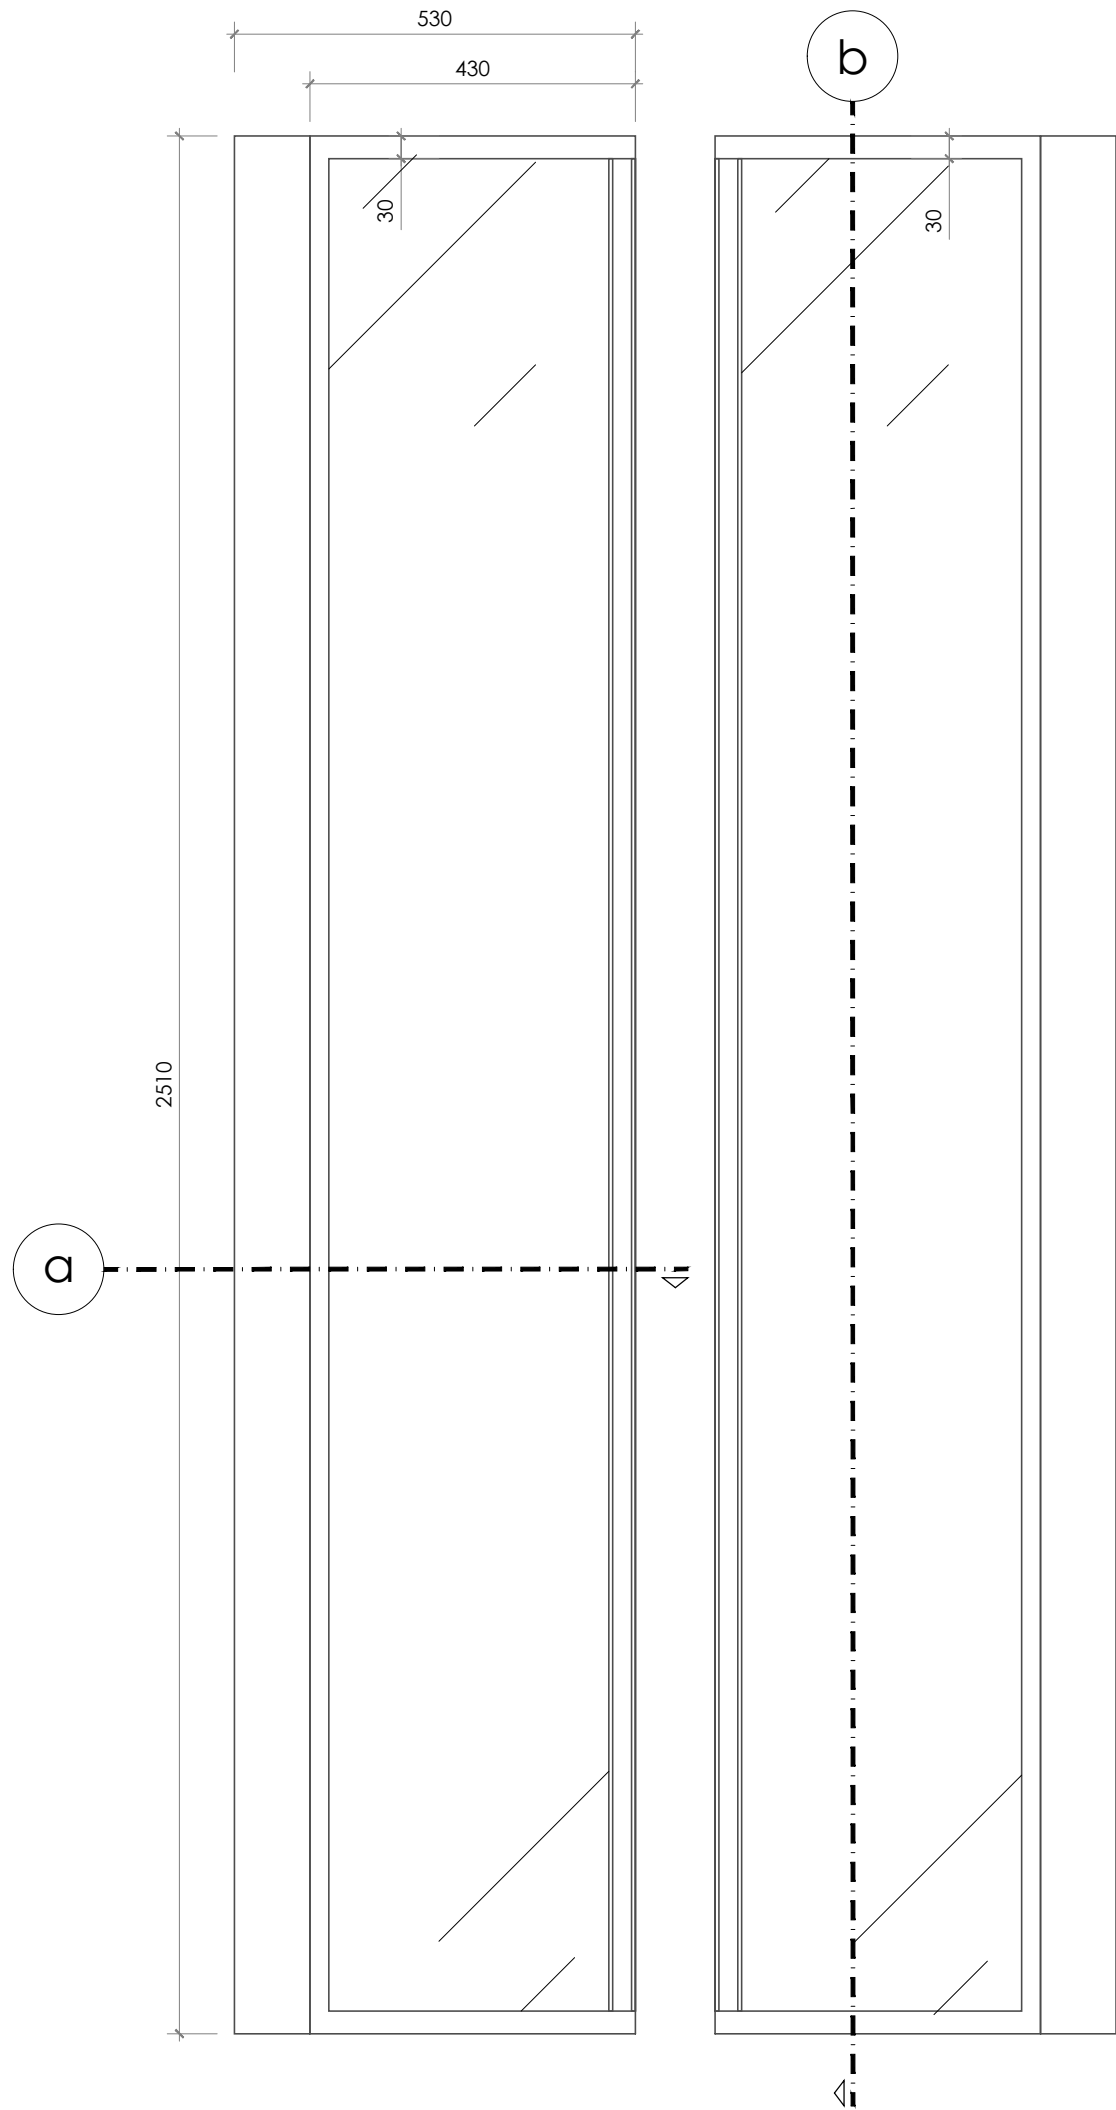

Revision

APPROVAL/核准

設計者:	建築師:
業主:	

備註:

- a. 圖面標註尺寸僅供參考，施作均以現場放樣檢討之。
b. 圖面標註尺寸、材料及文字敘述因版本不同之差異，均以出圖章簽認日期之最近為準。
c. 電腦圖檔除由合約訂定外，均不得以任何方式外流。
d. 圖面所示均為本公司所擁有之智慧財產，切勿以任何方式複製修改。



MULA DECO

▲ 3F, N.26, Ln.290, Guangfu S. Rd., Taipei.
☎ 886-2-2546-3258
✉ 886-2-2546-3257
E Guido@muladeco.com


Project / 案名

林口雲品薇閣姚宅

Sheet Title / 圖名
4F

細部大樣圖

Date / 日期	Scale / 比例
8/10/2026	1/10cm
Designer / 設計	Approval / 核准
MONICA LIN	
Job No / 業務編號	Drawn By / 繪圖
00000	GUIDO
Dwg No.	Page No.
DE-03	160

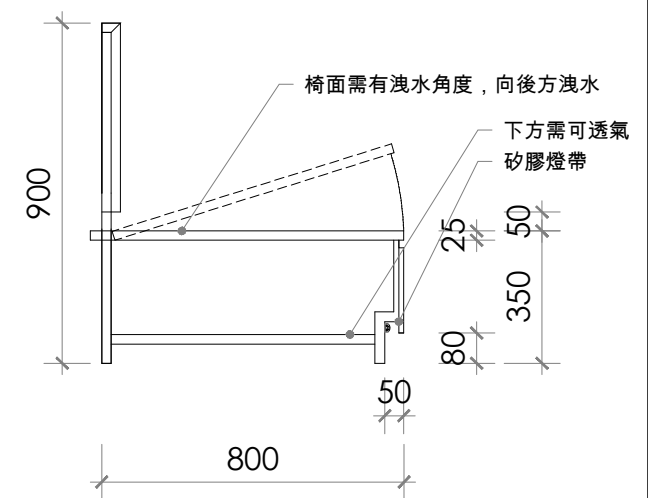[illegible]

備註:

- 圖面標註尺寸僅供參考，施作均以現場放樣檢討之。
- 圖面標註尺寸、材料及文字敘述因版本不同之差異，均以出圖章簽認日期之最近為準。
- 電腦圖檔除由合約訂定外，均不得以任何方式外流。
- 圖面所示均為本公司所擁有之智慧財產，切勿以任何方式複製修改。


MULA DECO
A 3F, N.26, Ln.290, Guangfu S. Rd., Taipei.
T 886-2-2546-3258
F 886-2-2546-3257
E Guido@mula deco.com

Project / 案名

林口雲品薇閣姚宅

Sheet Title / 圖名
P1

鏡面細部大樣圖

Date / 日期	Scale / 比例
8/10/2026	1/10MM
Designer / 設計	Approval / 核准
MONICA LIN	
Job No / 業務編號	Drawn By / 繪圖
80000	GUIDO
Dwg No.	Page No.