



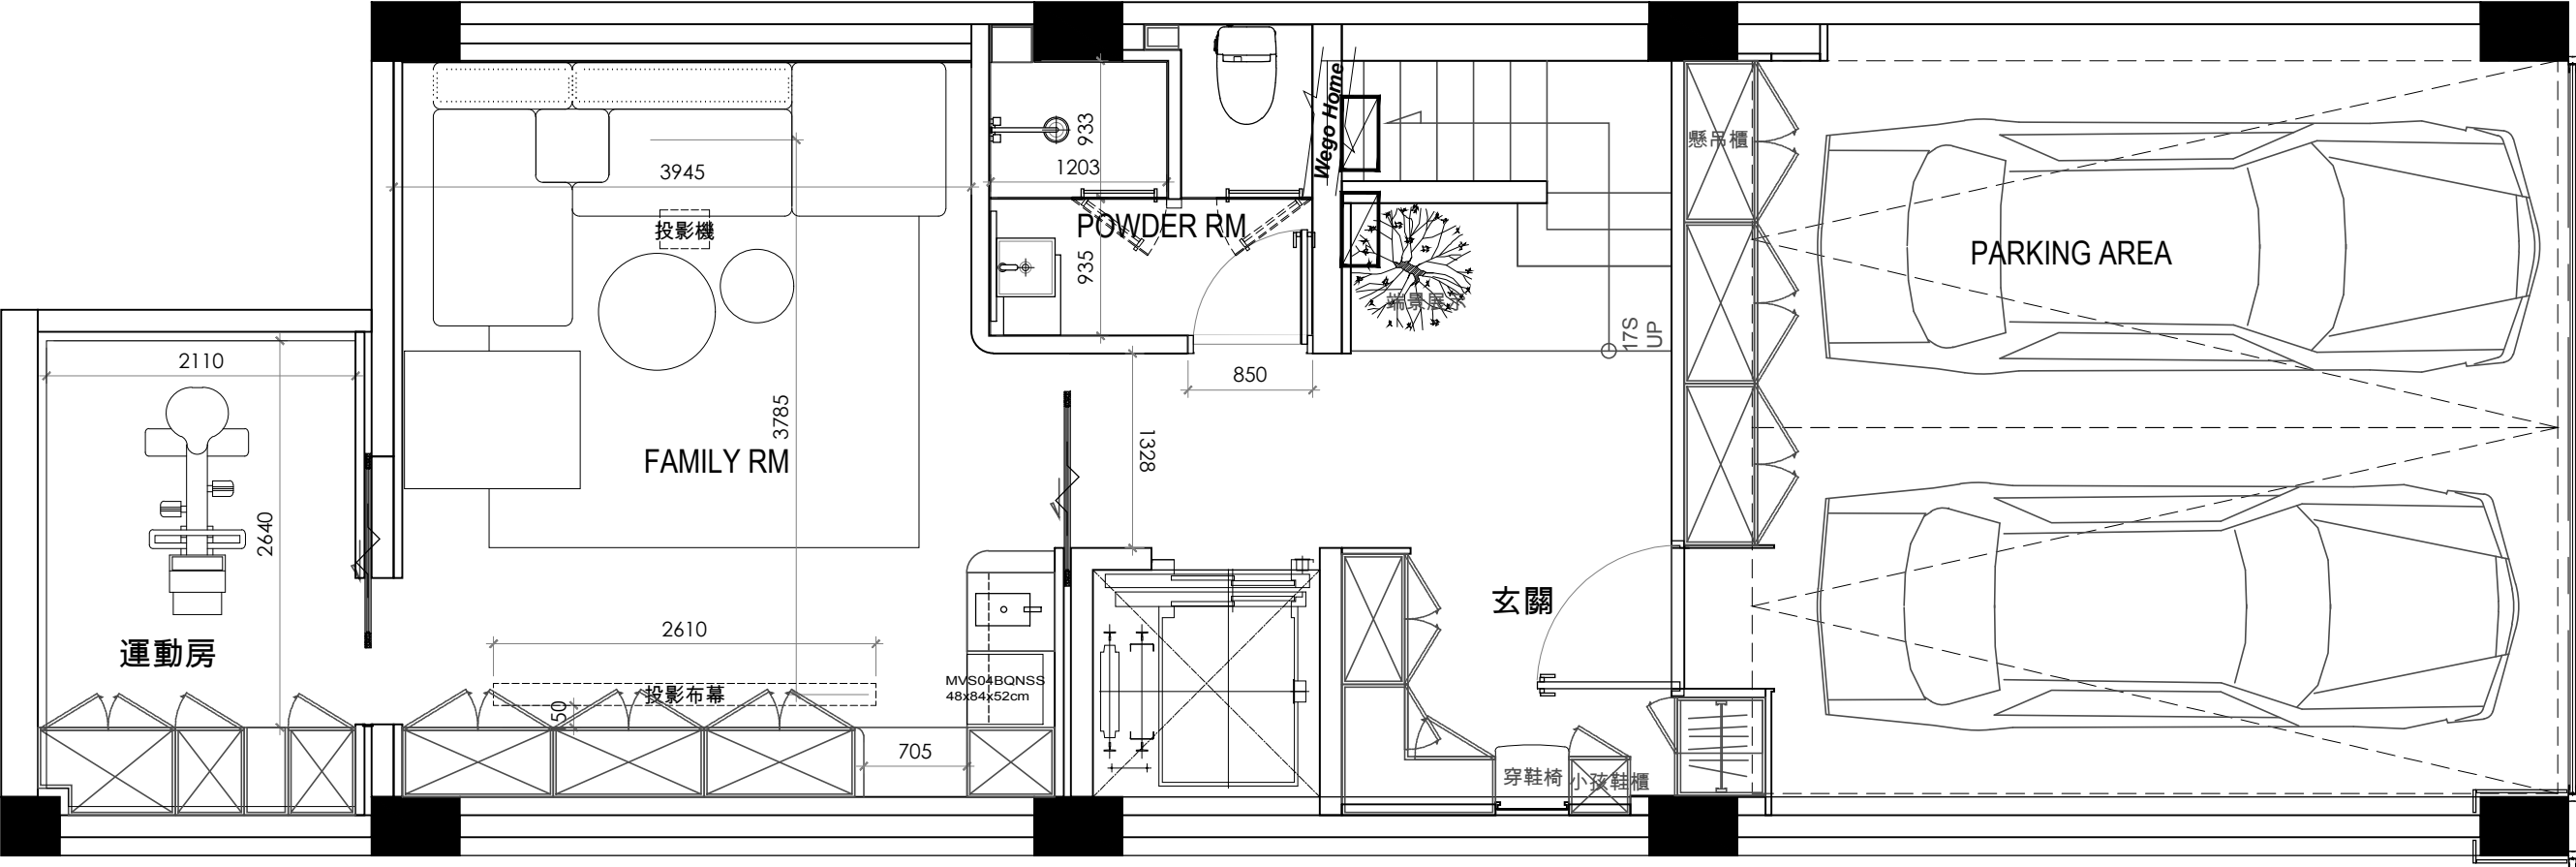

地下一層平面圖

牆 型 式	內 容	總 厚 度
	木作隔間牆	
	原有建築牆	154mm
	1/2B磚牆	120mm
	65mmC型骨架+單面(12mm石膏板+9mm矽酸鈣板),單面(12mm石膏板+9mm矽酸鈣板)	100mm
	65mmC型骨架+雙面矽酸鈣板	85mm

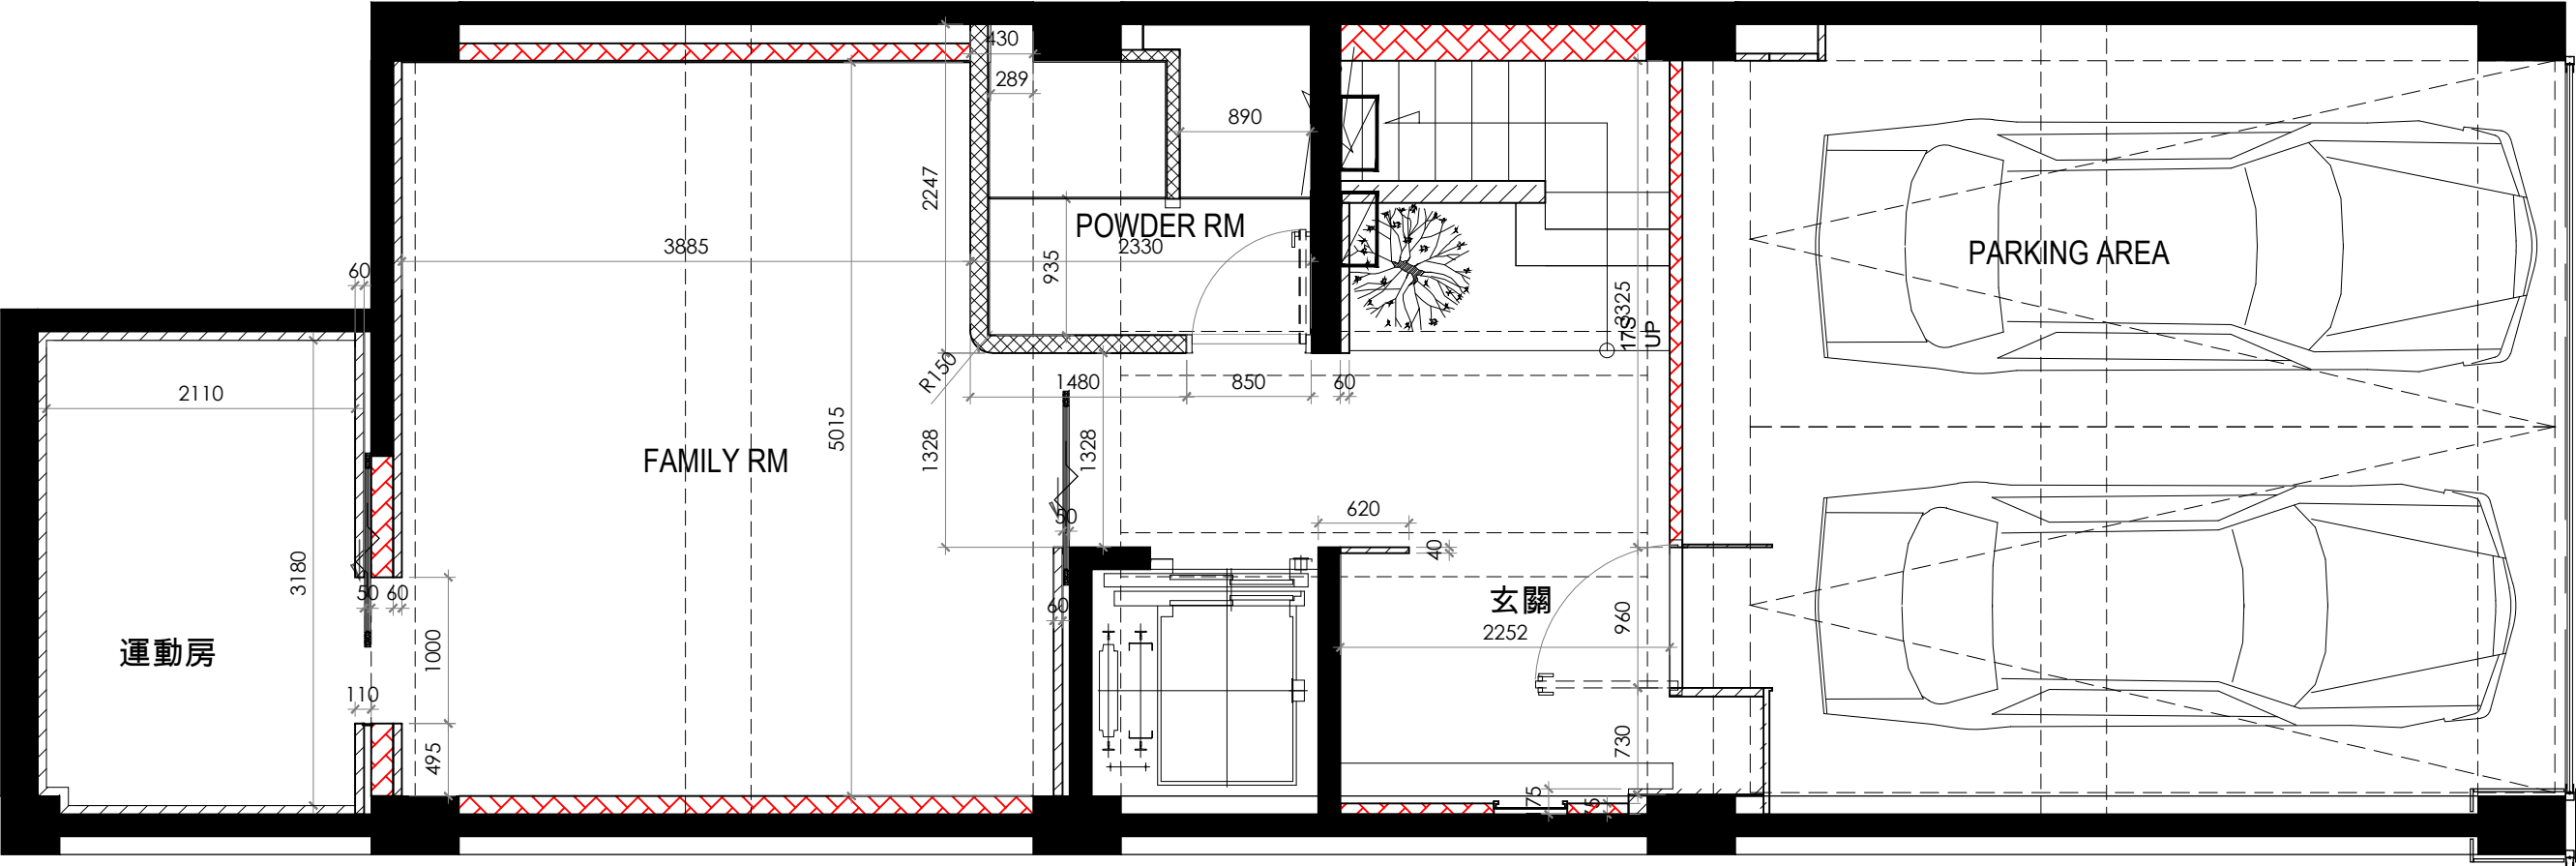

地下一層平面圖


編號	圖示	說明	尺寸	光源	備註
L1	◉	舞光LED可調角度嵌燈	88mm Dia x H25mm	KW-303 / 8W / 3000k / 嵌孔75mm	
L2	◉	2線式停電照明嵌燈	105mm Dia x H55mm	FH- 849-1B / 5W / 3000k / 嵌孔93mm	
L3	◉	3線式停電照明嵌燈	105mm Dia x H55mm	FH- 849-1B / 5W / 3000k / 嵌孔93mm	
L4	⊕	LED 15W 小吸頂燈	82mm Dia x H78mm	3000k	
L5	◉	舞光LED 邱比特軌道燈 白色	W88mm x L115mm x H50mm	AE-B07 / 7W / 3000k / 24°	
L6	◉	超薄嵌入式感應式嵌燈	85mm Dia x H50mm	3000k / 嵌孔75mm	
L7	----	LED軟條燈		3000k	
L8	=====	軌道燈軌道	W34mm x H20mm		
L9	•	小型嵌燈	63mm Dia x H72mm	3000k / 嵌孔55mm	
L10	▣	無邊框可調角LED單燈盒燈	W99mm x L99mm x H85mm	FH- 829-11C /10W /30° / 3000K	
L11	▣	無邊框可調角LED雙燈盒燈	W99mm x L199mm x H85mm	FH- 829-12C /10W /30° / 3000K	
L12	- · - · -	磁吸式軌道燈			
L13	=====	防塵防濕T5燈具			
L14	•	上照LED埋地燈	42mm Dia. x H90mm	LED /3W /12° /12V /3000K / 700mA	
DL-1	◆	吊燈			
DL-2	⊙	壁燈			

*燈具相關設備,需詳燈具規範最後確認.

*燈具供電皆為220V.

微波感應開關


微波感應開關

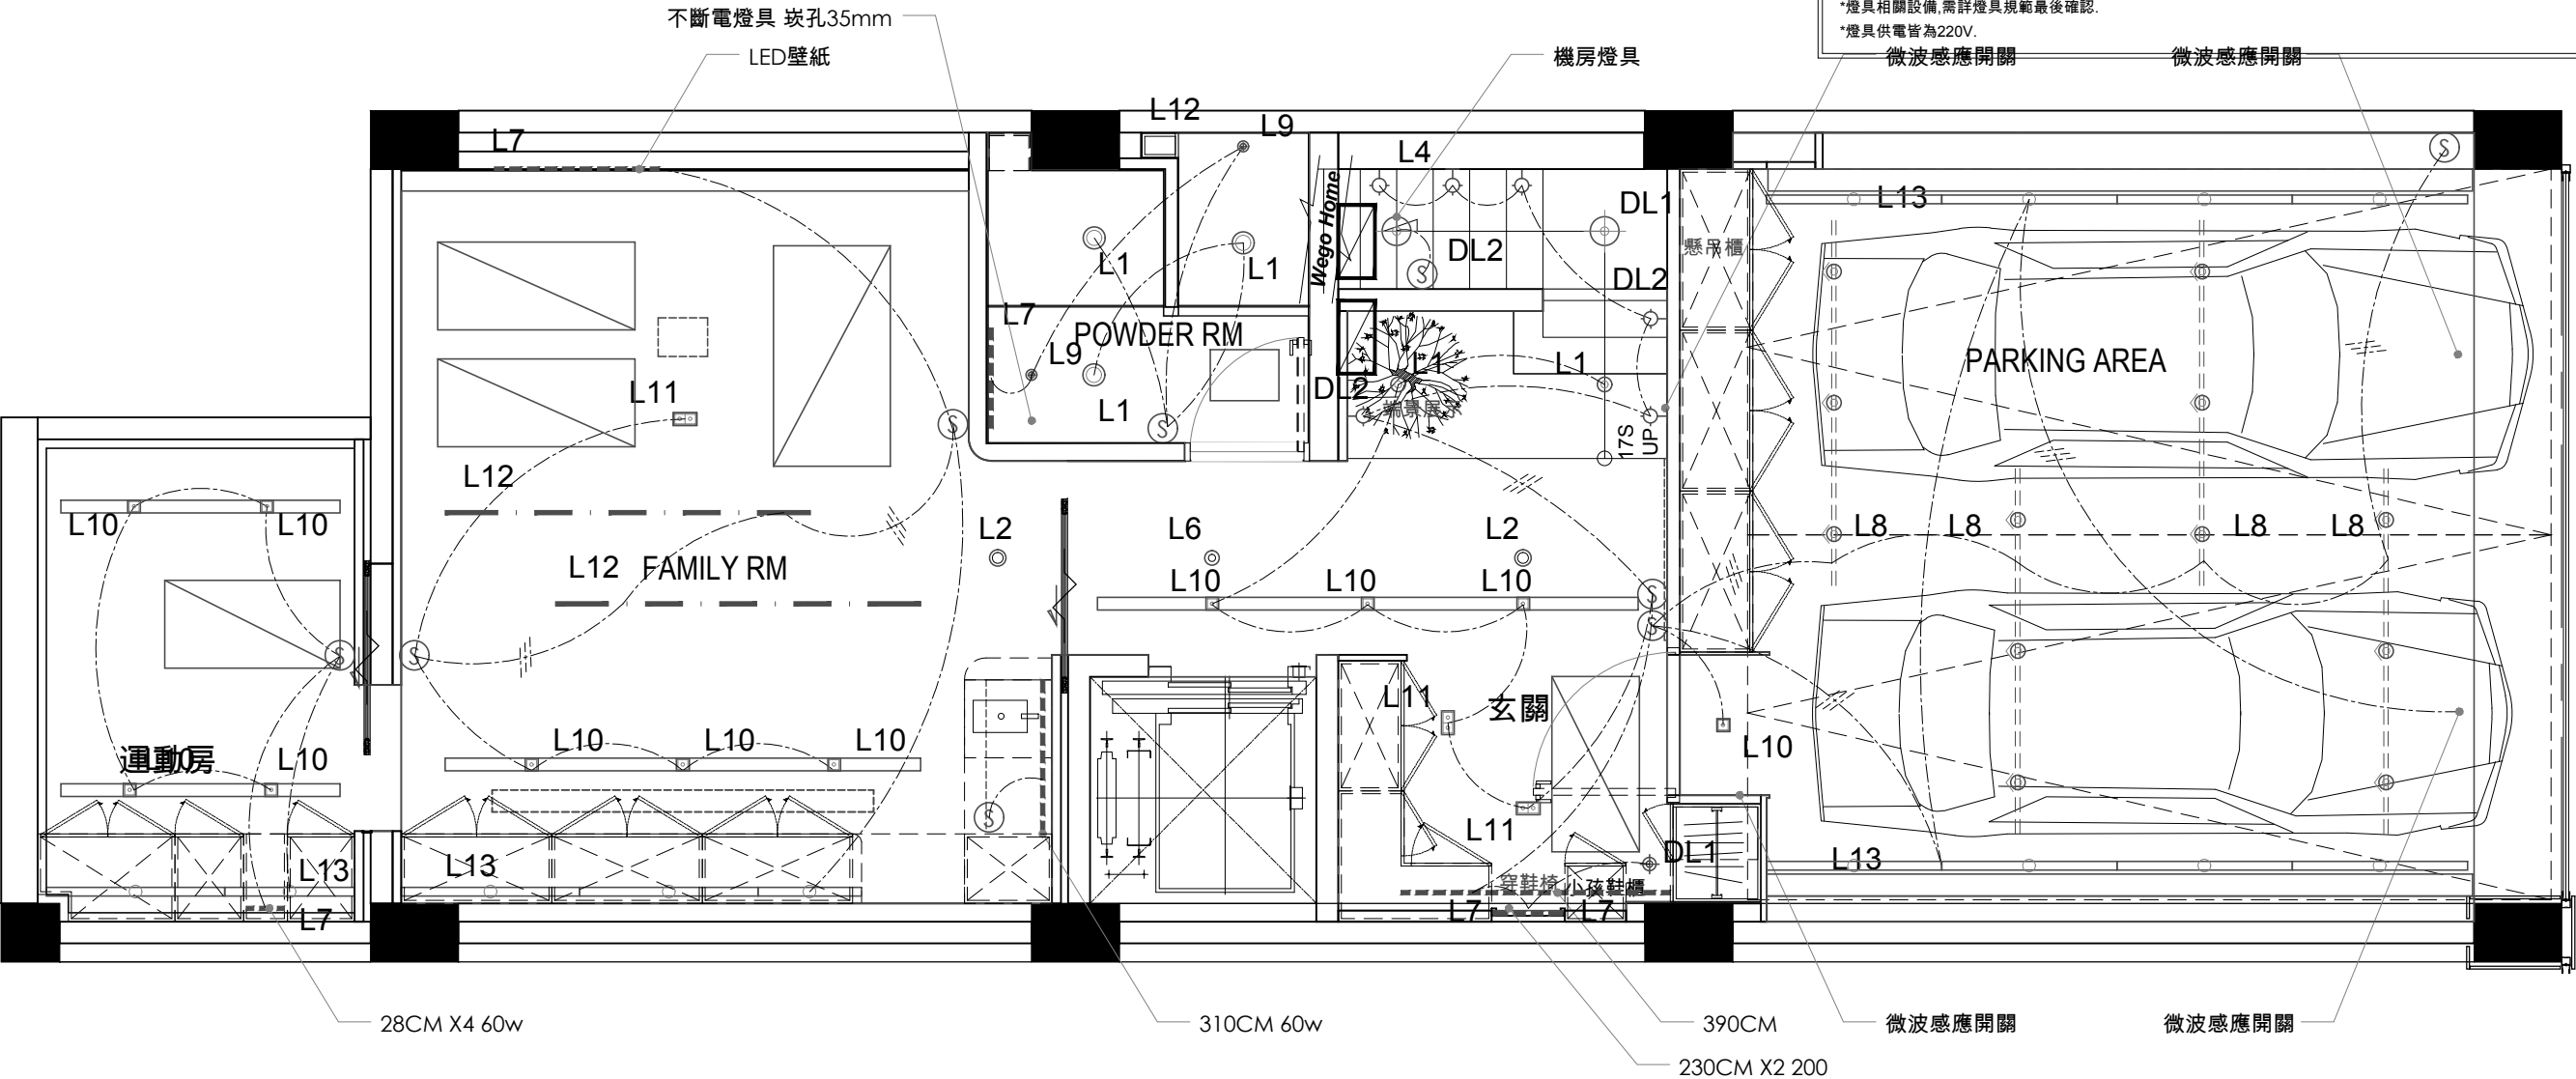


地下一層平面圖

編號	圖示	說明	尺寸	光源	備註
L1		舞光LED可調角度嵌燈	88mm Dia x H25mm	KW-303 / 8W / 3000k / 嵌孔75mm	
L2		2線式停電照明嵌燈	105mm Dia x H55mm	FH- 849-1B / 5W / 3000k / 嵌孔93mm	
L3		3線式停電照明嵌燈	105mm Dia x H55mm	FH- 849-1B / 5W / 3000k / 嵌孔93mm	
L4		LED 15W 小吸頂燈	82mm Dia x H78mm	3000k	
L5		舞光LED 邱比特軌道燈 白色	W88mm x L115mm x H50mm	AE-B07 / 7W / 3000k / 24°	
L6		超薄嵌入式感應式嵌燈	85mm Dia x H50mm	3000k / 嵌孔75mm	
L7		LED軟條燈		3000k	
L8		軌道燈軌道	W34mm x H20mm		
L9		小型嵌燈	63mm Dia x H72mm	3000k / 嵌孔55mm	
L10		無邊框可調角LED單燈盒燈	W99mm x L99mm x H85mm	FH- 829-11C /10W /30° / 3000K	
L11		無邊框可調角LED雙燈盒燈	W99mm x L199mm x H85mm	FH- 829-12C /10W /30° / 3000K	
L12		磁吸式軌道燈			
L13		防塵防濕T5燈具			
L14		上照LED埋地燈	42mm Dia. x H90mm	LED /3W /12° /12V /3000K / 700mA	
DL-1		吊燈			
DL-2		壁燈			
*燈具相關設備,需詳燈具規範最後確認。 *燈具供電皆為220V.					


空調設備圖例說明			
圖 例	說 明	圖 例	說 明
	側吹出風口		出風口
	側吹回風口		吊隱式除濕主機
	下吹出風口		五合一暖風機
	下吹回風口		全熱交換器

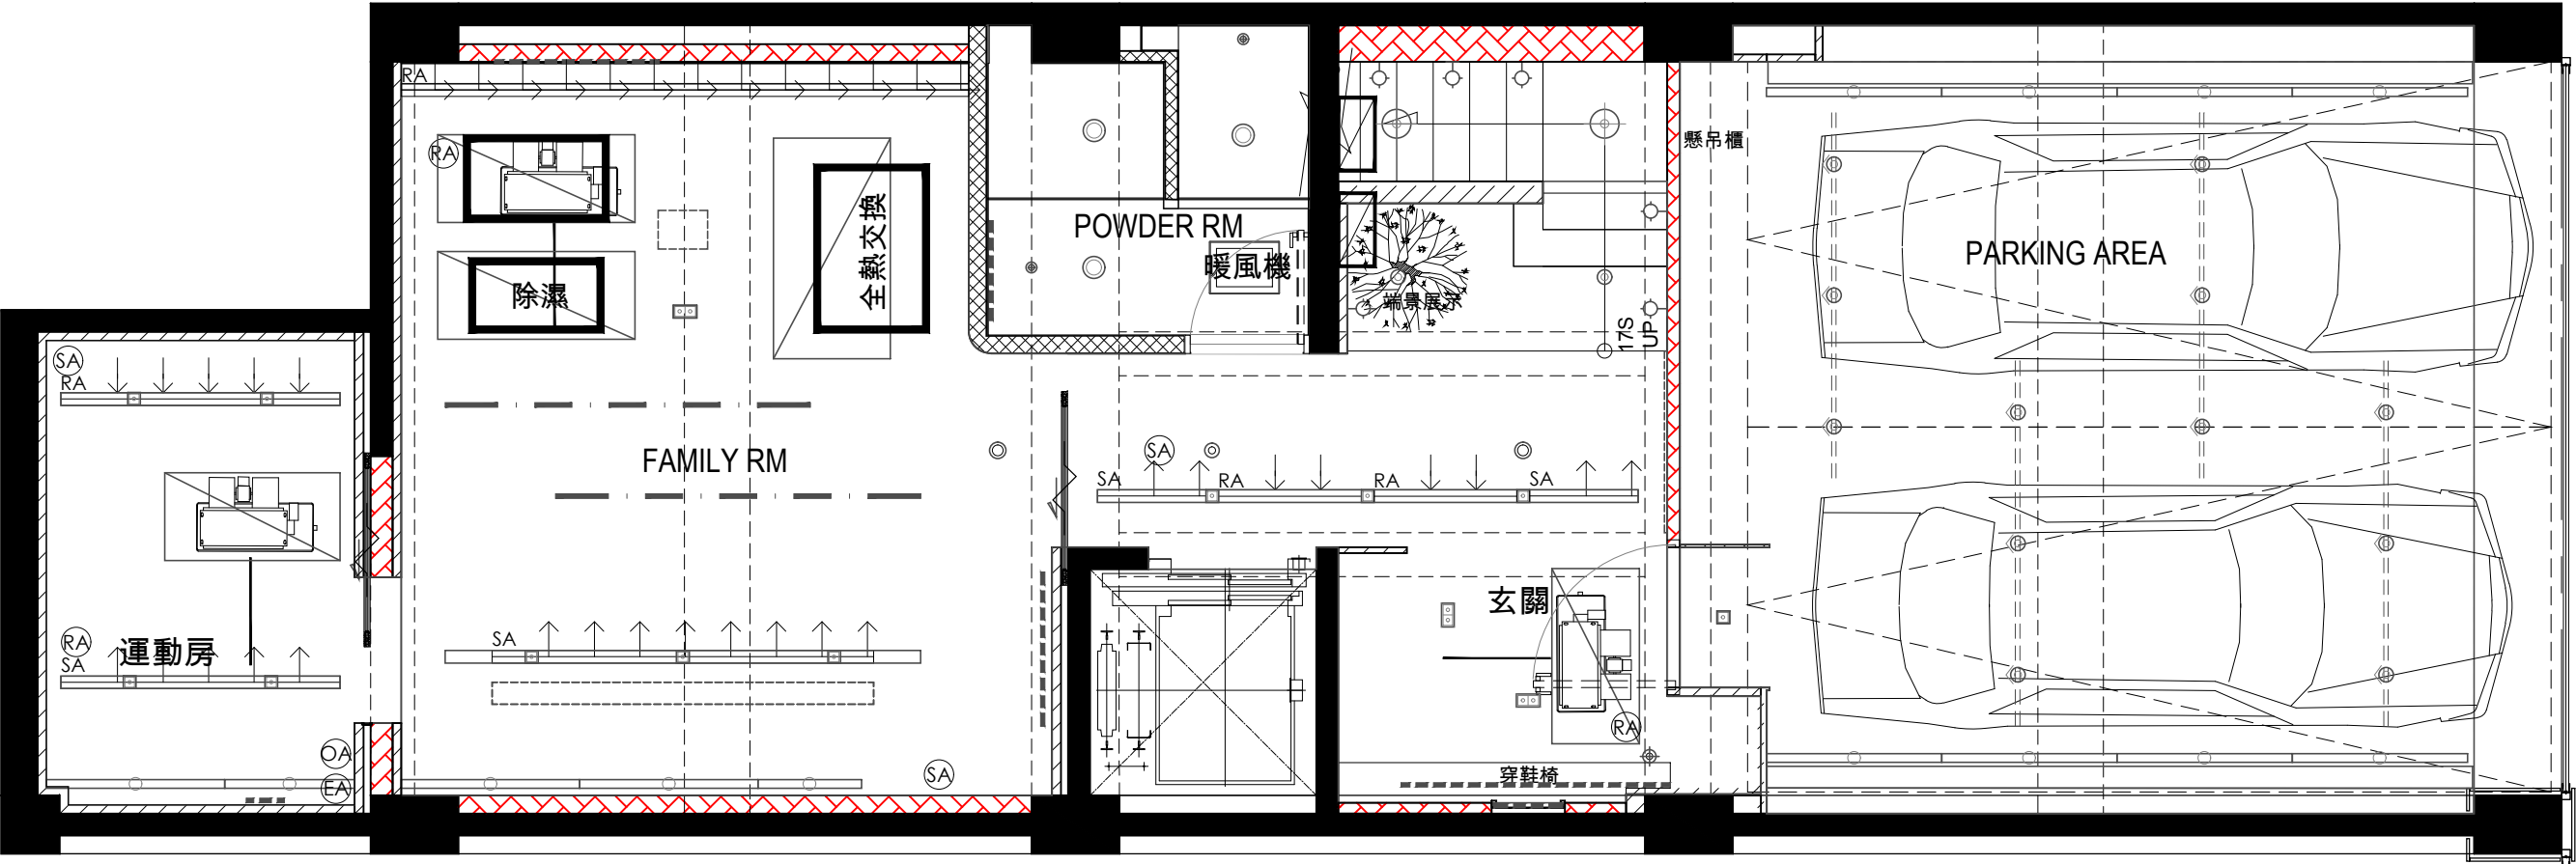


地下一層平面圖

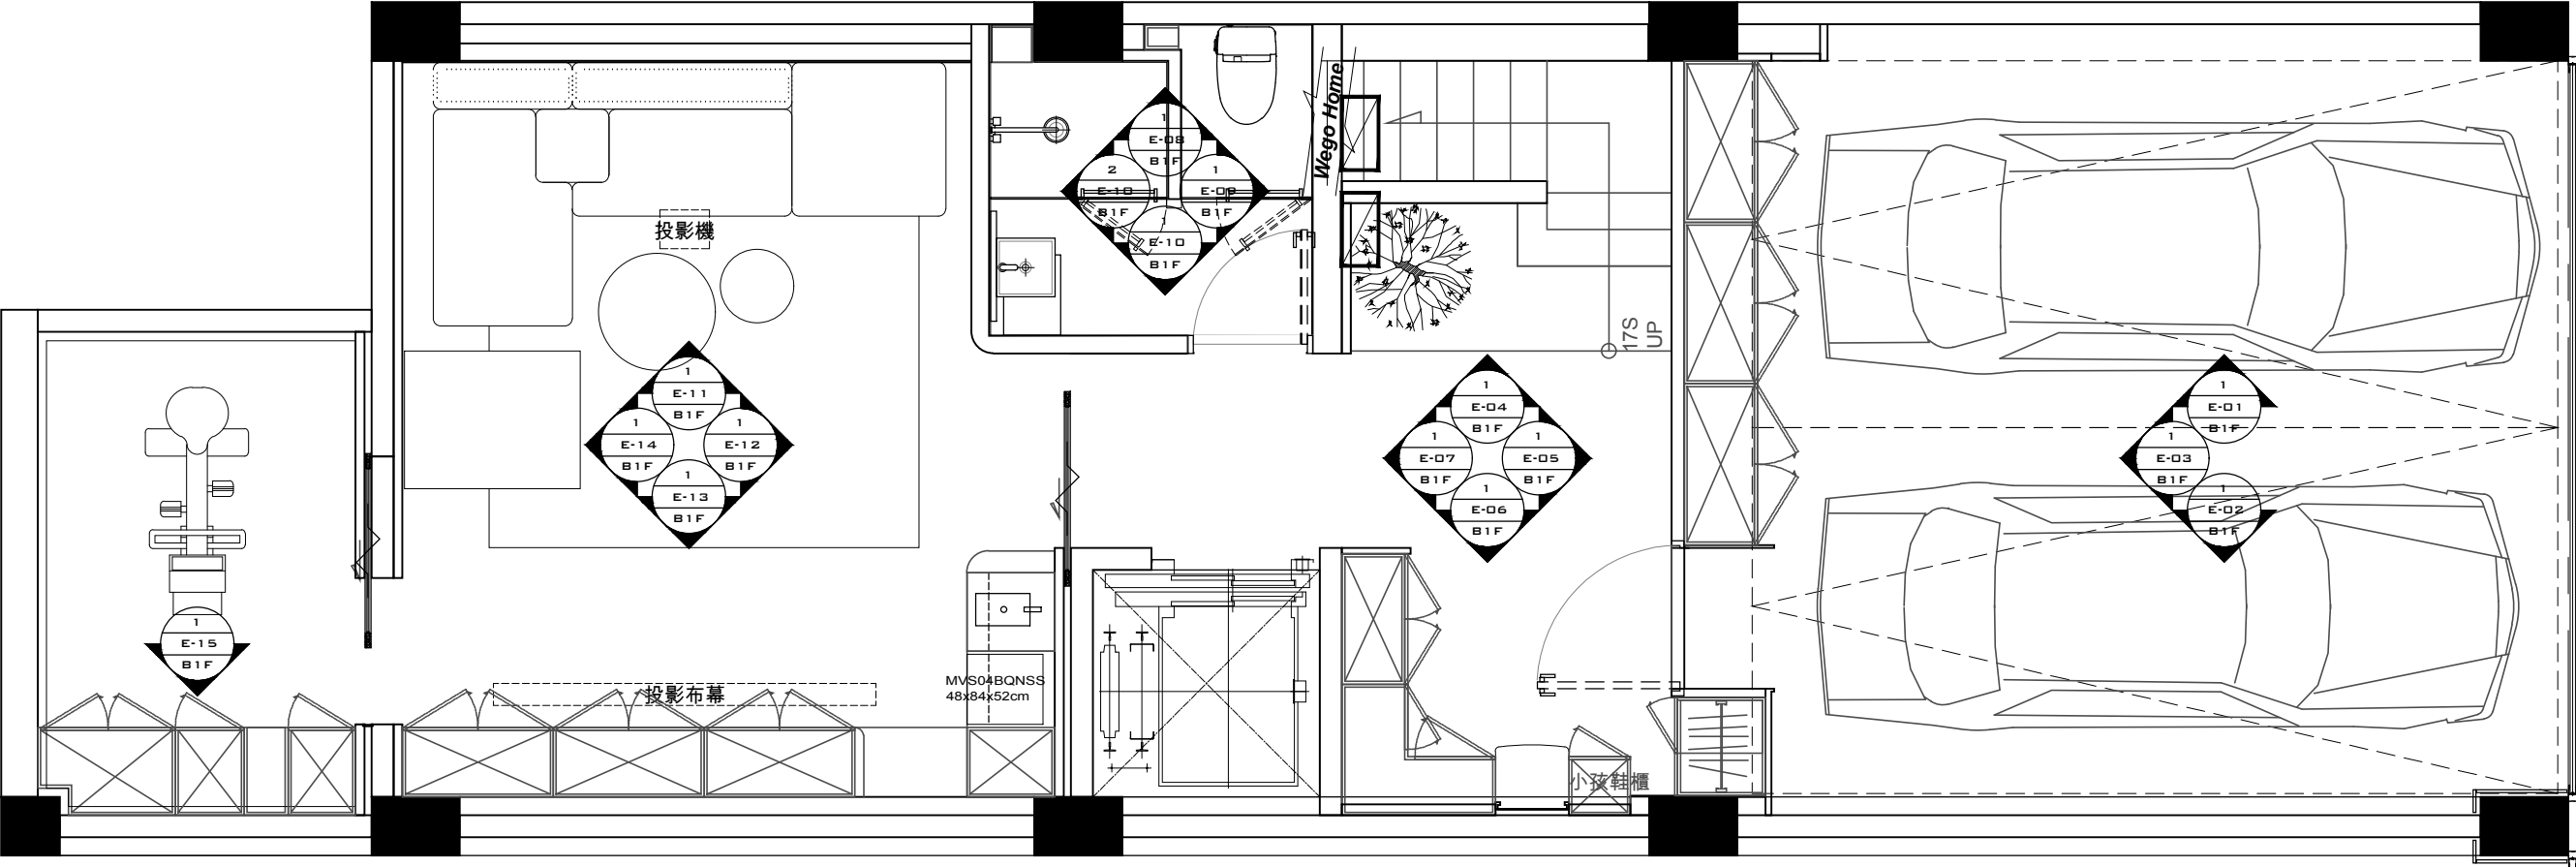

地下一層平面圖

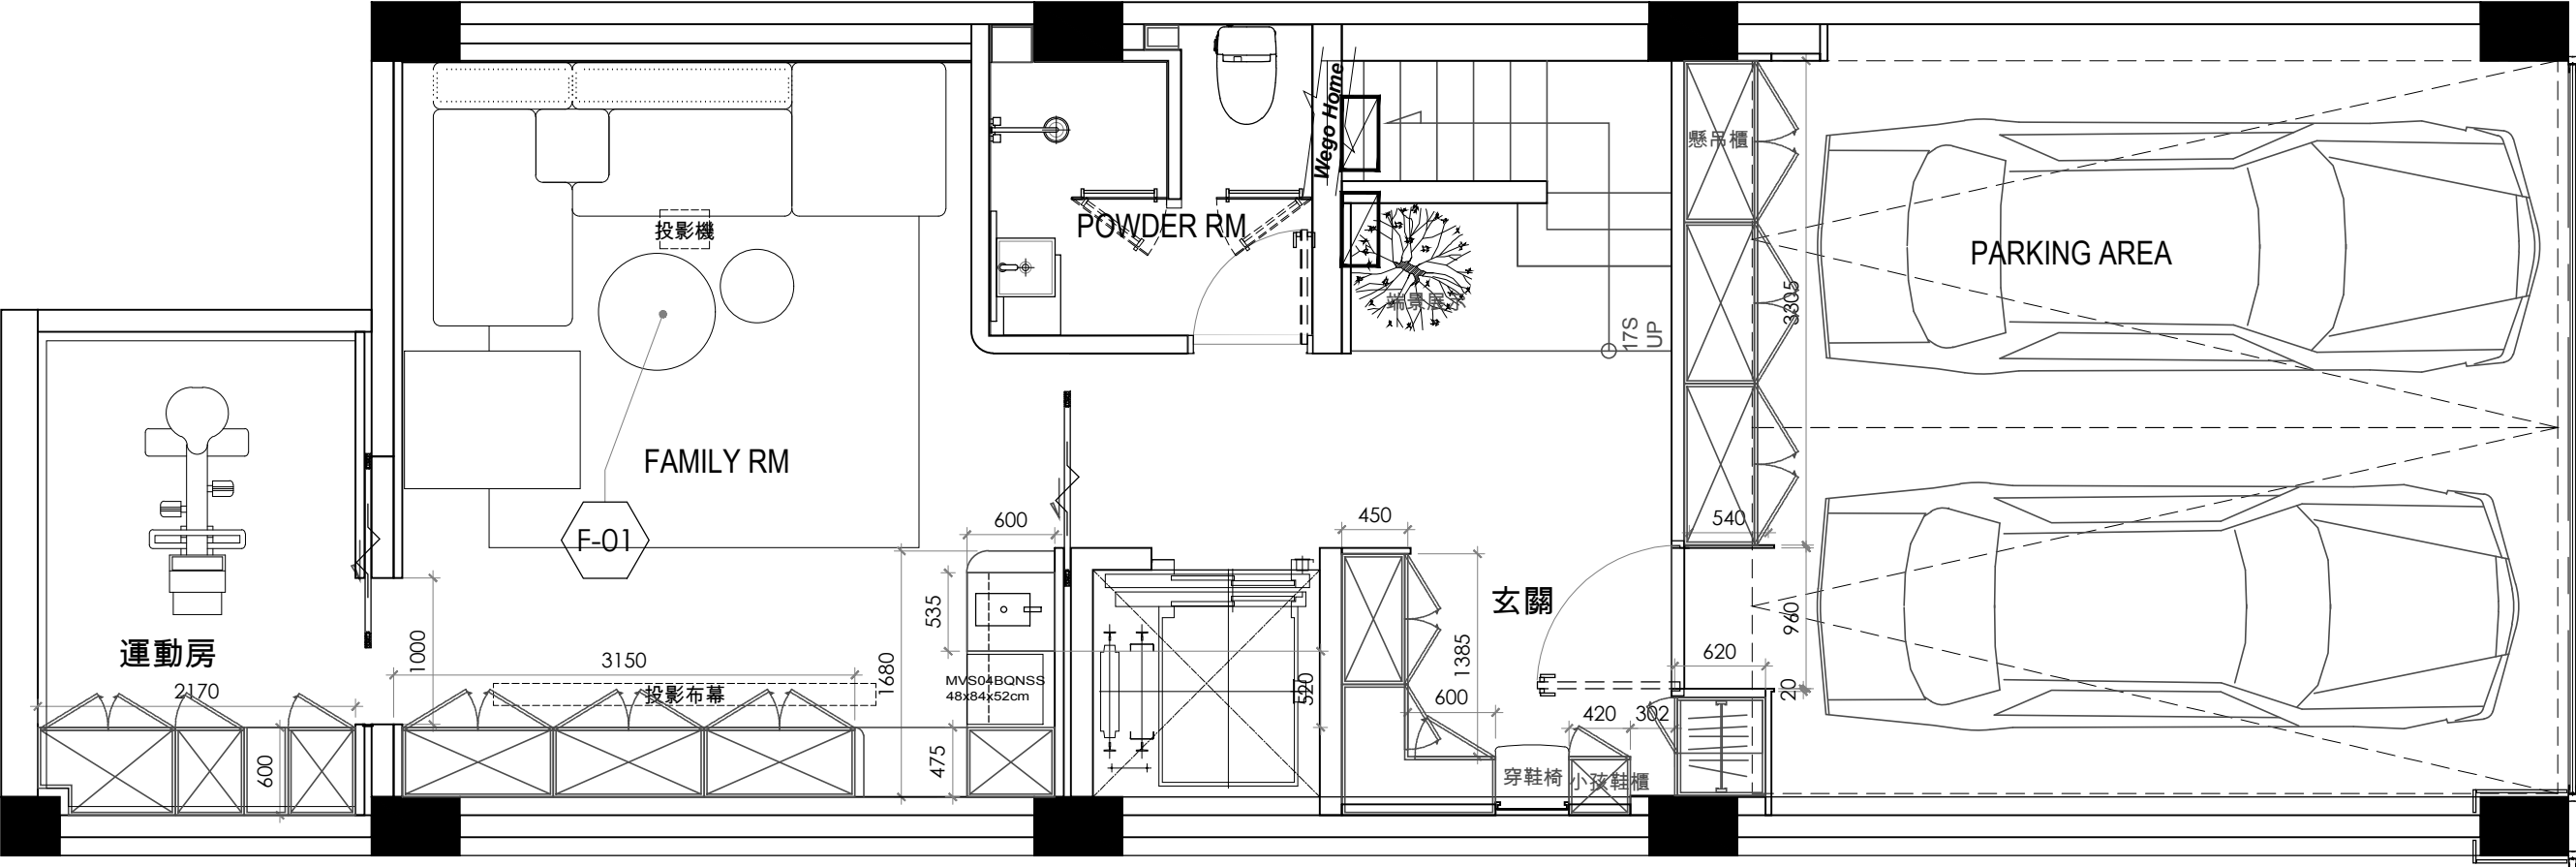


地下一層平面圖

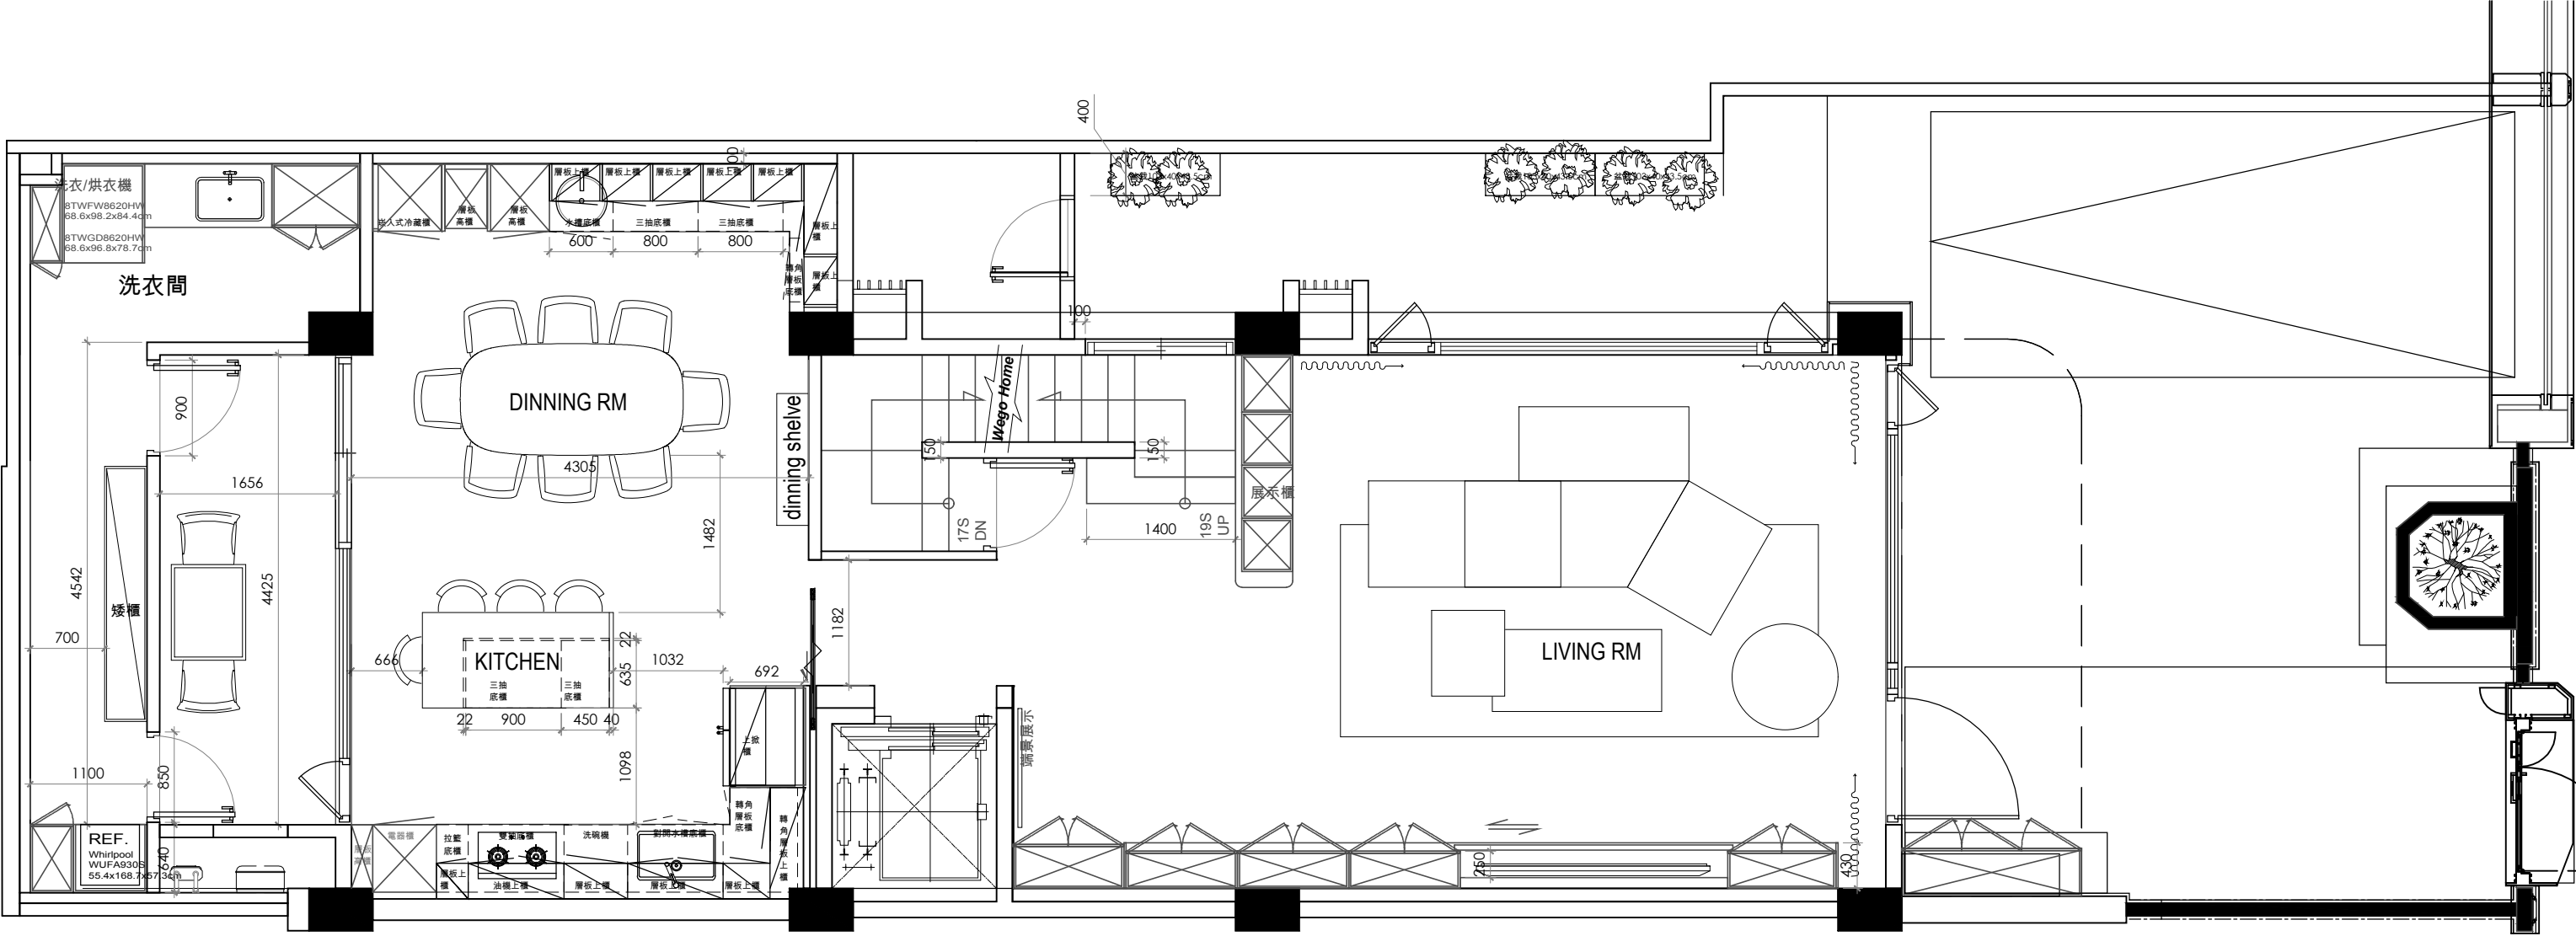


一層平面圖


牆 型 式	內 容	總 厚 度
	木作隔間牆	
	原有建築牆	154mm
	1/2B磚牆	120mm
	65mmC型骨架+單面(12mm石膏板+9mm矽酸鈣板),單面(12mm石膏板+9mm矽酸鈣板)	100mm
	65mmC型骨架+雙面矽酸鈣板	85mm

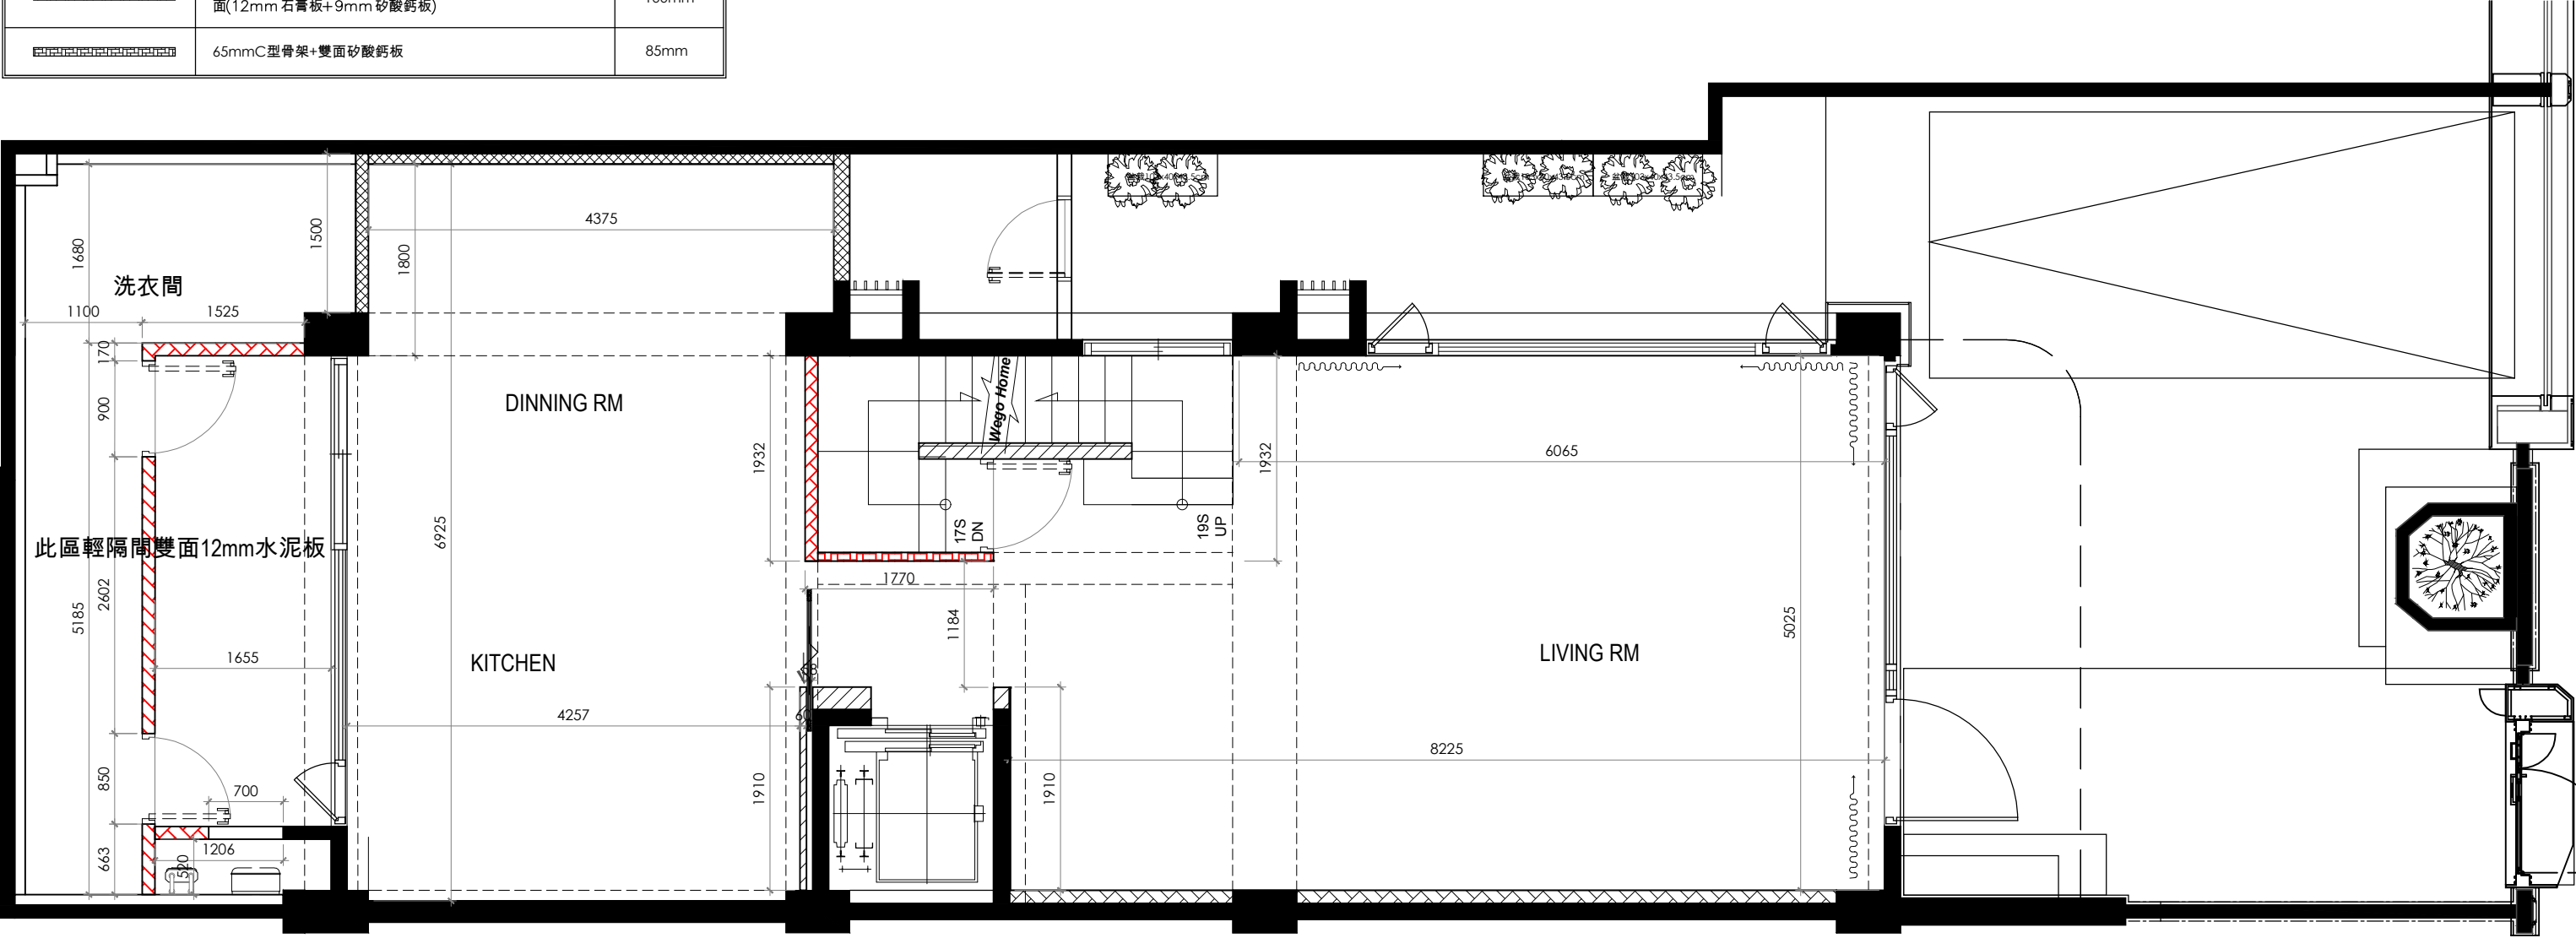

一層平面圖

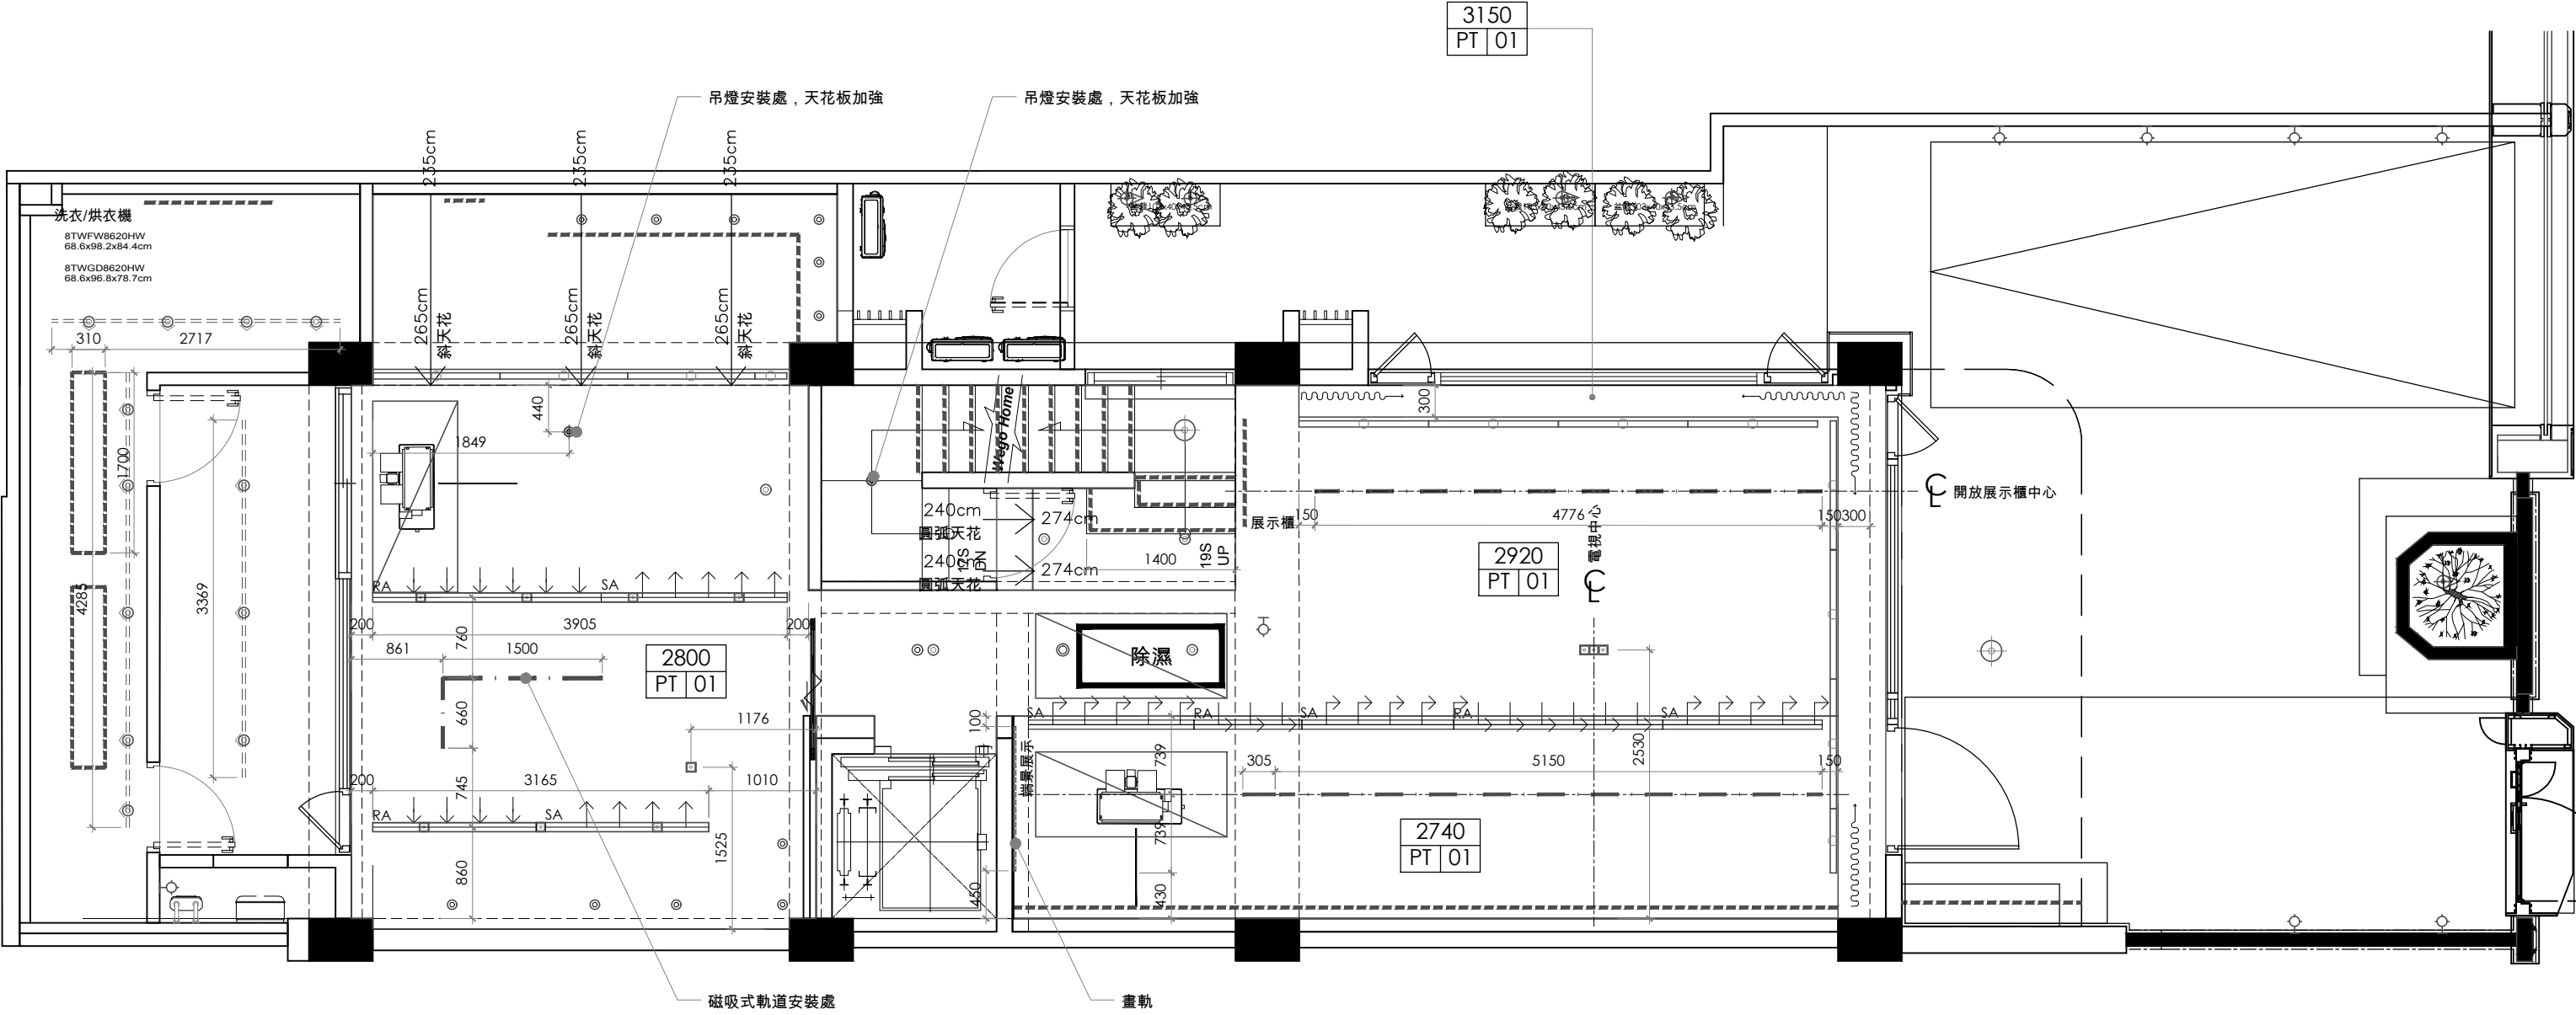


一層平面圖

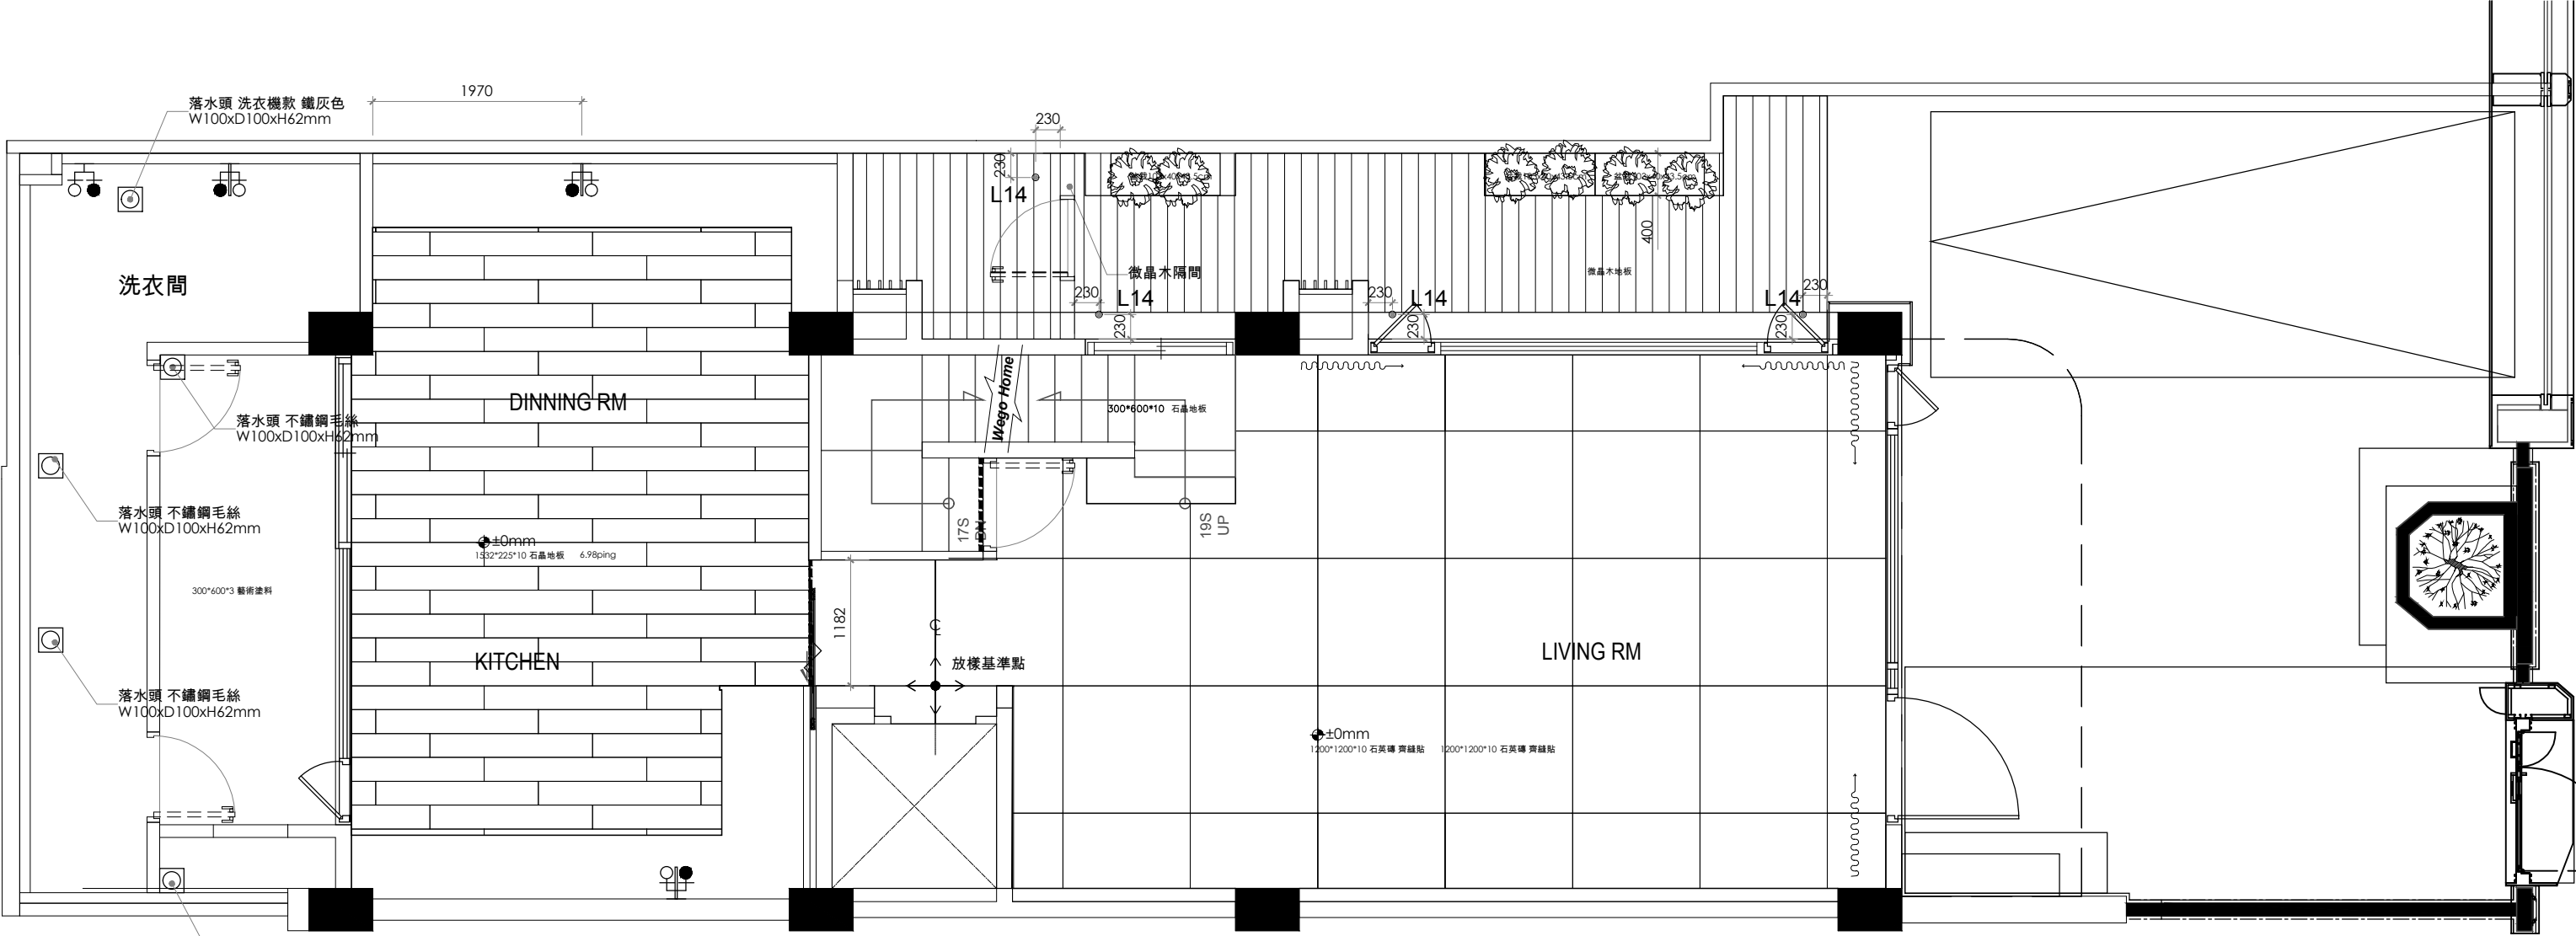

一層平面圖


編號	圖示	說明	尺寸	光源	備註
L1	●	舞光LED可調角度嵌燈	88mm Dia x H25mm	KW-303 / 8W / 3000k / 嵌孔75mm	
L2	●	2線式停電照明嵌燈	105mm Dia x H55mm	FH- 849-1B / 5W / 3000k / 嵌孔93mm	
L3	●	3線式停電照明嵌燈	105mm Dia x H55mm	FH- 849-1B / 5W / 3000k / 嵌孔93mm	
L4	⊕	LED 15W 小吸頂燈	82mm Dia x H78mm	3000k	
L5	●	舞光LED 邱比特軌道燈 白色	W88mm x L115mm x H50mm	AE-B07 / 7W / 3000k / 24°	
L6	●	超薄嵌入式感應式嵌燈	85mm Dia x H50mm	3000k / 嵌孔75mm	
L7	////	LED軟條燈		3000k	
L8	=====	軌道燈軌道	W34mm x H20mm		
L9	●	小型嵌燈	63mm Dia x H72mm	3000k / 嵌孔55mm	
L10	▣	無邊框可調角LED單燈盒燈	W99mm x L99mm x H85mm	FH- 829-11C /10W /30° / 3000K	
L11	▣	無邊框可調角LED雙燈盒燈	W99mm x L199mm x H85mm	FH- 829-12C /10W /30° / 3000K	
L12	— · — · —	磁吸式軌道燈			
L13	———	防塵防濕T5燈具			
L14	●	上照LED埋地燈	42mm Dia. x H90mm	LED /3W /12° /12V /3000K / 700mA	
DL-1	◆	吊燈			
DL-2	◇	壁燈			
*燈具相關設備,需詳燈具規範最後確認 *燈具供電皆為220V.					

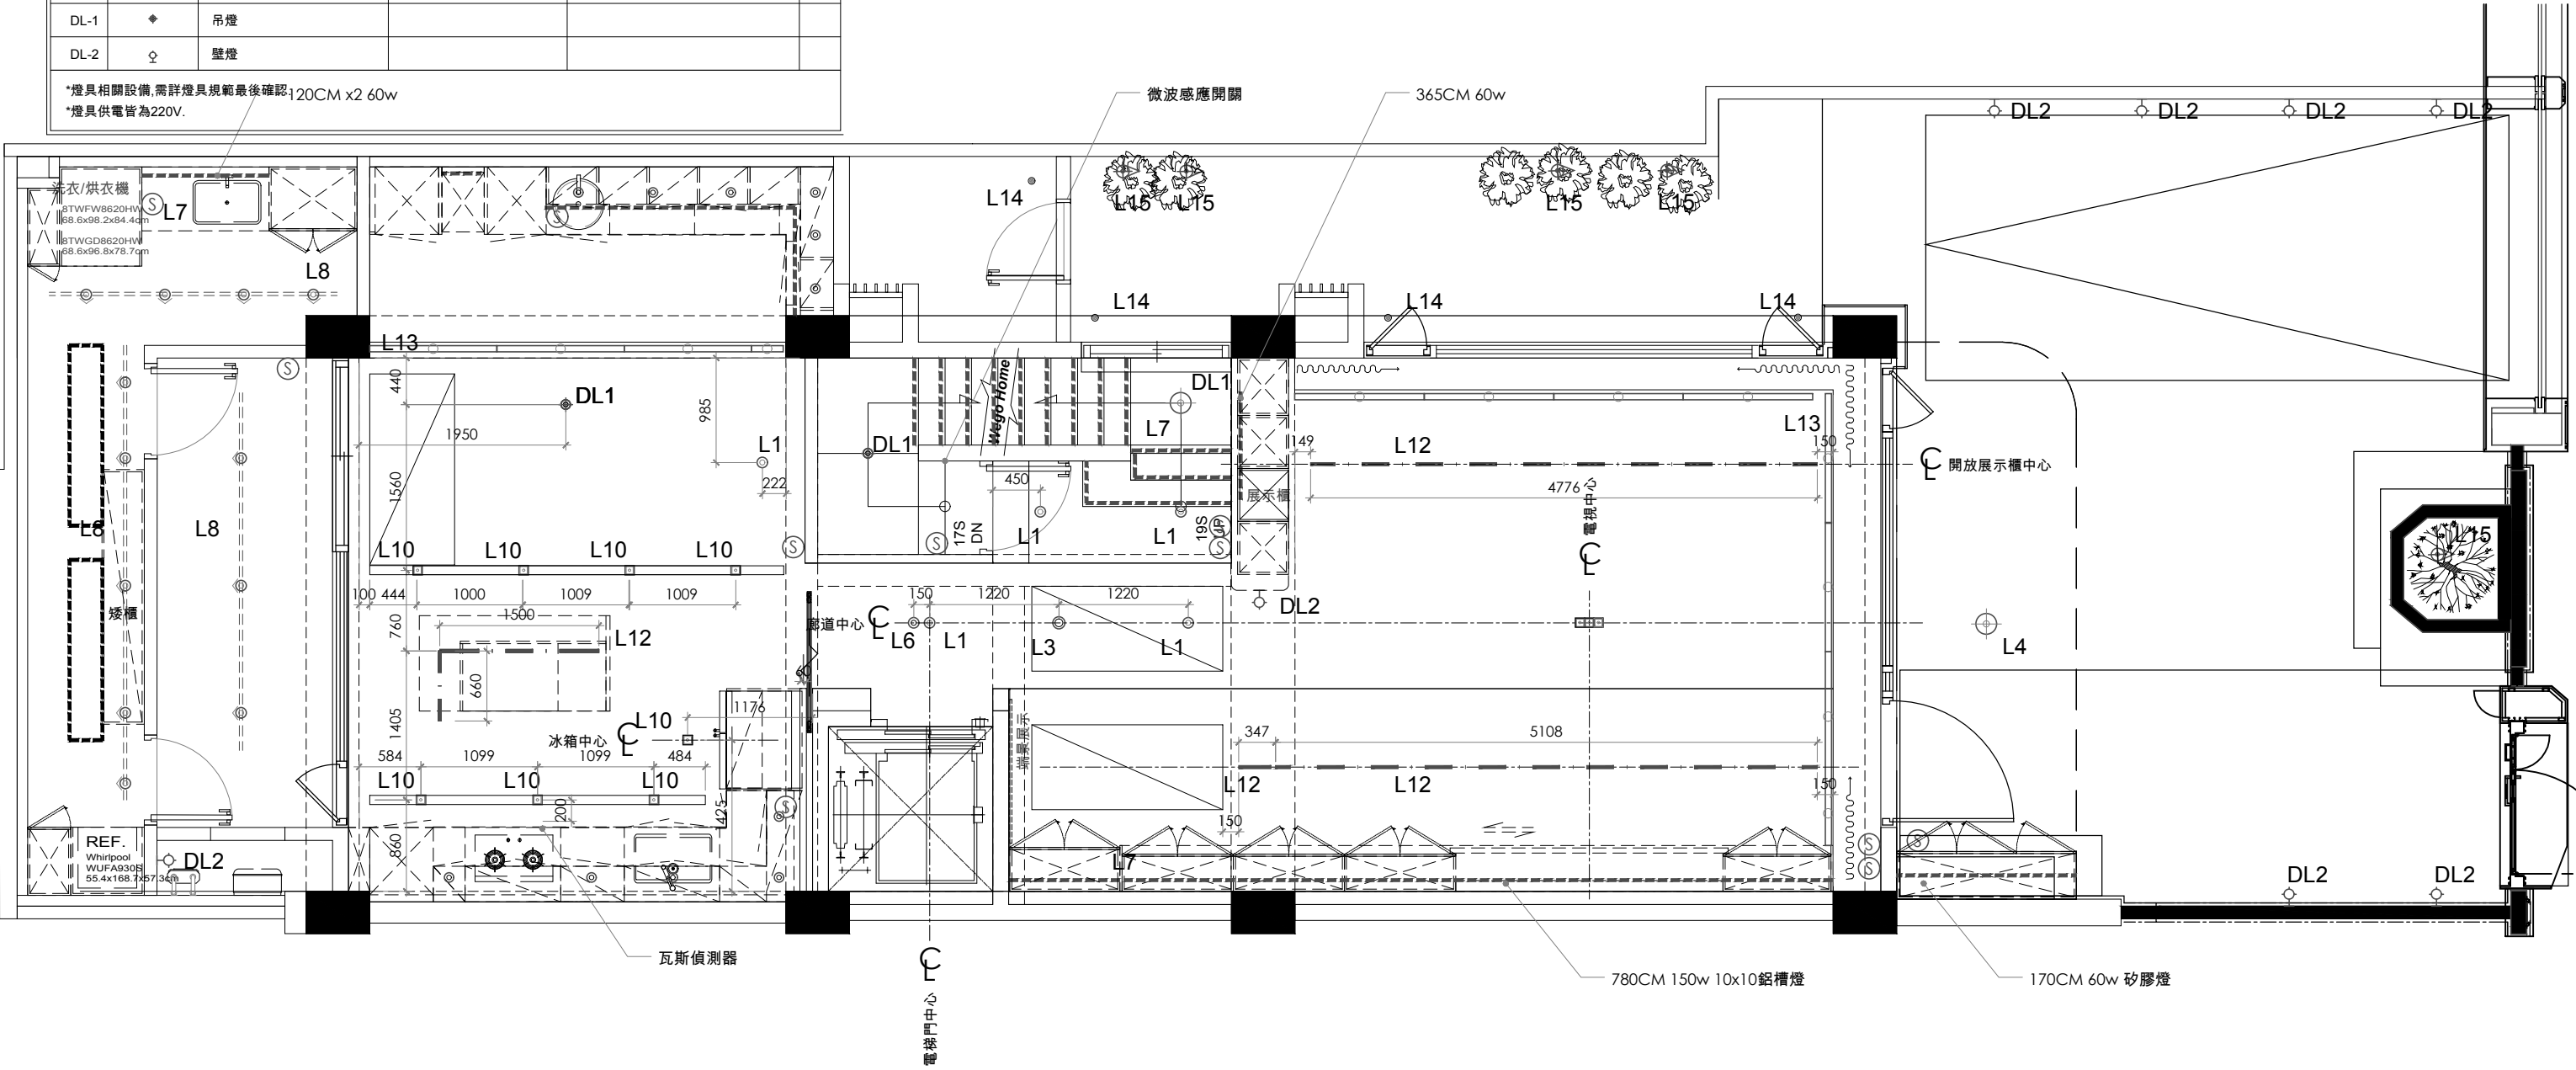

一層平面圖


弱電設備圖例說明					
圖 例	說 明	數 量	圖 例	說 明	數 量
	插座(110V雙插座)			HDMI插座	
	插座(220V雙插座)			音響出線	
	地板插座(110V雙插座)			電源出線口	
	不斷電插座(110V雙插座)			地板電源出線	
	獨立電源			空調開關	
	電話插座(大樓)			勿干擾顯示器,門鈴	
	掛壁式電話插座(內線)			對講機	
	電話插座(內線)			門上感應器(鈴聲)	
	大門陽極鎖控制按鈕			門禁刷卡器	
	電視插座			天花板鈴聲器	
	資訊插座			配電盤	
	燈具開關			消防箱	
	調光開關			緊急壓扣	
備註		1.插座,燈具出線口詳細位置尺寸,高度詳裝修圖。 2.所有壁面插座,除特別標示高度者之外,中心點一律離地完成面+300AFF。 3.所有壁面開關,除特別標示高度者之外,中心點一律離地完成面+1200AFF。 4.所有配管,線均由平頂天花配置。 5.影音視聽系統所需弱電設備,由影音視聽系統廠商規劃後,提供圖面予業主審核。			

給排水設備圖例說明表			
圖例	說 明	規格	高 度
	壁面冷給水		
	壁面熱給水		
	壁面冷熱給水		
	壁面冷熱給水及排水		
	地板排水口		
	糞管		
備註		1.淋浴間,蓮蓬頭出水口+2100AFF。 2.淋浴間,蓮蓬頭出水口+2100AFF	

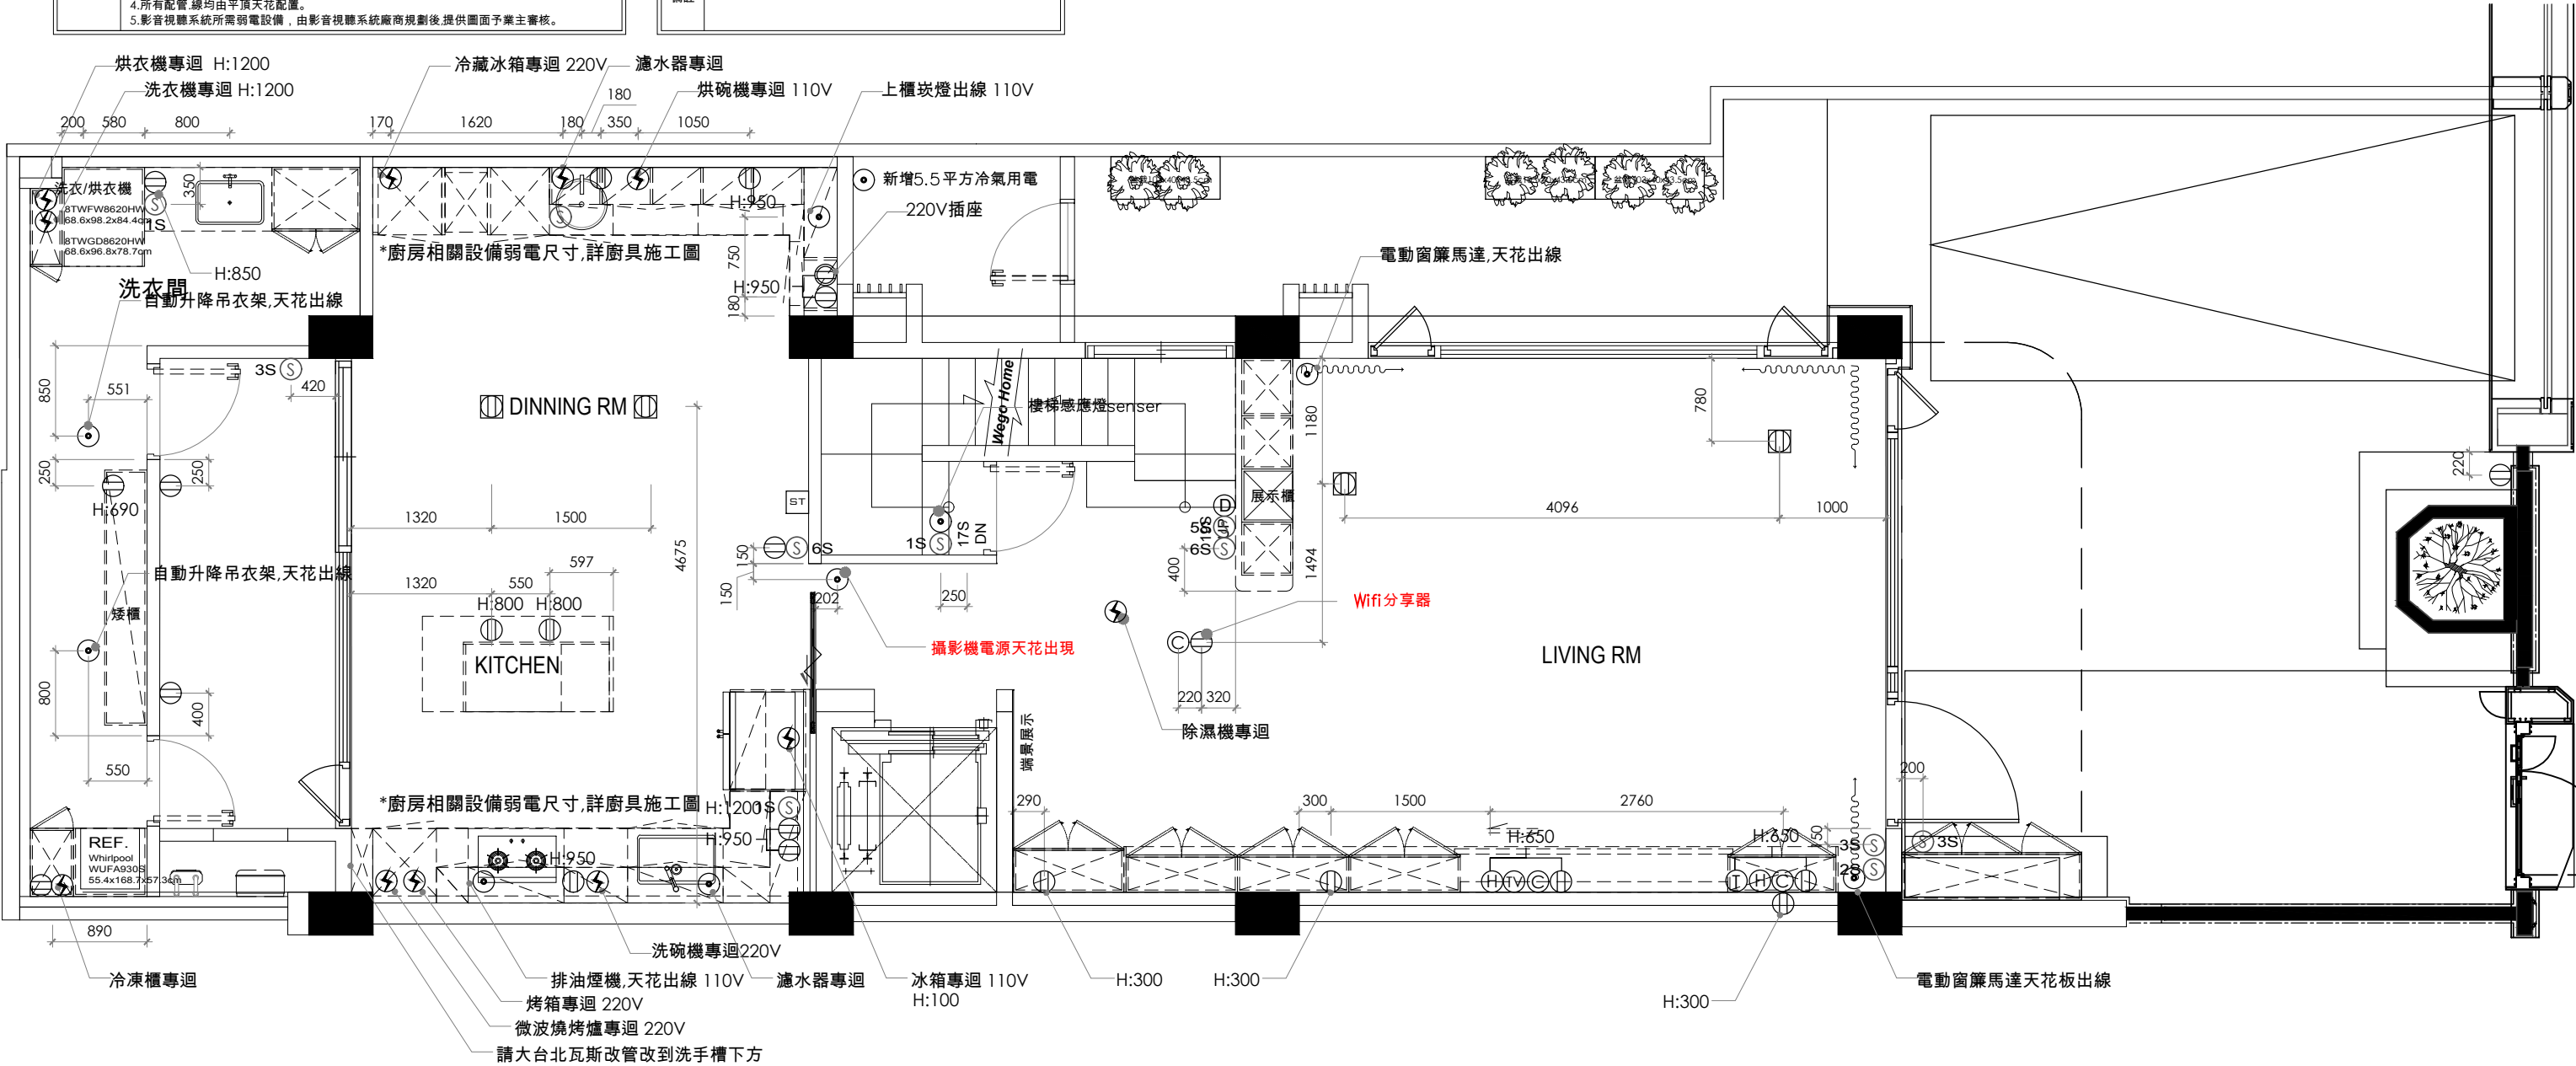

一層平面圖

編號	圖示	說明	尺寸	光源	備註
L1	●	舞光LED可調角度嵌燈	88mm Dia x H25mm	KW-303 / 8W / 3000k / 嵌孔75mm	
L2	●	2線式停電照明嵌燈	105mm Dia x H55mm	FH- 849-1B / 5W / 3000k / 嵌孔93mm	
L3	●	3線式停電照明嵌燈	105mm Dia x H55mm	FH- 849-1B / 5W / 3000k / 嵌孔93mm	
L4	⊕	LED 15W 小吸頂燈	82mm Dia x H78mm	3000k	
L5	●	舞光LED 邱比特軌道燈 白色	W88mm x L115mm x H50mm	AE-B07 / 7W / 3000k / 24°	
L6	●	超薄嵌入式感應式嵌燈	85mm Dia x H50mm	3000k / 嵌孔75mm	
L7	////	LED軟條燈		3000k	
L8	=====	軌道燈軌道	W34mm x H20mm		
L9	●	小型嵌燈	63mm Dia x H72mm	3000k / 嵌孔55mm	
L10	▣	無邊框可調角LED單燈盒燈	W99mm x L99mm x H85mm	FH- 829-11C /10W /30° / 3000K	
L11	▣	無邊框可調角LED雙燈盒燈	W99mm x L199mm x H85mm	FH- 829-12C /10W /30° / 3000K	
L12	- - - - -	磁吸式軌道燈			
L13	=====	防塵防濕T5燈具			
L14	●	上照LED埋地燈	42mm Dia. x H90mm	LED /3W /12° /12V /3000K / 700mA	
DL-1	◆	吊燈			
DL-2	◇	壁燈			
*燈具相關設備,需詳燈具規範最後確認 *燈具供電皆為220V.					

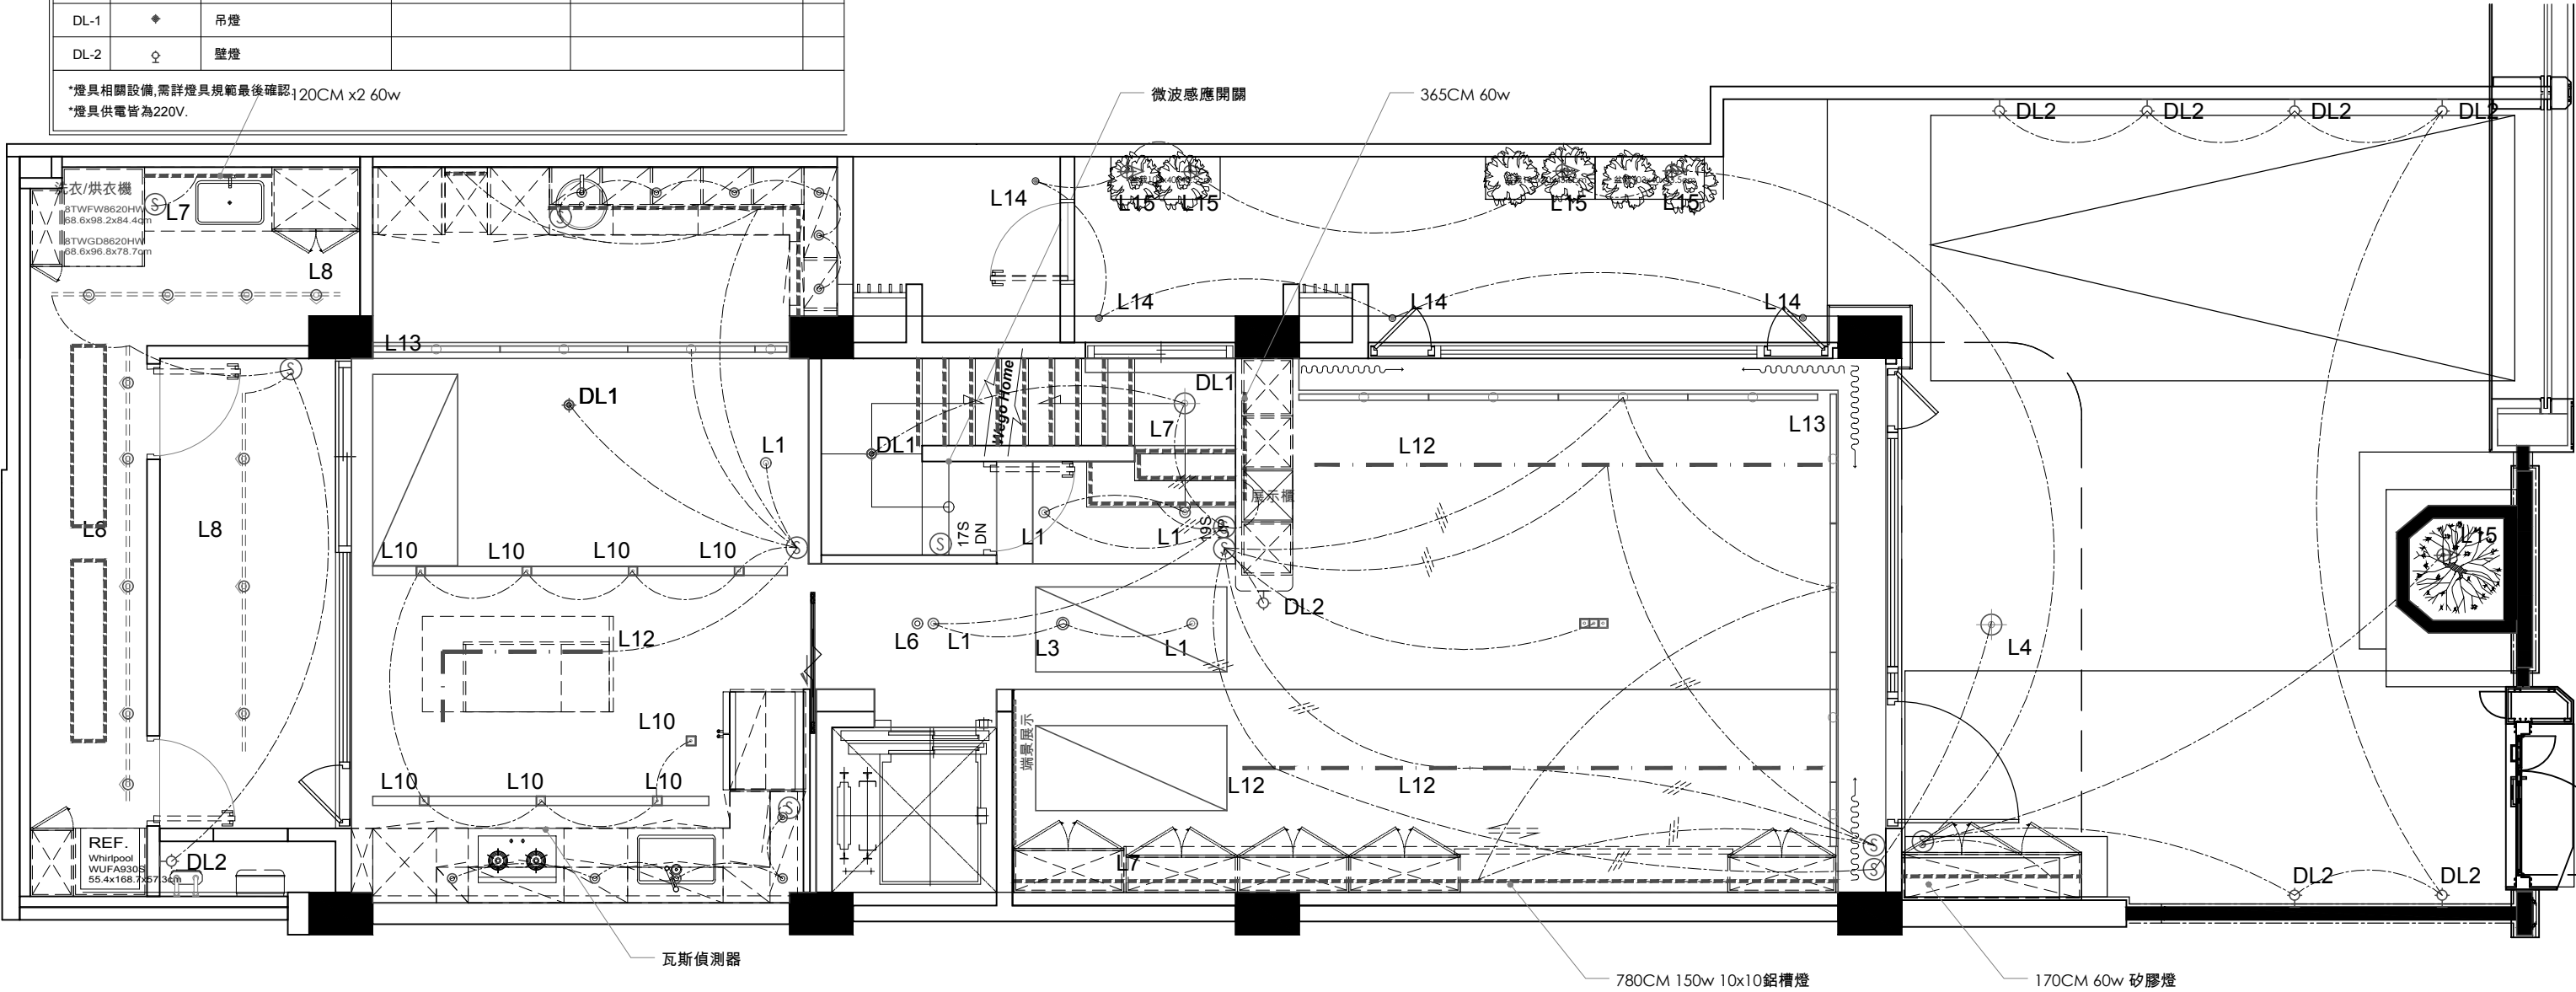


一層平面圖


編號	圖示	說明	尺寸	光源	備註
L1	⦿	舞光LED可調角度崁燈	88mm Dia x H25mm	KW-303 / 8W / 3000k / 崁孔75mm	
L2	⦿	2線式停電照明崁燈	105mm Dia x H55mm	FH- 849-1B / 5W / 3000k / 崁孔93mm	
L3	⦿	3線式停電照明崁燈	105mm Dia x H55mm	FH- 849-1B / 5W / 3000k / 崁孔93mm	
L4	⊕	LED 15W 小吸頂燈	82mm Dia x H78mm	3000k	
L5	⦿	舞光LED 邱比特軌道燈 白色	W88mm x L115mm x H50mm	AE-B07 / 7W / 3000k / 24°	
L6	⦿	超薄嵌入式感應式崁燈	85mm Dia x H50mm	3000k / 崁孔75mm	
L7	-----	LED軟條燈		3000k	
L8	-----	軌道燈軌道	W34mm x H20mm		
L9	●	小型崁燈	63mm Dia x H72mm	3000k / 崁孔55mm	
L10	▣	無邊框可調角LED單燈盒燈	W99mm x L99mm x H85mm	FH- 829-11C /10W /30° / 3000K	
L11	▣	無邊框可調角LED雙燈盒燈	W99mm x L199mm x H85mm	FH- 829-12C /10W /30° / 3000K	
L12	— · — · —	磁吸式軌道燈			
L13	— — — — —	防塵防濕T5燈具			
L14	●	上照LED埋地燈	42mm Dia. x H90mm	LED /3W /12° /12V /3000K / 700mA	
DL-1	◆	吊燈			
DL-2	◇	壁燈			

*燈具相關設備,需詳燈具規範最後確認。
*燈具供電皆為220V.


空調設備圖例說明			
圖例	說明	圖例	說明
	側吹出風口		出風口
	側吹回風口		吊隱式除濕主機
	下吹出風口		五合一暖風機
	下吹回風口		全熱交換器

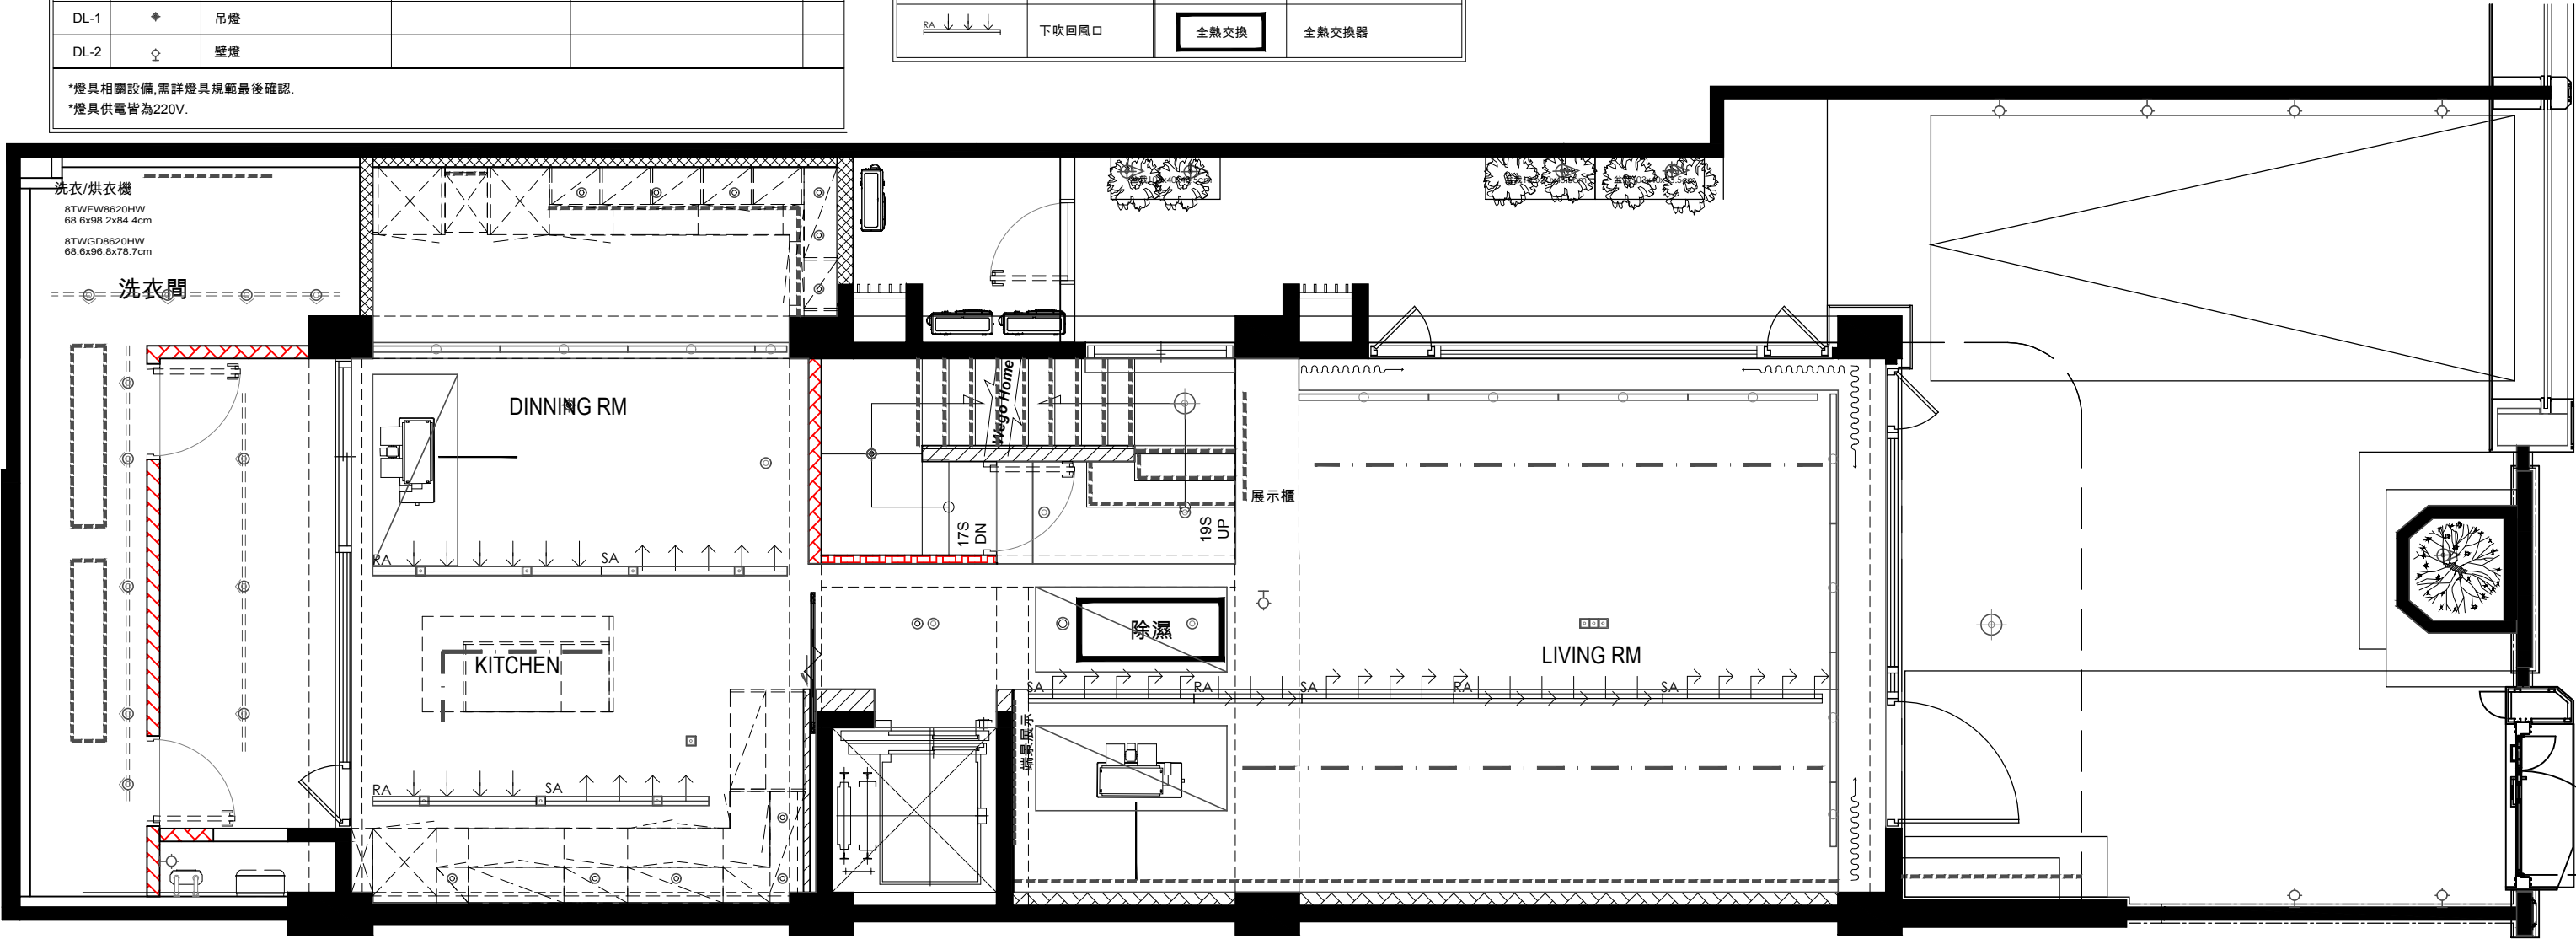


一層平面圖

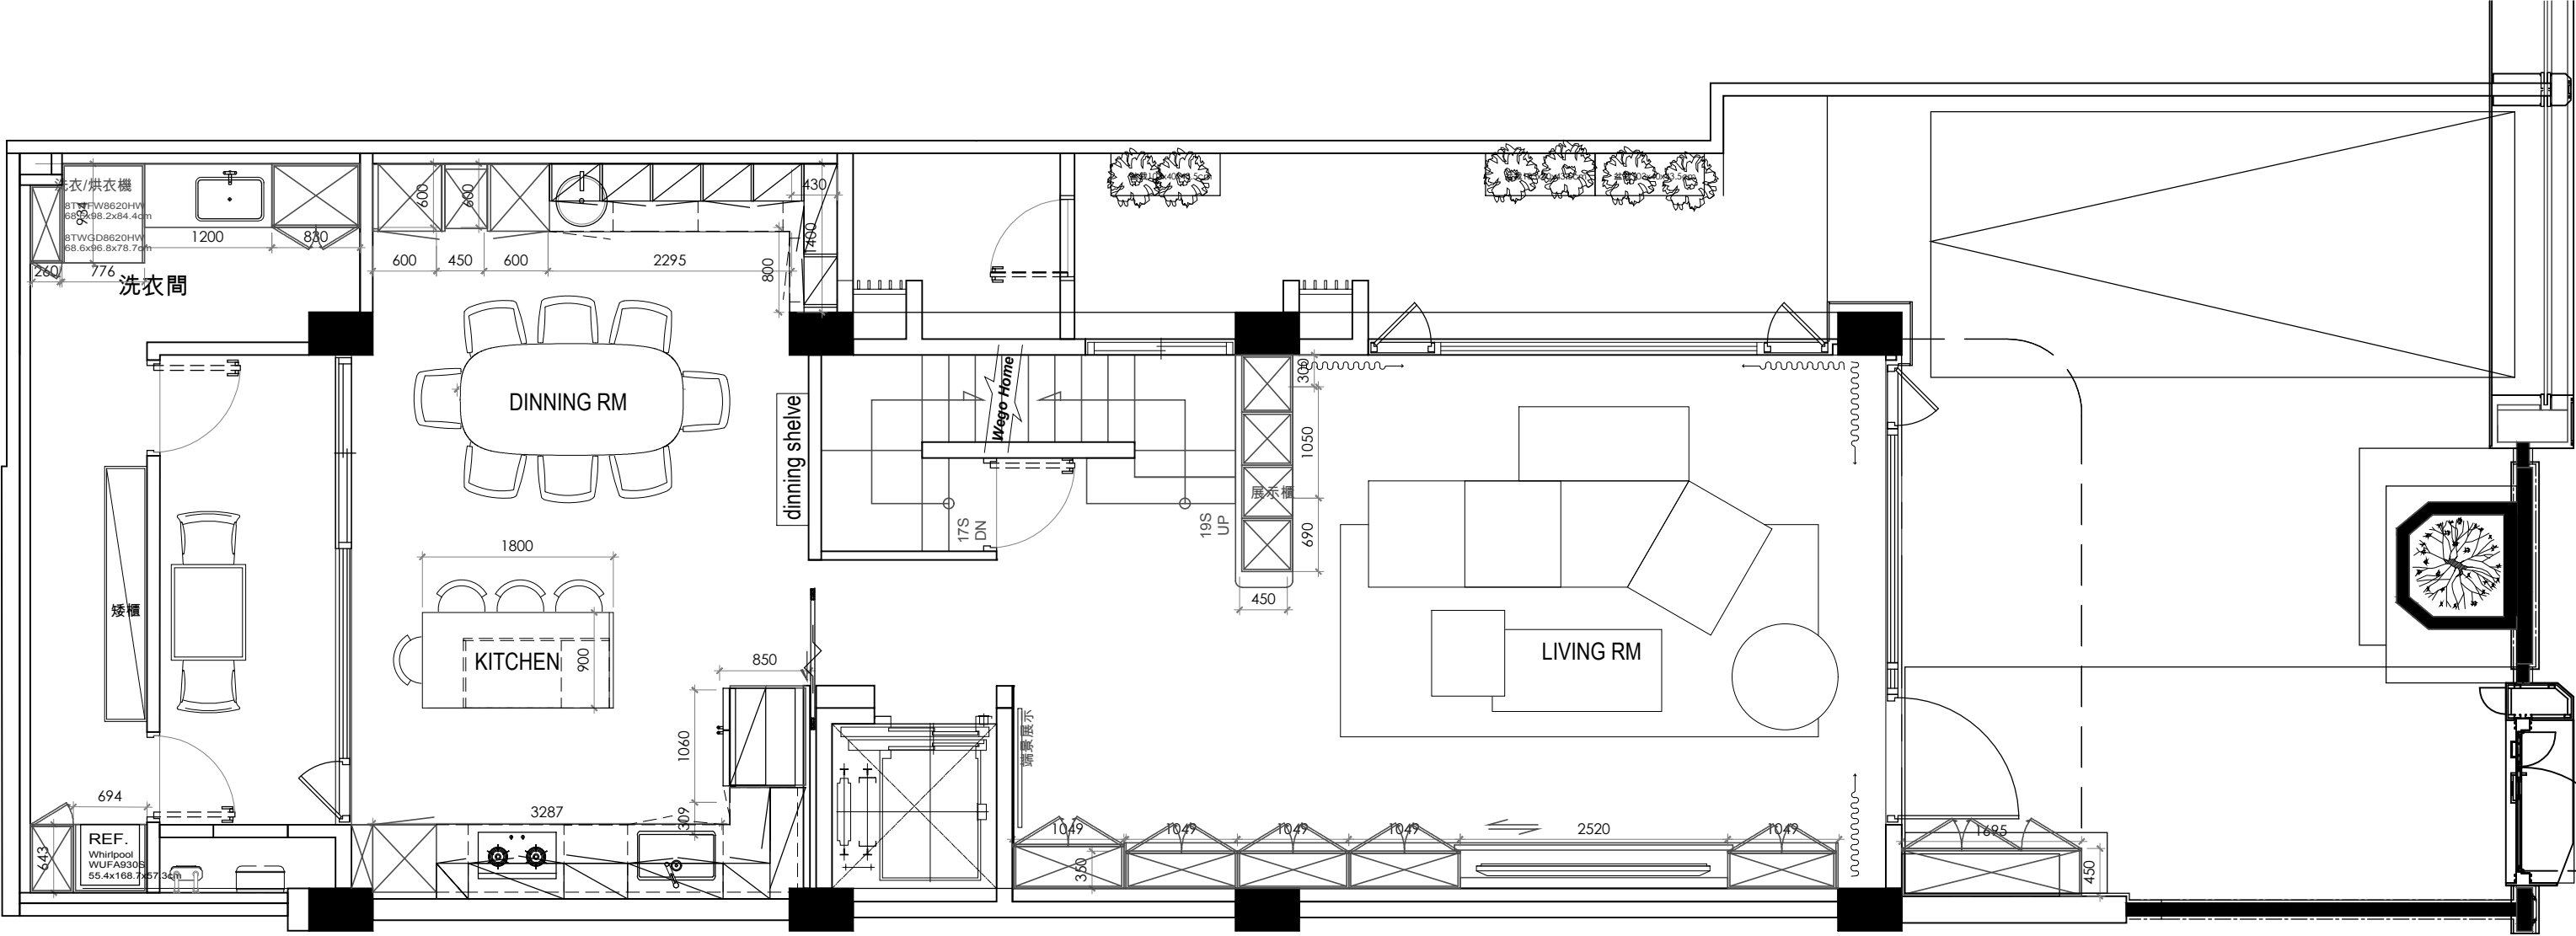


一層平面圖

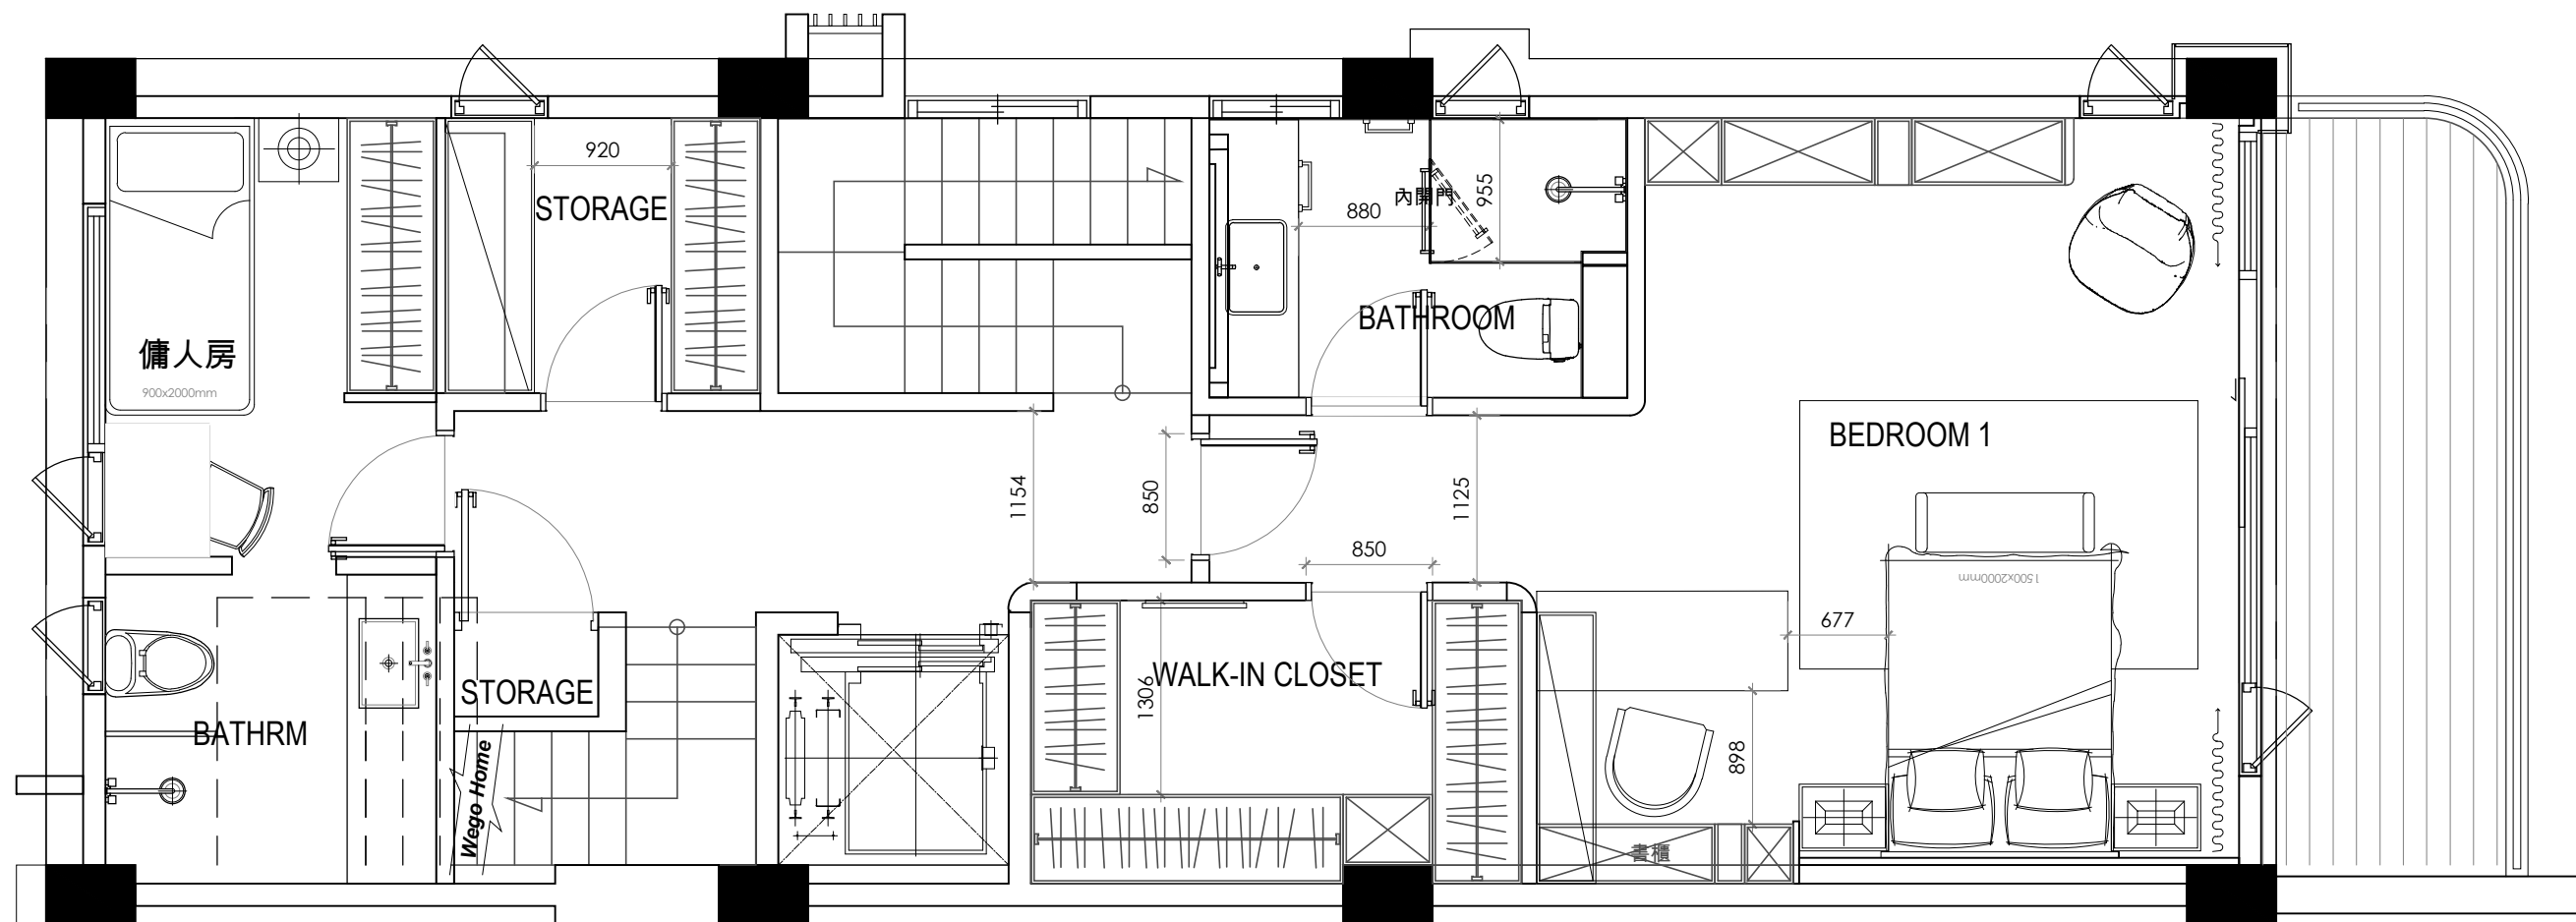


二層平面圖

 牆 型 式	內 容	總 厚 度
	木作隔間牆	
	原有建築牆	154mm
	1/2B磚牆	120mm
	65mmC型骨架+單面(12mm石膏板+9mm矽酸鈣板),單面(12mm石膏板+9mm矽酸鈣板)	100mm
	65mmC型骨架+雙面矽酸鈣板	85mm

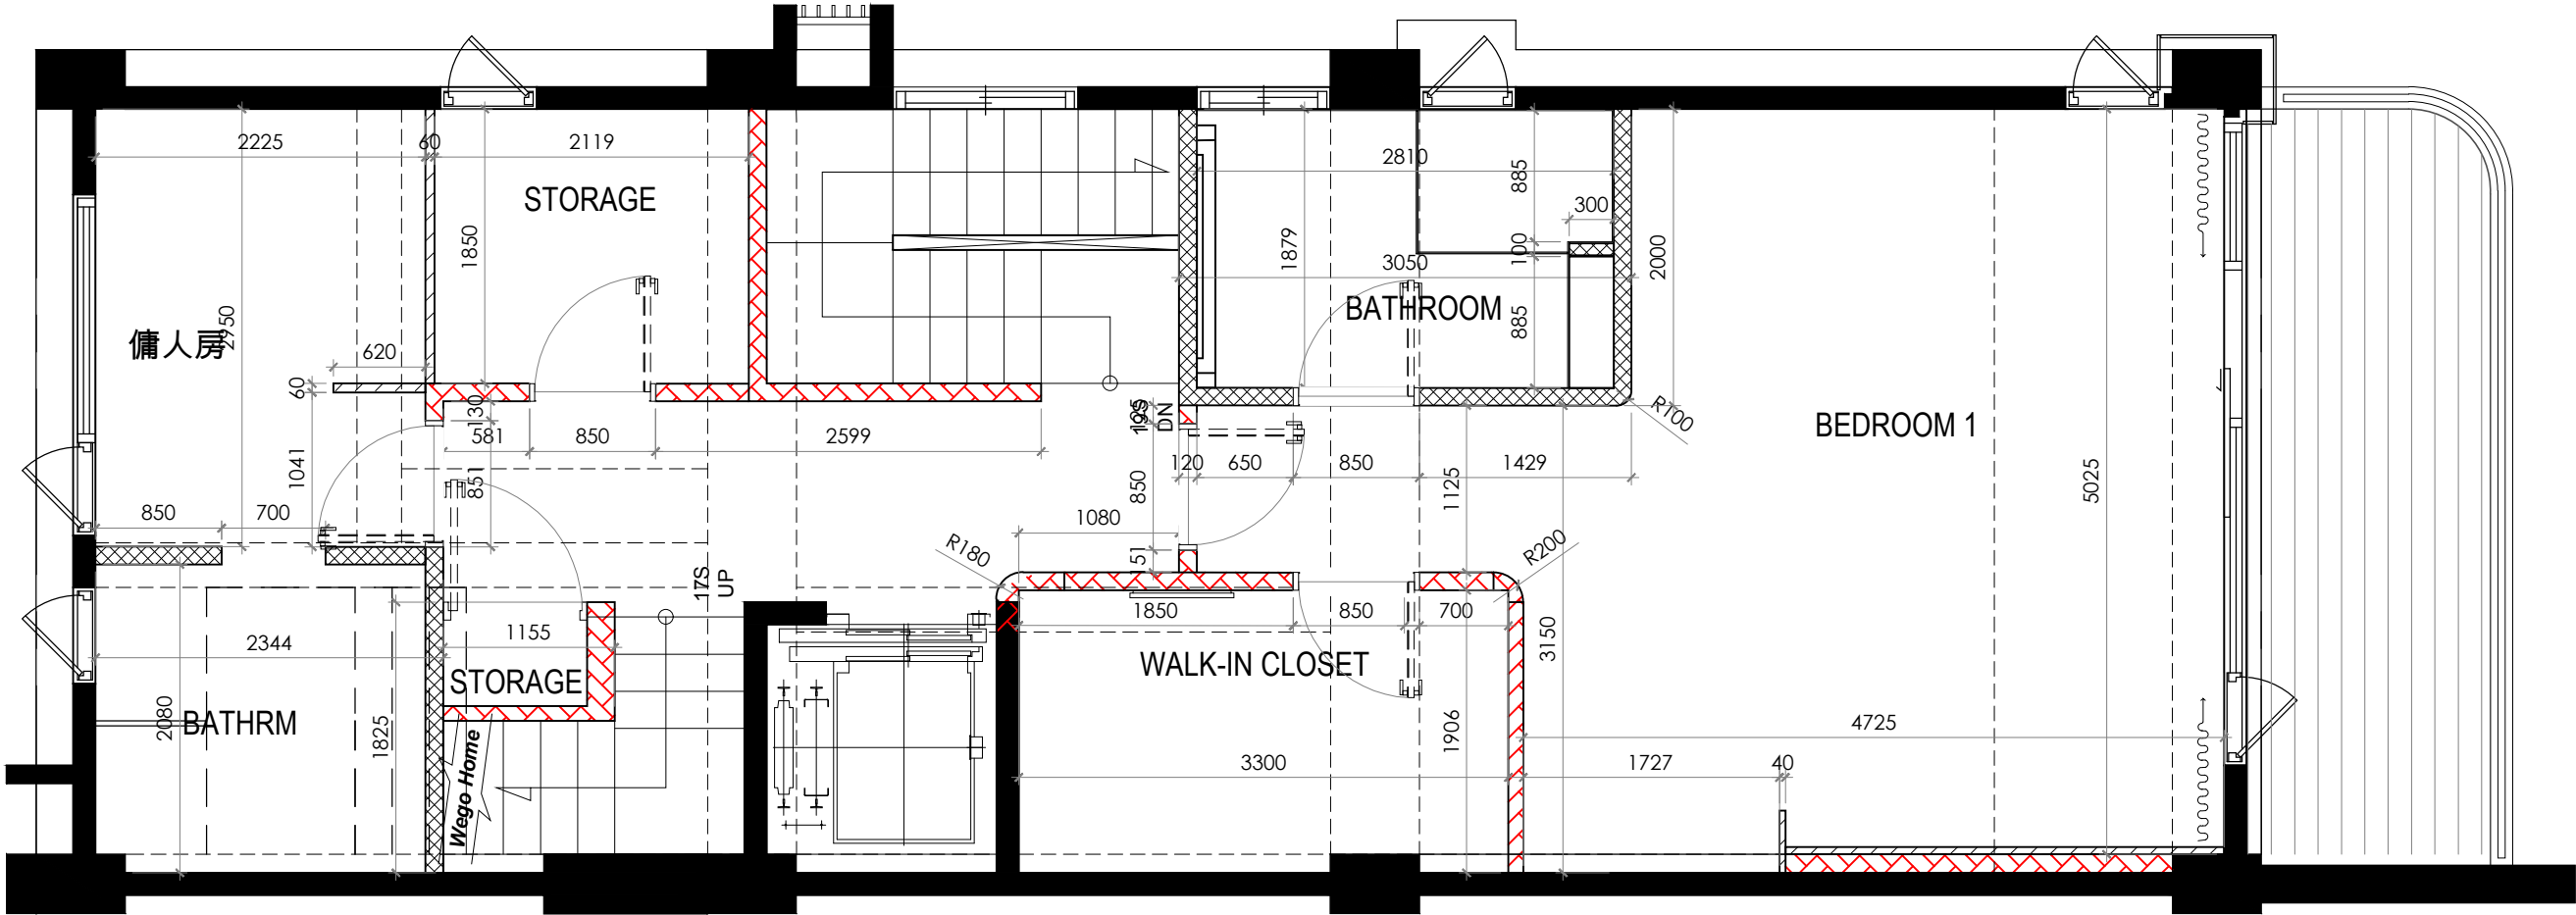


二層平面圖

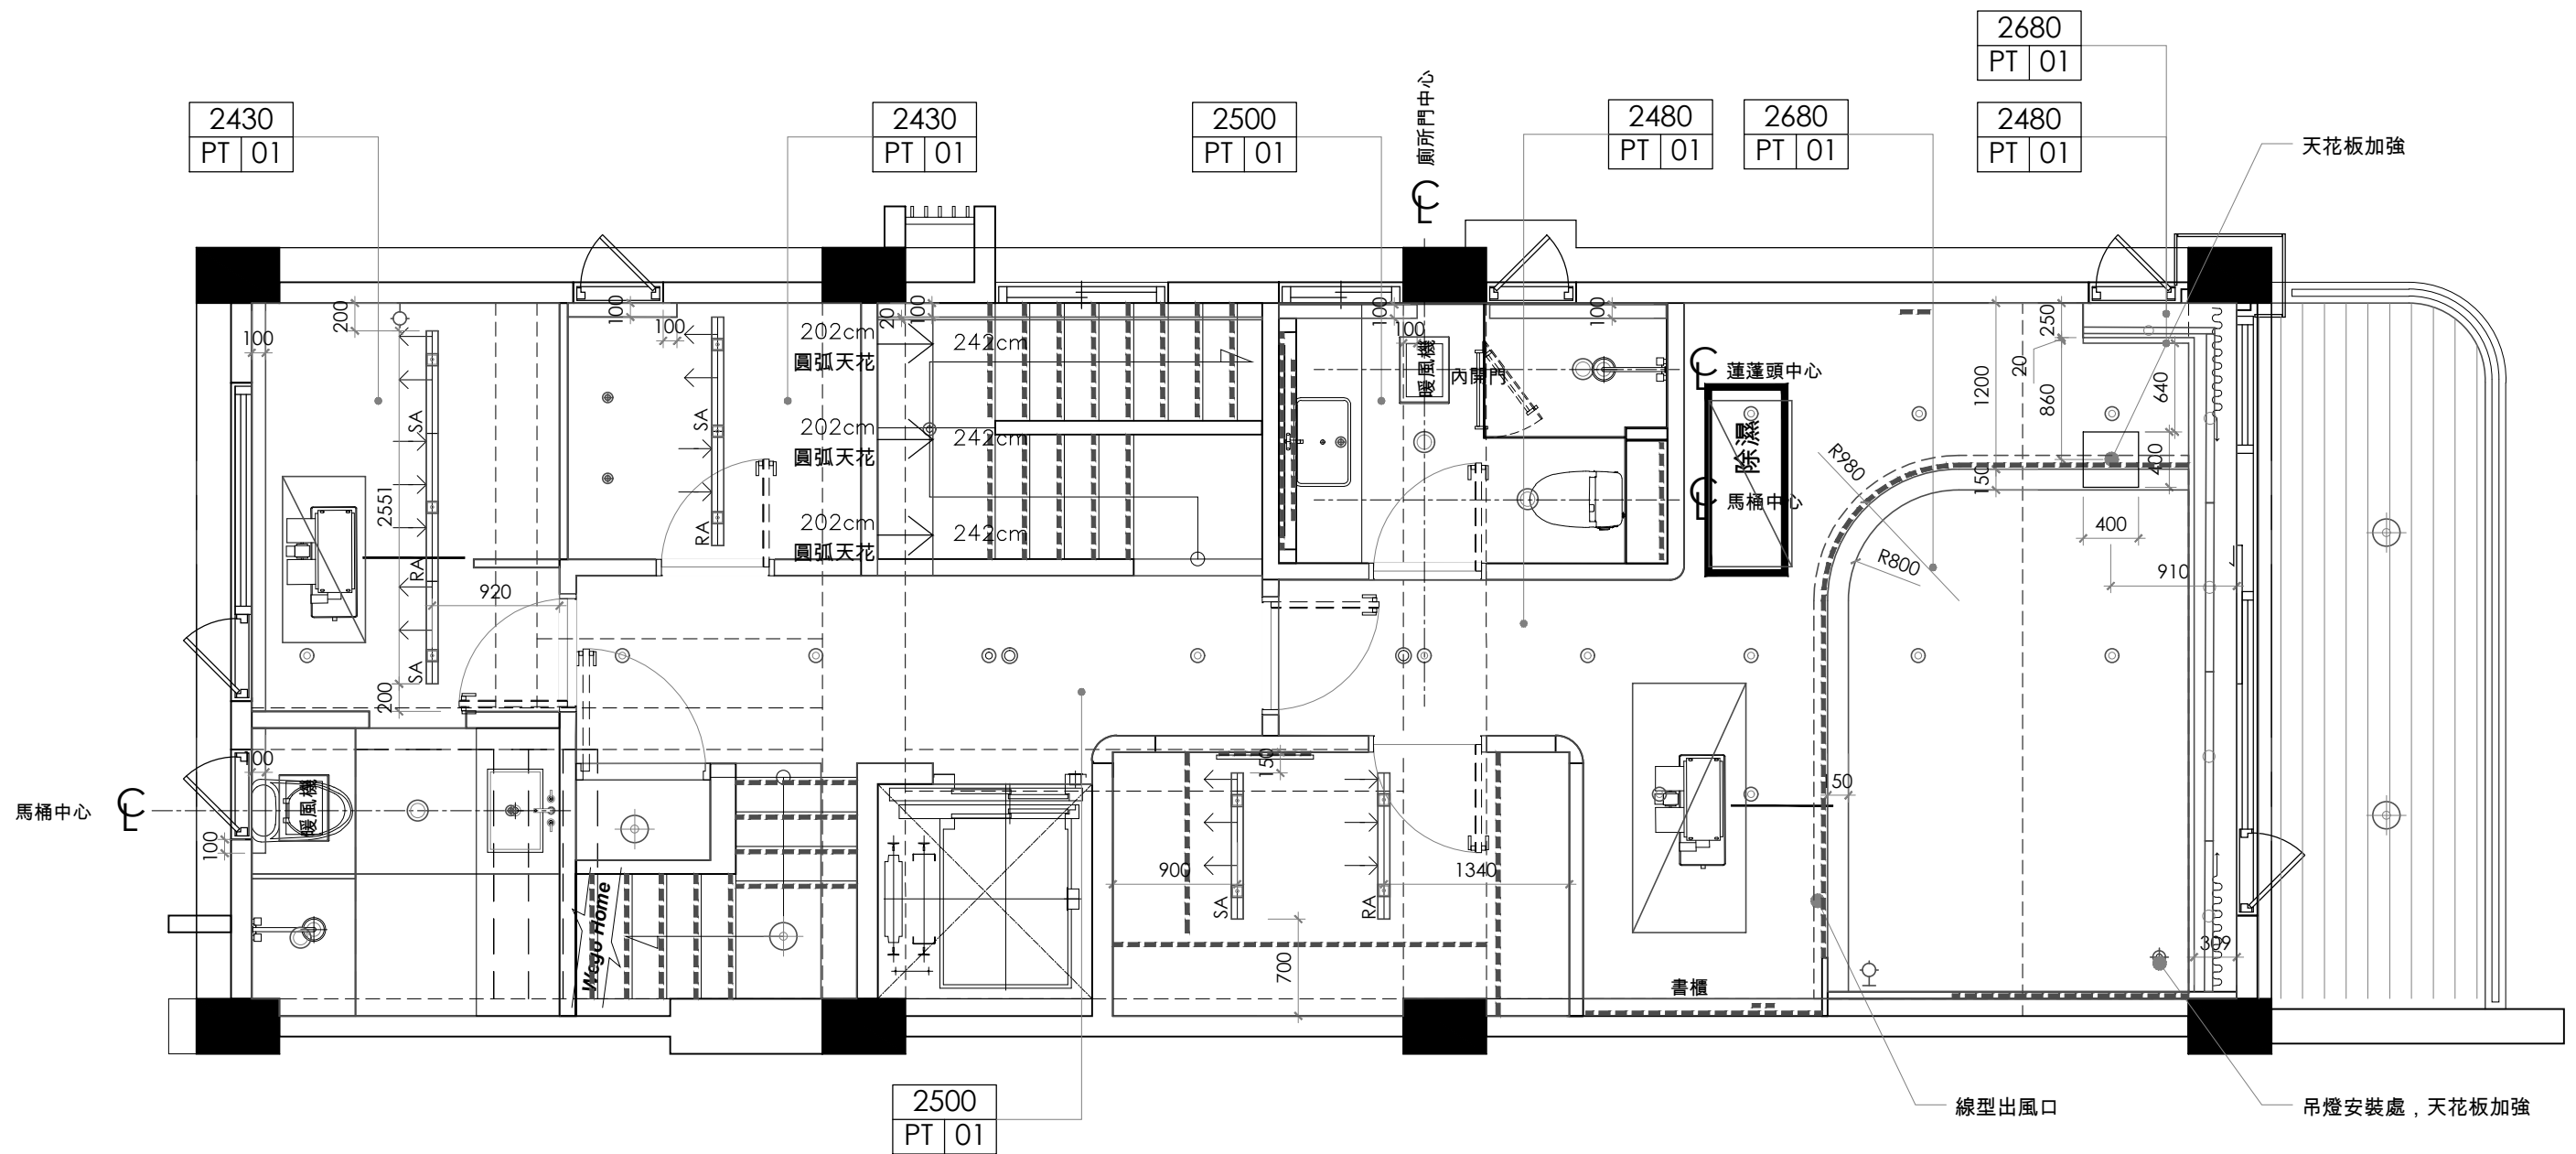

二層平面圖




*燈具相關設備,需詳燈具規範最後確認。
*燈具供電皆為220V。

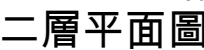






給排水設備圖例說明表			
圖例	說 明	規格	高 度
—○	壁面冷給水		
—●	壁面熱給水		
H●	壁面冷熱給水		
H●	壁面冷熱給水及排水		
□	地板排水口		
●	糞管		
備註			
1.淋浴間,蓮蓬頭出水口+2100AFF。 2.淋浴間,蓮蓬頭出水口+2100AFF			


弱電設備圖例說明					
圖 例	說 明	數 量	圖 例	說 明	數 量
⊖	插座(110V雙插座)		Ⓜ	HDMI插座	
⊖	插座(220V雙插座)		Ⓐ	音響出線	
Ⓜ	地板插座(110V雙插座)		⊙	電源出線口	
Ⓜ	不斷電插座(110V雙插座)		Ⓜ	地板電源出線	
⚡	獨立電源		Ⓜ	空調開關	
①	電話插座(大樓)		Ⓜ	勿干擾顯示器.門鈴	
⚠	掛壁式電話插座(內線)		BT	對講機	
①	電話插座(內線)		Ⓜ	門上感應器(鈴聲)	
Ⓜ	大門陽極鎖控制按鈕		Ⓜ	門禁刷卡器	
TV	電視插座		Ⓜ	天花板鈴聲器	
Ⓜ	資訊插座		Ⓜ	配電盤	
Ⓜ	燈具開關		Ⓜ	消防箱	
Ⓜ	調光開關		Ⓜ	緊急壓扣	
備註		1.插座,燈具出線口詳細位置尺寸,高度詳裝修圖。 2.所有壁面插座,除特別標示高度者之外,中心點一律離地完成面+300AFF。 3.所有壁面開關,除特別標示高度者之外,中心點一律離地完成面+1200AFF。 4.所有配管,線均由平頂天花配置。 5.影音視聽系統所需弱電設備,由影音視聽系統廠商規劃後,提供圖面予業主審核。			

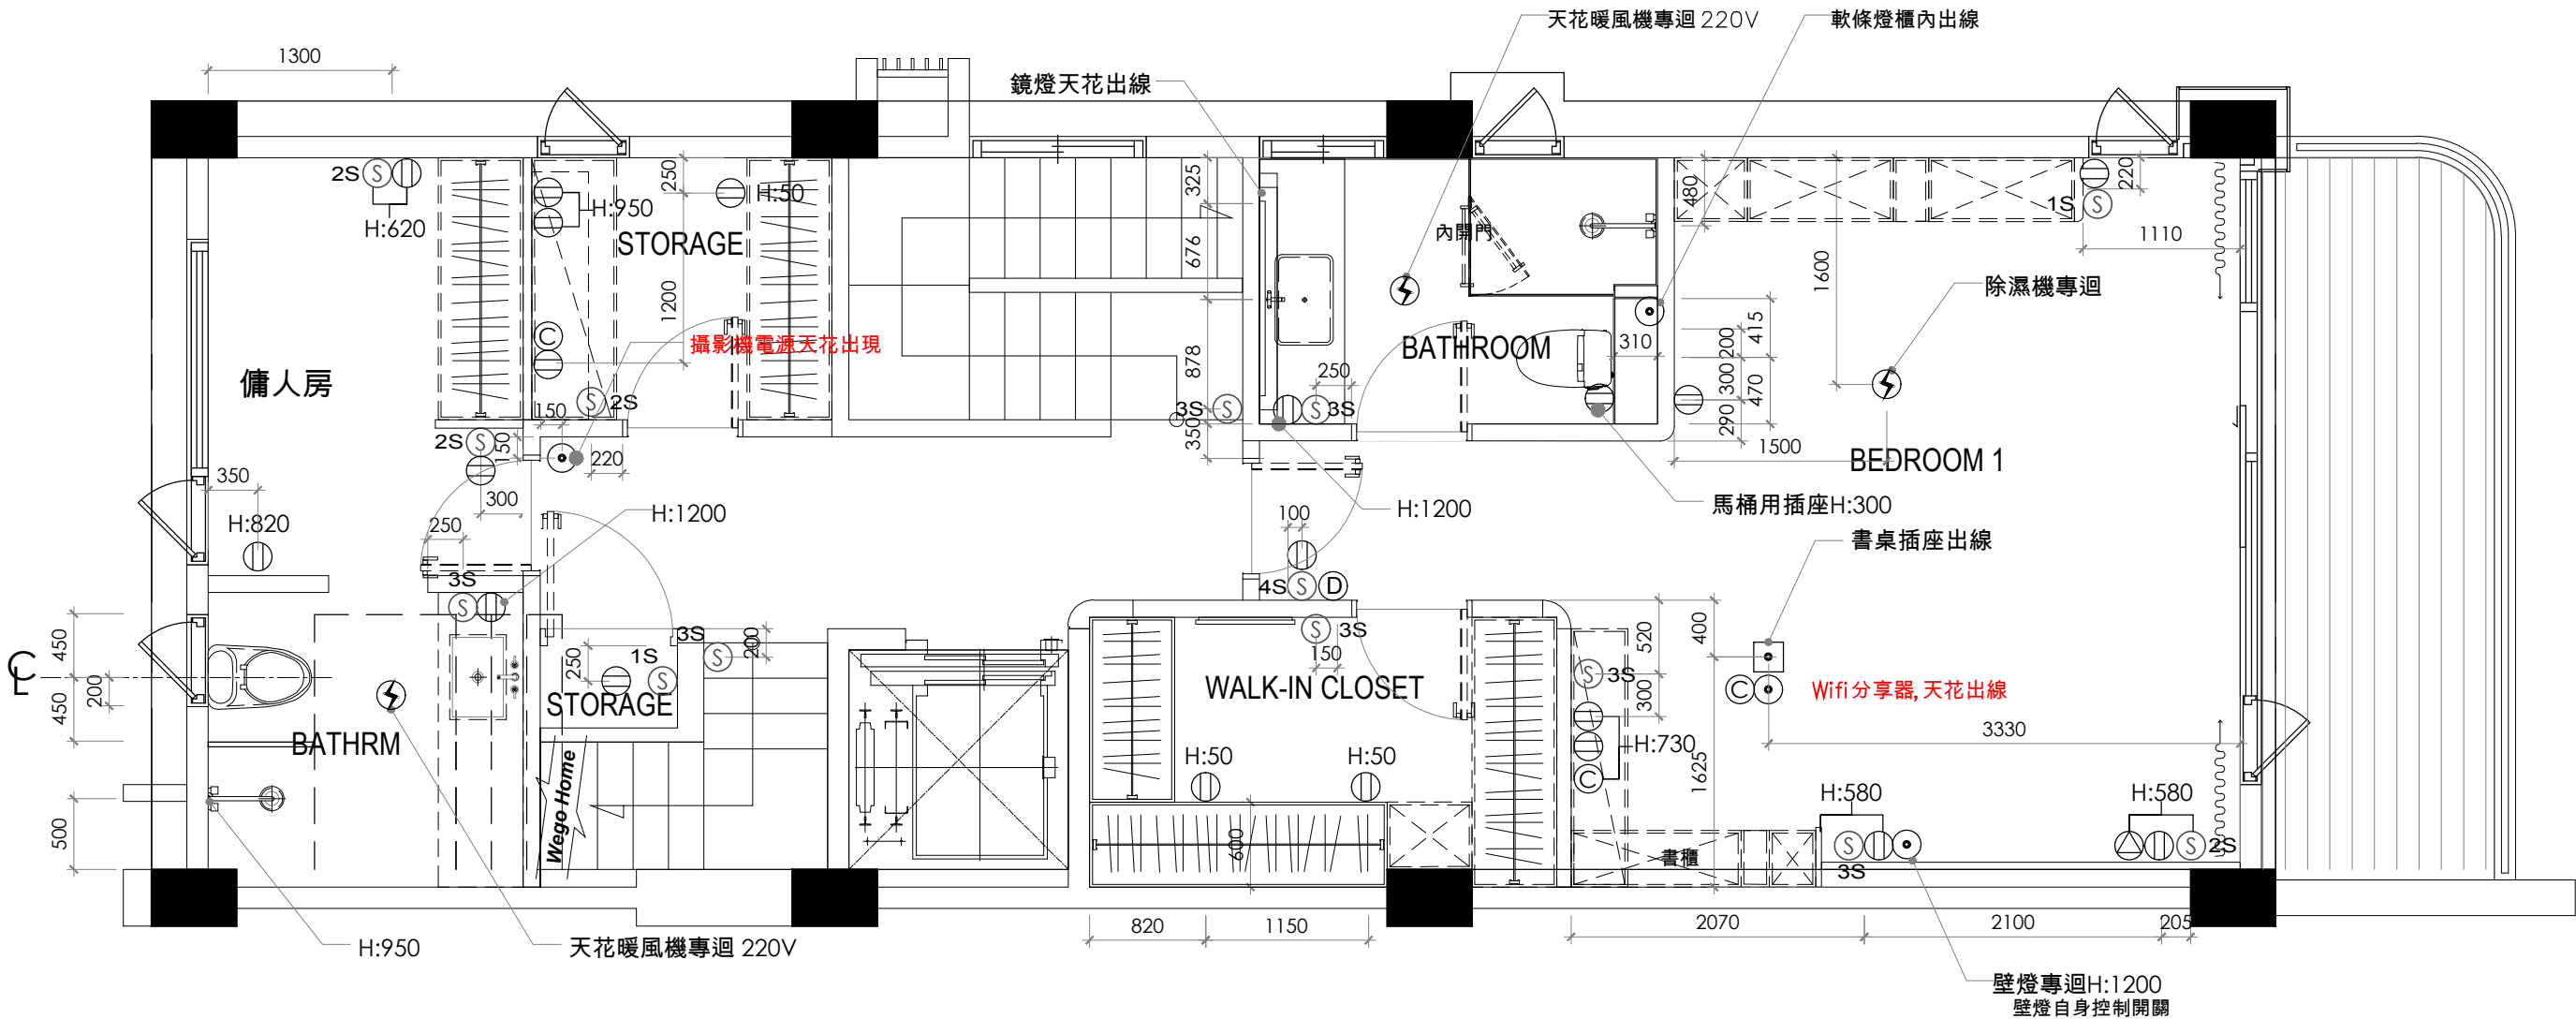


二層平面圖

編號	圖示	說明	尺寸	光源	備註
L1	●	舞光LED可調角度嵌燈	88mm Dia x H25mm	KW-303 / 8W / 3000k / 嵌孔75mm	
L2	●	2線式停電照明嵌燈	105mm Dia x H55mm	FH- 849-1B / 5W / 3000k / 嵌孔93mm	
L3	●	3線式停電照明嵌燈	105mm Dia x H55mm	FH- 849-1B / 5W / 3000k / 嵌孔93mm	
L4	⊕	LED 15W 小吸頂燈	82mm Dia x H78mm	3000k	
L5	●	舞光LED 邱比特軌道燈 白色	W88mm x L115mm x H50mm	AE-B07 / 7W / 3000k / 24°	
L6	●	超薄嵌入式感應式嵌燈	85mm Dia x H50mm	3000k / 嵌孔75mm	
L7	-----	LED軟條燈		3000k	
L8	=====	軌道燈軌道	W34mm x H20mm		
L9	●	小型嵌燈	63mm Dia x H72mm	3000k / 嵌孔55mm	
L10	■	無邊框可調角LED單燈盒燈	W99mm x L99mm x H85mm	FH- 829-11C /10W /30° / 3000K	
L11	■	無邊框可調角LED雙燈盒燈	W99mm x L199mm x H85mm	FH- 829-12C /10W /30° / 3000K	
L12	- · - · -	磁吸式軌道燈			
L13	—————	防塵防濕T5燈具			
L14	●	上照LED埋地燈	42mm Dia. x H90mm	LED /3W /12° /12V /3000K / 700mA	
DL-1	◆	吊燈			
DL-2	◇	壁燈			
*燈具相關設備,需詳燈具規範最後確認.					
*燈具供電皆為220V.					

 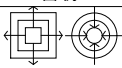  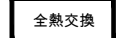
空調設備圖例說明			
圖 例	說 明	圖 例	說 明
	側吹出風口		出風口
	側吹回風口		吊隱式除濕主機
	下吹出風口		五合一暖風機
	下吹回風口		全熱交換器

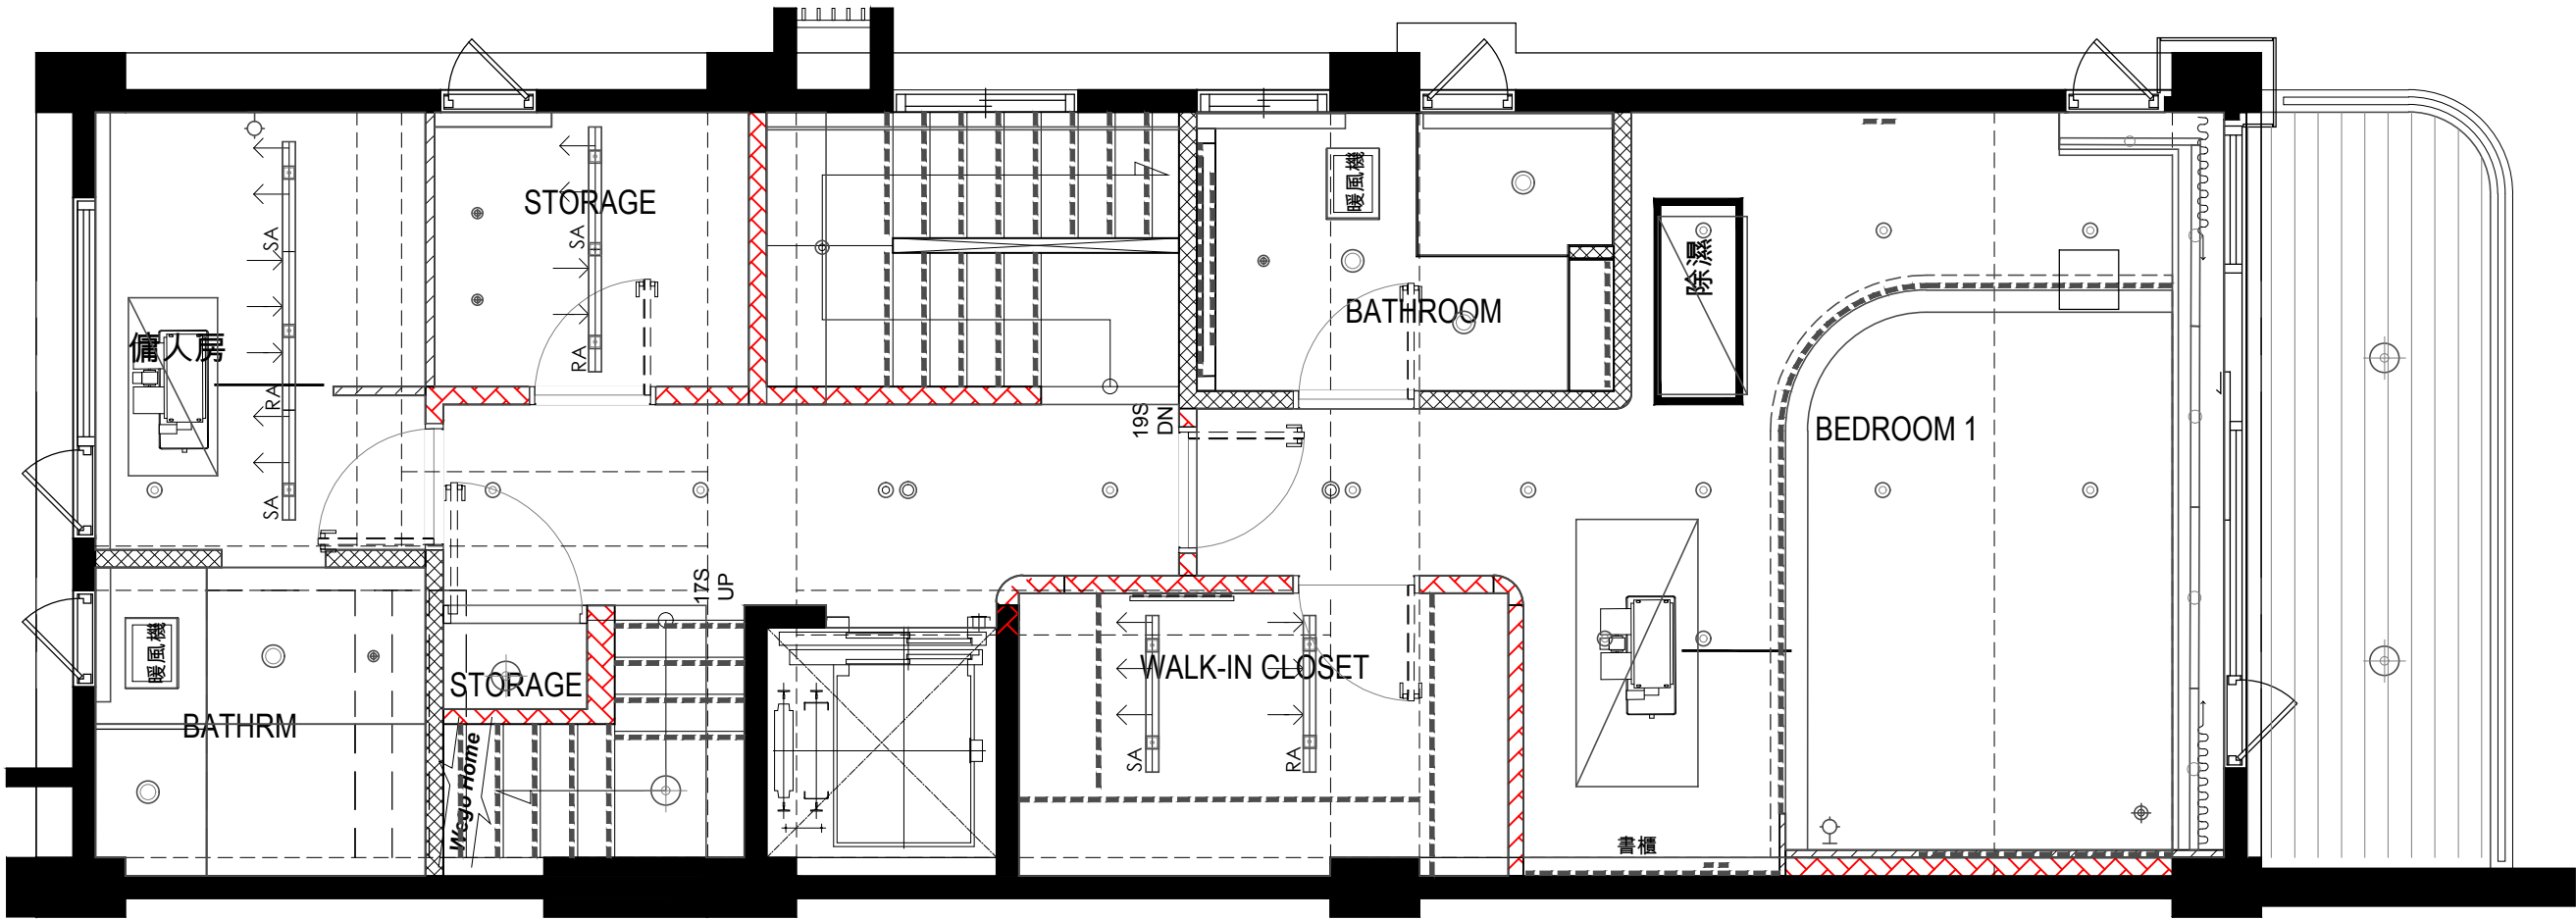



二層平面圖

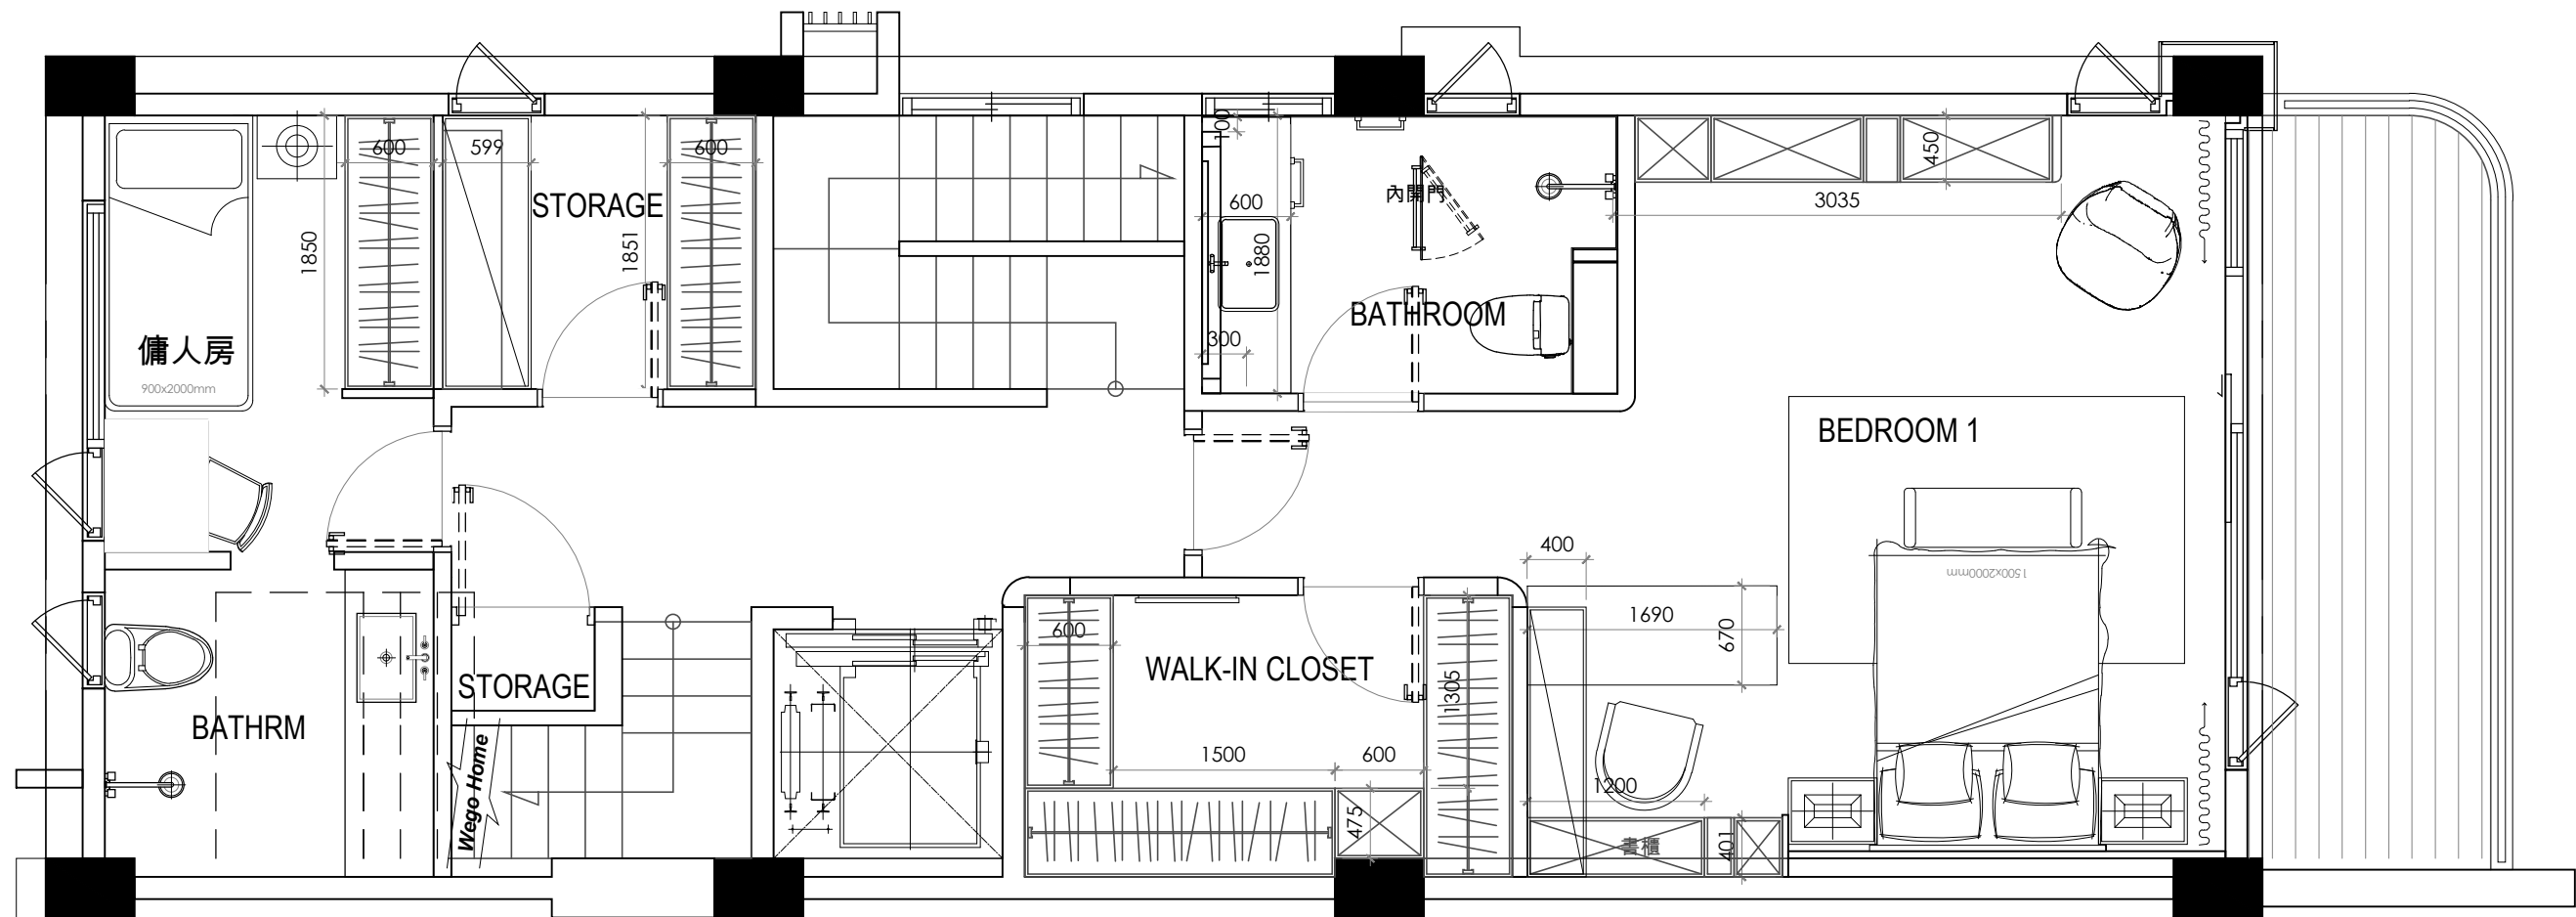


二層平面圖

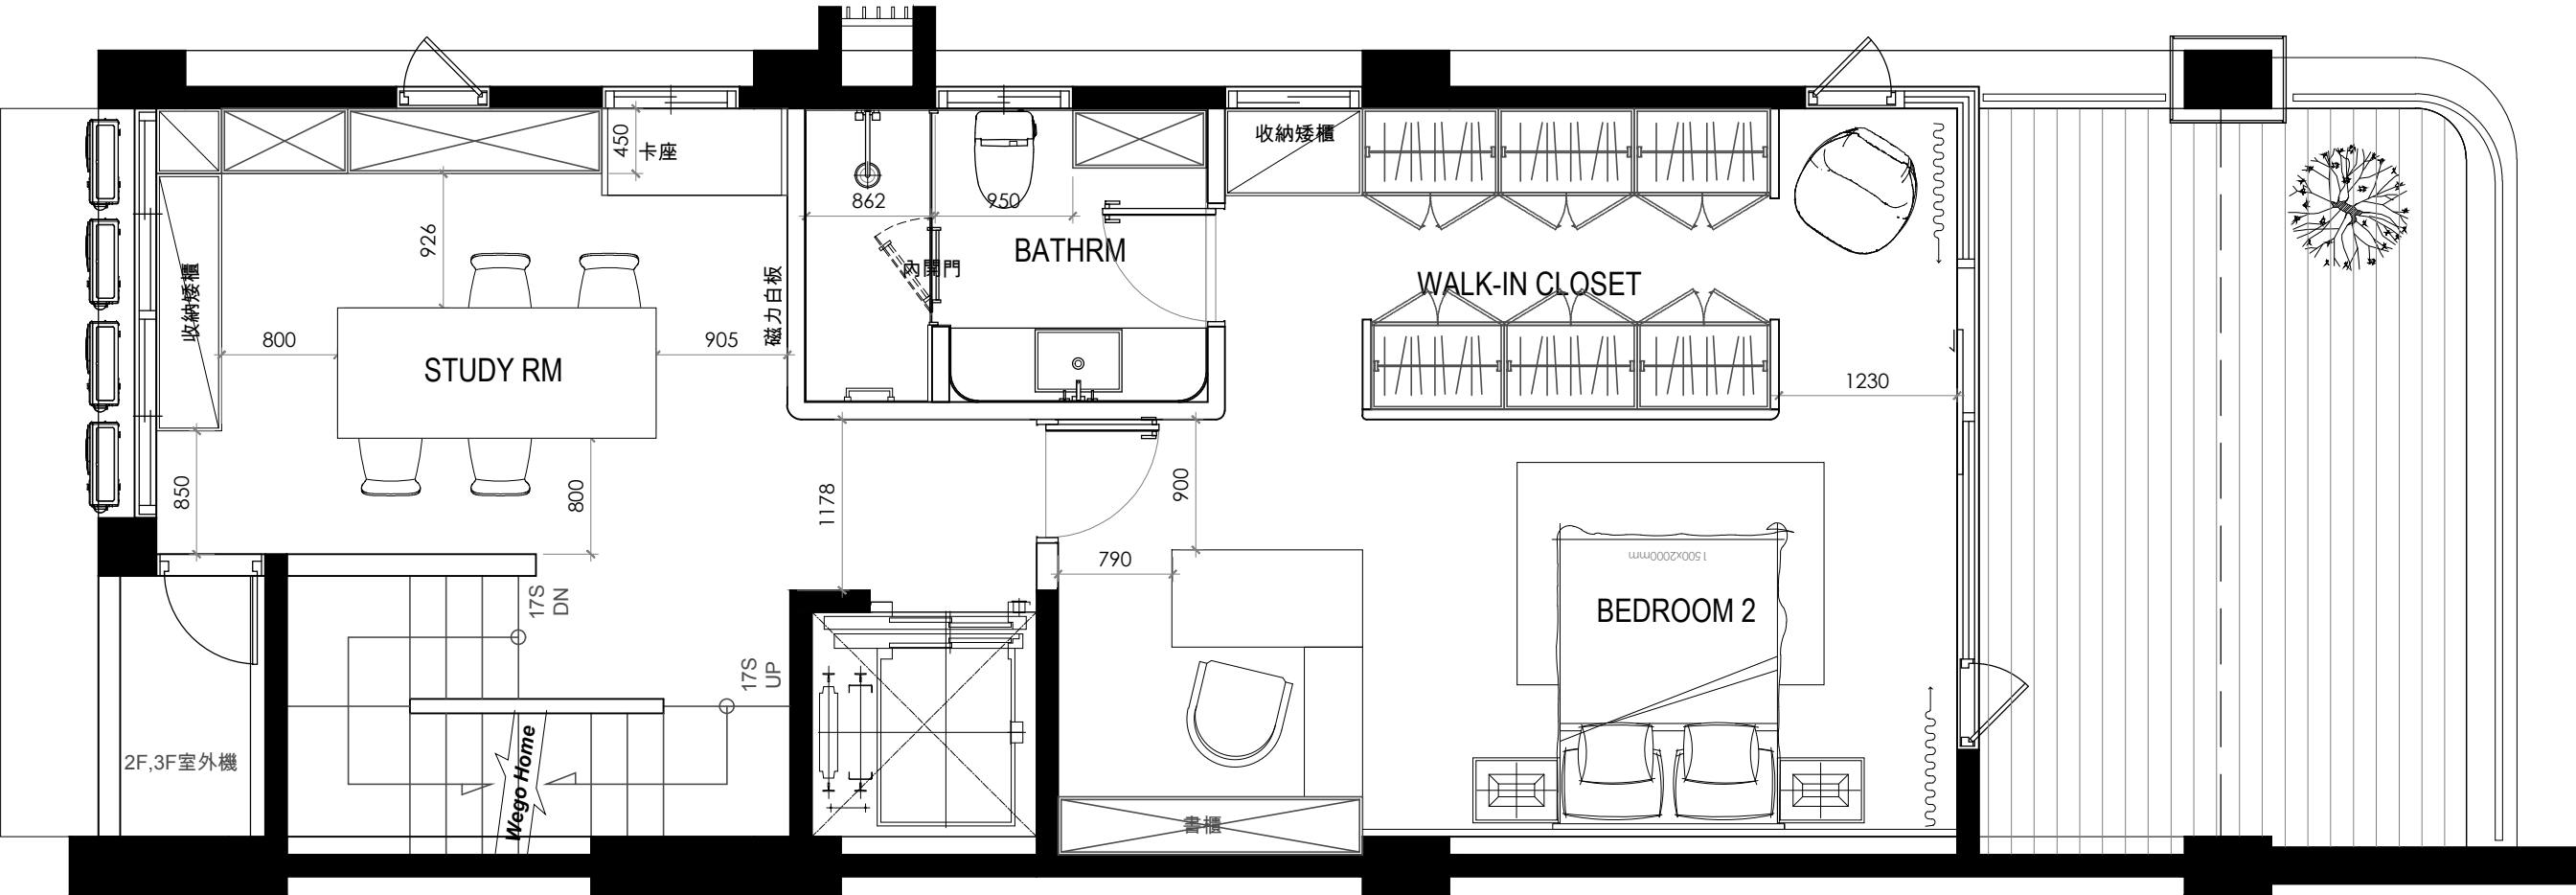


三層平面圖

  
牆 型 式	內 容	總 厚 度
	木作隔間牆	
	原有建築牆	154mm
	1/2B磚牆	120mm
	65mmC型骨架+單面(12mm石膏板+9mm矽酸鈣板), 單面(12mm石膏板+9mm矽酸鈣板)	100mm
	65mmC型骨架+雙面矽酸鈣板	85mm

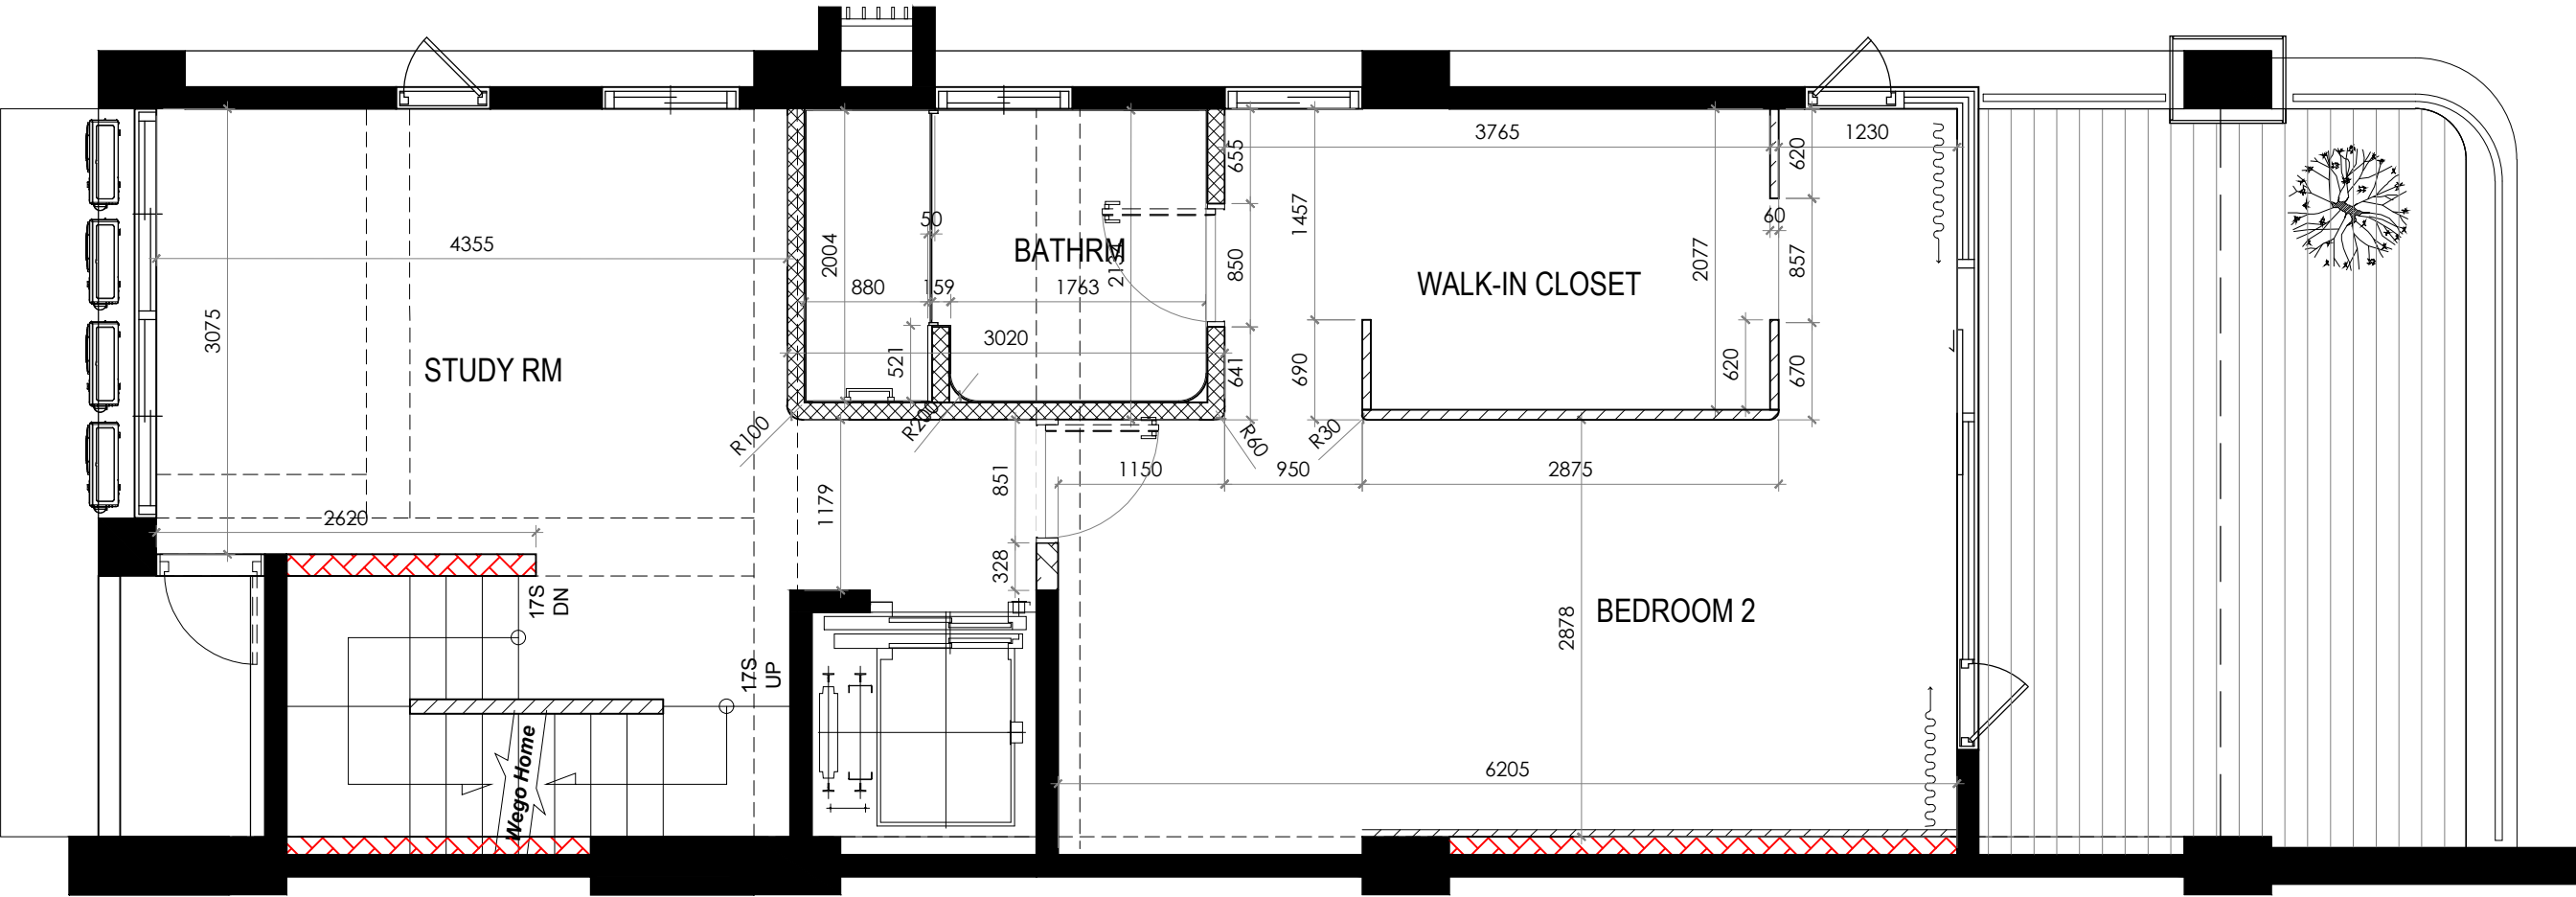

三層平面圖

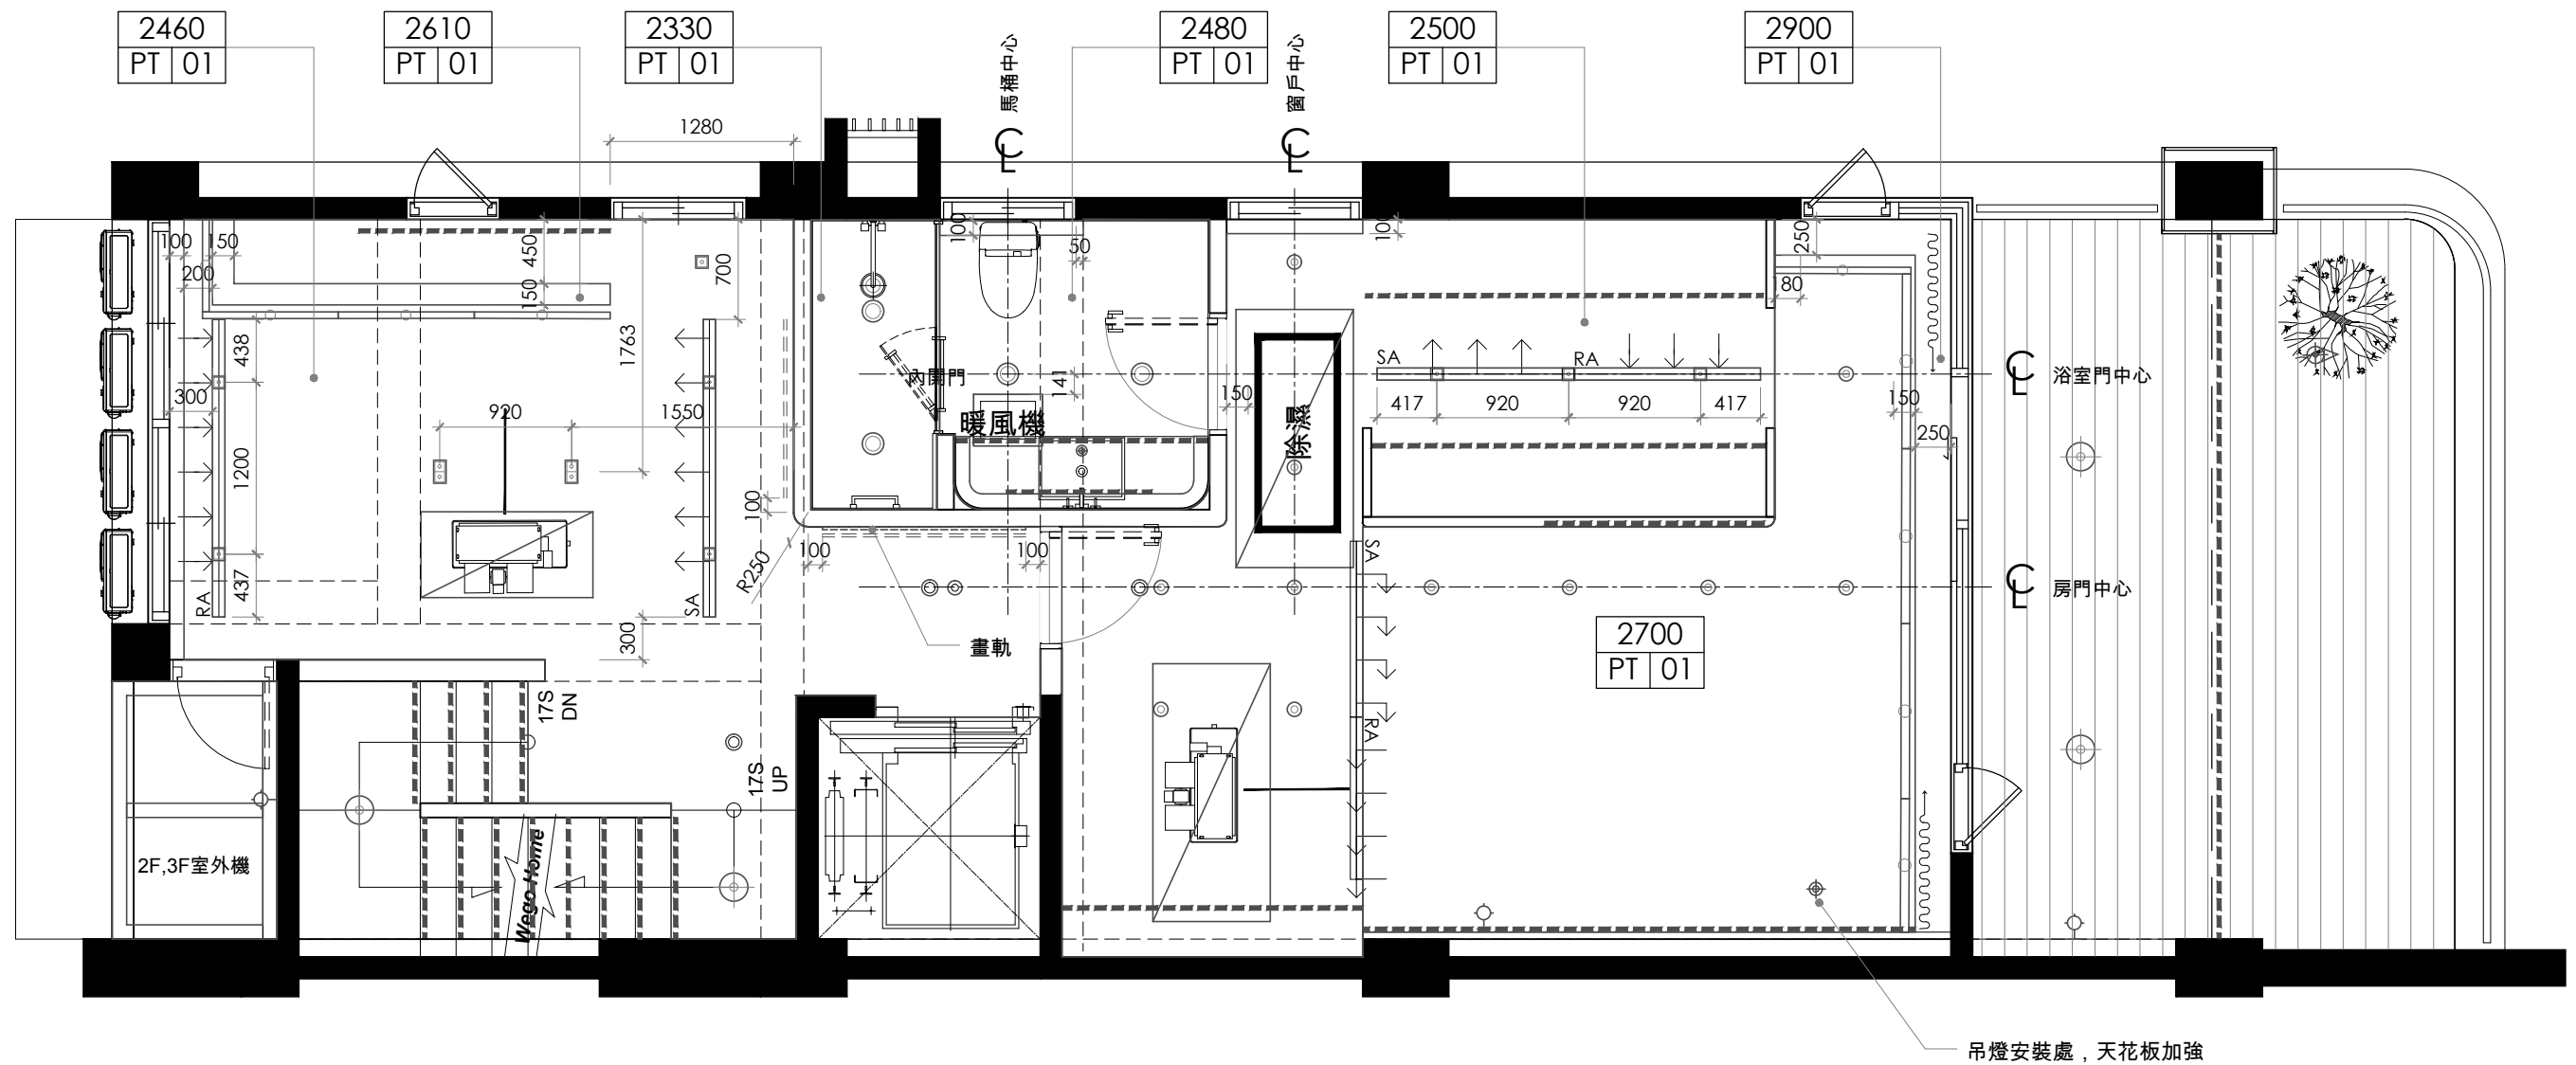


三層平面圖

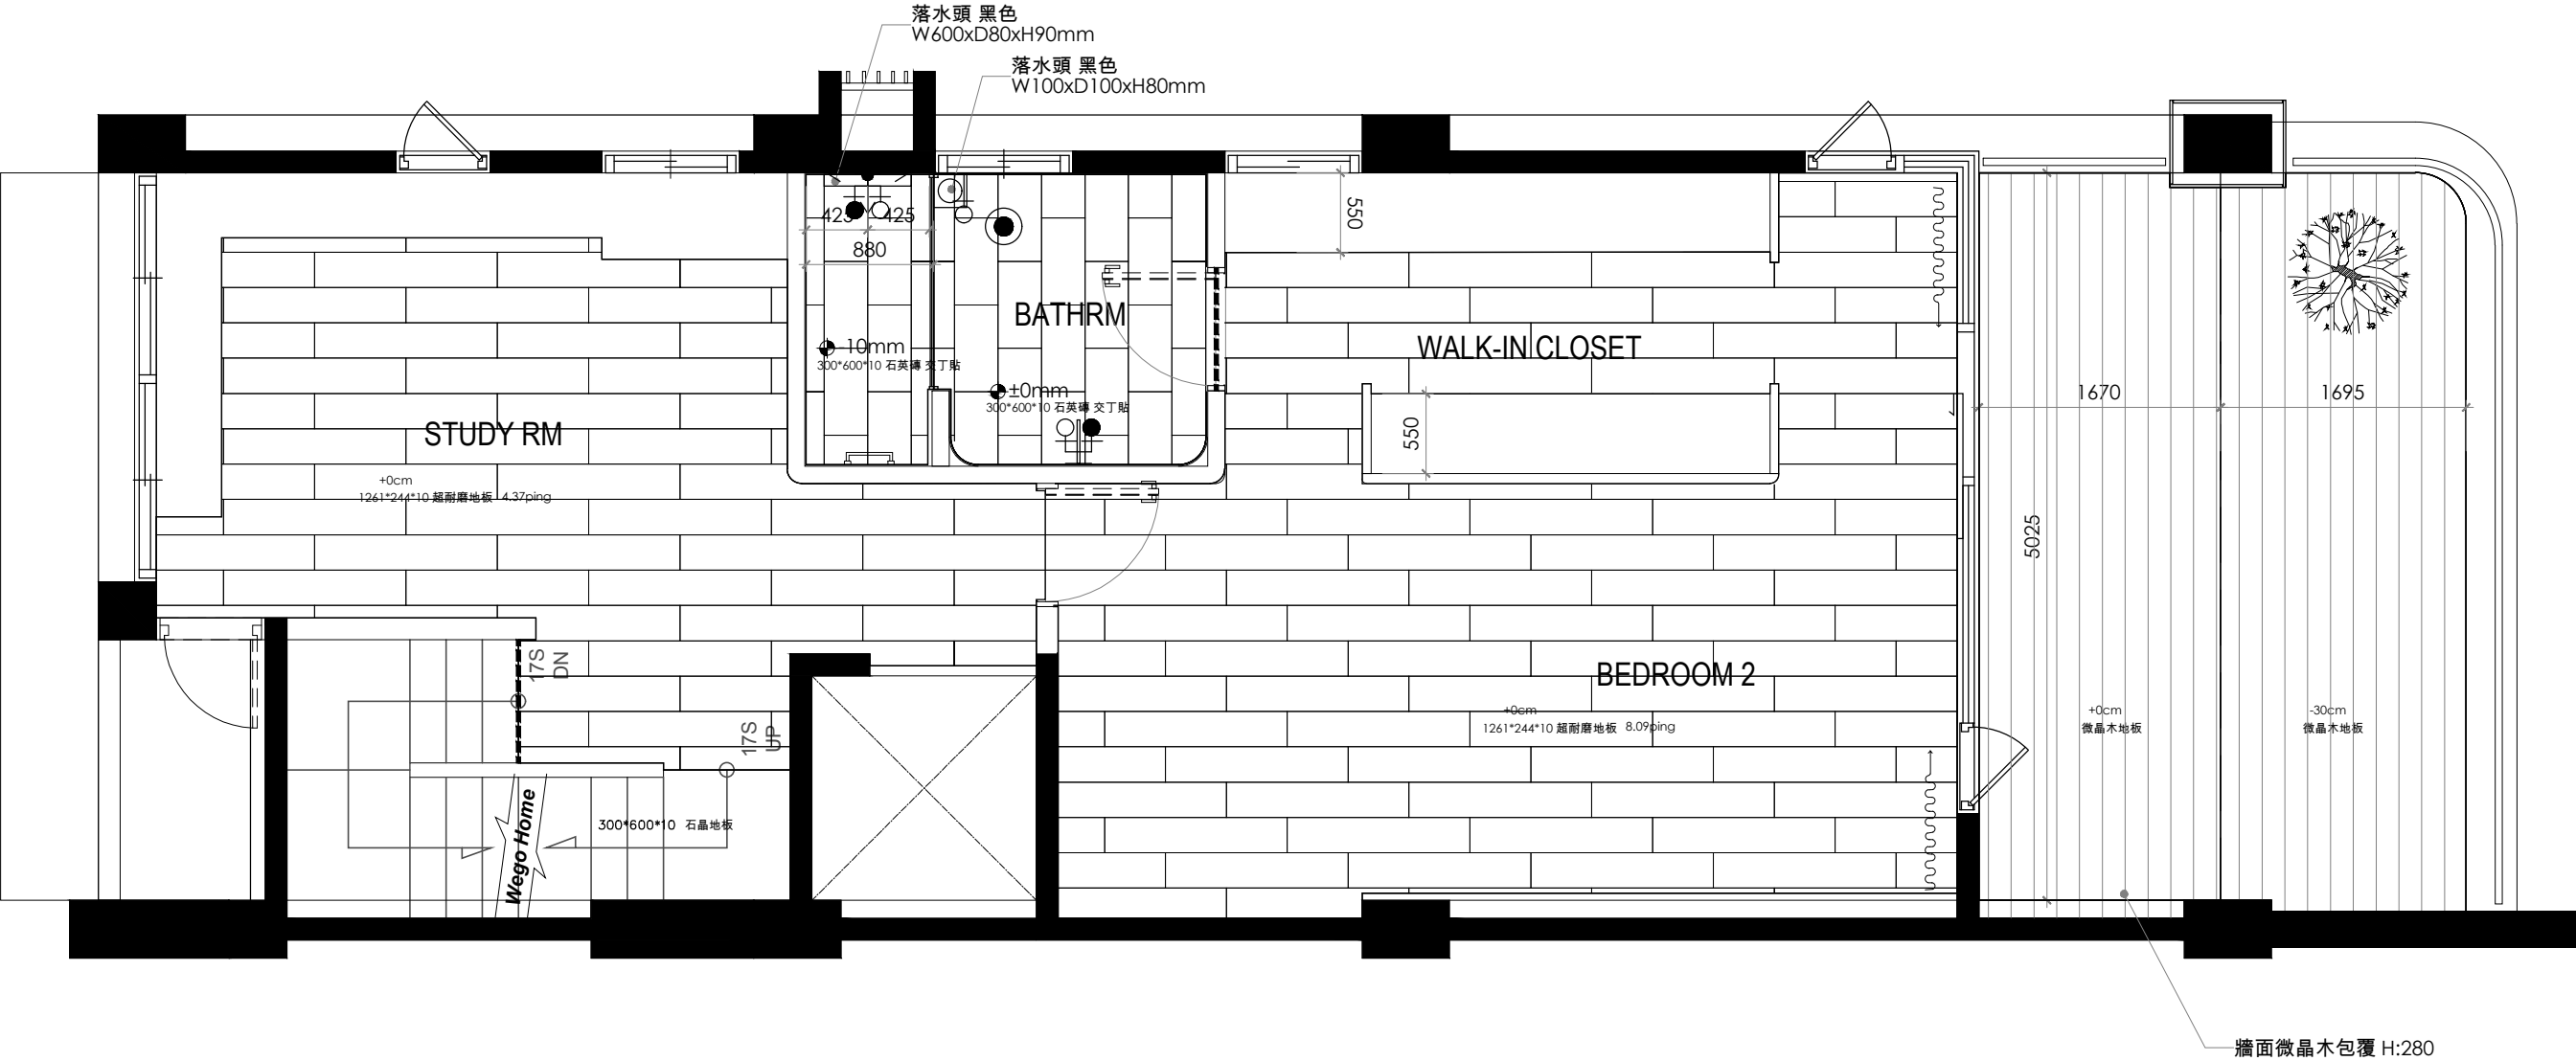


三層平面圖

編號	圖示	說明	尺寸	光源	備註
L1	●	舞光LED可調角度嵌燈	88mm Dia x H25mm	KW-303 / 8W / 3000k / 嵌孔75mm	
L2	●	2線式停電照明嵌燈	105mm Dia x H55mm	FH- 849-1B / 5W / 3000k / 嵌孔93mm	
L3	●	3線式停電照明嵌燈	105mm Dia x H55mm	FH- 849-1B / 5W / 3000k / 嵌孔93mm	
L4	⊕	LED 15W 小吸頂燈	82mm Dia x H78mm	3000k	
L5	●	舞光LED 邱比特軌道燈 白色	W88mm x L115mm x H50mm	AE-B07 / 7W / 3000k / 24°	
L6	●	超薄嵌入式感應式嵌燈	85mm Dia x H50mm	3000k / 嵌孔75mm	
L7	-----	LED軟條燈		3000k	
L8	=====	軌道燈軌道	W34mm x H20mm		
L9	●	小型嵌燈	63mm Dia x H72mm	3000k / 嵌孔55mm	
L10	■	無邊框可調角LED單燈盒燈	W99mm x L99mm x H85mm	FH- 829-11C /10W /30° / 3000K	
L11	■	無邊框可調角LED雙燈盒燈	W99mm x L199mm x H85mm	FH- 829-12C /10W /30° / 3000K	
L12	- · - · -	磁吸式軌道燈			
L13	———○———	防塵防濕T5燈具			
L14	●	上照LED埋地燈	42mm Dia. x H90mm	LED /3W /12° /12V /3000K / 700mA	
DL-1	◆	吊燈			
DL-2	◇	壁燈			
*燈具相關設備,需詳燈具規範最後確認。 *燈具供電皆為220V.					

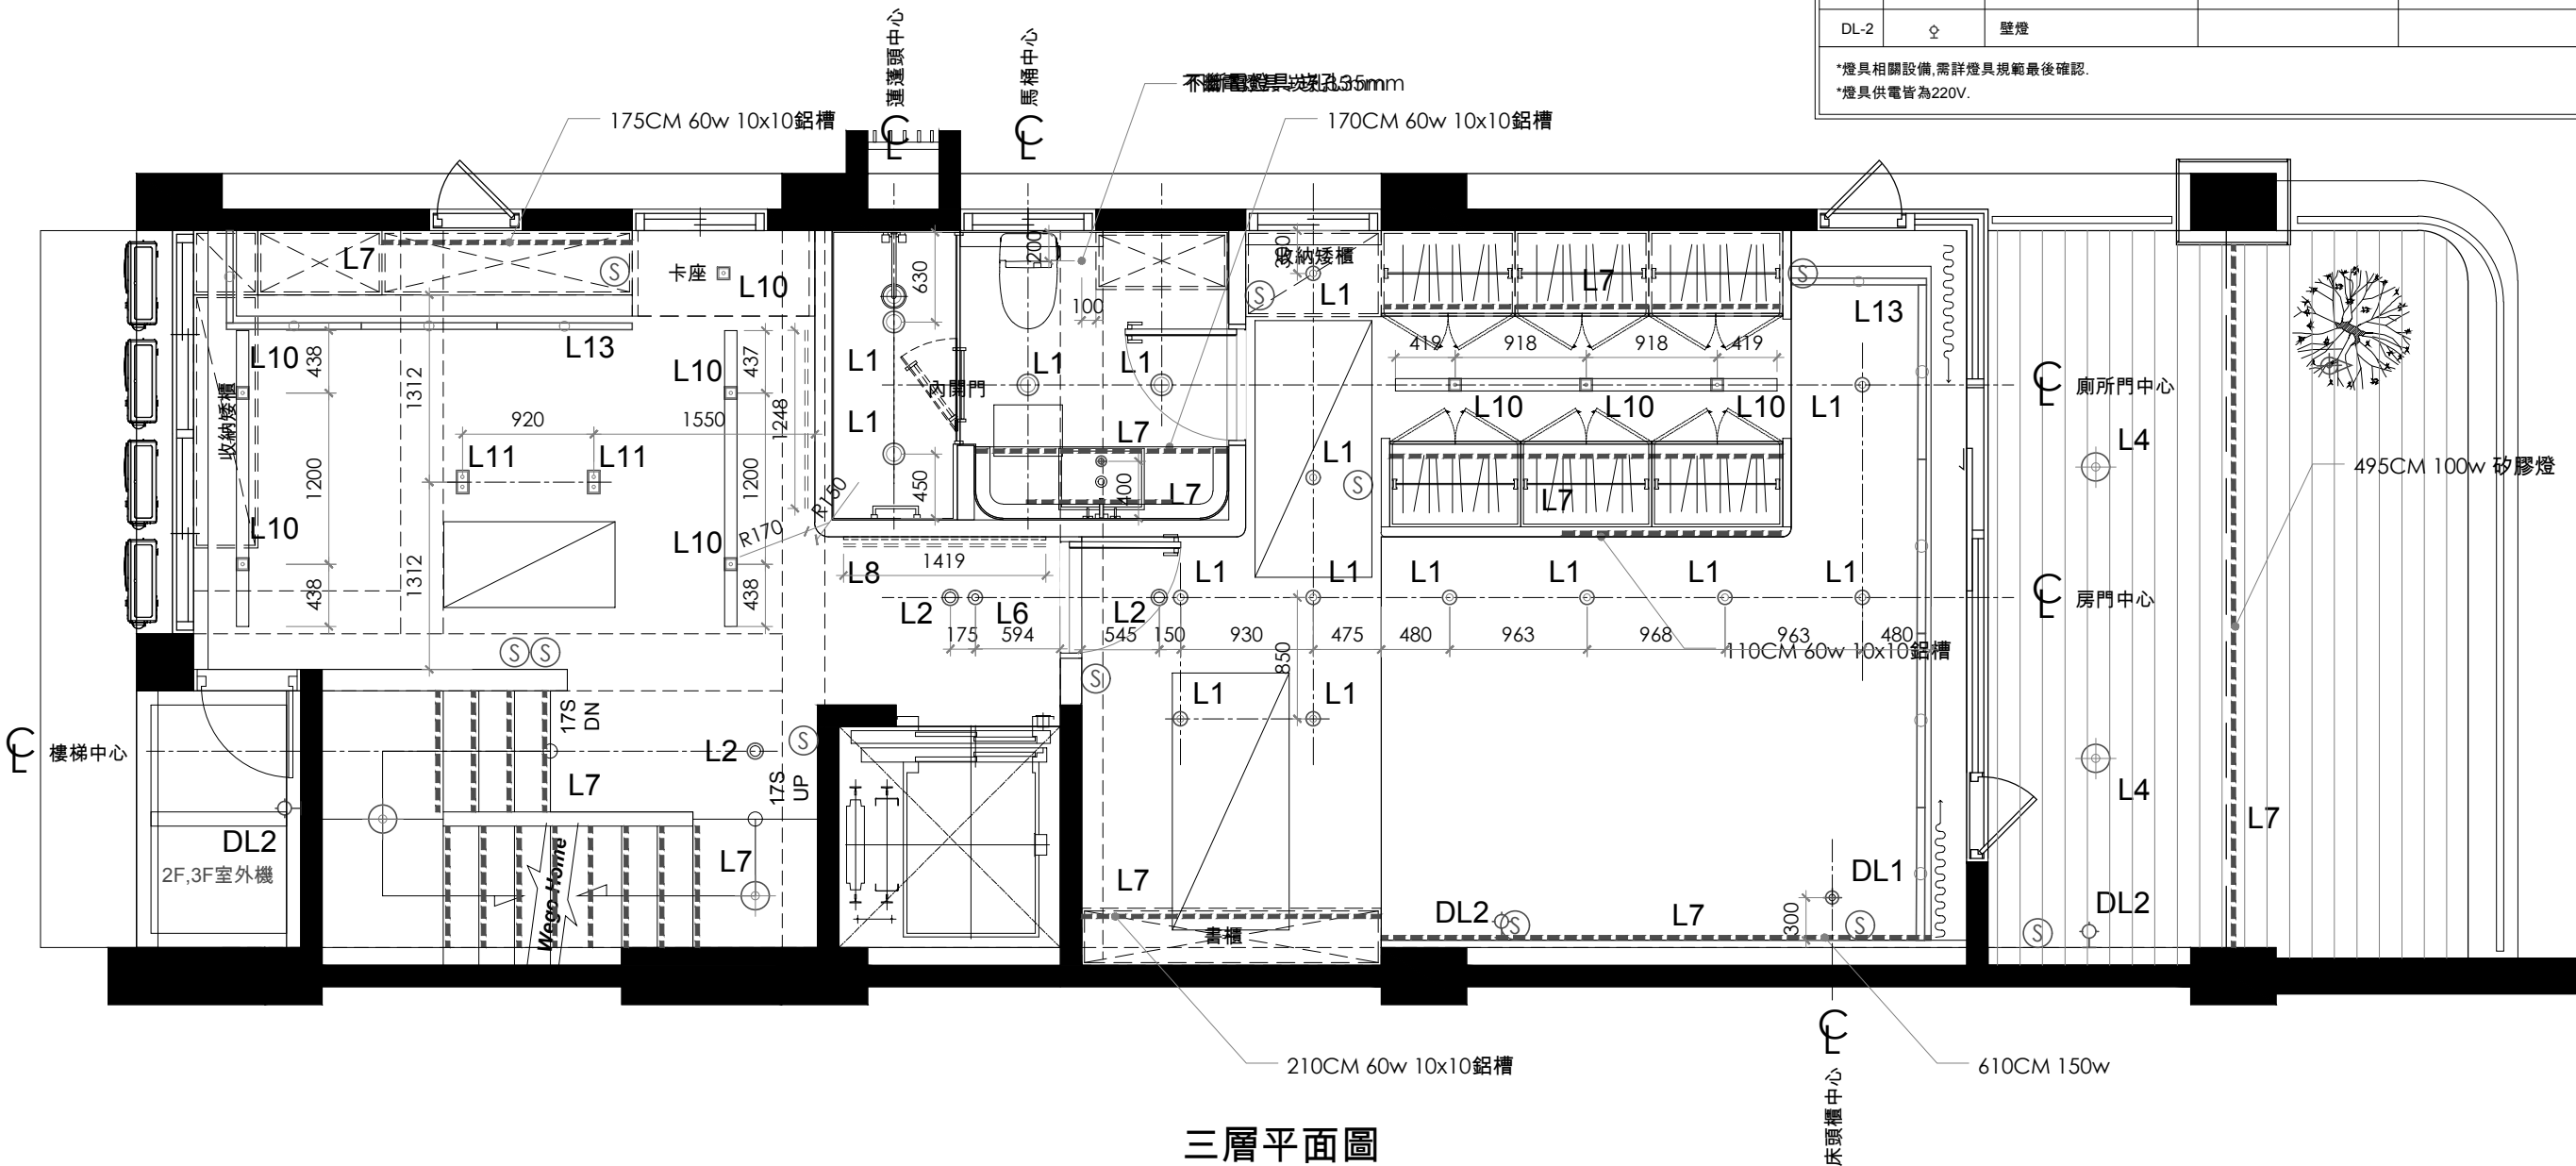

三層平面圖

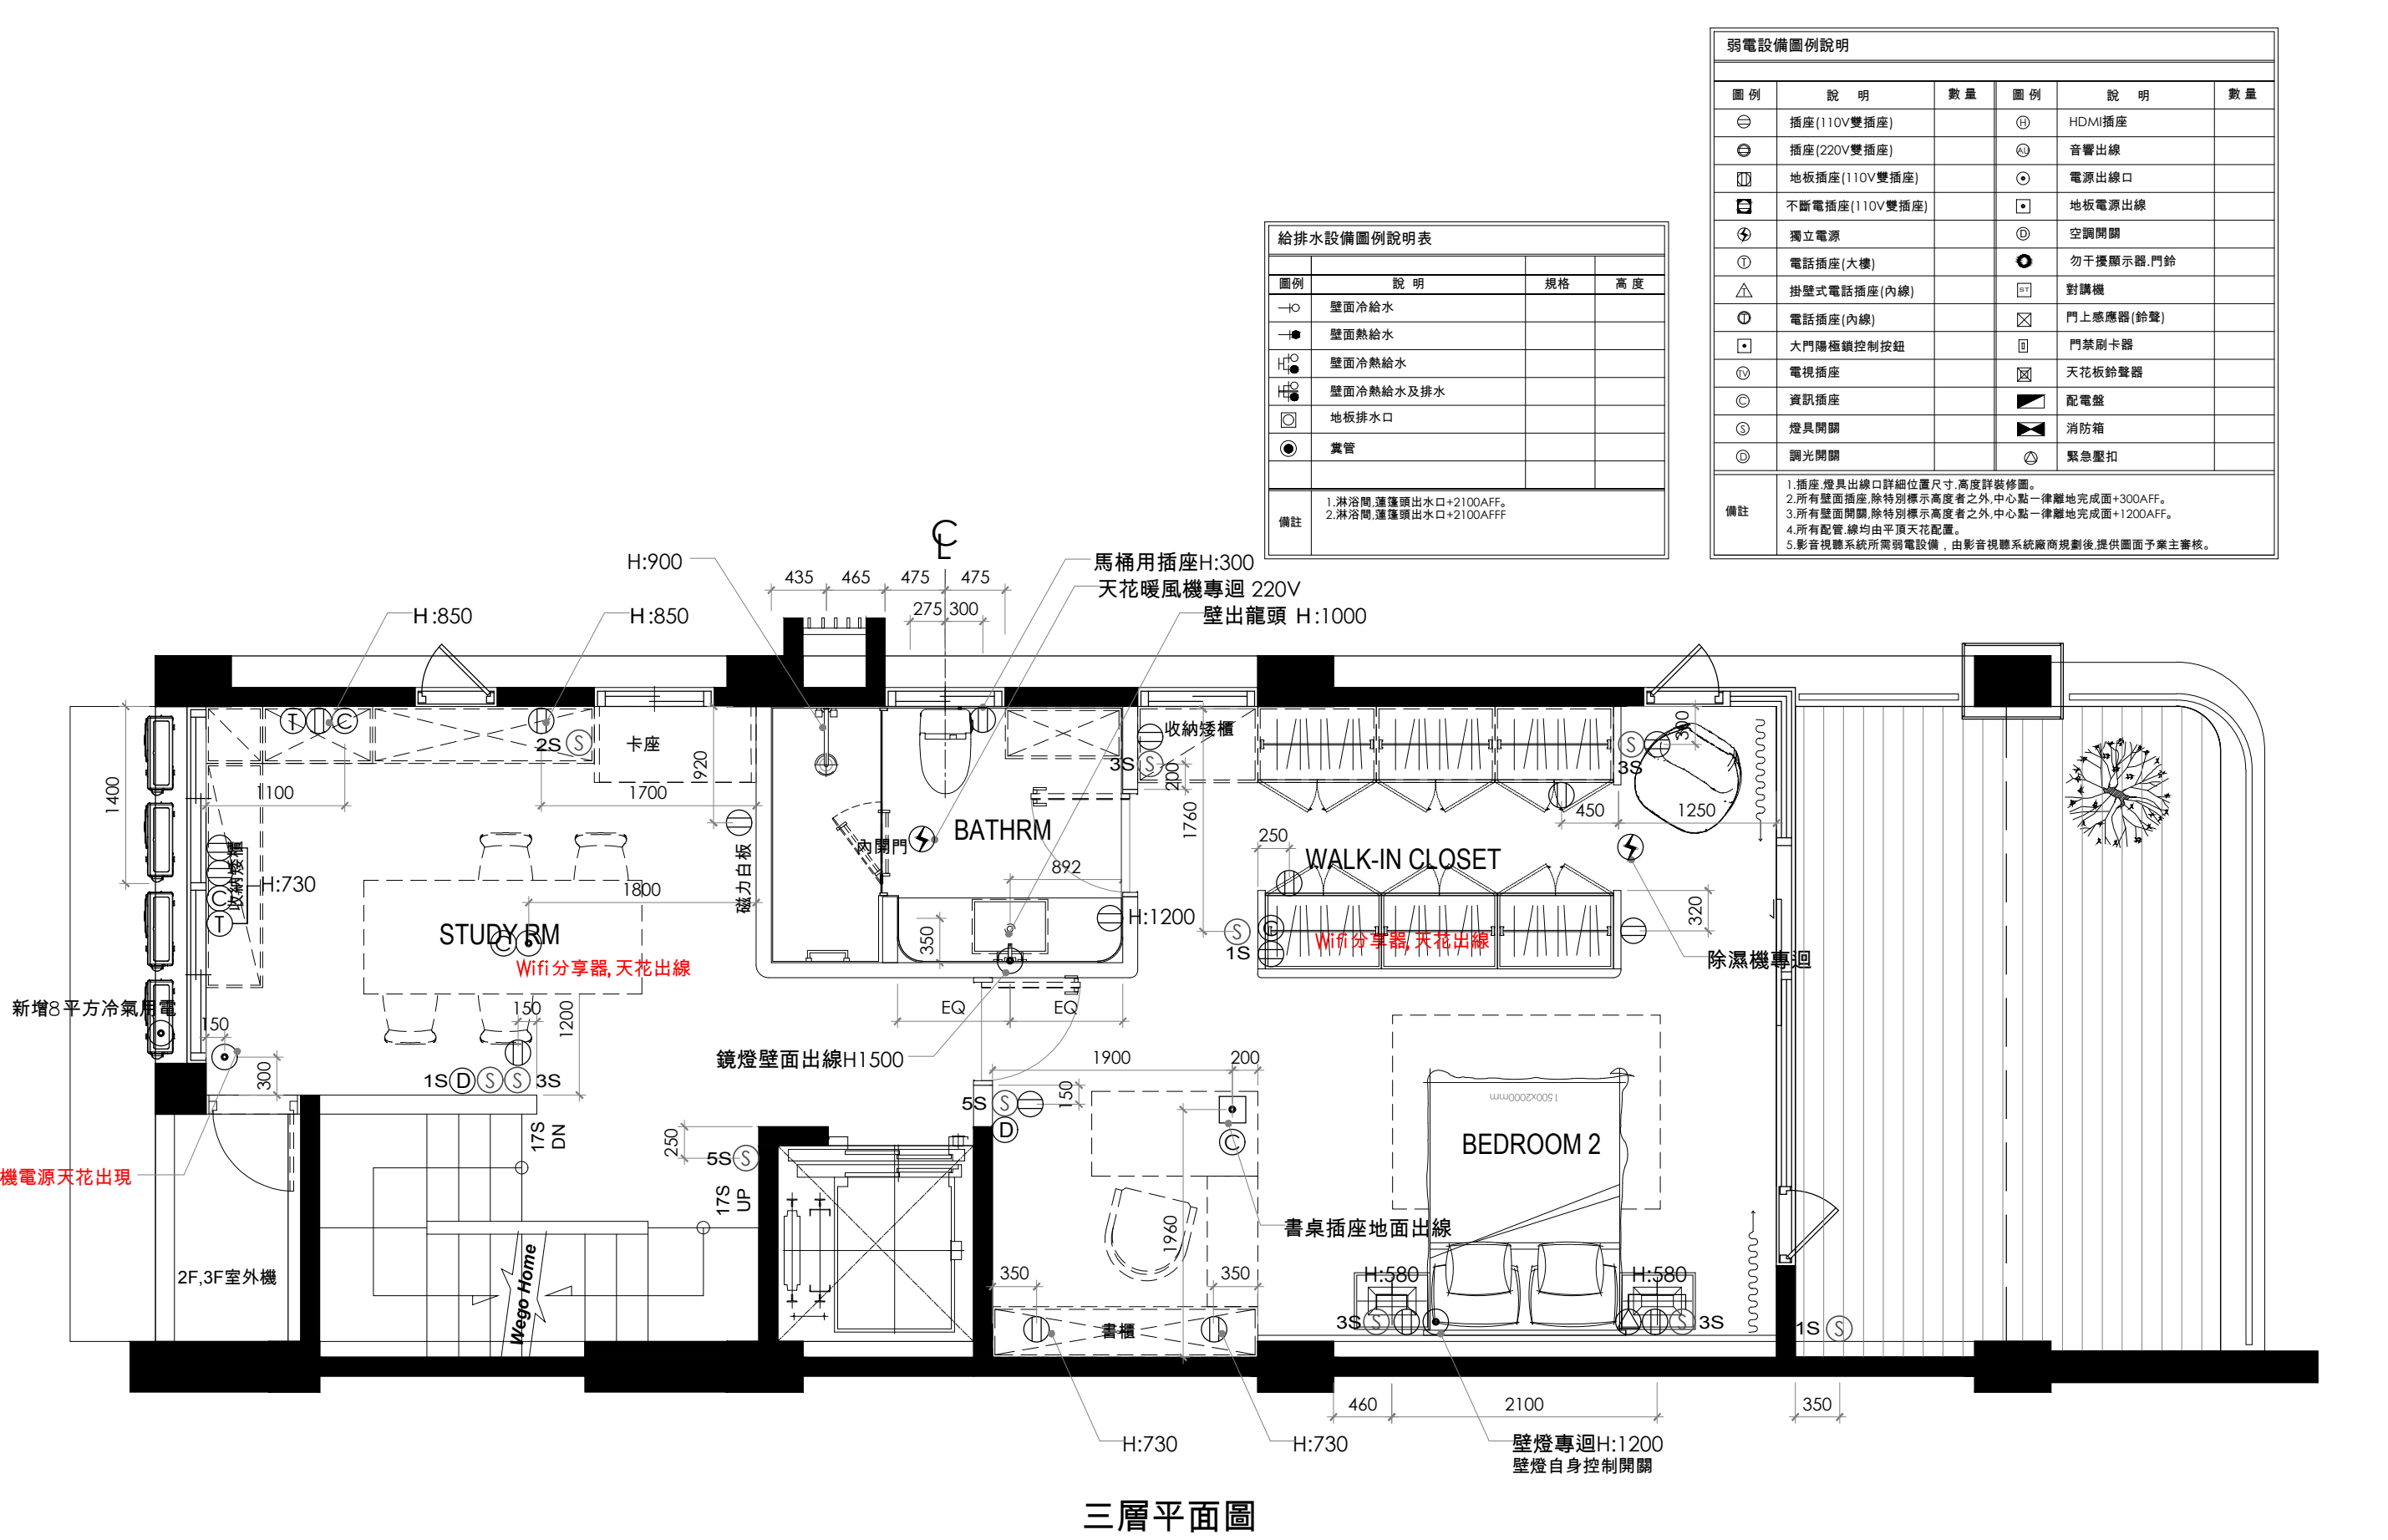


給排水設備圖例說明表			
圖例	說明	規格	高度
—○	壁面冷給水		
—●	壁面熱給水		
H●	壁面冷熱給水		
H●	壁面冷熱給水及排水		
□	地板排水口		
●	糞管		
備註			
1.淋浴間,蓮蓬頭出水口+2100AFF。 2.淋浴間,蓮蓬頭出水口+2100AFF			

弱電設備圖例說明					
圖例	說明	數量	圖例	說明	數量
⊖	插座(110V雙插座)		Ⓜ	HDMI插座	
⊖	插座(220V雙插座)		Ⓐ	音響出線	
Ⓜ	地板插座(110V雙插座)		⊙	電源出線口	
Ⓜ	不斷電插座(110V雙插座)		Ⓜ	地板電源出線	
Ⓜ	獨立電源		Ⓜ	空調開關	
Ⓜ	電話插座(大樓)		Ⓜ	勿干擾顯示器.門鈴	
Ⓜ	掛壁式電話插座(內線)		Ⓜ	對講機	
Ⓜ	電話插座(內線)		Ⓜ	門上感應器(鈴聲)	
Ⓜ	大門陽極鎖控制按鈕		Ⓜ	門禁刷卡器	
Ⓜ	電視插座		Ⓜ	天花板鈴聲器	
Ⓜ	資訊插座		Ⓜ	配電盤	
Ⓜ	燈具開關		Ⓜ	消防箱	
Ⓜ	調光開關		Ⓜ	緊急壓扣	
備註					
1.插座,燈具出線口詳細位置尺寸,高度詳裝修圖。 2.所有壁面插座,除特別標示高度者之外,中心點一律離地完成面+300AFF。 3.所有壁面開關,除特別標示高度者之外,中心點一律離地完成面+1200AFF。 4.所有配管,線均由平頂天花配置。 5.影音視聽系統所需弱電設備,由影音視聽系統廠商規劃後,提供圖面予業主審核。					

三層平面圖


編號	圖示	說明	尺寸	光源	備註
L1	●	舞光LED可調角度嵌燈	88mm Dia x H25mm	KW-303 / 8W / 3000k / 嵌孔75mm	
L2	●	2線式停電照明嵌燈	105mm Dia x H55mm	FH- 849-1B / 5W / 3000k / 嵌孔93mm	
L3	●	3線式停電照明嵌燈	105mm Dia x H55mm	FH- 849-1B / 5W / 3000k / 嵌孔93mm	
L4	⊕	LED 15W 小吸頂燈	82mm Dia x H78mm	3000k	
L5	●	舞光LED 邱比特軌道燈 白色	W88mm x L115mm x H50mm	AE-B07 / 7W / 3000k / 24°	
L6	●	超薄嵌入式感應式嵌燈	85mm Dia x H50mm	3000k / 嵌孔75mm	
L7	-----	LED軟條燈		3000k	
L8	=====	軌道燈軌道	W34mm x H20mm		
L9	●	小型嵌燈	63mm Dia x H72mm	3000k / 嵌孔55mm	
L10	▣	無邊框可調角LED單燈盒燈	W99mm x L99mm x H85mm	FH- 829-11C /10W /30° / 3000K	
L11	▣	無邊框可調角LED雙燈盒燈	W99mm x L199mm x H85mm	FH- 829-12C /10W /30° / 3000K	
L12	- · - · -	磁吸式軌道燈			
L13	—○—	防塵防濕T5燈具			
L14	●	上照LED埋地燈	42mm Dia. x H90mm	LED /3W /12° /12V /3000K / 700mA	
DL-1	◆	吊燈			
DL-2	◇	壁燈			
*燈具相關設備,需詳燈具規範最後確認。 *燈具供電皆為220V.					

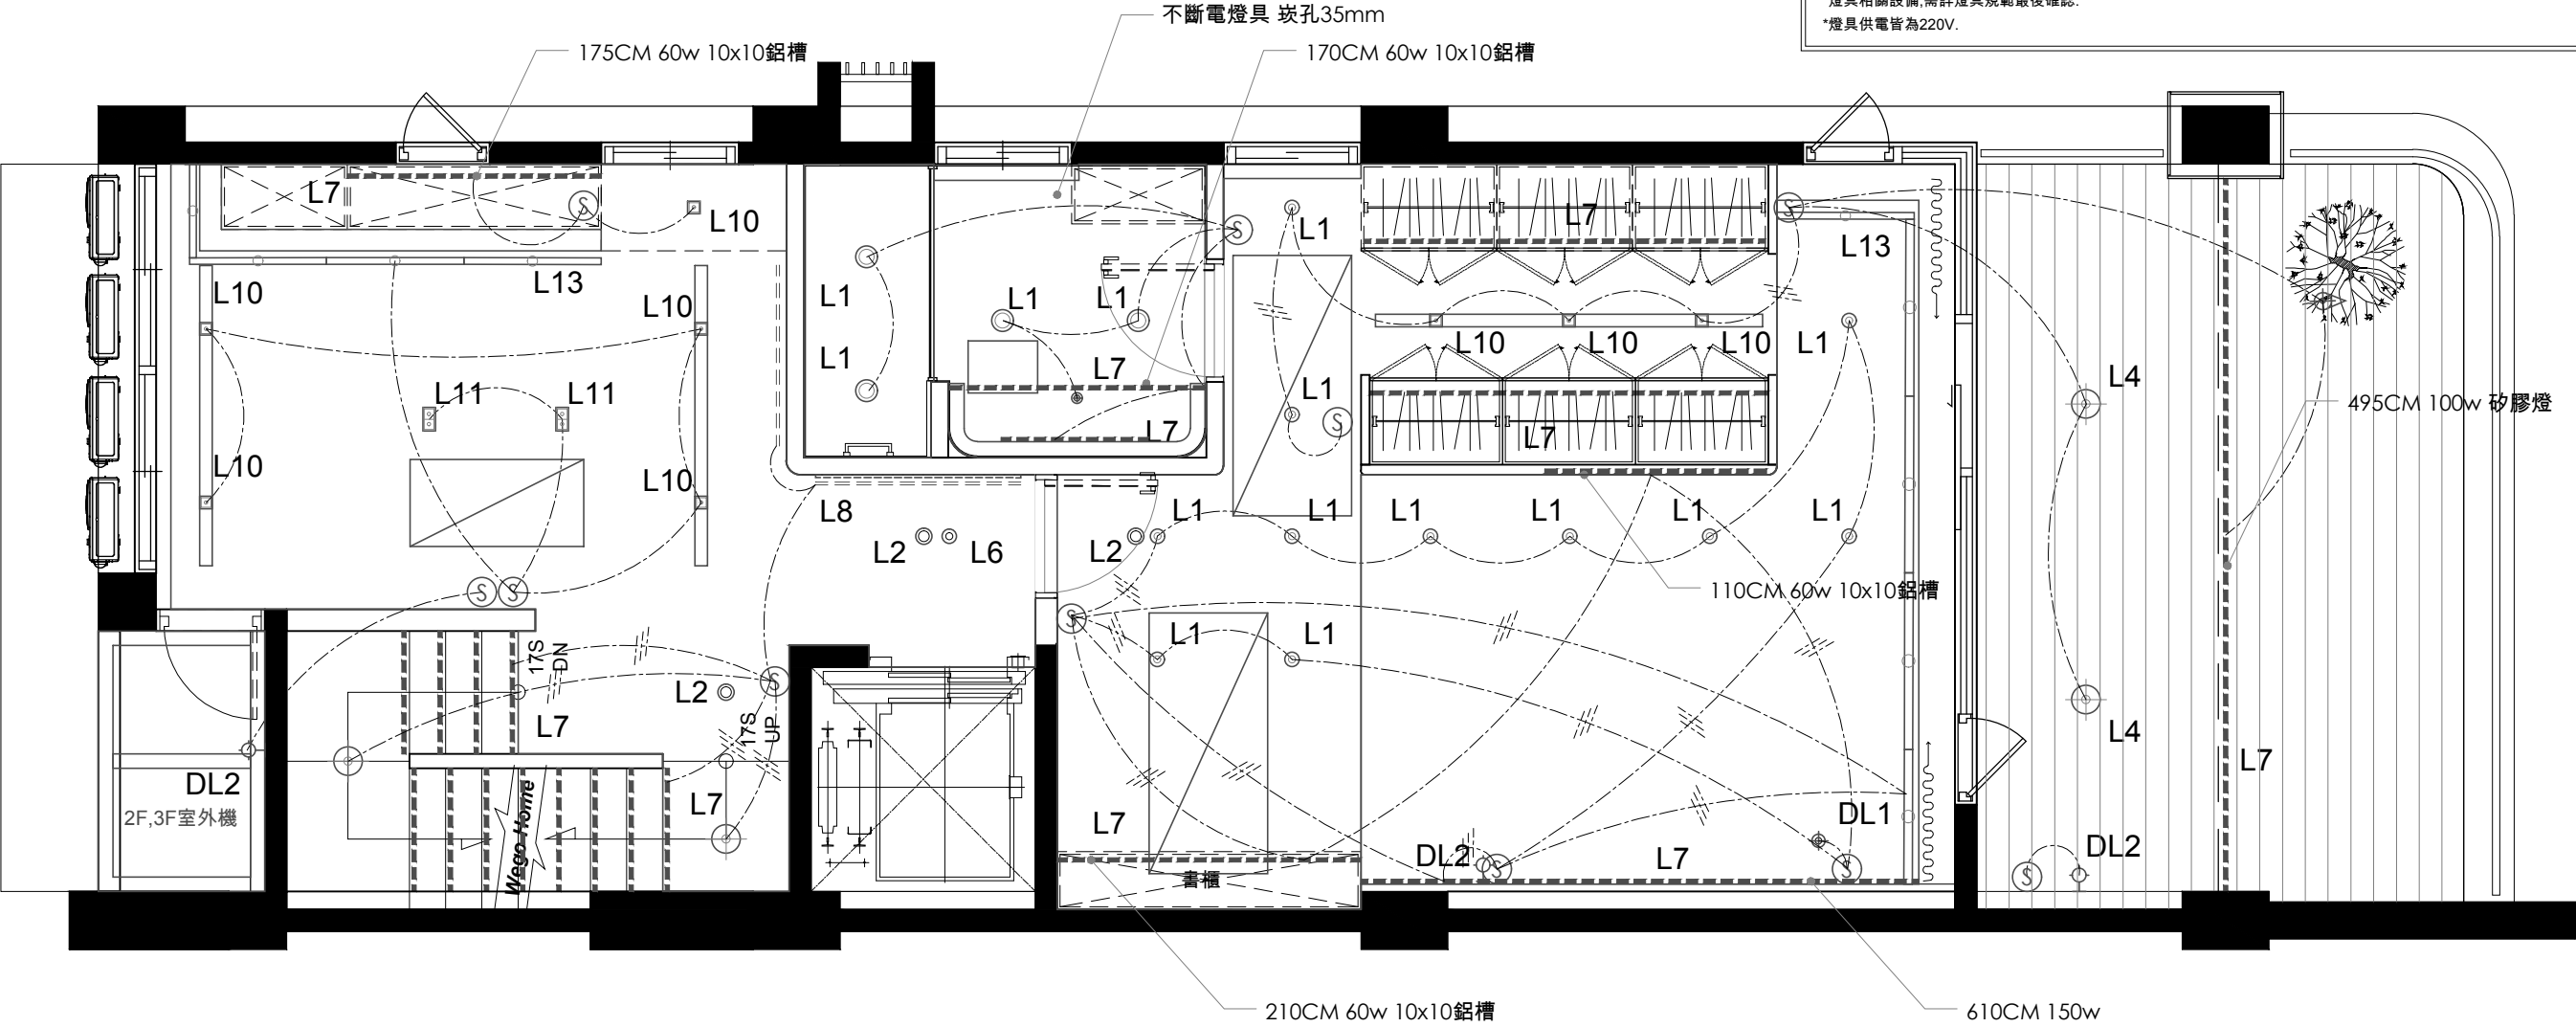


三層平面圖

編號	圖示	說明	尺寸	光源	備註
L1		舞光LED可調角度嵌燈	88mm Dia x H25mm	KW-303 / 8W / 3000k / 嵌孔75mm	
L2		2線式停電照明嵌燈	105mm Dia x H55mm	FH- 849-1B / 5W / 3000k / 嵌孔93mm	
L3		3線式停電照明嵌燈	105mm Dia x H55mm	FH- 849-1B / 5W / 3000k / 嵌孔93mm	
L4		LED 15W 小吸頂燈	82mm Dia x H78mm	3000k	
L5		舞光LED 邱比特軌道燈 白色	W88mm x L115mm x H50mm	AE-B07 / 7W / 3000k / 24°	
L6		超薄嵌入式感應式嵌燈	85mm Dia x H50mm	3000k / 嵌孔75mm	
L7		LED軟條燈		3000k	
L8		軌道燈軌道	W34mm x H20mm		
L9		小型嵌燈	63mm Dia x H72mm	3000k / 嵌孔55mm	
L10		無邊框可調角LED單燈盒燈	W99mm x L99mm x H85mm	FH- 829-11C /10W /30° / 3000K	
L11		無邊框可調角LED雙燈盒燈	W99mm x L199mm x H85mm	FH- 829-12C /10W /30° / 3000K	
L12		磁吸式軌道燈			
L13		防塵防濕T5燈具			
L14		上照LED埋地燈	42mm Dia. x H90mm	LED /3W /12° /12V /3000K / 700mA	
DL-1		吊燈			
DL-2		壁燈			
*燈具相關設備,需詳燈具規範最後確認。 *燈具供電皆為220V.					


空調設備圖例說明			
圖 例	說 明	圖 例	說 明
	側吹出風口		出風口
	側吹回風口		除濕 吊隱式除濕主機
	下吹出風口		五合一暖風機
	下吹回風口		全熱交換 全熱交換器

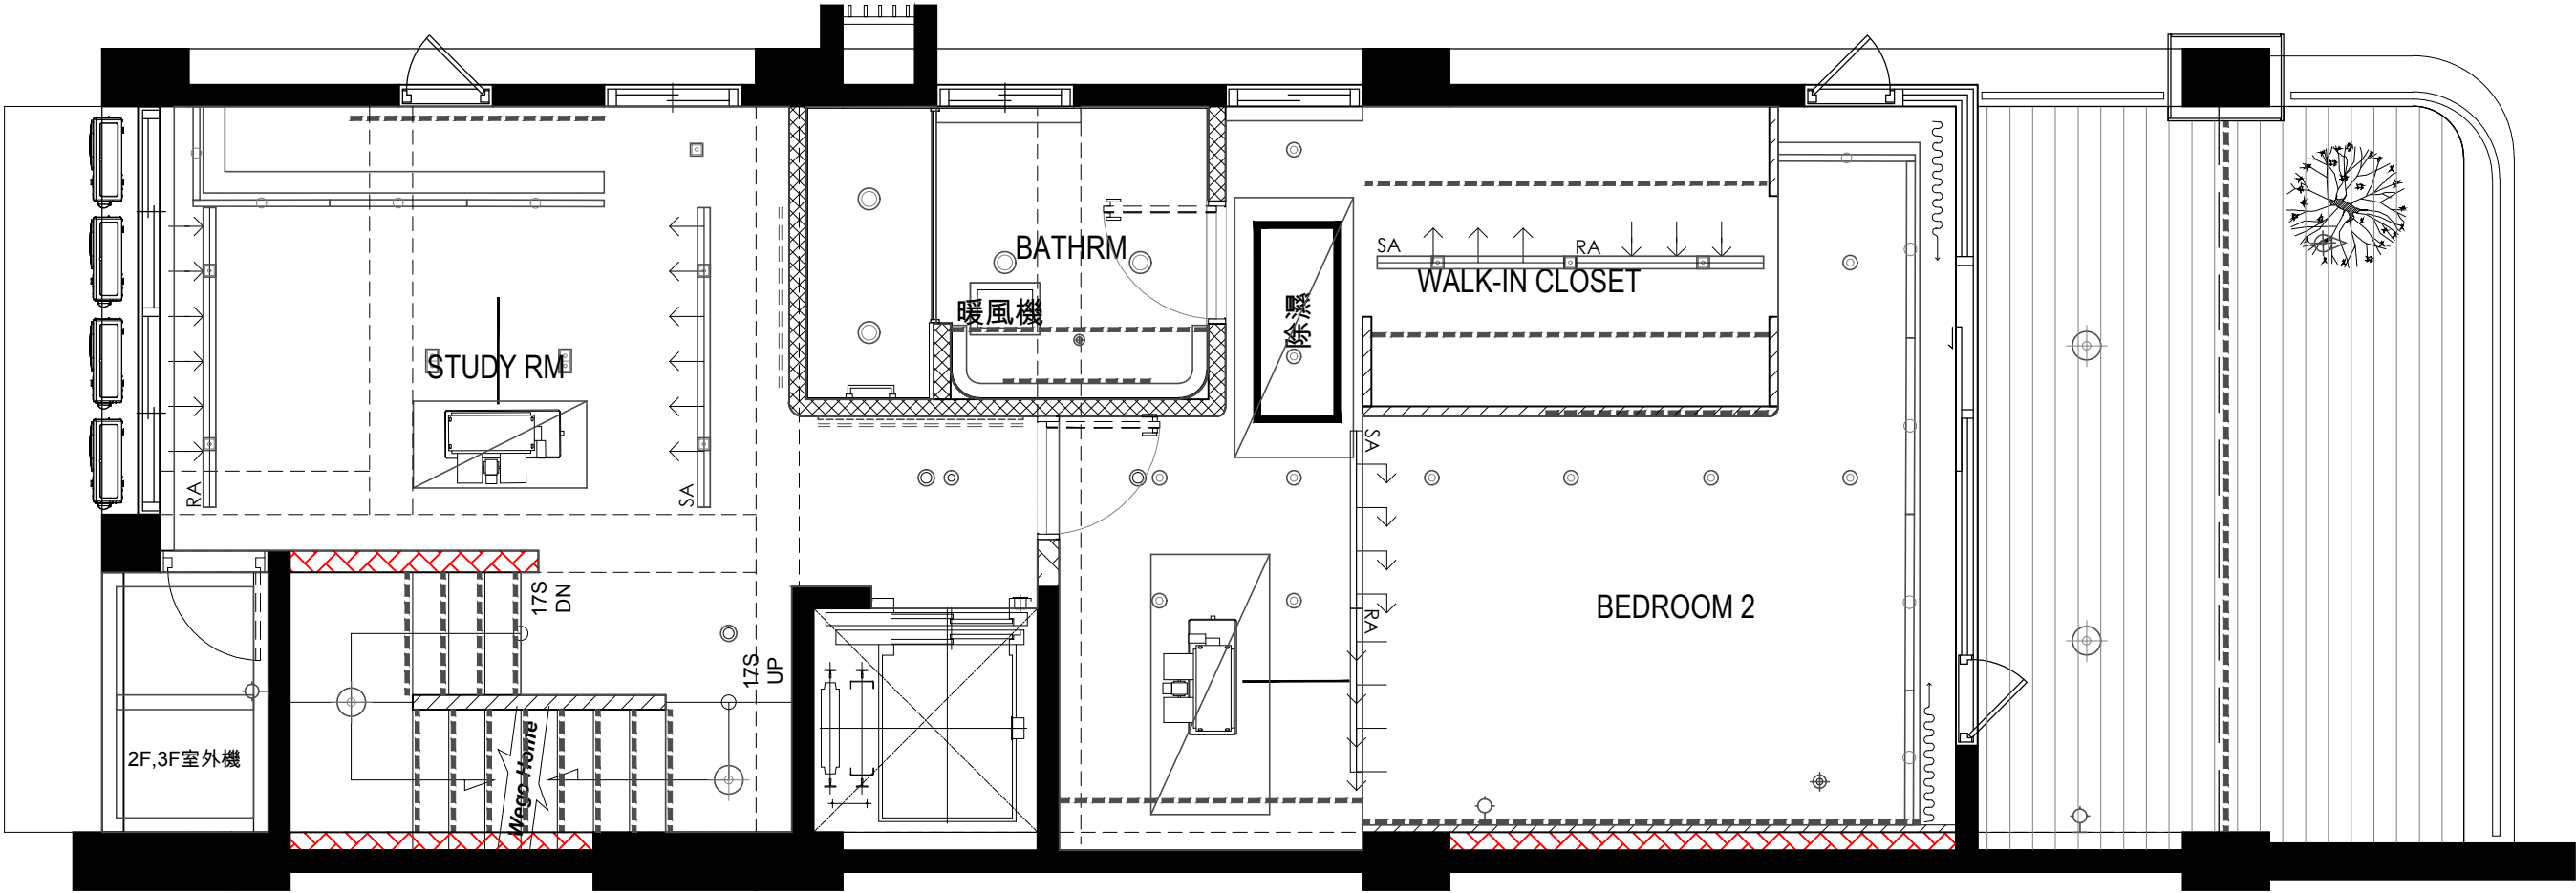


三層平面圖

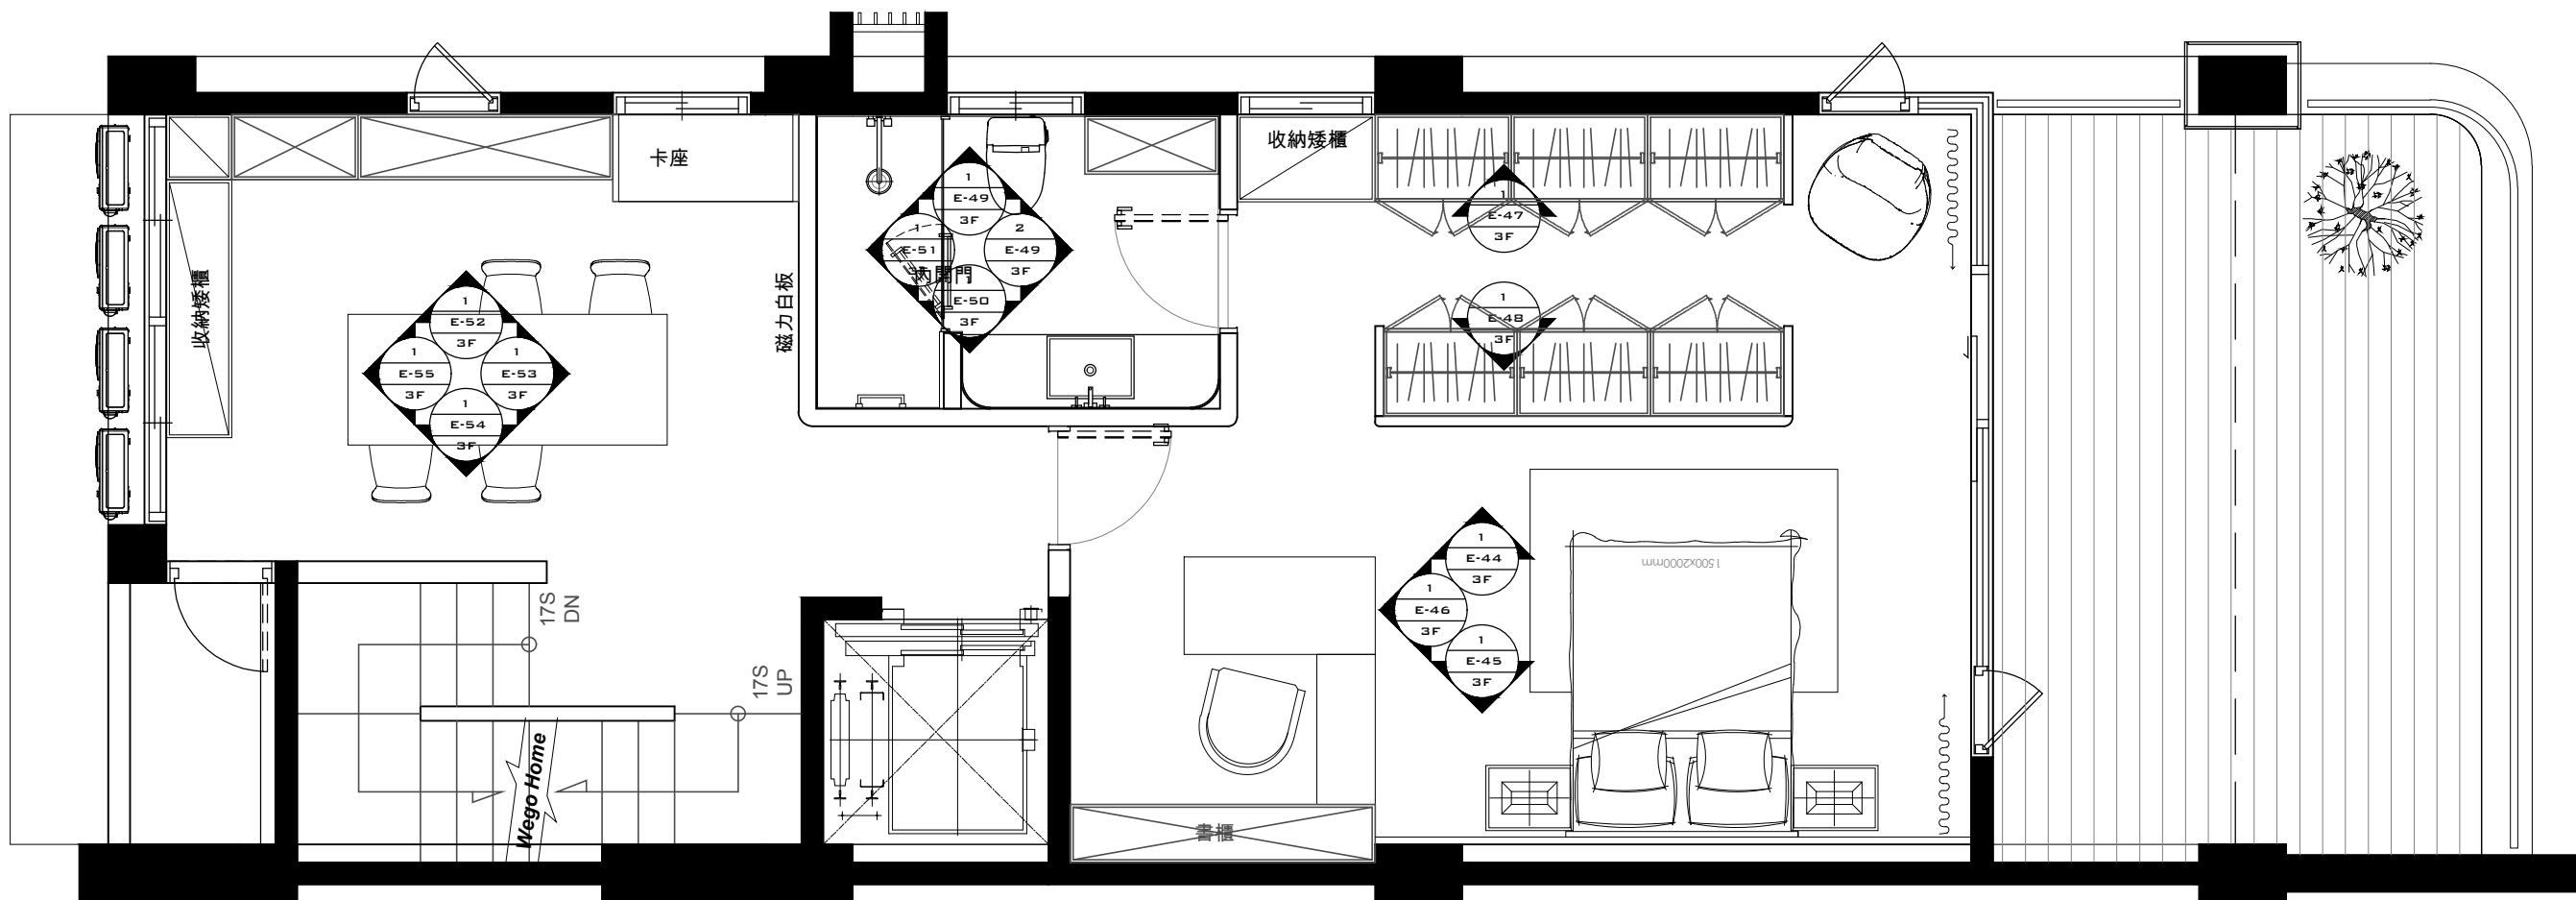


三層平面圖

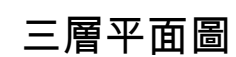

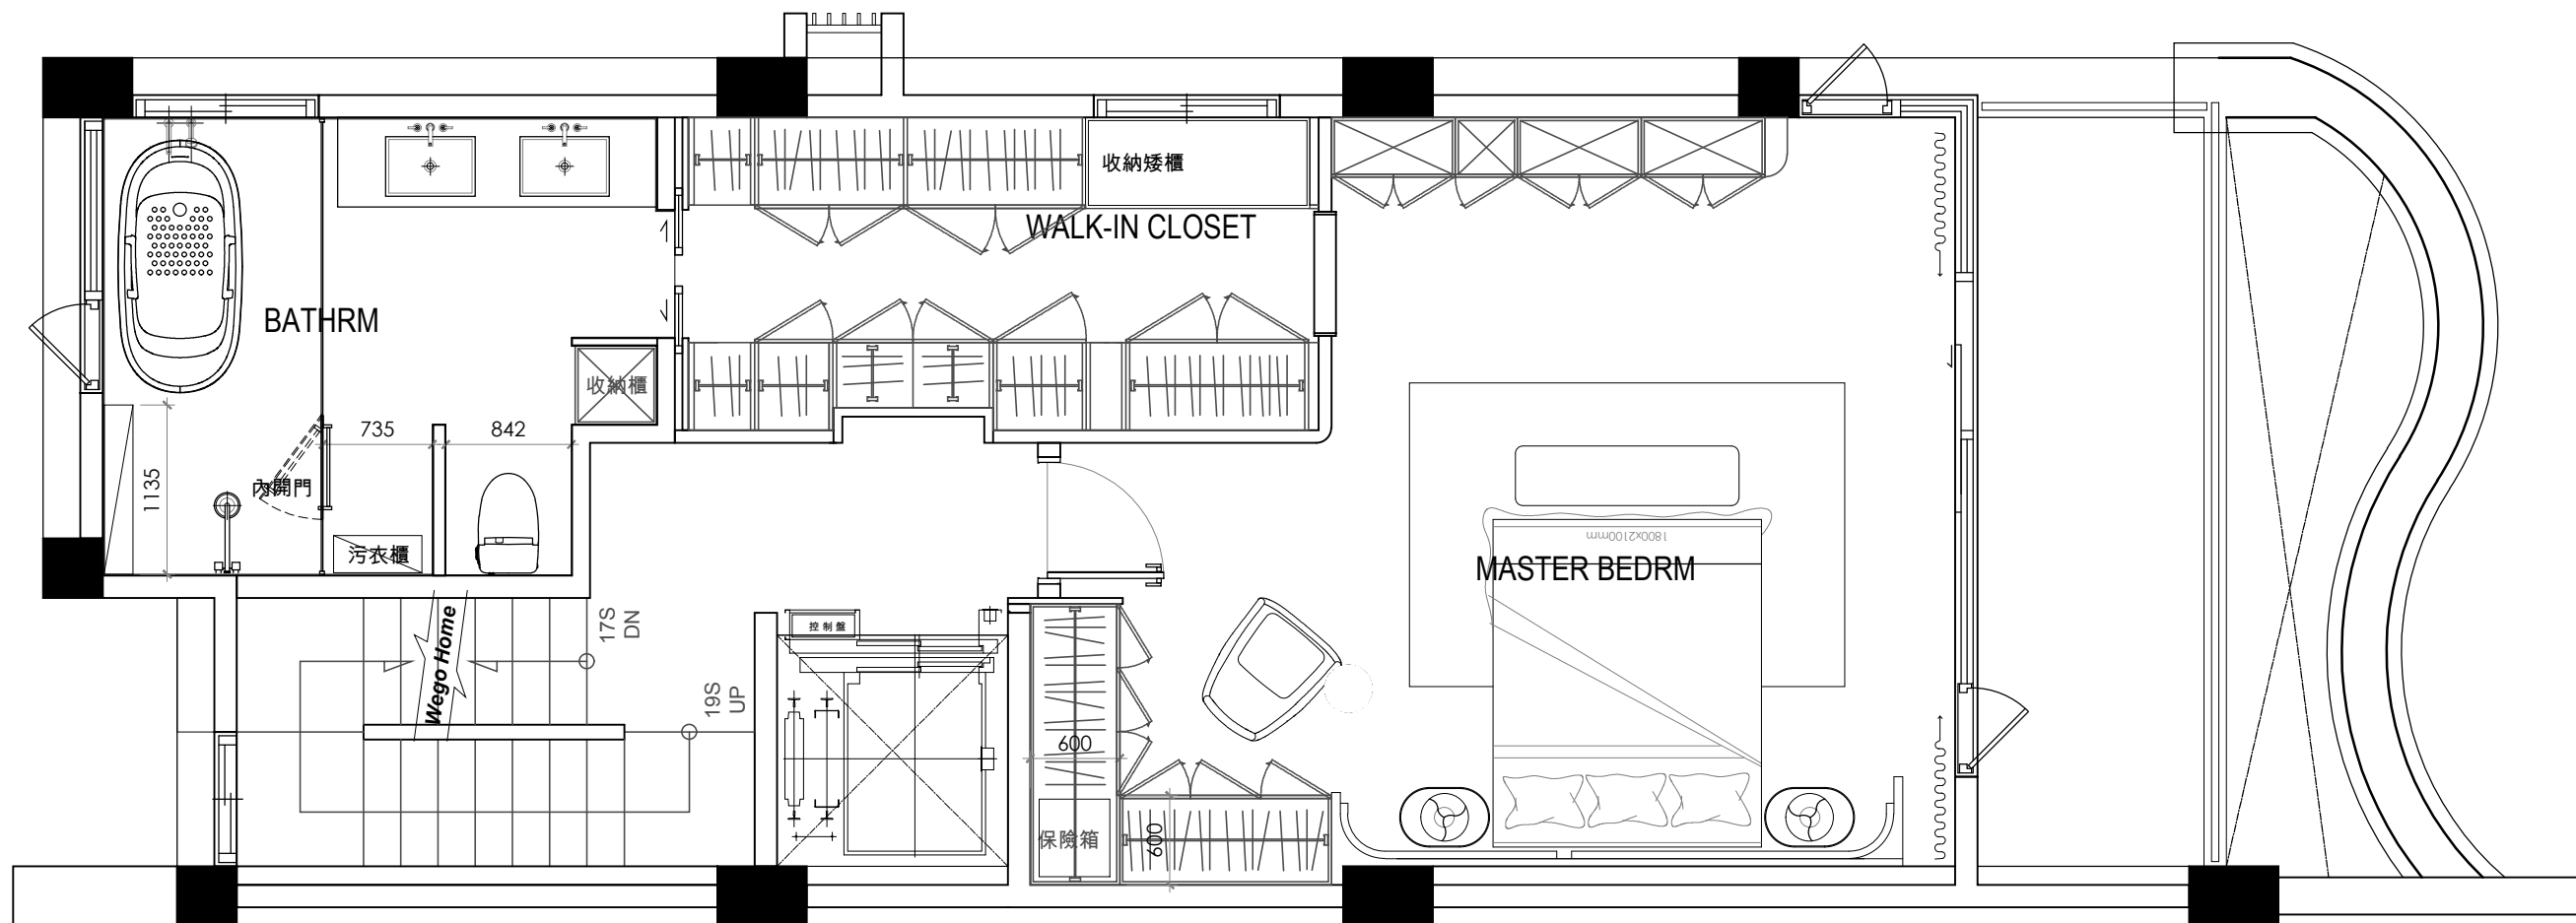


四層平面圖


牆 型 式	內 容	總 厚 度
	木作隔間牆	
	原有建築牆	154mm
	1/2B磚牆	120mm
	65mmC型骨架+單面(12mm石膏板+9mm矽酸鈣板),單面(12mm石膏板+9mm矽酸鈣板)	100mm
	65mmC型骨架+雙面矽酸鈣板	85mm

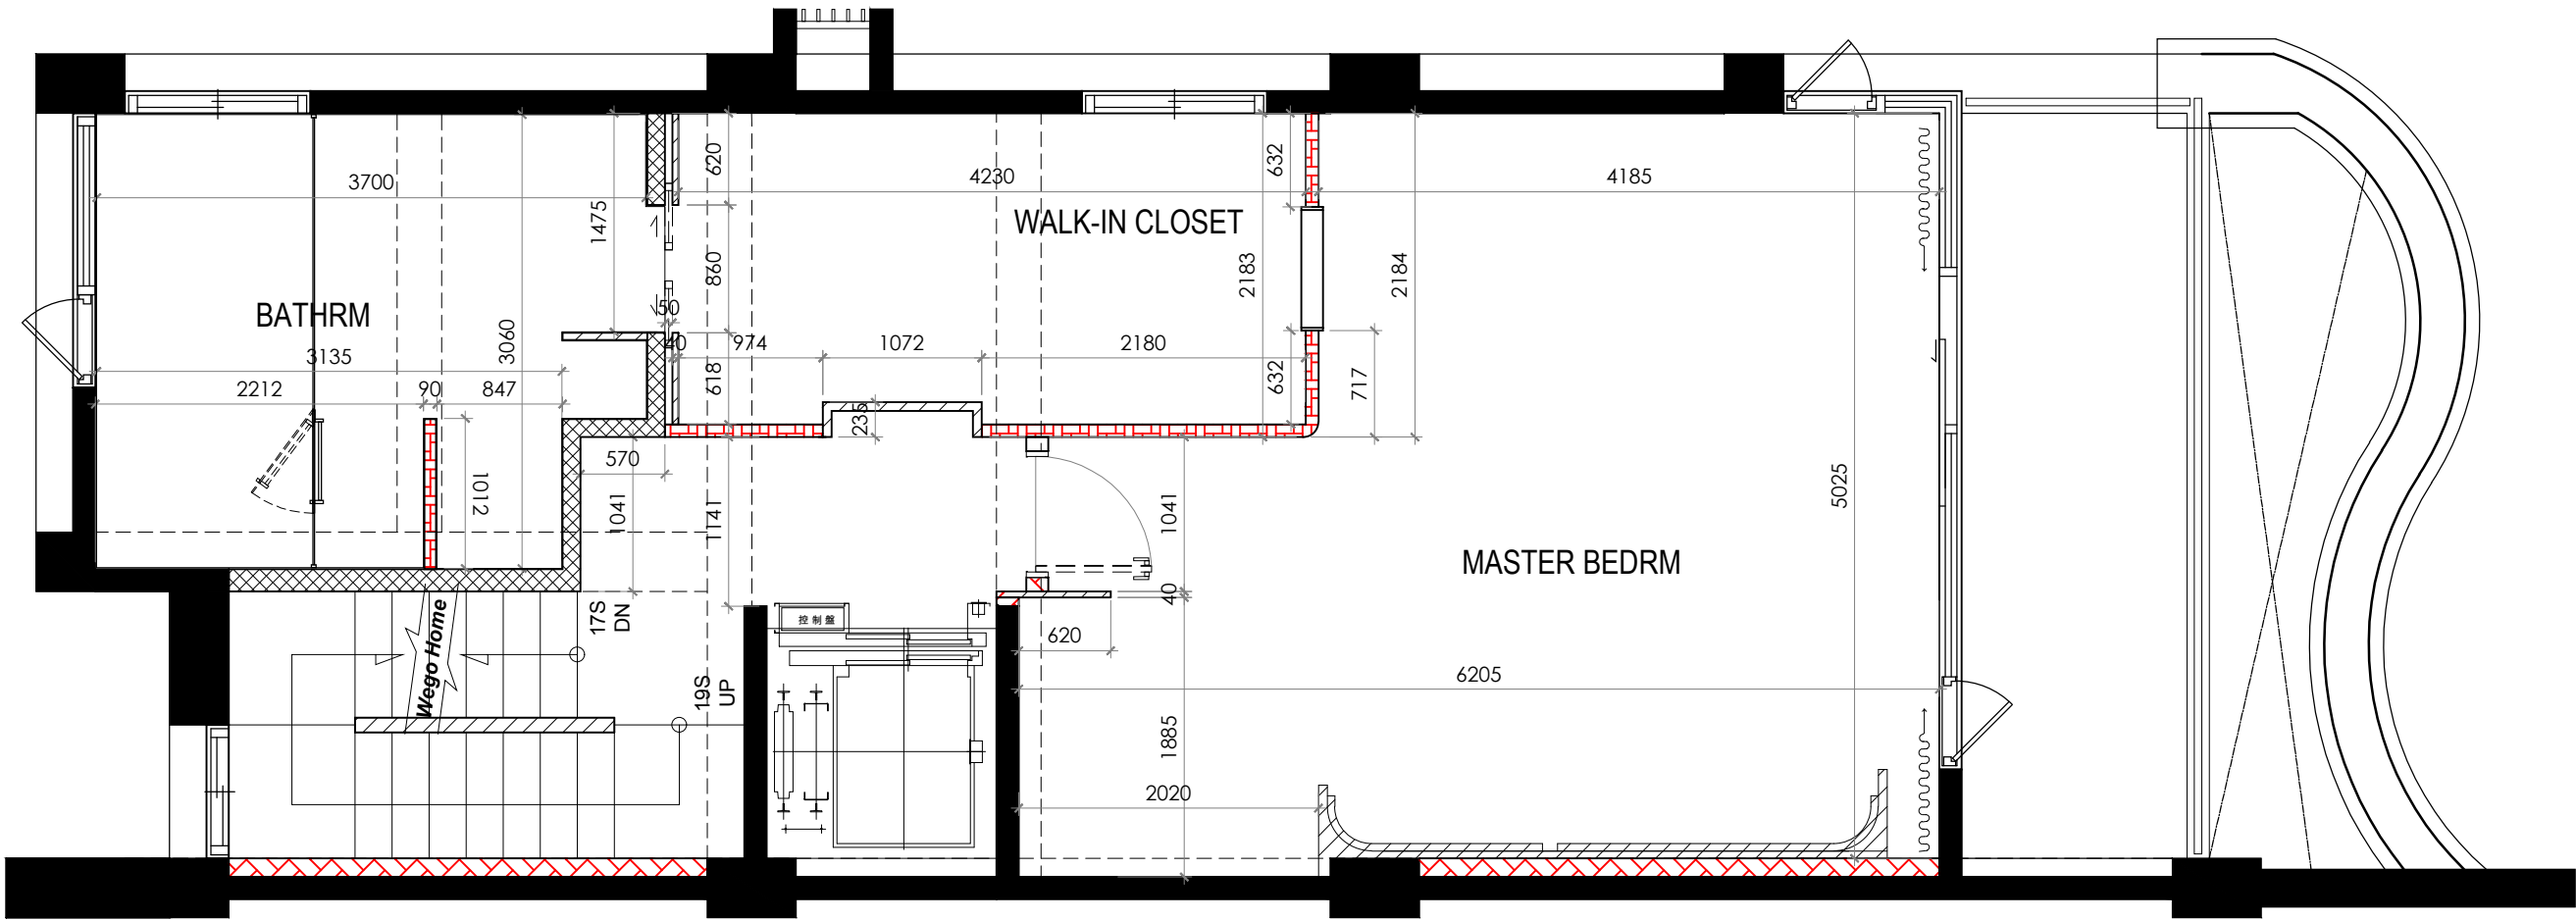


四層平面圖

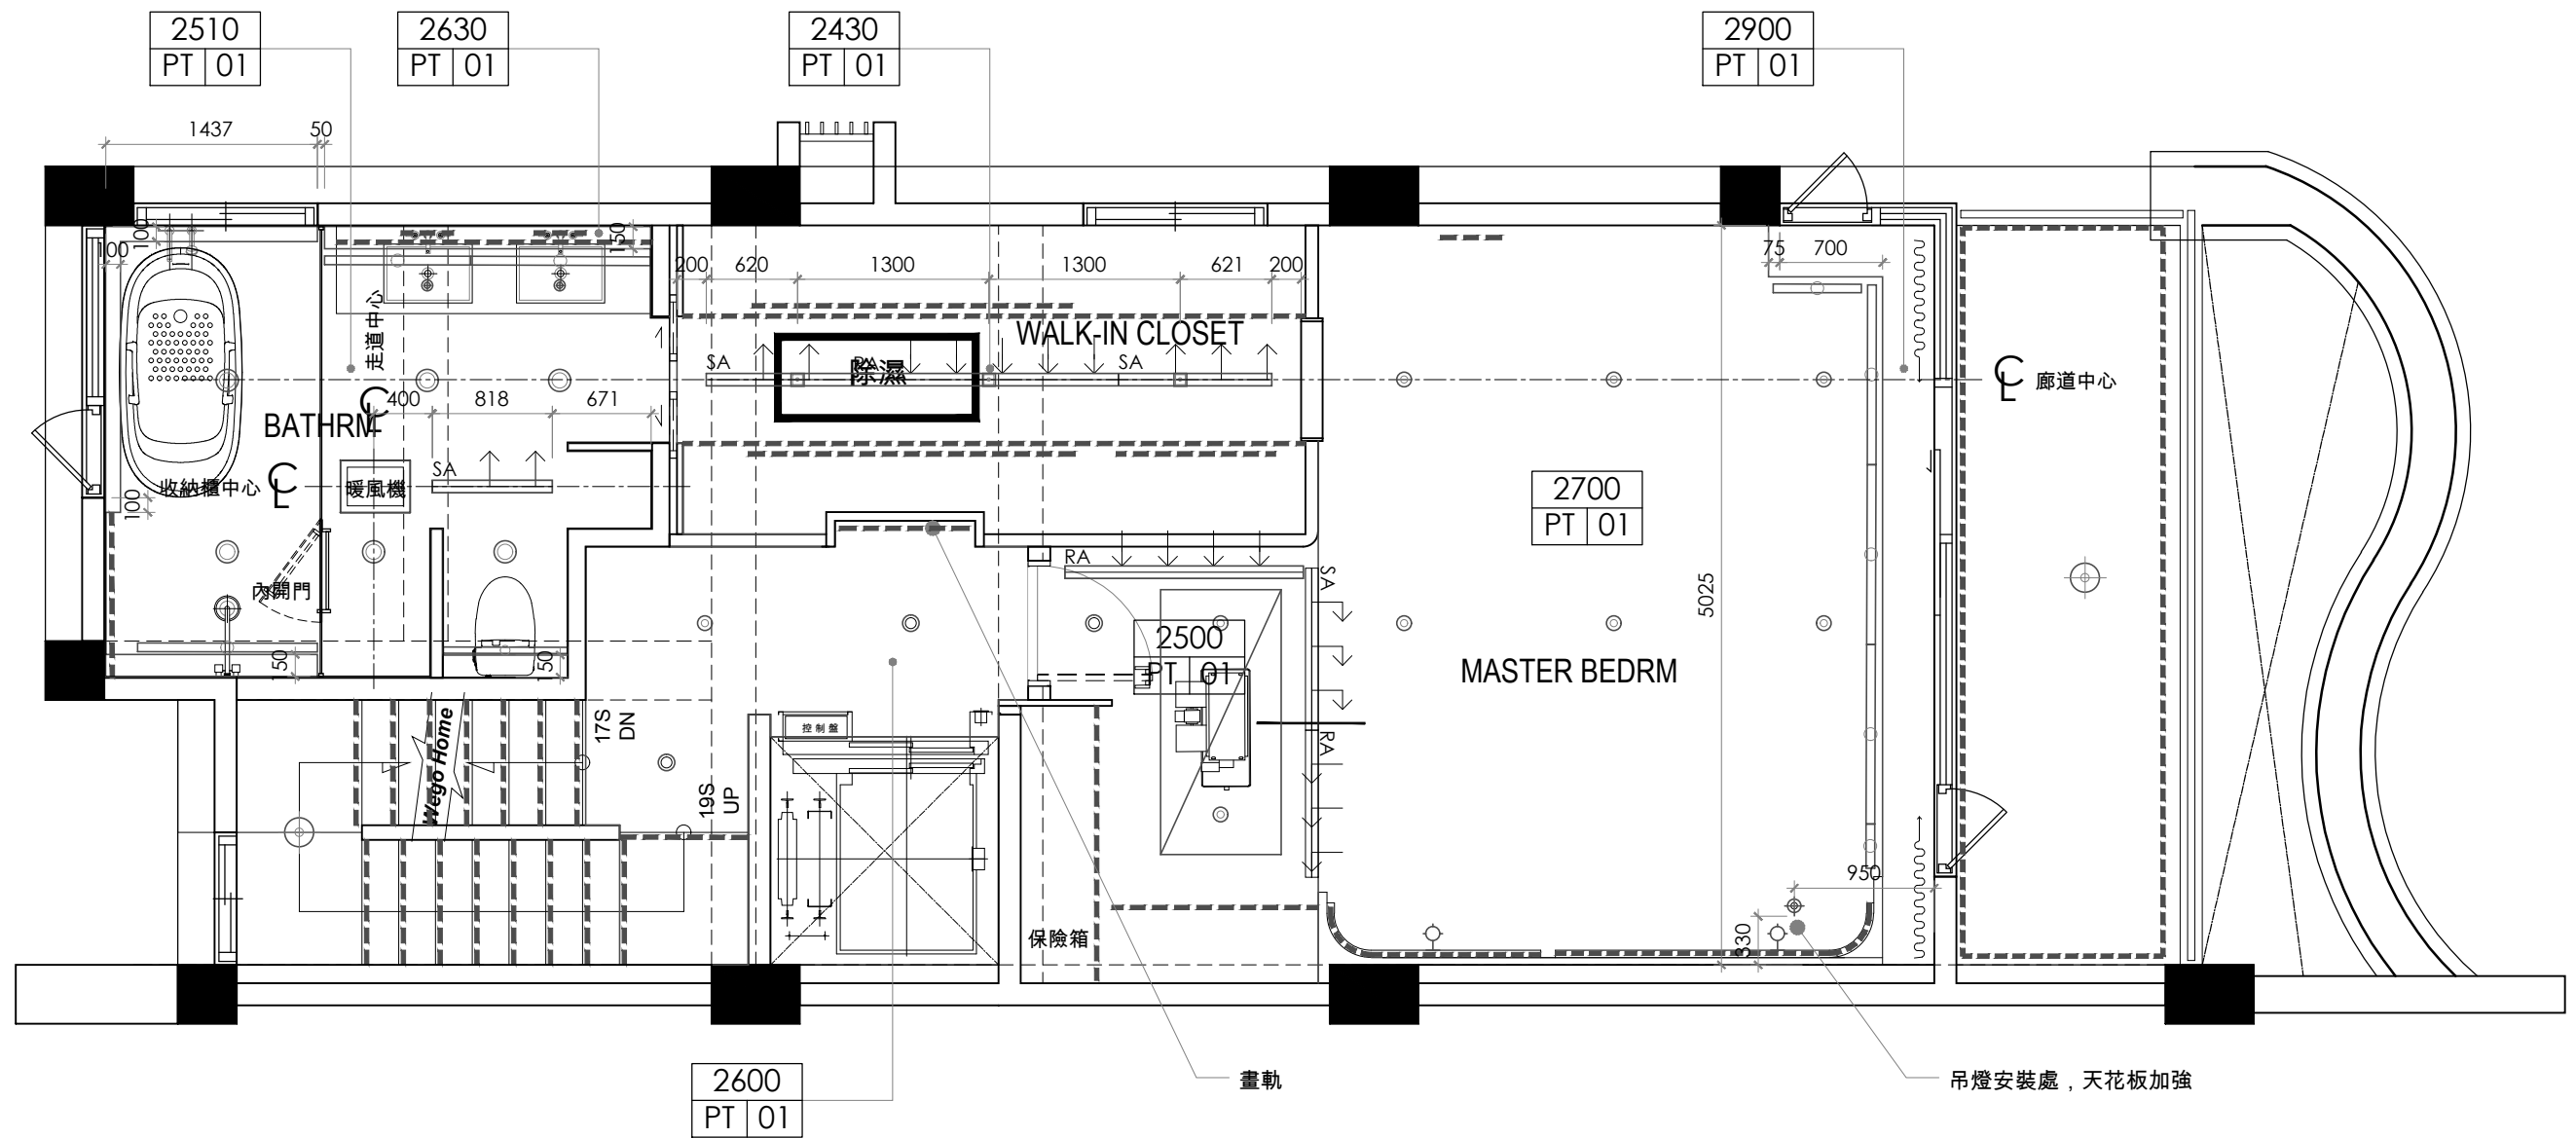

四層平面圖

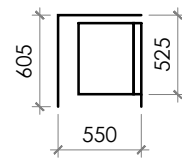


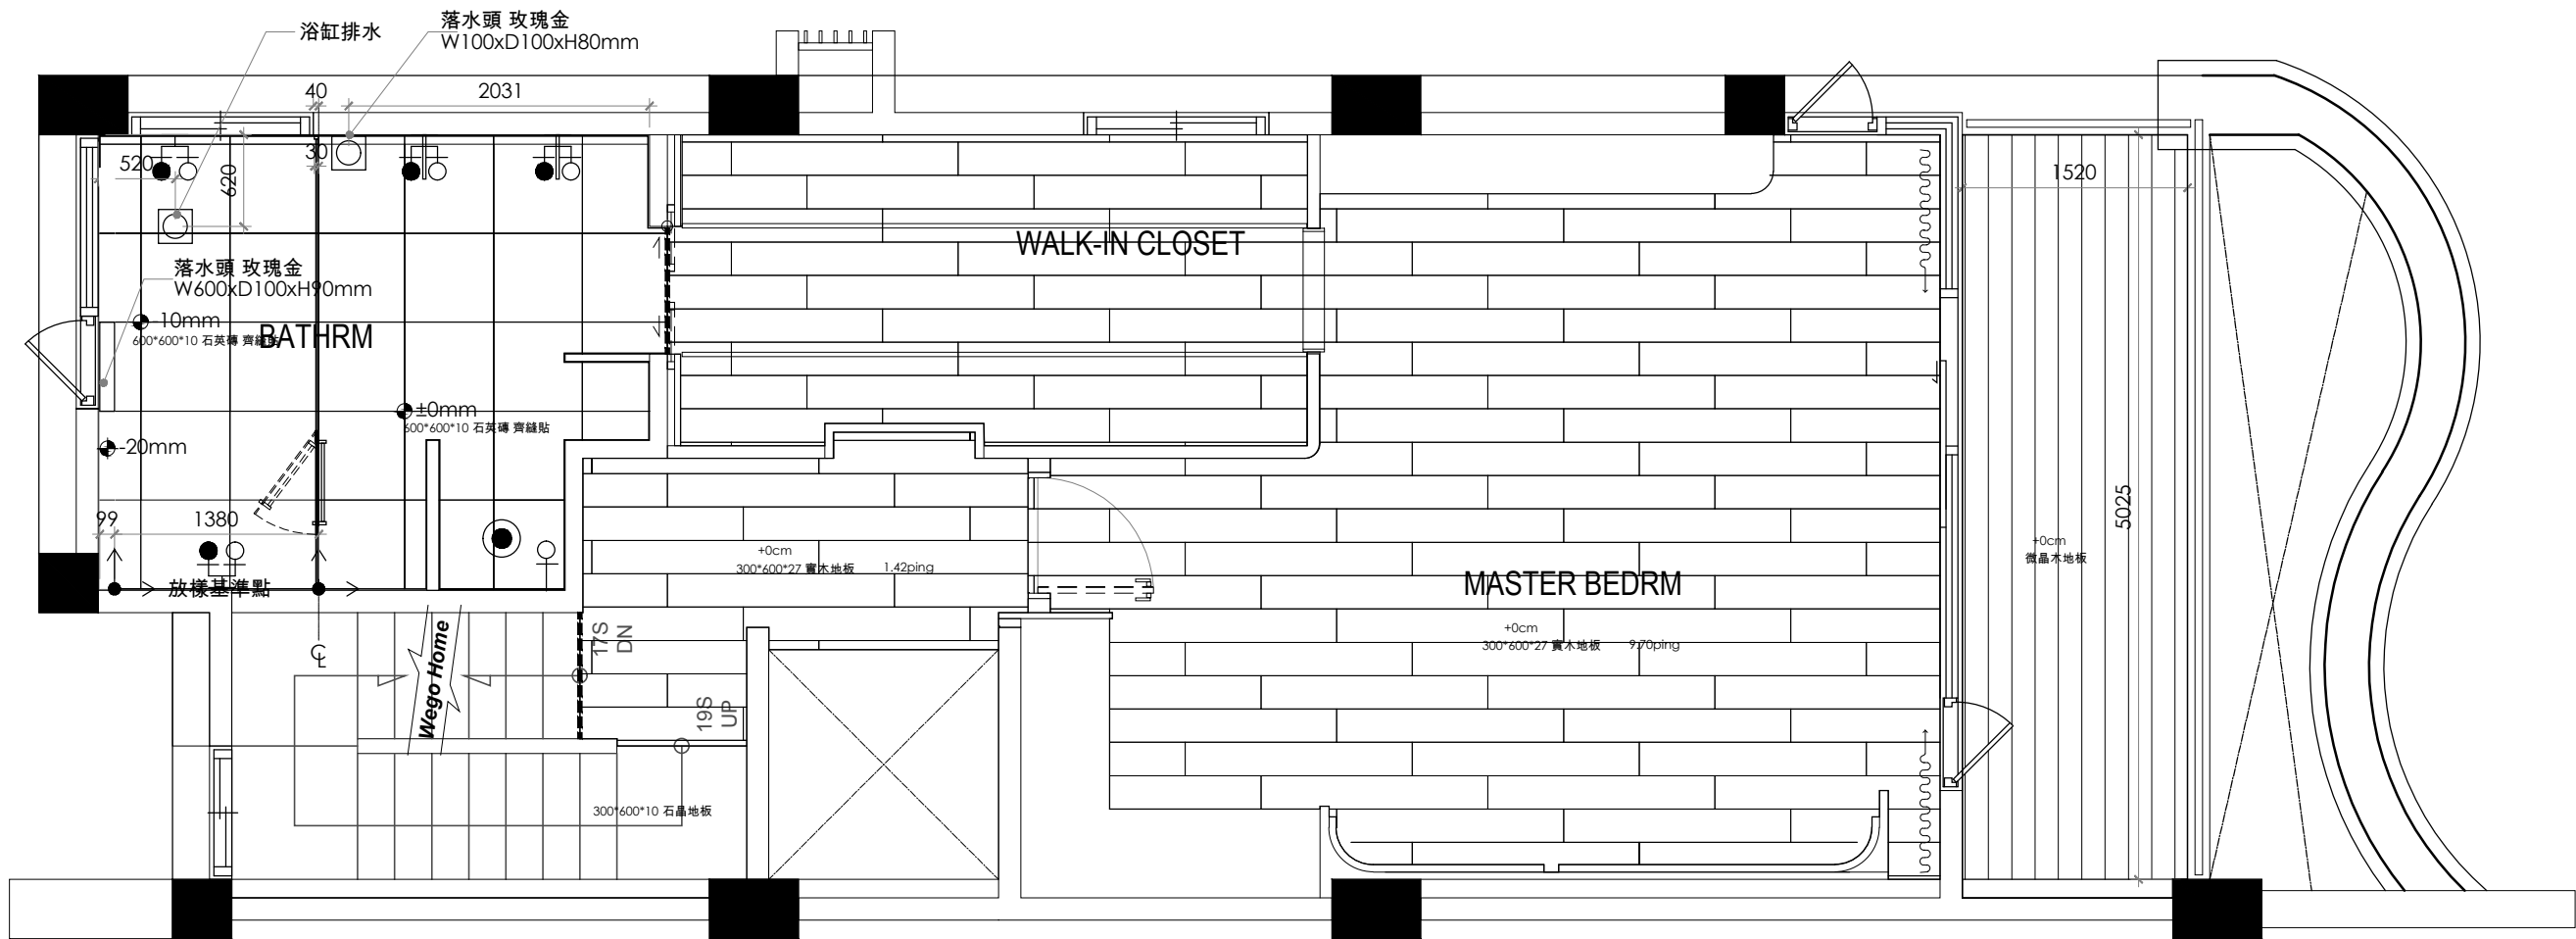

四層平面圖


編號	圖示	說明	尺寸	光源	備註
L1	●	舞光LED可調角度嵌燈	88mm Dia x H25mm	KW-303 / 8W / 3000k / 嵌孔75mm	
L2	●	2線式停電照明嵌燈	105mm Dia x H55mm	FH- 849-1B / 5W / 3000k / 嵌孔93mm	
L3	●	3線式停電照明嵌燈	105mm Dia x H55mm	FH- 849-1B / 5W / 3000k / 嵌孔93mm	
L4	⊕	LED 15W 小吸頂燈	82mm Dia x H78mm	3000k	
L5	●	舞光LED 邱比特軌道燈 白色	W88mm x L115mm x H50mm	AE-B07 / 7W / 3000k / 24°	
L6	●	超薄嵌入式感應式嵌燈	85mm Dia x H50mm	3000k / 嵌孔75mm	
L7	----	LED軟條燈		3000k	
L8	=====	軌道燈軌道	W34mm x H20mm		
L9	●	小型嵌燈	63mm Dia x H72mm	3000k / 嵌孔55mm	
L10	▢	無邊框可調角LED單燈盒燈	W99mm x L99mm x H85mm	FH- 829-11C /10W /30° / 3000K	
L11	▢	無邊框可調角LED雙燈盒燈	W99mm x L199mm x H85mm	FH- 829-12C /10W /30° / 3000K	
L12	---	磁吸式軌道燈			
L13	=====	防塵防濕T5燈具			
L14	●	上照LED埋地燈	42mm Dia. x H90mm	LED /3W /12° /12V /3000K / 700mA	
DL-1	◆	吊燈			
DL-2	⊙	壁燈			

燈具規格最後確認。
*燈具供電皆為220V.

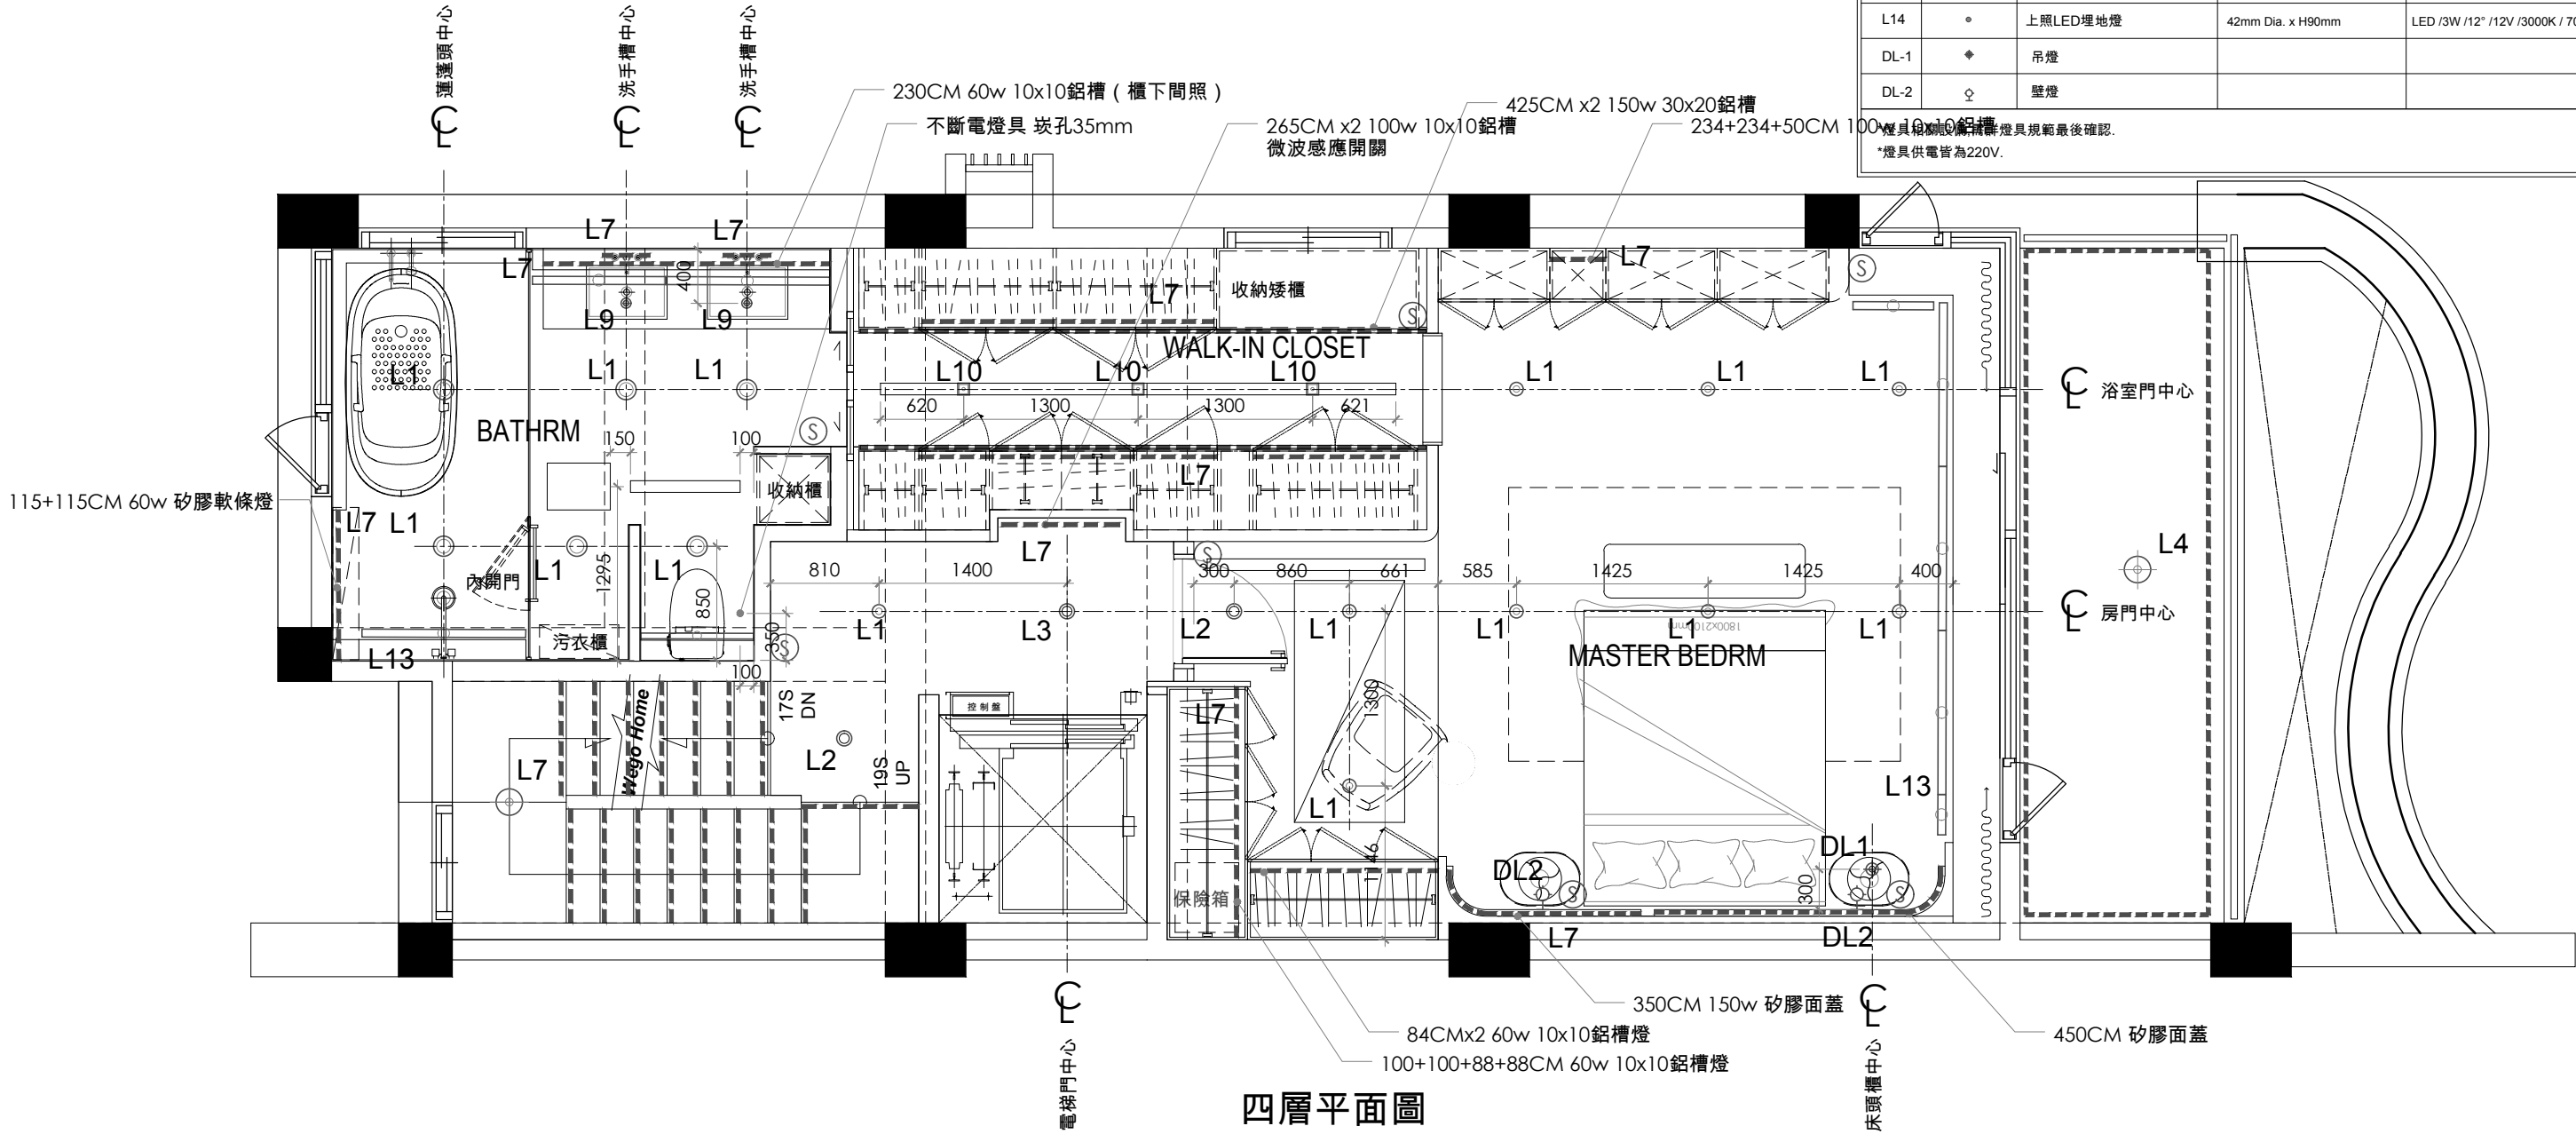


四層平面圖

弱電設備圖例說明					
圖 例	說 明	數 量	圖 例	說 明	數 量
	插座(110V雙插座)			HDMI插座	
	插座(220V雙插座)			音響出線	
	地板插座(110V雙插座)			電源出線口	
	不斷電插座(110V雙插座)			地板電源出線	
	獨立電源			空調開關	
	電話插座(大樓)			勿干擾顯示器.門鈴	
	掛壁式電話插座(內線)			對講機	
	電話插座(內線)			門上感應器(鈴聲)	
	大門陽極鎖控制按鈕			門禁刷卡器	
	電視插座			天花板鈴聲器	
	資訊插座			配電盤	
	燈具開關			消防箱	
	調光開關			緊急壓扣	
備註	1.插座.燈具出線口詳細位置尺寸.高度詳裝修圖。 2.所有壁面插座.除特別標示高度者之外.中心點一律離地完成面+300AFF。 3.所有壁面開關.除特別標示高度者之外.中心點一律離地完成面+1200AFF。 4.所有配管.線均由平頂天花配置。 5.影音視聽系統所需弱電設備，由影音視聽系統廠商規劃後.提供圖面予業主審核。				

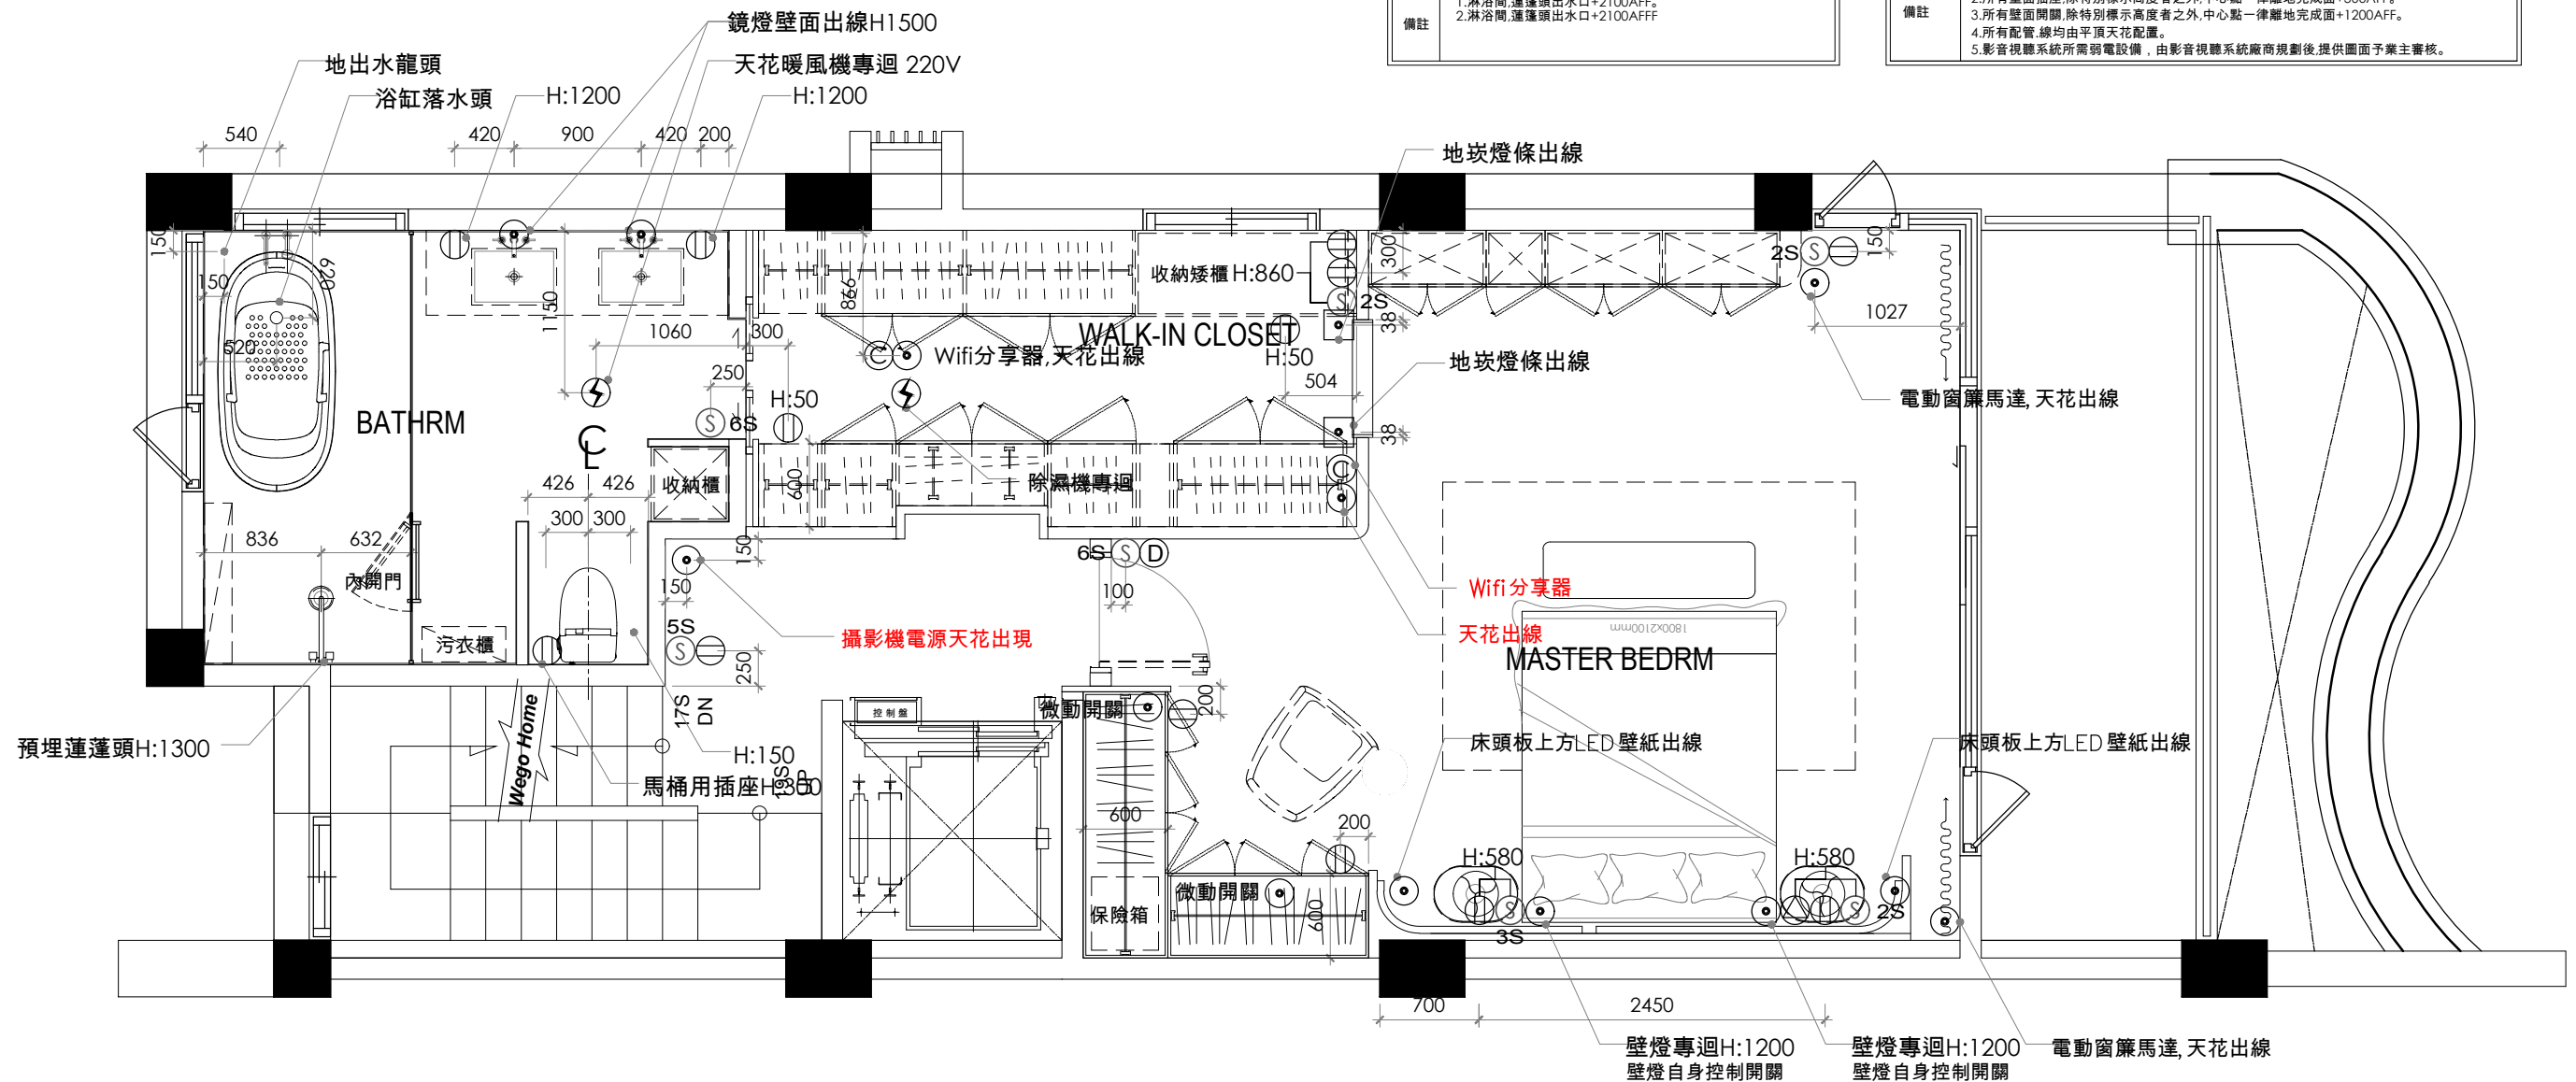

編號	圖示	說明	尺寸	光源	備註
L1	●	舞光LED可調角度嵌燈	88mm Dia x H25mm	KW-303 / 8W / 3000k / 嵌孔75mm	
L2	●	2線式停電照明嵌燈	105mm Dia x H55mm	FH- 849-1B / 5W / 3000k / 嵌孔93mm	
L3	●	3線式停電照明嵌燈	105mm Dia x H55mm	FH- 849-1B / 5W / 3000k / 嵌孔93mm	
L4	⊕	LED 15W 小吸頂燈	82mm Dia x H78mm	3000k	
L5	●	舞光LED 邱比特軌道燈 白色	W88mm x L115mm x H50mm	AE-B07 / 7W / 3000k / 24°	
L6	●	超薄嵌入式感應式嵌燈	85mm Dia x H50mm	3000k / 嵌孔75mm	
L7	-----	LED軟條燈		3000k	
L8	=====	軌道燈軌道	W34mm x H20mm		
L9	●	小型嵌燈	63mm Dia x H72mm	3000k / 嵌孔55mm	
L10	■	無邊框可調角LED單燈盒燈	W99mm x L99mm x H85mm	FH- 829-11C /10W /30° / 3000K	
L11	■	無邊框可調角LED雙燈盒燈	W99mm x L199mm x H85mm	FH- 829-12C /10W /30° / 3000K	
L12	- · - · -	磁吸式軌道燈			
L13	——○——	防塵防濕T5燈具			
L14	●	上照LED埋地燈	42mm Dia. x H90mm	LED /3W /12° /12V /3000K / 700mA	
DL-1	◆	吊燈			
DL-2	◇	壁燈			


*燈具相關設備,需詳燈具規範最後確認。
*燈具供電皆為220V。

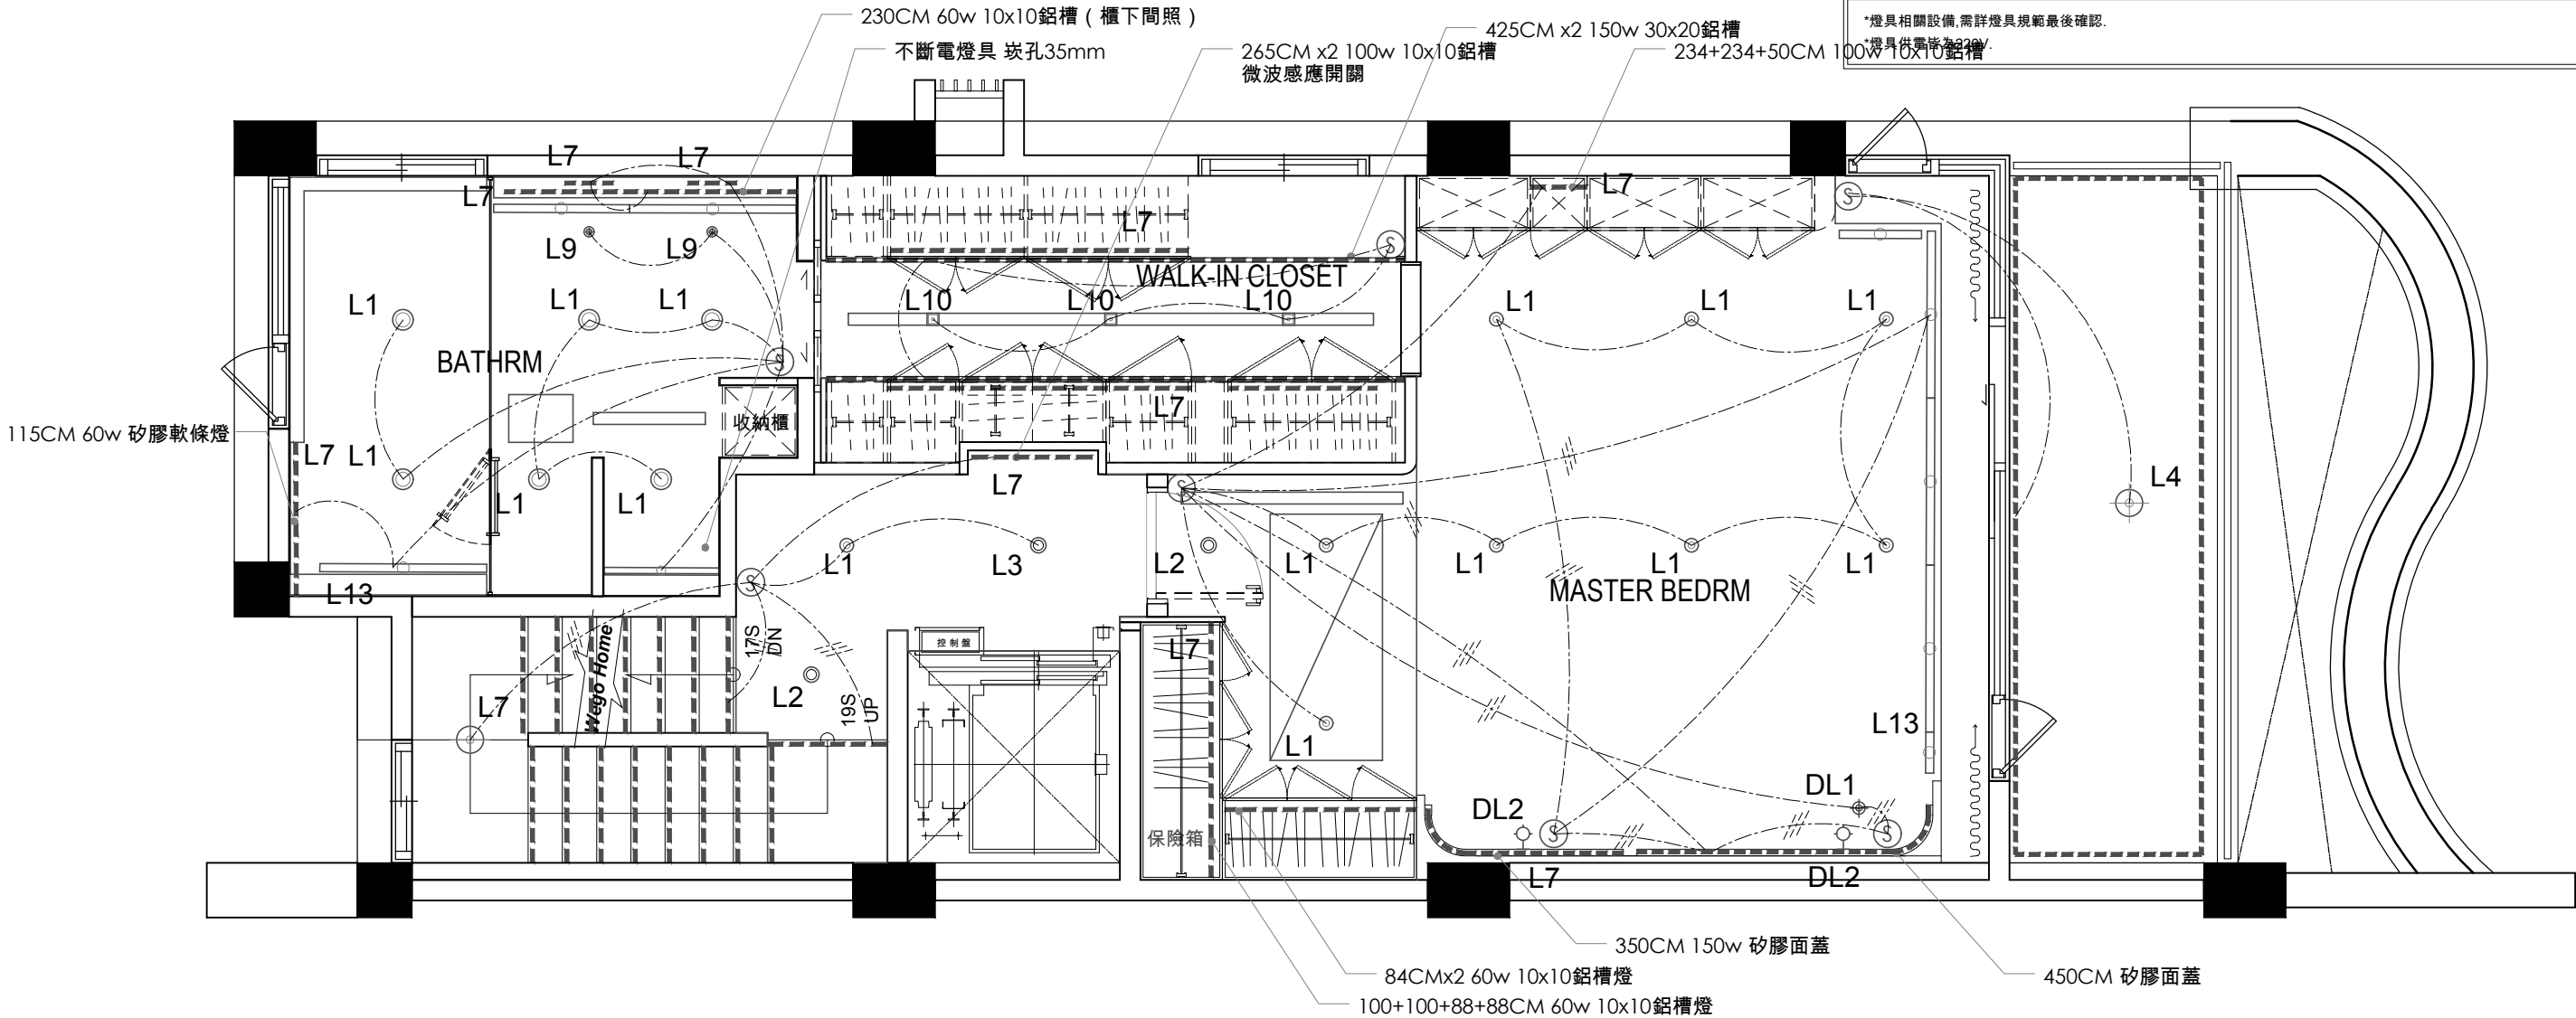


四層平面圖

編號	圖示	說明	尺寸	光源	備註
L1		舞光LED可調角度嵌燈	88mm Dia x H25mm	KW-303 / 8W / 3000k / 嵌孔75mm	
L2		2線式停電照明嵌燈	105mm Dia x H55mm	FH- 849-1B / 5W / 3000k / 嵌孔93mm	
L3		3線式停電照明嵌燈	105mm Dia x H55mm	FH- 849-1B / 5W / 3000k / 嵌孔93mm	
L4		LED 15W 小吸頂燈	82mm Dia x H78mm	3000k	
L5		舞光LED 邱比特軌道燈 白色	W88mm x L115mm x H50mm	AE-B07 / 7W / 3000k / 24°	
L6		超薄嵌入式感應式嵌燈	85mm Dia x H50mm	3000k / 嵌孔75mm	
L7		LED軟條燈		3000k	
L8		軌道燈軌道	W34mm x H20mm		
L9		小型嵌燈	63mm Dia x H72mm	3000k / 嵌孔55mm	
L10		無邊框可調角LED單燈盒燈	W99mm x L99mm x H85mm	FH- 829-11C /10W /30° / 3000K	
L11		無邊框可調角LED雙燈盒燈	W99mm x L199mm x H85mm	FH- 829-12C /10W /30° / 3000K	
L12		磁吸式軌道燈			
L13		防塵防濕T5燈具			
L14		上照LED埋地燈	42mm Dia. x H90mm	LED /3W /12° /12V /3000K / 700mA	
DL-1		吊燈			
DL-2		壁燈			
*燈具相關設備,需詳燈具規範最後確認。 *燈具供電皆為220V.					


空調設備圖例說明			
圖 例	說 明	圖 例	說 明
	側吹出風口		出風口
	側吹回風口		除濕 吊隱式除濕主機
	下吹出風口		五合一暖風機
	下吹回風口		全熱交換 全熱交換器

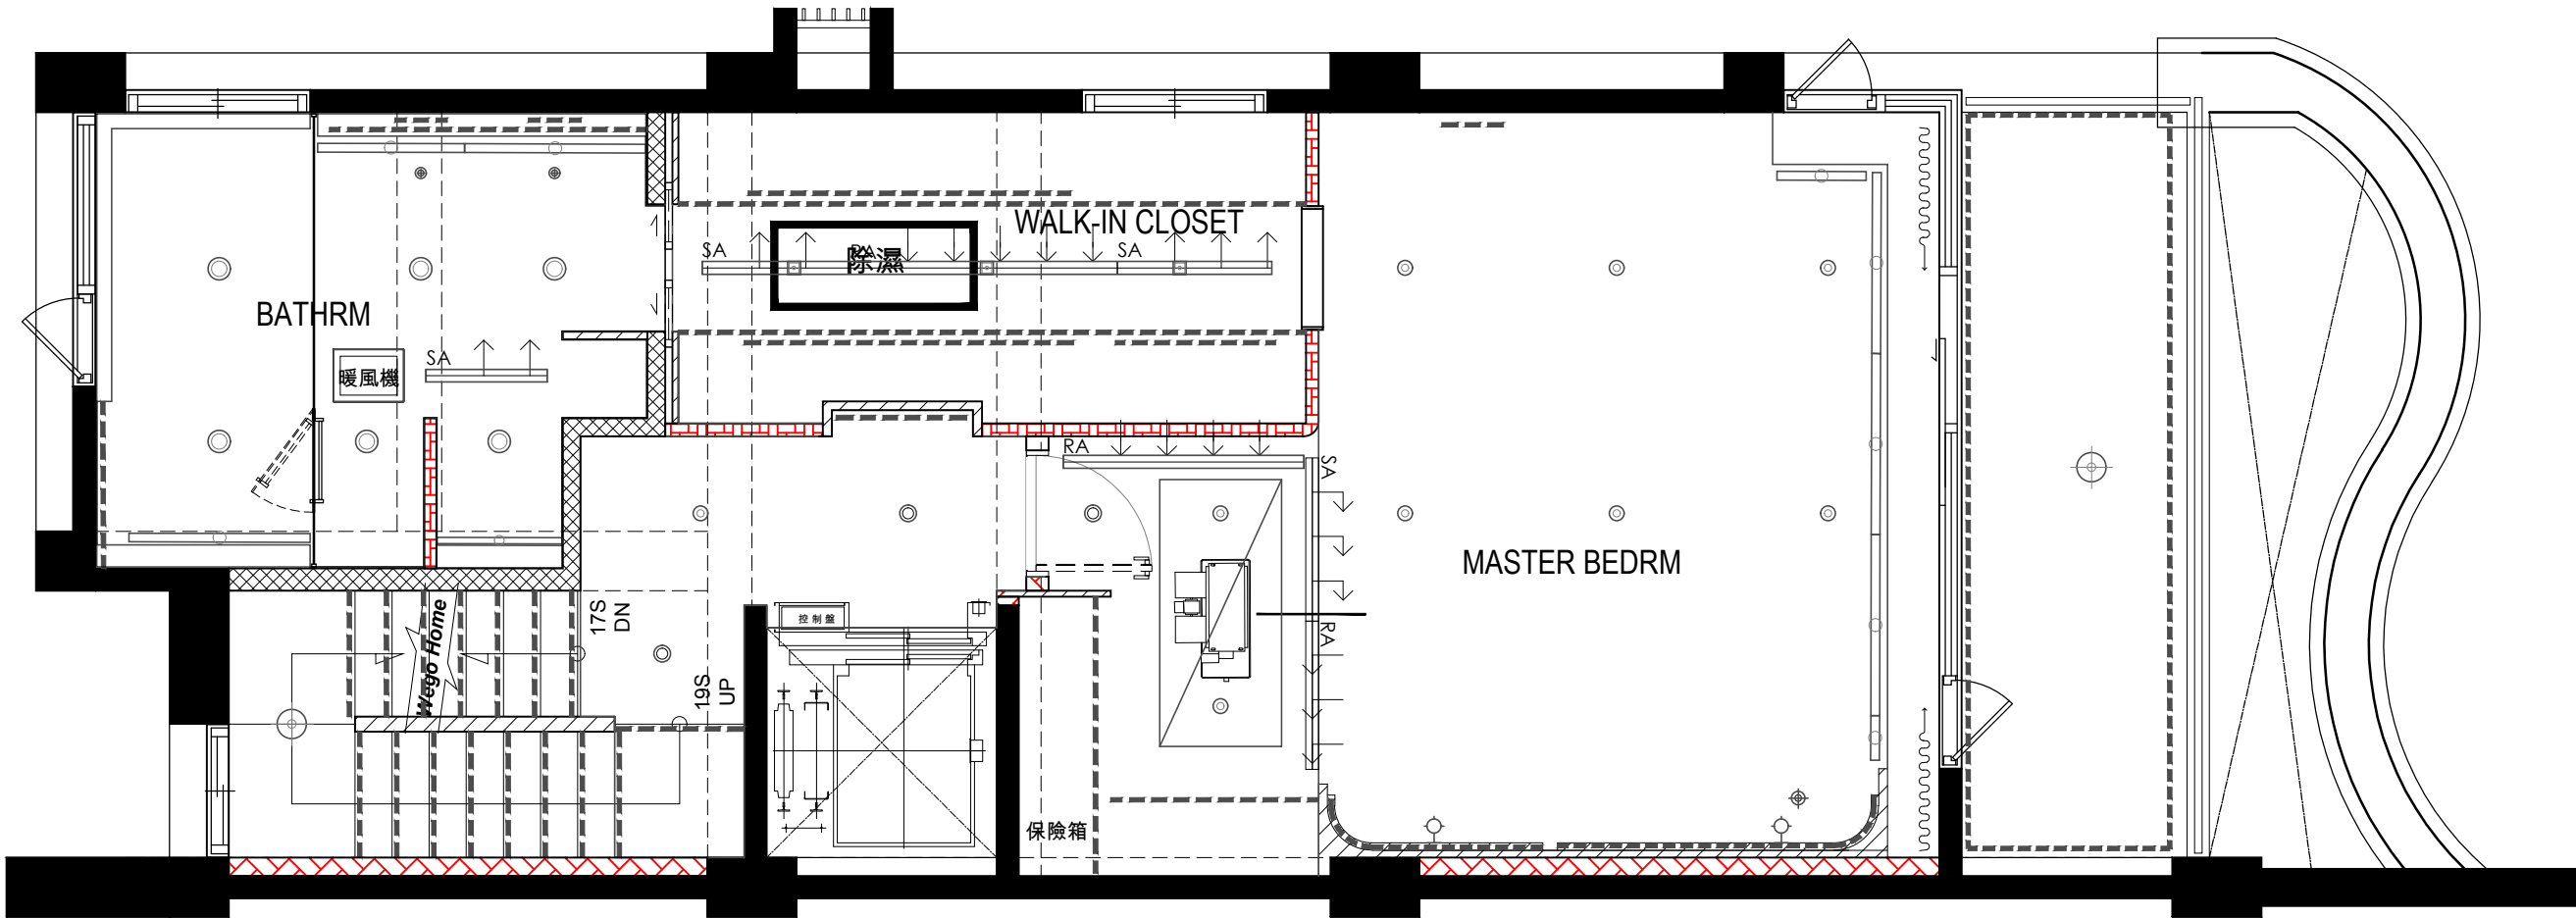


四層平面圖

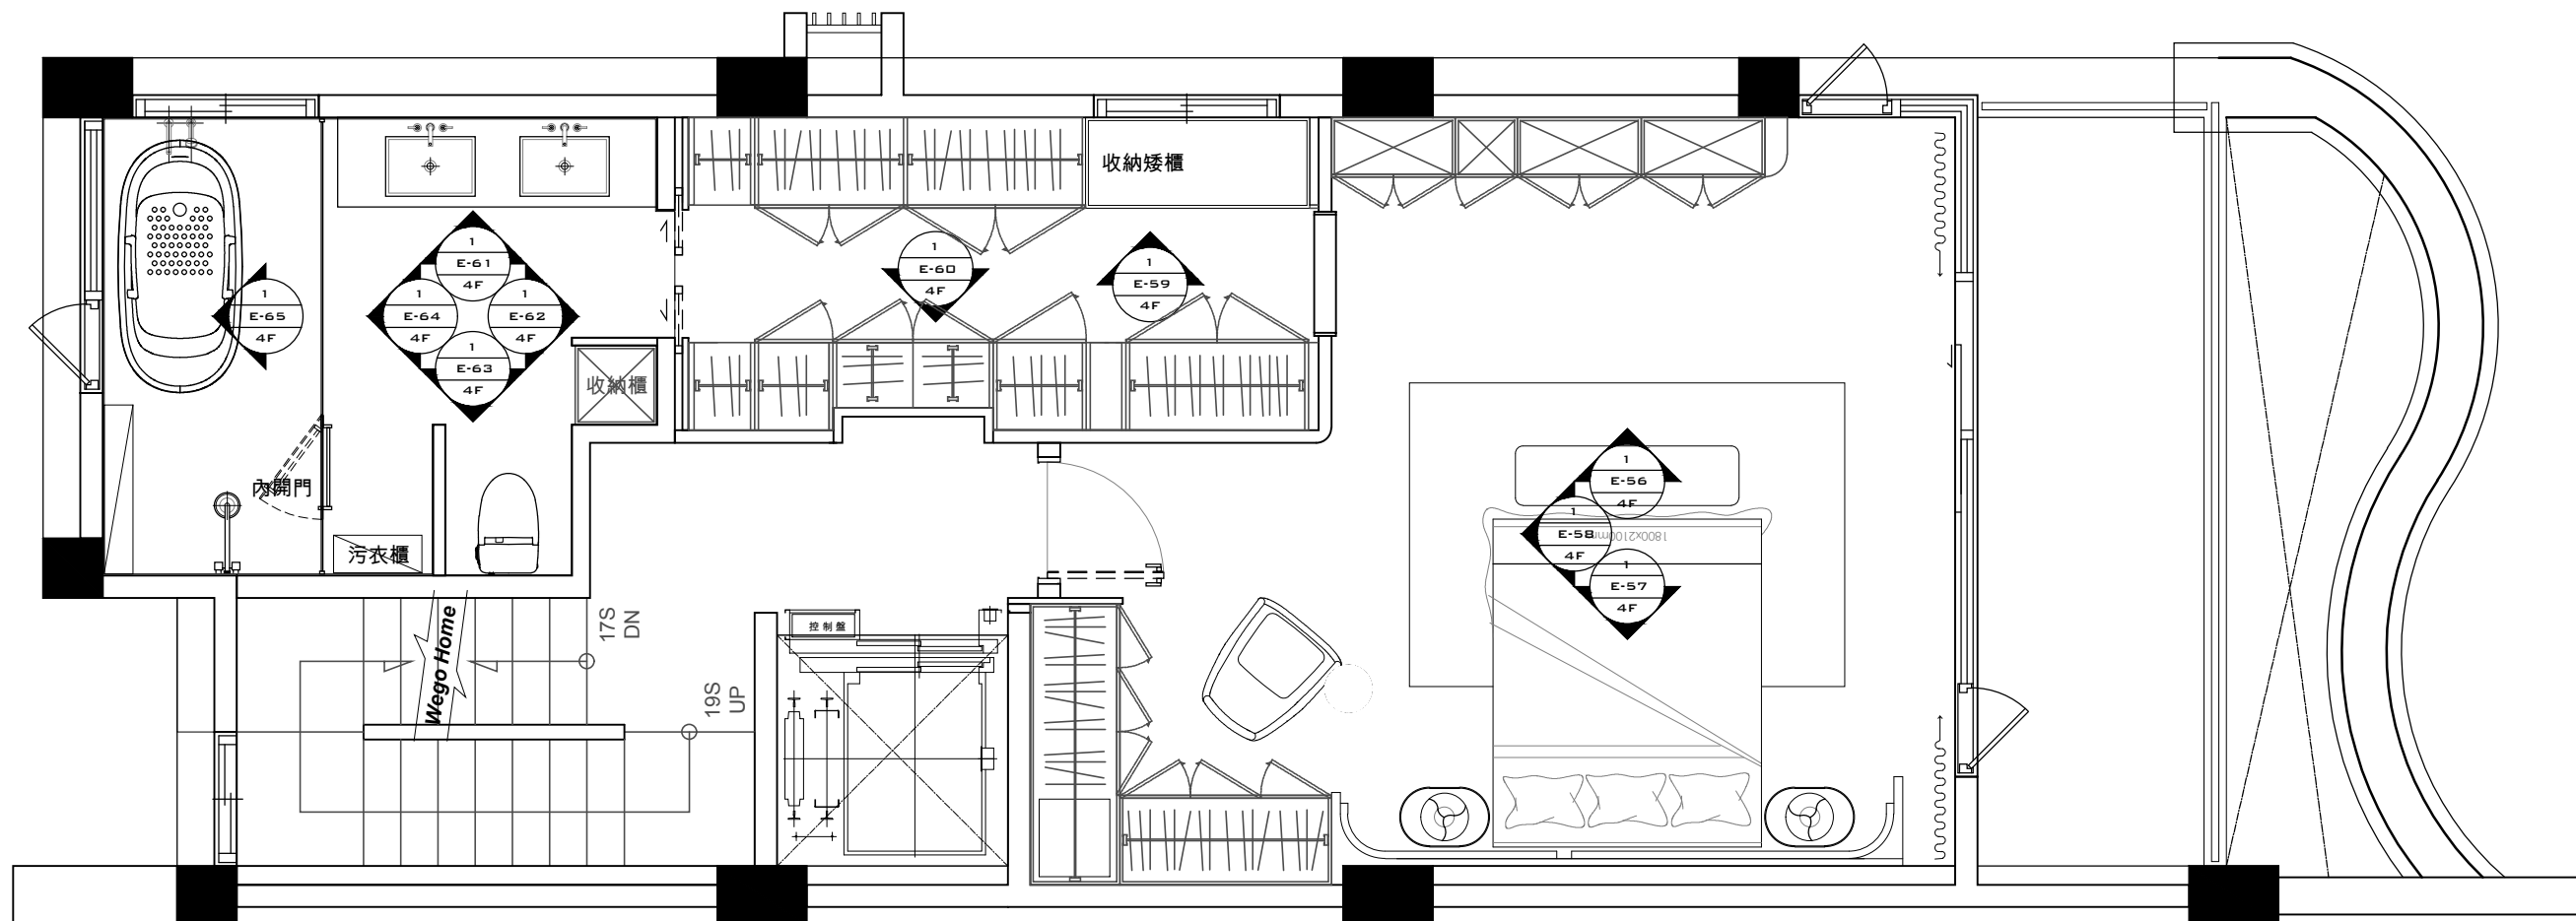

四層平面圖

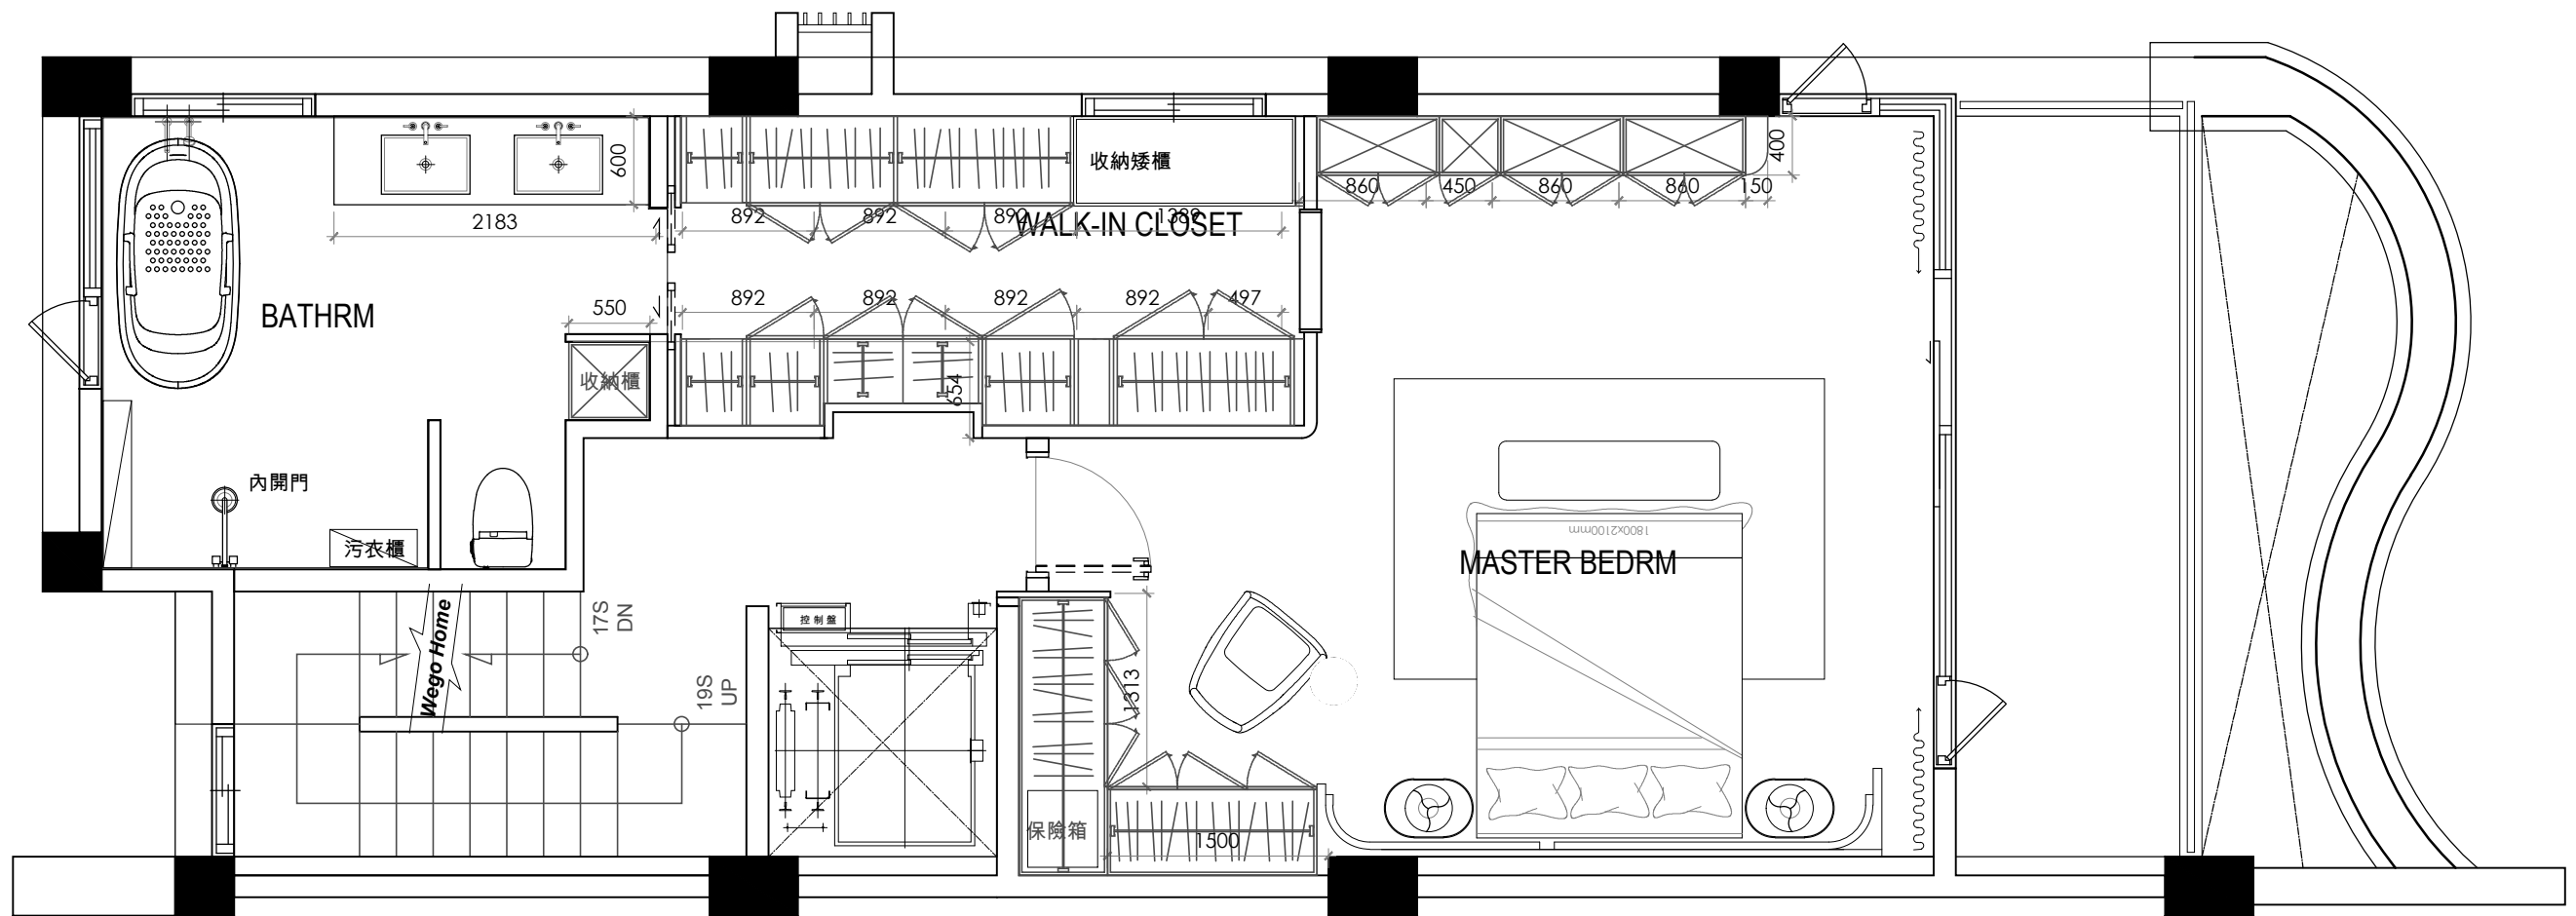


四層平面圖

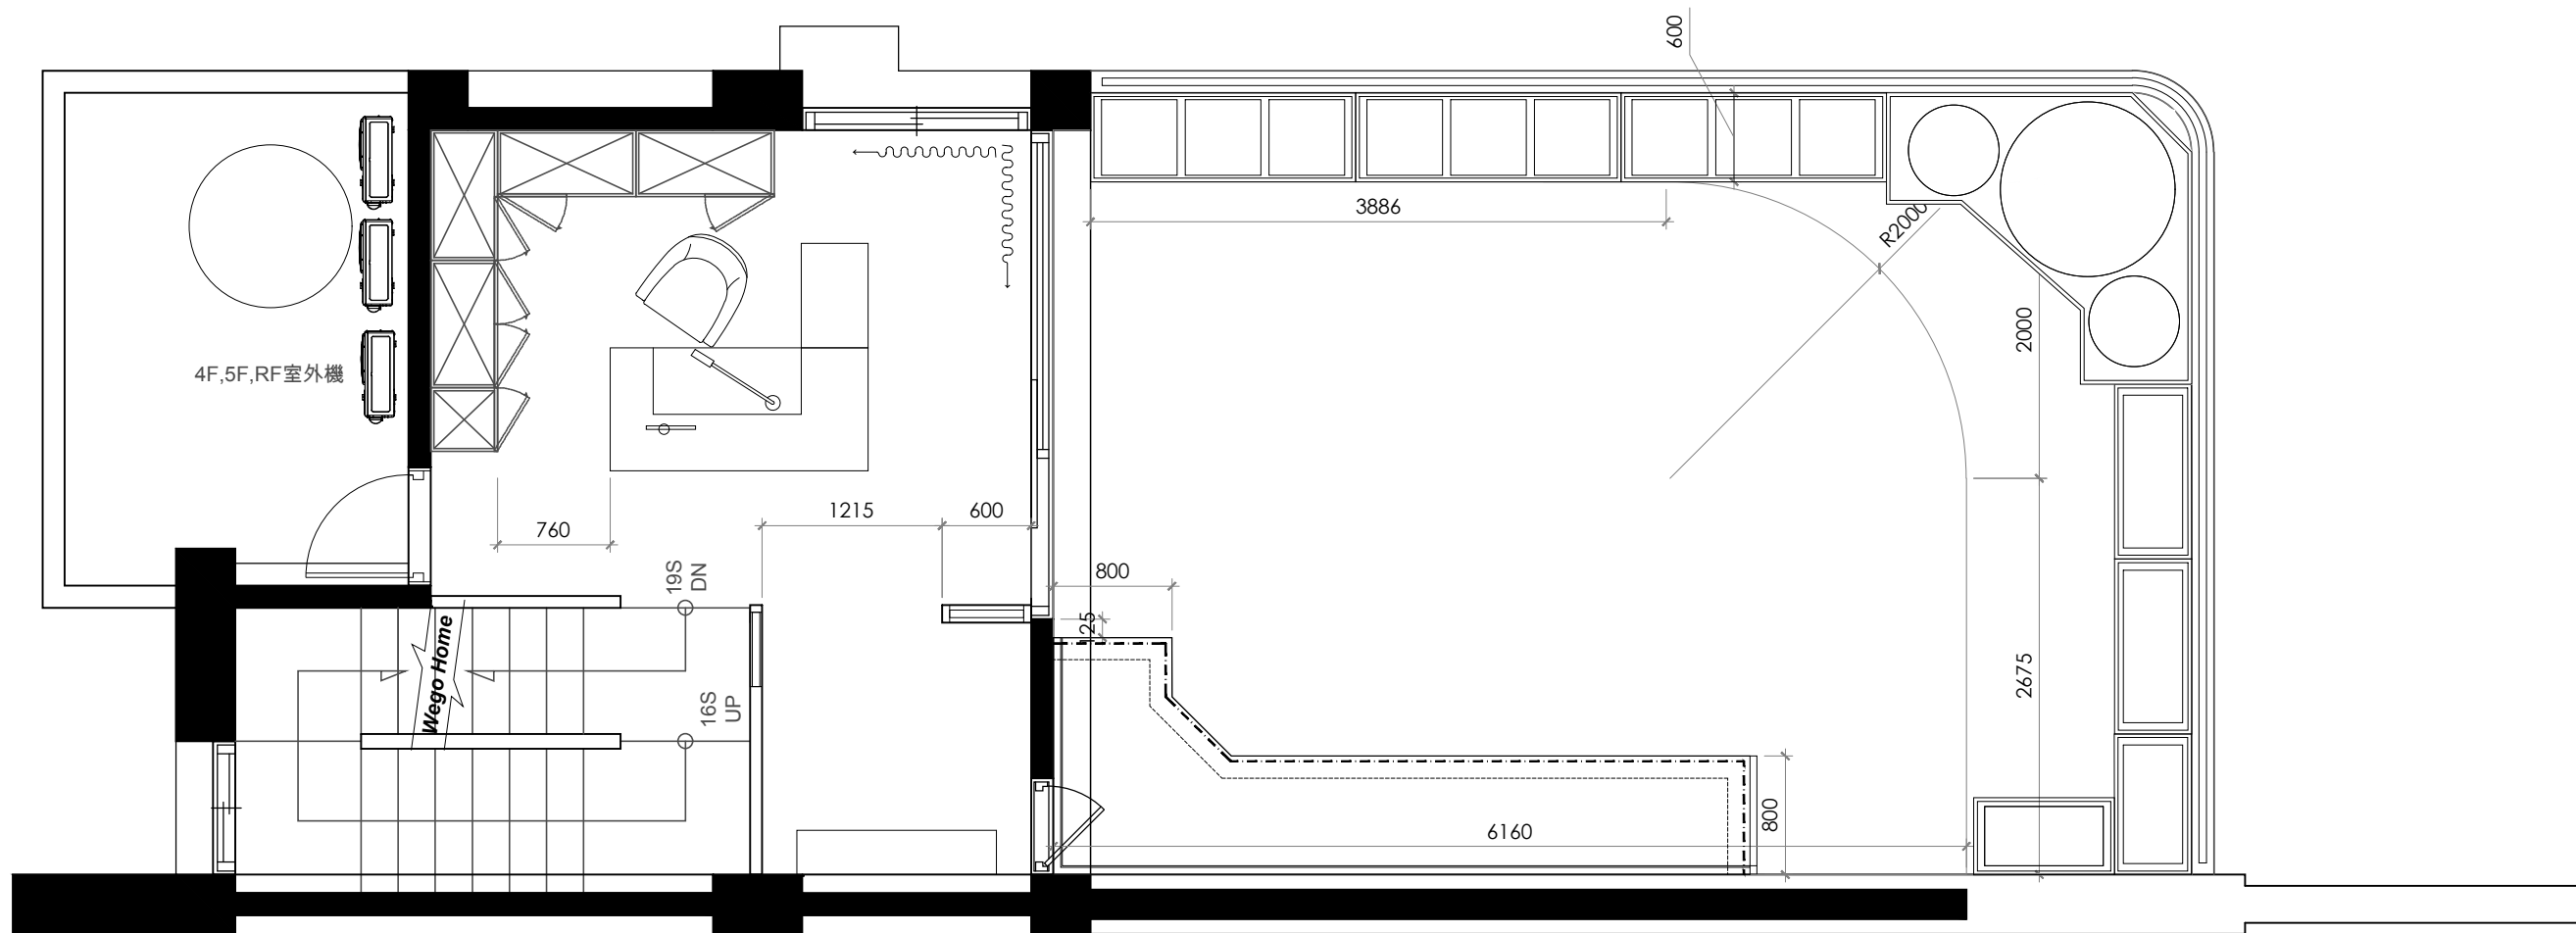


突一層平面圖

牆 型 式	內 容	總 厚 度
	木作隔間牆	
	原有建築牆	154mm
	1/2B磚牆	120mm
	65mmC型骨架+單面(12mm石膏板+9mm矽酸鈣板),單面(12mm石膏板+9mm矽酸鈣板)	100mm
	65mmC型骨架+雙面矽酸鈣板	85mm

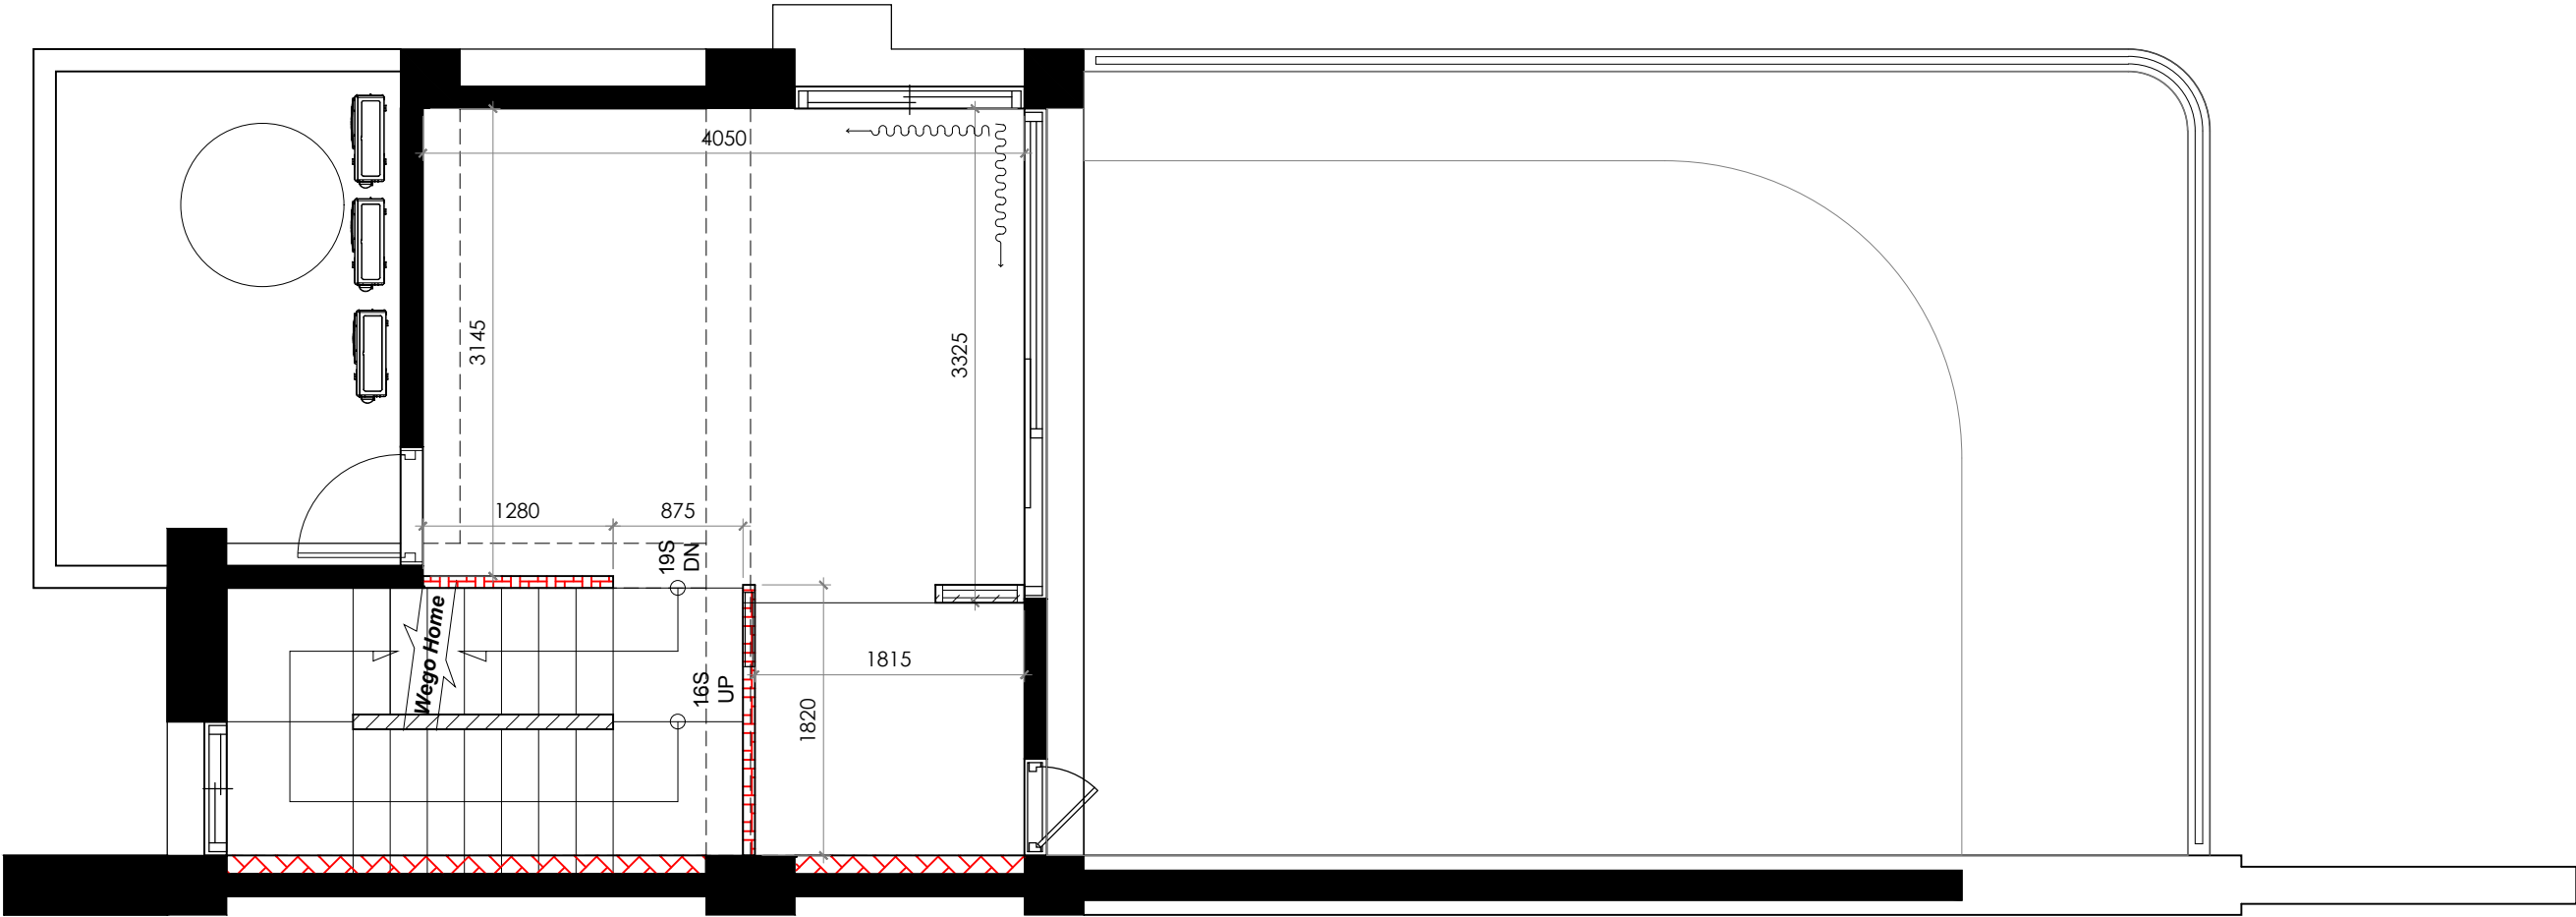


突一層平面圖

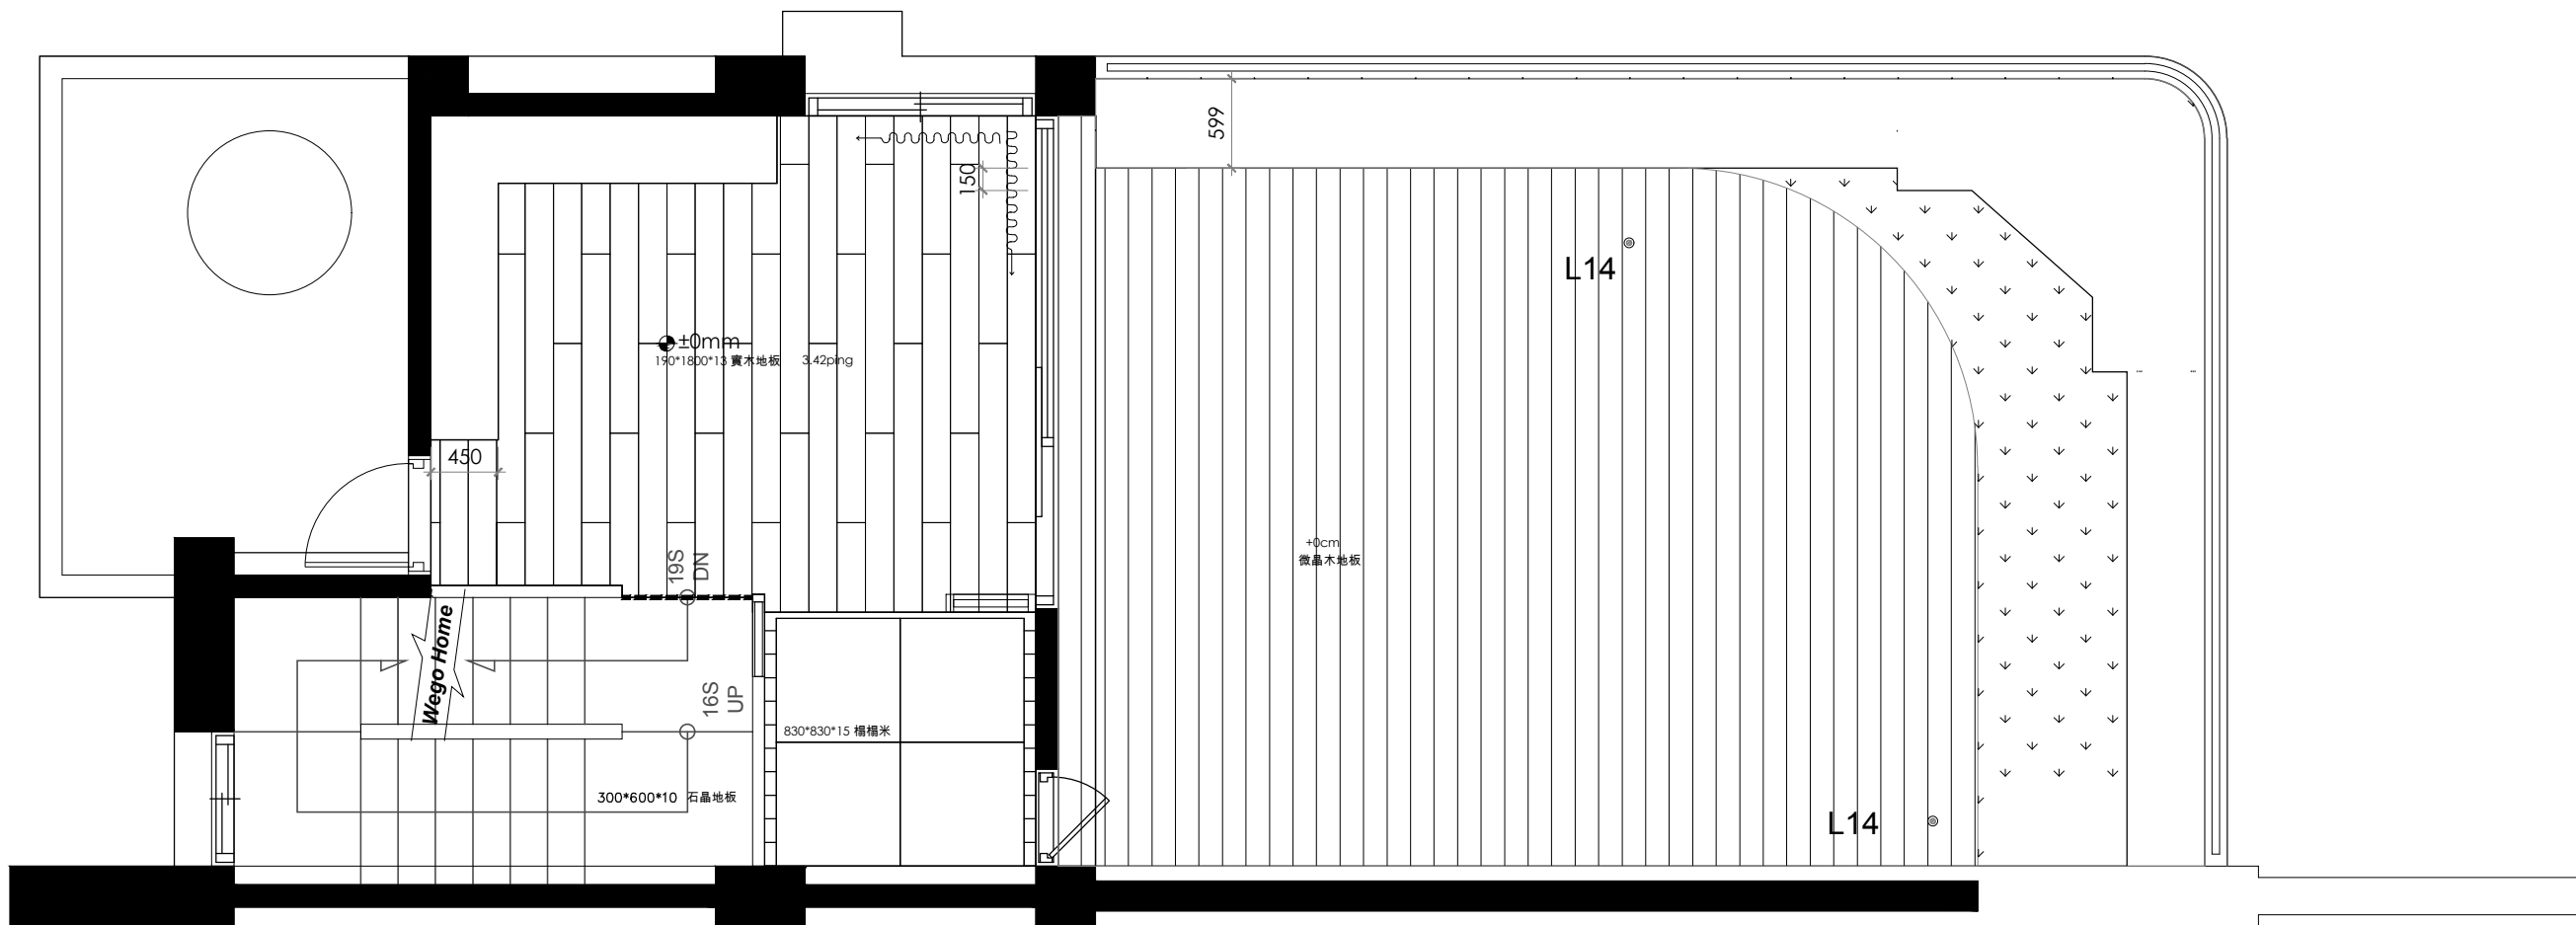

突一層平面圖


編號	圖示	說明	尺寸	光源	備註
L1	◉	舞光LED可調角度嵌燈	88mm Dia x H25mm	KW-303 / 8W / 3000k / 嵌孔75mm	
L2	◉	2線式停電照明嵌燈	105mm Dia x H55mm	FH- 849-1B / 5W / 3000k / 嵌孔93mm	
L3	◉	3線式停電照明嵌燈	105mm Dia x H55mm	FH- 849-1B / 5W / 3000k / 嵌孔93mm	
L4	⊕	LED 15W 小吸頂燈	82mm Dia x H78mm	3000k	
L5	◉	舞光LED 邱比特軌道燈 白色	W88mm x L115mm x H50mm	AE-B07 / 7W / 3000k / 24°	
L6	◉	超薄嵌入式感應式嵌燈	85mm Dia x H50mm	3000k / 嵌孔75mm	
L7	----	LED軟條燈		3000k	
L8	=====	軌道燈軌道	W34mm x H20mm		
L9	•	小型嵌燈	63mm Dia x H72mm	3000k / 嵌孔55mm	
L10	▣	無邊框可調角LED單燈盒燈	W99mm x L99mm x H85mm	FH- 829-11C /10W /30° / 3000K	
L11	▣	無邊框可調角LED雙燈盒燈	W99mm x L199mm x H85mm	FH- 829-12C /10W /30° / 3000K	
L12	- . - . -	磁吸式軌道燈			
L13	=====	防塵防濕T5燈具			
L14	•	上照LED埋地燈	42mm Dia. x H90mm	LED /3W /12° /12V /3000K / 700mA	
DL-1	◆	吊燈			
DL-2	⊙	壁燈			
*燈具相關設備,需詳燈具規範最後確認.					
*燈具供電皆為220V.					

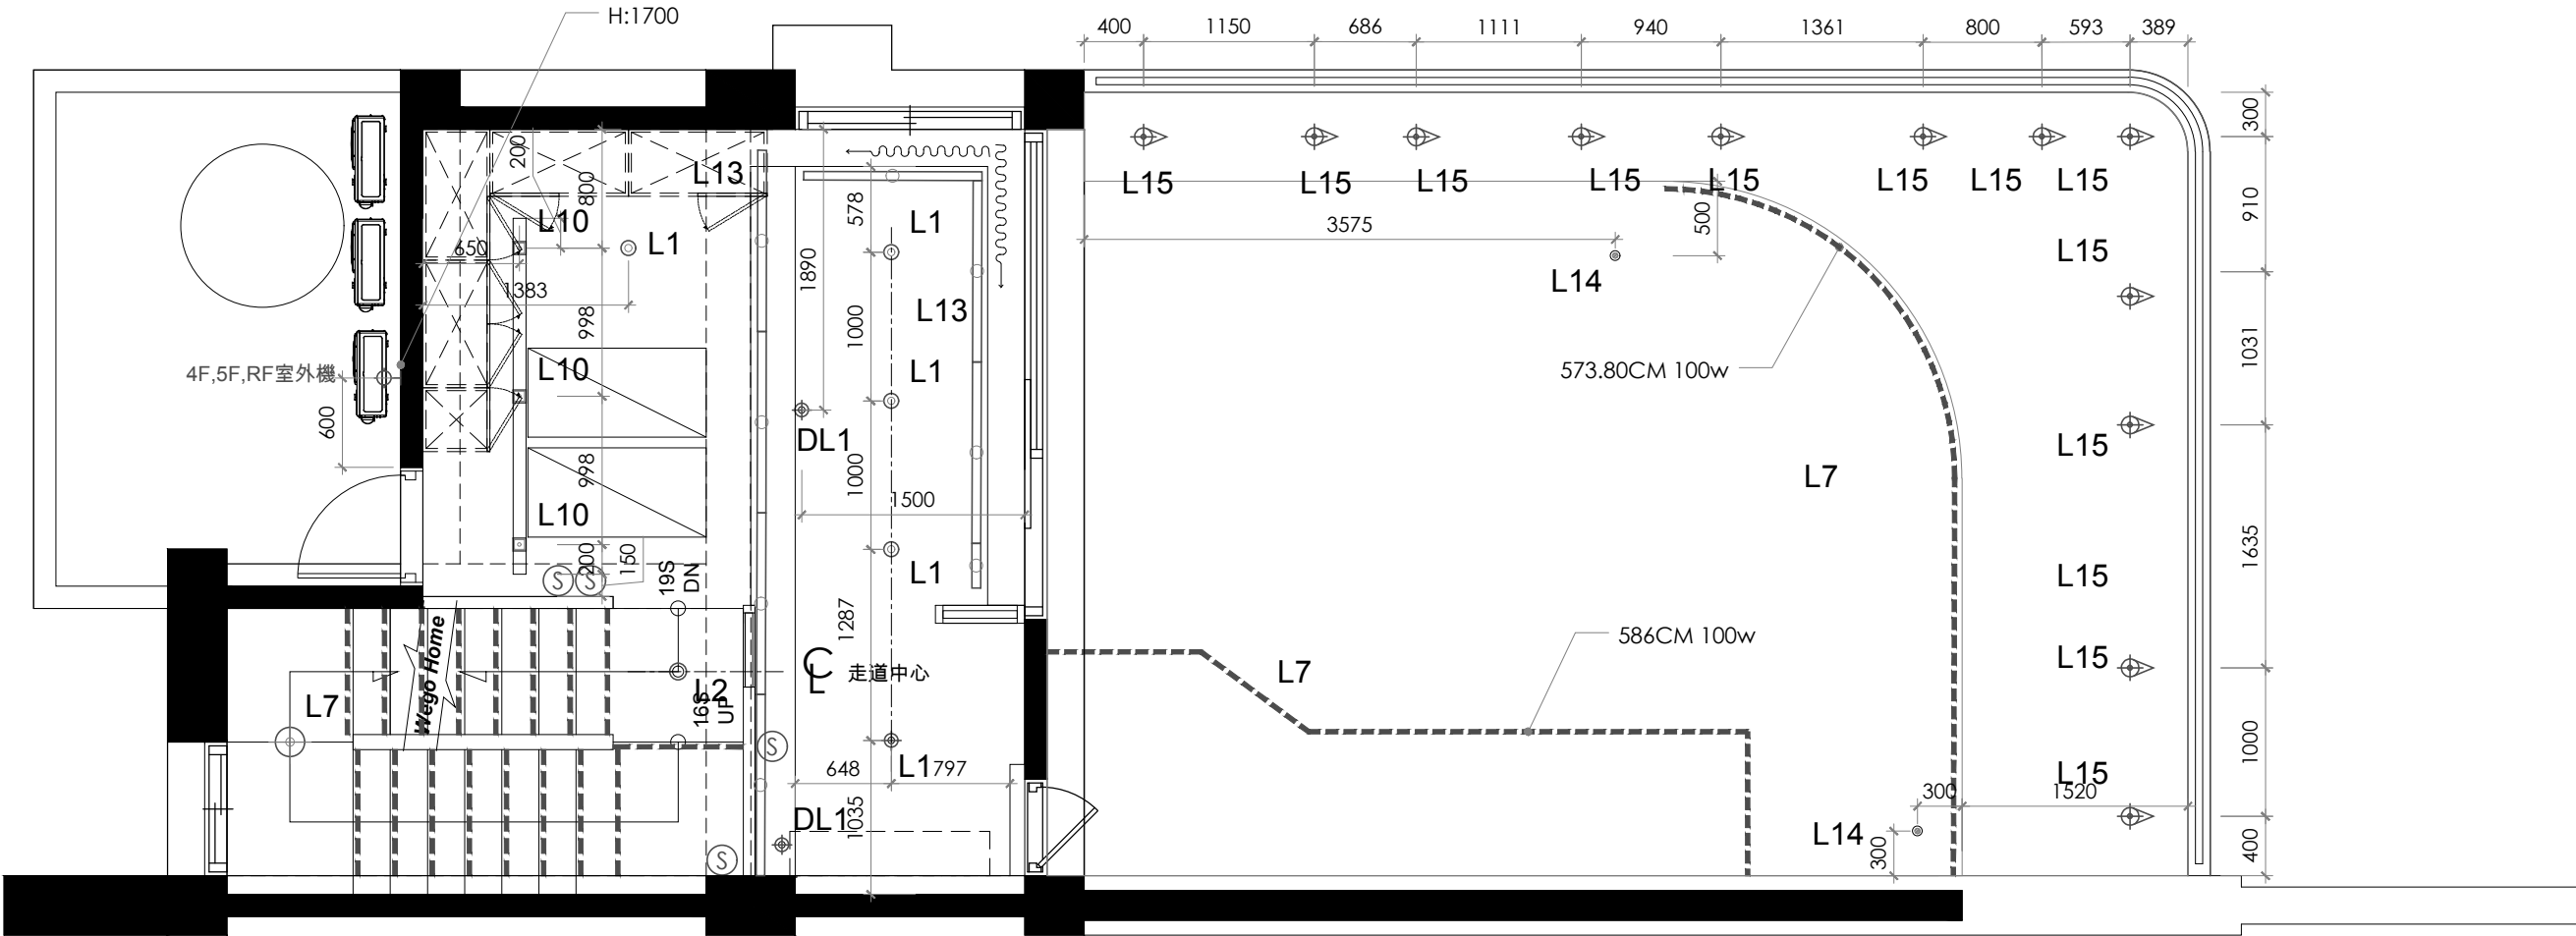

突一層平面圖


給排水設備圖例說明表			
圖例	說 明	規格	高 度
—○	壁面冷給水		
—●	壁面熱給水		
—○●	壁面冷熱給水		
—○●	壁面冷熱給水及排水		
○	地板排水口		
●	糞管		
備註	1.淋浴間,蓮蓬頭出水口+2100AFF。 2.淋浴間,蓮蓬頭出水口+2100AFF		

弱電設備圖例說明					
圖 例	說 明	數 量	圖 例	說 明	數 量
⊖	插座(110V雙插座)		Ⓜ	HDMI插座	
⊖	插座(220V雙插座)		Ⓐ	音響出線	
Ⓜ	地板插座(110V雙插座)		⊙	電源出線口	
Ⓜ	不斷電插座(110V雙插座)		Ⓜ	地板電源出線	
Ⓜ	獨立電源		Ⓜ	空調開關	
①	電話插座(大樓)		Ⓜ	勿干擾顯示器,門鈴	
△	掛壁式電話插座(內線)		Ⓜ	對講機	
①	電話插座(內線)		Ⓜ	門上感應器(鈴聲)	
Ⓜ	大門陽極鎖控制按鈕		Ⓜ	門禁刷卡器	
①	電視插座		Ⓜ	天花板鈴聲器	
Ⓜ	資訊插座		Ⓜ	配電盤	
Ⓜ	燈具開關		Ⓜ	消防箱	
Ⓜ	調光開關		Ⓜ	緊急壓扣	
備註	1.插座,燈具出線口詳細位置尺寸,高度詳裝修圖。 2.所有壁面插座,除特別標示高度者之外,中心點一律離地完成面+300AFF。 3.所有壁面開關,除特別標示高度者之外,中心點一律離地完成面+1200AFF。 4.所有配管,線均由平頂天花配置。 5.影音視聽系統所需弱電設備,由影音視聽系統廠商規劃後,提供圖面予業主審核。				

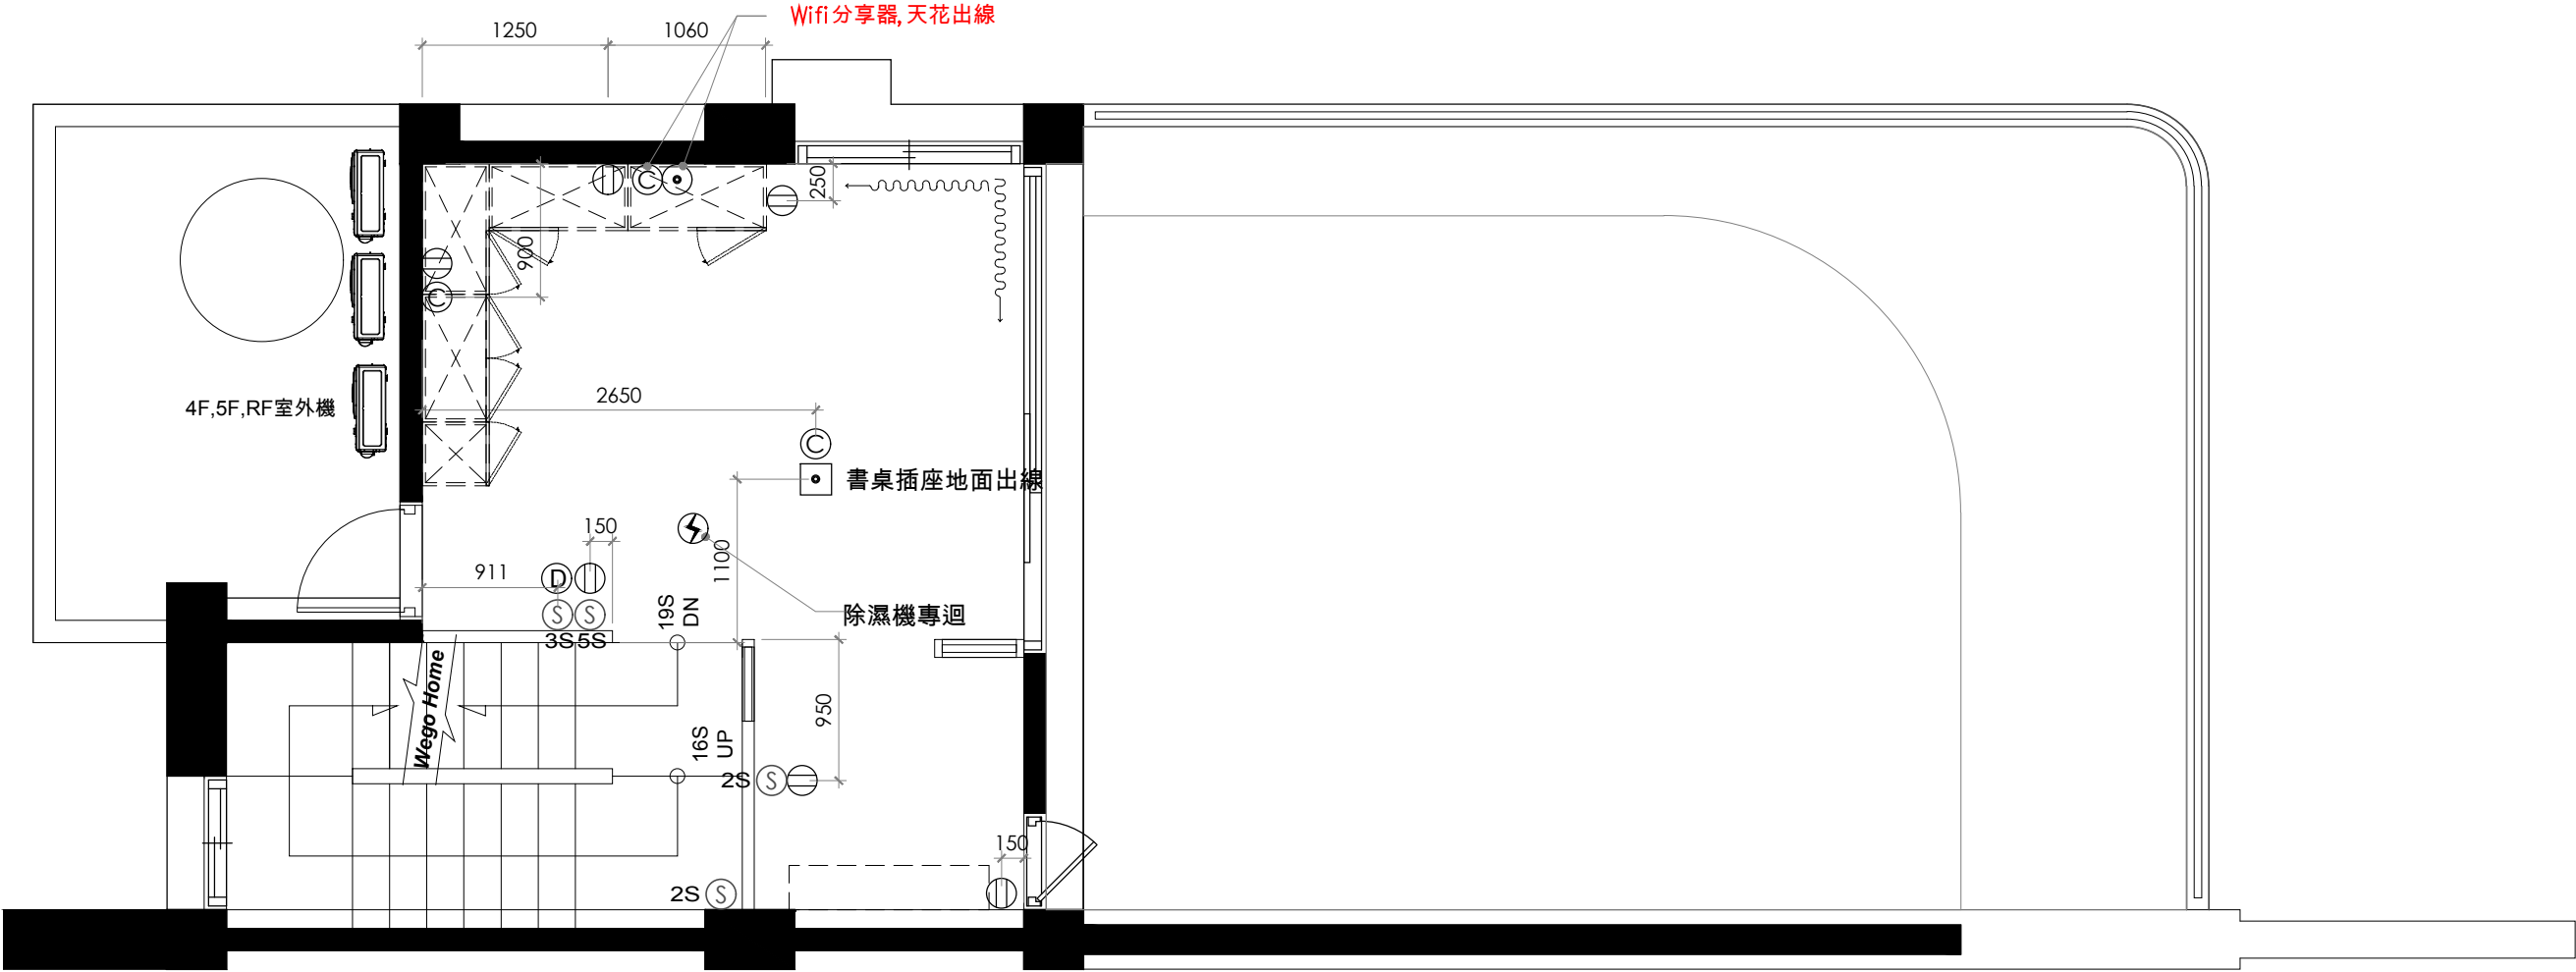



突一層平面圖


編號	圖示	說明	尺寸	光源	備註
L1	◉	舞光LED可調角度嵌燈	88mm Dia x H25mm	KW-303 / 8W / 3000k / 嵌孔75mm	
L2	◉	2線式停電照明嵌燈	105mm Dia x H55mm	FH- 849-1B / 5W / 3000k / 嵌孔93mm	
L3	◉	3線式停電照明嵌燈	105mm Dia x H55mm	FH- 849-1B / 5W / 3000k / 嵌孔93mm	
L4	⊕	LED 15W 小吸頂燈	82mm Dia x H78mm	3000k	
L5	◉	舞光LED 邱比特軌道燈 白色	W88mm x L115mm x H50mm	AE-B07 / 7W / 3000k / 24°	
L6	◉	超薄嵌入式感應式嵌燈	85mm Dia x H50mm	3000k / 嵌孔75mm	
L7	----	LED軟條燈		3000k	
L8	=====	軌道燈軌道	W34mm x H20mm		
L9	•	小型嵌燈	63mm Dia x H72mm	3000k / 嵌孔55mm	
L10	▣	無邊框可調角LED單燈盒燈	W99mm x L99mm x H85mm	FH- 829-11C /10W /30° / 3000K	
L11	▣	無邊框可調角LED雙燈盒燈	W99mm x L199mm x H85mm	FH- 829-12C /10W /30° / 3000K	
L12	— · — · —	磁吸式軌道燈			
L13	▢	防塵防濕T5燈具			
L14	•	上照LED埋地燈	42mm Dia. x H90mm	LED /3W /12° /12V /3000K / 700mA	
DL-1	◆	吊燈			
DL-2	◇	壁燈			
*燈具相關設備,需詳燈具規範最後確認。 *燈具供電皆為220V.					

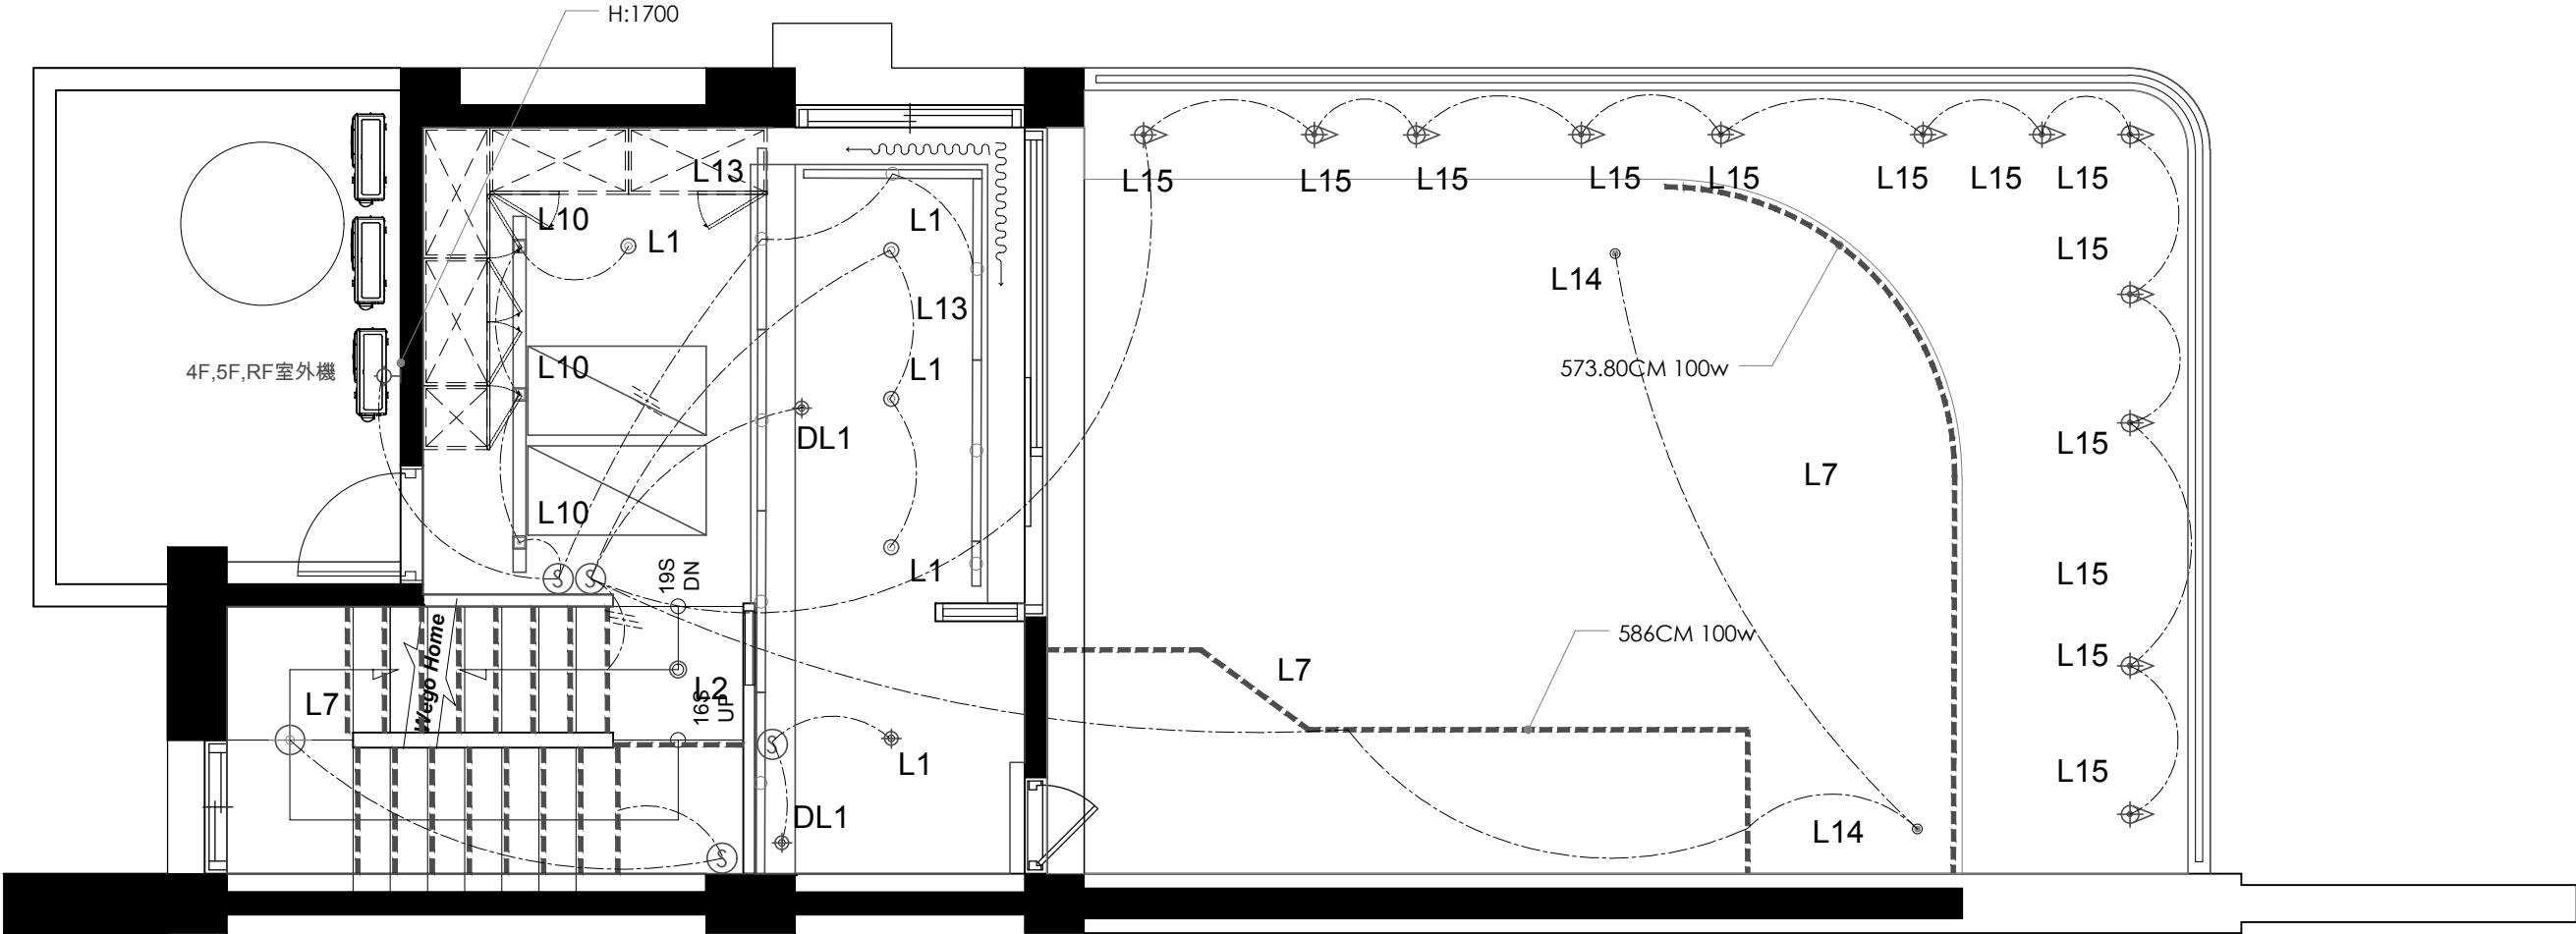


突一層平面圖

編號	圖示	說明	尺寸	光源	備註
L1	◉	舞光LED可調角度嵌燈	88mm Dia x H25mm	KW-303 / 8W / 3000k / 嵌孔75mm	
L2	◉	2線式停電照明嵌燈	105mm Dia x H55mm	FH- 849-1B / 5W / 3000k / 嵌孔93mm	
L3	◉	3線式停電照明嵌燈	105mm Dia x H55mm	FH- 849-1B / 5W / 3000k / 嵌孔93mm	
L4	⊕	LED 15W 小吸頂燈	82mm Dia x H78mm	3000k	
L5	◉	舞光LED 邱比特軌道燈 白色	W88mm x L115mm x H50mm	AE-B07 / 7W / 3000k / 24°	
L6	◉	超薄嵌入式感應式嵌燈	85mm Dia x H50mm	3000k / 嵌孔75mm	
L7	----	LED軟條燈		3000k	
L8	=====	軌道燈軌道	W34mm x H20mm		
L9	•	小型嵌燈	63mm Dia x H72mm	3000k / 嵌孔55mm	
L10	▣	無邊框可調角LED單燈盒燈	W99mm x L99mm x H85mm	FH- 829-11C /10W /30° / 3000K	
L11	▣	無邊框可調角LED雙燈盒燈	W99mm x L199mm x H85mm	FH- 829-12C /10W /30° / 3000K	
L12	- · - · -	磁吸式軌道燈			
L13	▬	防塵防濕T5燈具			
L14	•	上照LED埋地燈	42mm Dia. x H90mm	LED /3W /12° /12V /3000K / 700mA	
DL-1	◆	吊燈			
DL-2	⊙	壁燈			
*燈具相關設備,需詳燈具規範最後確認。 *燈具供電皆為220V.					

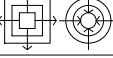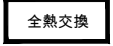空調設備圖例說明			
圖 例	說 明	圖 例	說 明
	側吹出風口		出風口
	側吹回風口		吊隱式除濕主機
	下吹出風口		五合一暖風機
	下吹回風口		全熱交換器

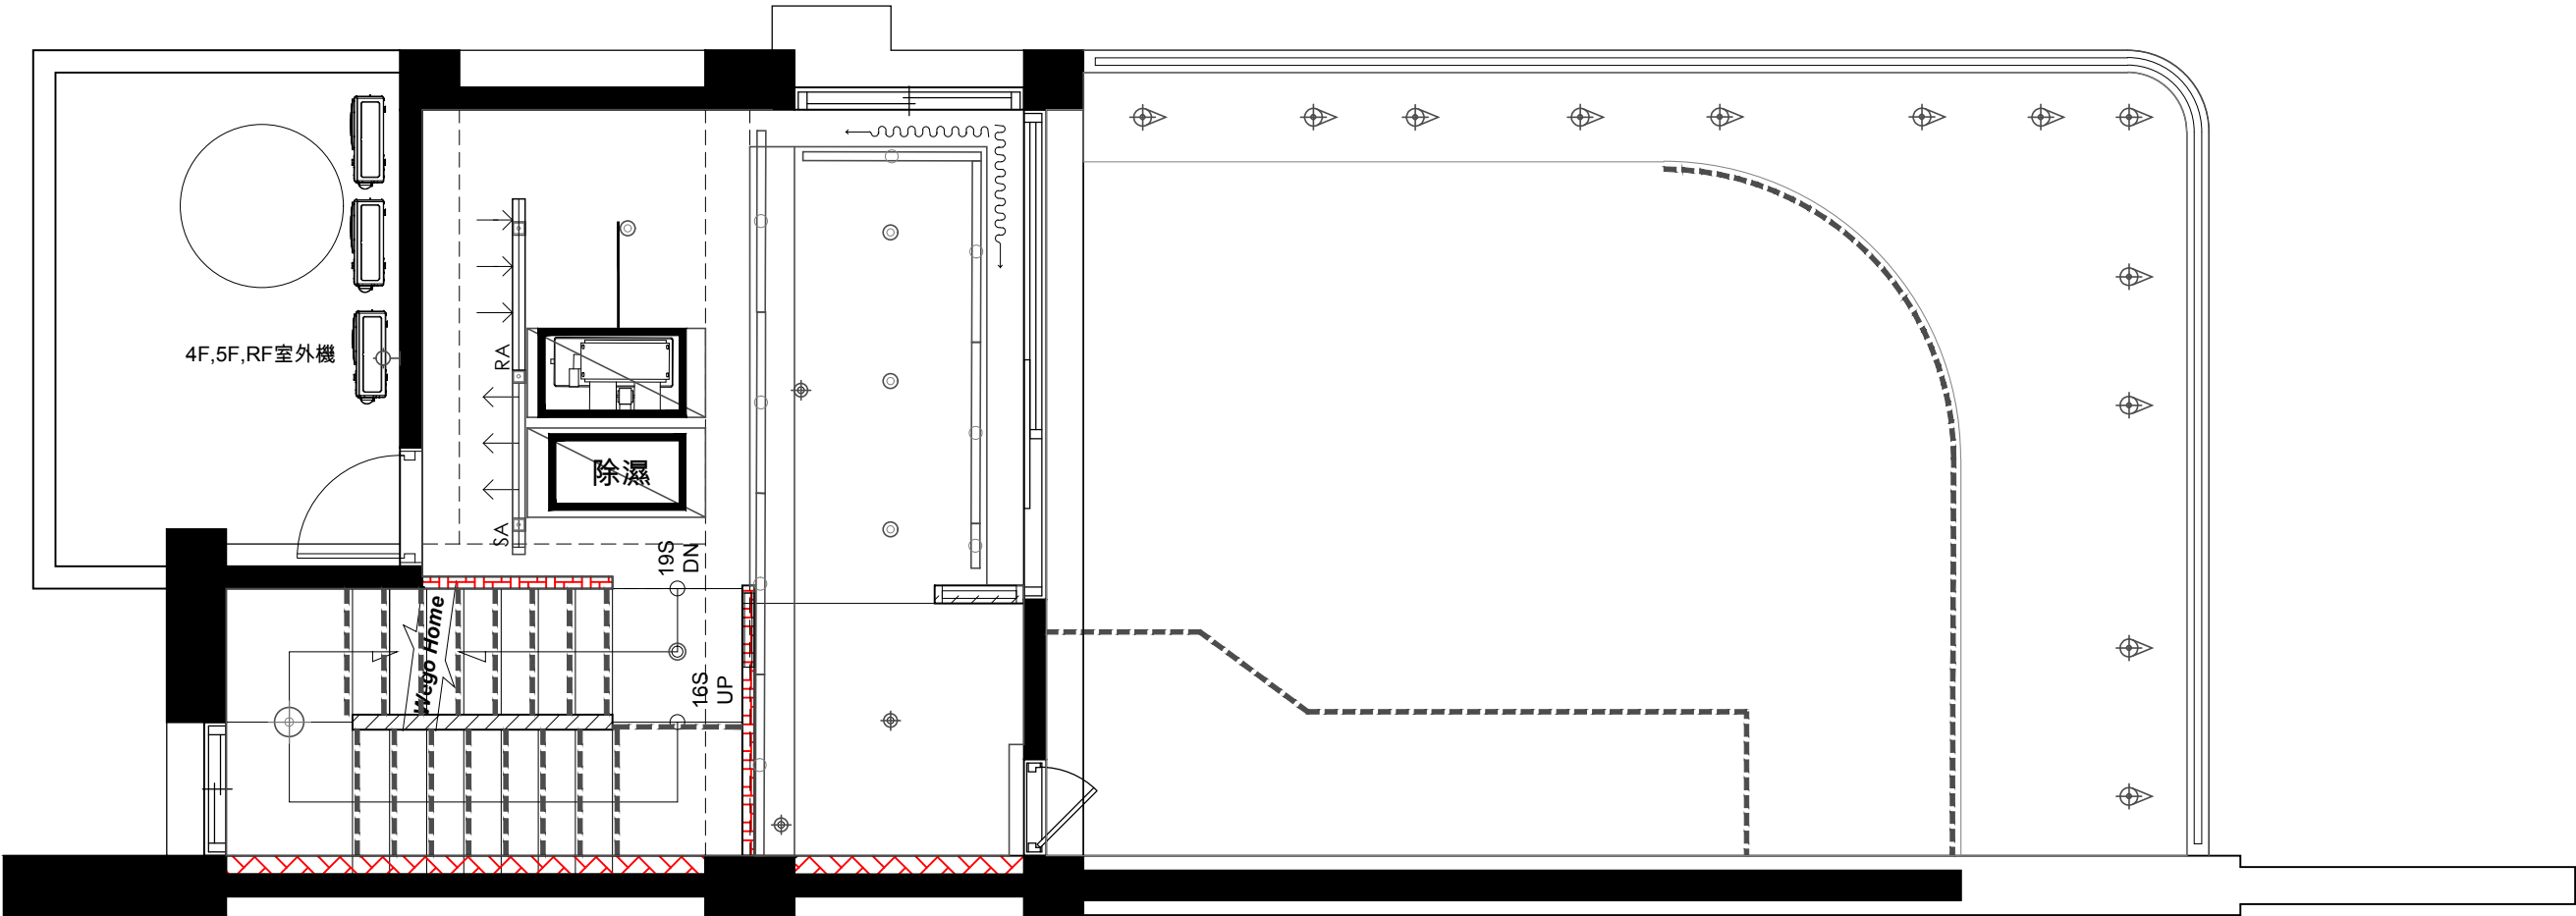


突一層平面圖

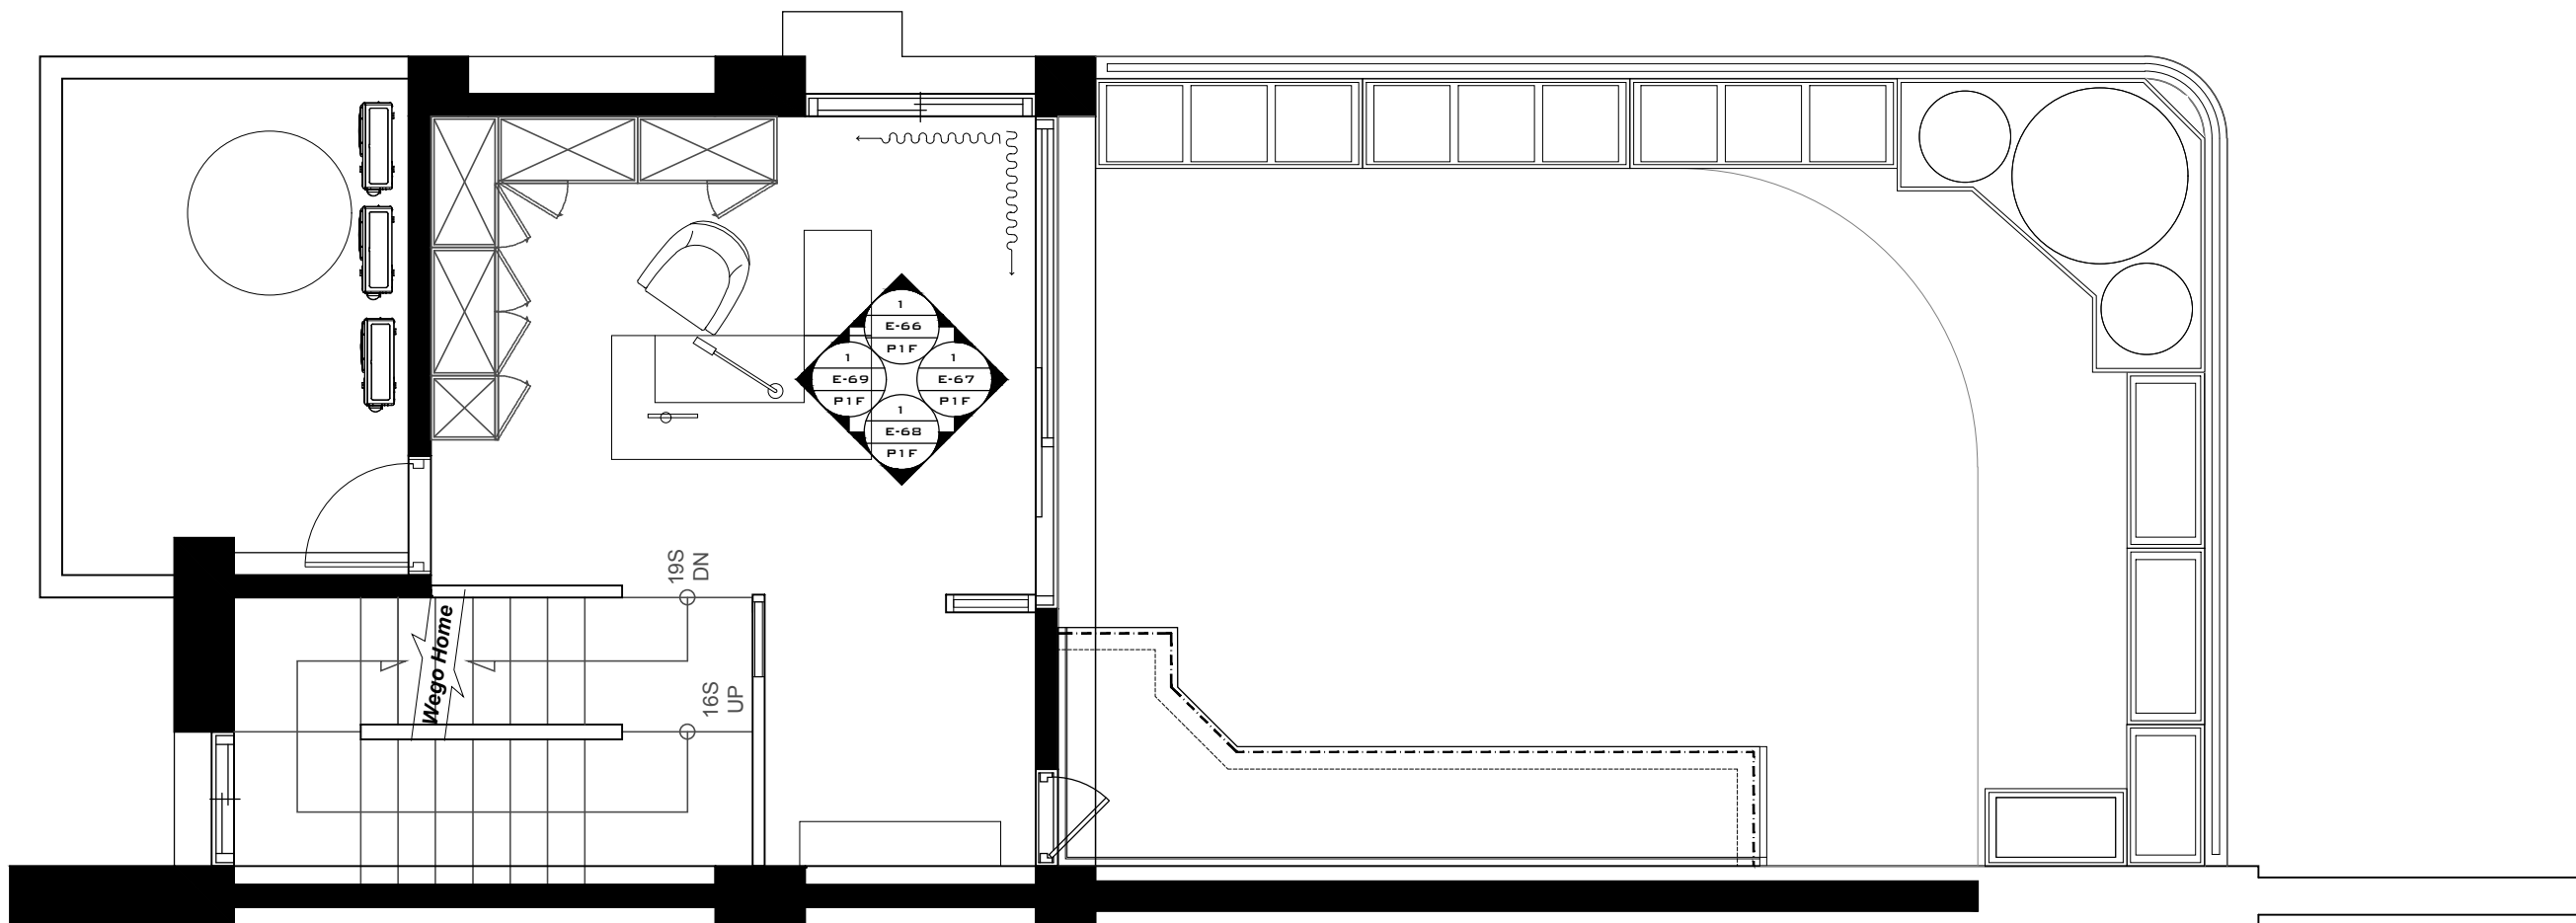


突一層平面圖



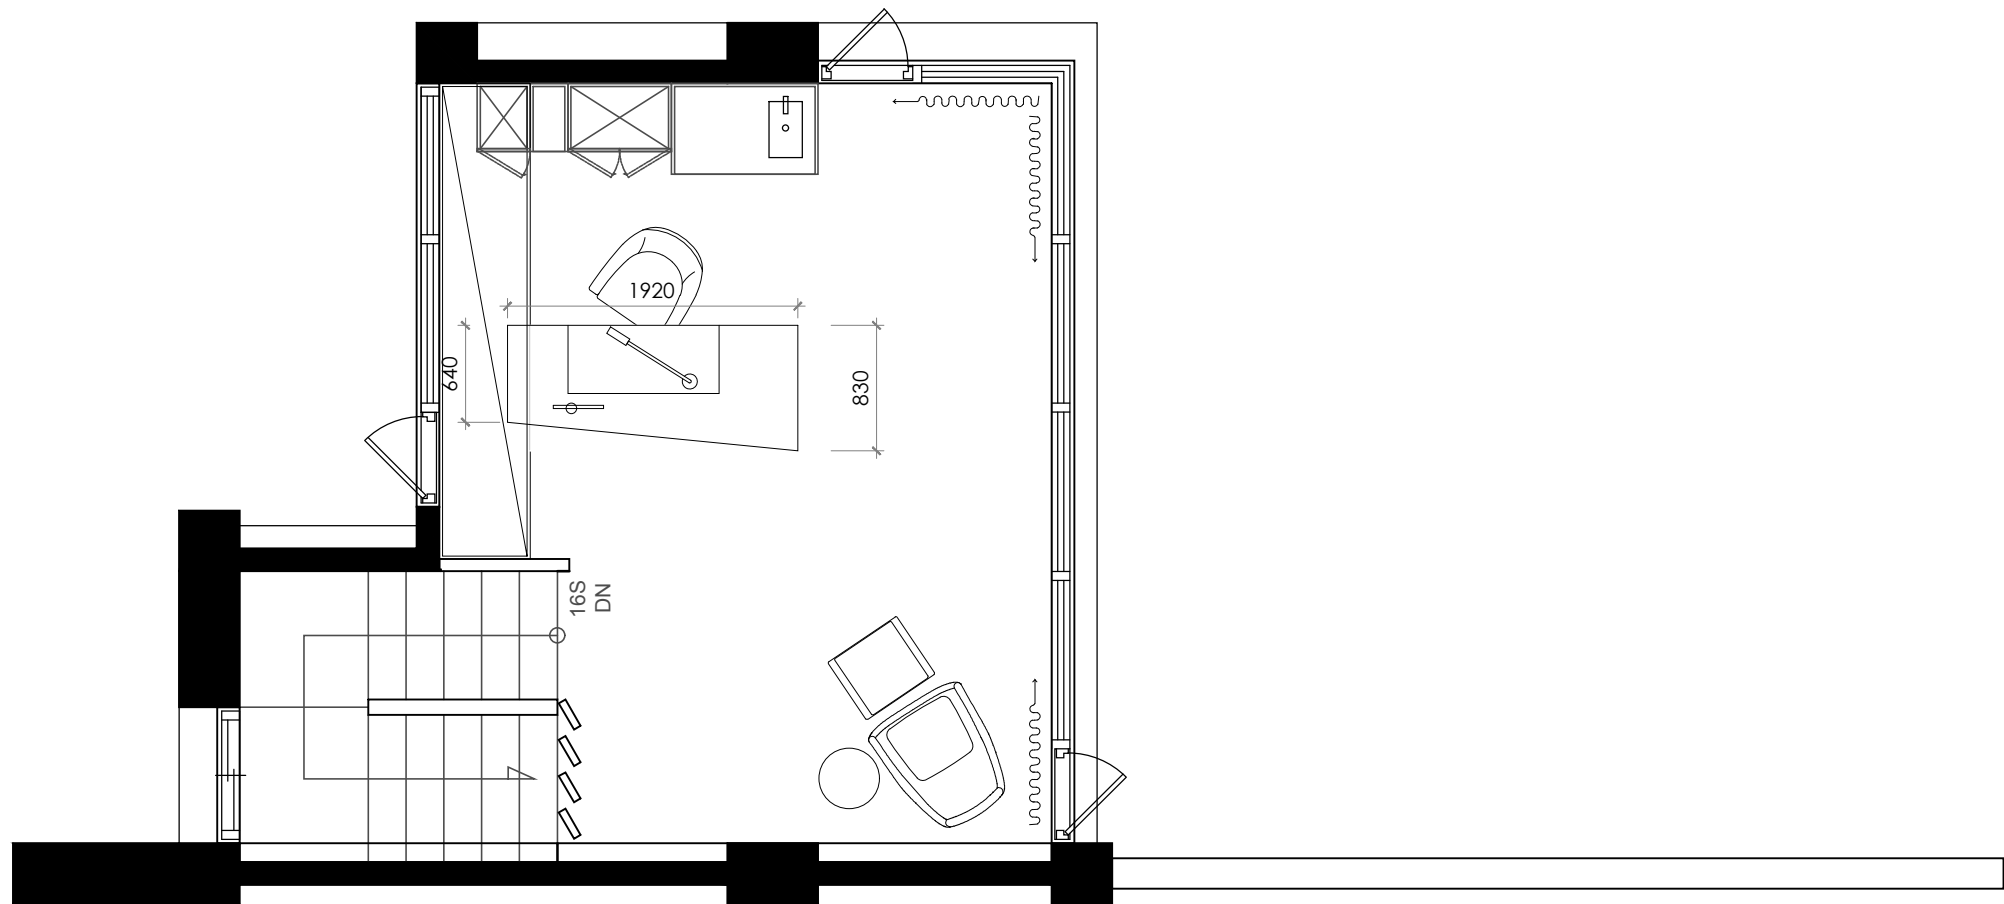


突二層平面圖

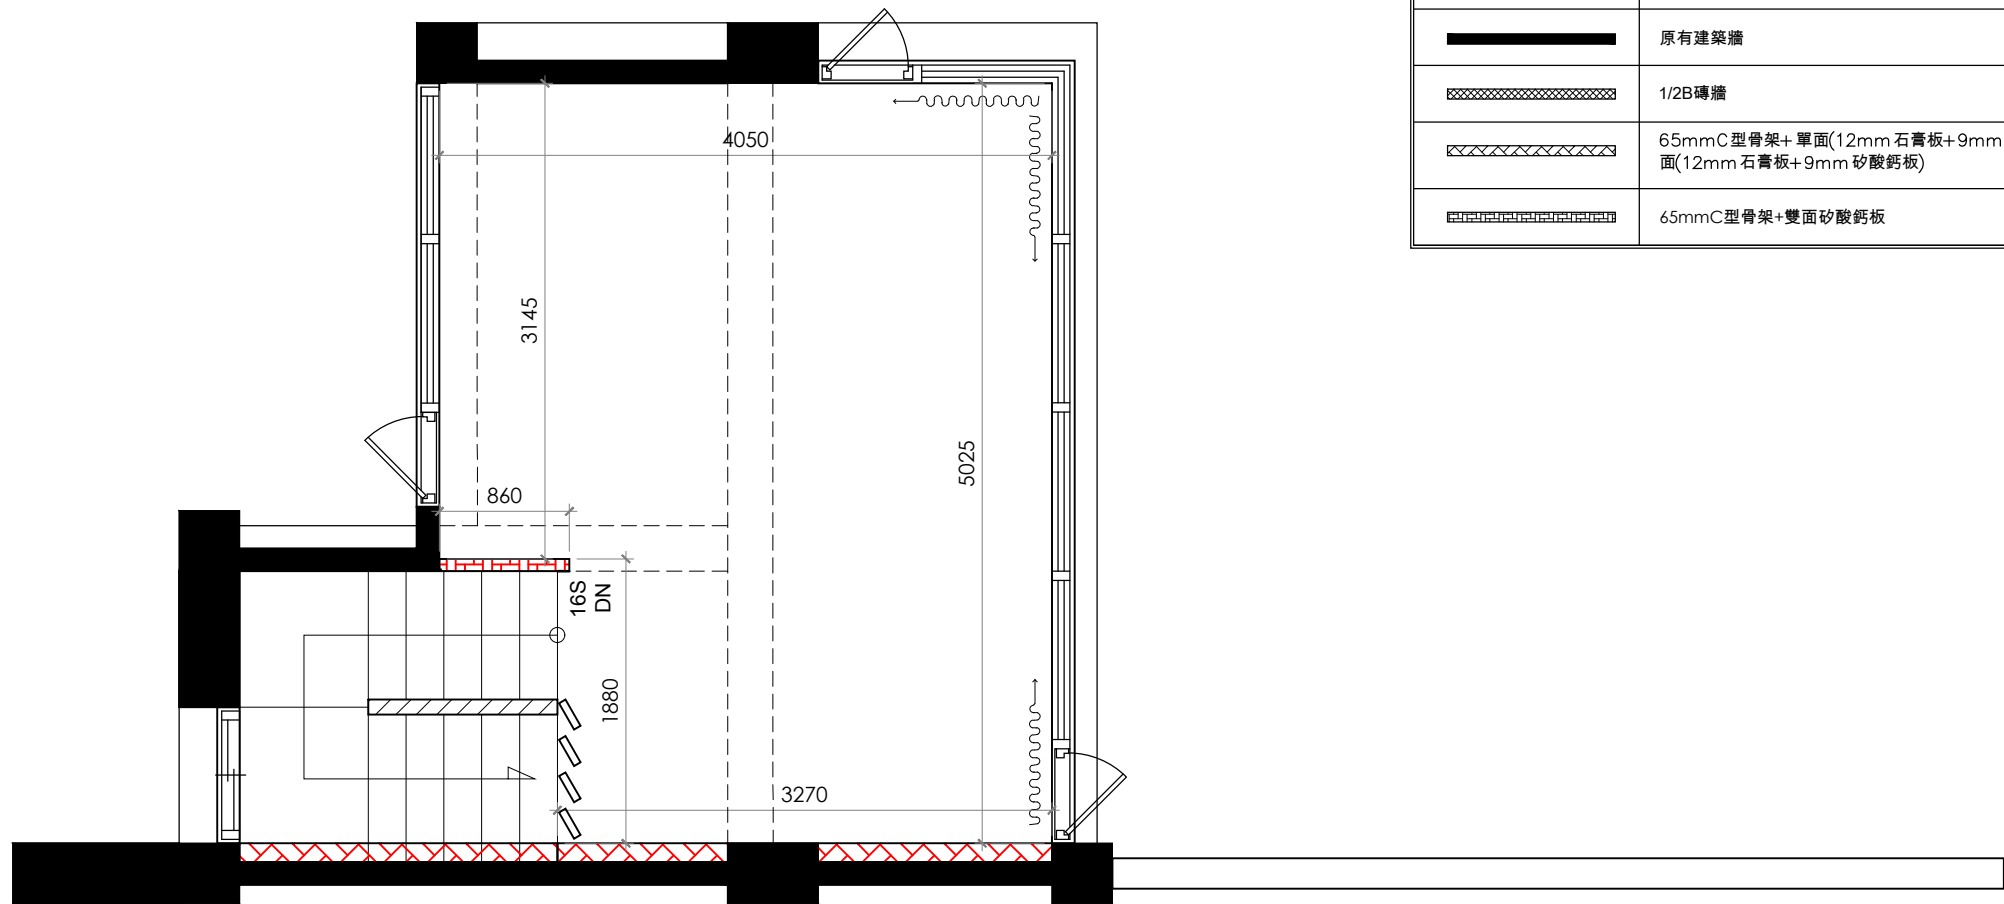


突二層平面圖

牆 型 式	內 容	總 厚 度
	木作隔間牆	
	原有建築牆	154mm
	1/2B磚牆	120mm
	65mmC型骨架+單面(12mm石膏板+9mm矽酸鈣板),單面(12mm石膏板+9mm矽酸鈣板)	100mm
	65mmC型骨架+雙面矽酸鈣板	85mm



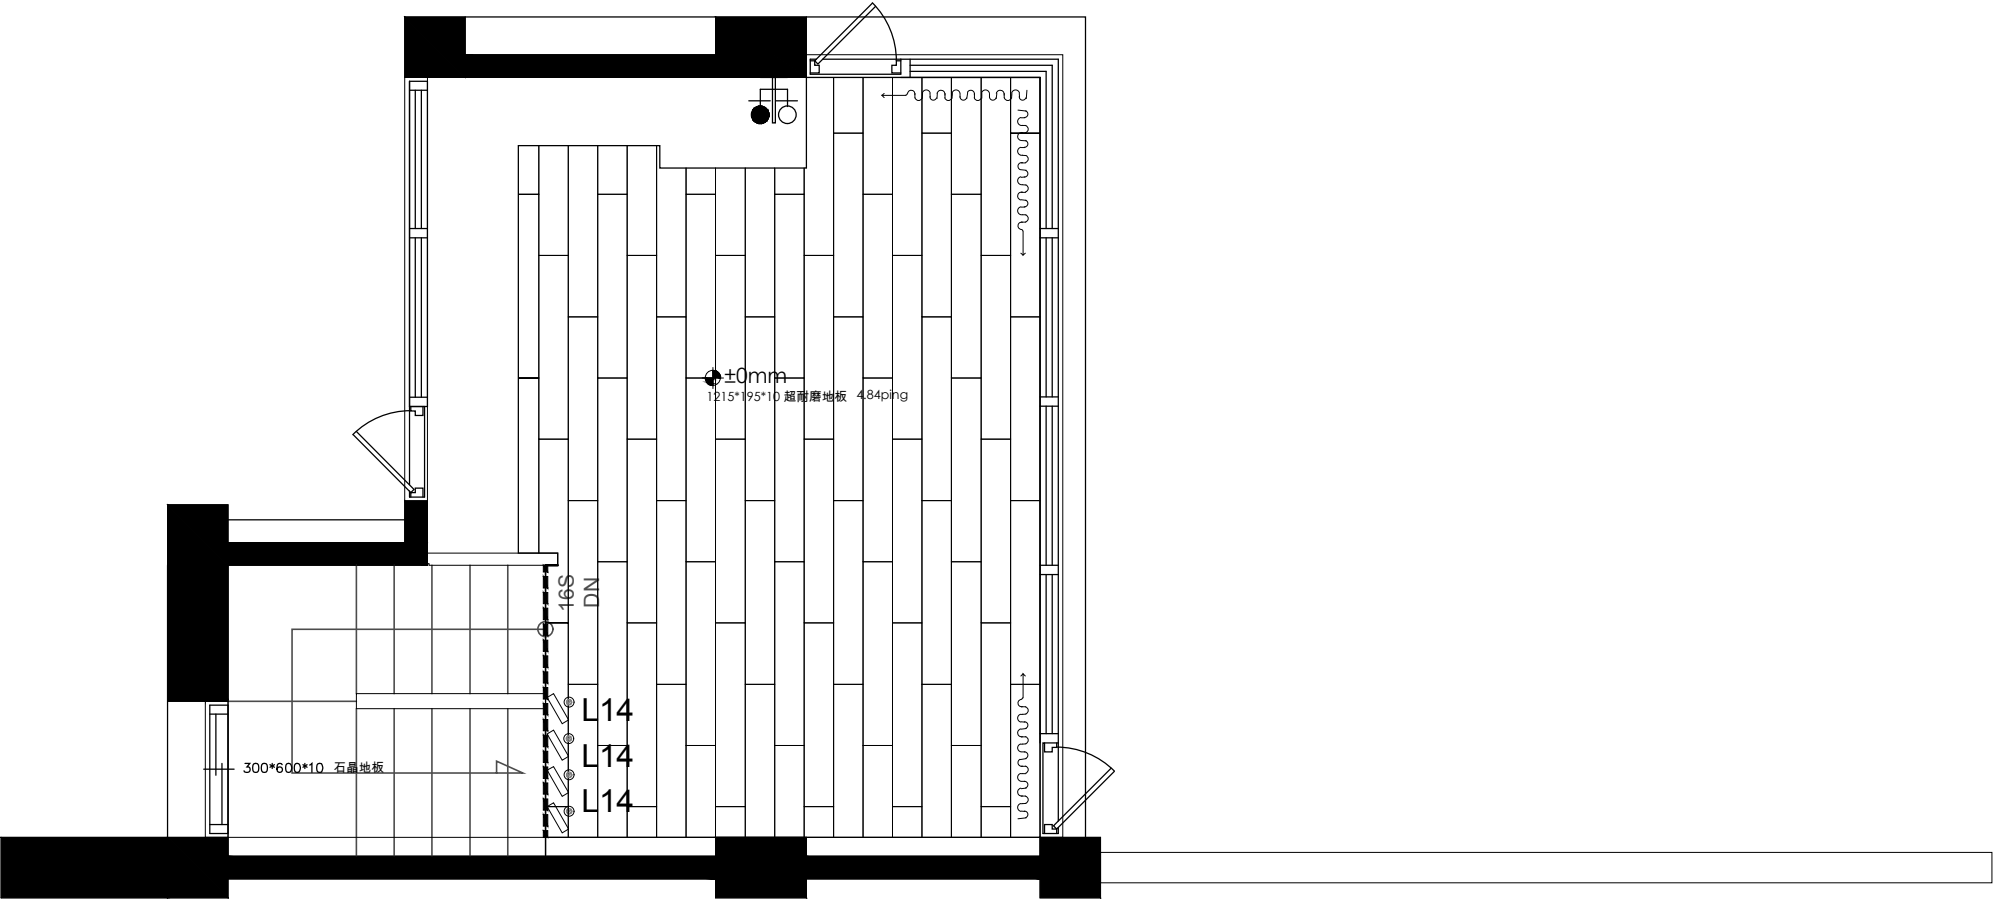


突二層平面圖

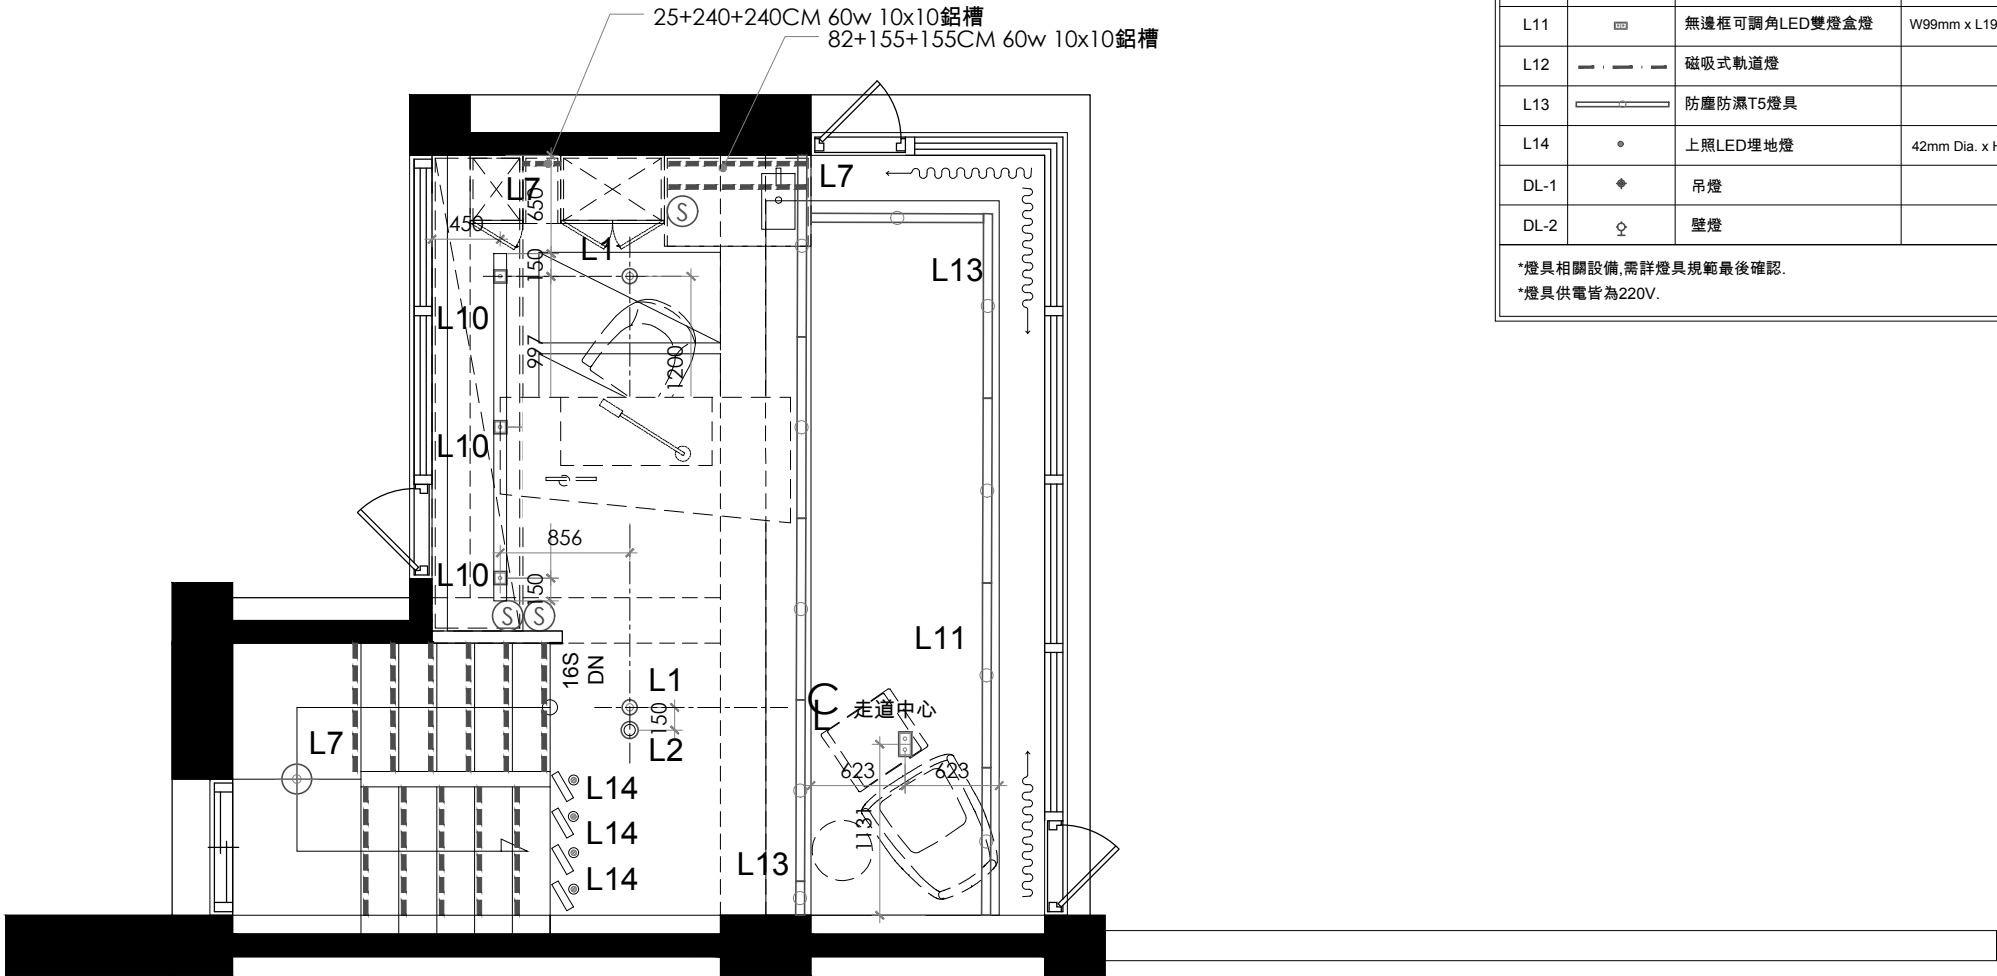

突二層平面圖

編號	圖示	說明	尺寸	光源	備註
L1	◉	舞光LED可調角度嵌燈	88mm Dia x H25mm	KW-303 / 8W / 3000k / 嵌孔75mm	
L2	◉	2線式停電照明嵌燈	105mm Dia x H55mm	FH- 849-1B / 5W / 3000k / 嵌孔93mm	
L3	◉	3線式停電照明嵌燈	105mm Dia x H55mm	FH- 849-1B / 5W / 3000k / 嵌孔93mm	
L4	⊕	LED 15W 小吸頂燈	82mm Dia x H78mm	3000k	
L5	◉	舞光LED 邱比特軌道燈 白色	W88mm x L115mm x H50mm	AE-B07 / 7W / 3000k / 24°	
L6	◉	超薄嵌入式感應式嵌燈	85mm Dia x H50mm	3000k / 嵌孔75mm	
L7	----	LED軟條燈		3000k	
L8	=====	軌道燈軌道	W34mm x H20mm		
L9	•	小型嵌燈	63mm Dia x H72mm	3000k / 嵌孔55mm	
L10	▣	無邊框可調角LED單燈盒燈	W99mm x L99mm x H85mm	FH- 829-11C / 10W / 30° / 3000K	
L11	▣	無邊框可調角LED雙燈盒燈	W99mm x L199mm x H85mm	FH- 829-12C / 10W / 30° / 3000K	
L12	— · — · —	磁吸式軌道燈			
L13	=====	防塵防濕T5燈具			
L14	•	上照LED埋地燈	42mm Dia. x H90mm	LED / 3W / 12° / 12V / 3000K / 700mA	
DL-1	◆	吊燈			
DL-2	⊙	壁燈			
*燈具相關設備,需詳燈具規範最後確認。 *燈具供電皆為220V.					

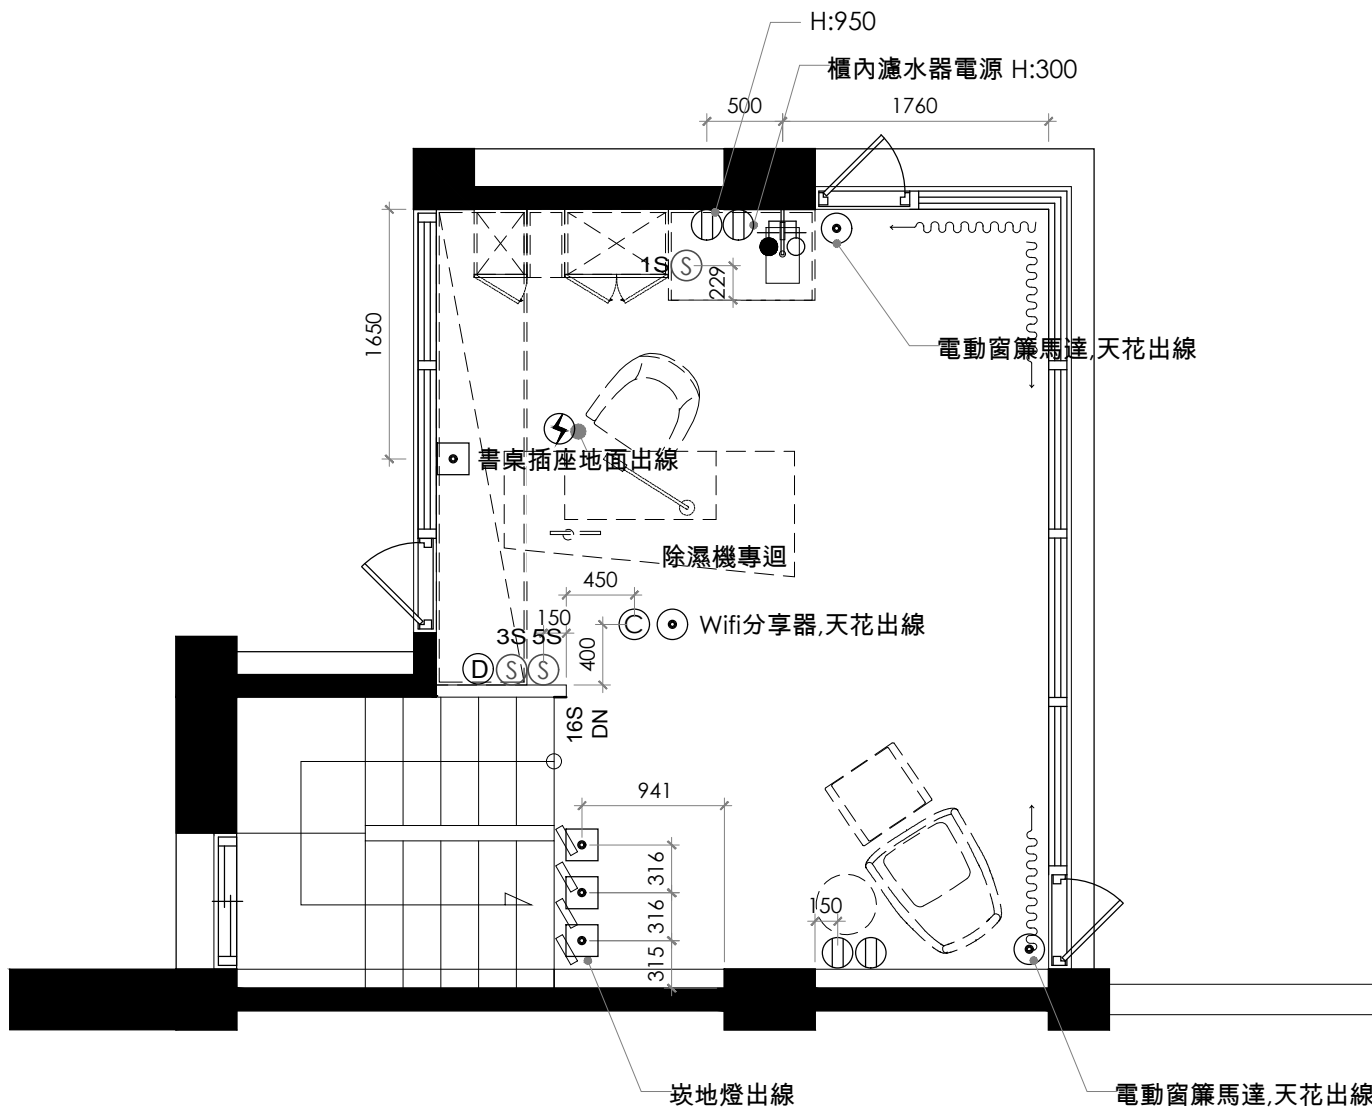


弱電設備圖例說明					
圖 例	說 明	數 量	圖 例	說 明	數 量
⊖	插座(110V雙插座)		Ⓜ	HDMI插座	
⊖	插座(220V雙插座)		Ⓐ	音響出線	
Ⓜ	地板插座(110V雙插座)		⊙	電源出線口	
Ⓜ	不斷電插座(110V雙插座)		Ⓜ	地板電源出線	
Ⓜ	獨立電源		Ⓜ	空調開關	
①	電話插座(大樓)		Ⓜ	勿干擾顯示器.門鈴	
△	掛壁式電話插座(內線)		BT	對講機	
Ⓜ	電話插座(內線)		Ⓜ	門上感應器(鈴聲)	
Ⓜ	大門陽極鎖控制按鈕		Ⓜ	門禁刷卡器	
Ⓜ	電視插座		Ⓜ	天花板鈴聲器	
Ⓜ	資訊插座		Ⓜ	配電盤	
Ⓜ	燈具開關		Ⓜ	消防箱	
Ⓜ	調光開關		Ⓜ	緊急壓扣	
備註		1.插座,燈具出線口詳細位置尺寸,高度詳裝修圖。			
		2.所有壁面插座,除特別標示高度者之外,中心點一律離地完成面+300AFF。			
		3.所有壁面開關,除特別標示高度者之外,中心點一律離地完成面+1200AFF。			
		4.所有配管,線均由平頂天花配置。			
		5.影音視聽系統所需弱電設備,由影音視聽系統廠商規劃後,提供圖面予業主審核。			


給排水設備圖例說明表			
圖例	說 明	規格	高度
—○	壁面冷給水		
—●	壁面熱給水		
Ⓜ○	壁面冷熱給水		
Ⓜ●	壁面冷熱給水及排水		
Ⓜ	地板排水口		
●	糞管		
備註		1.淋浴間,蓮蓬頭出水口+2100AFF。	
		2.淋浴間,蓮蓬頭出水口+2100AFF	

突二層平面圖

編號	圖示	說明	尺寸	光源	備註
L1	◉	舞光LED可調角度嵌燈	88mm Dia x H25mm	KW-303 / 8W / 3000k / 嵌孔75mm	
L2	◉	2線式停電照明嵌燈	105mm Dia x H55mm	FH- 849-1B / 5W / 3000k / 嵌孔93mm	
L3	◉	3線式停電照明嵌燈	105mm Dia x H55mm	FH- 849-1B / 5W / 3000k / 嵌孔93mm	
L4	⊕	LED 15W 小吸頂燈	82mm Dia x H78mm	3000k	
L5	◉	舞光LED 邱比特軌道燈 白色	W88mm x L115mm x H50mm	AE-B07 / 7W / 3000k / 24°	
L6	◉	超薄嵌入式感應式嵌燈	85mm Dia x H50mm	3000k / 嵌孔75mm	
L7	----	LED軟條燈		3000k	
L8	=====	軌道燈軌道	W34mm x H20mm		
L9	•	小型嵌燈	63mm Dia x H72mm	3000k / 嵌孔55mm	
L10	▣	無邊框可調角LED單燈盒燈	W99mm x L99mm x H85mm	FH- 829-11C / 10W / 30° / 3000K	
L11	▣	無邊框可調角LED雙燈盒燈	W99mm x L199mm x H85mm	FH- 829-12C / 10W / 30° / 3000K	
L12	- · - · -	磁吸式軌道燈			
L13	=====	防塵防濕T5燈具			
L14	•	上照LED埋地燈	42mm Dia. x H90mm	LED / 3W / 12° / 12V / 3000K / 700mA	
DL-1	◆	吊燈			
DL-2	⊙	壁燈			
*燈具相關設備,需詳燈具規範最後確認。 *燈具供電皆為220V.					

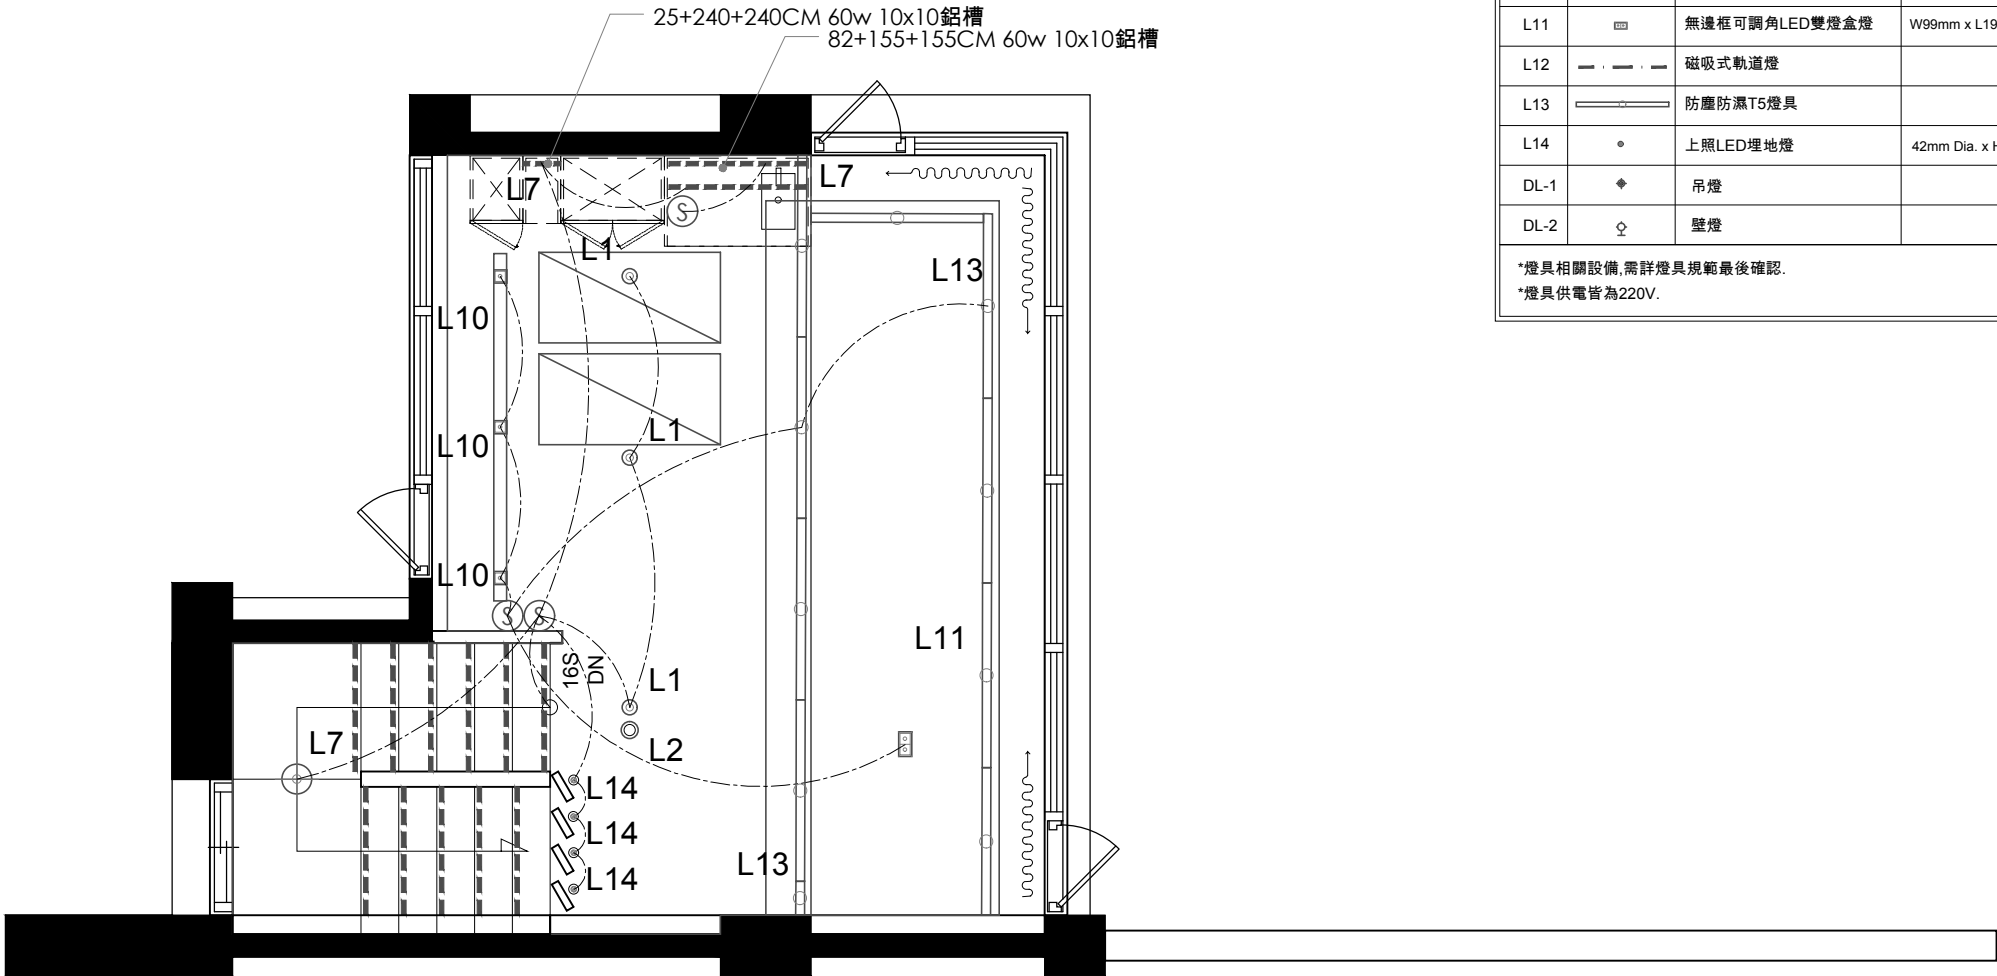


突二層平面圖

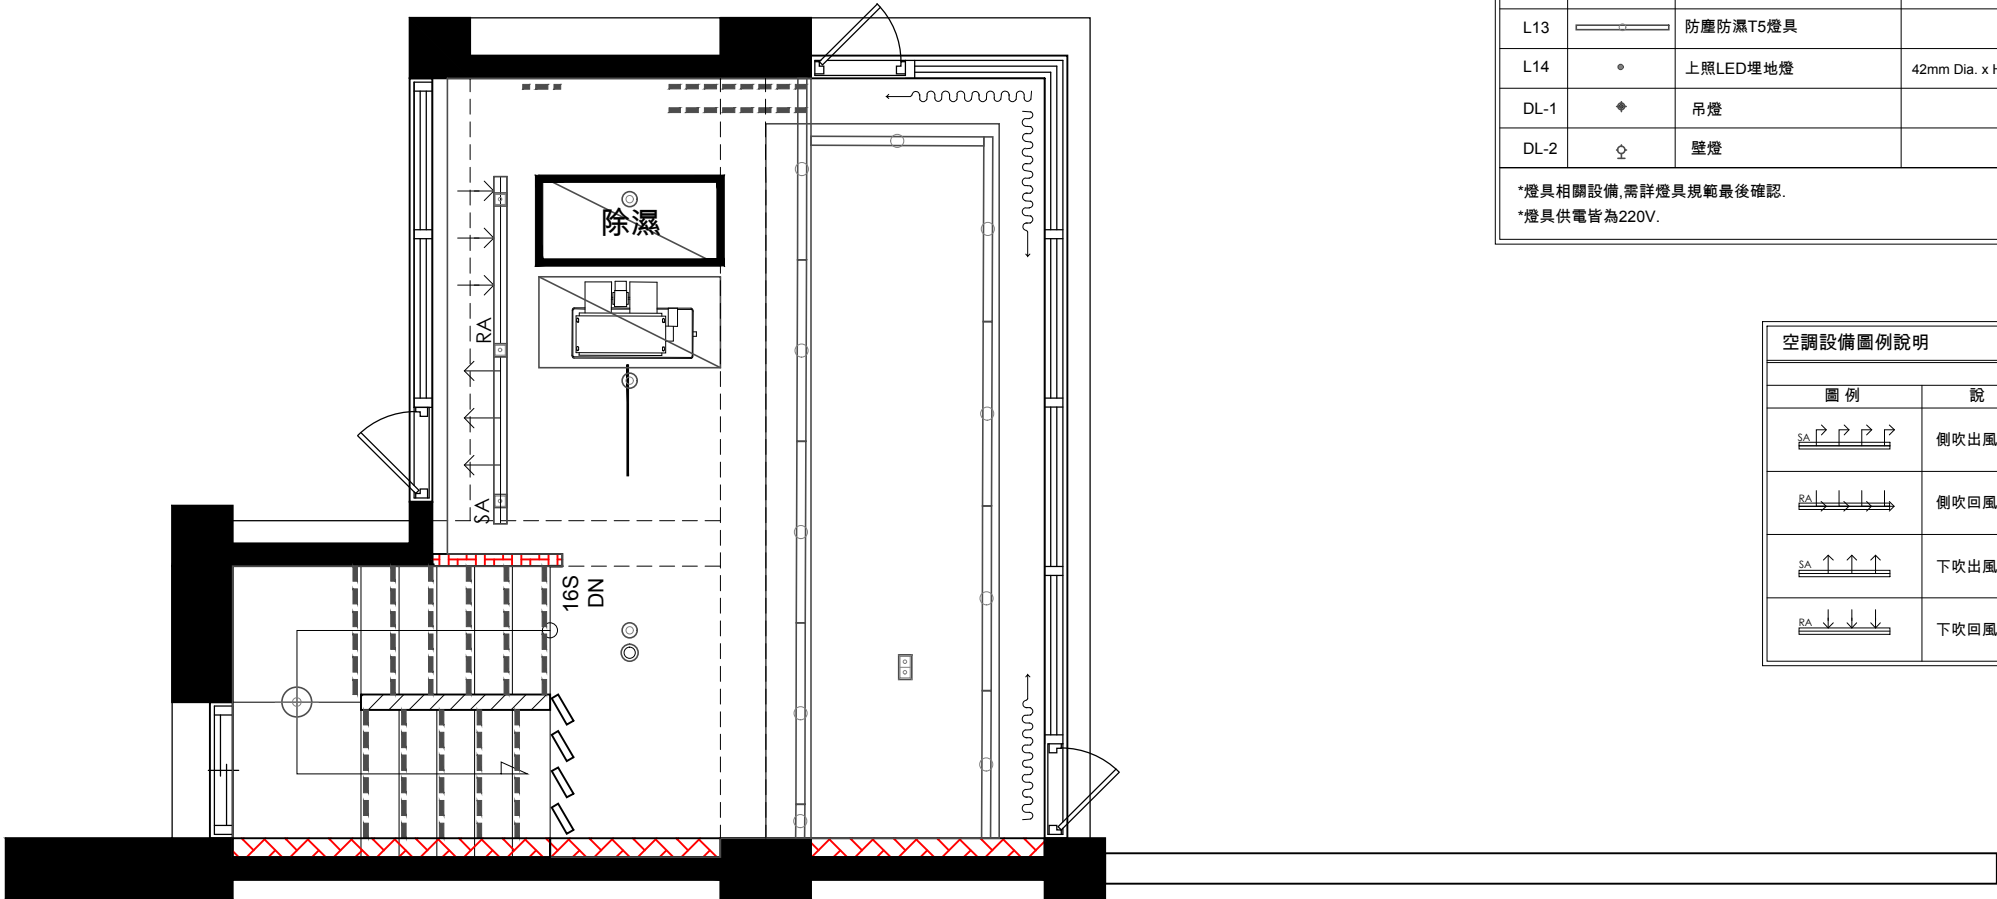


突二層平面圖

編號	圖示	說明	尺寸	光源	備註
L1		舞光LED可調角度嵌燈	88mm Dia x H25mm	KW-303 / 8W / 3000k / 嵌孔75mm	
L2		2線式停電照明嵌燈	105mm Dia x H55mm	FH- 849-1B / 5W / 3000k / 嵌孔93mm	
L3		3線式停電照明嵌燈	105mm Dia x H55mm	FH- 849-1B / 5W / 3000k / 嵌孔93mm	
L4		LED 15W 小吸頂燈	82mm Dia x H78mm	3000k	
L5		舞光LED 邱比特軌道燈 白色	W88mm x L115mm x H50mm	AE-B07 / 7W / 3000k / 24°	
L6		超薄嵌入式感應式嵌燈	85mm Dia x H50mm	3000k / 嵌孔75mm	
L7		LED軟條燈		3000k	
L8		軌道燈軌道	W34mm x H20mm		
L9		小型嵌燈	63mm Dia x H72mm	3000k / 嵌孔55mm	
L10		無邊框可調角LED單燈盒燈	W99mm x L99mm x H85mm	FH- 829-11C /10W /30° / 3000K	
L11		無邊框可調角LED雙燈盒燈	W99mm x L199mm x H85mm	FH- 829-12C /10W /30° / 3000K	
L12		磁吸式軌道燈			
L13		防塵防濕T5燈具			
L14		上照LED埋地燈	42mm Dia. x H90mm	LED /3W /12° /12V /3000K / 700mA	
DL-1		吊燈			
DL-2		壁燈			
*燈具相關設備,需詳燈具規範最後確認。 *燈具供電皆為220V.					

空調設備圖例說明			
圖 例	說 明	圖 例	說 明
	側吹出風口		出風口
	側吹回風口		吊隱式除濕主機
	下吹出風口		五合一暖風機
	下吹回風口		全熱交換器

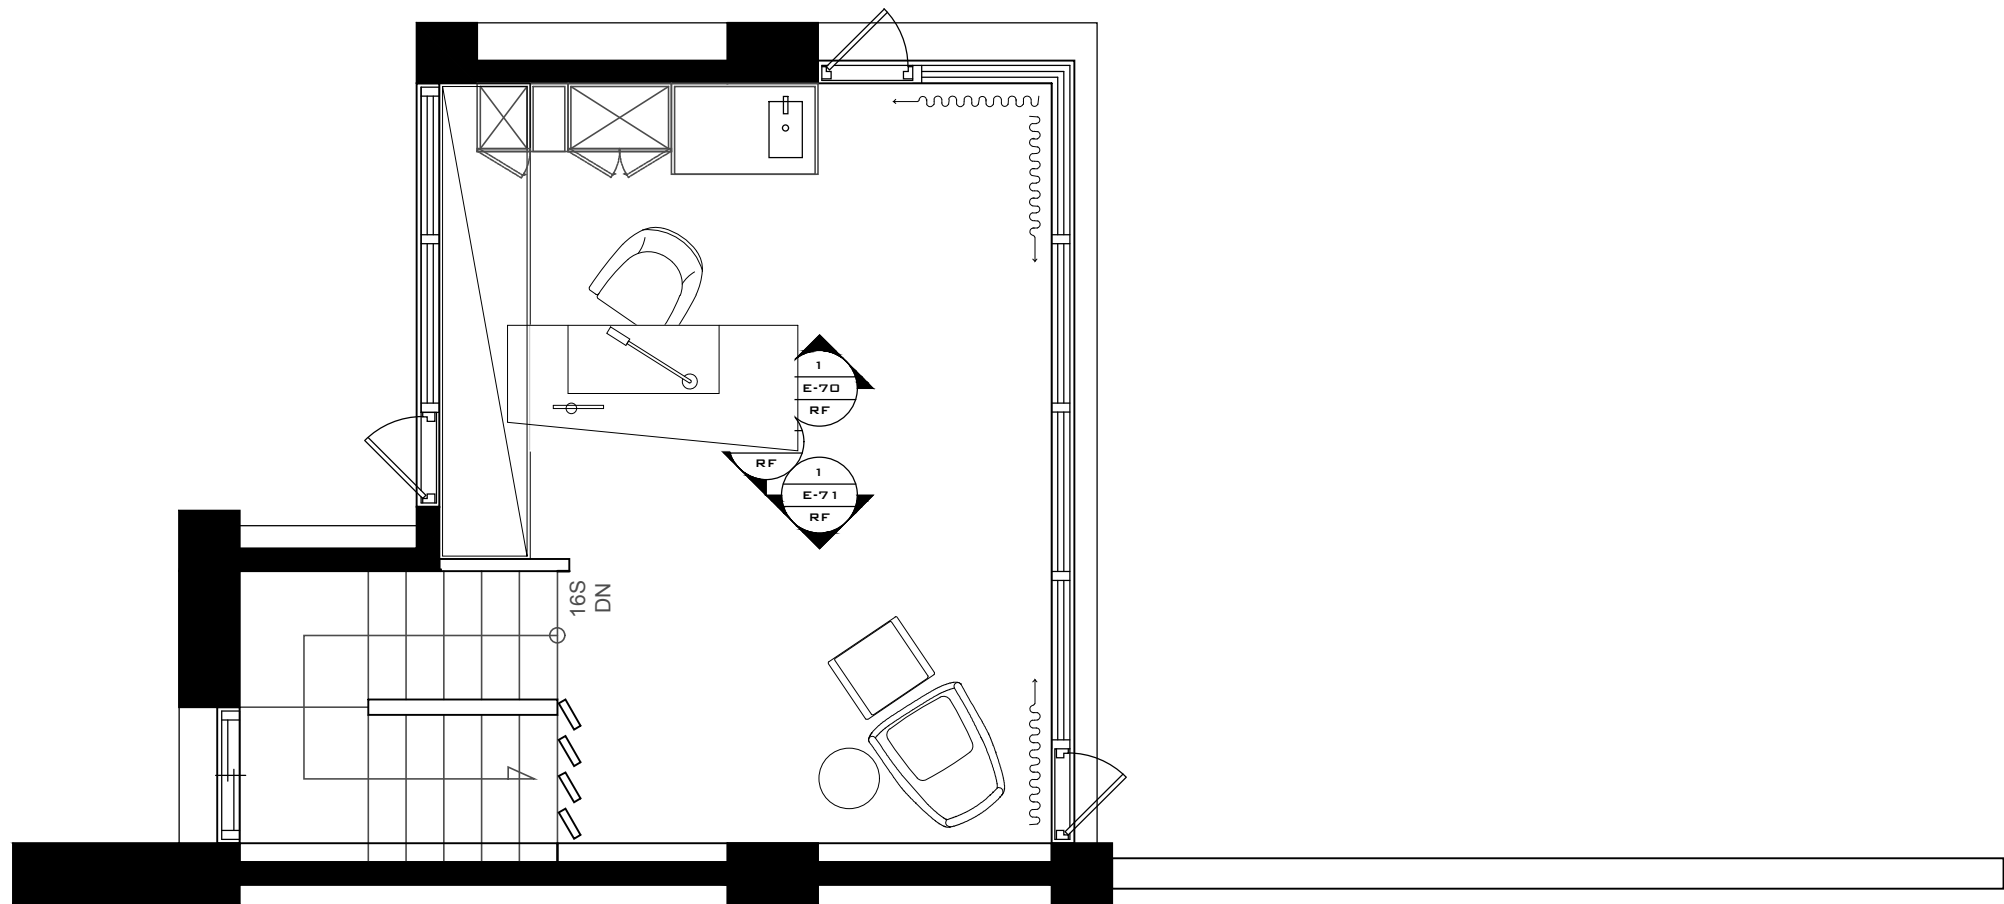

突二層平面圖

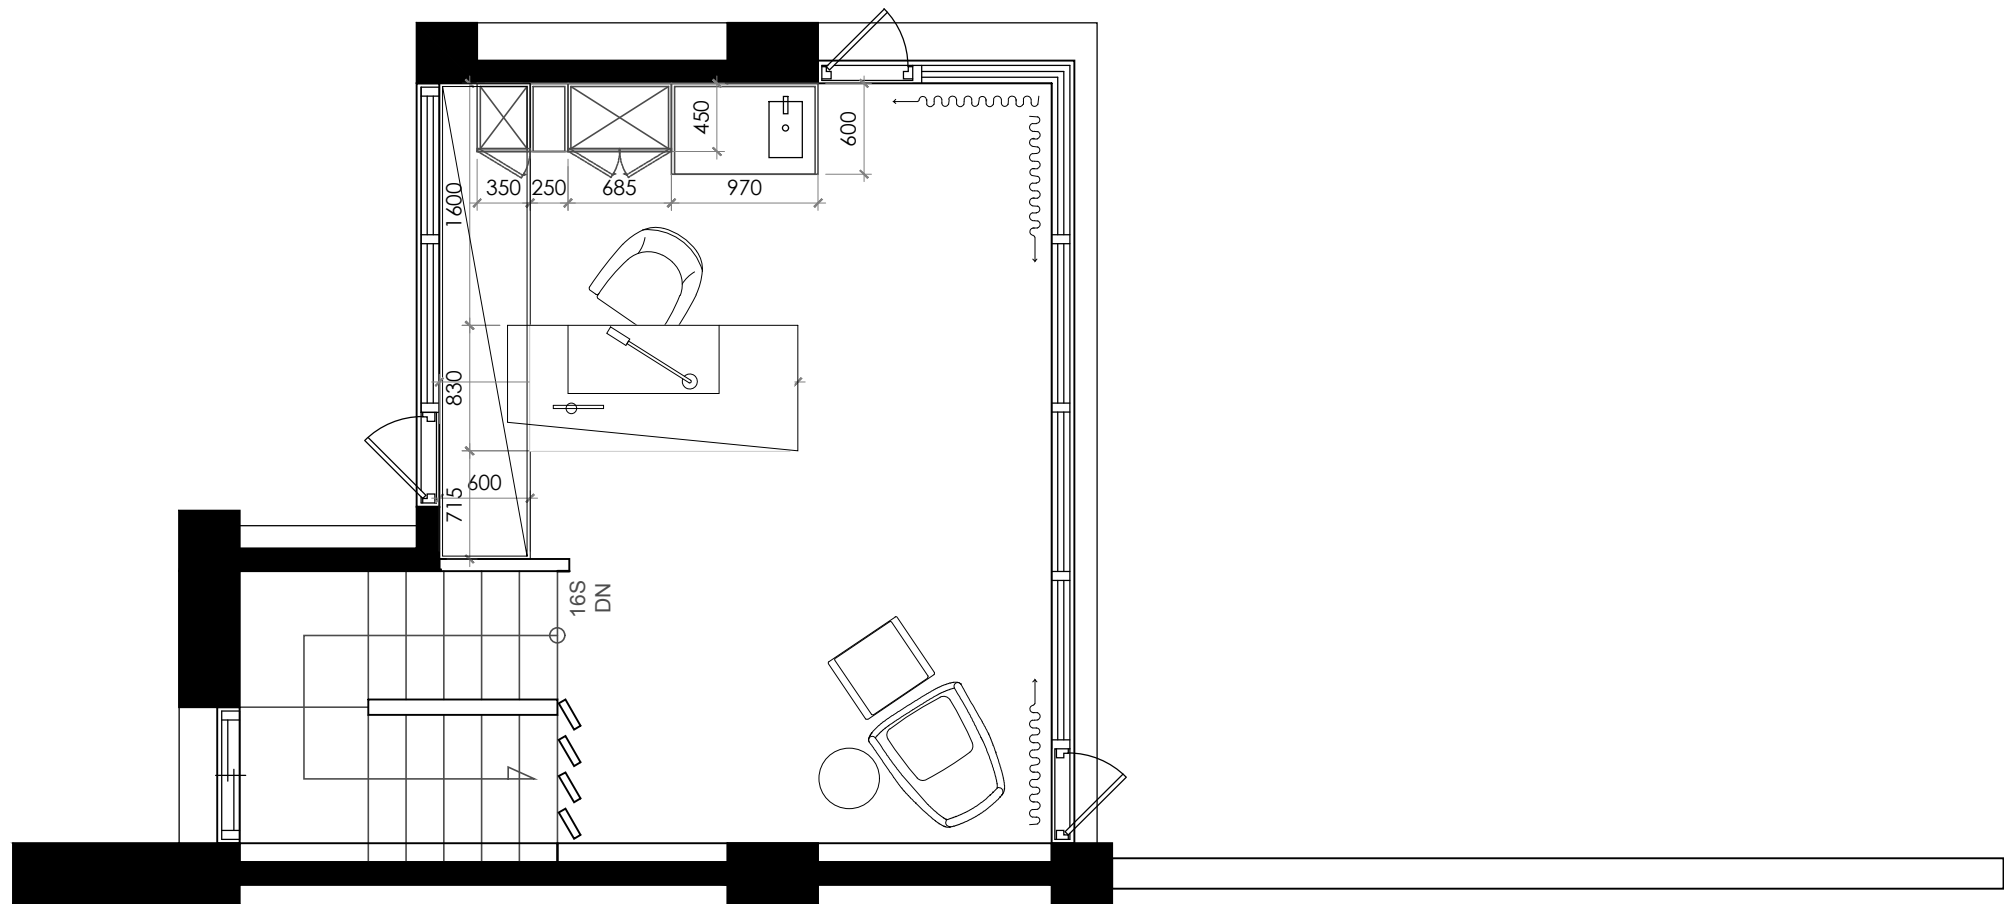

突二層平面圖