
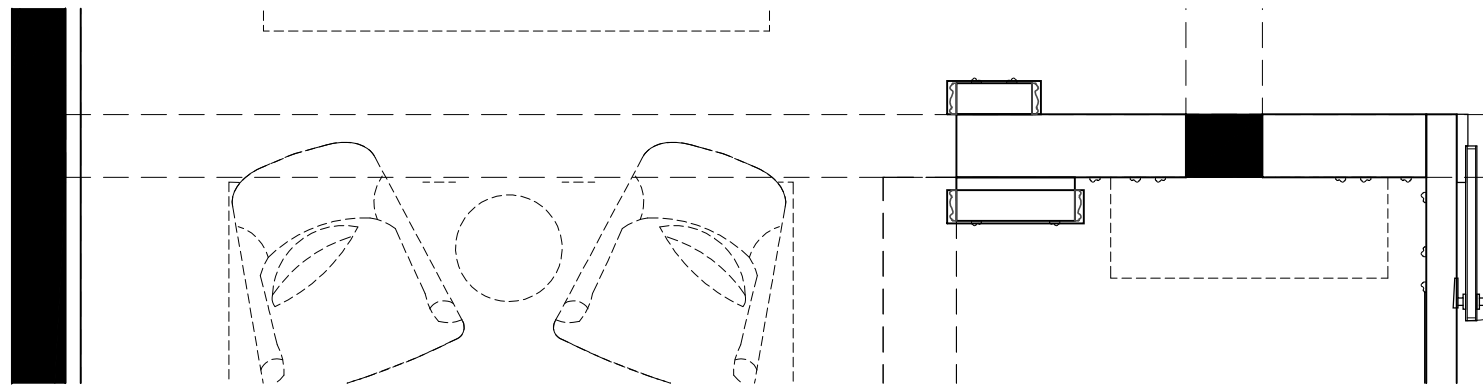


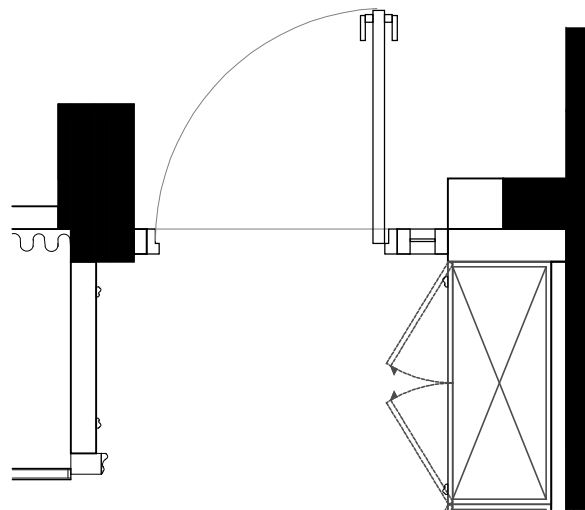


▲CH 2902mm

▲CH 2650mm

▼FL ±0 mm


▲FL -50 mm

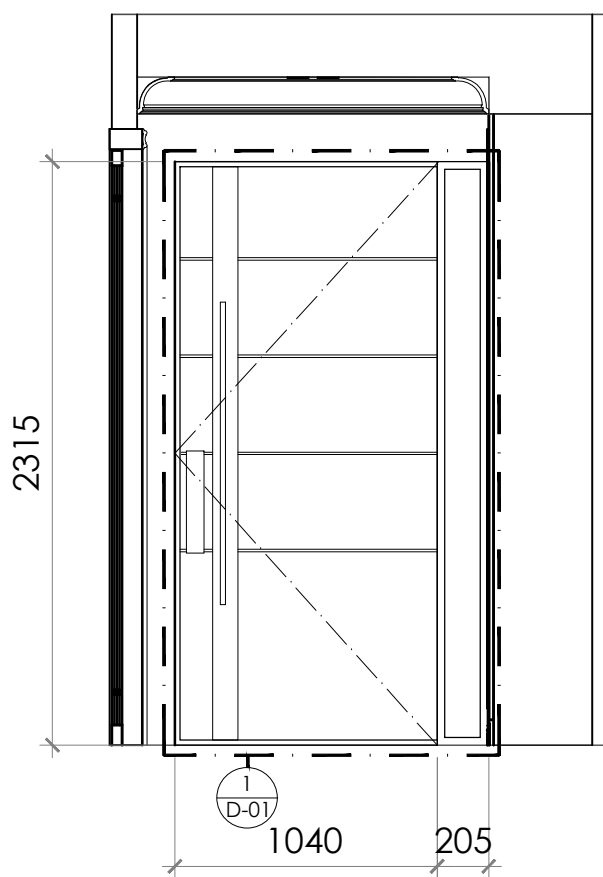

1
E-01

ELEVATION

Scale=1:30

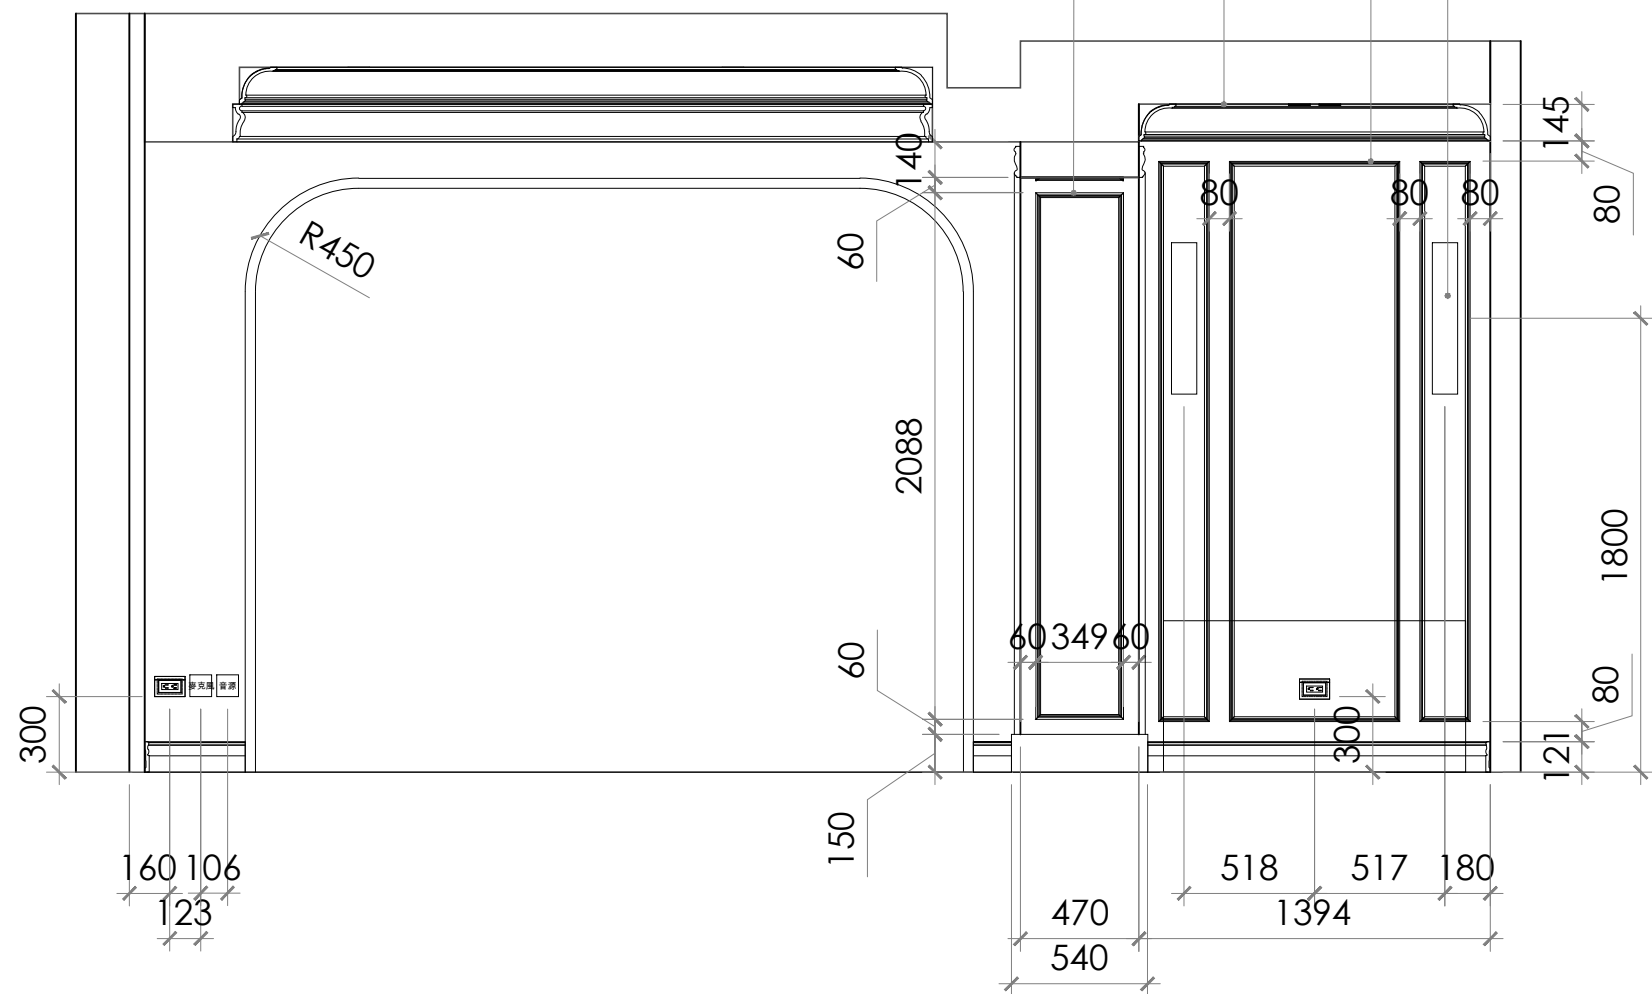

2
E-01

ELEVATION

Scale=1:30

Revision

APPROVAL/核准

設計者:	建築師:
業主:	

備註:

- 圖面標註尺寸僅供參考，施作均以現場放樣檢討之。
- 圖面標註尺寸、材料及文字敘述因版本不同之差異，均以出圖章簽認日期之最近為準。
- 電腦圖檔除由合約訂定外，均不得以任何方式外流。
- 圖面所示均為本公司所擁有之智慧財產，切勿以任何方式複製修改。



MULA DECO

▲ 3F, N.26, Ln.290, Guangfu S. Rd., Taipei.
☎ 886-2-2546-3258
☎ 886-2-2546-3257
✉ Guido@muladeco.com

Project / 案名

天母葉公館

Sheet Title / 圖名



1F

立面圖

Date / 日期	Scale / 比例
8/10/2026	1/30CM
Designer / 設計	Approval / 核准
MONICA LIN	
Job No / 業務編號	Drawn By / 繪圖
00000	GUIDO
Dwg No.	Page No.

E-01

28

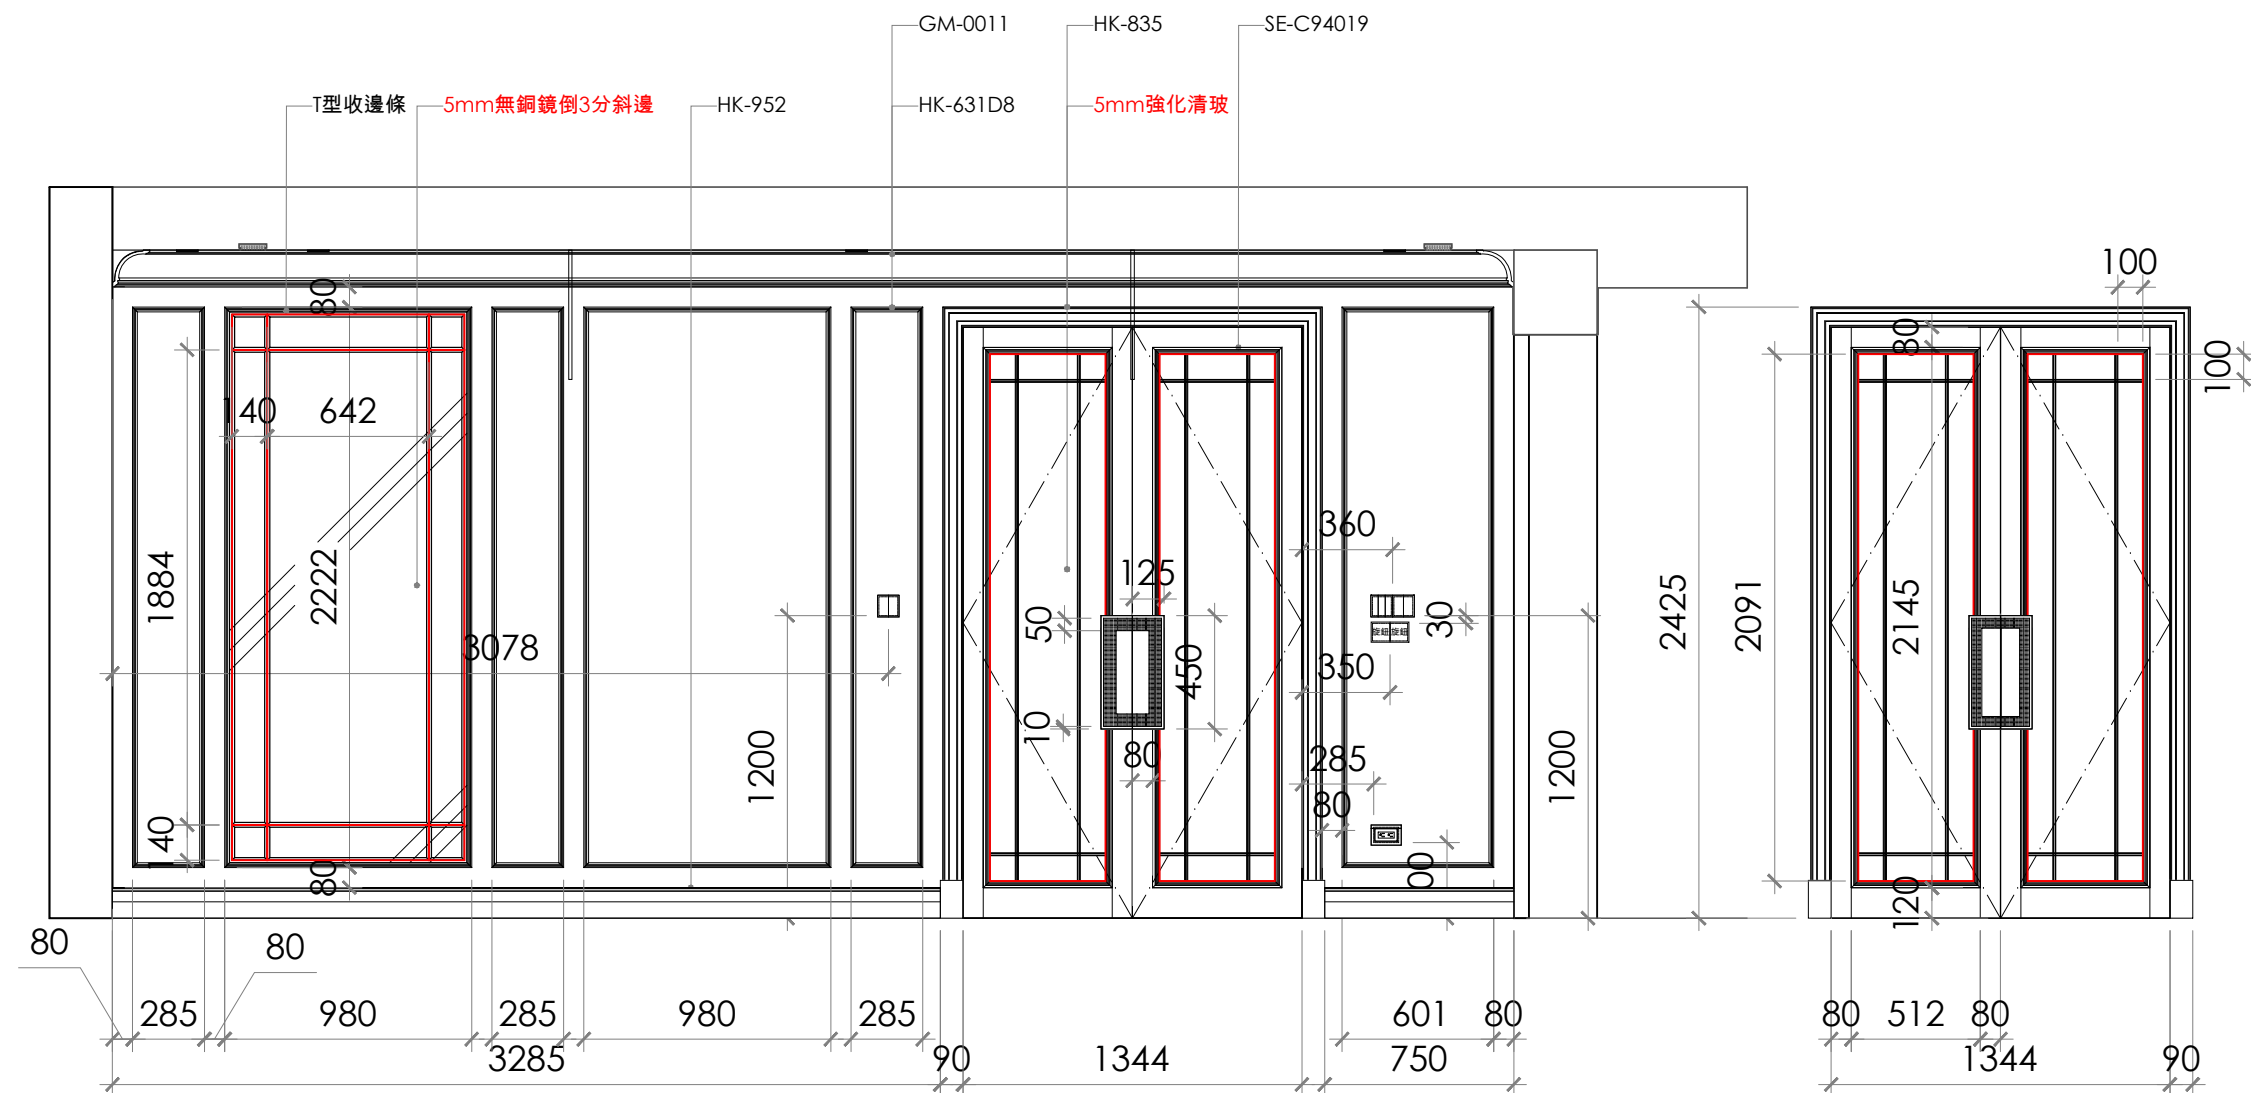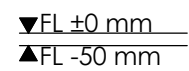

1 ELEVATION
E-02 Scale=1:30

[illegible]

APPROVAL/核准

設計者:	建築師:
業主:	

葡註:

- g. 圖面標註尺寸僅供參考，施作均以現場放樣檢討之。
- h. 圖面標註尺寸、材料及文字敘述因版本不同之差異，均以出圖章簽認日期之最近為準。
- i. 電腦圖檔除由合約訂定外，均不得以任何方式外流。
- j. 圖面所示均為本公司所擁有之智慧財產，切勿以任何方式複製修改。



MULA DECO

A 3F, N.26, Ln.290, Guangfu S. Rd., Taipei.
T 886-2-2546-3258
F 886-2-2546-3257
E Guido@muladeco.com


Project / 案名

天母葉公館

Sheet Title / 圖名
1F

立面圖

Date / 日期	Scale / 比例
8/10/2026	1/30CM
Designer / 設計	Approval / 核准
MONICA LIN	ABC
Job No / 業務編號	Drawn By / 繪圖
00000	GUIDO
Dwg No.	Page No.
E-02	29

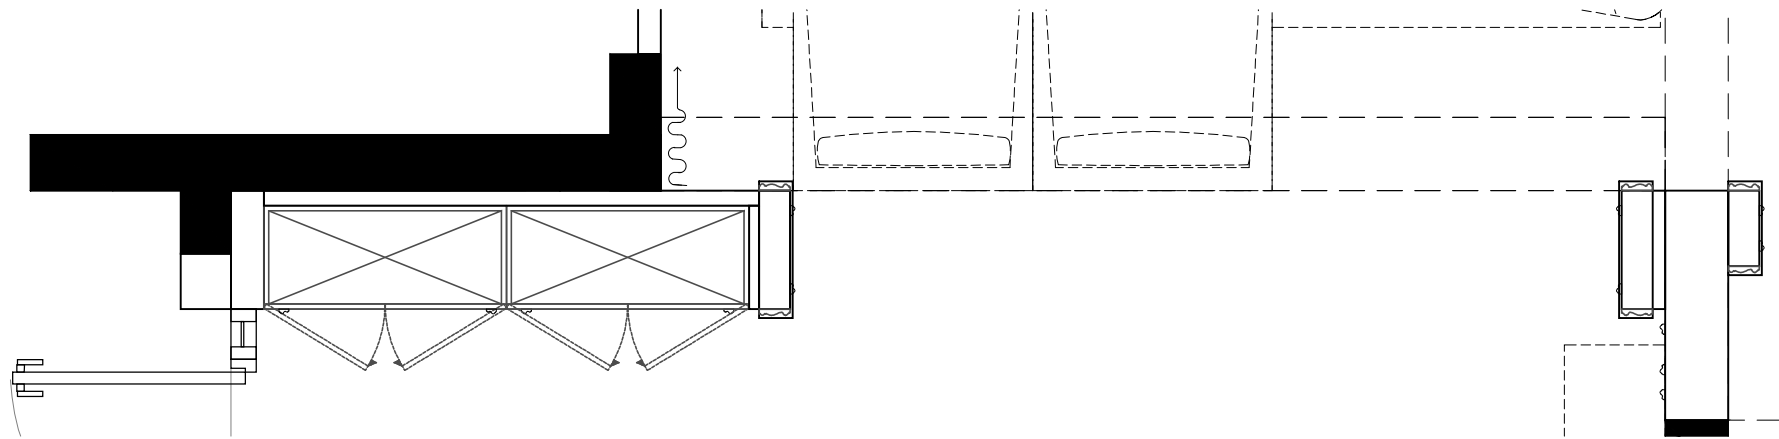


▲CH 2902mm

▲CH 2650mm

▼FL ±0 mm

▲FL -50 mm

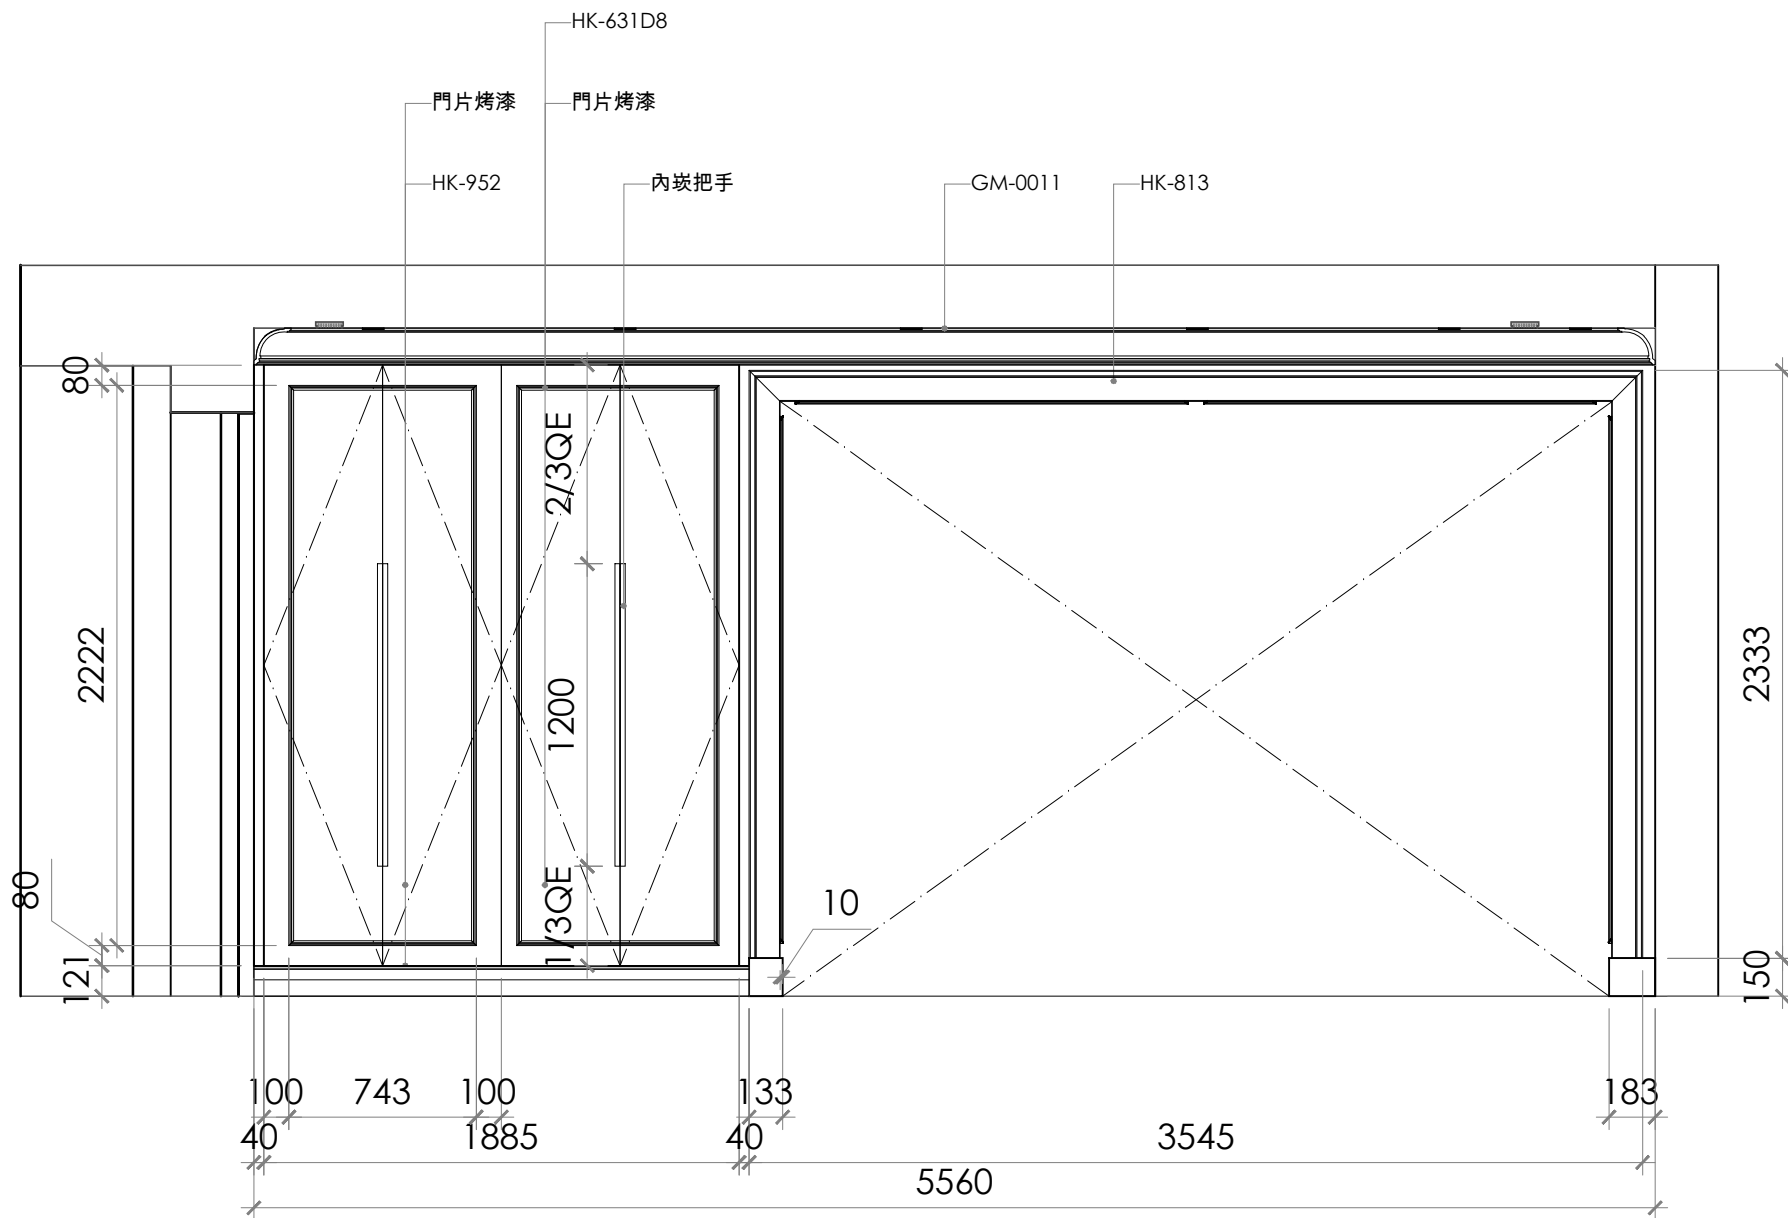

1
E-03

ELEVATION

Scale=1:30

Revision

APPROVAL/核准

設計者:	建築師:
業主:	

備註:

- a. 圖面標註尺寸僅供參考，施作均以現場放樣檢討之。
- b. 圖面標註尺寸、材料及文字敘述因版本不同之差異，均以出圖章簽認日期之最近為準。
- c. 電腦圖檔除由合約訂定外，均不得以任何方式外流。
- d. 圖面所示均為本公司所擁有之智慧財產，切勿以任何方式複製修改。



MULA DECO

▲ 3F, N.26, Ln.290, Guangfu S. Rd., Taipei.
☎ 886-2-2546-3258
☎ 886-2-2546-3257
✉ Guido@muladeco.com

Project / 案名


天母葉公館

Sheet Title / 圖名

1F

立面圖

Date / 日期	Scale / 比例
8/10/2026	1/30CM
Designer / 設計	Approval / 核准
MONICA LIN	
Job No / 業務編號	Drawn By / 繪圖
00000	GUIDO
Dwg No.	Page No.
E-03	30

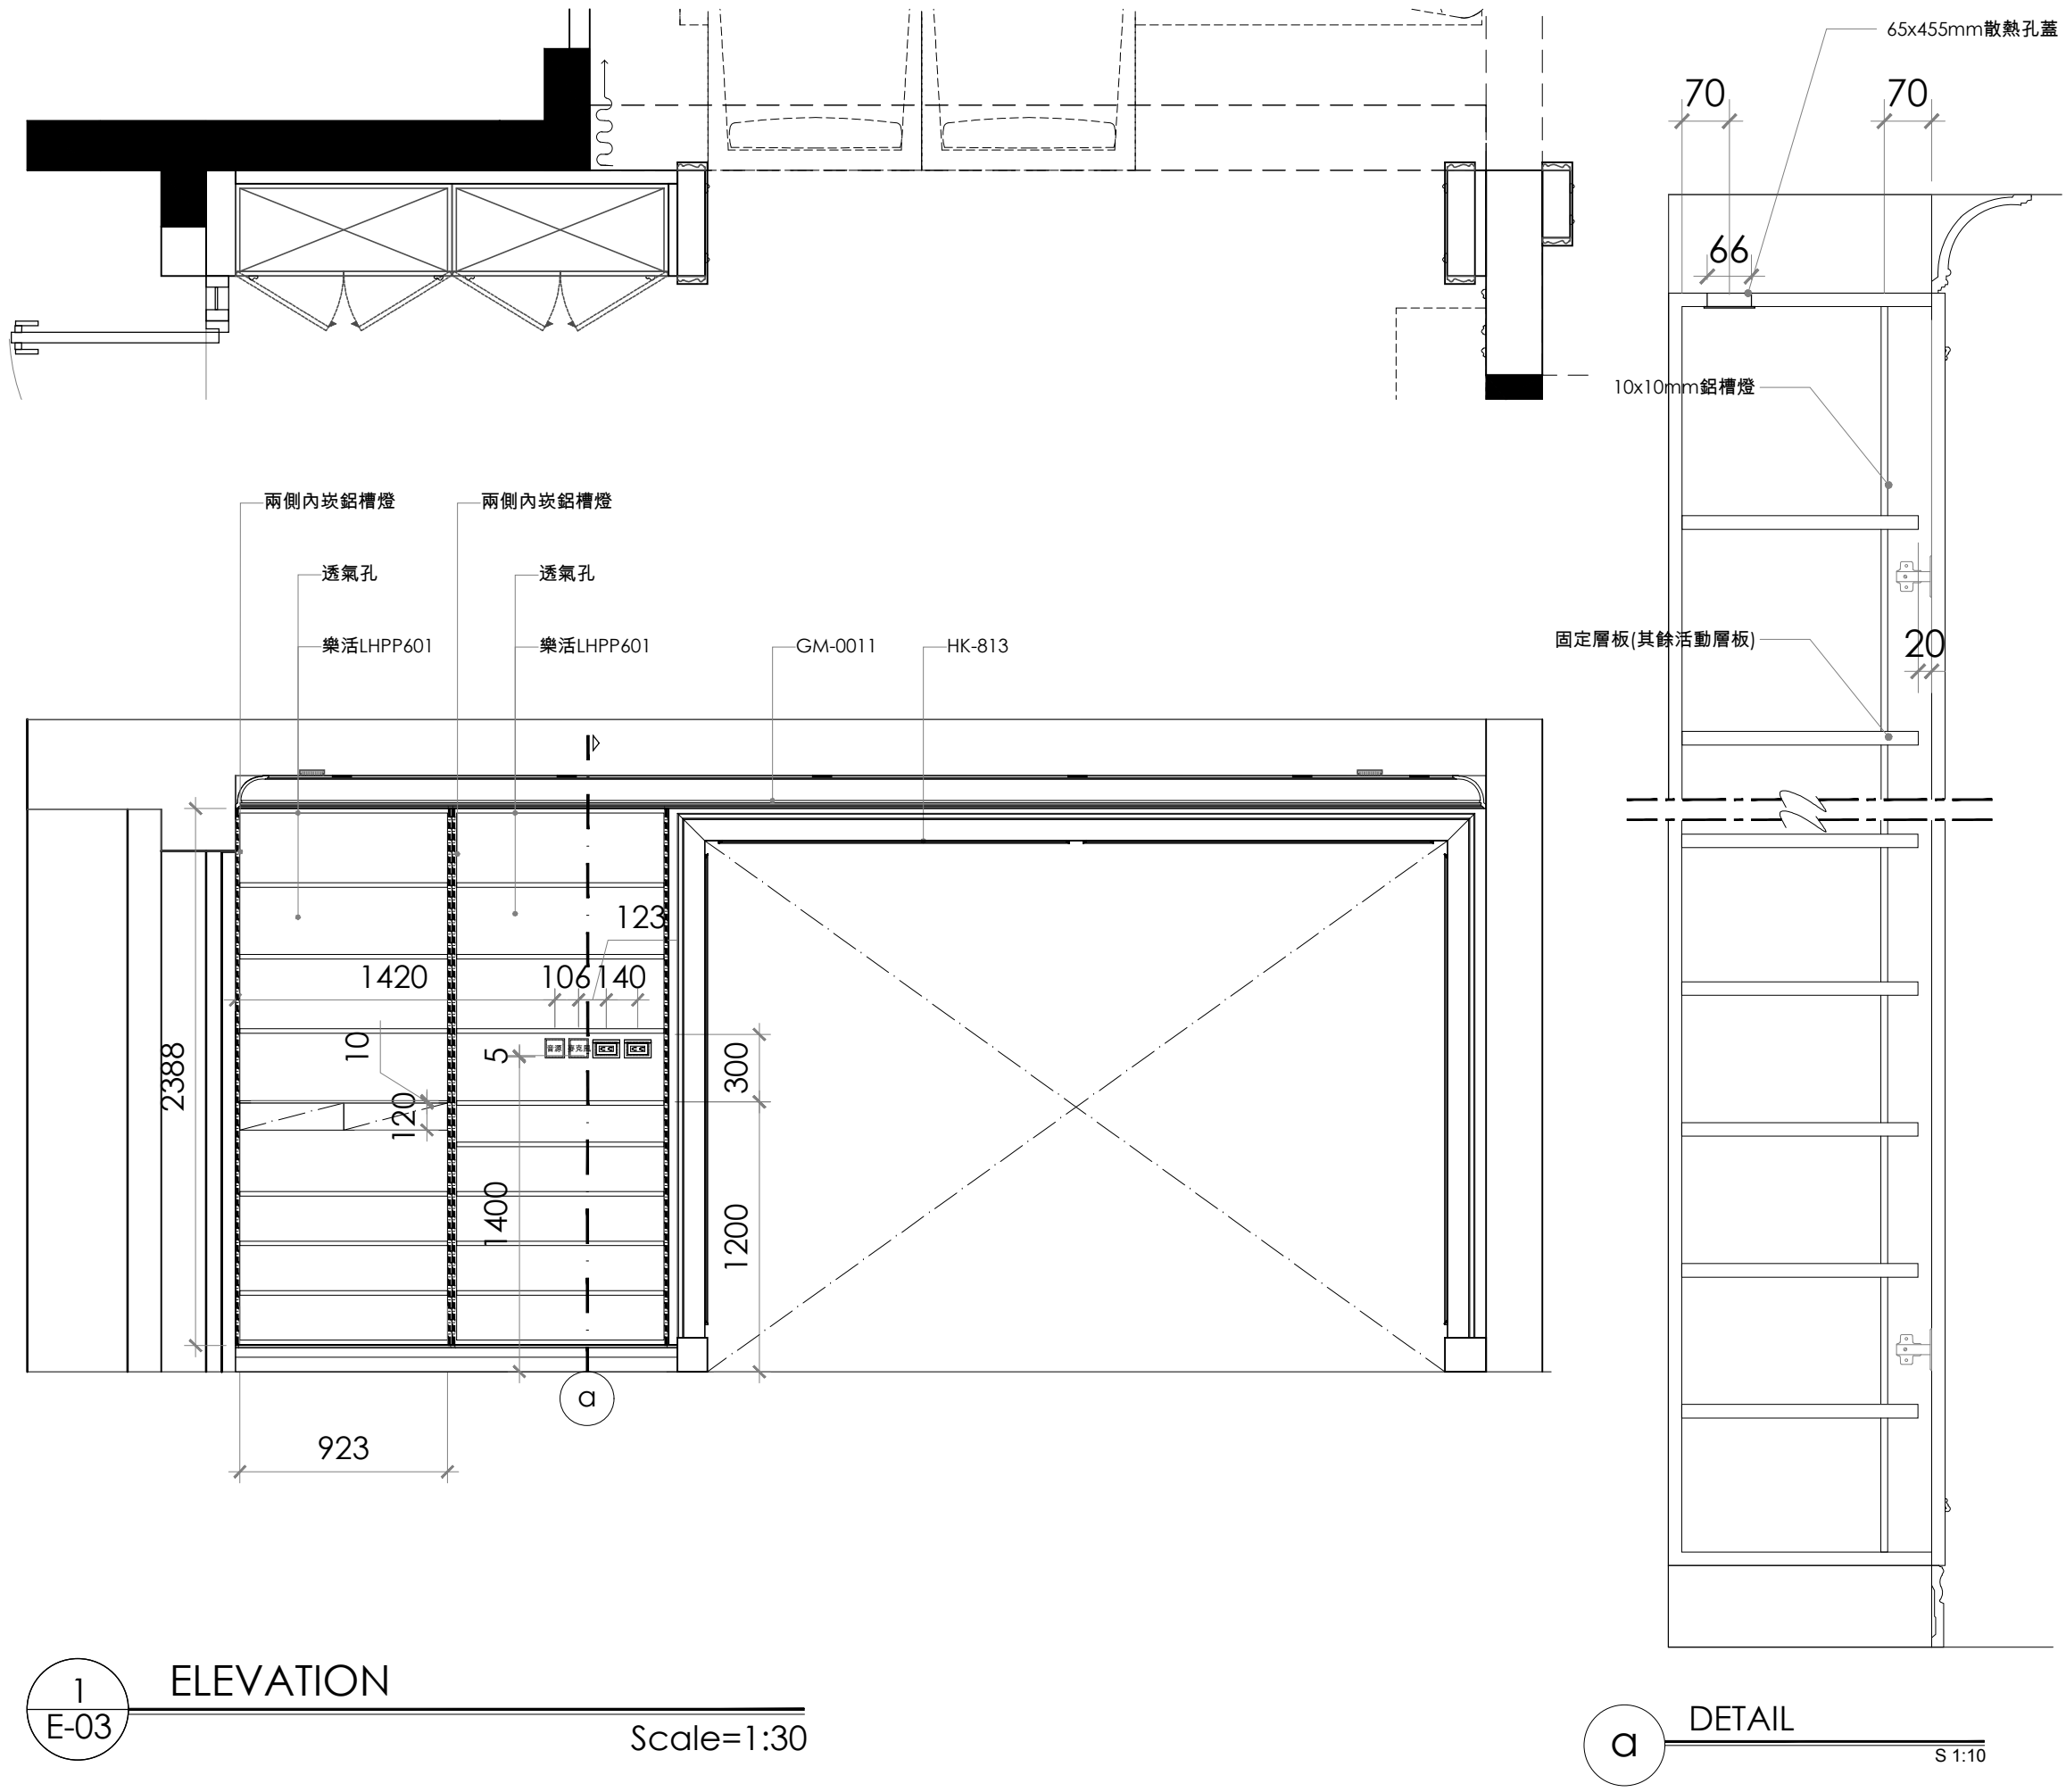

Revision	
APPROVAL / 核准	
設計者:	建築師:
業主:	

備註:
a. 圖面標註尺寸僅供參考，施作均以現場放樣檢討之。
b. 圖面標註尺寸、材料及文字敘述因版本不同之差異，均以圖章簽認日期之最近為準。
c. 電腦圖檔除由合約訂定外，均不得以任何方式外流。
d. 圖面所示均為本公司所擁有之智慧財產，切勿以任何方式複製修改。



MULA DECO

▲ 3F, N.26, Ln.290, Guangfu S. Rd., Taipei.
☎ 886-2-2546-3258
☎ 886-2-2546-3257
✉ Guido@muladeco.com

Project / 案名


天母葉公館

Sheet Title / 圖名

1F

立面圖


Date / 日期	Scale / 比例
8/10/2026	1/30CM
Designer / 設計	Approval / 核准
MONICA LIN	
Job No / 業務編號	Drawn By / 繪圖
00000	GUIDO
Dwg No.	Page No.
E-03	31

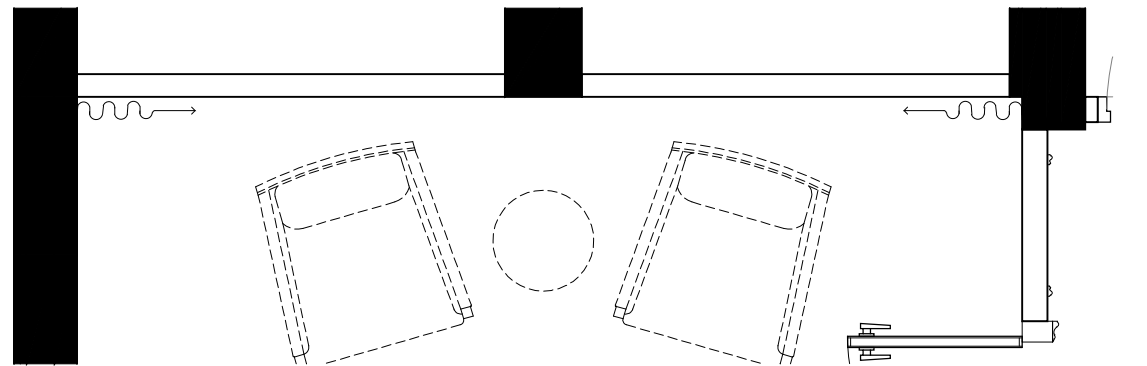

▲CH 2900mm

▲CH 2450mm

▼FL ±0 mm
▲FL -50 mm

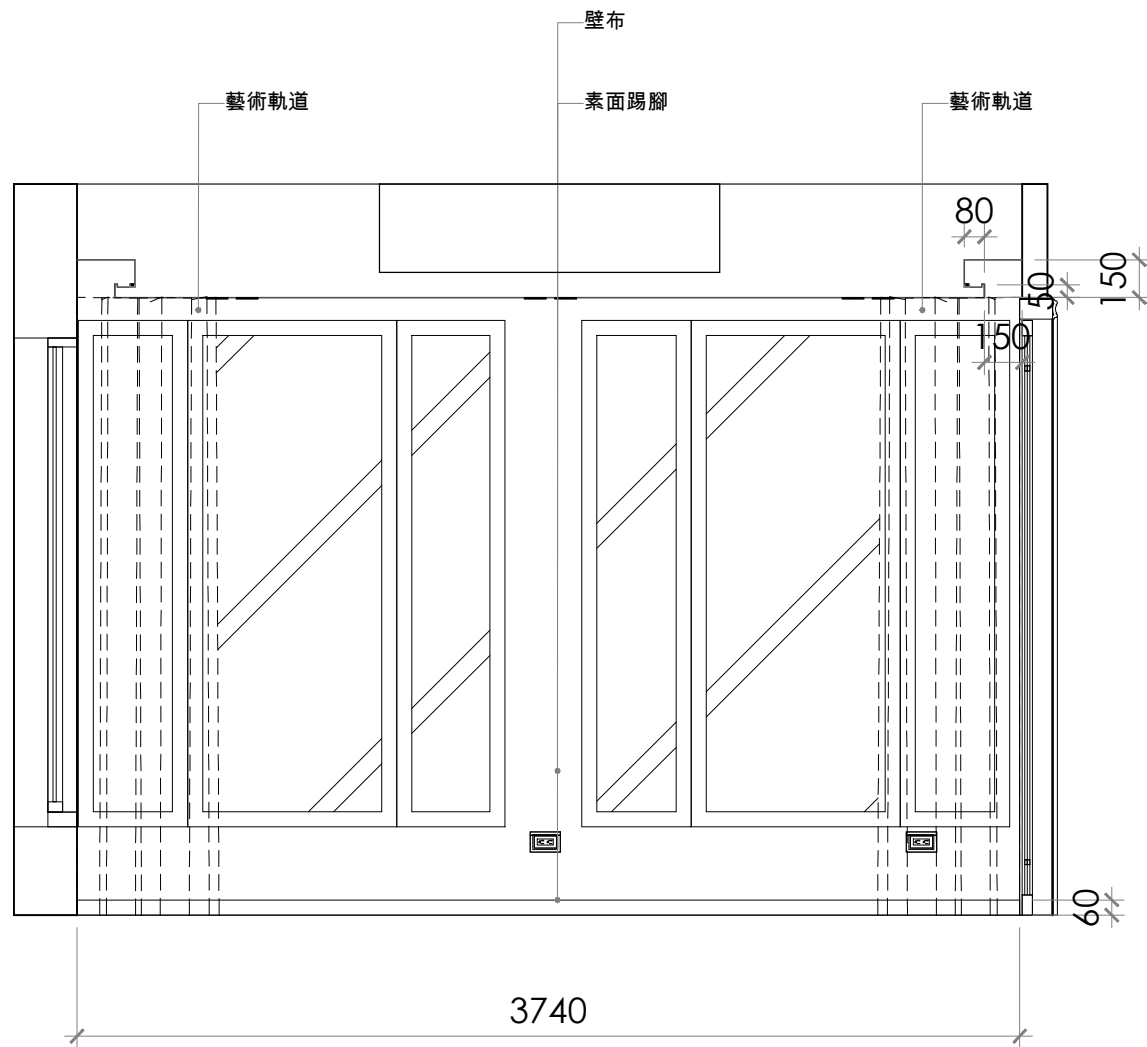

1
E-04

ELEVATION

Scale=1:30

Revision

APPROVAL/核准

設計者:	建築師:
業主:	

備註:

- 圖面標註尺寸僅供參考，施作均以現場放樣檢討之。
- 圖面標註尺寸、材料及文字敘述因版本不同之差異，均以出圖章簽認日期之最近為準。
- 電腦圖檔除由合約訂定外，均不得以任何方式外流。
- 圖面所示均為本公司所擁有之智慧財產，切勿以任何方式複製修改。



MULA DECO

▲ 3F, N.26, Ln.290, Guangfu S. Rd., Taipei.
☎ 886-2-2546-3258
☎ 886-2-2546-3257
✉ Guido@muladeco.com

Project / 案名


天母葉公館

Sheet Title / 圖名

1F

立面圖

Date / 日期	Scale / 比例
8/10/2026	1/30CM
Designer / 設計	Approval / 核准
MONICA LIN	
Job No / 業務編號	Drawn By / 繪圖
00000	GUIDO
Dwg No.	Page No.
E-04	32

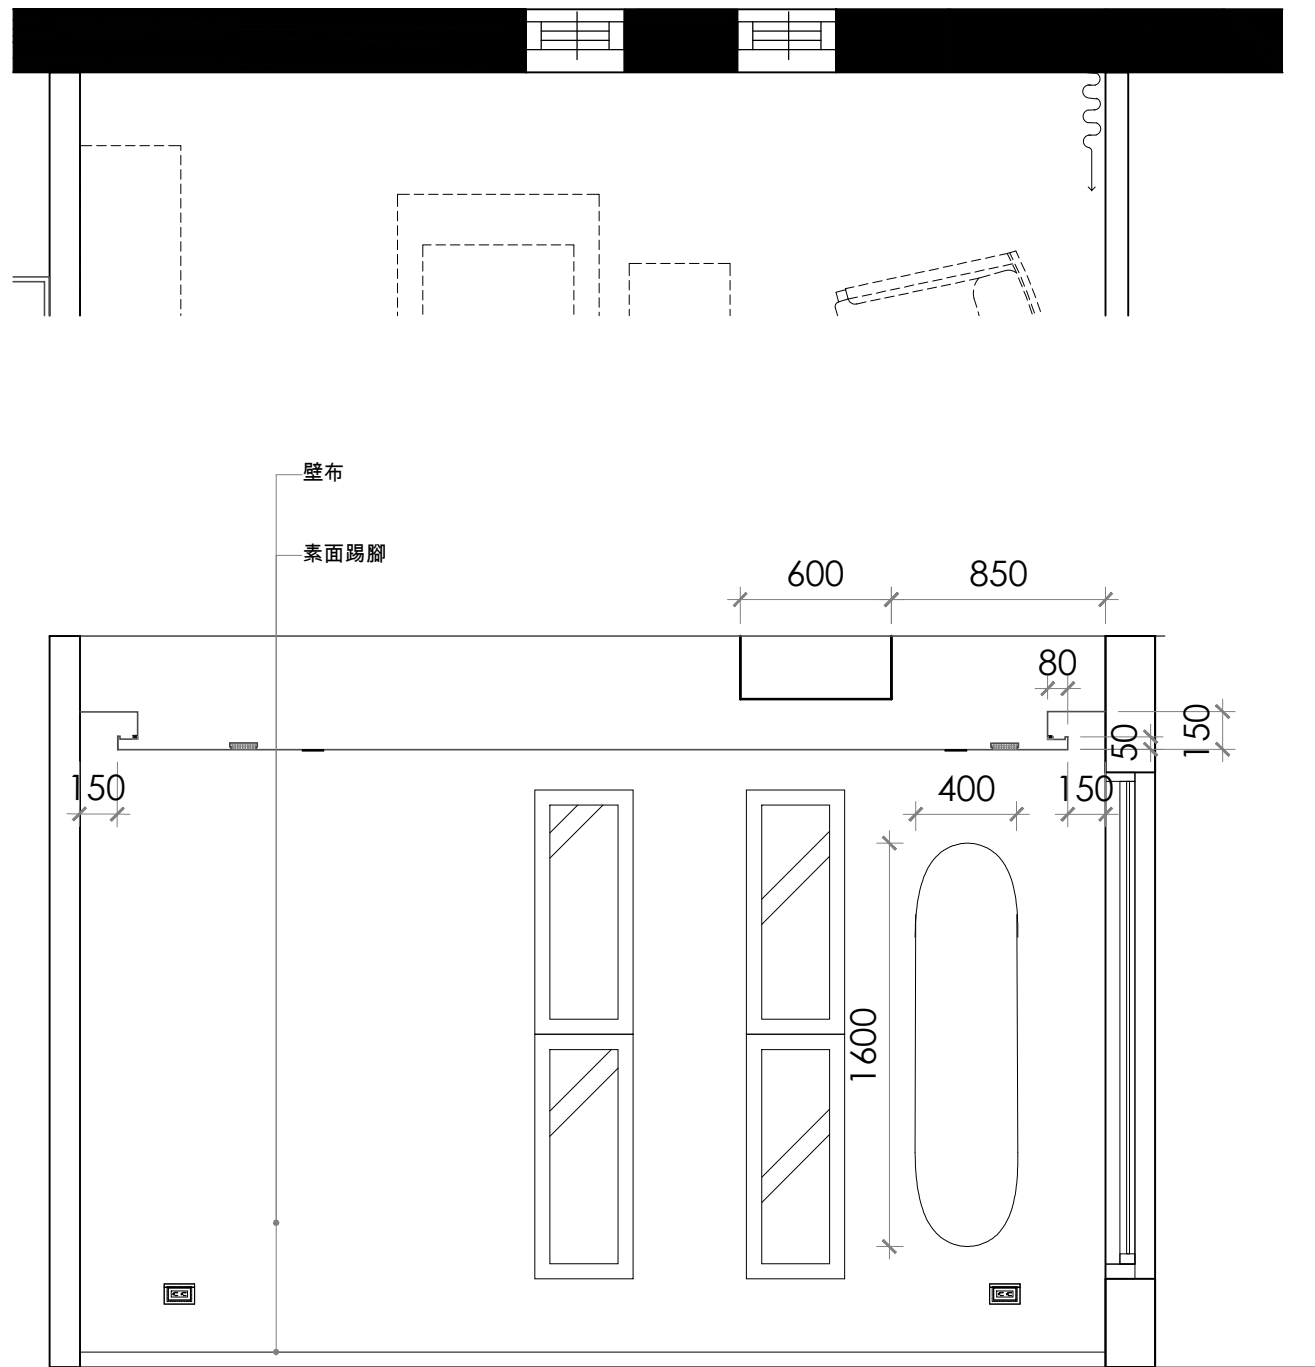

1
E-05

ELEVATION

Scale=1:30

Revision	
APPROVAL/核准	
設計者:	建築師:
業主:	


備註:
a. 圖面標註尺寸僅供參考，施作均以現場放樣檢討之。
b. 圖面標註尺寸、材料及文字敘述因版本不同之差異，均以出圖章簽認日期之最近為準。
c. 電腦圖檔除由合約訂定外，均不得以任何方式外流。
d. 圖面所示均為本公司所擁有之智慧財產，切勿以任何方式複製修改。



MULA DECO

▲ 3F, N.26, Ln.290, Guangfu S. Rd., Taipei.
☎ 886-2-2546-3258
☎ 886-2-2546-3257
✉ Guido@muladeco.com

Project / 案名	
天母葉公館	
Sheet Title / 圖名	
1F 立面圖	
Date / 日期	Scale / 比例
8/10/2026	1/30CM
Designer / 設計	Approval / 核准
MONICA LIN	
Job No / 業務編號	Drawn By / 繪圖
00000	GUIDO
Dwg No.	Page No.
E-05	33

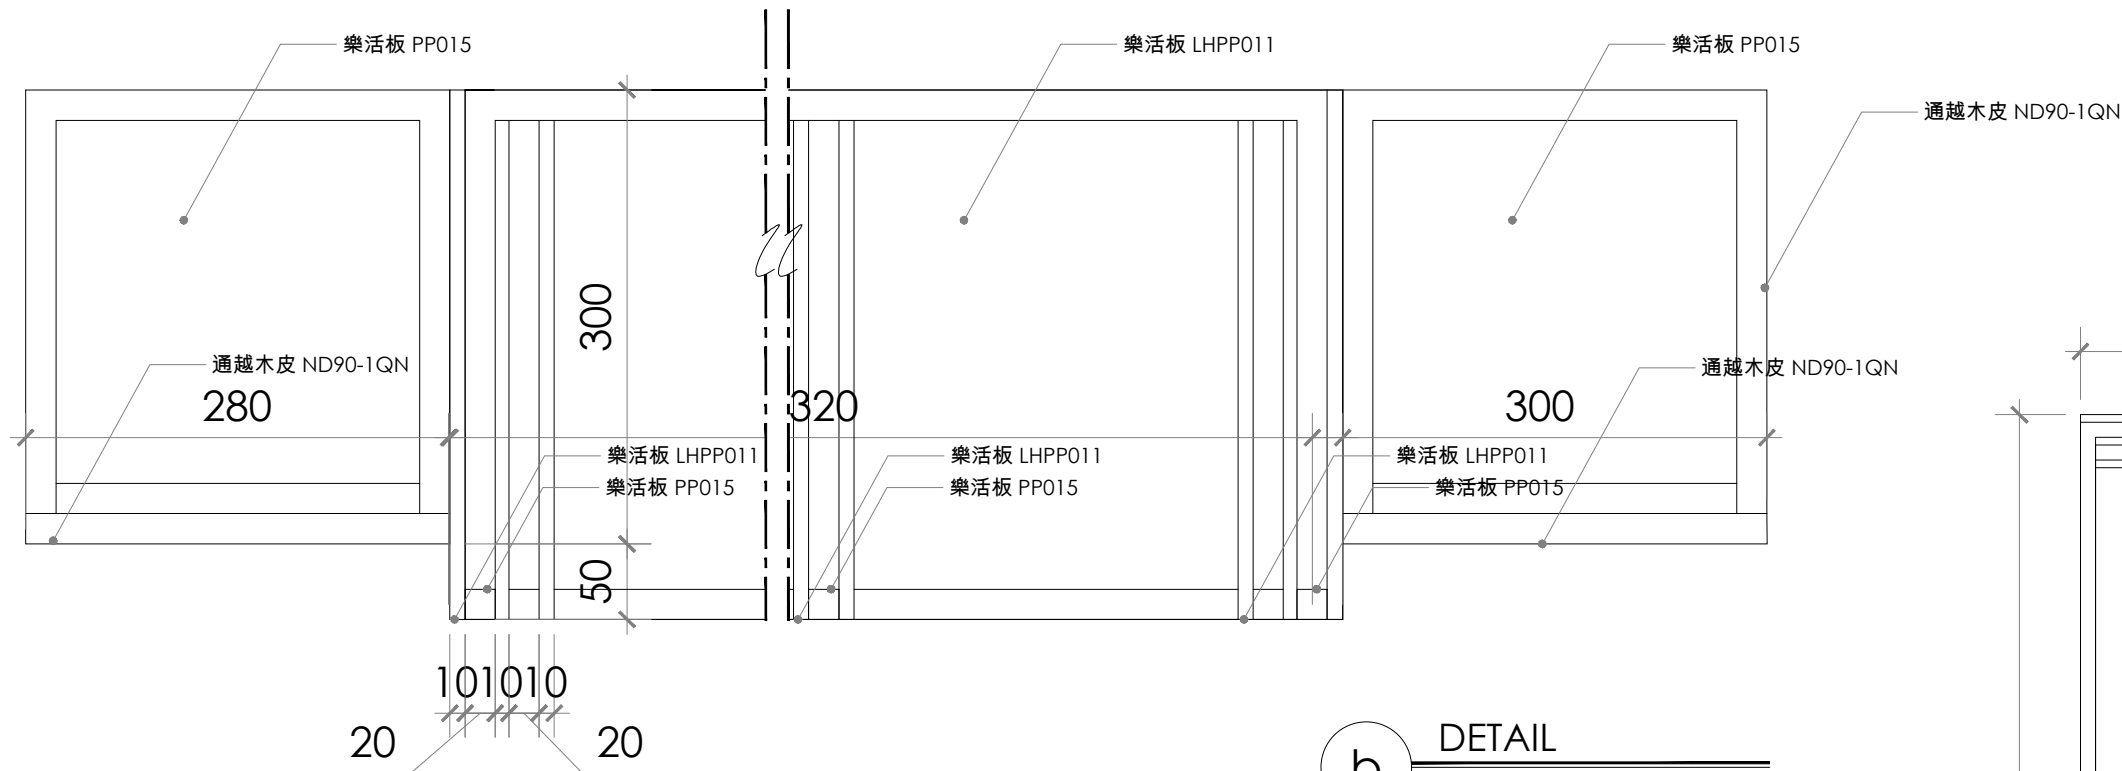


b DETAIL S 1:5


▲CH 2900mm

▲CH 2450mm

▼FL ±0 mm
▲FL -50 mm

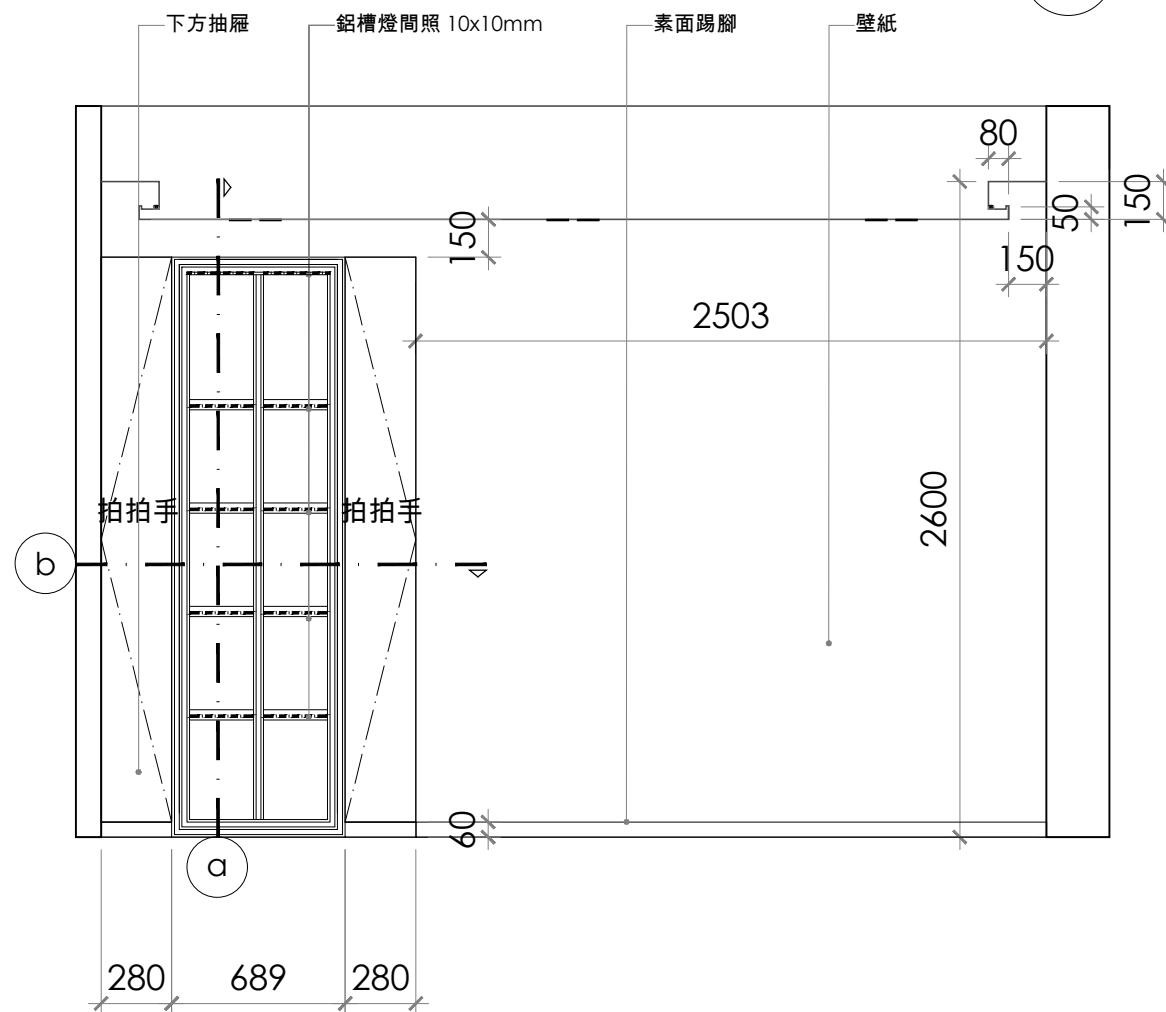

1 ELEVATION E-06 Scale=1:30

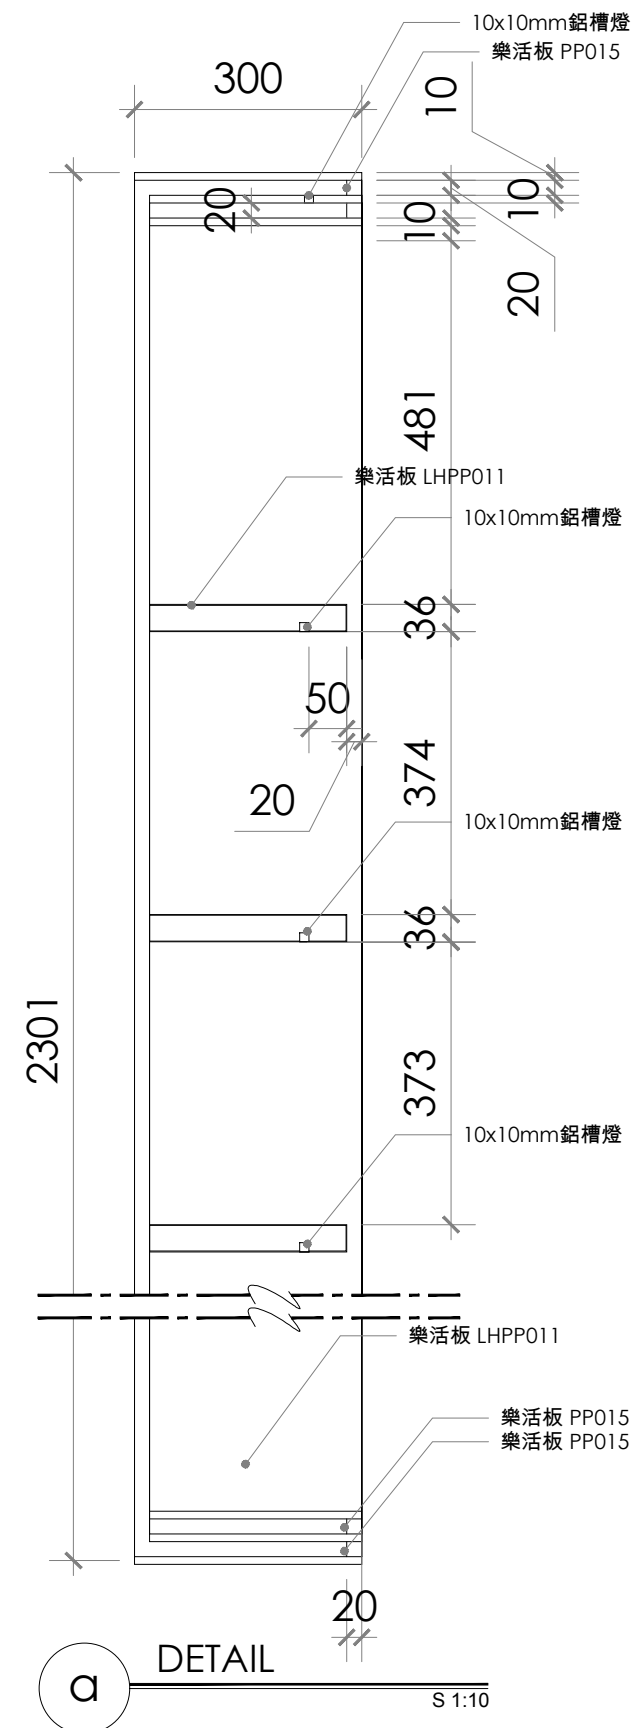

a DETAIL S 1:10

Revision

APPROVAL/核准

設計者:	建築師:
業主:	

備註:

- 圖面標註尺寸僅供參考，施作均以現場放樣檢討之。
- 圖面標註尺寸、材料及文字敘述因版本不同之差異，均以出圖章簽認日期之最近為準。
- 電腦圖檔除由合約訂定外，均不得以任何方式外流。
- 圖面所示均為本公司所擁有之智慧財產，切勿以任何方式複製修改。



MULA DECO

▲ 3F, N.26, Ln.290, Guangfu S. Rd., Taipei.
☎ 886-2-2546-3258
☎ 886-2-2546-3257
✉ Guido@muladeco.com



Project / 案名

天母葉公館

Sheet Title / 圖名
1F

立面圖


Date / 日期	Scale / 比例
8/10/2026	1/30CM
Designer / 設計	Approval / 核准
MONICA LIN	
Job No / 業務編號	Drawn By / 繪圖
00000	GUIDO
Dwg No.	Page No.
E-06	34

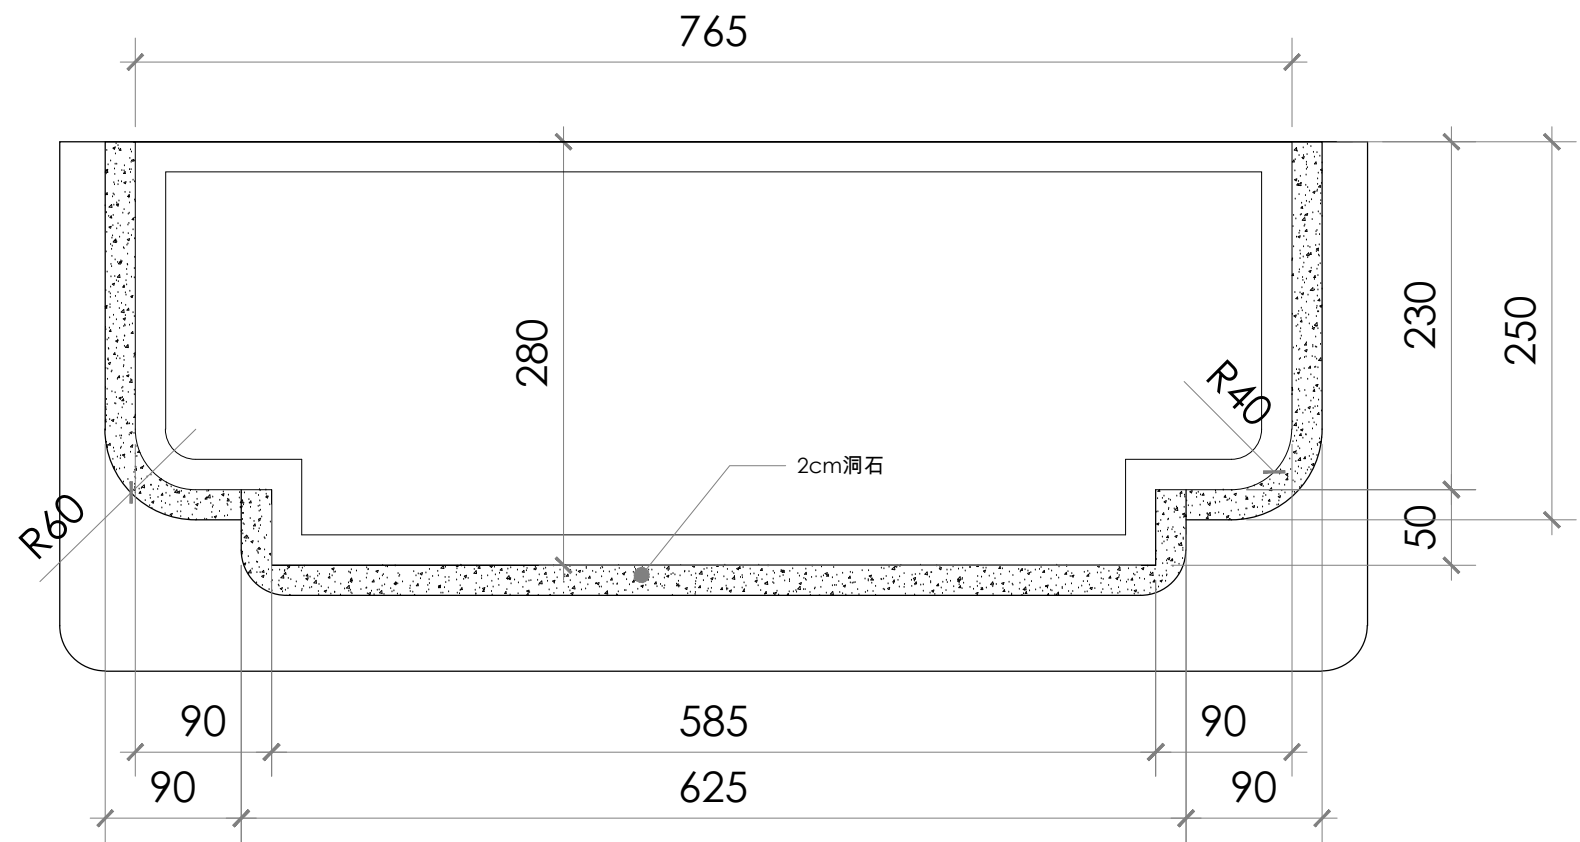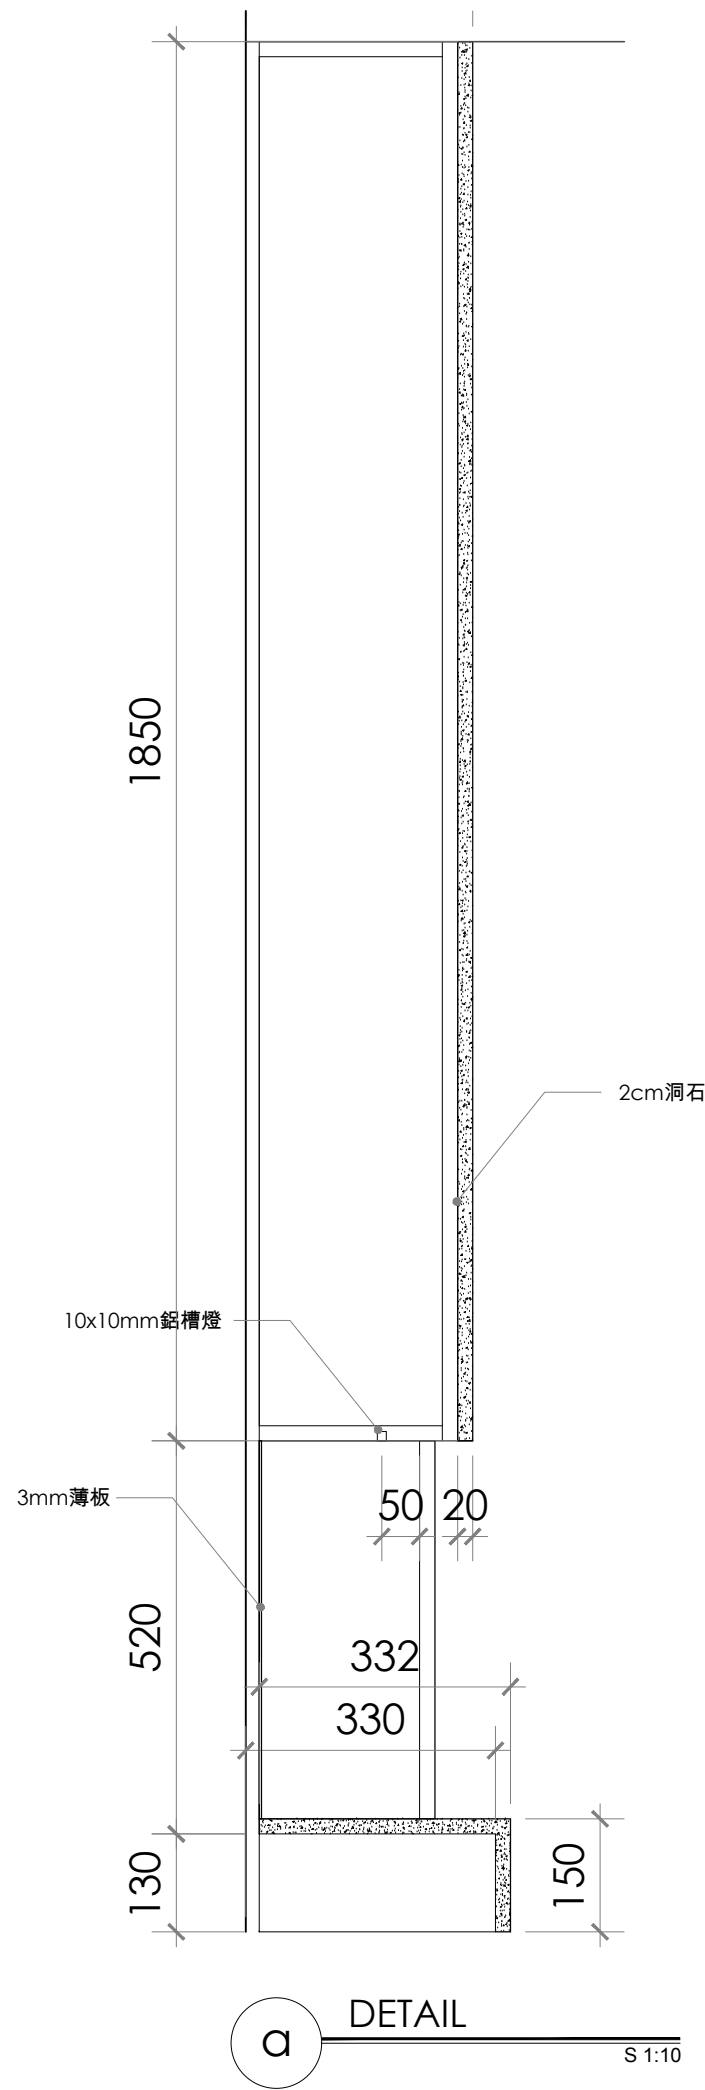

b

DETAIL

S 1:5

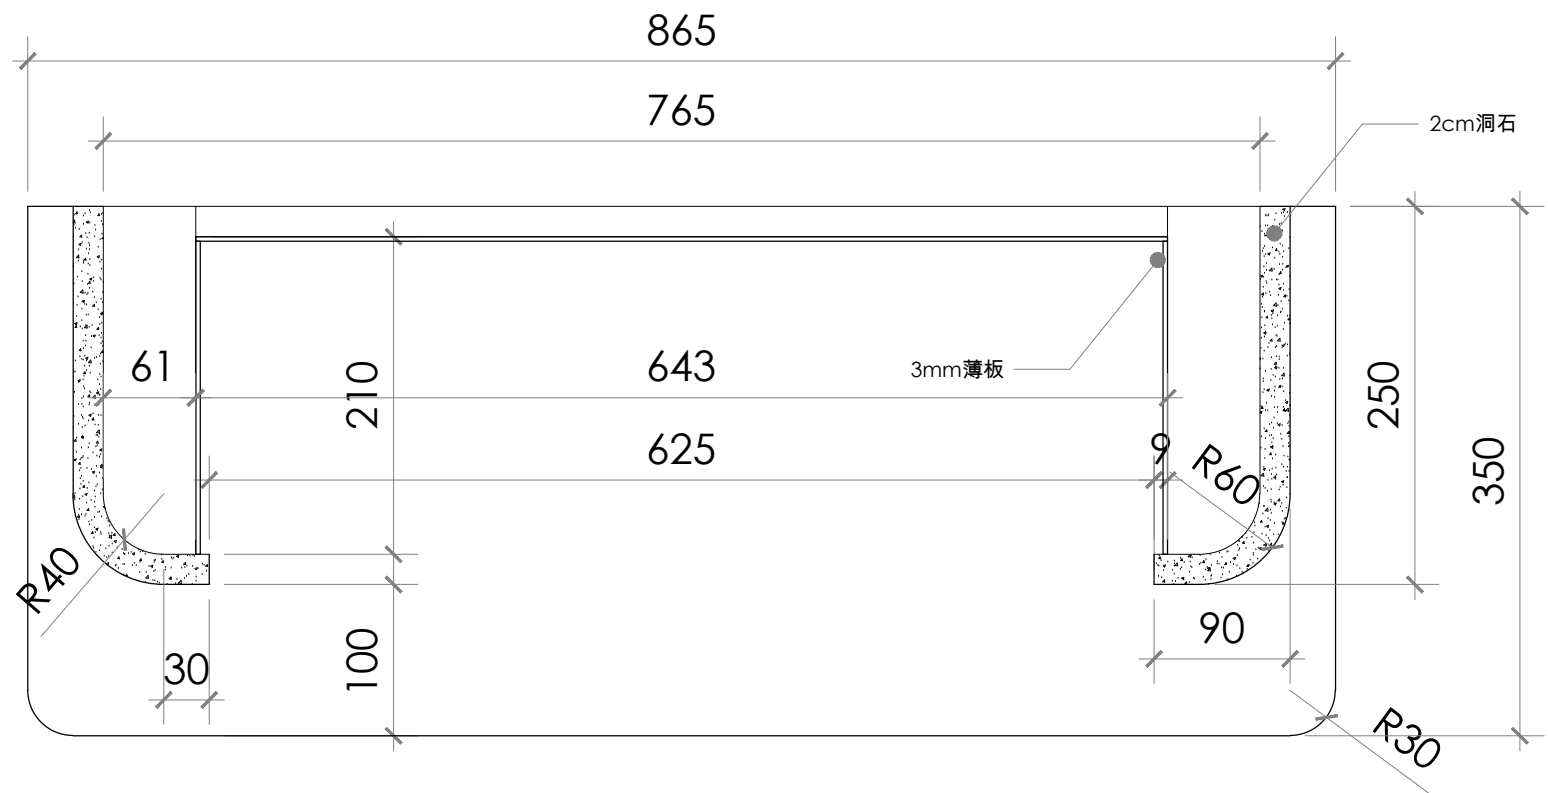

c

DETAIL

S 1:5

Revision	
APPROVAL / 核准	
設計者:	建築師:
業主:	

備註:

a. 圖面標註尺寸僅供參考，施作均以現場放樣檢討之。

b. 圖面標註尺寸、材料及文字敘述因版本不同之差異，均以出圖章簽認日期之最近為準。

c. 電腦圖檔除由合約訂定外，均不得以任何方式外流。


d. 圖面所示均為本公司所擁有之智慧財產，切勿以任何方式複製修改。



MULA DECO

▲ 3F, N.26, Ln.290, Guangfu S. Rd., Taipei.
☎ 886-2-2546-3258
☎ 886-2-2546-3257
✉ Guido@muladeco.com

Project / 案名	
天母葉公館	
Sheet Title / 圖名	
1F 立面圖	
Date / 日期	Scale / 比例
8/10/2026	1/30CM
Designer / 設計	Approval / 核准
MONICA LIN	
Job No / 業務編號	Drawn By / 繪圖
00000	GUIDO
Dwg No.	Page No.
E-08	37

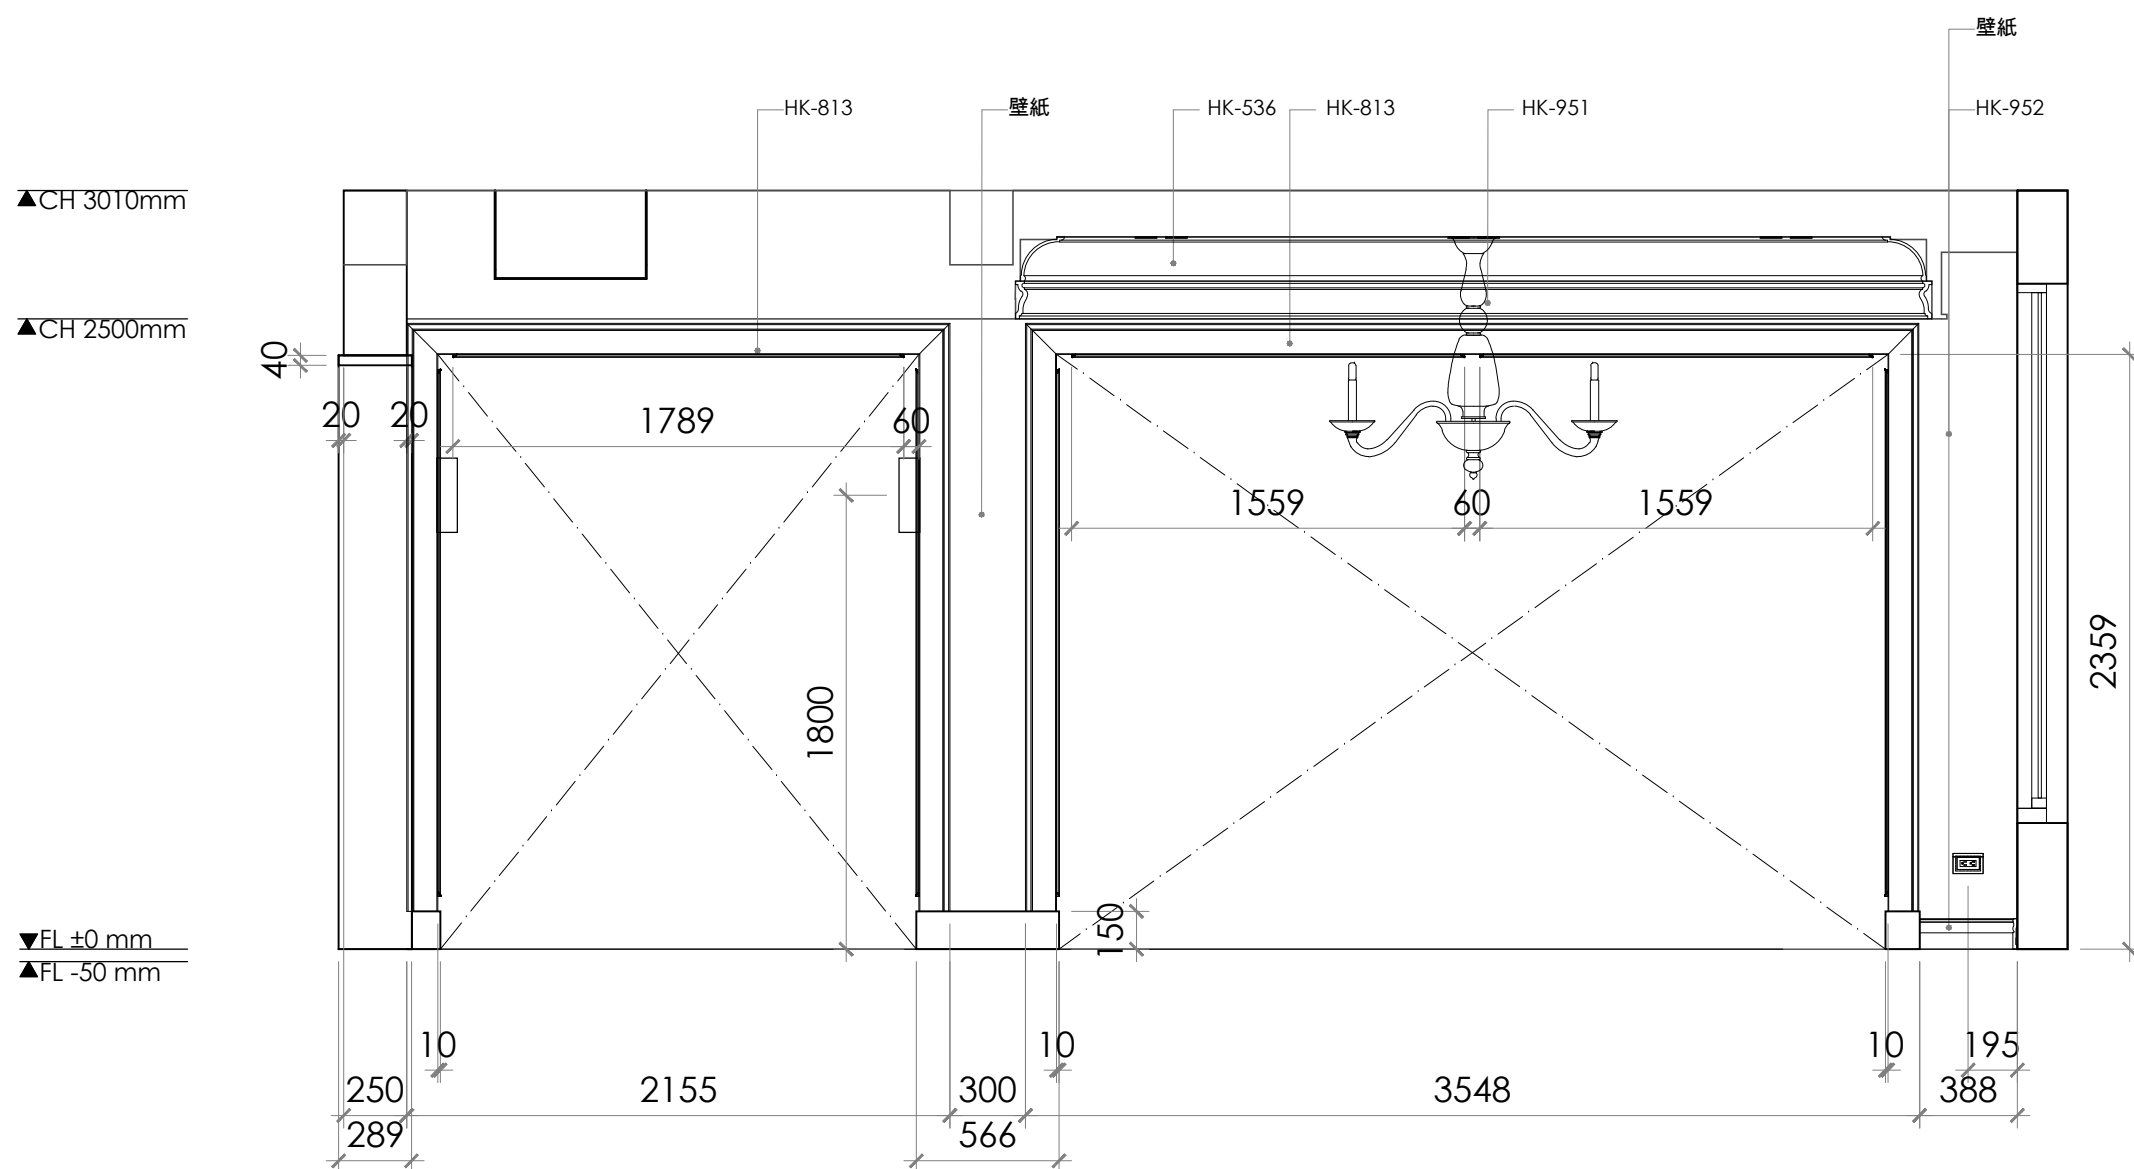

1
E-10

ELEVATION

Scale=1:30

Revision

APPROVAL/核准

設計者:	建築師:
業主:	

備註:

- a. 圖面標註尺寸僅供參考，施作均以現場放樣檢討之。
- b. 圖面標註尺寸、材料及文字敘述因版本不同之差異，均以出圖章簽認日期之最近為準。
- c. 電腦圖檔除由合約訂定外，均不得以任何方式外流。
- d. 圖面所示均為本公司所擁有之智慧財產，切勿以任何方式複製修改。



MULA DECO

A 3F, N.26, Ln.290, Guangfu S. Rd., Taipei.
T 886-2-2546-3258
F 886-2-2546-3257
E Guido@muladeco.com


Project / 案名

天母葉公館

Sheet Title / 圖名
1F

立面圖

Date / 日期	Scale / 比例
8/10/2026	1/30CM
Designer / 設計	Approval / 核准
MONICA LIN	
Job No / 業務編號	Drawn By / 繪圖
00000	GUIDO
Dwg No.	Page No.
E-10	39

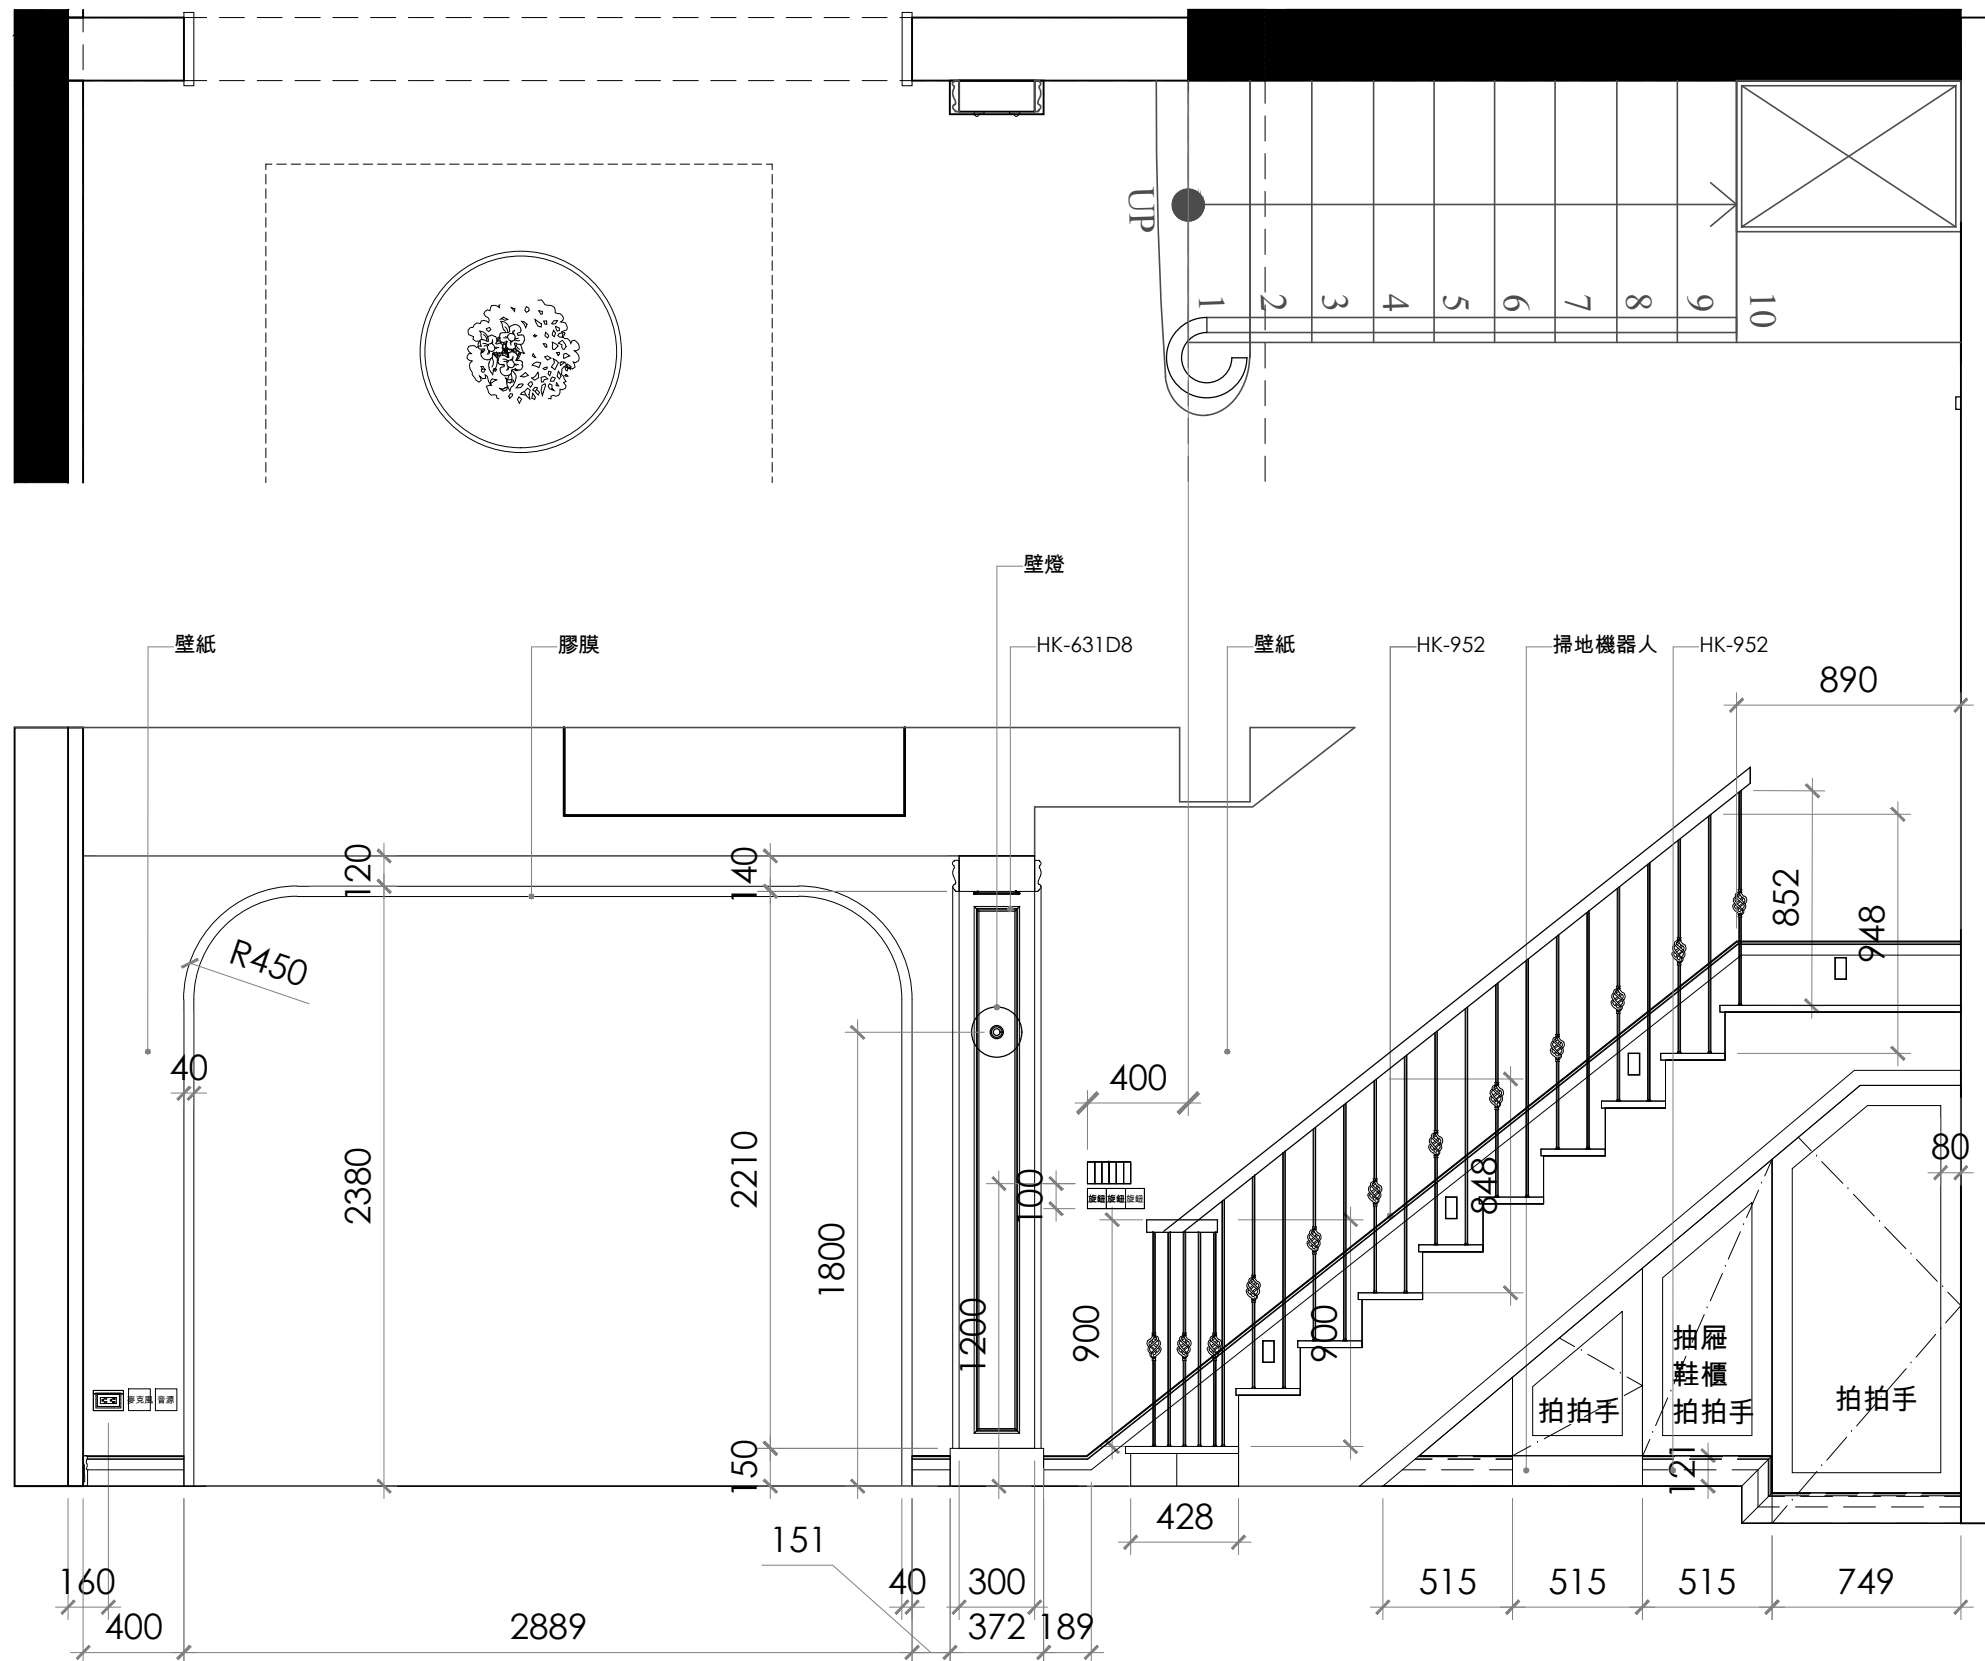

▲CH 3010mm

▲CH 2500mm

▼FL ±0 mm
▲FL -50 mm

1
E-11

ELEVATION

Scale=1:30

Revision

APPROVAL/核准

設計者:	建築師:
業主:	

備註:

- 圖面標註尺寸僅供參考，施作均以現場放樣檢討之。
- 圖面標註尺寸、材料及文字敘述因版本不同之差異，均以出圖章簽認日期之最近為準。
- 電腦圖檔除由合約訂定外，均不得以任何方式外流。
- 圖面所示均為本公司所擁有之智慧財產，切勿以任何方式複製修改。



MULA DECO

▲ 3F, N.26, Ln.290, Guangfu S. Rd., Taipei.
T 886-2-2546-3258
F 886-2-2546-3257
E Guido@mulatedeco.com

Project / 案名

天母葉公館

Sheet Title / 圖名



1F

立面圖

Date / 日期	Scale / 比例
8/10/2026	1/30CM
Designer / 設計	Approval / 核准
MONICA LIN	
Job No / 業務編號	Drawn By / 繪圖
00000	GUIDO
Dwg No.	Page No.


E-11

40

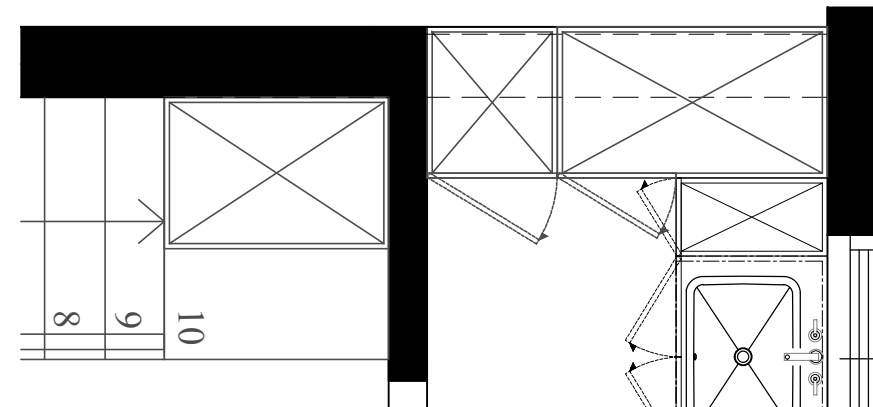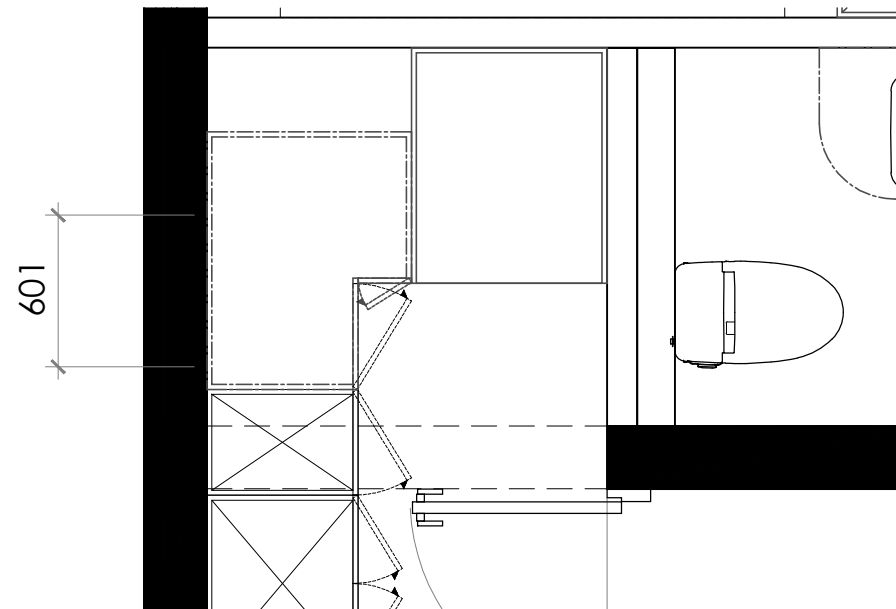


- ▲CH 3010mm
- ▲CH 2820mm
- ▲CH 2540mm
- ▲CH 2360mm

- ▼FL ±0 mm
- ▲FL -50 mm

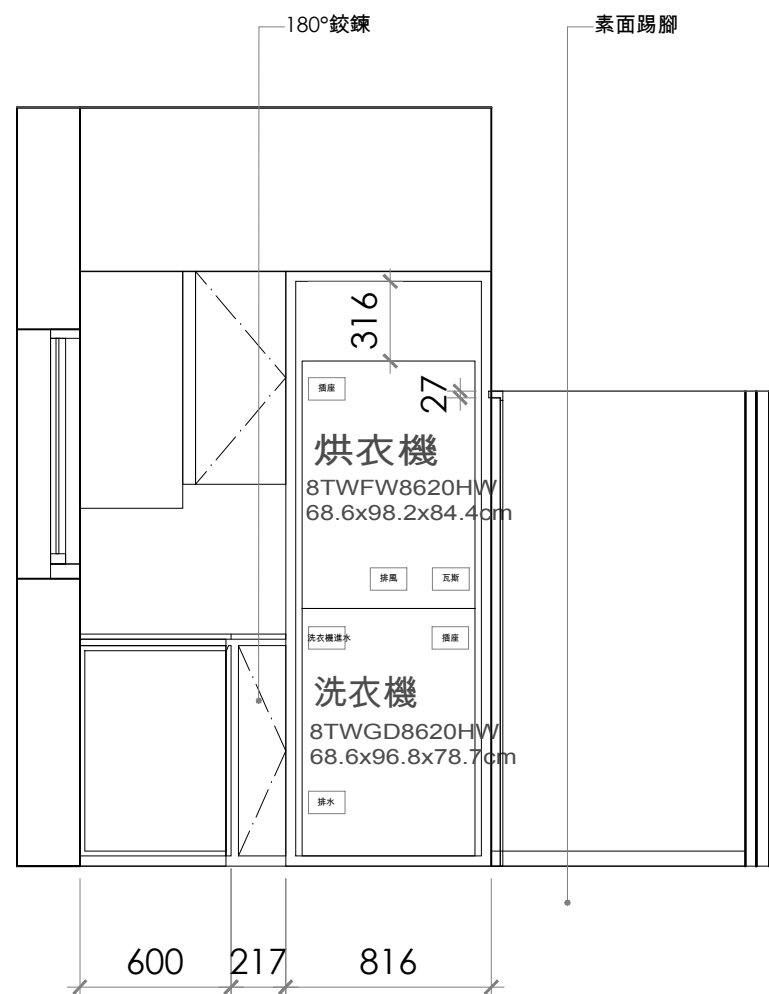

1 ELEVATION Scale=1:30

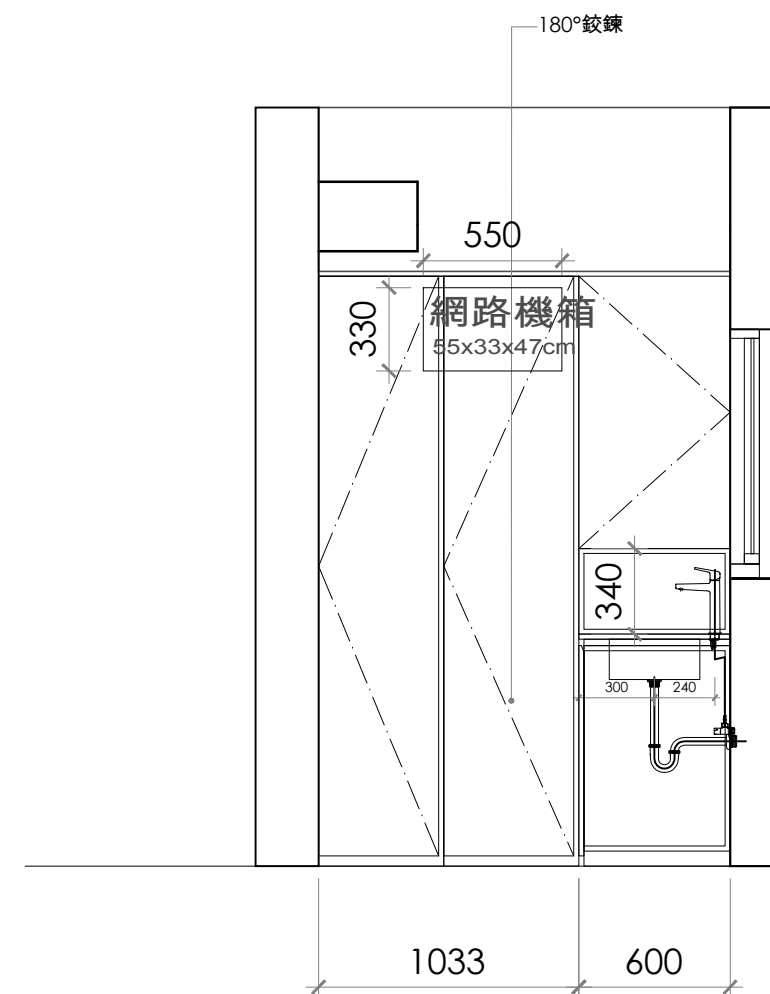

2 ELEVATION Scale=1:30

Revision

APPROVAL/核准

設計者:	建築師:
業主:	

備註:

a. 圖面標註尺寸僅供參考，施作均以現場放樣檢討之。

b. 圖面標註尺寸、材料及文字敘述因版本不同之差異，均以出圖章簽認日期之最近為準。

c. 電腦圖檔除由合約訂定外，均不得以何方式外流。

d. 圖面所示均為本公司所擁有之智慧財產，切勿以任何方式複製修改。

M

MULA DECO

▲ 3F, N.26, Ln.290, Guangfu S. Rd., Taipei.

☎ 886-2-2546-3258

☎ 886-2-2546-3257

✉ Guido@muladeco.com

Project / 案名


天母葉公館

Sheet Title / 圖名

1F

立面圖

Date / 日期	Scale / 比例
8/10/2026	1/30CM
Designer / 設計	Approval / 核准
MONICA LIN	
Job No / 業務編號	Drawn By / 繪圖
00000	GUIDO
Dwg No.	Page No.
E-15	45

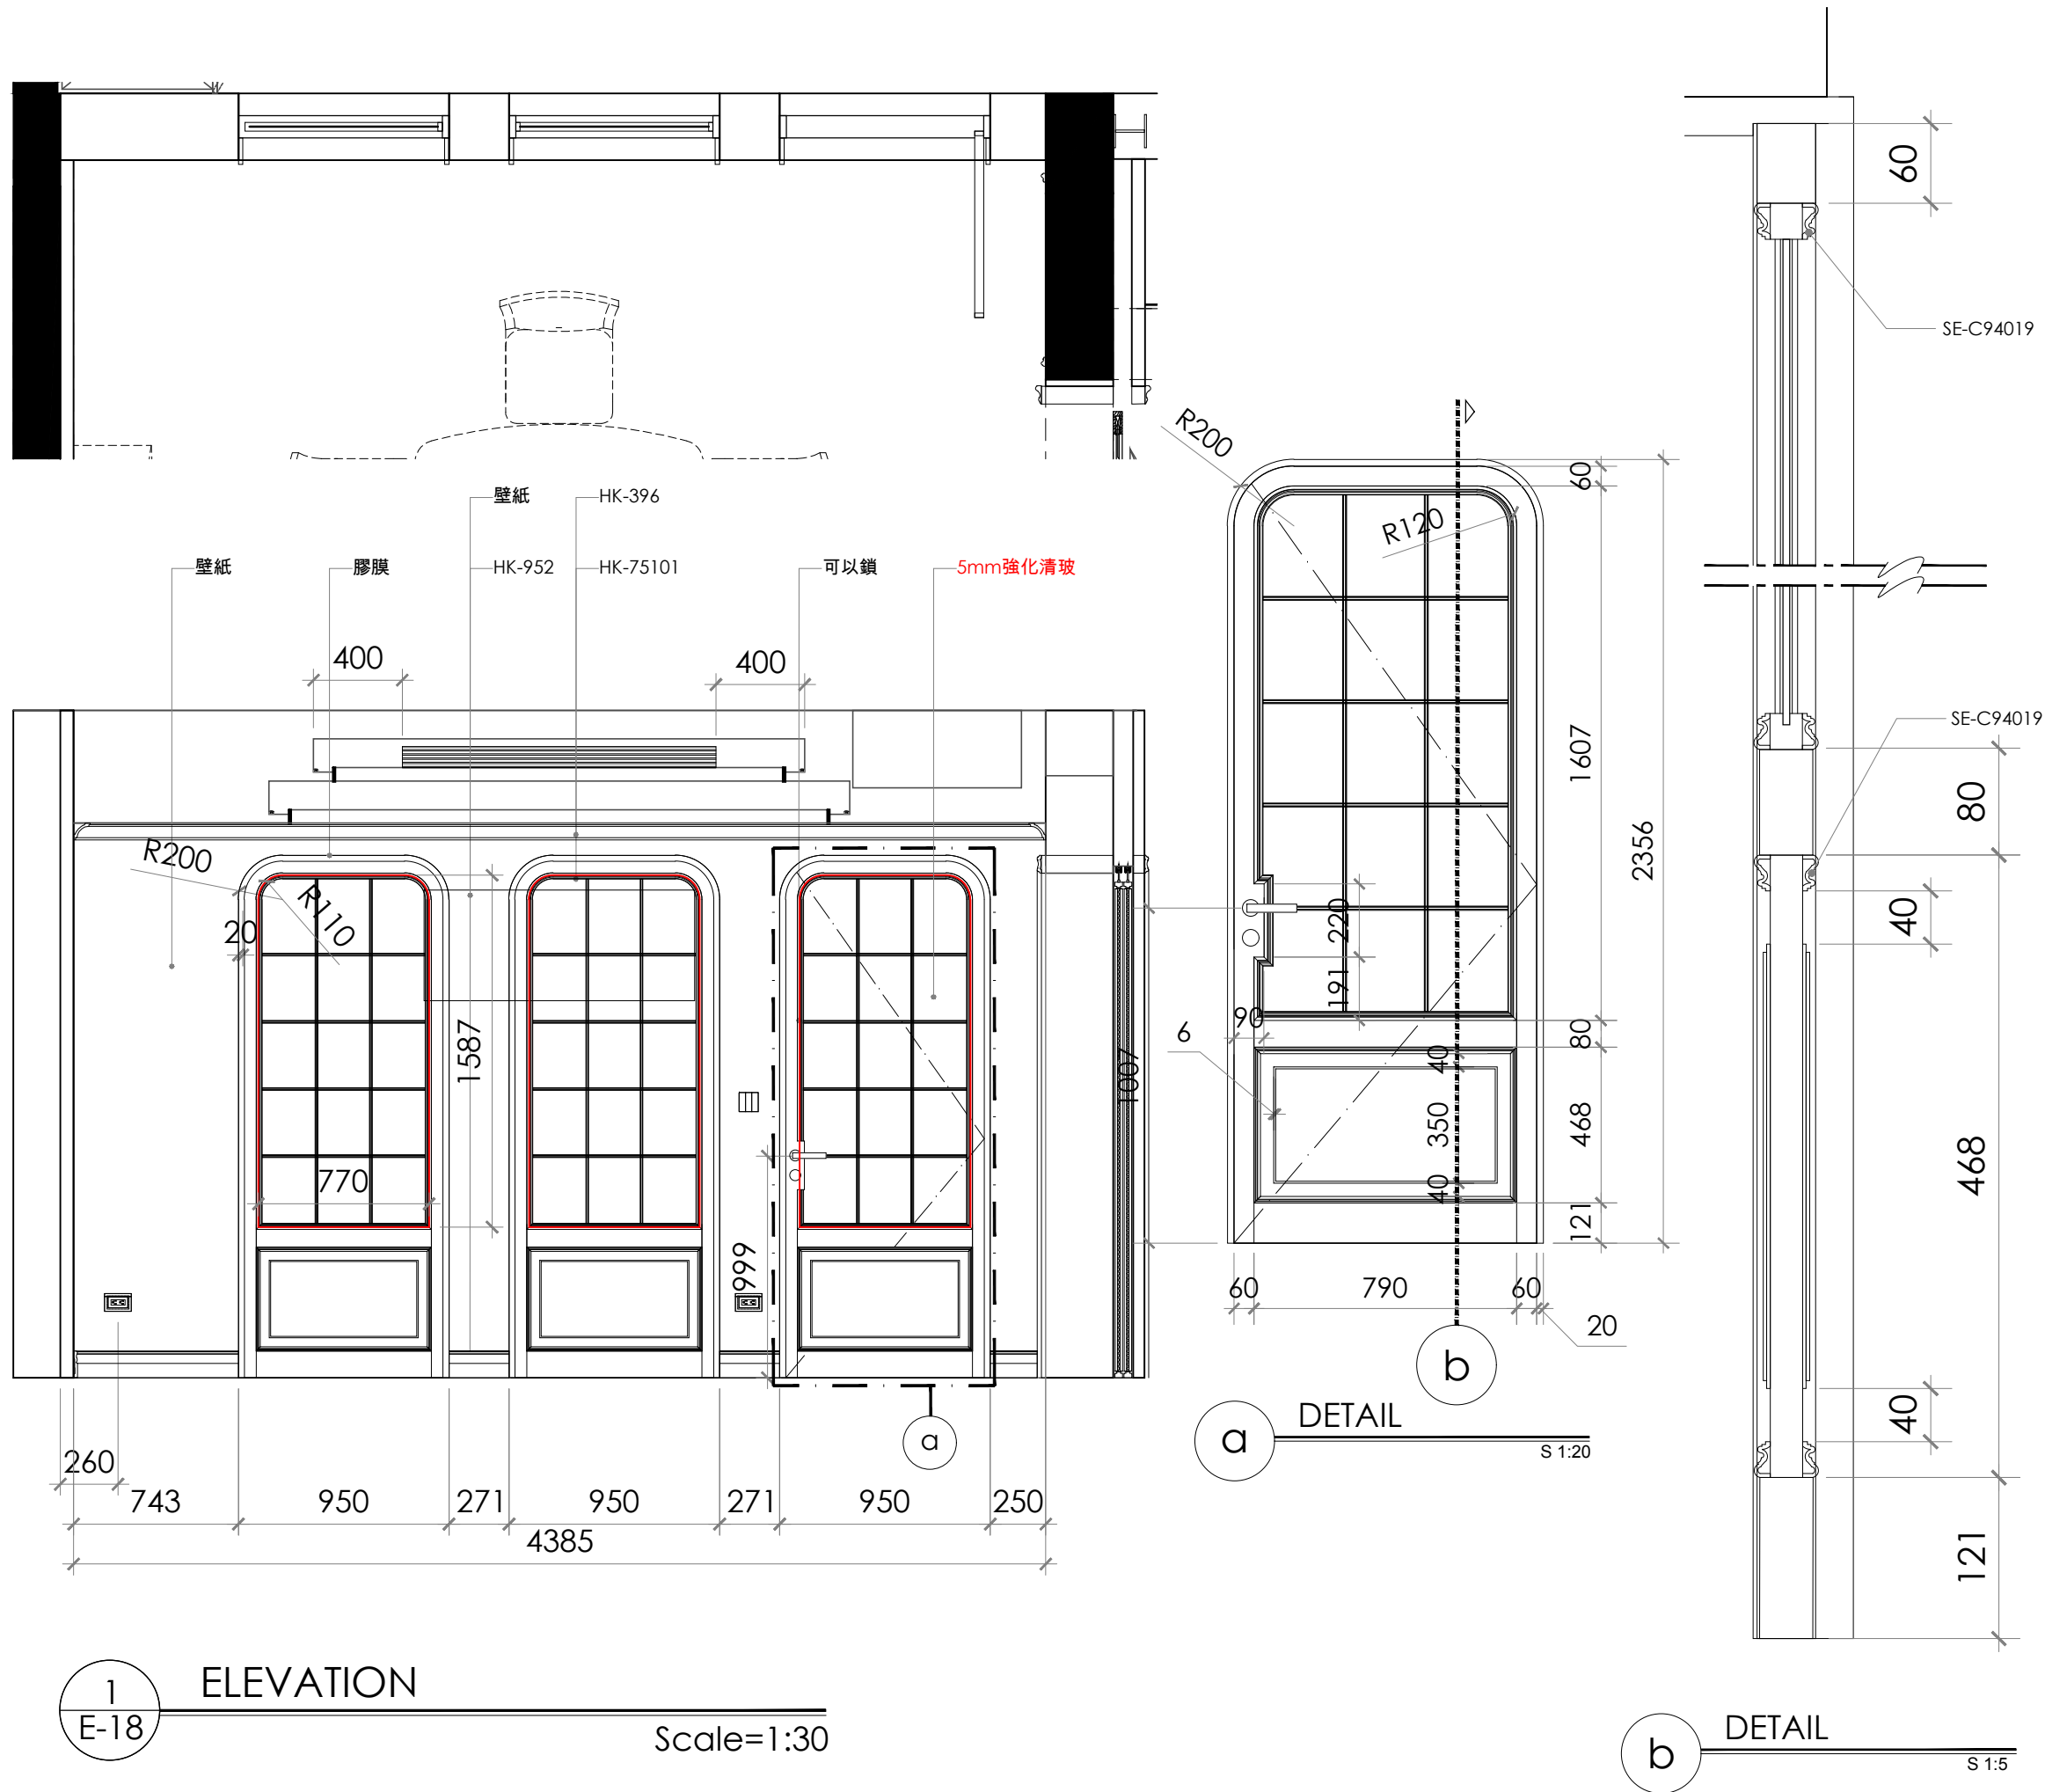

Revision

APPROVAL / 核准

設計者:	建築師:
業主:	

備註:

a. 圖面標註尺寸僅供參考，施作均以現場放樣檢討之。

b. 圖面標註尺寸、材料及文字敘述因版本不同之差異，均以出圖章簽認日期之最近為準。

c. 電腦圖檔除由合約訂定外，均不得以何方式外流。

d. 圖面所示均為本公司所擁有之智慧財產，切勿以任何方式複製修改。

M

MULA DECO

▲ 3F, N.26, Ln.290, Guangfu S. Rd., Taipei.

☎ 886-2-2546-3258

☎ 886-2-2546-3257

✉ Guido@muladeco.com

Project / 案名


天母葉公館

Sheet Title / 圖名

1F

立面圖


Date / 日期	Scale / 比例
8/10/2026	1/30CM
Designer / 設計	Approval / 核准
MONICA LIN	
Job No / 業務編號	Drawn By / 繪圖
00000	GUIDO
Dwg No.	Page No.
E-18	48

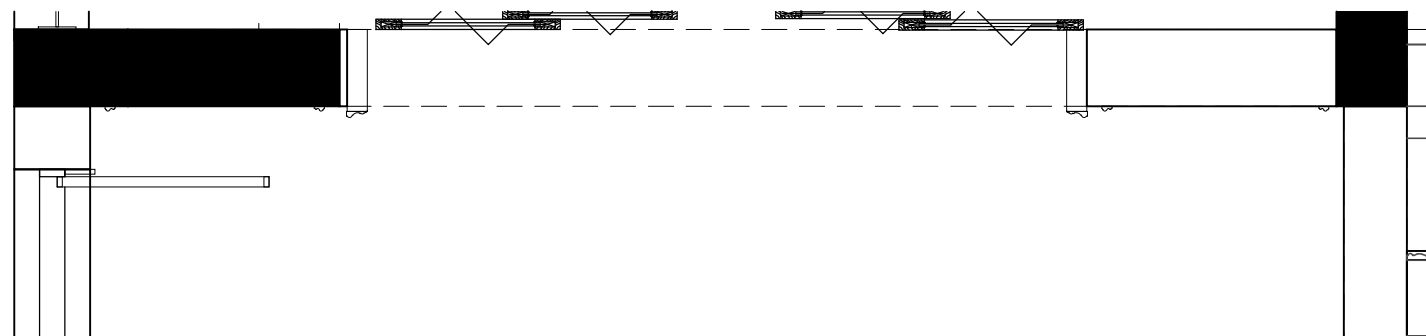

▲CH 3010mm

▲CH 2500mm

▼FL ±0 mm
▲FL -50 mm

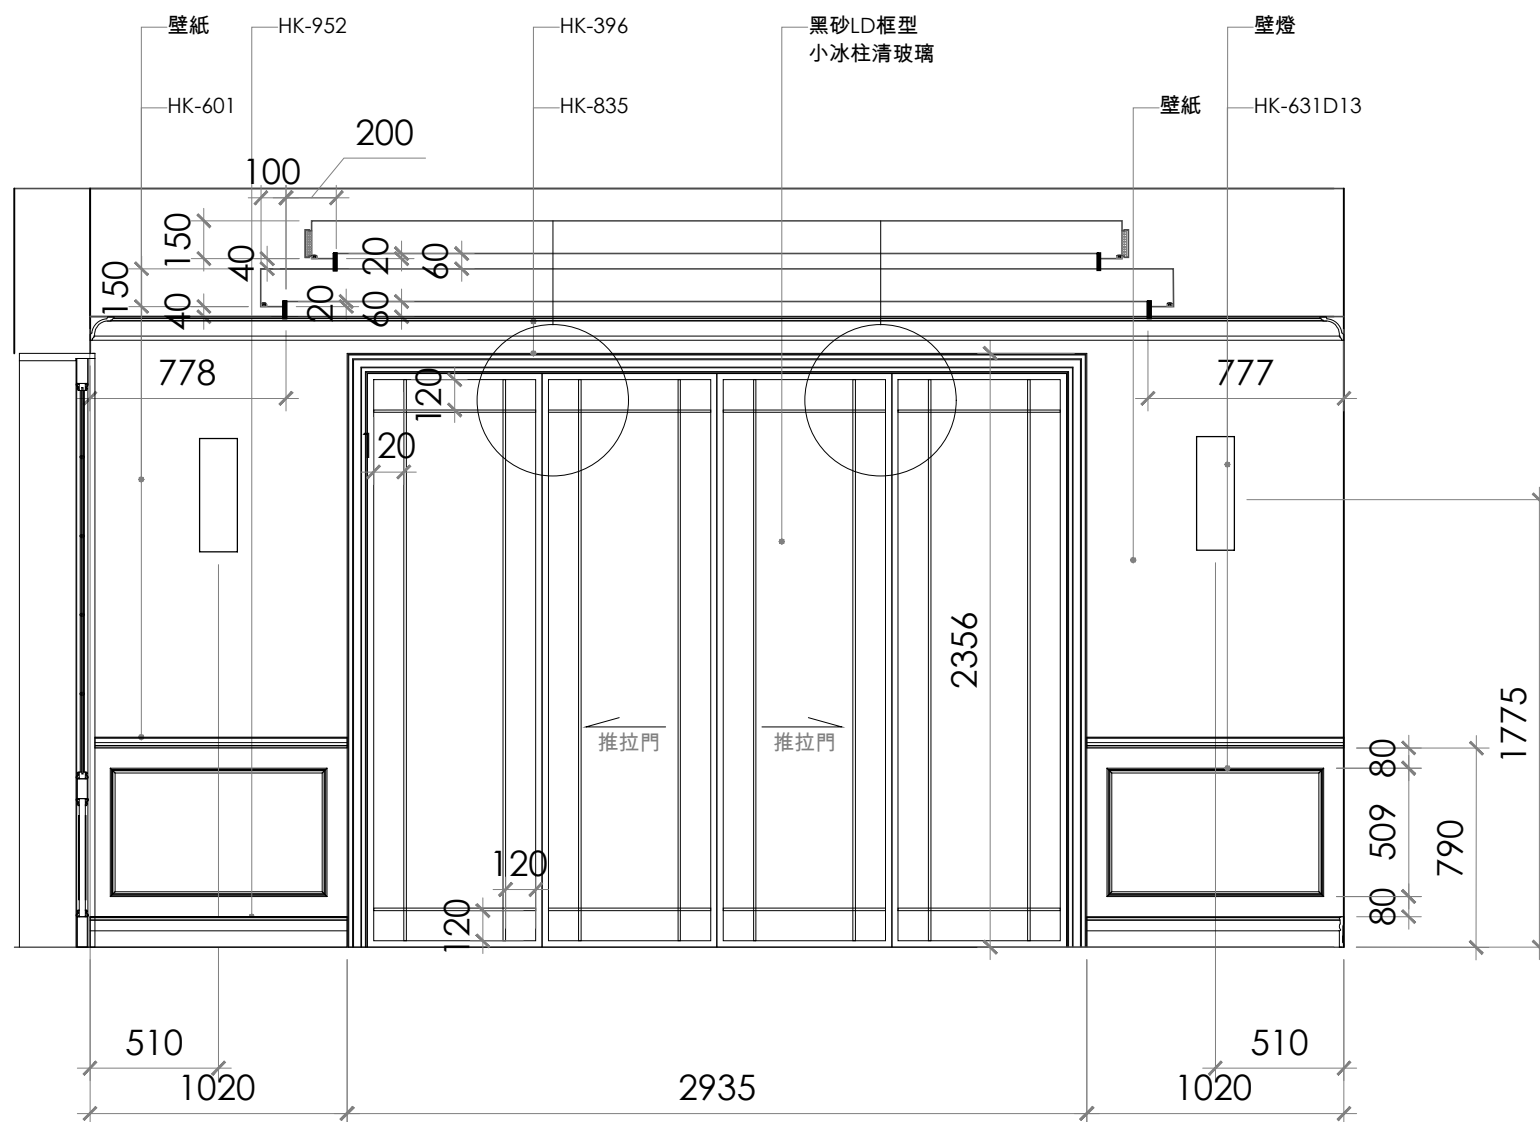

1
E-19

ELEVATION

Scale=1:30

Revision

APPROVAL/核准

設計者:	建築師:
業主:	

備註:

- 圖面標註尺寸僅供參考，施作均以現場放樣檢討之。
- 圖面標註尺寸、材料及文字敘述因版本不同之差異，均以出圖章簽認日期之最近為準。
- 電腦圖檔除由合約訂定外，均不得以任何方式外流。
- 圖面所示均為本公司所擁有之智慧財產，切勿以任何方式複製修改。



MULA DECO

▲ 3F, N.26, Ln.290, Guangfu S. Rd., Taipei.
☎ 886-2-2546-3258
☎ 886-2-2546-3257
✉ Guido@muladeco.com

Project / 案名

天母葉公館

Sheet Title / 圖名


1F

立面圖

Date / 日期	Scale / 比例
8/10/2026	1/30CM
Designer / 設計	Approval / 核准
MONICA LIN	
Job No / 業務編號	Drawn By / 繪圖
00000	GUIDO
Dwg No.	Page No.

E-19

49

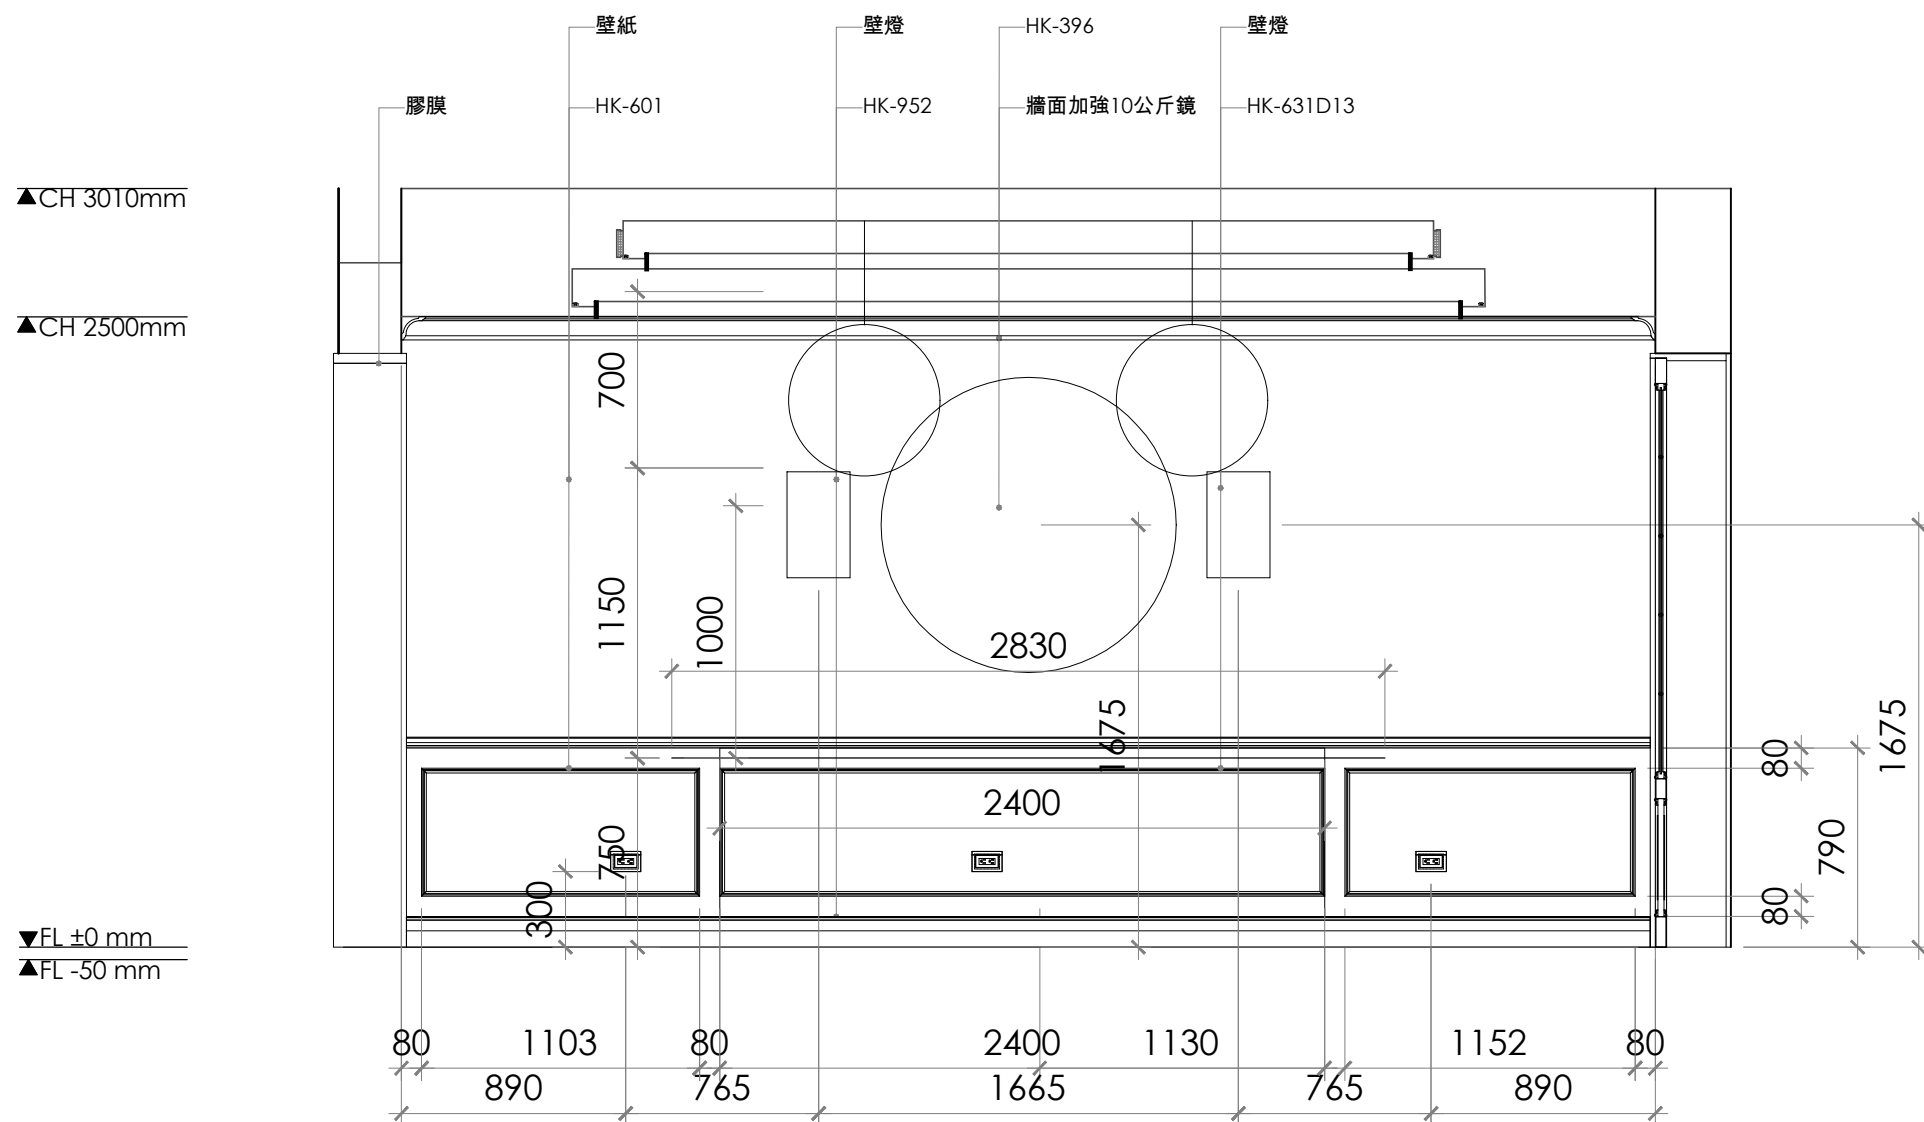

1
E-20

ELEVATION

Scale=1:30

[illegible]

APPROVAL/核准

設計者:	建築師:
業主:	

葡註:

- g. 圖面標註尺寸僅供參考，施作均以現場放樣檢討之。
- h. 圖面標註尺寸、材料及文字敘述因版本不同之差異，均以出圖章簽認日期之最近為準。
- i. 電腦圖檔除由合約訂定外，均不得以任何方式外流。
- j. 圖面所示均為本公司所擁有之智慧財產，切勿以任何方式複製修改。



MULA DECO

A 3F, N.26, Ln.290, Guangfu S. Rd., Taipei.
T 886-2-2546-3258
F 886-2-2546-3257
E Guido@muladeco.com



Project / 案名

天母葉公館

Sheet Title / 圖名
1F

立面圖


Date / 日期	Scale / 比例
8/10/2026	1/30CM
Designer / 設計	Approval / 核准
MONICA LIN	
Job No / 業務編號	Drawn By / 繪圖
00000	GUIDO
Dwg No.	Page No.
E-20	50

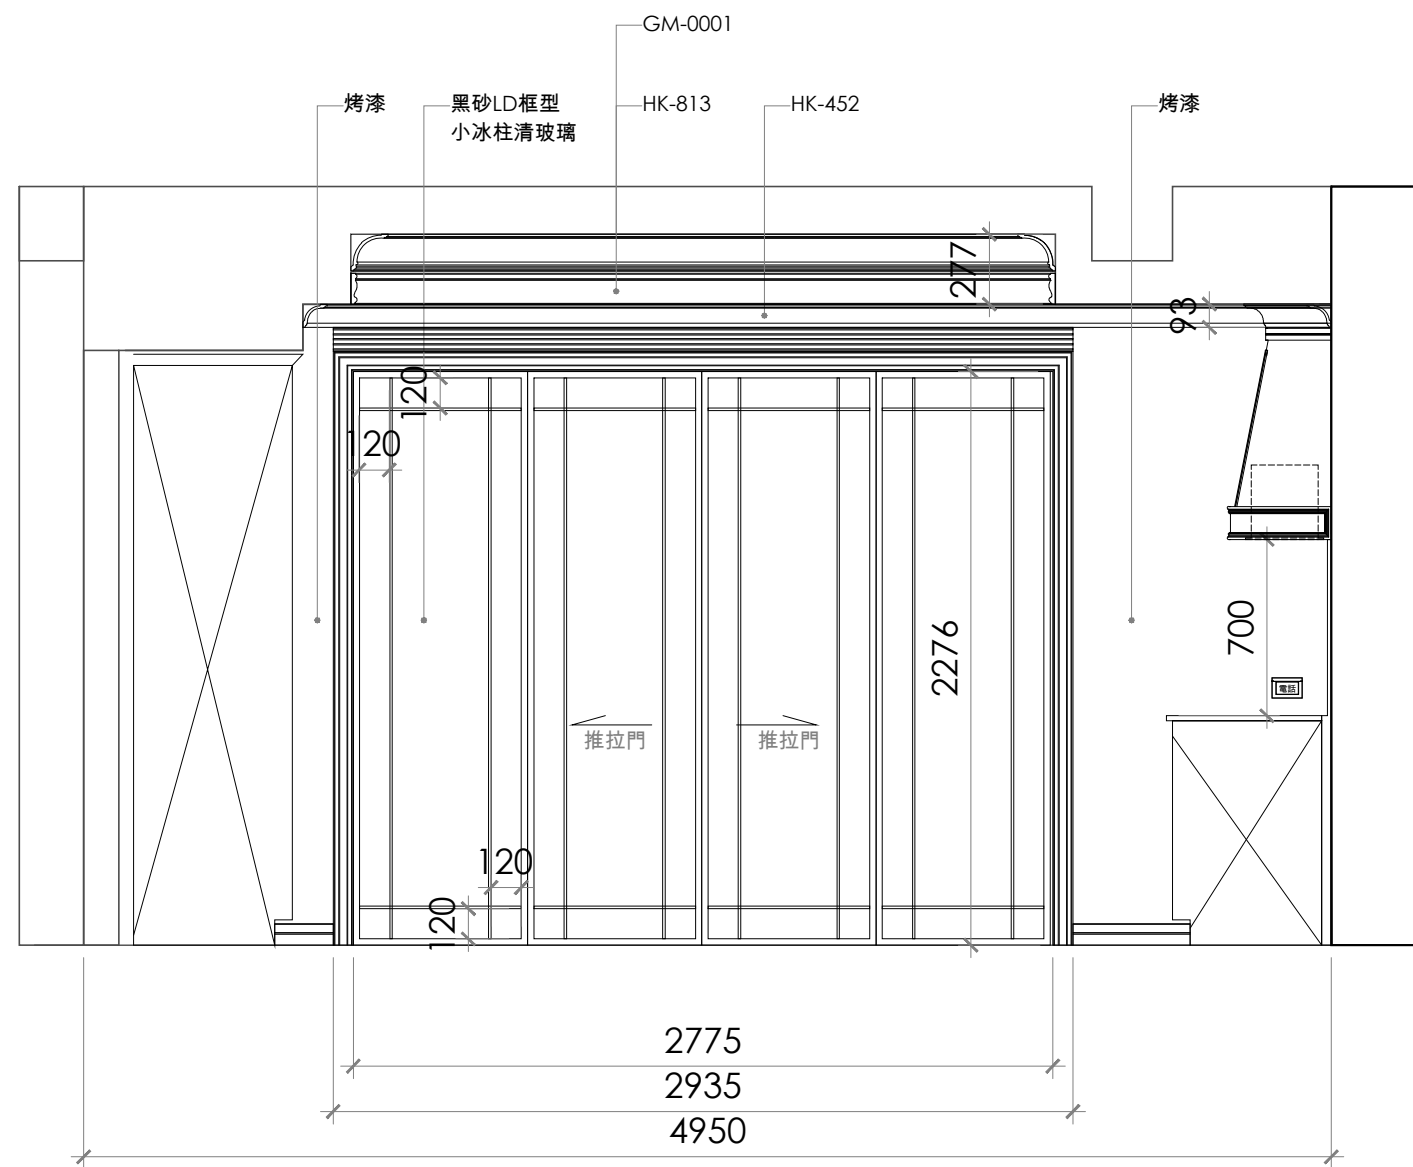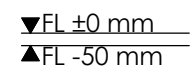

1
E-21


ELEVATION

Scale=1:30

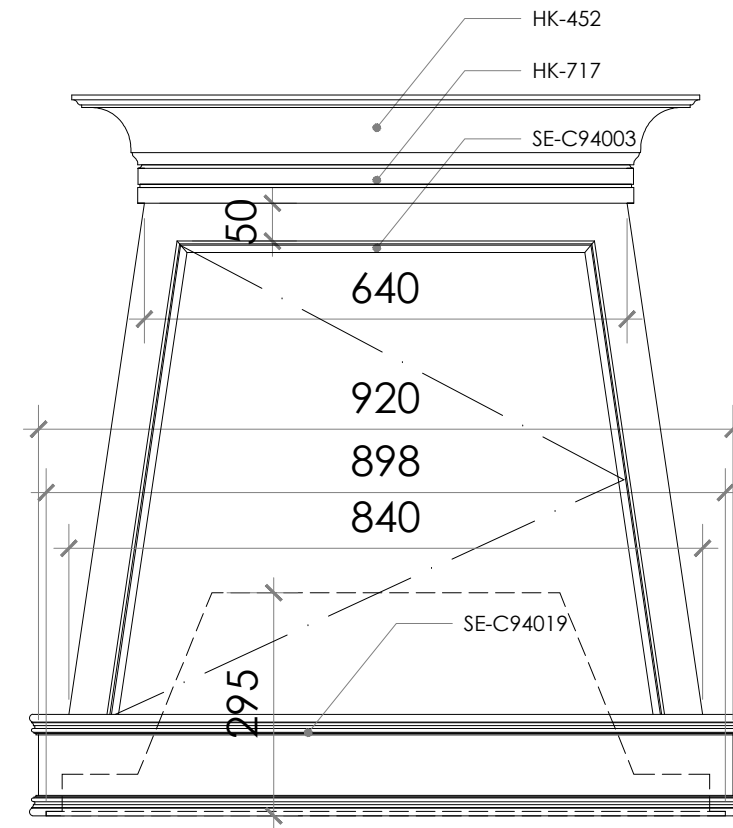

DETAIL

S 1:10

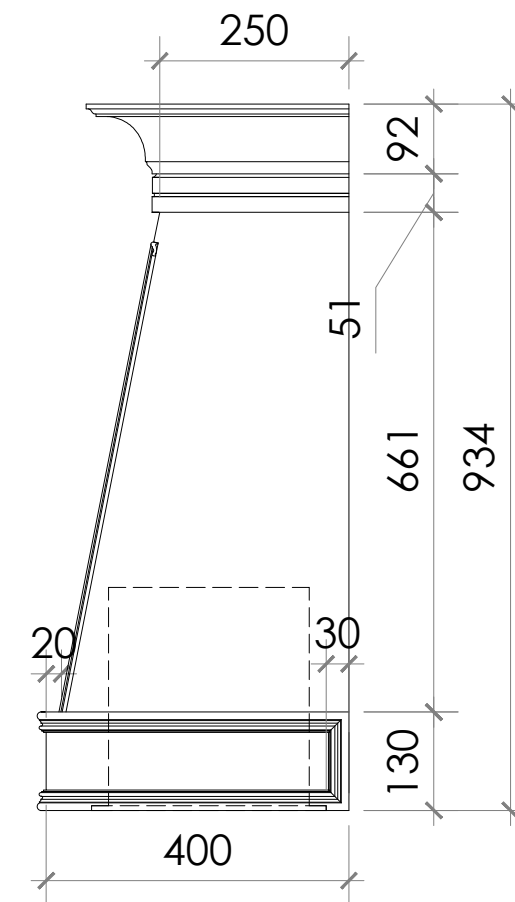

DETAIL

S 1:10

[illegible]

附註:

- ①.圖面標註尺寸僅供參考，施作均以現場放樣檢討之。
- ②.圖面標註尺寸、材料及文字敘述因版本不同之差異，均以出圖章簽認日期之最近為準。
- ③.電腦圖檔除由合約訂定外，均不得以任何方式外流。
- ④.圖面所有均為本公司所擁有之智慧財產，切勿以任何方式複製修改。



MULA DECO

A 3F, N.26, Ln.290, Guangfu S. Rd., Taipei.
T 886-2-2546-3258
F 886-2-2546-3257
E Guido@muladeco.com


Project / 案名

天母葉公館

Sheet Title / 圖名
1F


立面圖

Date / 日期	Scale / 比例
8/10/2026	1/30MM
Designer / 設計	Approval / 核准
MONICA LIN	
Job No / 業務編號	Drawn By / 繪圖
00000	GUIDO
Dwg No.	Page No.
E-21	51

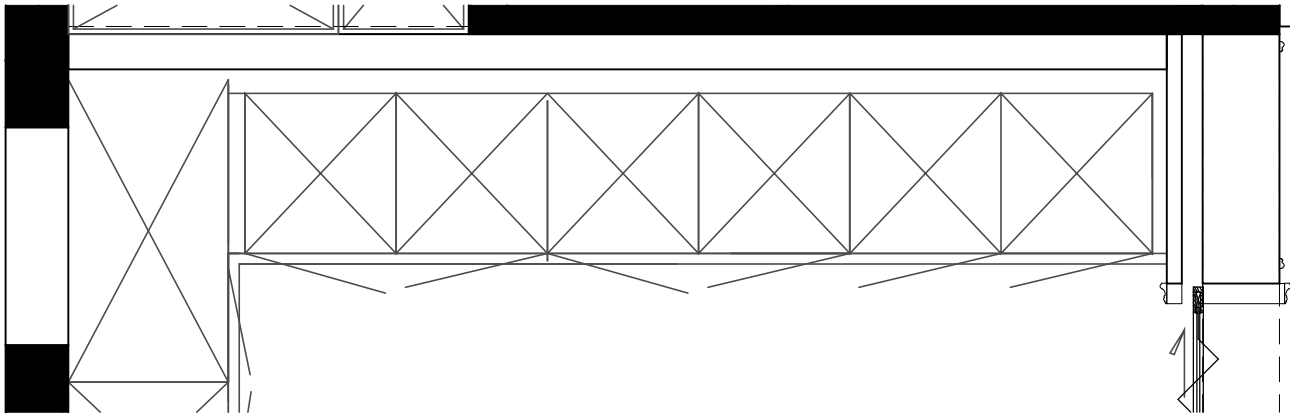

- ▲CH 3010mm
- ▲CH 2820mm
- ▲CH 2540mm
- ▲CH 2360mm

- ▼FL ±0 mm
- ▲FL -50 mm

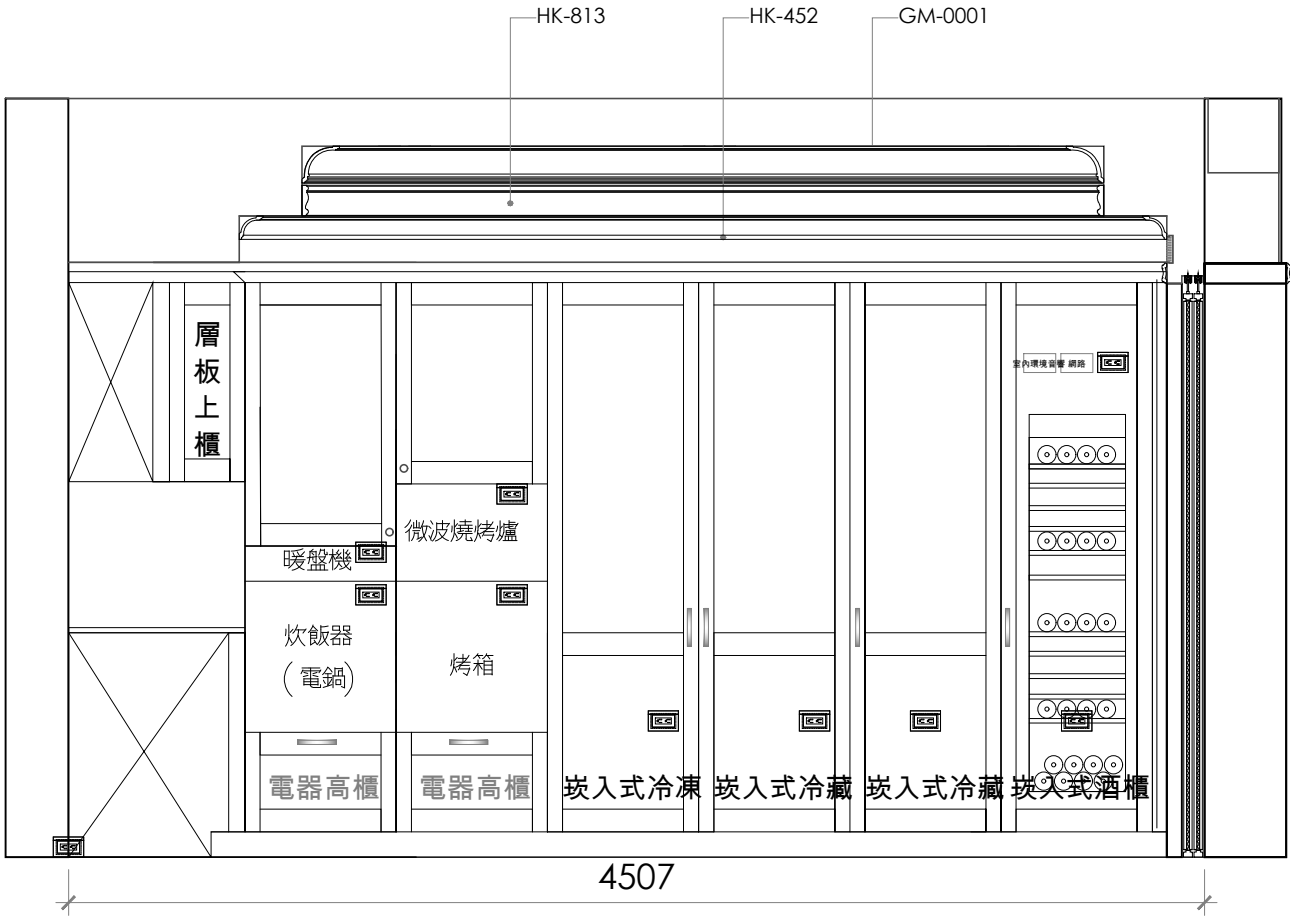

1
E-22

ELEVATION

Scale=1:30

Revision

設計者:	建築師:
業主:	

備註:

a. 圖面標註尺寸僅供參考，施作均以現場放樣檢討之。

b. 圖面標註尺寸、材料及文字敘述因版本不同之差異，均以出圖章簽認日期之最近為準。

c. 電腦圖檔除由合約訂定外，均不得以任何方式外流。

d. 圖面所示均為本公司所擁有之智慧財產，切勿以任何方式複製修改。

M

MULA DECO

▲ 3F, N.26, Ln.290, Guangfu S. Rd., Taipei.
☎ 886-2-2546-3258
☎ 886-2-2546-3257
✉ Guido@muladeco.com


Project / 案名

天母葉公館

Sheet Title / 圖名

1F
立面圖

Date / 日期	Scale / 比例
8/10/2026	1/30MM
Designer / 設計	Approval / 核准
MONICA LIN	
Job No / 業務編號	Drawn By / 繪圖
00000	GUIDO
Dwg No.	Page No.
E-22	52

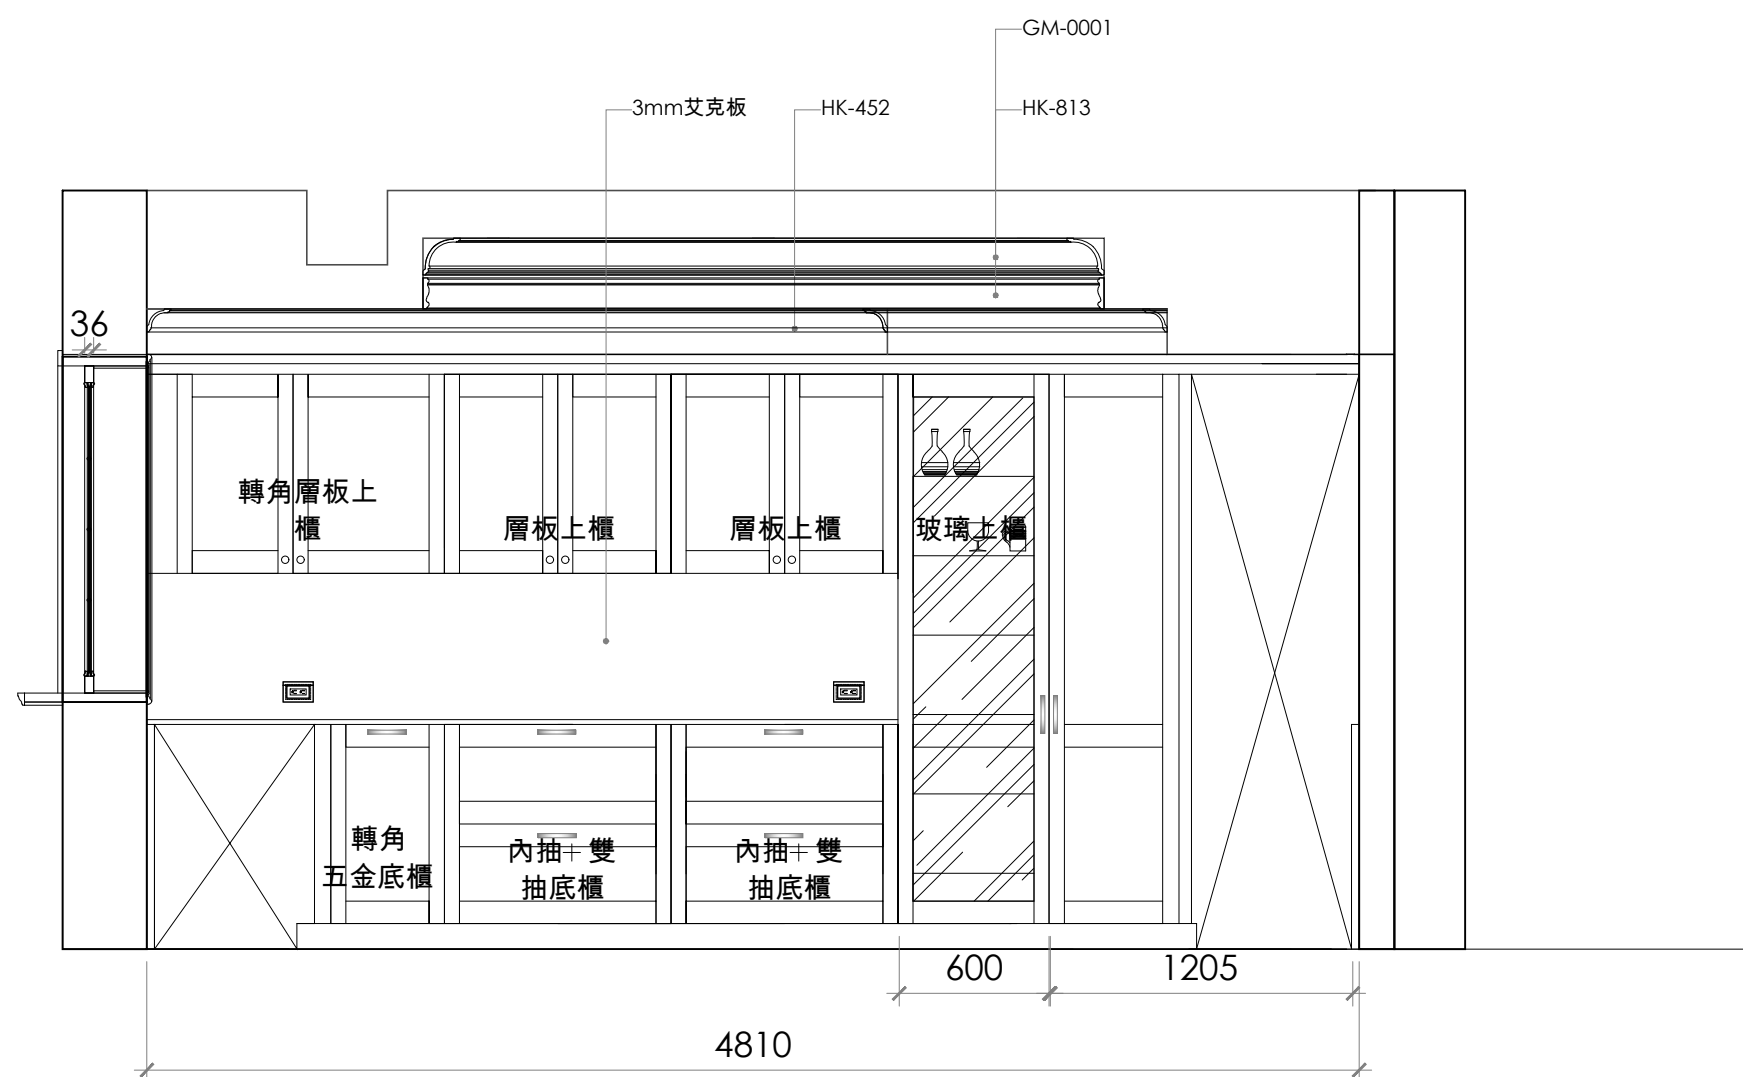

▲CH 3010mm
▲CH 2820mm
▲CH 2540mm
▲CH 2360mm

▼FL ±0 mm
▲FL -50 mm

1
E-23

ELEVATION

Scale=1:30

Revisor

APPROVAL/核准

設計者:

建築師:	
------	--

業主:

備註:

- a. 圖面標註尺寸僅供參考，施作均以現場放樣檢討之。
- b. 圖面標註尺寸、材料及文字敘述因版本不同之差異，均以出圖章簽認日期之最近為準。
- c. 電腦圖檔除由合約訂定外，均不得以任何方式外流。
- d. 圖面所示均為本公司所擁有之智慧財產，切勿以任何方式複製修改。



MULA DECO

A 3F, N.26, Ln.290, Guangfu S. Rd., Taipei.
T 886-2-2546-3258
F 886-2-2546-3257
E Guido@muladeco.com


Project / 案名

天母葉公館

Sheet Title / 圖名
1F



立面圖

Date / 日期	Scale / 比例
8/10/2026	1/30MM
Designer / 設計	Approval / 核准
MONICA LN	
Job No / 業務編號	Drawn By / 繪圖
00000	GUIDO
Dwg No.	Page No.
E-23	53

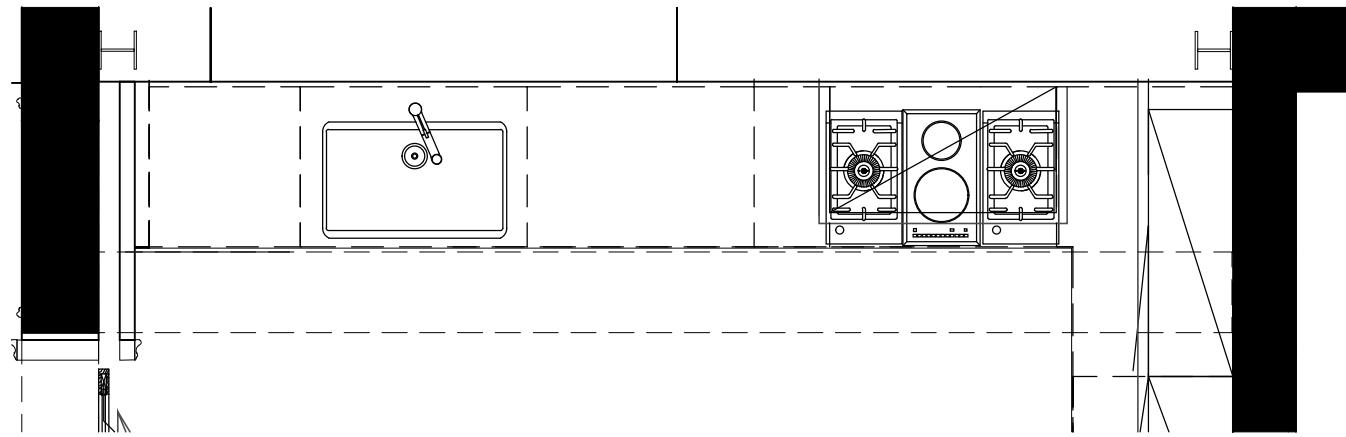

- ▲CH 3010mm
- ▲CH 2820mm
- ▲CH 2540mm
- ▲CH 2360mm

- ▼FL ±0 mm
- ▲FL -50 mm

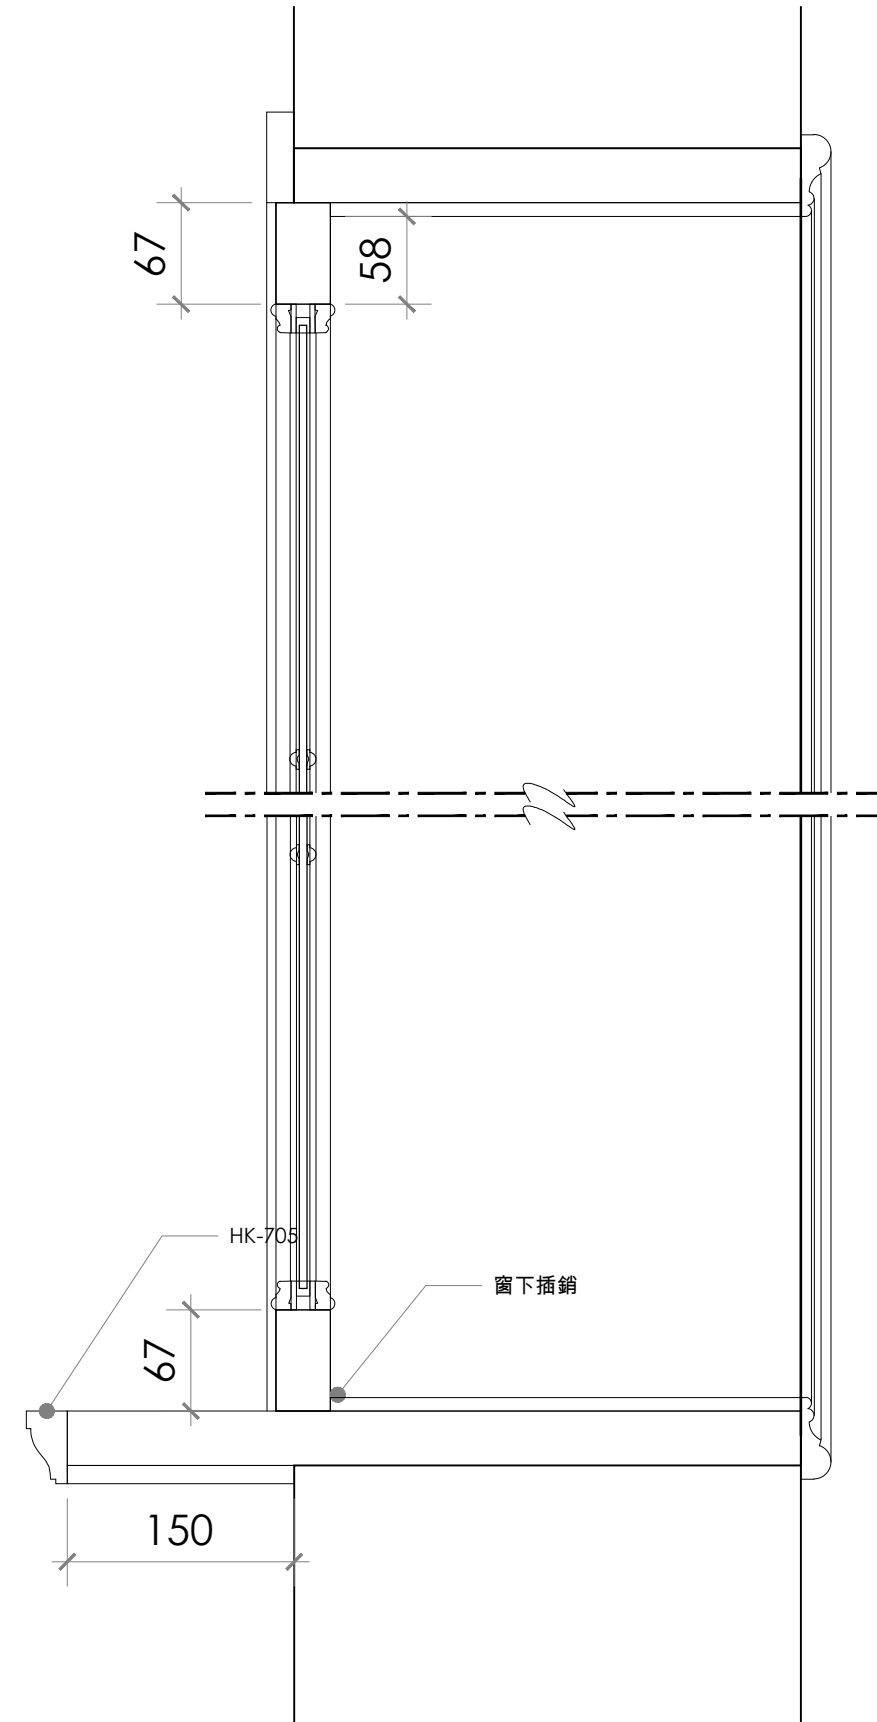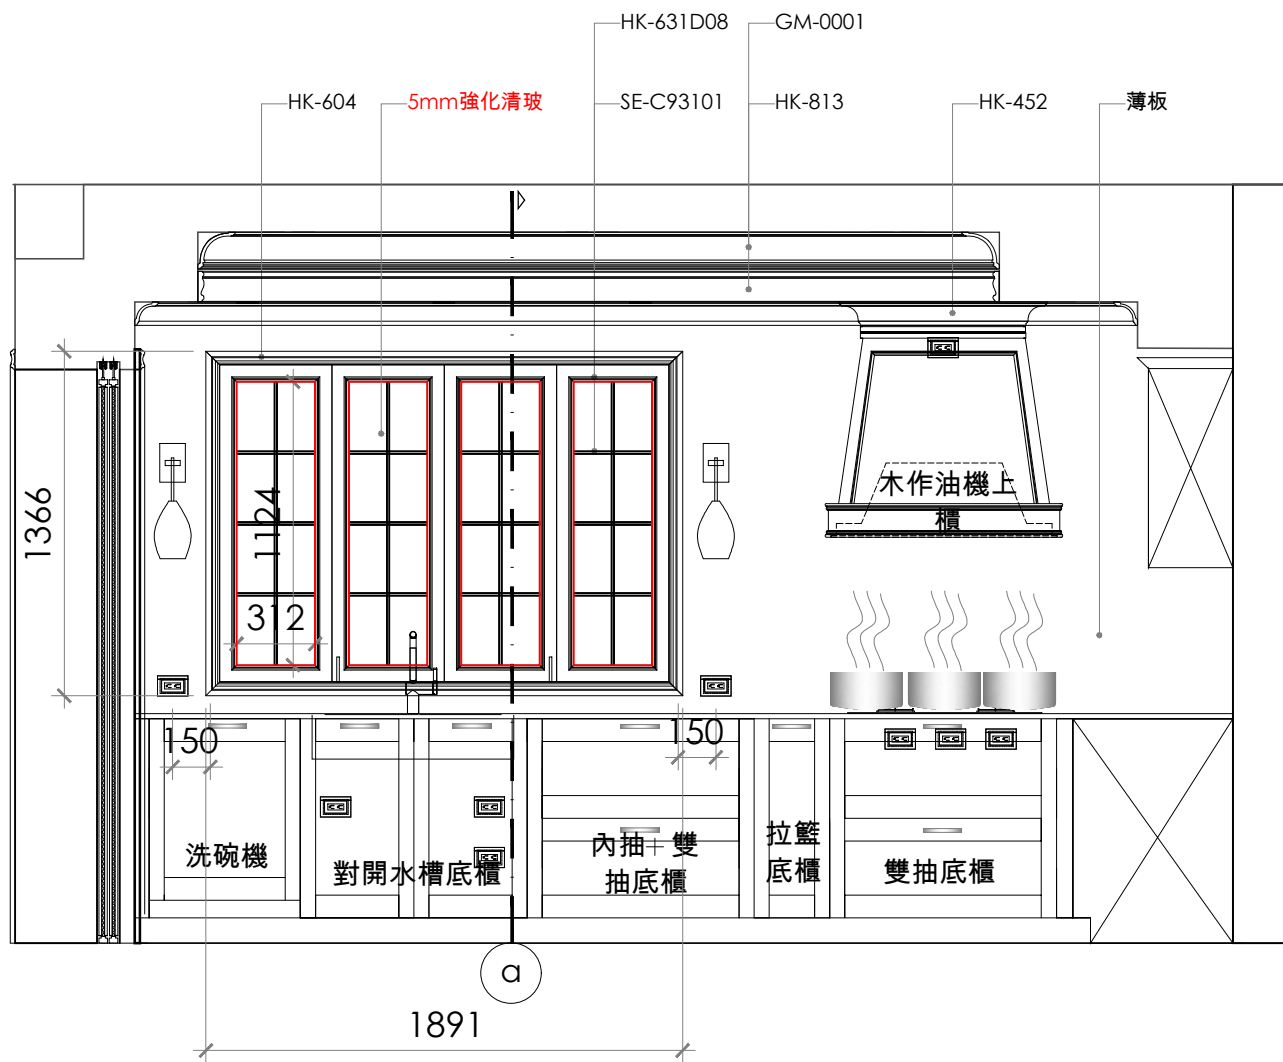

1 ELEVATION
E-24 Scale=1:30

a DETAIL
S 1:5

Revision

APPROVAL/核准

設計者:	建築師:
業主:	

備註:
a. 圖面標註尺寸僅供參考, 施作均以現場放樣檢討之。
b. 圖面標註尺寸、材料及文字敘述因版本不同之差異, 均以出圖章簽認日期之最近為準。
c. 電腦圖檔除由合約訂定外, 均不得以何方式外流。
d. 圖面所示均為本公司所擁有之智慧財產, 切勿以任何方式複製修改。

M
MULA DECO
A 3F, N.26, Ln.290, Guangfu S. Rd., Taipei.
T 886-2-2546-3258
F 886-2-2546-3257
E Guido@muladeco.com

Project / 案名


天母葉公館

Sheet Title / 圖名

1F

立面圖

Date / 日期	Scale / 比例
8/10/2026	1/30MM
Designer / 設計	Approval / 核准
MONICA LIN	
Job No / 業務編號	Drawn By / 繪圖
00000	GUIDO
Dwg No.	Page No.
E-24	54

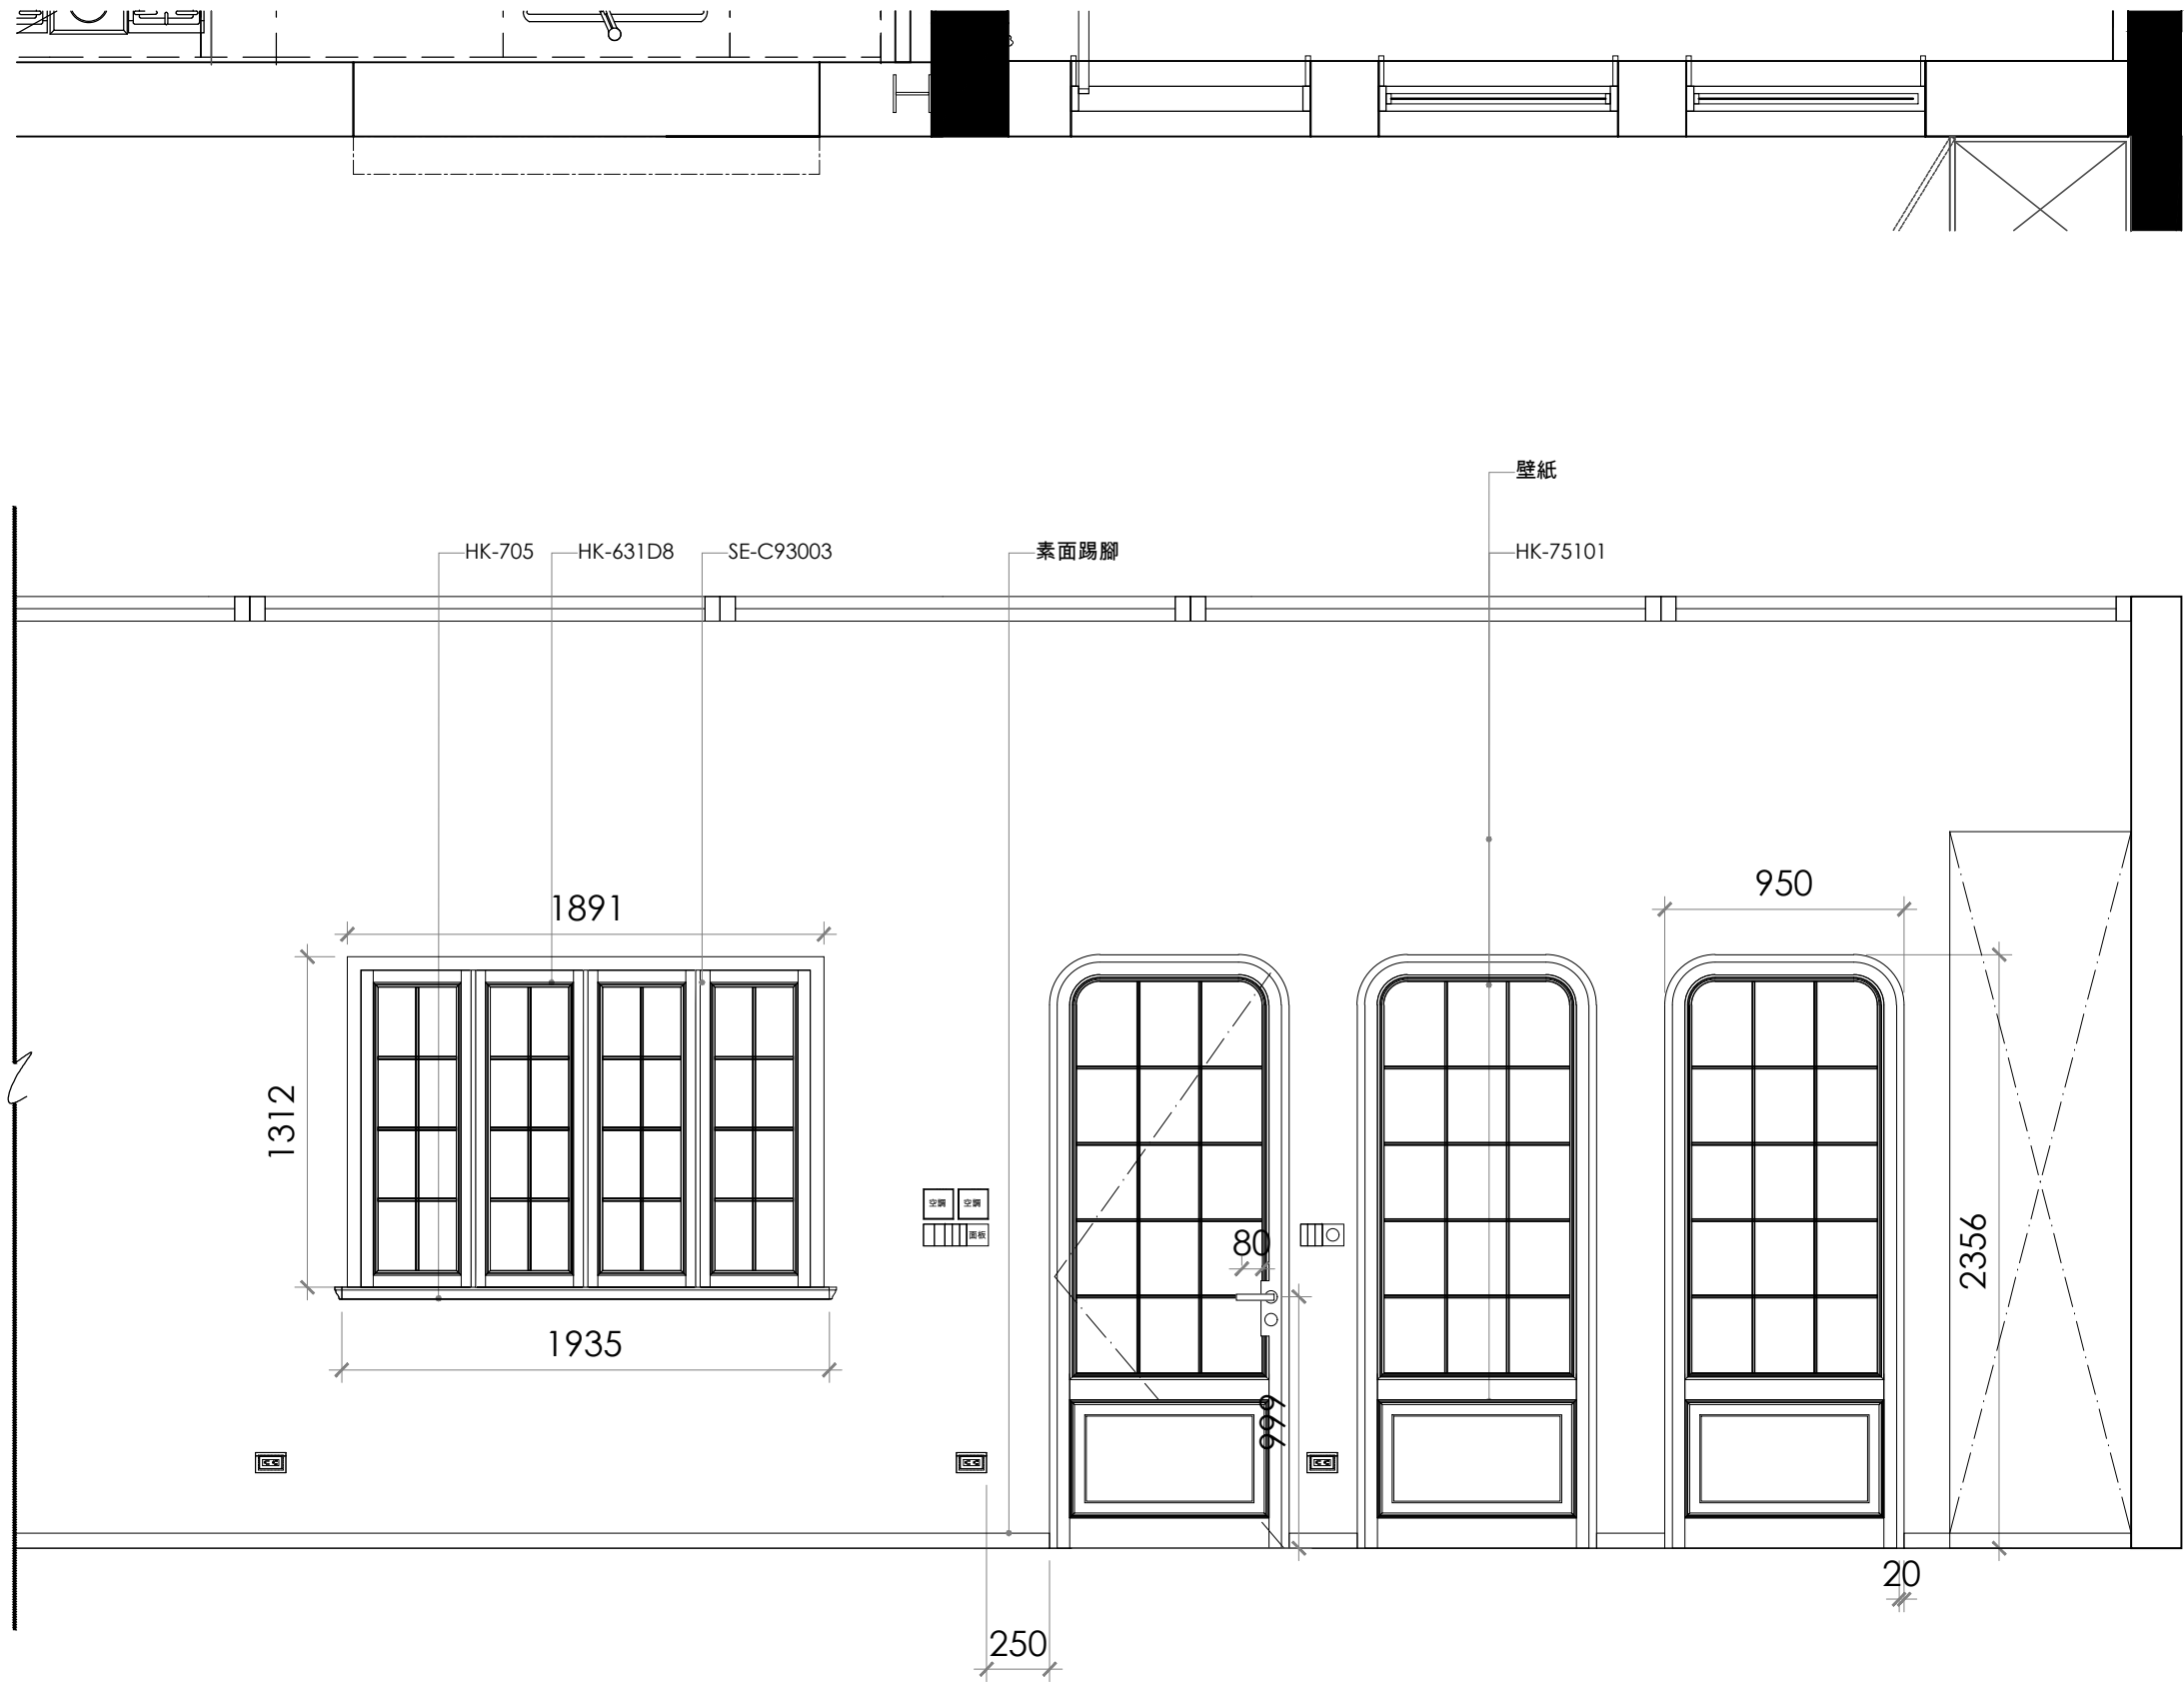

1
E-25

ELEVATION

Scale=1:30

Revision

APPROVAL/核准

設計者:	建築師:
業主:	

備註:

- 圖面標註尺寸僅供參考，施作均以現場放樣檢討之。
- 圖面標註尺寸、材料及文字敘述因版本不同之差異，均以圖章簽認日期之最近為準。
- 電腦圖檔除由合約訂定外，均不得以何方式外流。
- 圖面所示均為本公司所擁有之智慧財產，切勿以任何方式複製修改。



MULA DECO

▲ 3F, N.26, Ln.290, Guangfu S. Rd., Taipei.
☎ 886-2-2546-3258
☎ 886-2-2546-3257
✉ Guido@muladeco.com

Project / 案名

天母葉公館

Sheet Title / 圖名


1F

立面圖

Date / 日期	Scale / 比例
8/10/2026	1/30CM
Designer / 設計	Approval / 核准
MONICA LIN	
Job No / 業務編號	Drawn By / 繪圖
00000	GUIDO
Dwg No.	Page No.

E-25

55

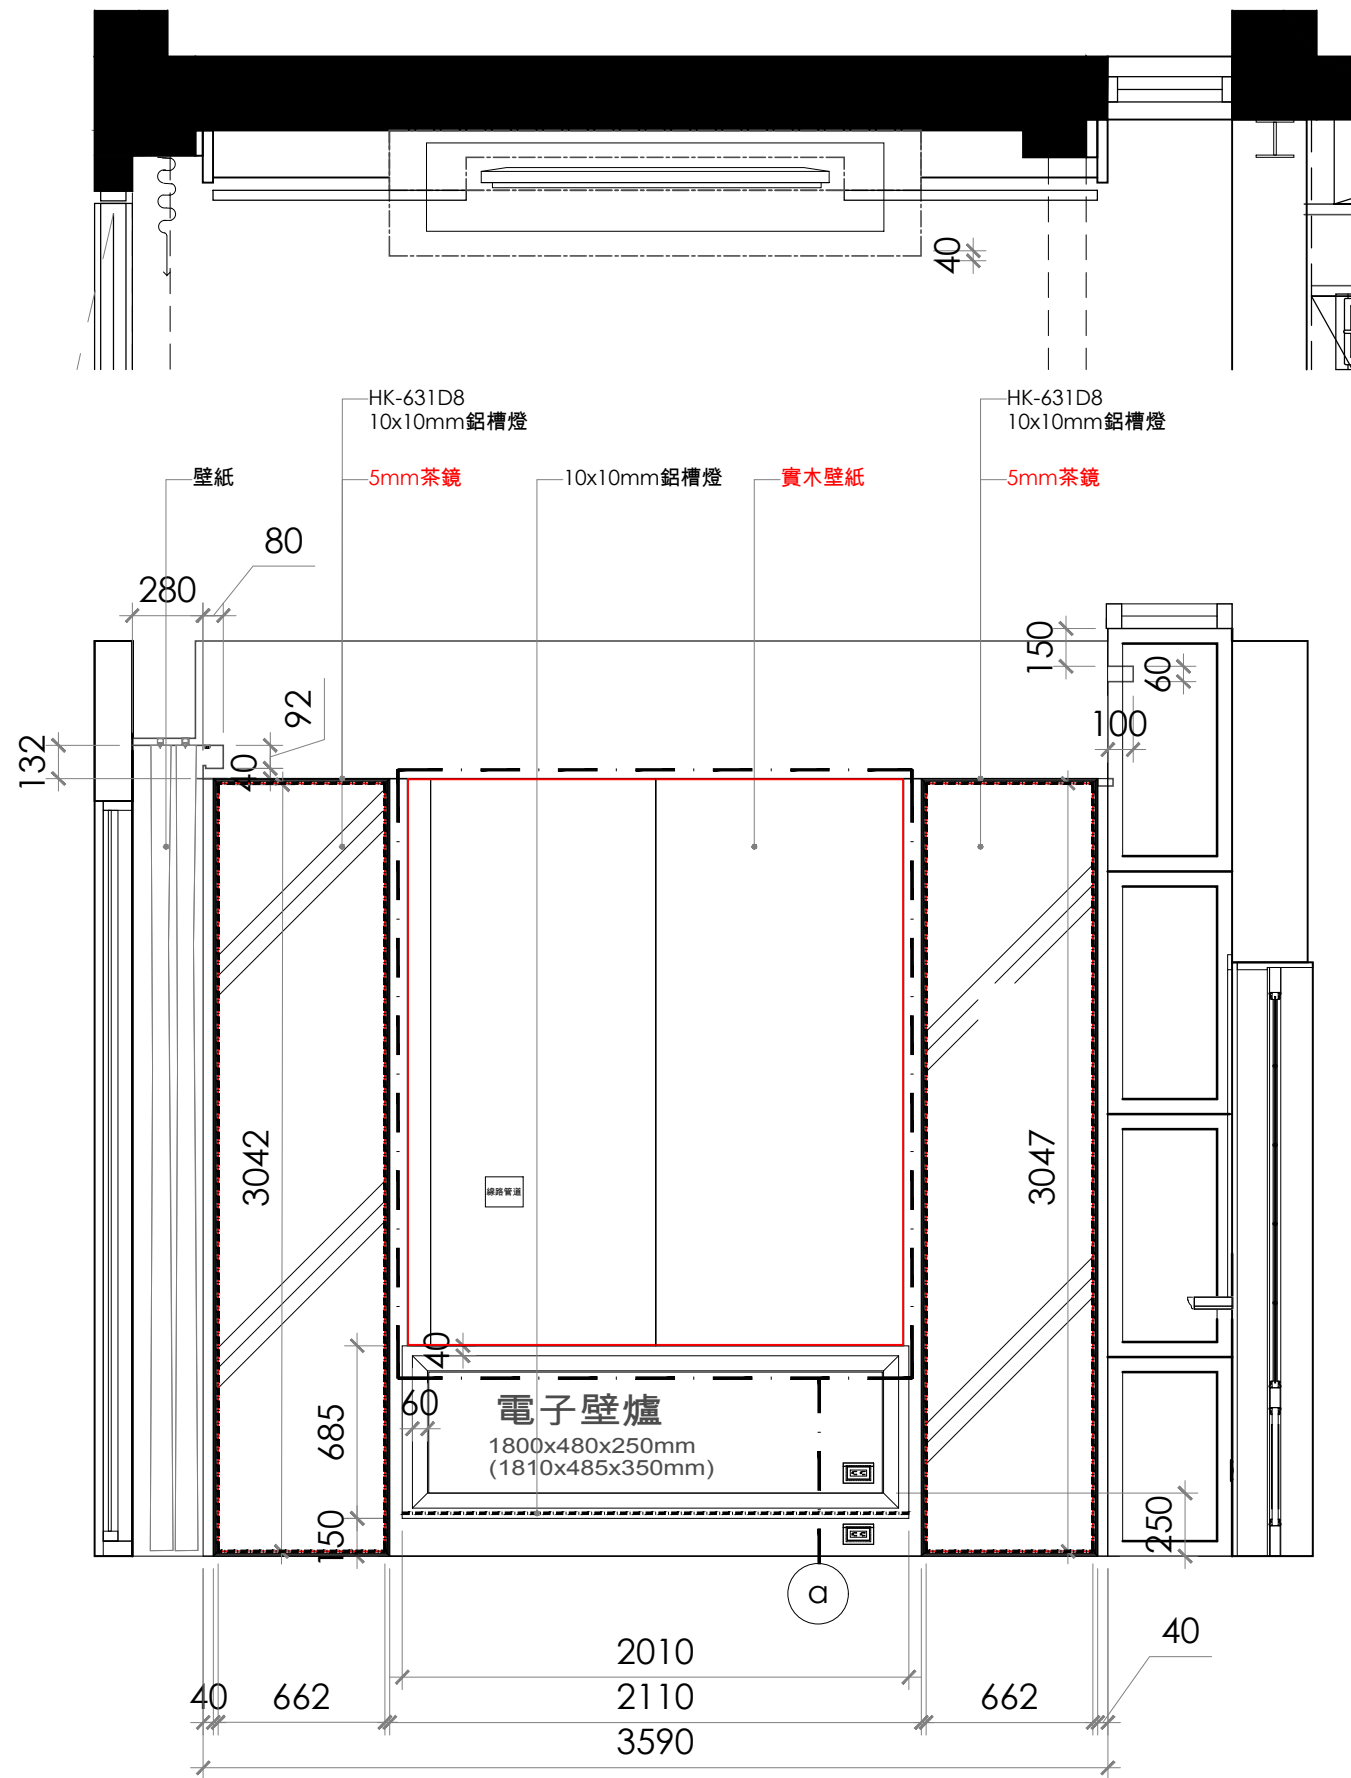

1
E-26

ELEVATION

Scale=1:30

Revision

APPROVAL/核准

設計者:	建築師:
業主:	

備註:

- 圖面標註尺寸僅供參考，施作均以現場放樣檢討之。
- 圖面標註尺寸、材料及文字敘述因版本不同之差異，均以出圖章簽認日期之最近為準。
- 電腦圖檔除由合約訂定外，均不得以任何方式外流。
- 圖面所示均為本公司所擁有之智慧財產，切勿以任何方式複製修改。



MULA DECO

▲ 3F, N.26, Ln.290, Guangfu S. Rd., Taipei.
☎ 886-2-2546-3258
☎ 886-2-2546-3257
✉ Guido@muladeco.com

Project / 案名

天母葉公館



Sheet Title / 圖名
1F

立面圖


Date / 日期	Scale / 比例
8/10/2026	1/30CM
Designer / 設計	Approval / 核准
MONICA LIN	
Job No / 業務編號	Drawn By / 繪圖
00000	GUIDO
Dwg No.	Page No.

E-26

56

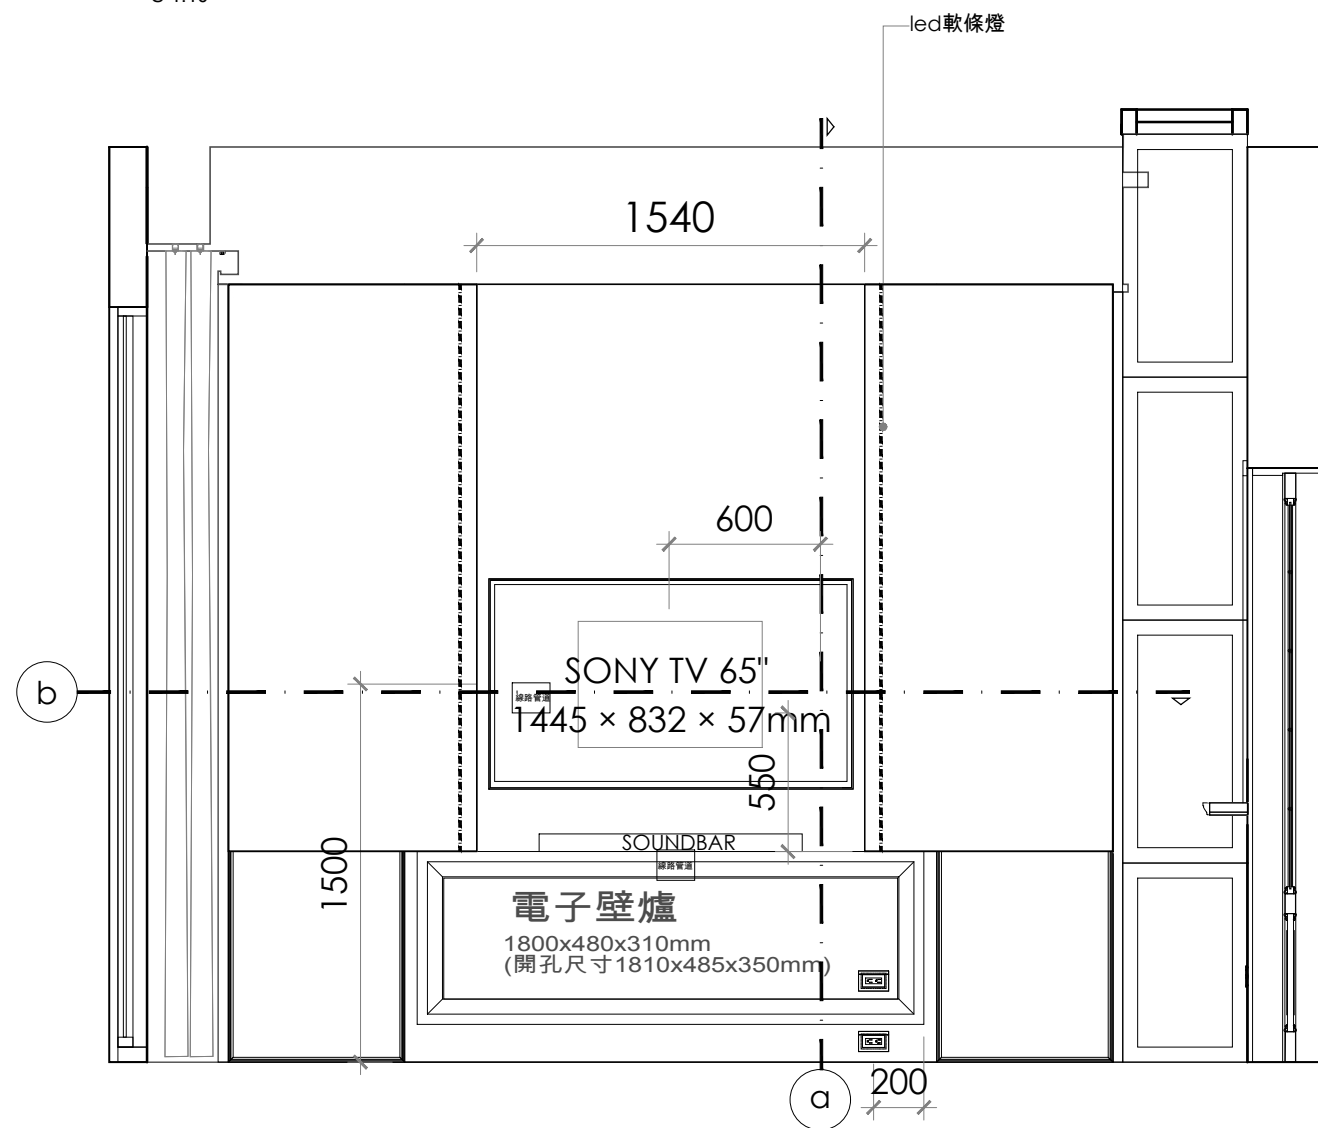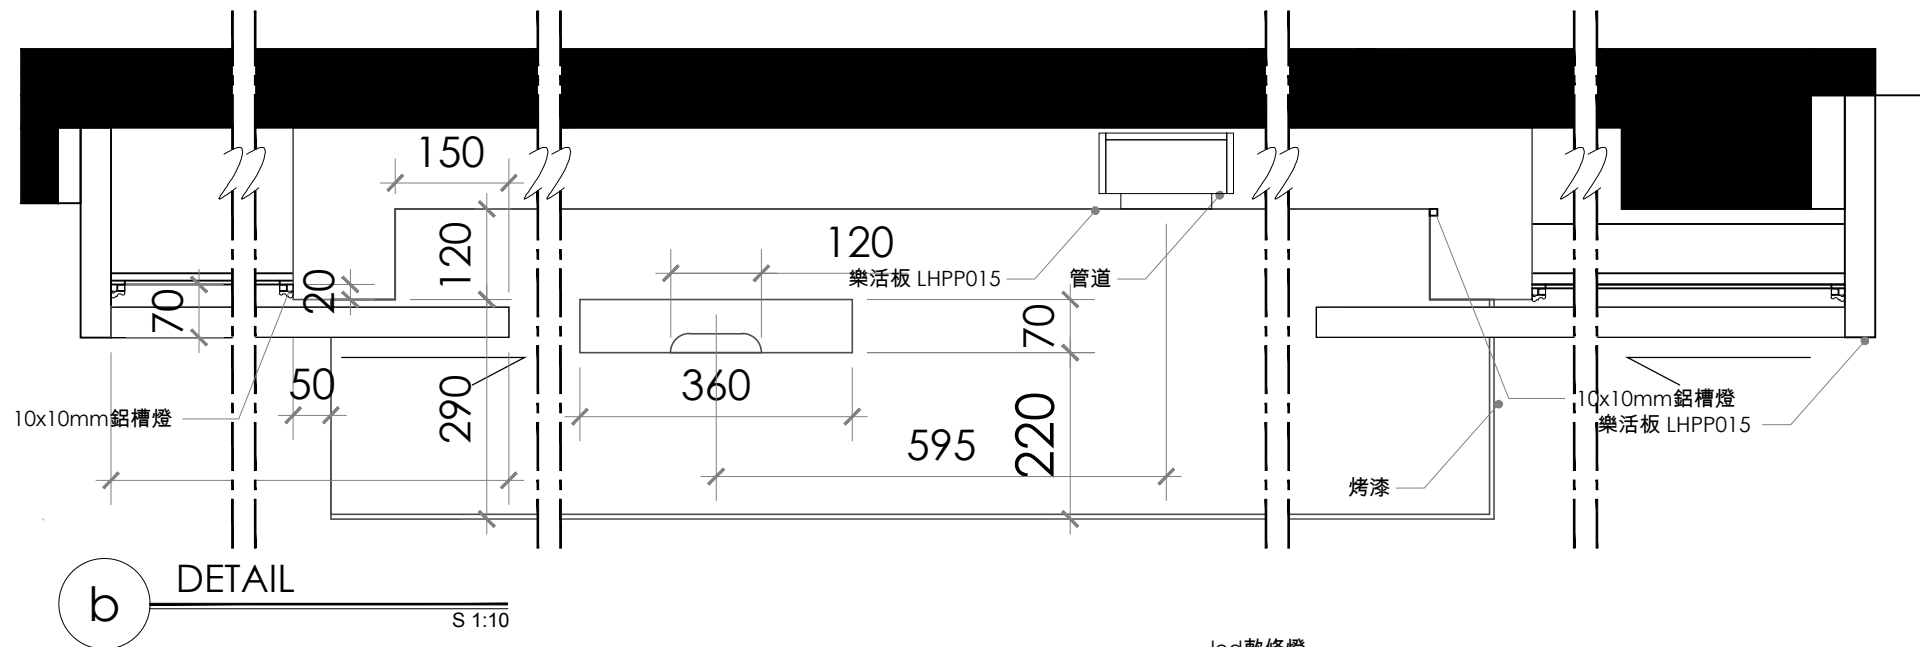

1 ELEVATION Scale=1:30 E-26

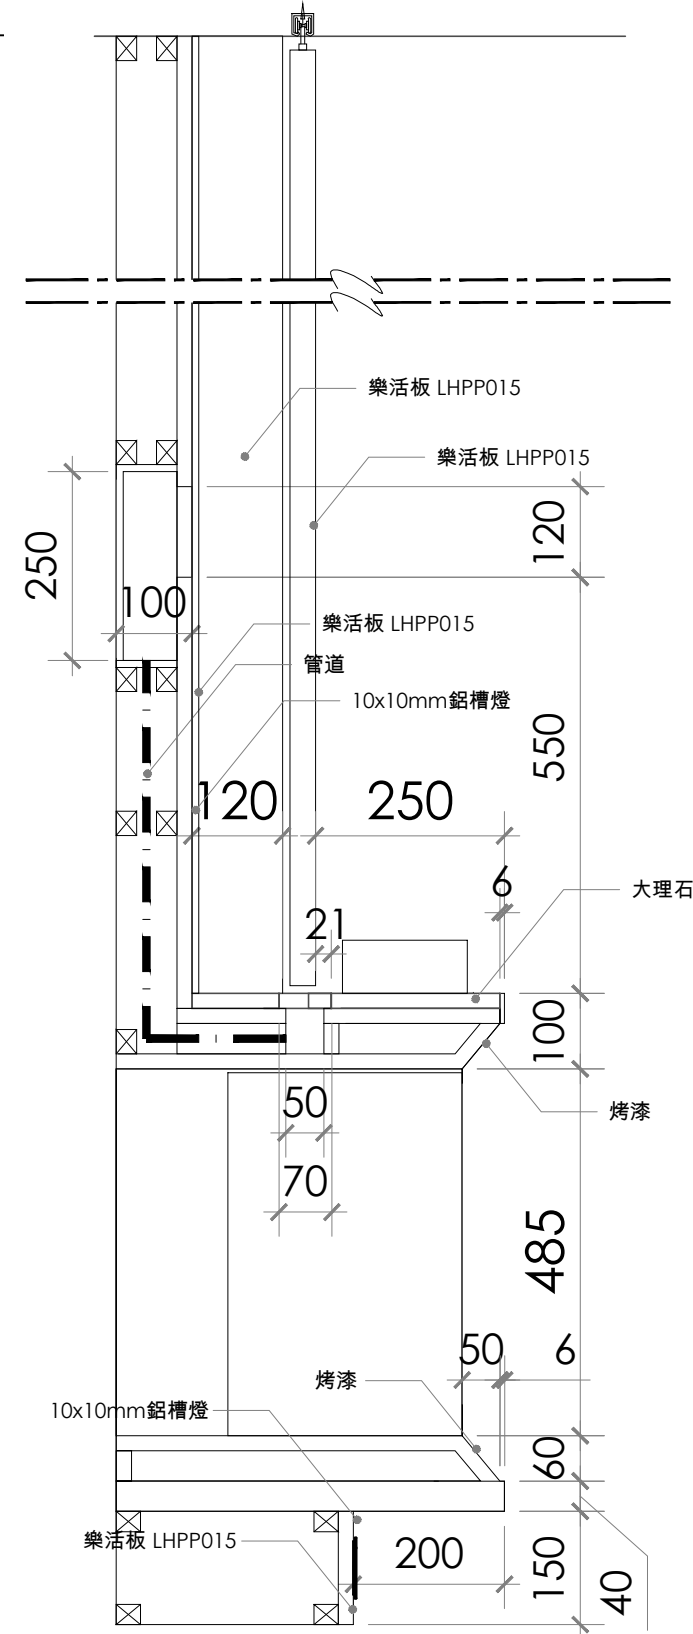

a DETAIL S 1:10


Revision	
APPROVAL/核准	
設計者:	建築師:
業主:	

備註:
a. 圖面標註尺寸僅供參考，施作均以現場放樣檢討之。
b. 圖面標註尺寸、材料及文字敘述因版本不同之差異，均以出圖章簽認日期之最近為準。
c. 電腦圖檔除由合約訂定外，均不得以任何方式外流。
d. 圖面所示均為本公司所擁有之智慧財產，切勿以任何方式複製修改。

M
MULA DECO
A 3F, N.26, Ln.290, Guangfu S. Rd., Taipei.
T 886-2-2546-3258
F 886-2-2546-3257
E Guido@muladeco.com

Project / 案名
天母葉公館
Sheet Title / 圖名
1F
立面圖

Date / 日期	Scale / 比例
8/10/2026	1/30CM
Designer / 設計	Approval / 核准
MONICA LIN	
Job No / 業務編號	Drawn By / 繪圖
00000	GUIDO
Dwg No.	Page No.
E-26	57

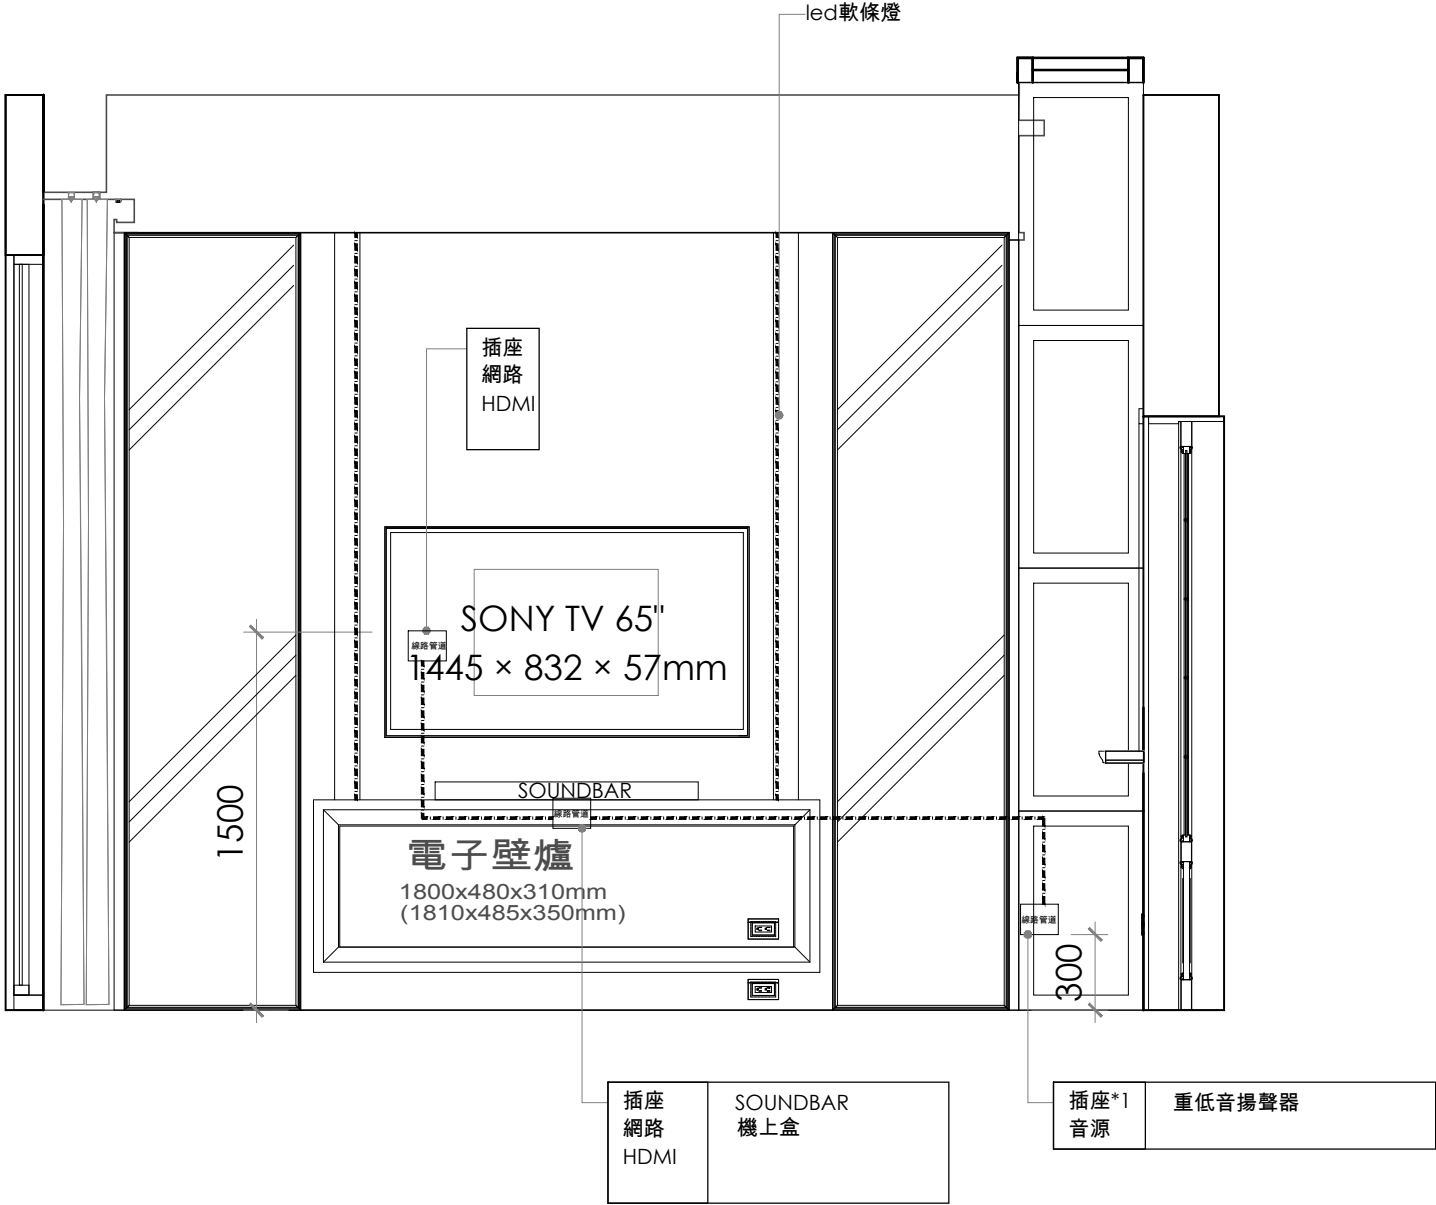

Revision

APPROVAL/核准

設計者:	建築師:
業主:	

備註:

- a. 圖面標註尺寸僅供參考，施作均以現場放樣檢討之。
b. 圖面標註尺寸、材料及文字敘述因版本不同之差異，均以出圖章簽認日期之最近為準。
c. 電腦圖檔除由合約訂定外，均不得以任何方式外流。
d. 圖面所示均為本公司所擁有之智慧財產，切勿以任何方式複製修改。



MULA DECO

▲ 3F, N.26, Ln.290, Guangfu S. Rd., Taipei.
☎ 886-2-2546-3258
☎ 886-2-2546-3257
✉ Guido@muladeco.com

Project / 案名

天母葉公館


Sheet Title / 圖名



1F

立面圖

Date / 日期	Scale / 比例
8/10/2026	1/30CM
Designer / 設計	Approval / 核准
MONICA LIN	
Job No / 業務編號	Drawn By / 繪圖
00000	GUIDO

Dwg No.	Page No.
E-26	58

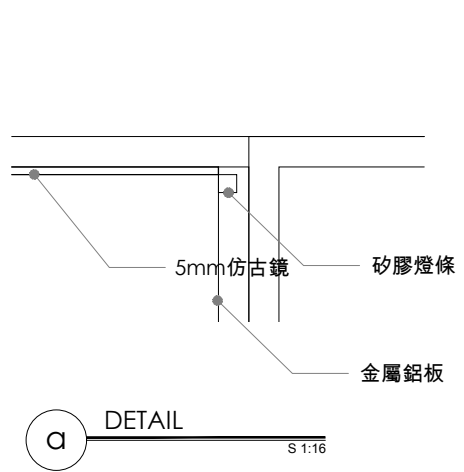

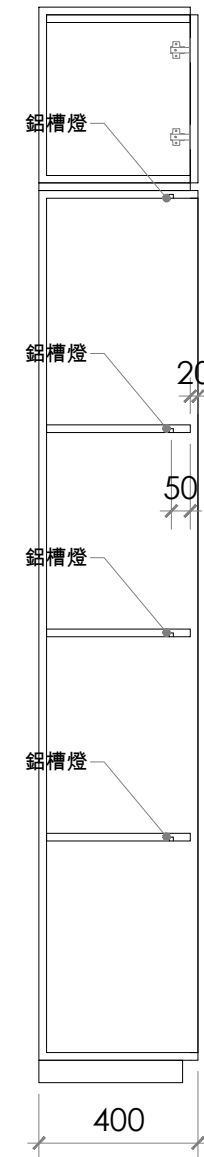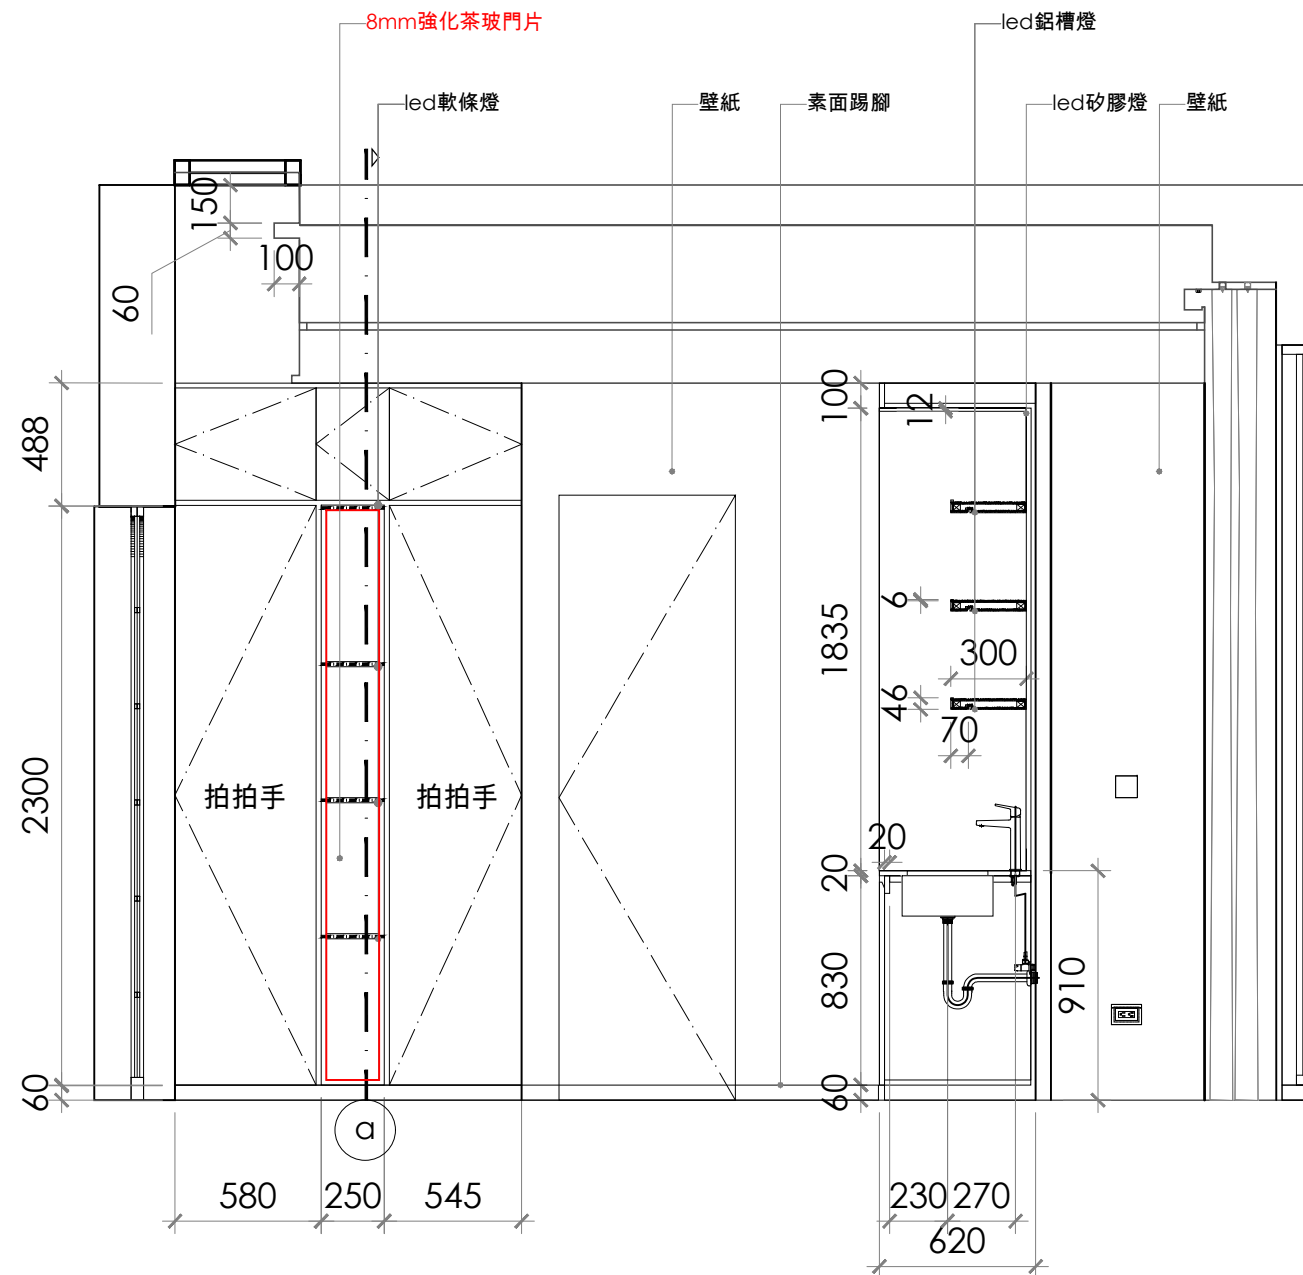

DETAIL

S 1:20

[illegible]

設計者:	建築師:
業主:	




A 3F, N.26, Ln.290, Guangfu S. Rd., Taipei.
T 886-2-2546-3258
F 886-2-2546-3257
E Guido@muladeco.com


天母葉公館

立面圖

Date / 日期	Scale / 比例
8/10/2026	1/30CM
Designer / 設計	Approval / 核准
MONICA LIN	
Job No / 業務編號	Drawn By / 繪圖
00000	GUIDO
Dwg No.	Page No.
E-28	60

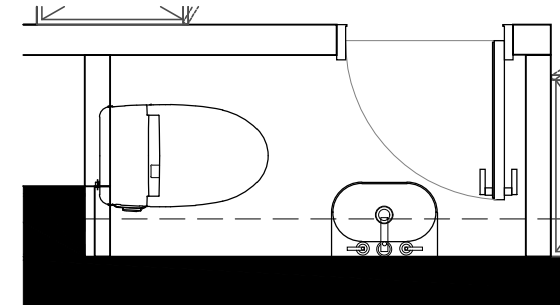

▼FL ±0 mm
▲FL -50 mm

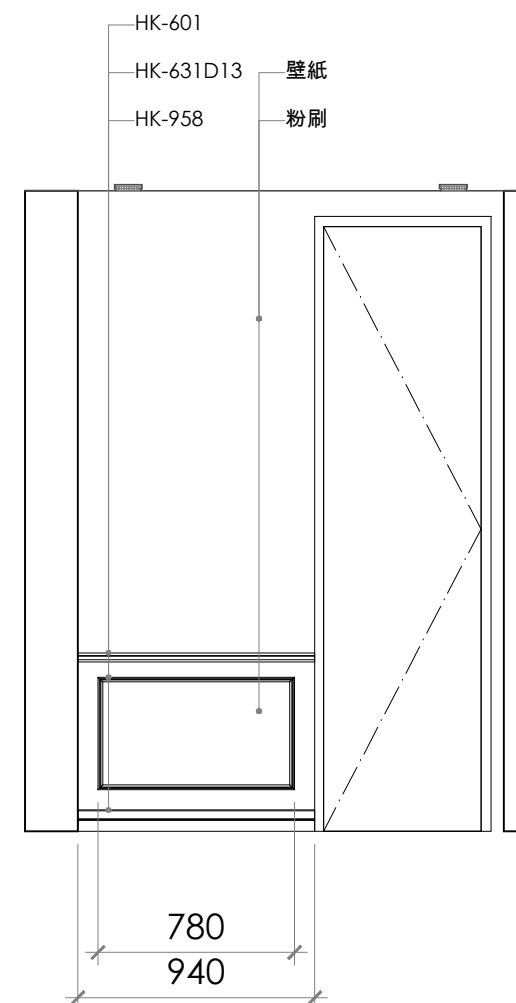[illegible]

備註:

- 圖面標註尺寸僅供參考，施作均以現場放樣檢討之。
- 圖面標註尺寸、材料與文字敘述因版本不同之差異，均以出圖章簽認日期之最近為準。
- 電腦圖檔除由合約訂定外，均不得以任何方式外流。
- 圖面所示均為本公司所擁有之智慧財產，切勿以任何方式複製修改。



MULA DECO

A 3F, N.26, Ln.290, Guangfu S. Rd., Taipei.
T 886-2-2546-3258
F 886-2-2546-3257
E Guido@muladeco.com


Project / 案名

天母葉公館

Sheet Title / 圖名
1F

立面圖

Date / 日期	Scale / 比例
8/10/2026	1/30CM
Designer / 設計	Approval / 核准
MONICA LIN	
Job No / 業務編號	Drawn By / 繪圖
00000	GUIDO
Dwg No.	Page No.
E-29	61

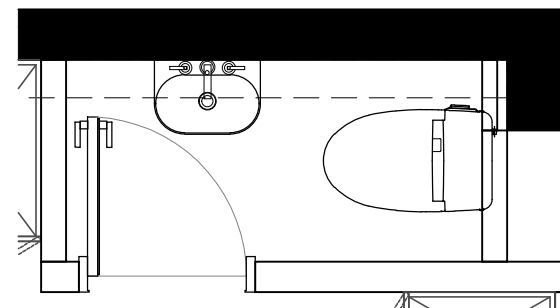

Technical drawing of a bathroom vanity unit. The drawing shows a front view of the unit with a central arched mirror, two side cabinets, and a rectangular basin. Dimensions are provided in millimeters (mm). The overall width is 1690 mm, and the overall height is 1500 mm. The vanity unit is 1530 mm wide and 900 mm high. The side cabinets are 260 mm wide. The mirror is 600 mm wide. The basin is 600 mm wide. The drawing includes labels for materials and components: 壁紙 (Wallpaper), 粉刷 (Paint), HK-958, HK-601, and HK-631D13.

Dimensions (mm):


- Overall width: 1690
- Overall height: 1500
- Vanity unit width: 1530
- Vanity unit height: 900
- Side cabinet width: 260
- Mirror width: 600
- Basin width: 600

Labels:

- 壁紙 (Wallpaper)
- 粉刷 (Paint)
- HK-958
- HK-601
- HK-631D13


Scale=1:30

E-30 62

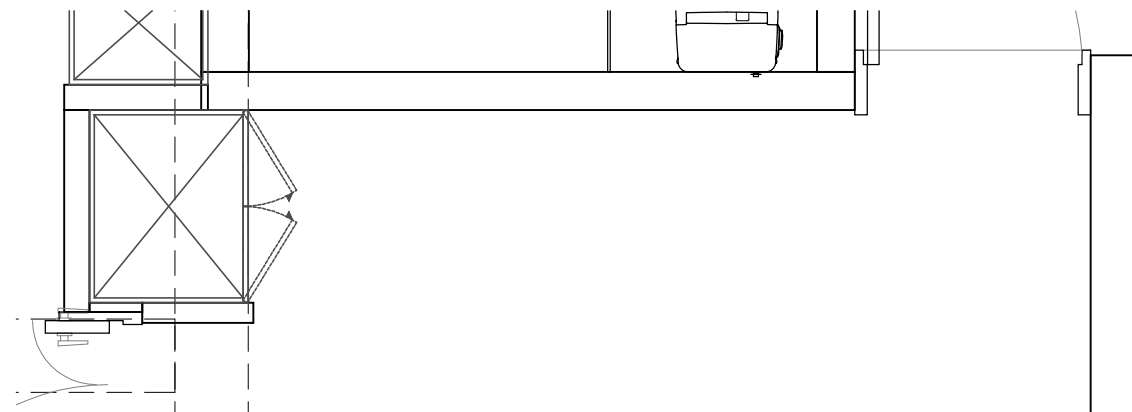

▲CH 2920mm
▲CH 2720mm
▲CH 2490mm

▼FL ±0 mm
▲FL -50 mm

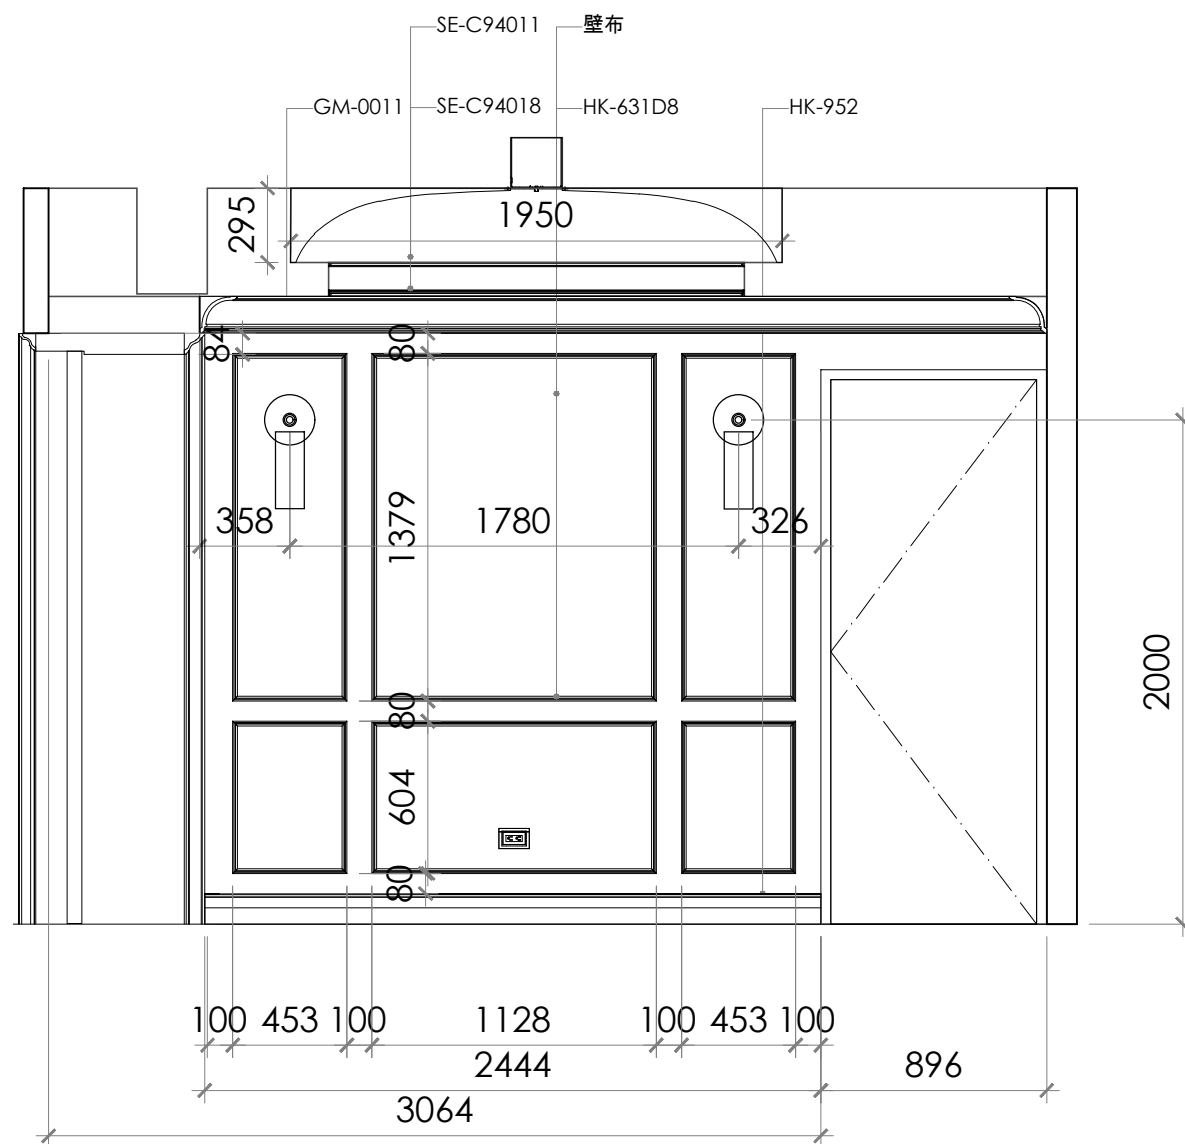

1
E-31

ELEVATION

Scale=1:30

Revision

APPROVAL/核准

設計者:	建築師:
業主:	

備註:

- 圖面標註尺寸僅供參考，施作均以現場放樣檢討之。
- 圖面標註尺寸、材料及文字敘述因版本不同之差異，均以出圖章簽認日期之最近為準。
- 電腦圖檔除由合約訂定外，均不得以任何方式外流。
- 圖面所示均為本公司所擁有之智慧財產，切勿以任何方式複製修改。



MULA DECO

▲ 3F, N.26, Ln.290, Guangfu S. Rd., Taipei.
☎ 886-2-2546-3258
☎ 886-2-2546-3257
✉ Guido@muladeco.com


Project / 案名

天母葉公館

Sheet Title / 圖名
2F


立面圖

Date / 日期	Scale / 比例
8/10/2026	1/30CM
Designer / 設計	Approval / 核准
MONICA LIN	
Job No / 業務編號	Drawn By / 繪圖
00000	GUIDO
Dwg No.	Page No.
E-31	63

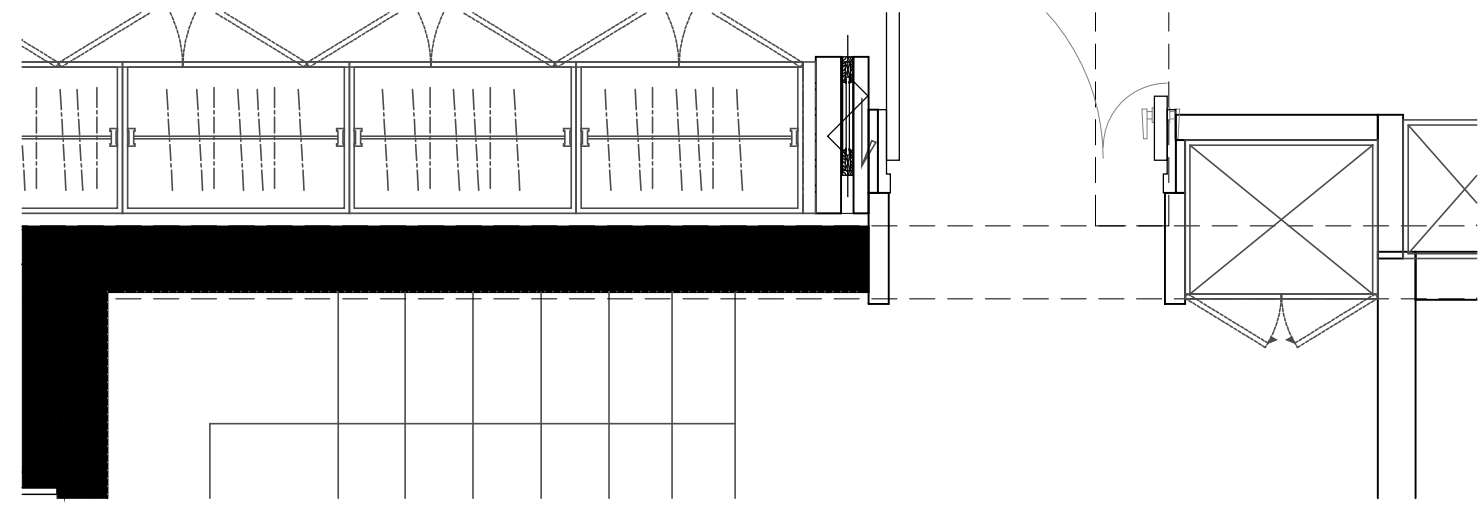


▲CH 2920mm
▲CH 2720mm
▲CH 2490mm

▼FL ±0 mm
▲FL -50 mm

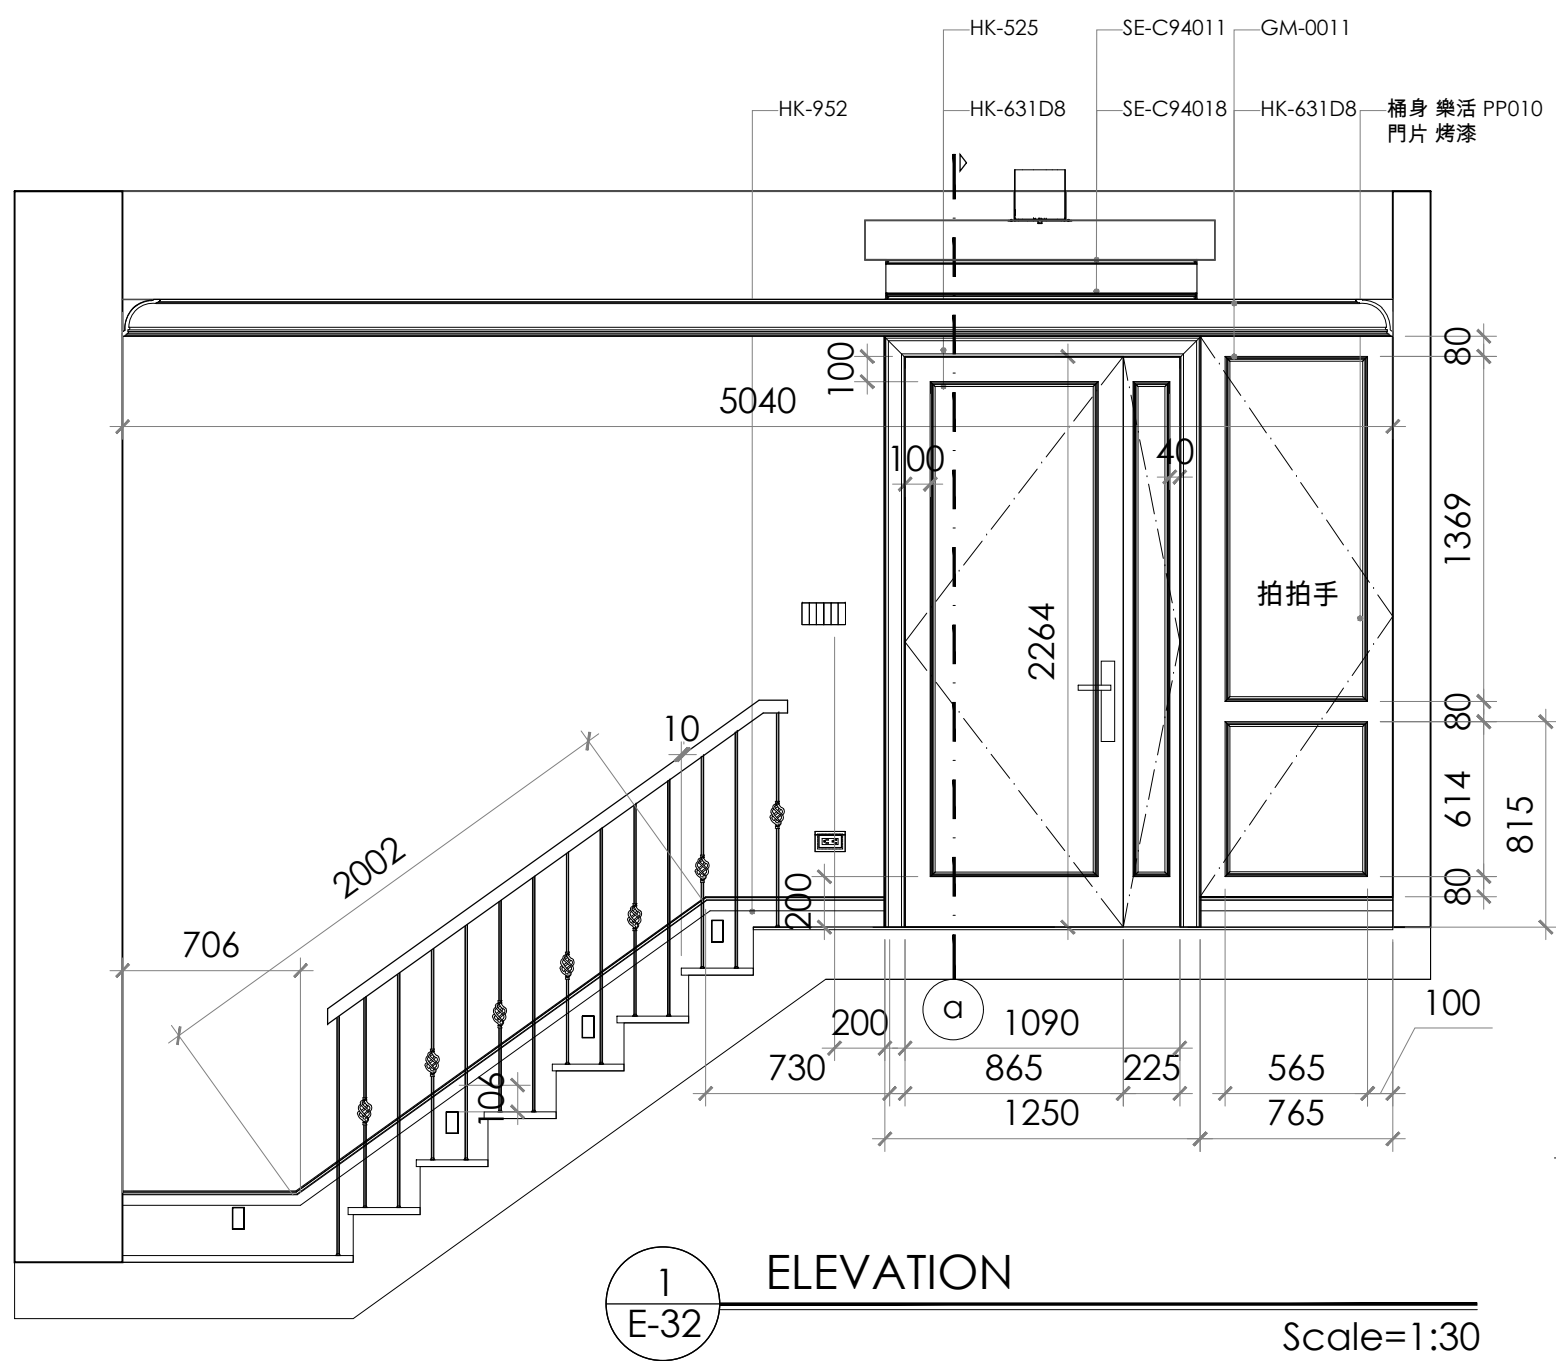

1 ELEVATION
E-32 Scale=1:30

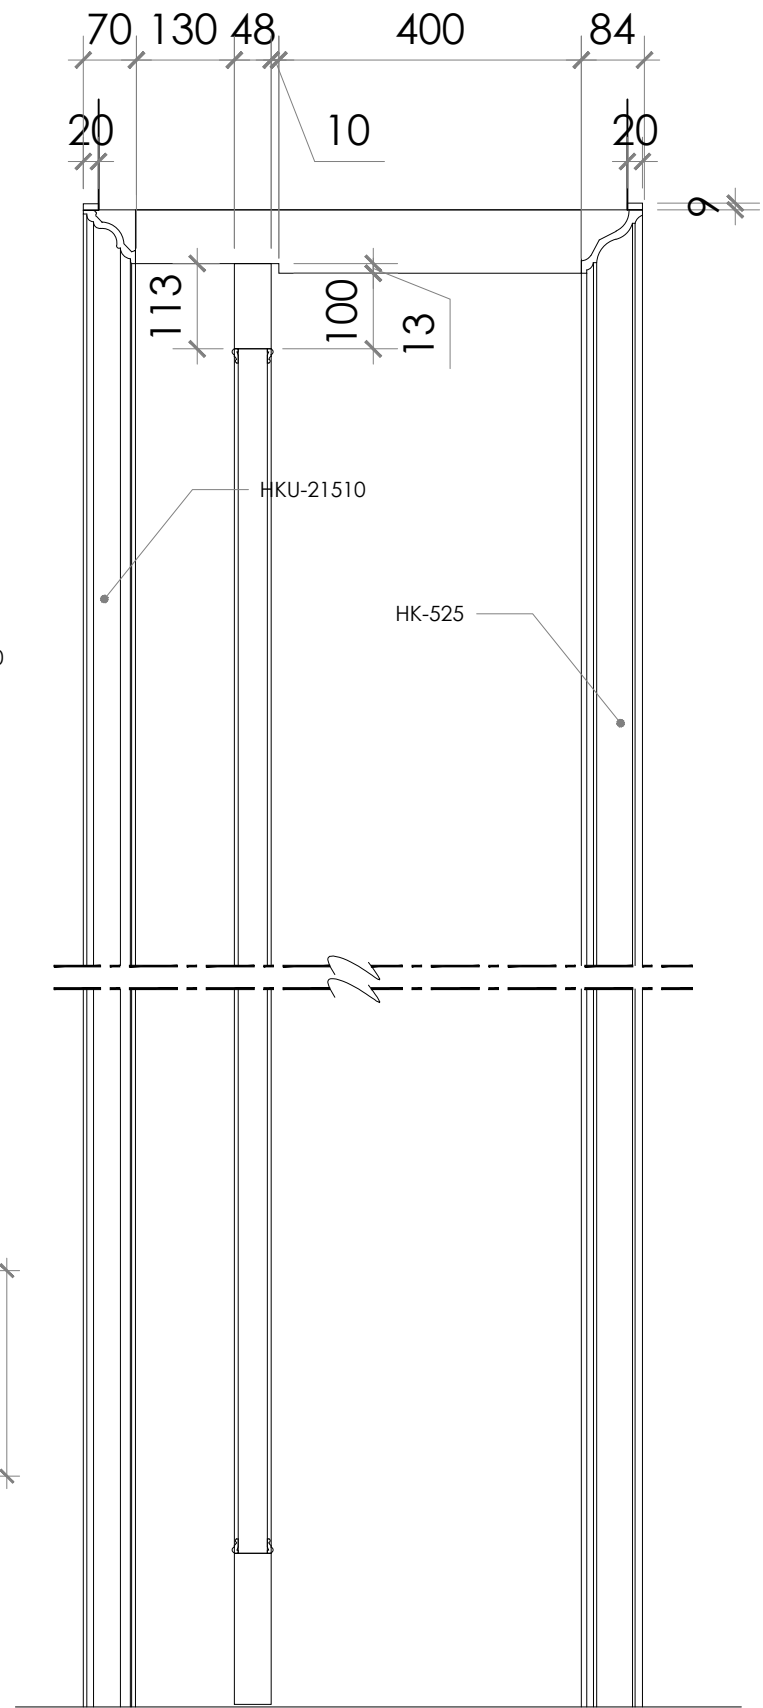

a DETAIL
S 1:10

Revision

APPROVAL/核准

設計者:	建築師:
業主:	

備註:
a. 圖面標註尺寸僅供參考，施作均以現場放樣檢討之。
b. 圖面標註尺寸、材料及文字敘述因版本不同之差異，均以出圖章簽認日期之最近為準。
c. 電腦圖檔除由合約訂定外，均不得以何方式外流。
d. 圖面所示均為本公司所擁有之智慧財產，切勿以任何方式複製修改。

M

MULA DECO

▲ 3F, N.26, Ln.290, Guangfu S. Rd., Taipei.
☎ 886-2-2546-3258
☎ 886-2-2546-3257
✉ Guido@muladeco.com

Project / 案名

天母葉公館

Sheet Title / 圖名

2F

立面圖

Date / 日期	Scale / 比例
8/10/2026	1/30CM
Designer / 設計	Approval / 核准
MONICA LIN	
Job No / 業務編號	Drawn By / 繪圖
00000	GUIDO
Dwg No.	Page No.
E-32	64



▼FL ±0 mm
▲FL -50 mm

[illegible]

APPROVAL/核准

設計者:	建築師:
業主:	

備註:

- g. 圖面標註尺寸僅供參考，施作均以現場放樣檢討之。
- h. 圖面標註尺寸、材料及文字敘述因版本不同之差異，均以圖章簽認日期之最近為準。
- i. 電腦圖檔除由合約訂定外，均不得以任何方式外流。
- j. 圖面所示均為本公司所擁有之智慧財產，切勿以任何方式複製修改。



MULA DECO

A 3F, N.26, Ln.290, Guangfu S. Rd., Taipei.
T 886-2-2546-3258
F 886-2-2546-3257
E Guido@muladeco.com


Project / 案名

天母葉公館

Sheet Title / 圖名
2F


立面圖

Date / 日期	Scale / 比例
8/10/2026	1/30CM
Designer / 設計	Approval / 核准
MONICA LIN	
Job No / 案卷編號	Drawn By / 繪圖
00000	GUIDO
Dwg No.	Page No.
E-33	65

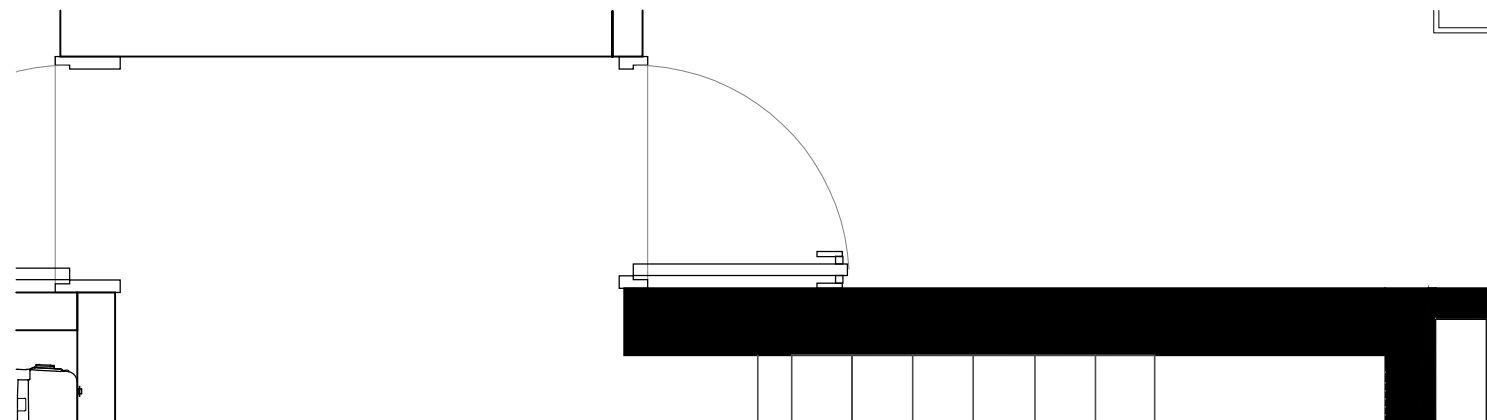

▲CH 2920mm
▲CH 2720mm
▲CH 2490mm


▼FL ±0 mm
▲FL -50 mm

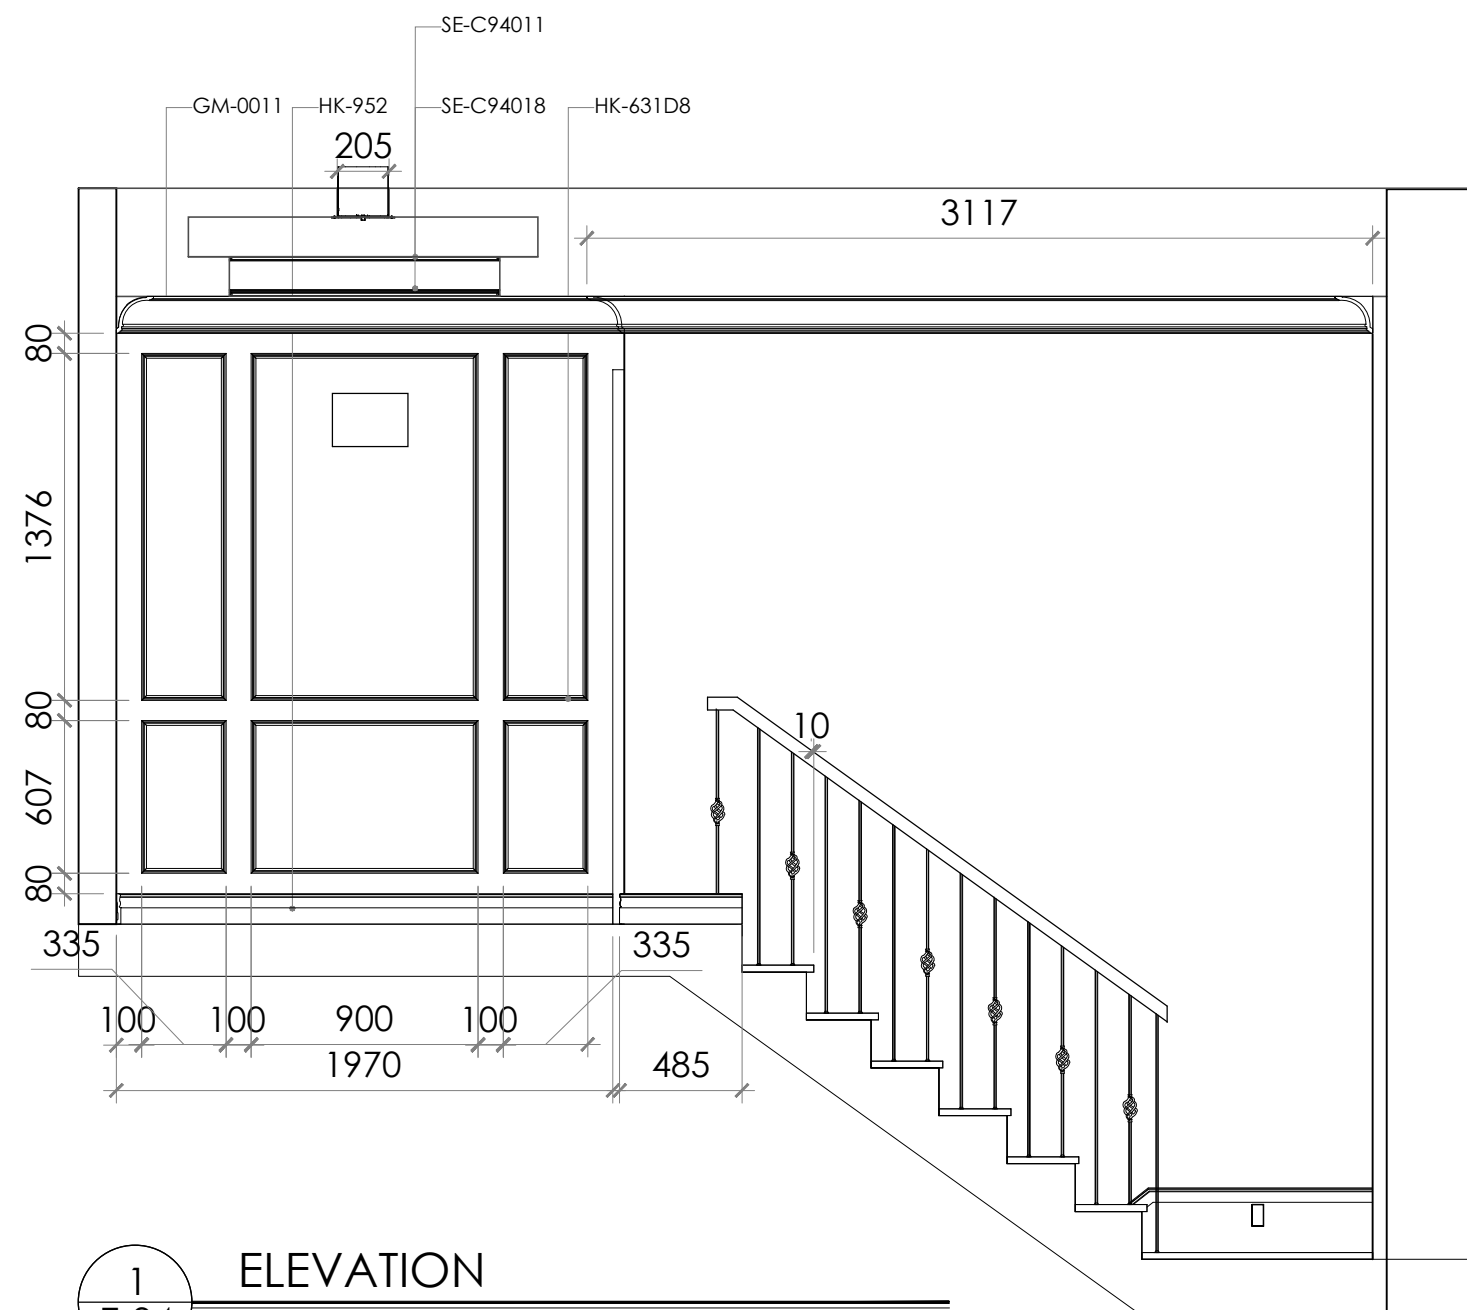

1
E-34

ELEVATION

Scale=1:30

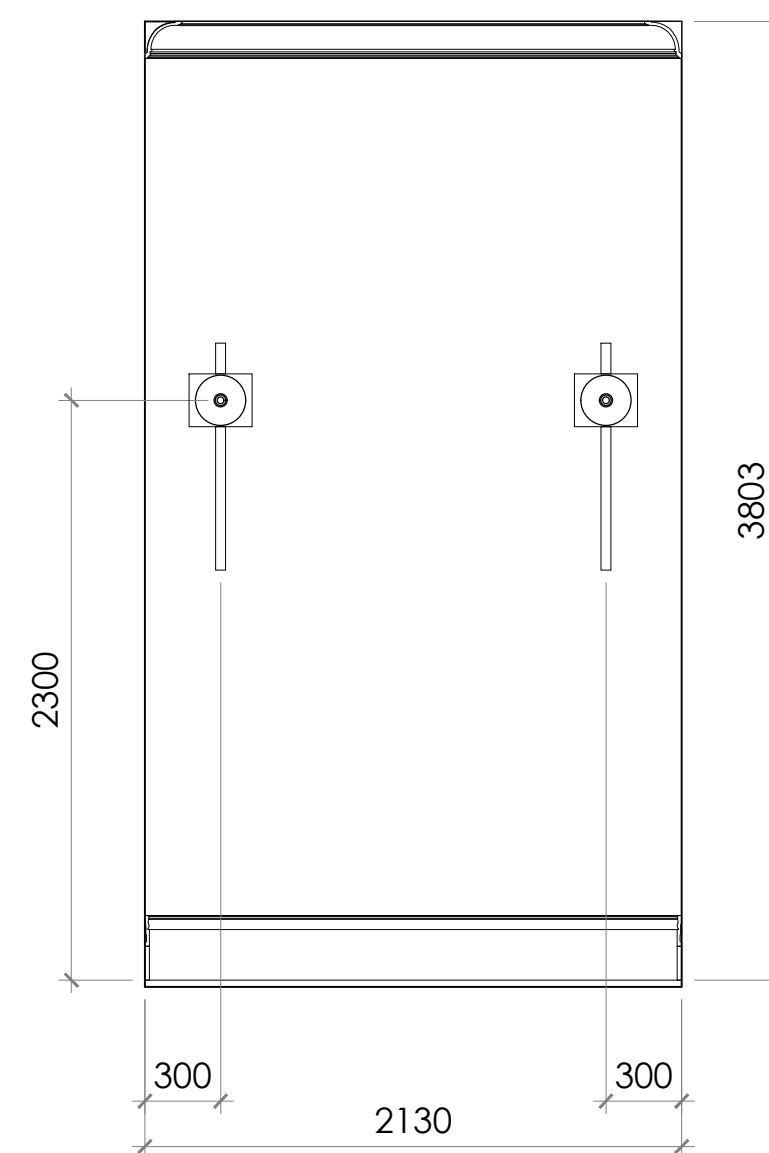

APPROVAL/核准

設計者:	建築師:
業主:	

備註:

- 圖面標註尺寸僅供參考，施作均以現場放樣檢討之。
- 圖面標註尺寸、材料及文字敘述因版本不同之差異，均以出圖章簽認日期之最近為準。
- 電腦圖檔除由合約訂定外，均不得以任何方式外流。
- 圖面所示均為本公司所擁有之智慧財產，切勿以任何方式複製修改。



MULA DECO

▲ 3F, N.26, Ln.290, Guangfu S. Rd., Taipei.
☎ 886-2-2546-3258
☎ 886-2-2546-3257
✉ Guido@muladeco.com

Project / 案名

天母葉公館


Sheet Title / 圖名
2F

立面圖

Date / 日期	Scale / 比例
8/10/2026	1/30CM
Designer / 設計	Approval / 核准
MONICA LIN	
Job No / 業務編號	Drawn By / 繪圖
00000	GUIDO
Dwg No.	Page No.


E-34

66

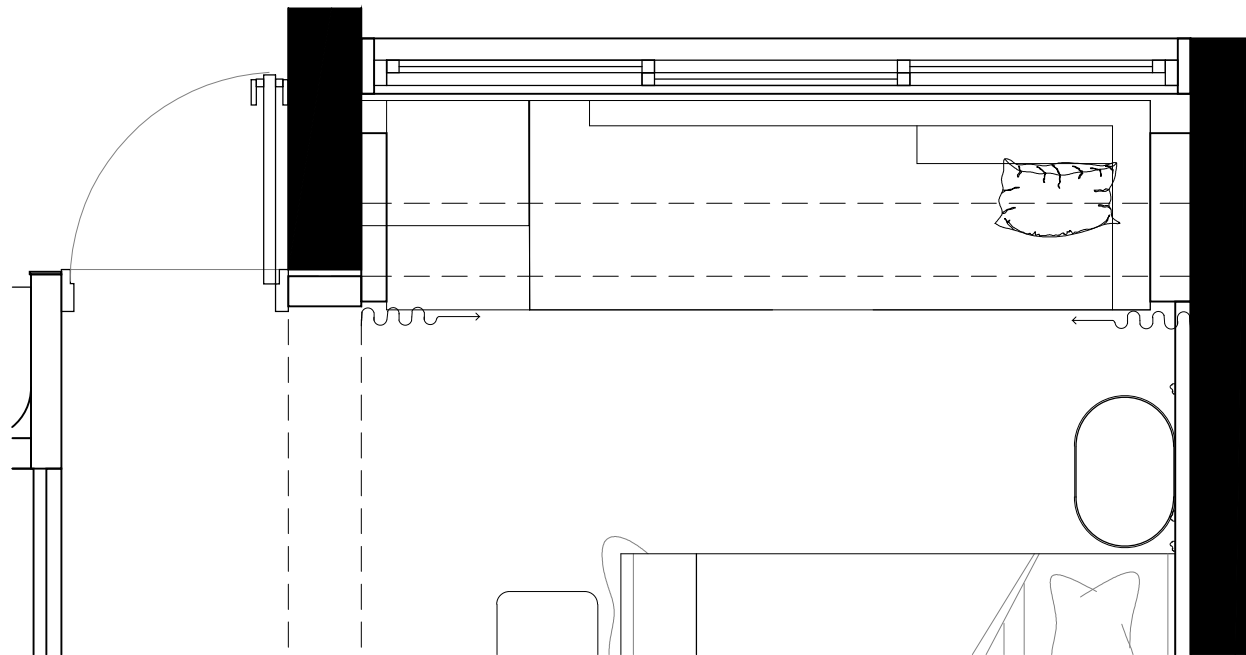

▲CH 2920mm
▲CH 2720mm
▲CH 2490mm

▼FL ±0 mm
▲FL -50 mm

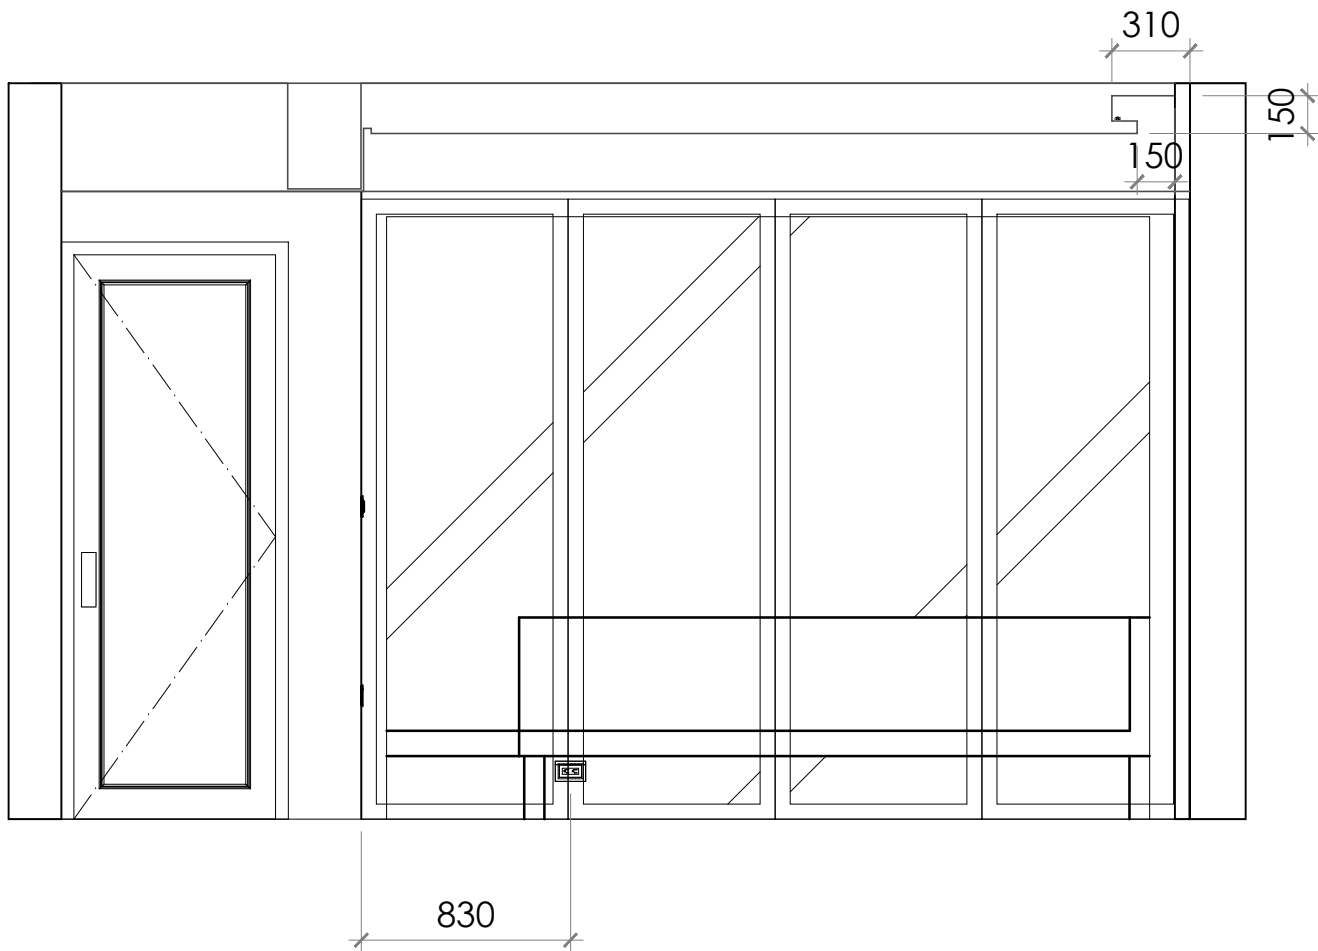

1
E-37

ELEVATION

Scale=1:30

Revision

APPROVAL/核准

設計者:	建築師:
業主:	

備註:

- a. 圖面標註尺寸僅供參考，施作均以現場放樣檢討之。
- b. 圖面標註尺寸、材料及文字敘述因版本不同之差異，均以出圖章簽認日期之最近為準。
- c. 電腦圖檔除由合約訂定外，均不得以任何方式外流。
- d. 圖面所示均為本公司所擁有之智慧財產，切勿以任何方式複製修改。



MULA DECO

▲ 3F, N.26, Ln.290, Guangfu S. Rd., Taipei.
☎ 886-2-2546-3258
☎ 886-2-2546-3257
✉ Guido@muladeco.com

Project / 案名

天母葉公館

Sheet Title / 圖名


2F

立面圖

Date / 日期	Scale / 比例
8/10/2026	1/30CM
Designer / 設計	Approval / 核准
MONICA LIN	
Job No / 業務編號	Drawn By / 繪圖
00000	GUIDO
Dwg No.	Page No.


E-37

69

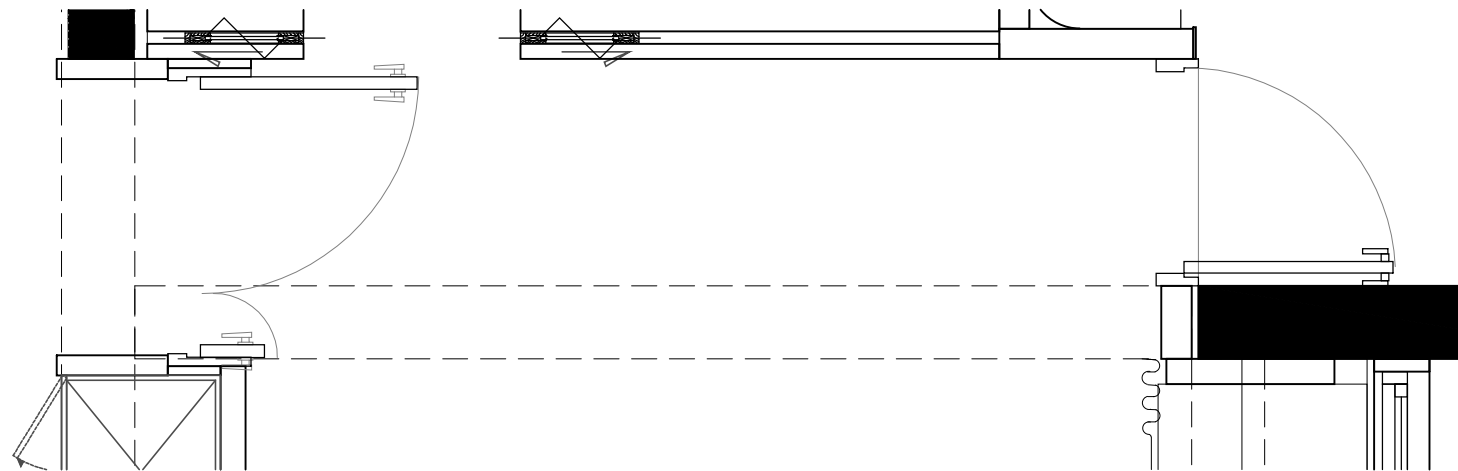

▲CH 2920mm
▲CH 2720mm
▲CH 2490mm

▼FL ±0 mm
▲FL -50 mm

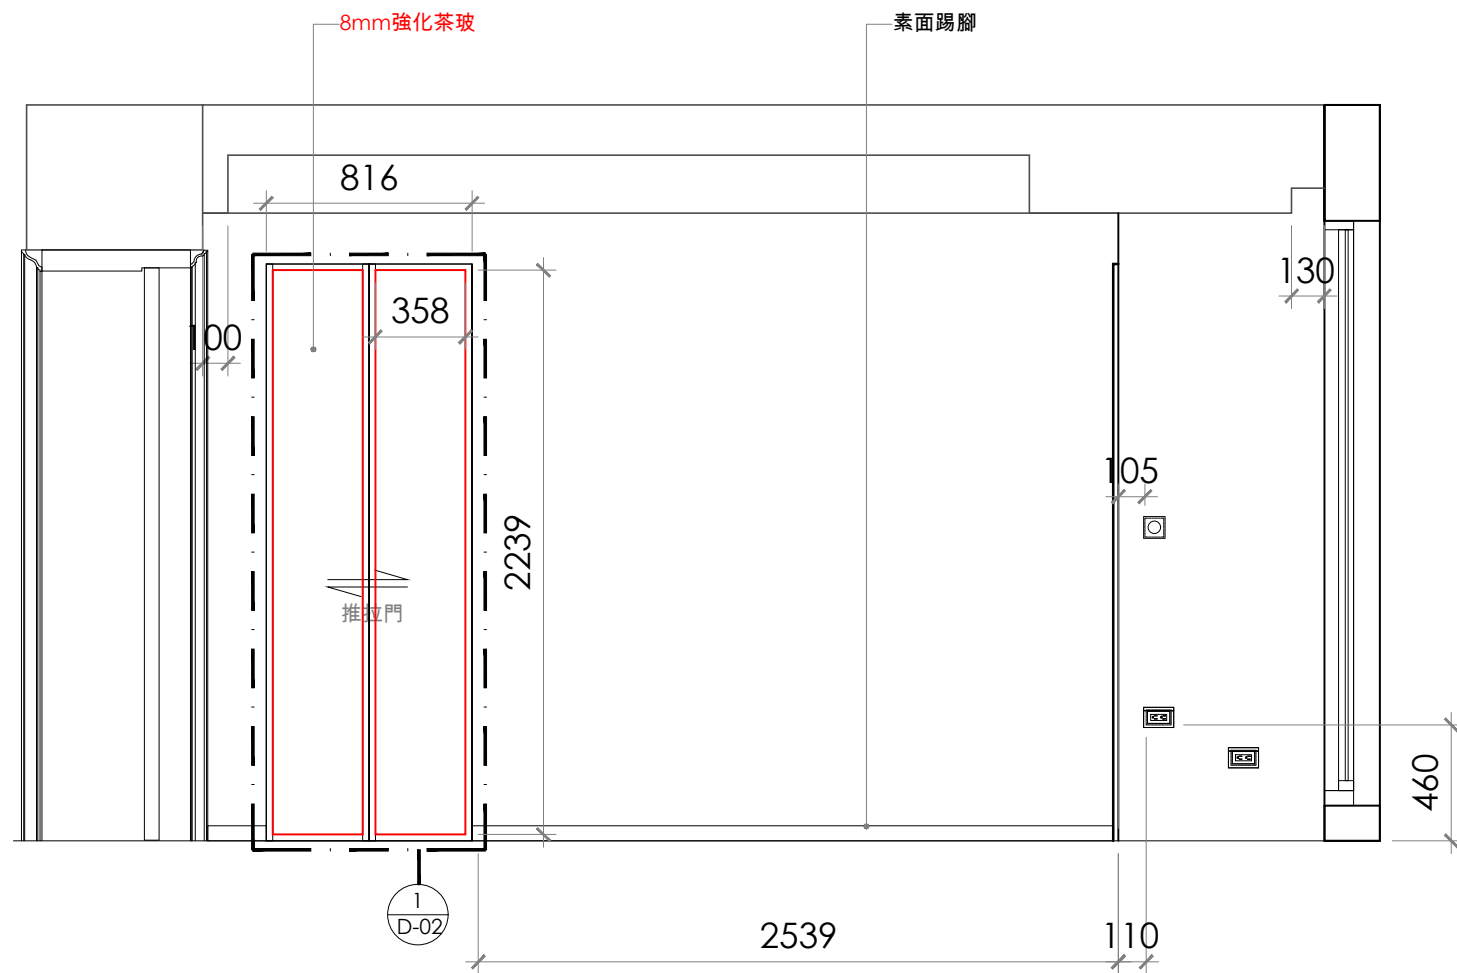

1
E-38

ELEVATION

Scale=1:30

Revision

APPROVAL/核准

設計者:	建築師:
業主:	

備註:

- 圖面標註尺寸僅供參考，施作均以現場放樣檢討之。
- 圖面標註尺寸、材料及文字敘述因版本不同之差異，均以出圖章簽認日期之最近為準。
- 電腦圖檔除由合約訂定外，均不得以任何方式外流。
- 圖面所示均為本公司所擁有之智慧財產，切勿以任何方式複製修改。



MULA DECO

▲ 3F, N.26, Ln.290, Guangfu S. Rd., Taipei.
☎ 886-2-2546-3258
☎ 886-2-2546-3257
✉ Guido@muladeco.com


Project / 案名

天母葉公館

Sheet Title / 圖名
2F


立面圖

Date / 日期	Scale / 比例
8/10/2026	1/30CM
Designer / 設計	Approval / 核准
MONICA LIN	
Job No / 業務編號	Drawn By / 繪圖
00000	GUIDO
Dwg No.	Page No.
E-38	70

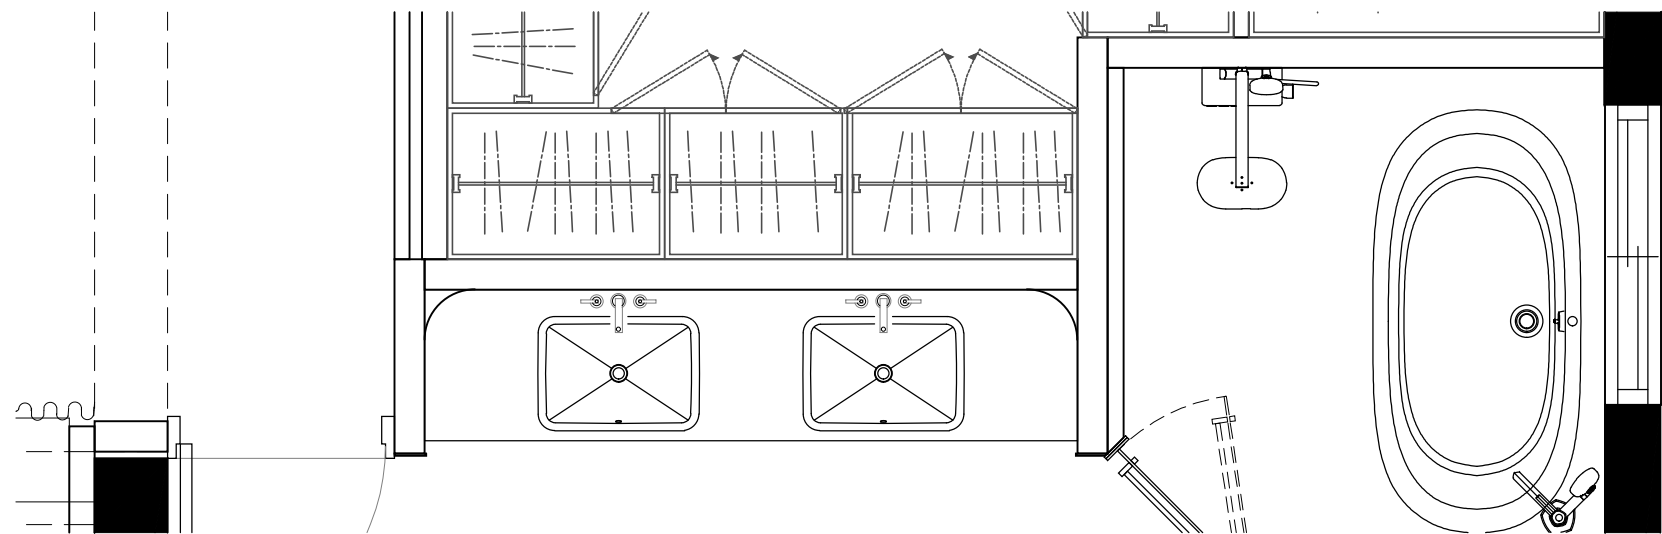

▲CH 2920mm
▲CH 2720mm
▲CH 2490mm

▼FL ±0 mm
▲FL -50 mm

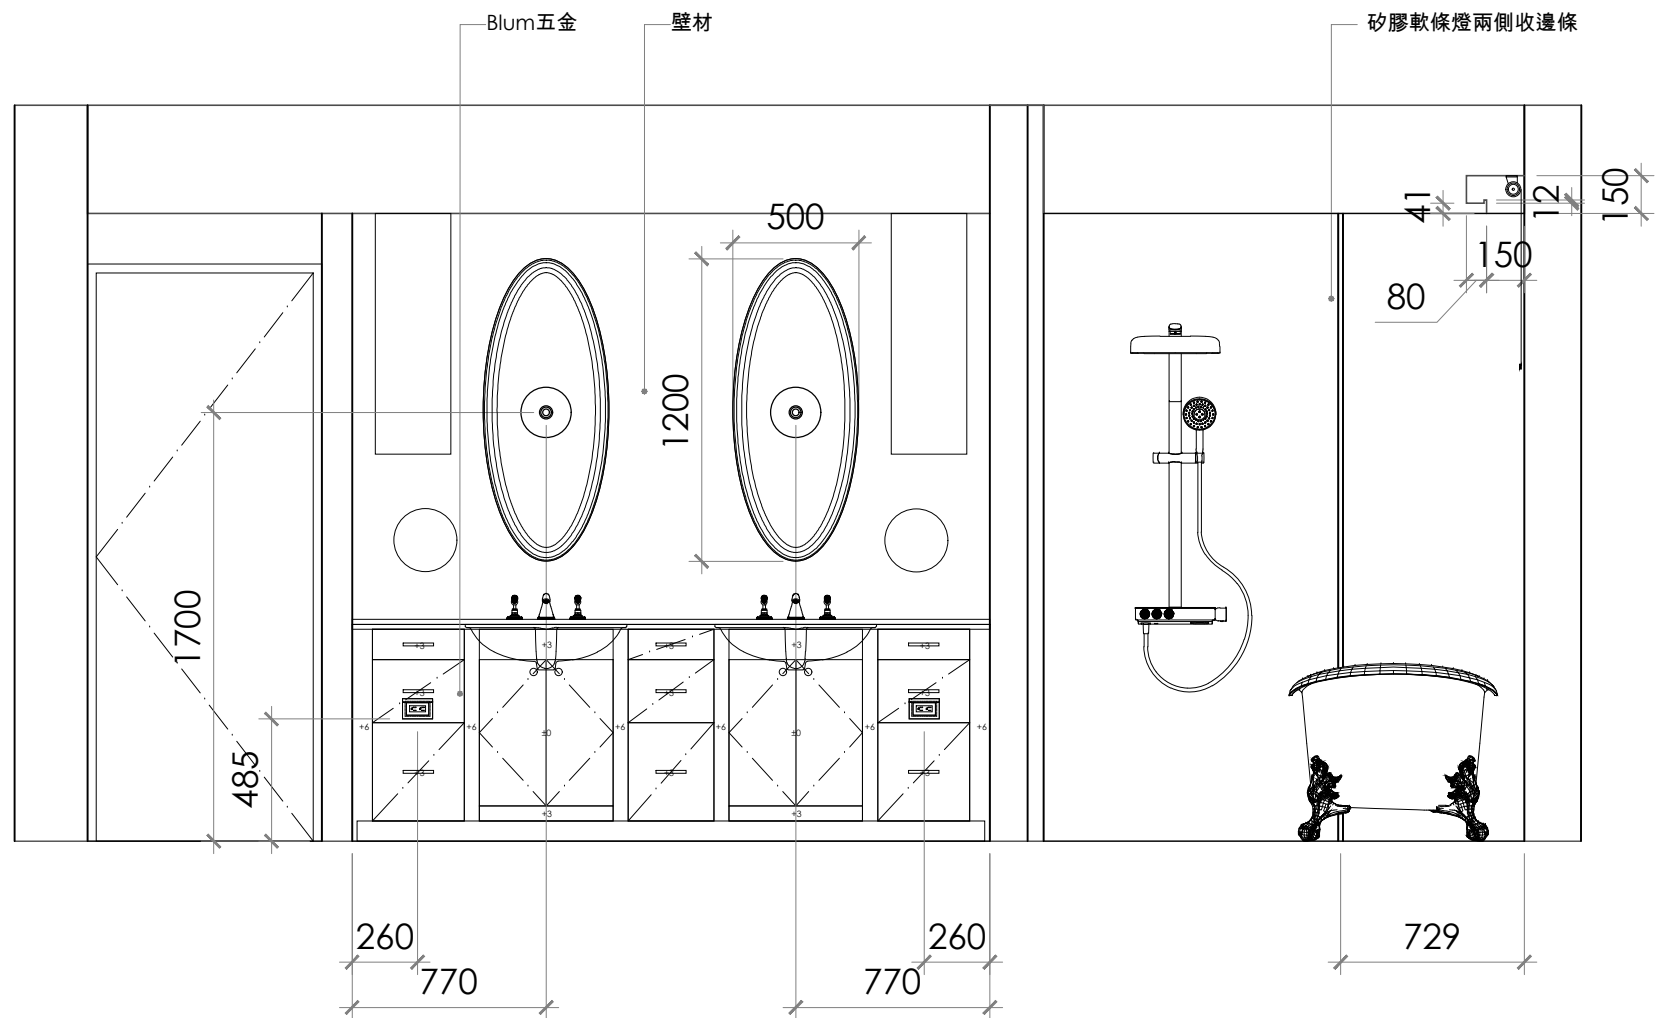

1
E-39

ELEVATION

Scale=1:30

Revision

APPROVAL/核准

設計者:	建築師:
業主:	

備註:

- 圖面標註尺寸僅供參考，施作均以現場放樣檢討之。
- 圖面標註尺寸、材料及文字敘述因版本不同之差異，均以出圖章簽認日期之最近為準。
- 電腦圖檔除由合約訂定外，均不得以任何方式外流。
- 圖面所示均為本公司所擁有之智慧財產，切勿以任何方式複製修改。



MULA DECO

▲ 3F, N.26, Ln.290, Guangfu S. Rd., Taipei.
☎ 886-2-2546-3258
☎ 886-2-2546-3257
✉ Guido@muladeco.com


Project / 案名

天母葉公館

Sheet Title / 圖名
2F


立面圖

Date / 日期	Scale / 比例
8/10/2026	1/30CM
Designer / 設計	Approval / 核准
MONICA LIN	
Job No / 業務編號	Drawn By / 繪圖
00000	GUIDO
Dwg No.	Page No.
E-39	71

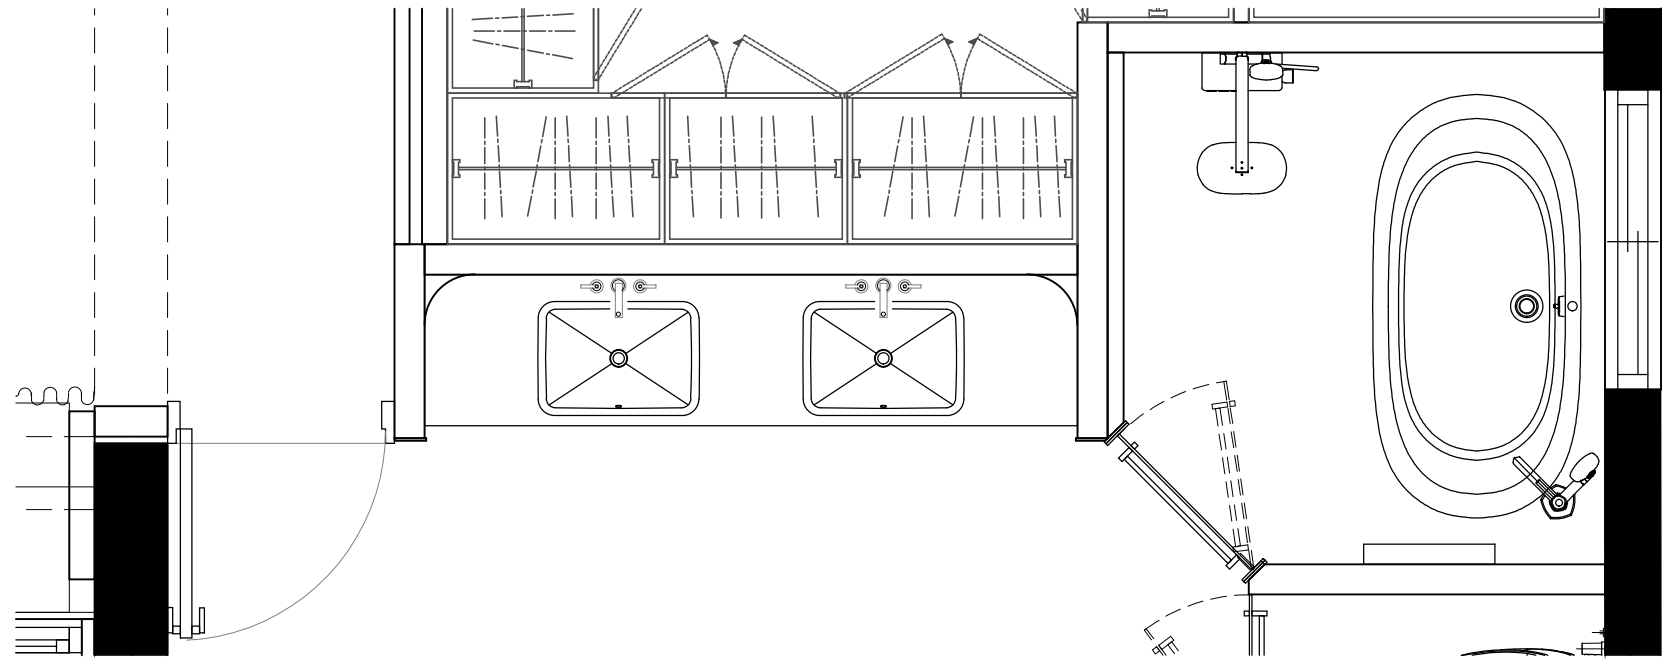

▲CH 2920mm
▲CH 2720mm
▲CH 2490mm

▼FL ±0 mm
▲FL -50 mm

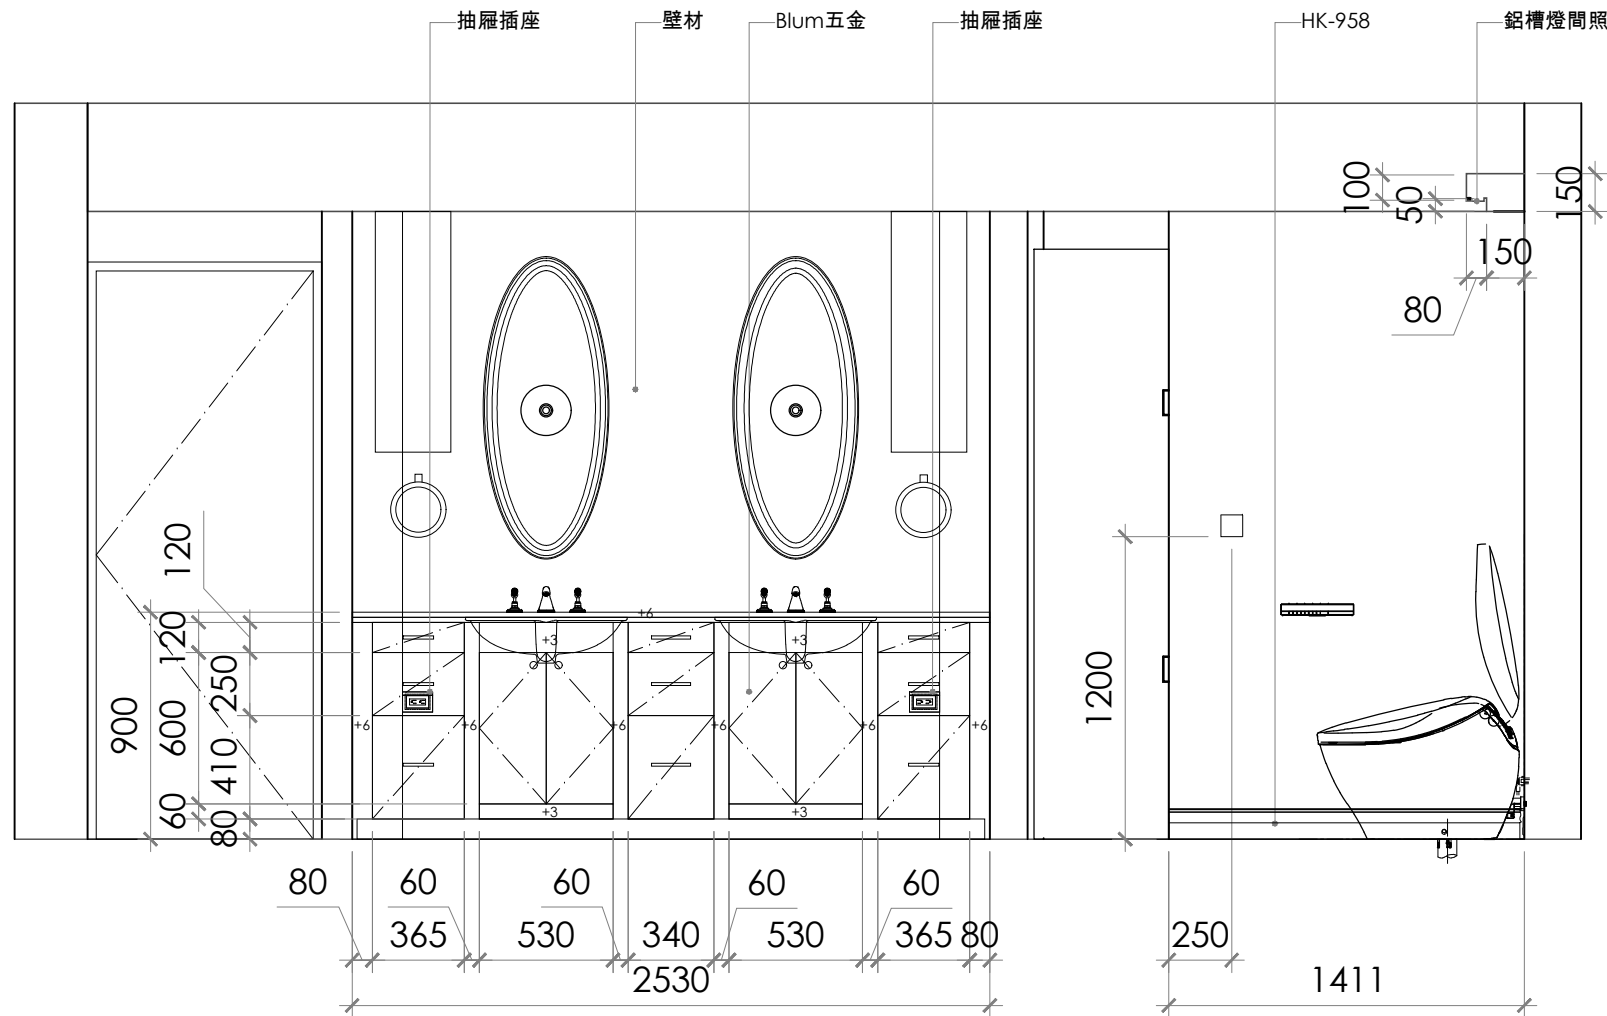

1
E-39

ELEVATION

Scale=1:30

Revision

APPROVAL/核准

設計者:	建築師:
業主:	

備註:

- 圖面標註尺寸僅供參考，施作均以現場放樣檢討之。
- 圖面標註尺寸、材料及文字敘述因版本不同之差異，均以出圖章簽認日期之最近為準。
- 電腦圖檔除由合約訂定外，均不得以何方式外流。
- 圖面所示均為本公司所擁有之智慧財產，切勿以任何方式複製修改。



MULA DECO

▲ 3F, N.26, Ln.290, Guangfu S. Rd., Taipei.
☎ 886-2-2546-3258
☎ 886-2-2546-3257
✉ Guido@muladeco.com





Project / 案名

天母葉公館

Sheet Title / 圖名
2F

立面圖

Date / 日期	Scale / 比例
8/10/2026	1/30CM
Designer / 設計	Approval / 核准
MONICA LIN	ABC
Job No / 業務編號	Drawn By / 繪圖
00000	GUIDO
Dwg No.	Page No.
E-39	72

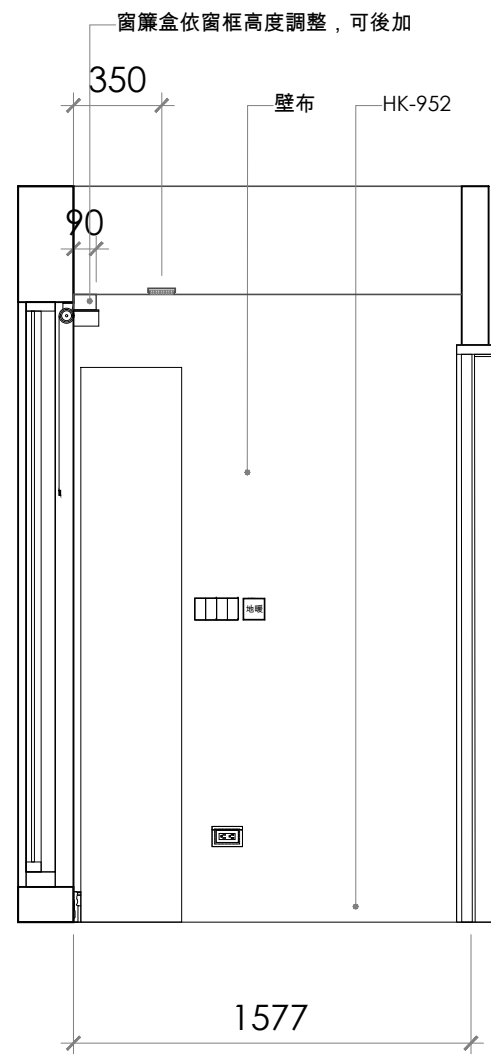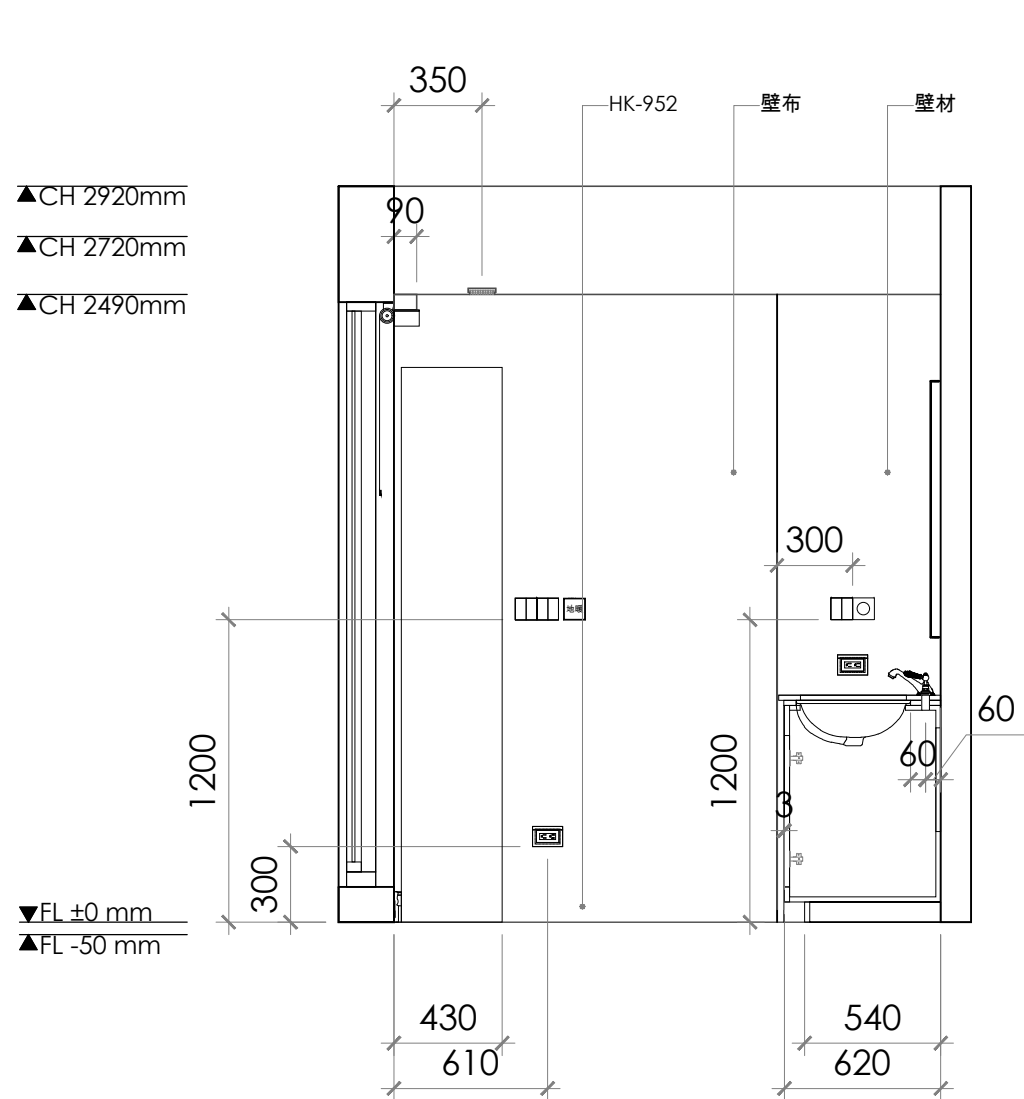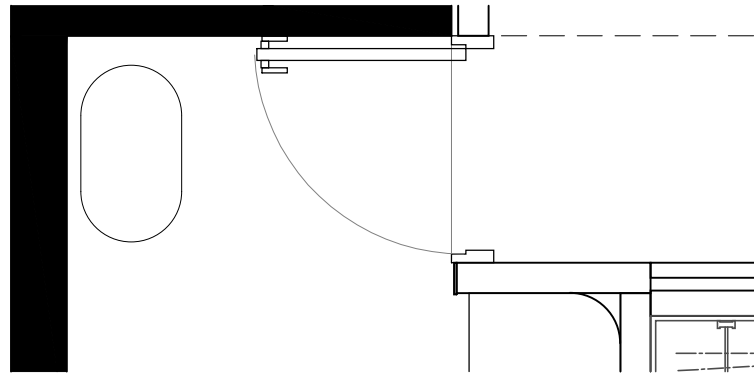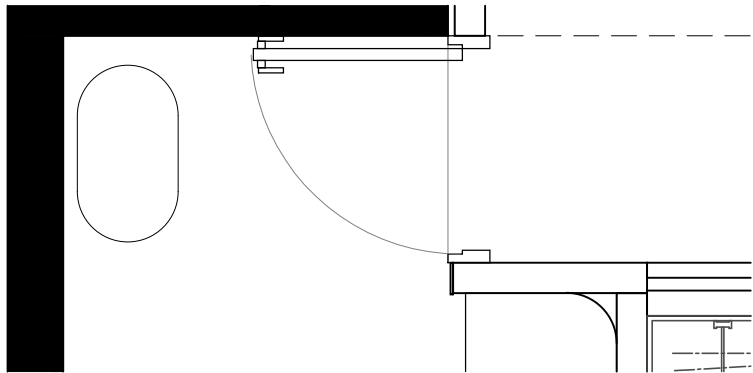

1
E-40

ELEVATION

Scale=1:30

Revision

APPROVAL/核准

設計者:	建築師:
業主:	

備註:

- 圖面標註尺寸僅供參考，施作均以現場放樣檢討之。
- 圖面標註尺寸、材料及文字敘述因版本不同之差異，均以出圖章簽認日期之最近為準。
- 電腦圖檔除由合約訂定外，均不得以任何方式外流。
- 圖面所示均為本公司所擁有之智慧財產，切勿以任何方式複製修改。



MULA DECO

▲ 3F, N.26, Ln.290, Guangfu S. Rd., Taipei.
☎ 886-2-2546-3258
☎ 886-2-2546-3257
✉ Guido@muladeco.com

Project / 案名

天母葉公館



Sheet Title / 圖名
2F

立面圖

Date / 日期	Scale / 比例
8/10/2026	1/30CM
Designer / 設計	Approval / 核准
MONICA LIN	
Job No / 業務編號	Drawn By / 繪圖
00000	GUIDO
Dwg No.	Page No.

E-40

73

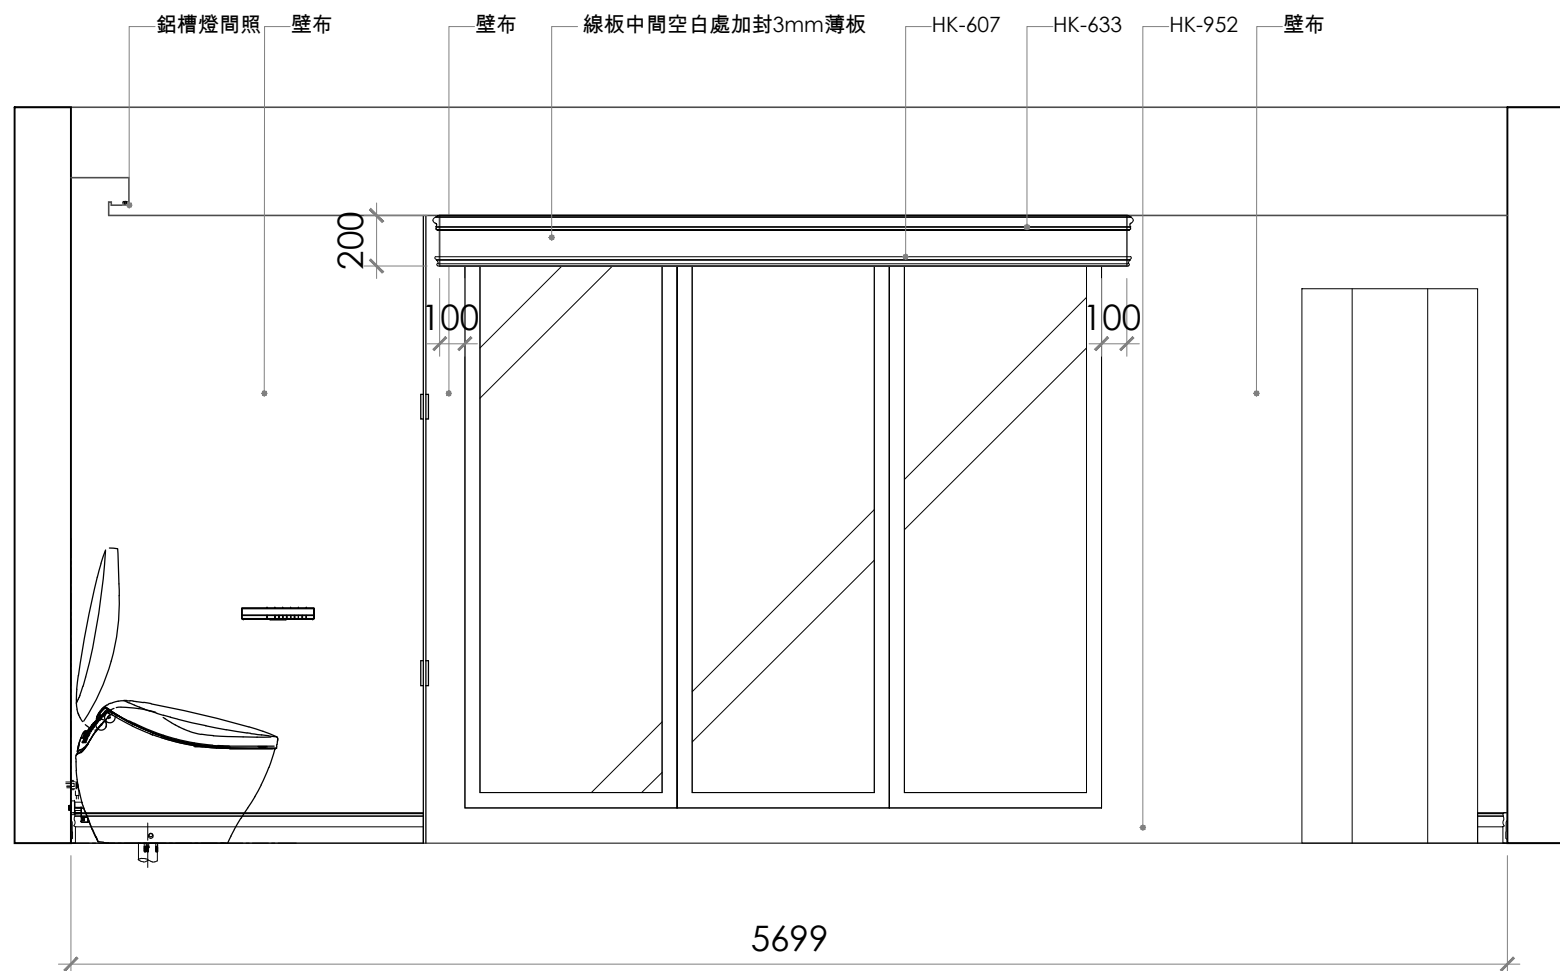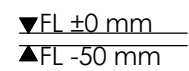

1
E-41

ELEVATION

Scale=1:30

Revision

APPROVAL/核准

設計者:

建築師:

業主:

葡註:

- 圖面標註尺寸僅供參考，施作均以現場放樣檢討。
- 圖面標註尺寸、材料及文字敘述因版本不同之差異，均以出圖圖章簽日期之最近為準。
- 電腦圖檔除由合約訂定外，均不得以任何方式外流。
- 圖面所示均為本公司所擁有之智慧財產，切勿以任何方式複製修改。



MULA DECO

A 3F, N.26, Ln.290, Guangfu S. Rd., Taipei.
T 886-2-2546-3258
F 886-2-2546-3257
E Guido@muladeco.com

Project / 案名

天母葉公館

Sheet Title / 圖名
2F

立面圖


Date / 日期	Scale / 比例
8/10/2026	1/30CM
Designer / 設計	Approval / 核准
MONICA LIN	ABC
Job No / 業務編號	Drawn By / 繪圖
00000	GUIDO

Dwg No.

Page No.

E-41

4

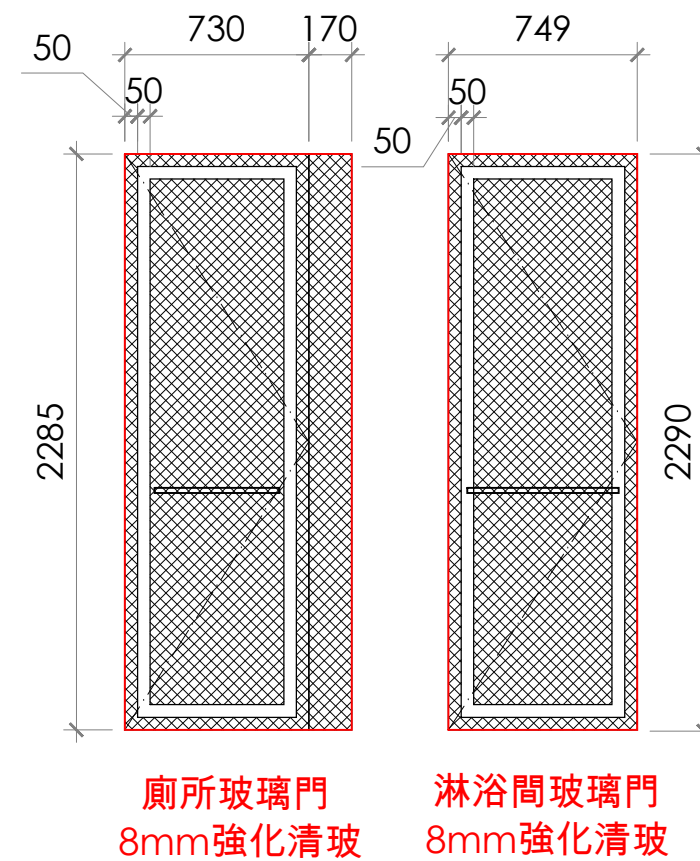[illegible]

APPROVAL/核准

設計者:	建築師:
業主:	

葡註:

- g. 圖面標註尺寸僅供參考，施作均以現場放樣檢討之。
- h. 圖面標註尺寸、材料及文字敘述因版本不同之差異，均以出圖章簽認日期之最近為準。
- i. 電腦圖檔除由合約訂定外，均不得以任何方式外流。
- j. 圖面所示均為本公司所擁有之智慧財產，切勿以任何方式複製修改。



MULA DECO

A 3F, N.26, Ln.290, Guangfu S. Rd., Taipei.
T 886-2-2546-3258
F 886-2-2546-3257
E Guido@muladeco.com



Project / 案名

天母葉公館

Sheet Title / 圖名
2F



立面圖

Date / 日期	Scale / 比例
8/10/2026	1/30CM
Designer / 設計	Approval / 核准
MONICA LIN	
Job No / 業務編號	Drawn By / 繪圖
00000	GUIDO
Dwg No.	Page No.
E-42	75

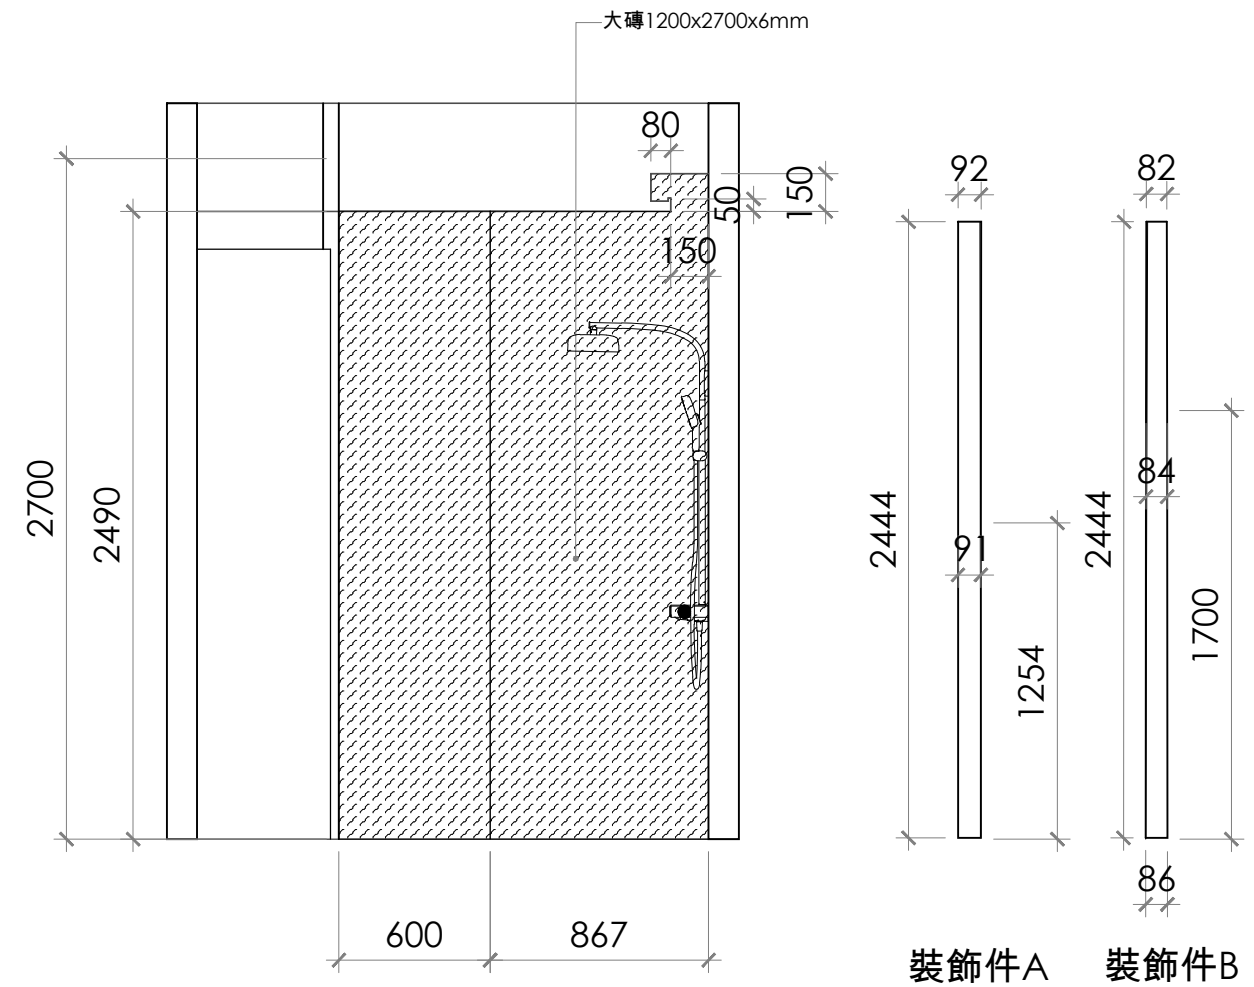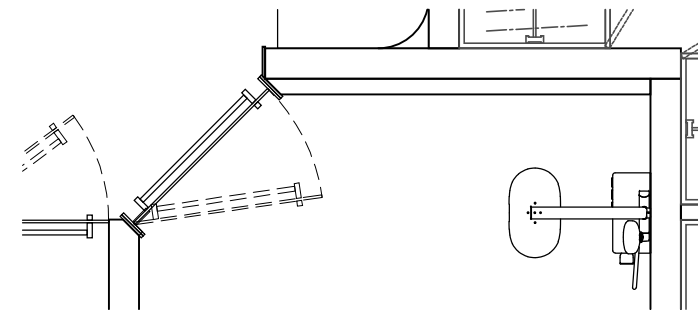


1 ELEVATION
E-43 Scale=1:30

Date / 日期	Scale / 比例
8/10/2026	1/30CM
Designer / 設計	Approval / 核准
MONICA LN	ABC
Job No / 業務編號	Drawn By / 繪圖
00000	GUIDO
Dwg No.	Page No.
E-43	76

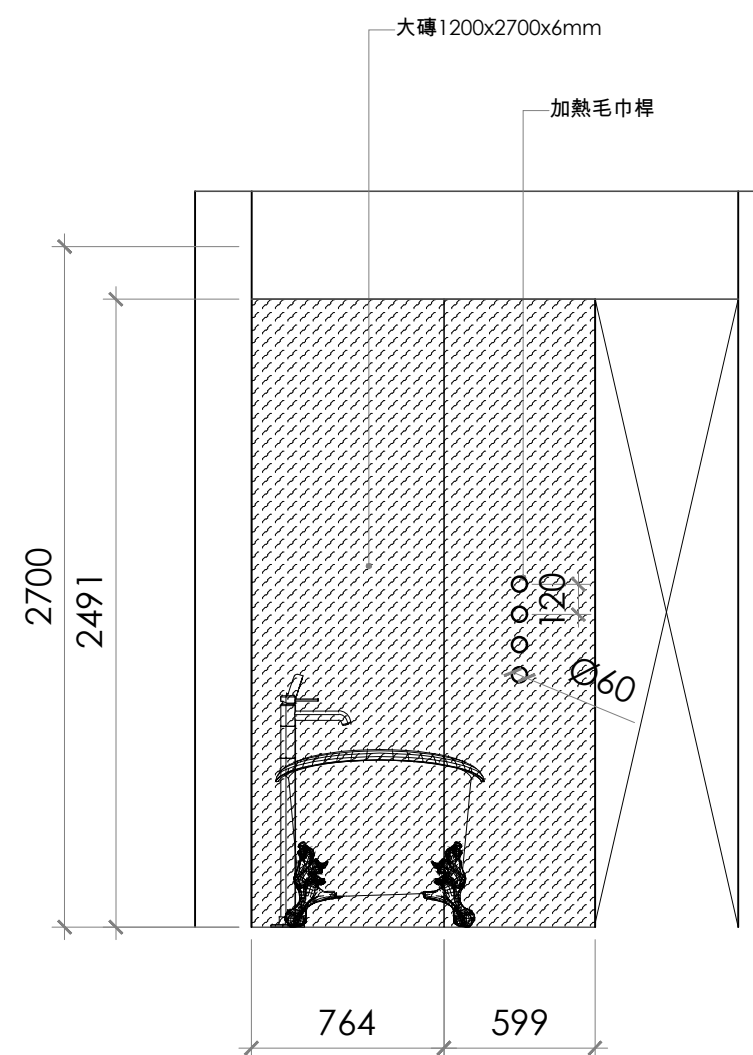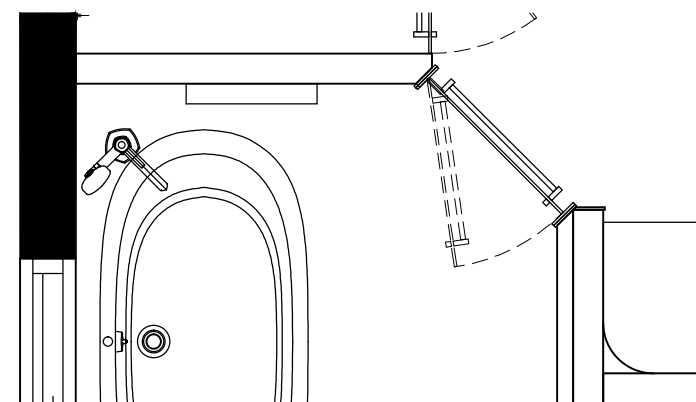

ELEVATION 1 E-44 Scale=1:30


Date / 日期	Scale / 比例
8/10/2026	1/30CM
Designer / 設計	Approval / 核准
MONICA LN	ABC
Job No / 業務編號	Drawn By / 繪圖
00000	GUIDO
Dwg No.	Page No.
E-44	77

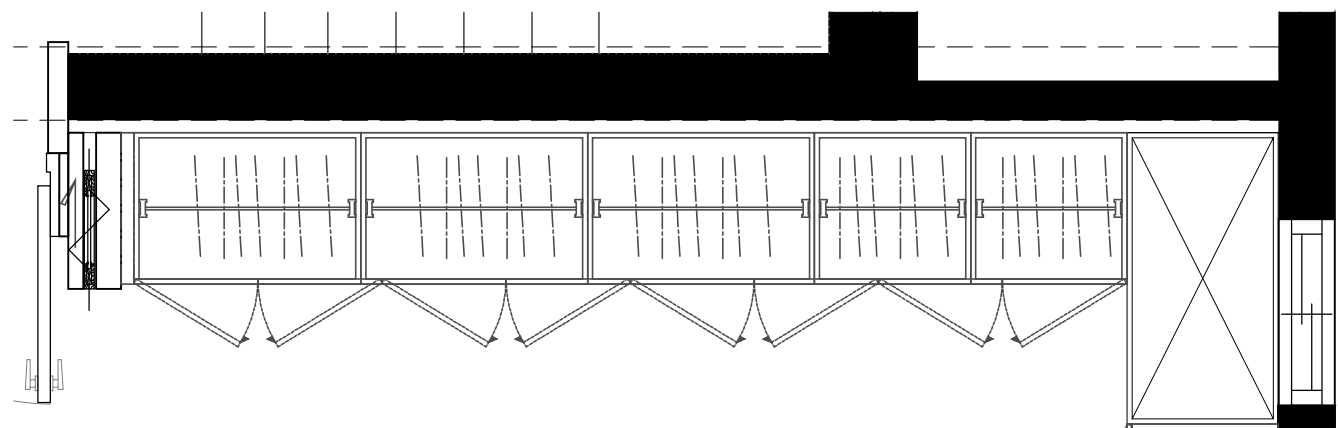

▲CH 2920mm

▲CH 2420mm

▼FL ±0 mm
▲FL -50 mm

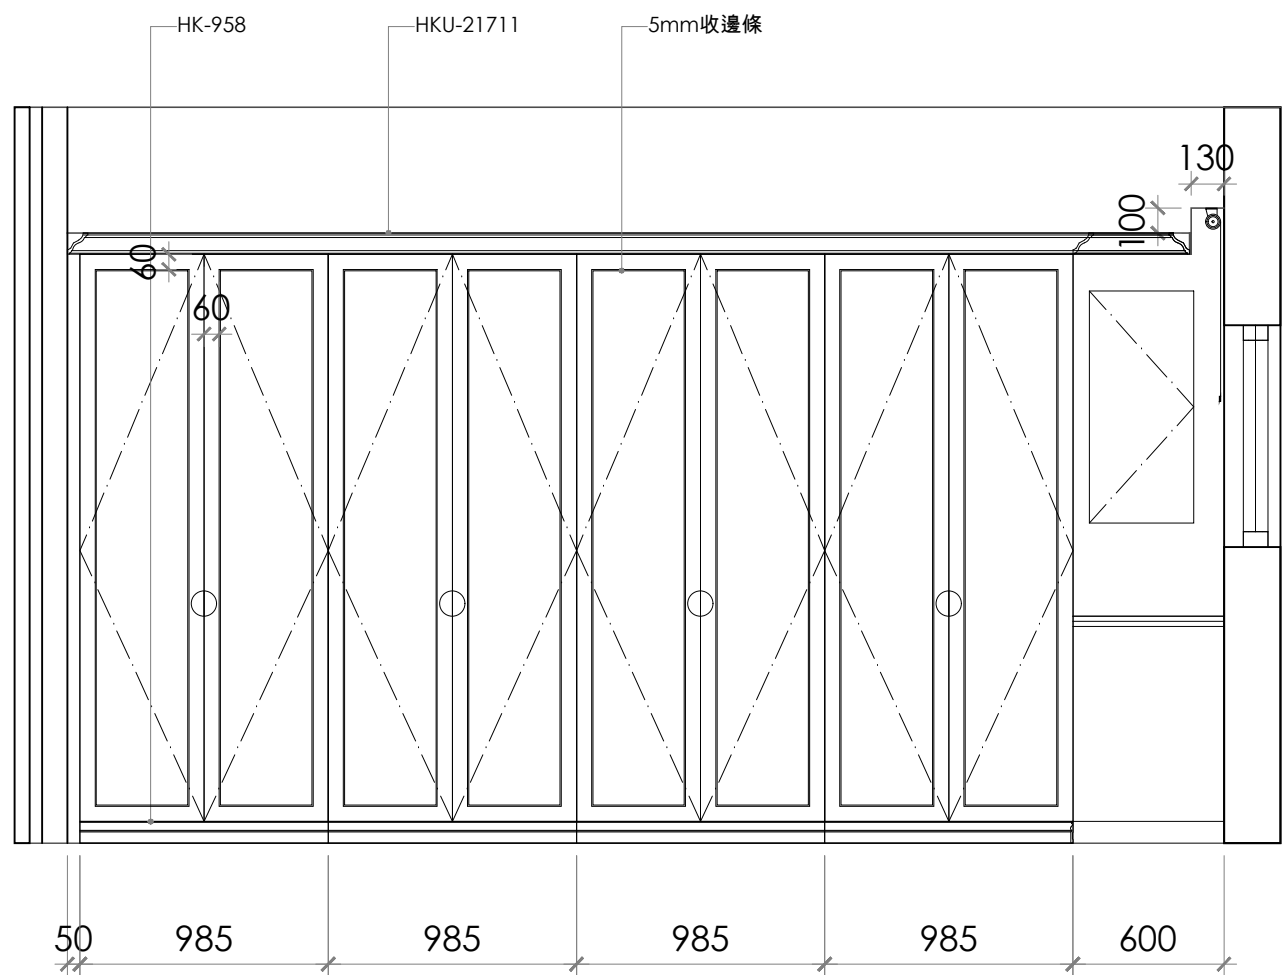

1
E-45

ELEVATION

Scale=1:30

Revision

APPROVAL/核准

設計者:	建築師:
業主:	

備註:

- 圖面標註尺寸僅供參考，施作均以現場放樣檢討之。
- 圖面標註尺寸、材料及文字敘述因版本不同之差異，均以出圖章簽認日期之最近為準。
- 電腦圖檔除由合約訂定外，均不得以任何方式外流。
- 圖面所示均為本公司所擁有之智慧財產，切勿以任何方式複製修改。



MULA DECO

▲ 3F, N.26, Ln.290, Guangfu S. Rd., Taipei.
☎ 886-2-2546-3258
☎ 886-2-2546-3257
✉ Guido@muladeco.com

Project / 案名

天母葉公館



Sheet Title / 圖名
2F

立面圖

Date / 日期	Scale / 比例
8/10/2026	1/30CM
Designer / 設計	Approval / 核准
MONICA LIN	
Job No / 業務編號	Drawn By / 繪圖
00000	GUIDO
Dwg No.	Page No.

E-45

78

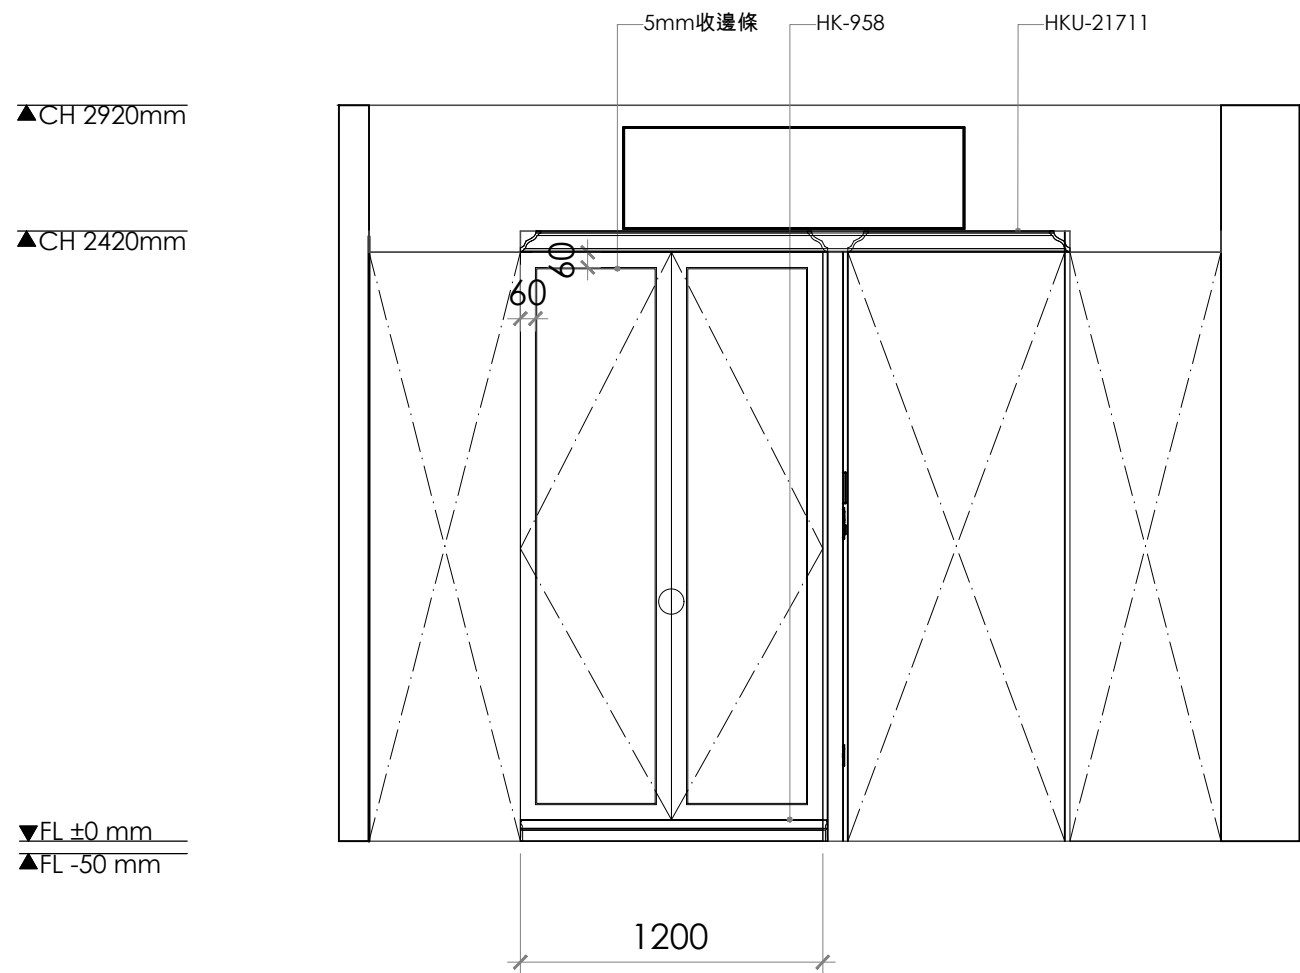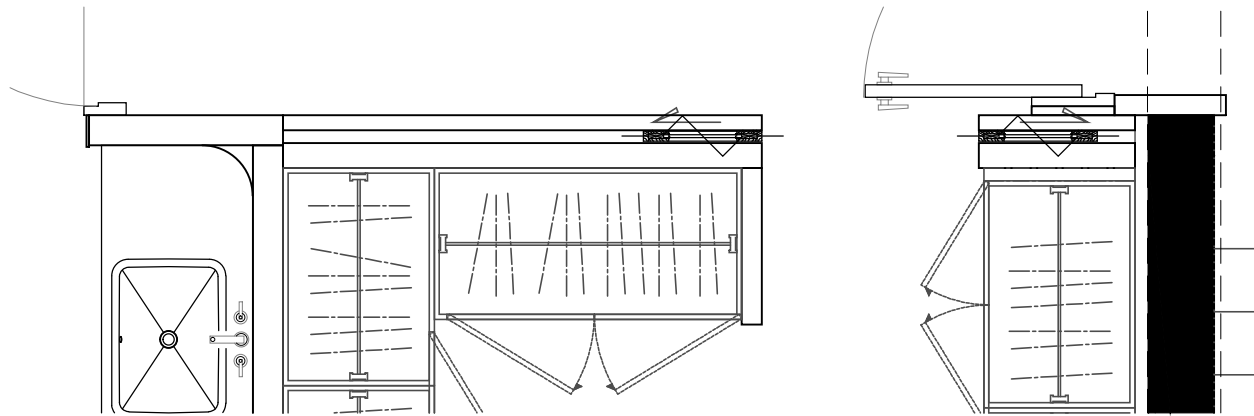

1
E-47

ELEVATION

Scale=1:30

Revision

APPROVAL/核准

設計者:	建築師:
業主:	

備註:

- 圖面標註尺寸僅供參考，施作均以現場放樣檢討之。
- 圖面標註尺寸、材料及文字敘述因版本不同之差異，均以出圖章簽認日期之最近為準。
- 電腦圖檔除由合約訂定外，均不得以任何方式外流。
- 圖面所示均為本公司所擁有之智慧財產，切勿以任何方式複製修改。



MULA DECO

▲ 3F, N.26, Ln.290, Guangfu S. Rd., Taipei.
☎ 886-2-2546-3258
✉ 886-2-2546-3257
E Guido@muladeco.com

Project / 案名

天母葉公館



Sheet Title / 圖名
2F

立面圖

Date / 日期	Scale / 比例
8/10/2026	1/30CM
Designer / 設計	Approval / 核准
MONICA LIN	
Job No / 業務編號	Drawn By / 繪圖
00000	GUIDO
Dwg No.	Page No.

E-47


80

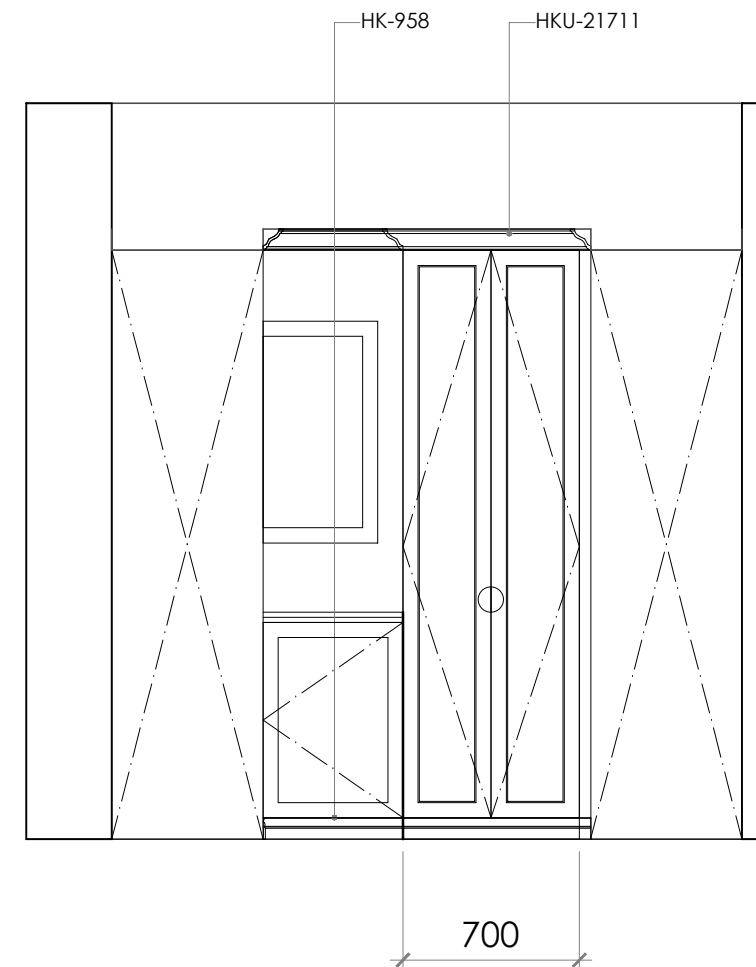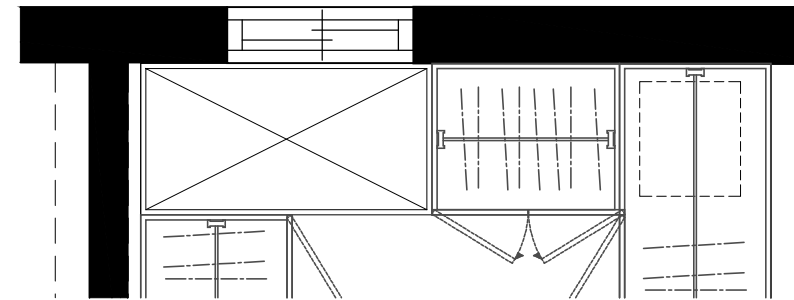

▼FL ±0 mm
▲FL -50 mm


Scale=1:30

Date / 日期	Scale / 比例
8/10/2026	1/30CM
Designer / 設計	Approval / 核准
MONICA LIN	
Job No / 業務編號	Drawn By / 繪圖
00000	GUIDO
Dwg No.	Page No.
E-48	81

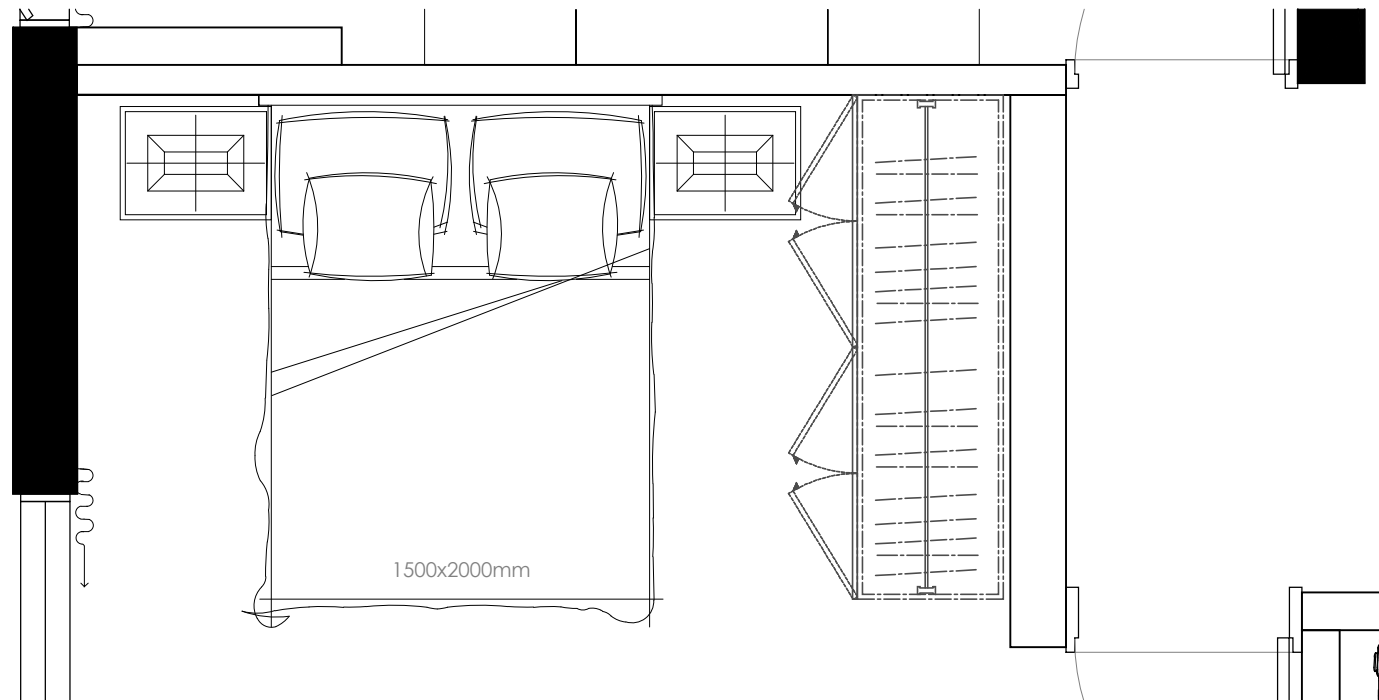

▲CH 2902mm
▲CH 2642mm
▲CH 2465mm

▼FL ±0 mm
▲FL -50 mm

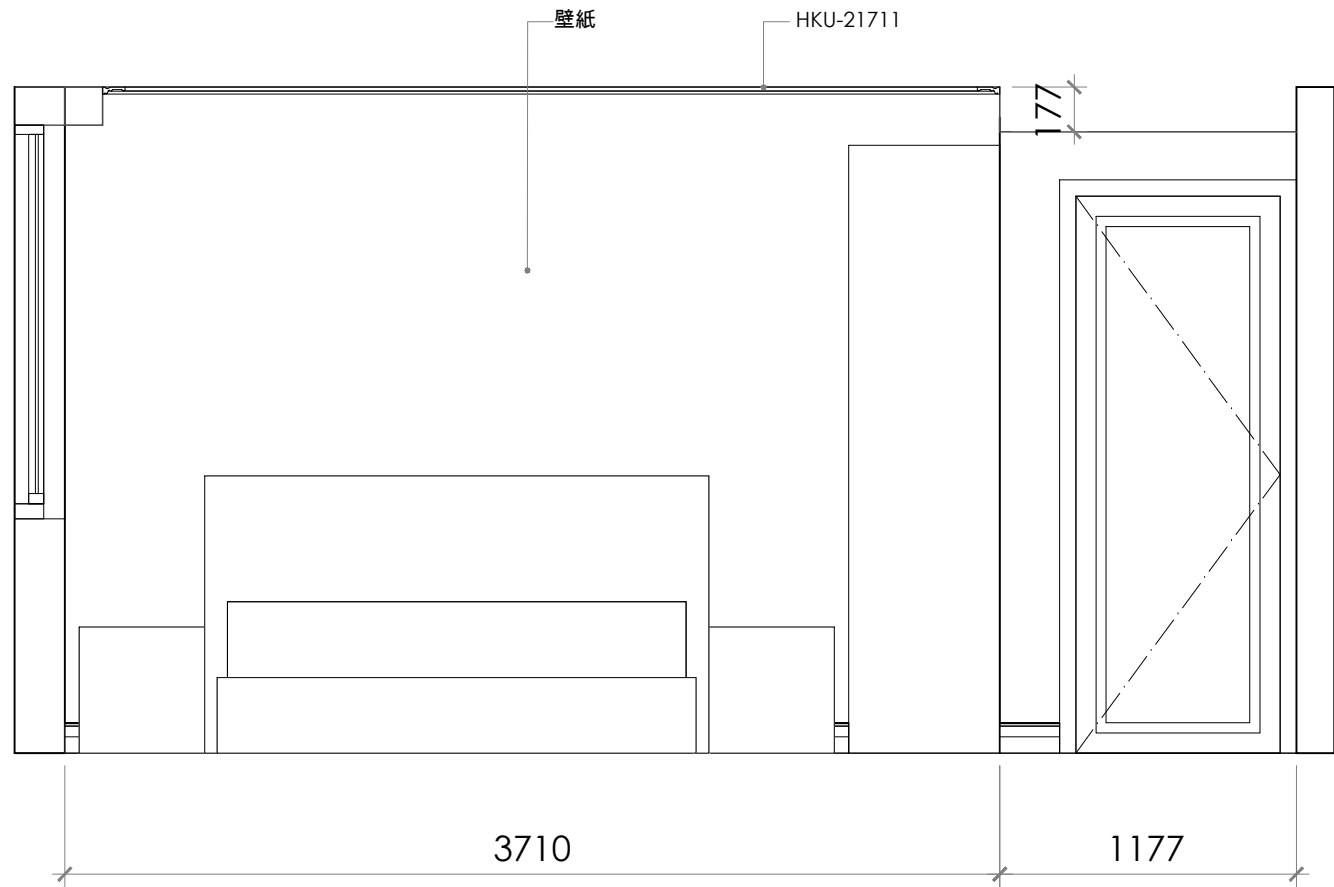

1
E-49

ELEVATION

Scale=1:30

Revision

APPROVAL/核准

設計者:	建築師:
業主:	

備註:

- a. 圖面標註尺寸僅供參考，施作均以現場放樣檢討之。
- b. 圖面標註尺寸、材料及文字敘述因版本不同之差異，均以出圖章簽認日期之最近為準。
- c. 電腦圖檔除由合約訂定外，均不得以任何方式外流。
- d. 圖面所示均為本公司所擁有之智慧財產，切勿以任何方式複製修改。



MULA DECO

▲ 3F, N.26, Ln.290, Guangfu S. Rd., Taipei.
☎ 886-2-2546-3258
☎ 886-2-2546-3257
✉ Guido@muladeco.com

Project / 案名

天母葉公館



Sheet Title / 圖名
2F

立面圖

Date / 日期	Scale / 比例
8/10/2026	1/30CM
Designer / 設計	Approval / 核准
MONICA LIN	
Job No / 業務編號	Drawn By / 繪圖
00000	GUIDO
Dwg No.	Page No.

E-49



82

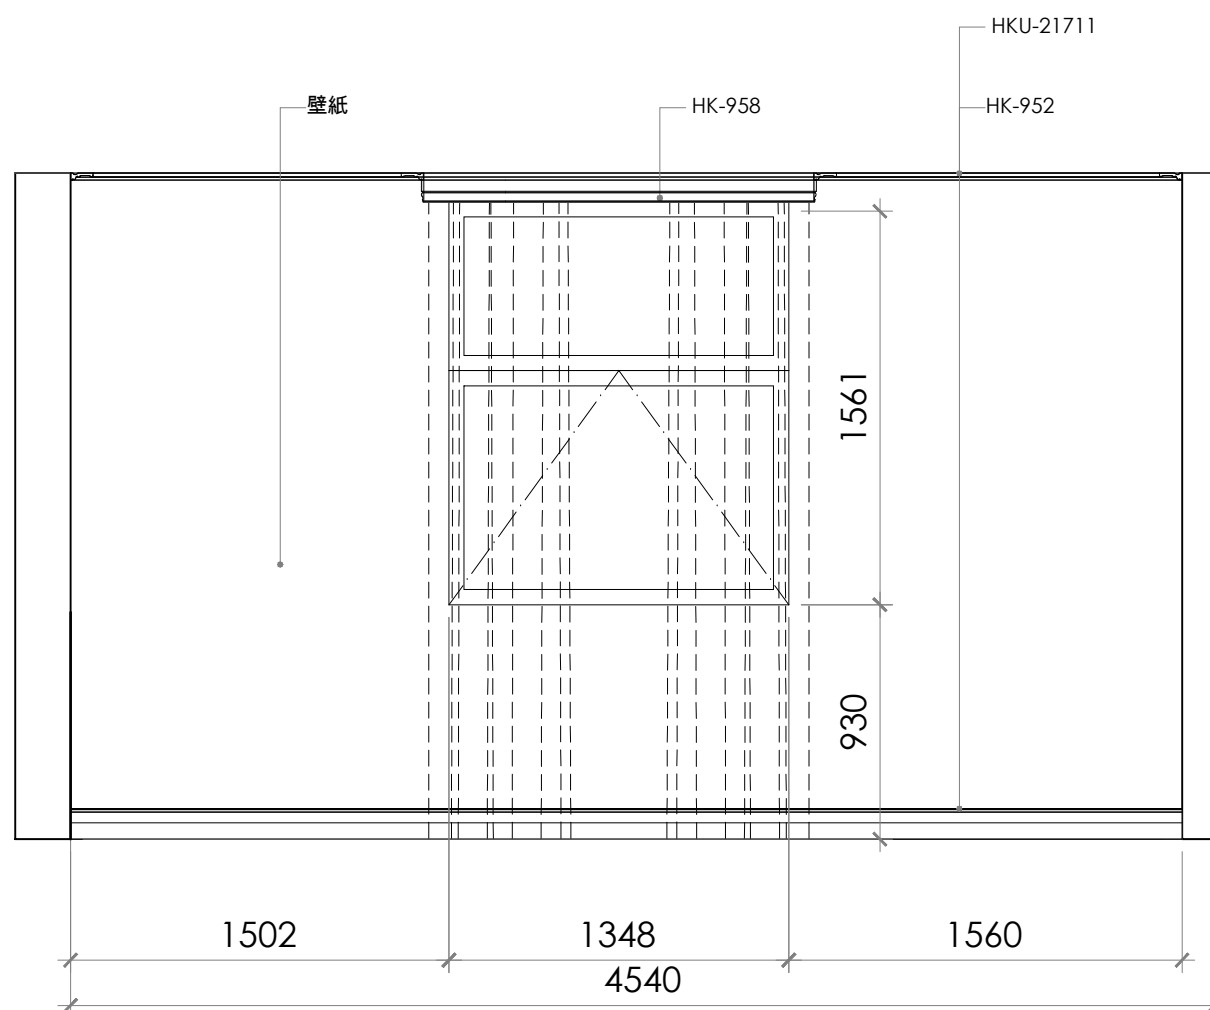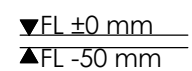

1
E-50

ELEVATION

Scale=1:30

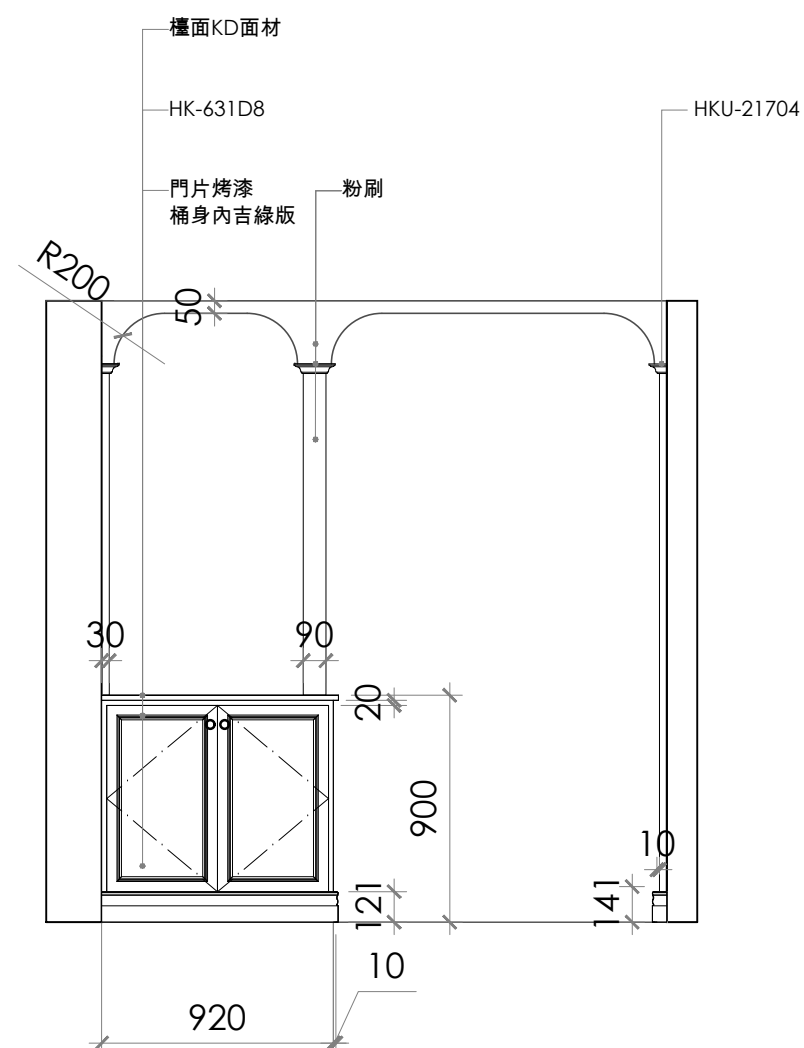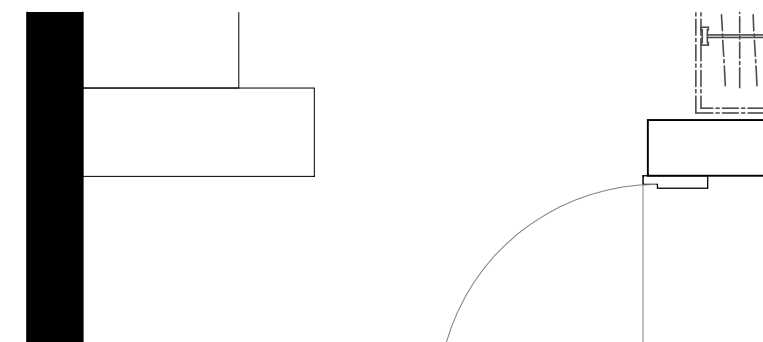

2 ELEVATION
E-50 Scale=1:30

[illegible]

備註:

- 圖面標註尺寸僅供參考，施作均以現場放樣檢封之。
- 圖面標註尺寸、材料及文字敘述因版本不同之差異，均以出圖章簽認日期之最近為準。
- 電腦圖檔除由合約訂定外，均不得以任何方式外流。
- 圖面所示均為本公司所擁有之智慧財產，切勿以任何方式複製修改。



MULA DECO

A 3F, N.26, Ln.290, Guangfu S. Rd., Taipei.
T 886-2-2546-3258
F 886-2-2546-3257
E Guido@muladeco.com


Project / 案名

天母葉公館

Sheet Title / 圖名
2F



立面圖

Date / 日期	Scale / 比例
8/10/2026	1/30CM
Designer / 設計	Approval / 核准
MONICA LIN	
Job No / 業務編號	Drawn By / 繪圖
00000	GUIDO
Dwg No.	Page No.
E-50	83

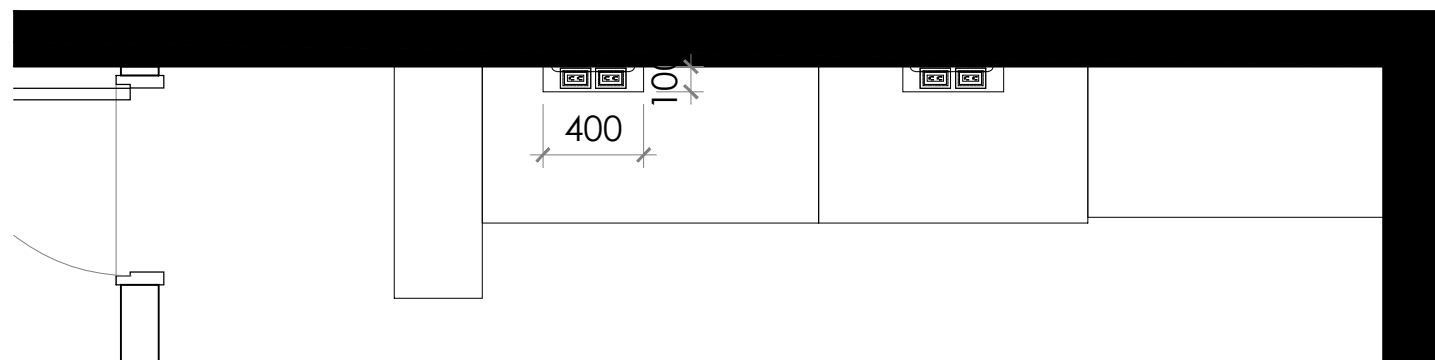

▲CH 2902mm
▲CH 2642mm
▲CH 2465mm

▼FL ±0 mm
▲FL -50 mm

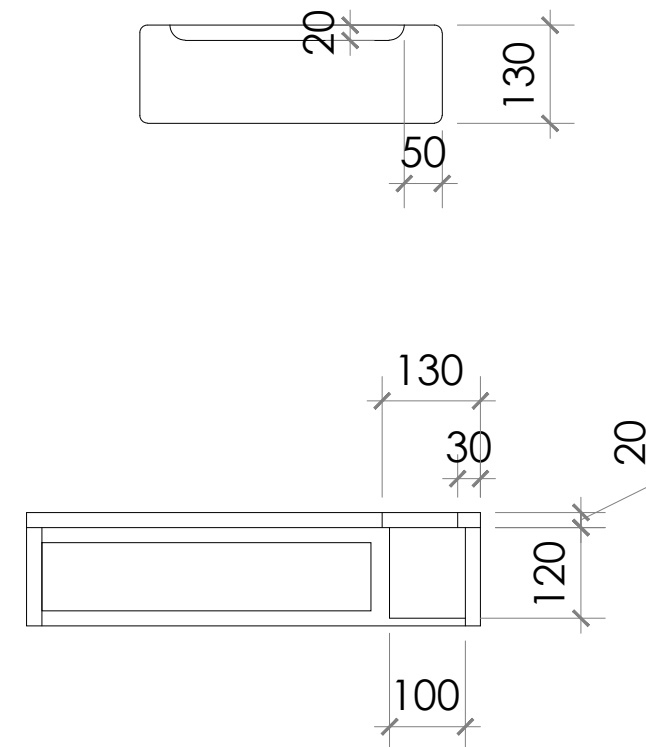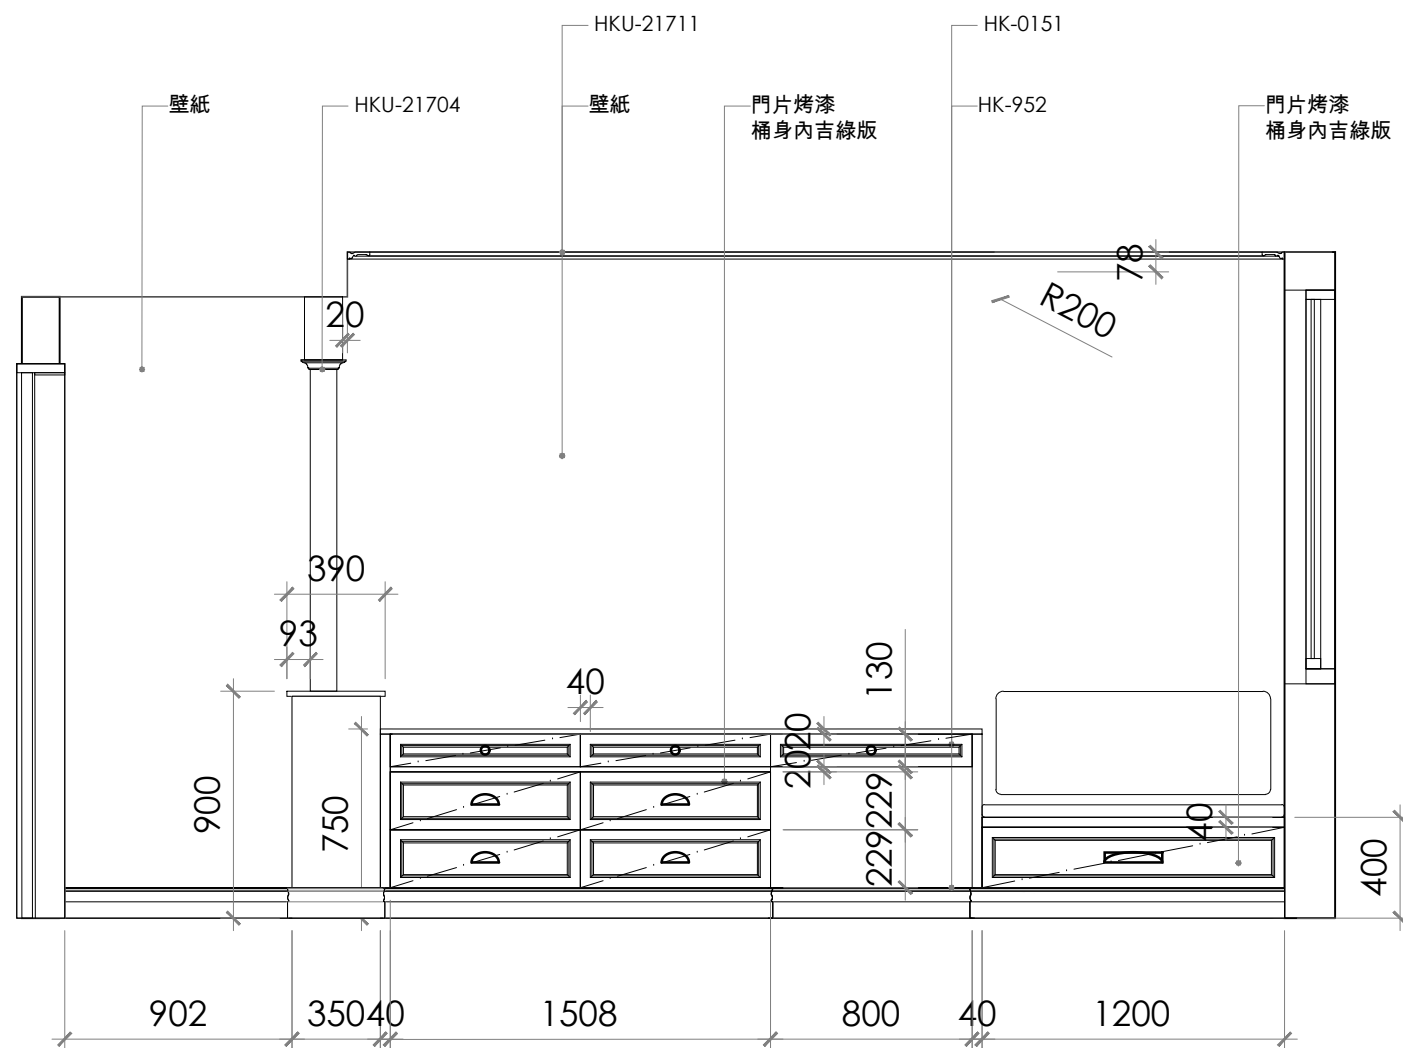

1 ELEVATION
E-51
Scale=1:30

Revision	
APPROVAL/核准	
設計者:	建築師:
業主:	



備註:
a. 圖面標註尺寸僅供參考，施作均以現場放樣檢討之。
b. 圖面標註尺寸、材料及文字敘述因版本不同之差異，均以出圖章簽認日期之最近為準。
c. 電腦圖檔除由合約訂定外，均不得以任何方式外流。
d. 圖面所示均為本公司所擁有之智慧財產，切勿以任何方式複製修改。



MULA DECO

▲ 3F, N.26, Ln.290, Guangfu S. Rd., Taipei.
☎ 886-2-2546-3258
☎ 886-2-2546-3257
✉ Guido@muladeco.com

Project / 案名	
天母葉公館	
Sheet Title / 圖名	
2F 立面圖	
Date / 日期	Scale / 比例
8/10/2026	1/30CM
Designer / 設計	Approval / 核准
MONICA LIN	
Job No / 業務編號	Drawn By / 繪圖
00000	GUIDO
Dwg No.	Page No.
E-51	84

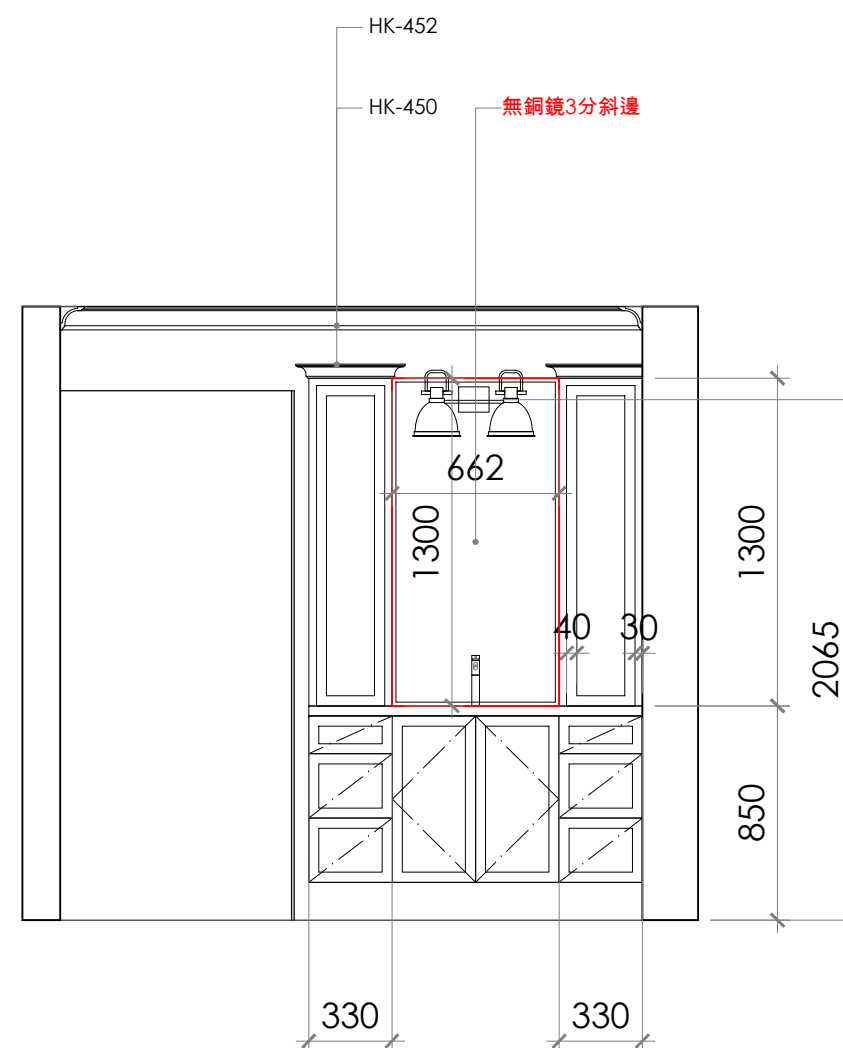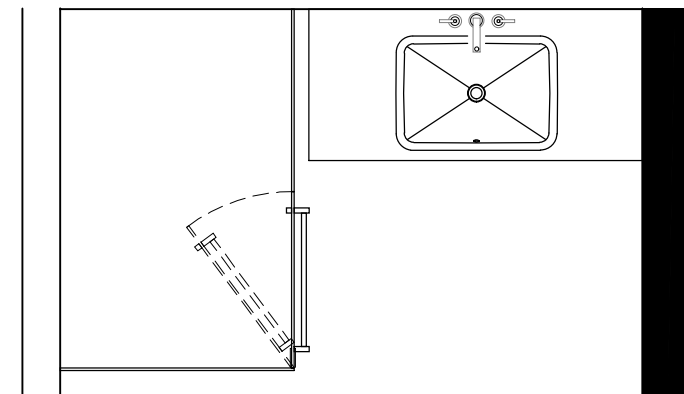

2 ELEVATION
E-52

Scale=1:30


Date / 日期	Scale / 比例
8/10/2026	1/30CM
Designer / 設計	Approval / 核准
MONICA LIN	
Job No / 案卷編號	Drawn By / 繪圖
00000	GUIDO
Dwg No.	Page No.
E-52	85



▲CH 2920mm

▲CH 2440mm

▼FL ±0 mm
▲FL -50 mm

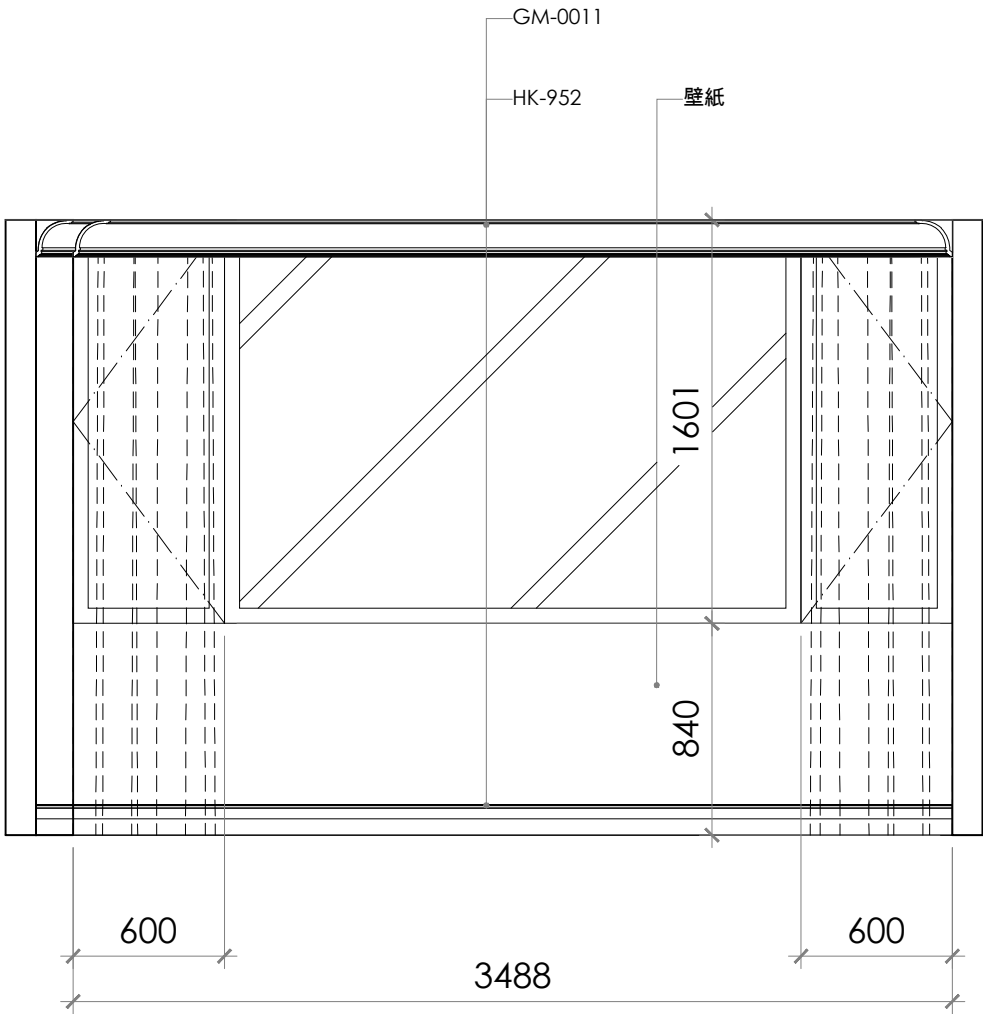

1
E-54

ELEVATION

Scale=1:30

Revision

APPROVAL/核准

設計者:	建築師:
業主:	

備註:

- a. 圖面標註尺寸僅供參考，施作均以現場放樣檢討之。
- b. 圖面標註尺寸、材料及文字敘述因版本不同之差異，均以出圖章簽認日期之最近為準。
- c. 電腦圖檔除由合約訂定外，均不得以任何方式外流。
- d. 圖面所示均為本公司所擁有之智慧財產，切勿以任何方式複製修改。



MULA DECO

▲ 3F, N.26, Ln.290, Guangfu S. Rd., Taipei.
☎ 886-2-2546-3258
☎ 886-2-2546-3257
✉ Guido@muladeco.com

Project / 案名

天母葉公館


Sheet Title / 圖名
2F

立面圖

Date / 日期	Scale / 比例
8/10/2026	1/30CM
Designer / 設計	Approval / 核准
MONICA LIN	
Job No / 業務編號	Drawn By / 繪圖
00000	GUIDO
Dwg No.	Page No.

E-54


87

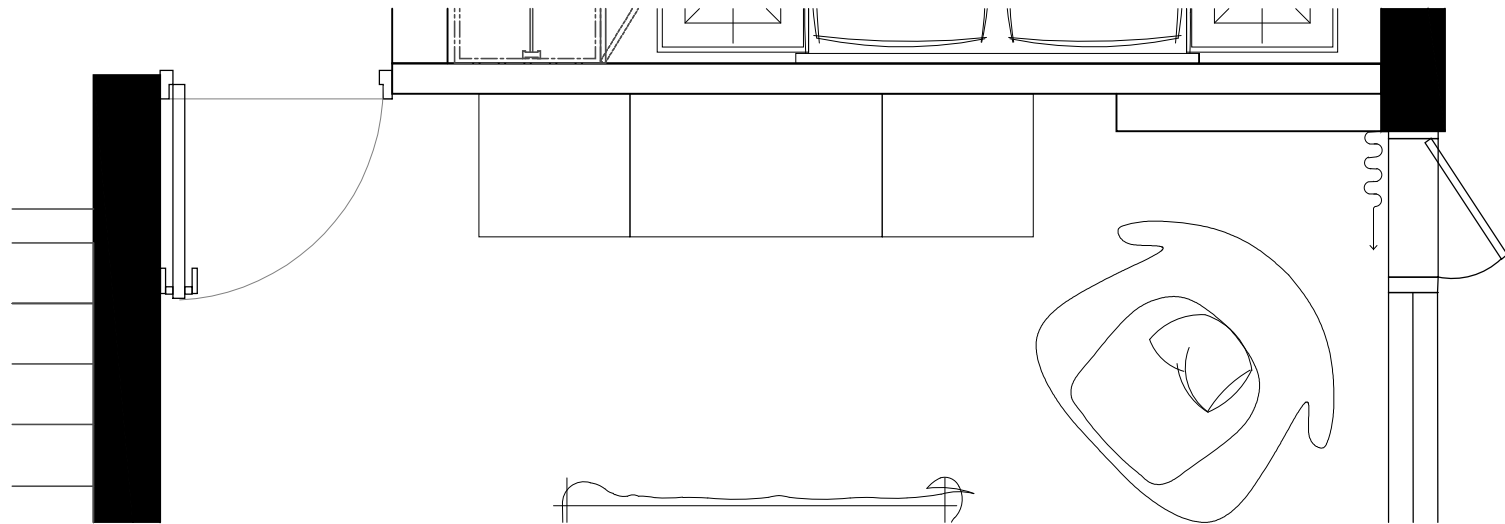

▲CH 2920mm

▲CH 2440mm

▼FL ±0 mm
▲FL -50 mm

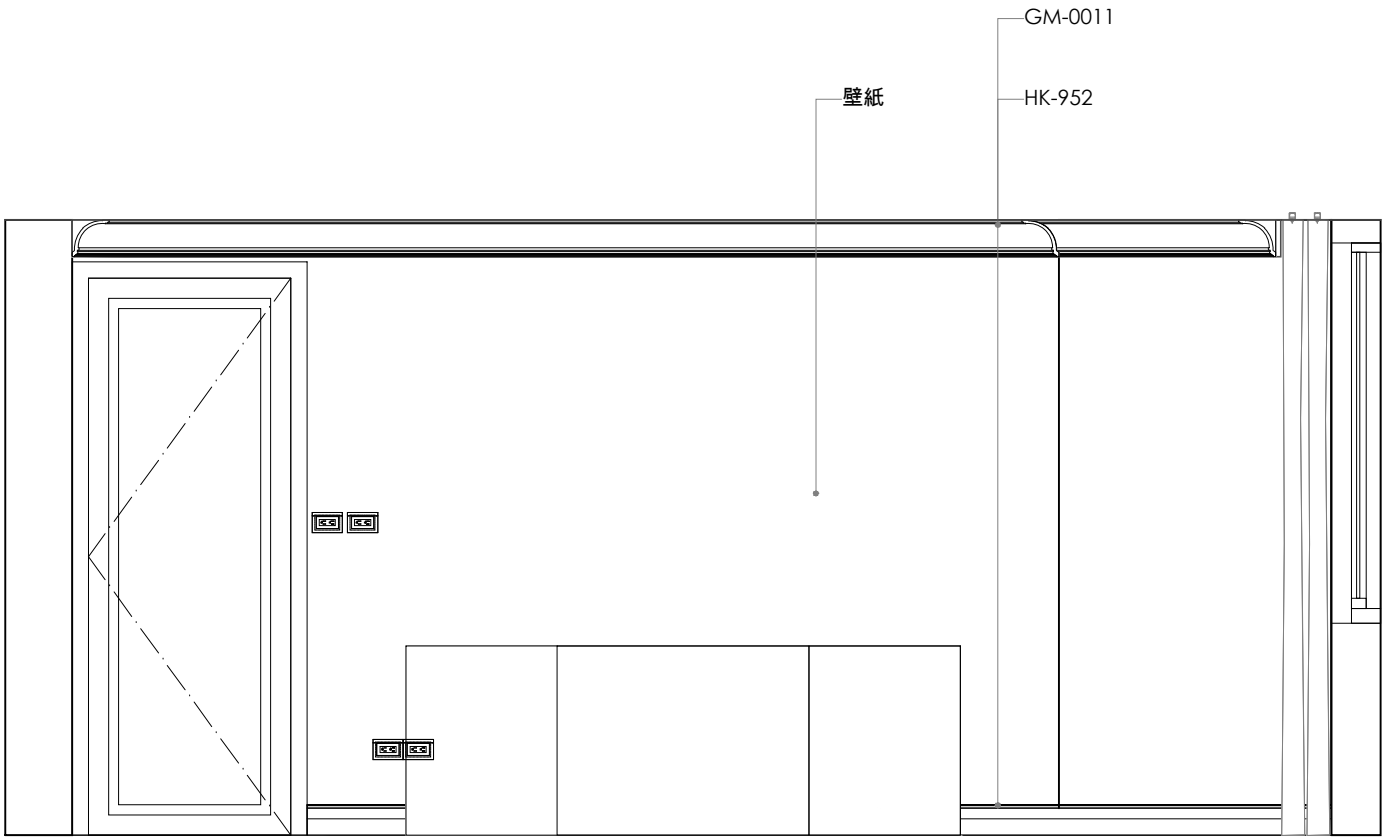

1
E-55

ELEVATION

Scale=1:30

Revision

APPROVAL/核准

設計者:	建築師:
業主:	

備註:

- a. 圖面標註尺寸僅供參考，施作均以現場放樣檢討之。
- b. 圖面標註尺寸、材料及文字敘述因版本不同之差異，均以出圖章簽認日期之最近為準。
- c. 電腦圖檔除由合約訂定外，均不得以任何方式外流。
- d. 圖面所示均為本公司所擁有之智慧財產，切勿以任何方式複製修改。



MULA DECO

▲ 3F, N.26, Ln.290, Guangfu S. Rd., Taipei.
☎ 886-2-2546-3258
✉ 886-2-2546-3257
E Guido@muladeco.com

Project / 案名

天母葉公館


Sheet Title / 圖名
2F

立面圖

Date / 日期	Scale / 比例
8/10/2026	1/30CM
Designer / 設計	Approval / 核准
MONICA LIN	
Job No / 業務編號	Drawn By / 繪圖
00000	GUIDO
Dwg No.	Page No.

E-55


89

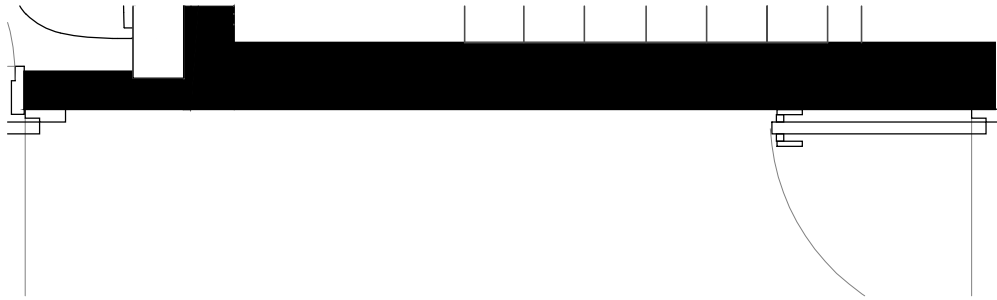

▲CH 2920mm

▲CH 2440mm

▼FL ±0 mm
▲FL -50 mm

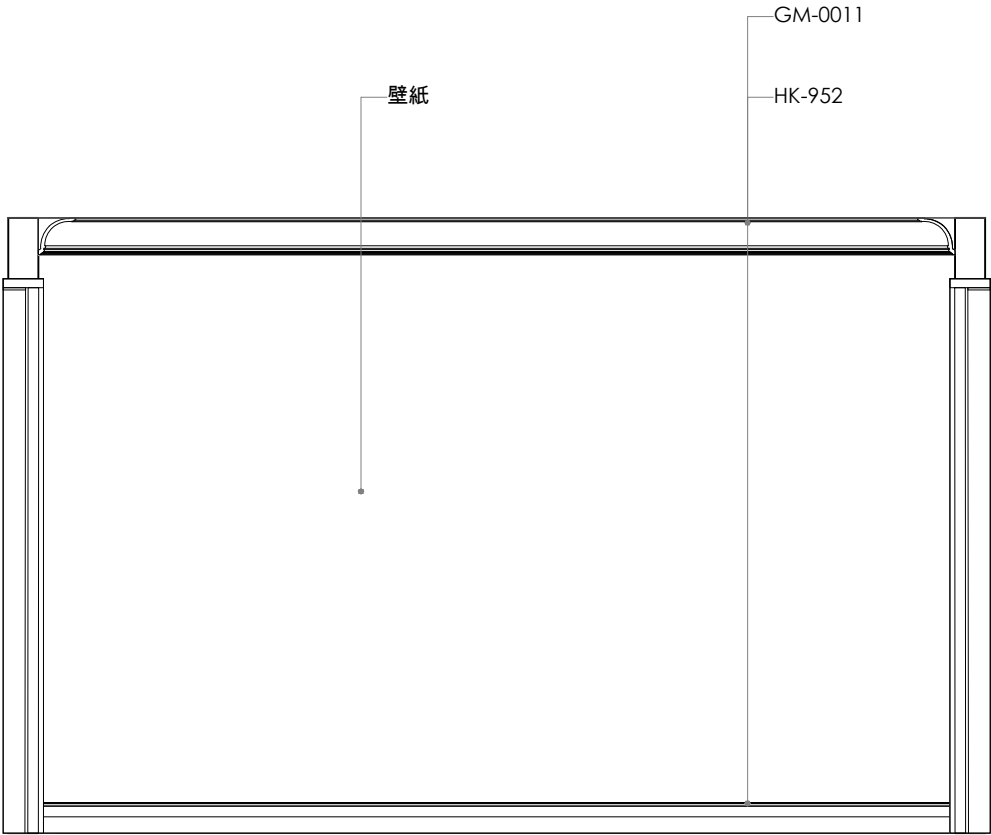

1
E-56

ELEVATION

Scale=1:30

Revision

APPROVAL/核准

設計者:	建築師:
業主:	

備註:

- a. 圖面標註尺寸僅供參考，施作均以現場放樣檢討之。
- b. 圖面標註尺寸、材料及文字敘述因版本不同之差異，均以出圖章簽認日期之最近為準。
- c. 電腦圖檔除由合約訂定外，均不得以任何方式外流。
- d. 圖面所示均為本公司所擁有之智慧財產，切勿以任何方式複製修改。



MULA DECO

▲ 3F, N.26, Ln.290, Guangfu S. Rd., Taipei.
☎ 886-2-2546-3258
✉ 886-2-2546-3257
E Guido@muladeco.com

Project / 案名

天母葉公館



Sheet Title / 圖名
2F

立面圖

Date / 日期	Scale / 比例
8/10/2026	1/30CM
Designer / 設計	Approval / 核准
MONICA LIN	
Job No / 業務編號	Drawn By / 繪圖
00000	GUIDO
Dwg No.	Page No.

E-56

90

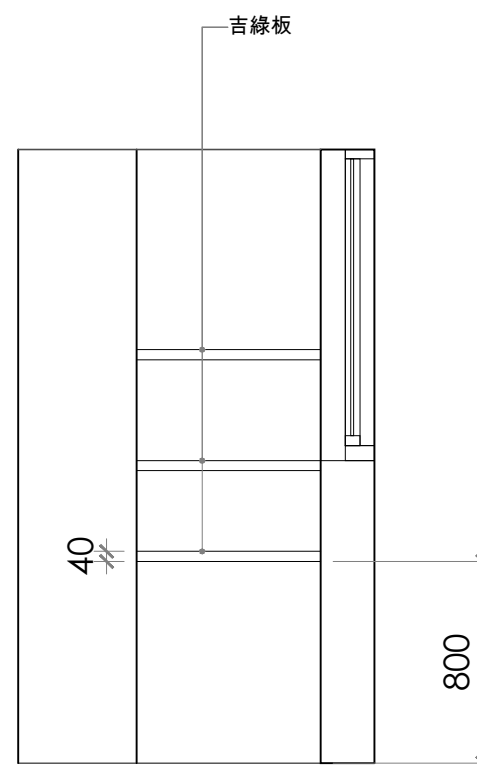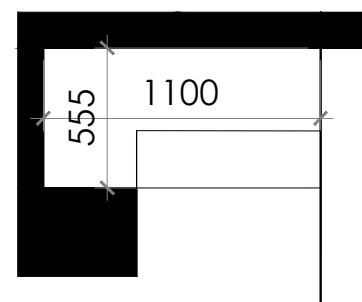

2 ELEVATION
E-57 Scale=1:30

Revision

APPROVAL/核准

設計者:	建築師:
業主:	

備註:

- a. 圖面標註尺寸僅供參考，施作均以現場放樣檢討之。
- b. 圖面標註尺寸、材料及文字敘述因版本不同之差異，均以圖章簽認日期之最近為準。
- c. 電腦圖檔除由合約訂定外，均不得以任何方式外流。
- d. 圖面所示均為本公司所擁有之智慧財產，切勿以任何方式複製修改。



MULA DECO

A 3F, N.26, Ln.290, Guangfu S. Rd., Taipei.
T 886-2-2546-3258
F 886-2-2546-3257
E Guido@muladeco.com


Project / 案名

天母葉公館

Sheet Title / 圖名
2F

立面圖

Date / 日期	Scale / 比例
8/10/2026	1/30CM
Designer / 設計	Approval / 核准
MONICA LIN	
Job No / 案卷編號	Drawn By / 繪圖
00000	GUIDO
Dwg No.	Page No.
E-57	91

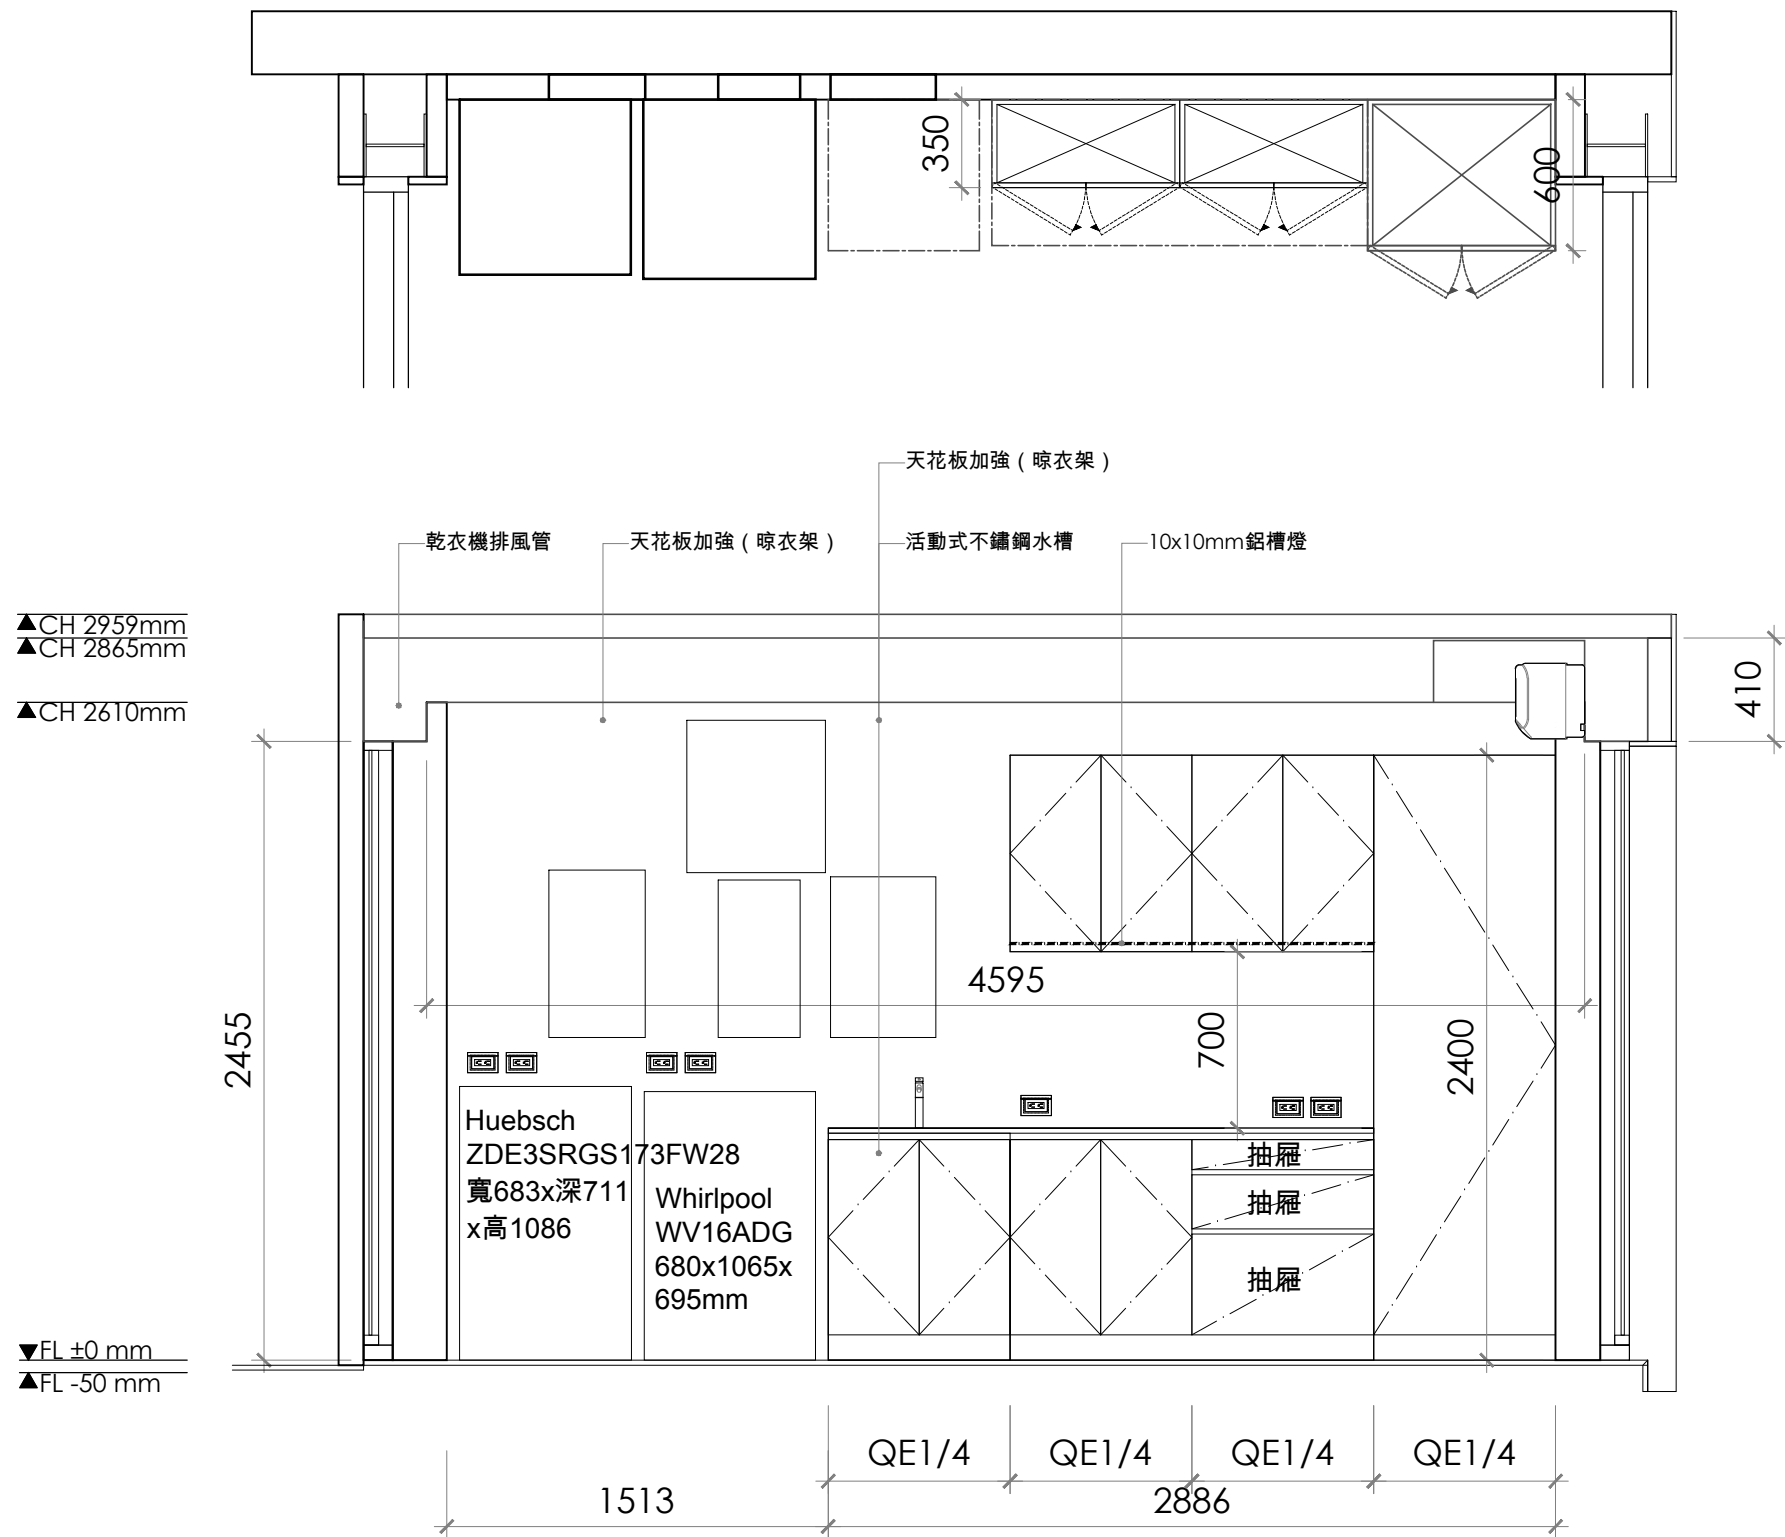

Revision

APPROVAL/核准

設計者:	建築師:
業主:	

備註:

- 圖面標註尺寸僅供參考，施作均以現場放樣檢討之。
- 圖面標註尺寸、材料及文字敘述因版本不同之差異，均以出圖章簽認日期之最近為準。
- 電腦圖檔除由合約訂定外，均不得以任何方式外流。
- 圖面所示均為本公司所擁有之智慧財產，切勿以任何方式複製修改。



MULA DECO

▲ 3F, N.26, Ln.290, Guangfu S. Rd., Taipei.
☎ 886-2-2546-3258
☎ 886-2-2546-3257
✉ Guido@muladeco.com

Project / 案名

天母葉公館



Sheet Title / 圖名
1F

立面圖

Date / 日期	Scale / 比例
8/10/2026	1/30CM
Designer / 設計	Approval / 核准
MONICA LIN	
Job No / 業務編號	Drawn By / 繪圖
00000	GUIDO
Dwg No.	Page No.


E-58

92

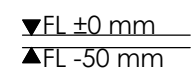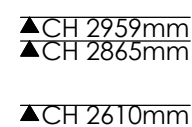

Scale=1:30

93

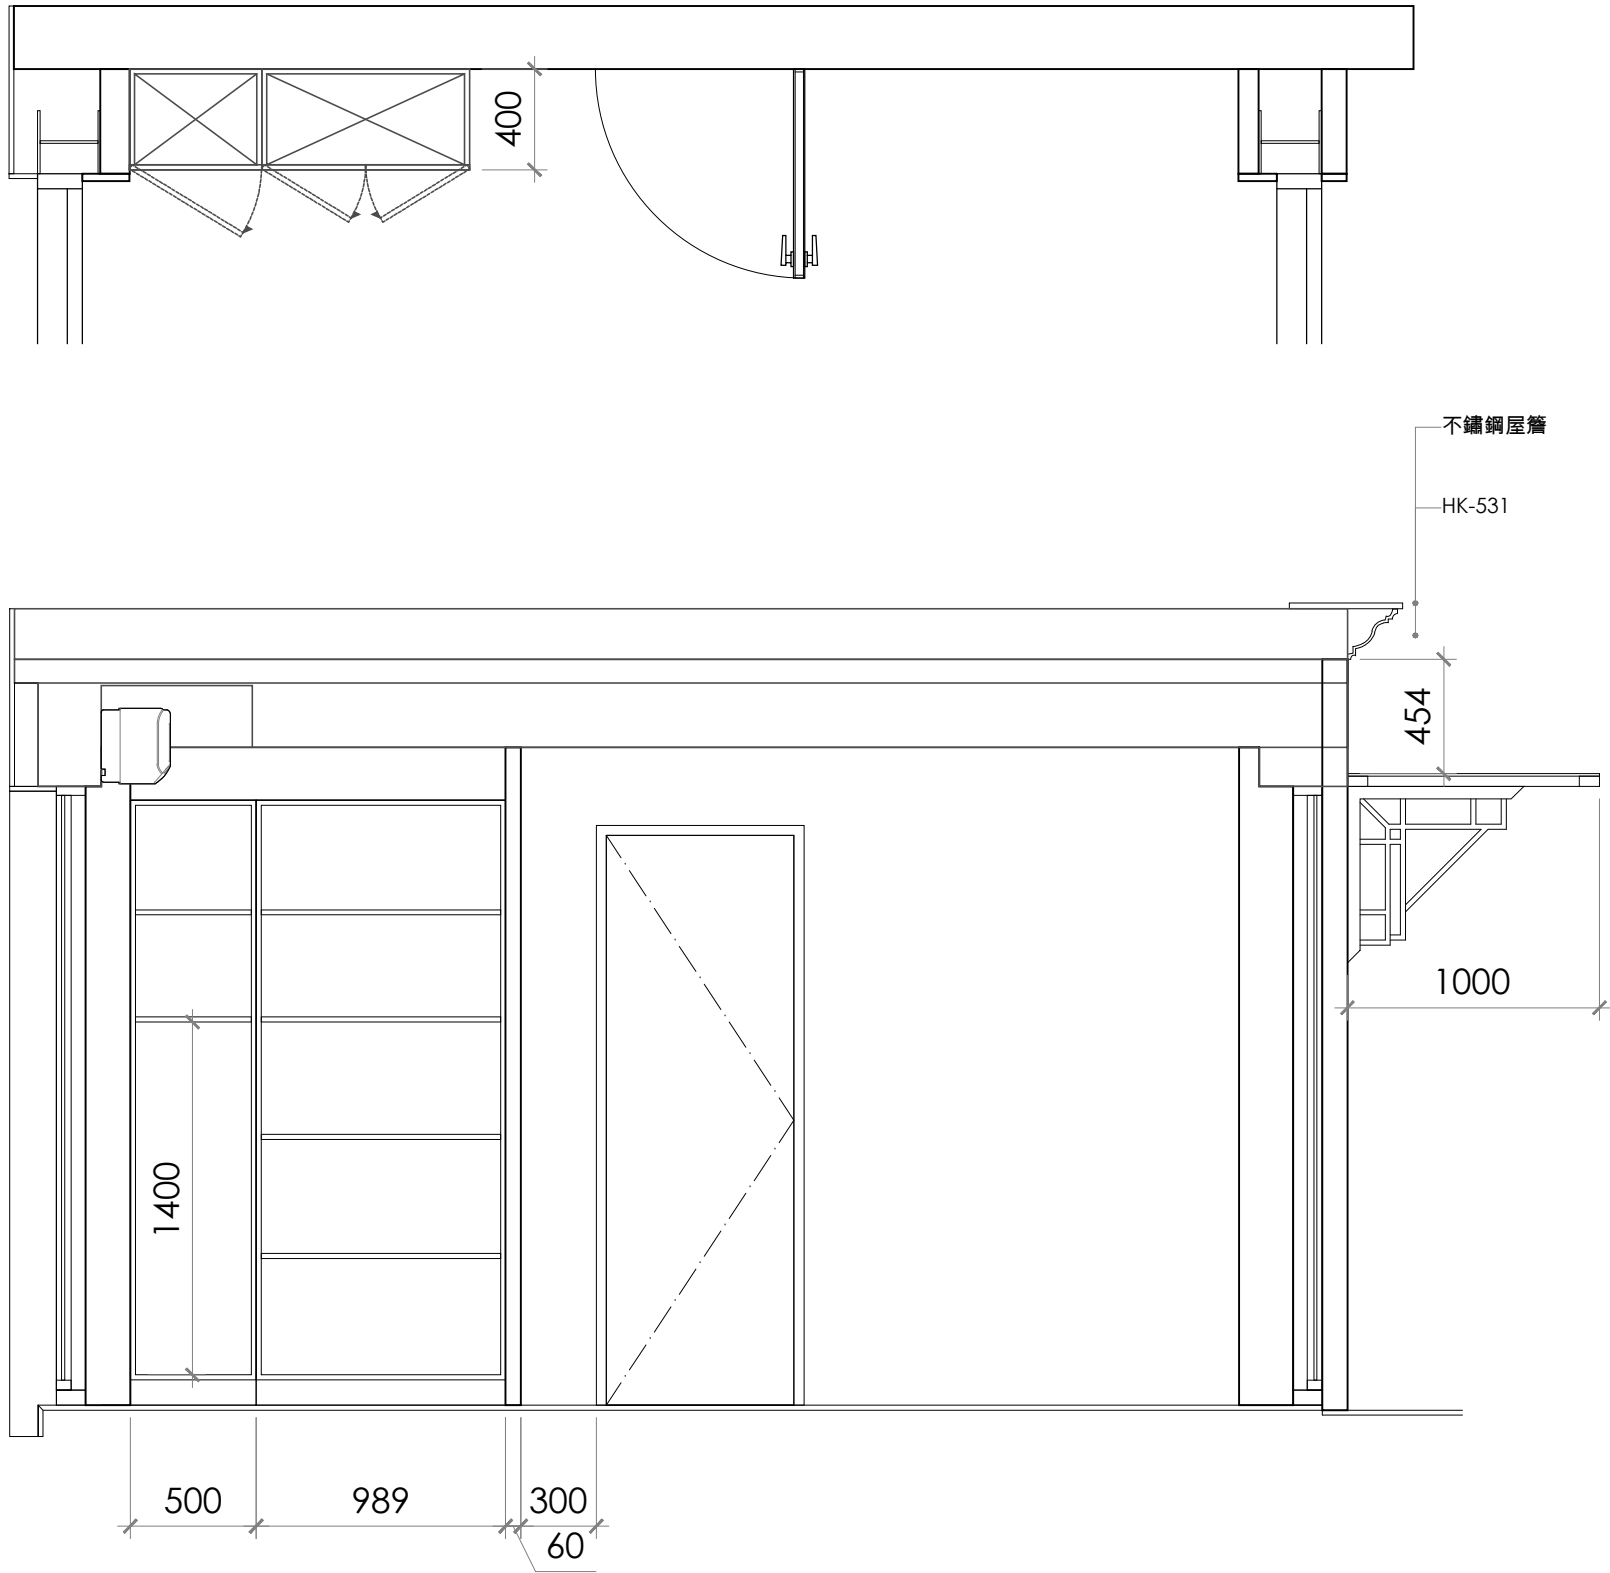

▲CH 2959mm
▲CH 2865mm
▲CH 2610mm

▼FL ±0 mm
▲FL -50 mm

1
E-59

ELEVATION

Scale=1:30

Revision	
APPROVAL/核准	
設計者:	建築師:
業主:	



備註:
a. 圖面標註尺寸僅供參考，施作均以現場放樣檢討之。
b. 圖面標註尺寸、材料及文字敘述因版本不同之差異，均以出圖章簽認日期之最近為準。
c. 電腦圖檔除由合約訂定外，均不得以任何方式外流。
d. 圖面所示均為本公司所擁有之智慧財產，切勿以任何方式複製修改。




MULA DECO

▲ 3F, N.26, Ln.290, Guangfu S. Rd., Taipei.
☎ 886-2-2546-3258
✉ 886-2-2546-3257
E Guido@muladeco.com

Project / 案名	
天母葉公館	
Sheet Title / 圖名	
1F 立面圖	
Date / 日期	Scale / 比例
8/10/2026	1/30CM
Designer / 設計	Approval / 核准
MONICA LIN	
Job No / 業務編號	Drawn By / 繪圖
00000	GUIDO
Dwg No.	Page No.
E-59	95

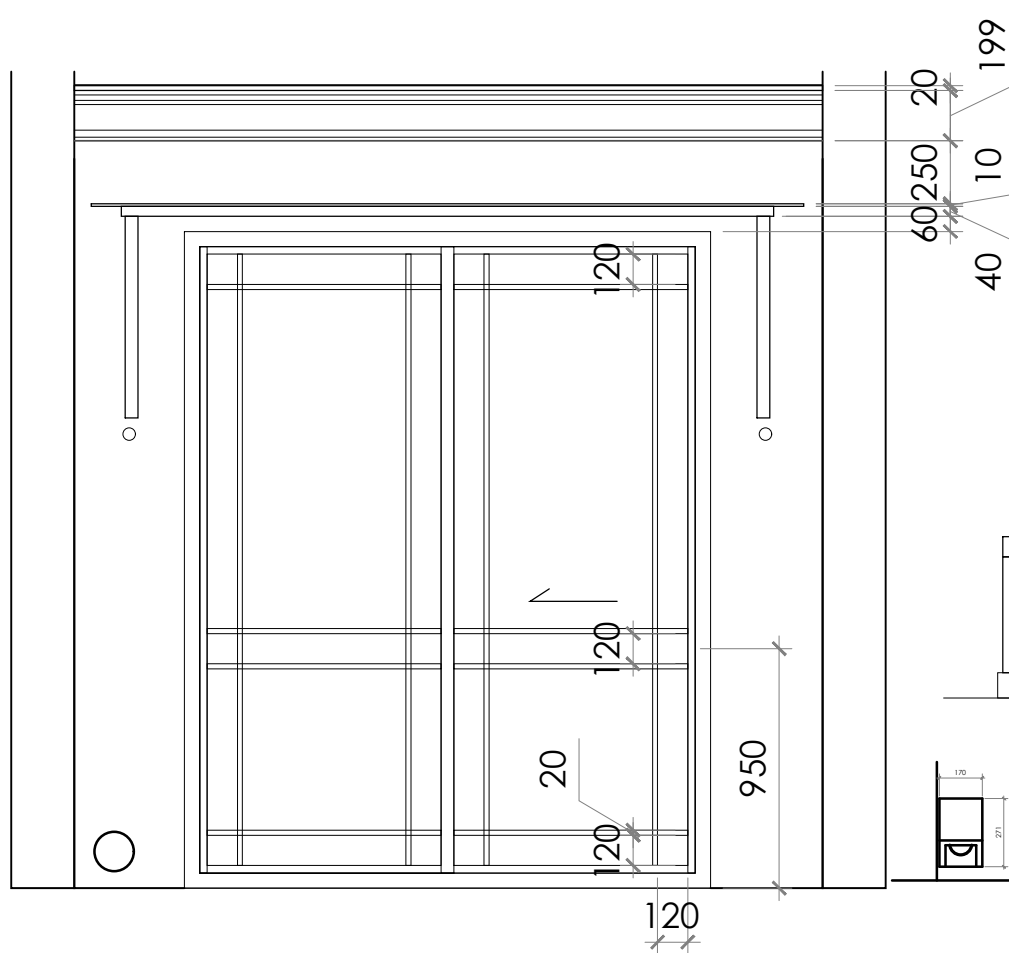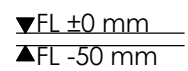

*實際尺寸依照風扇可安裝作微調。

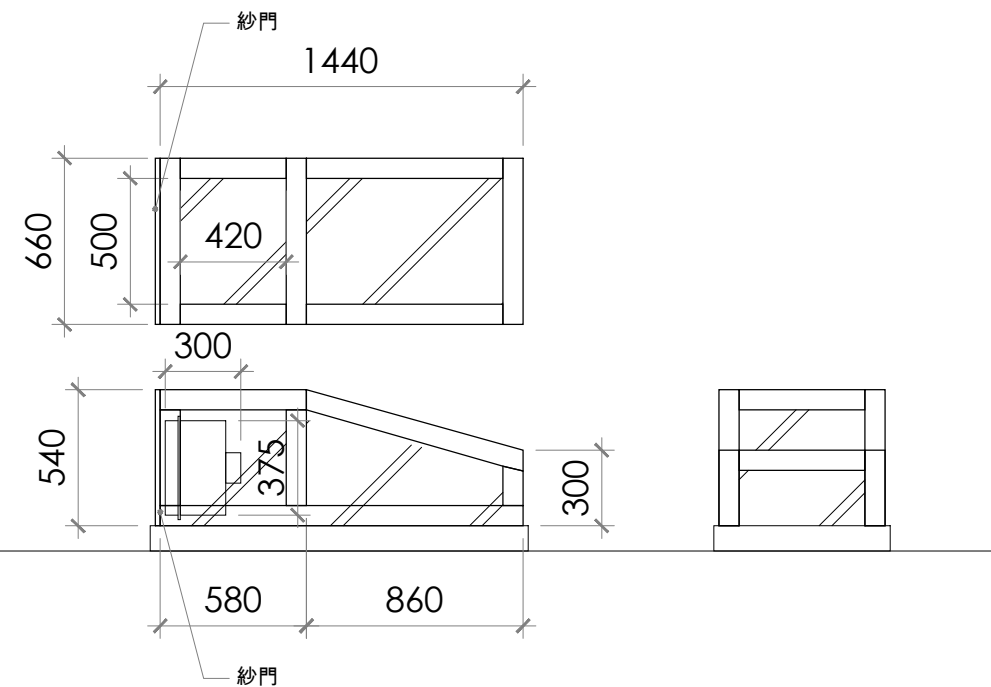

1
E-60

ELEVATION

Scale=1:30

[illegible]

APPROVAL/核准

設計者:	建築師:
業主:	

葡註:

- g. 圖面標註尺寸僅供參考，施作均以現場放樣檢討之。
- h. 圖面標註尺寸、材料及文字敘述因版本不同之差異，均以出圖章簽認日期之最近為準。
- i. 電腦圖檔除由合約訂定外，均不得以任何方式外流。
- j. 圖面所示均為本公司所擁有之智慧財產，切勿以任何方式複製修改。



MULA DECO

A 3F, N.26, Ln.290, Guangfu S. Rd., Taipei.
T 886-2-2546-3258
F 886-2-2546-3257
E Guido@muladeco.com





Project / 案名

天母葉公館

Sheet Title / 圖名
1F

立面圖

Date / 日期	Scale / 比例
8/10/2026	1/30CM
Designer / 設計	Approval / 核准
MONICA LIN	
Job No / 業務編號	Drawn By / 繪圖
00000	GUIDO
Dwg No.	Page No.
E-60	96

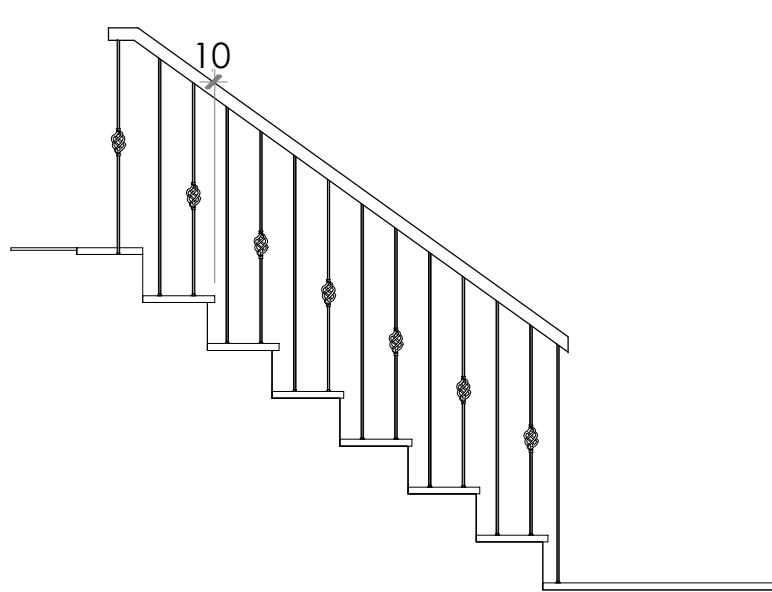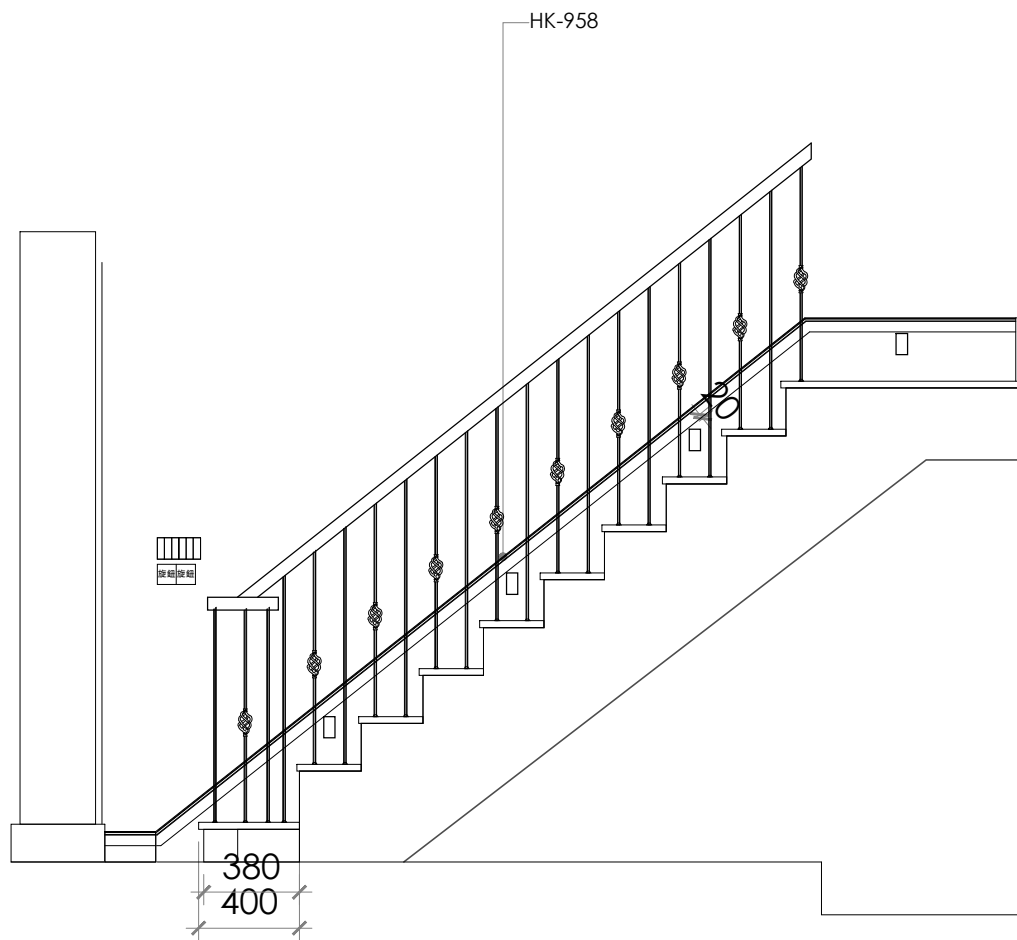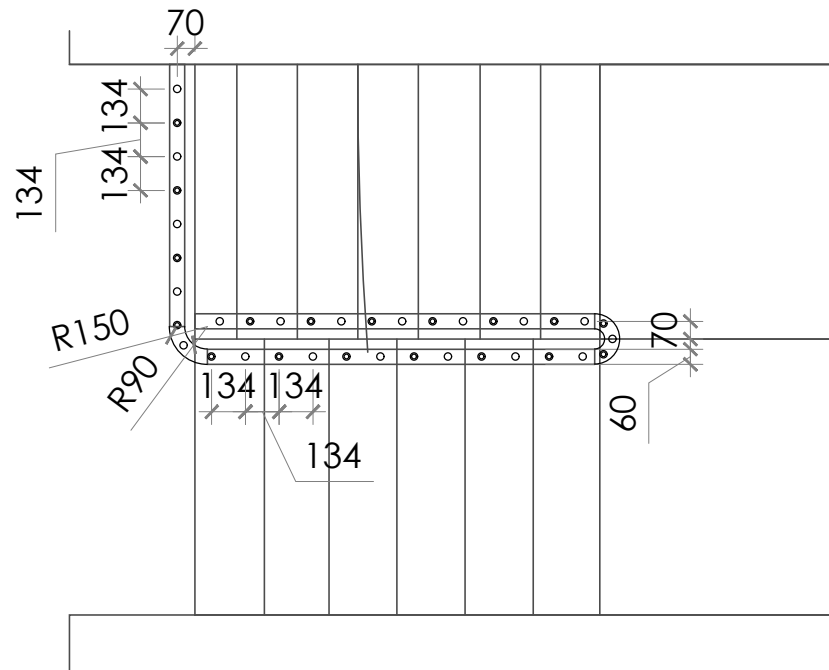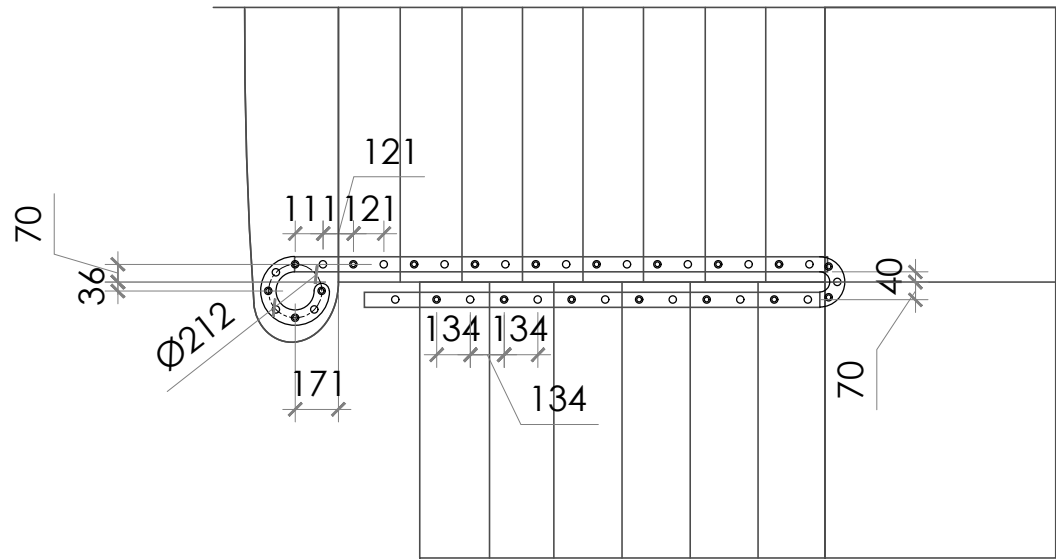

Revision

APPROVAL / 核准

設計者:	建築師:
業主:	

備註:

- 圖面標註尺寸僅供參考，施作均以現場放樣檢討之。
- 圖面標註尺寸、材料及文字敘述因版本不同之差異，均以出圖章簽認日期之最近為準。
- 電腦圖檔除由合約訂定外，均不得以任何方式外流。
- 圖面所示均為本公司所擁有之智慧財產，切勿以任何方式複製修改。



MULA DECO

▲ 3F, N.26, Ln.290, Guangfu S. Rd., Taipei.
☎ 886-2-2546-3258
☎ 886-2-2546-3257
✉ Guido@muladeco.com

Project / 案名

天母葉公館

Sheet Title / 圖名




1F

立面圖

Date / 日期	Scale / 比例
8/10/2026	1/30CM
Designer / 設計	Approval / 核准
MONICA LIN	
Job No / 業務編號	Drawn By / 繪圖
00000	GUIDO
Dwg No.	Page No.

E-60

97

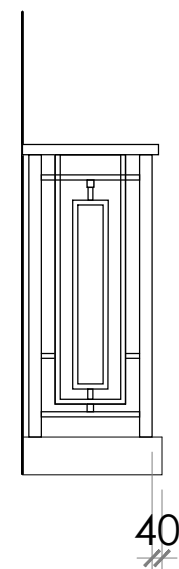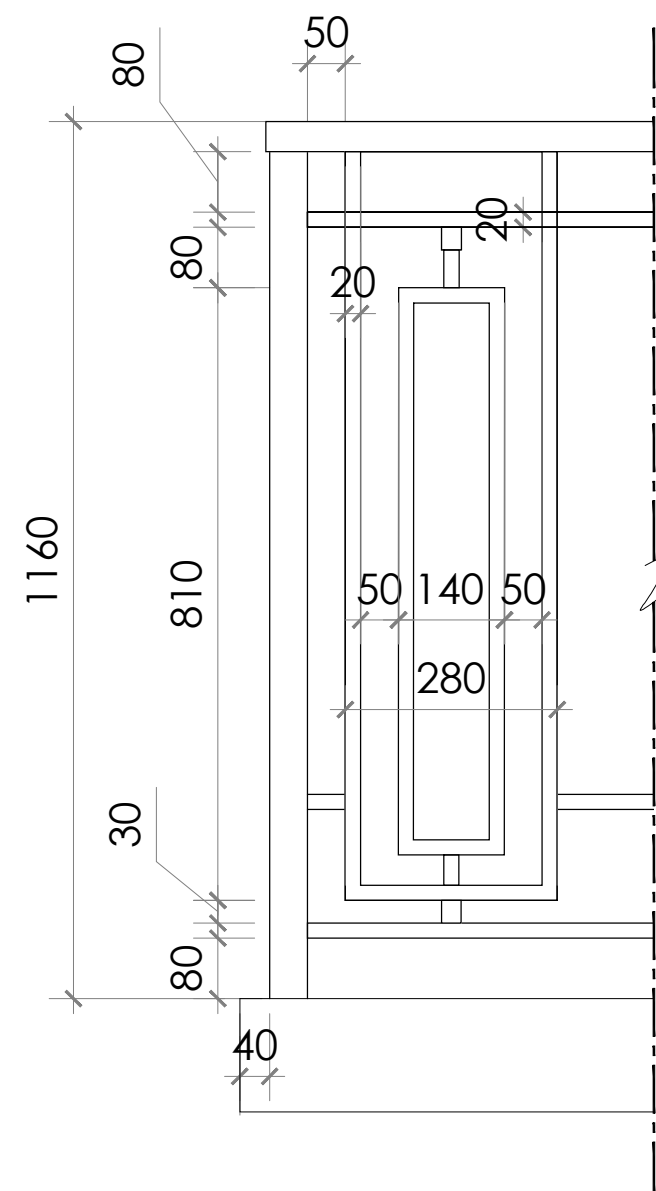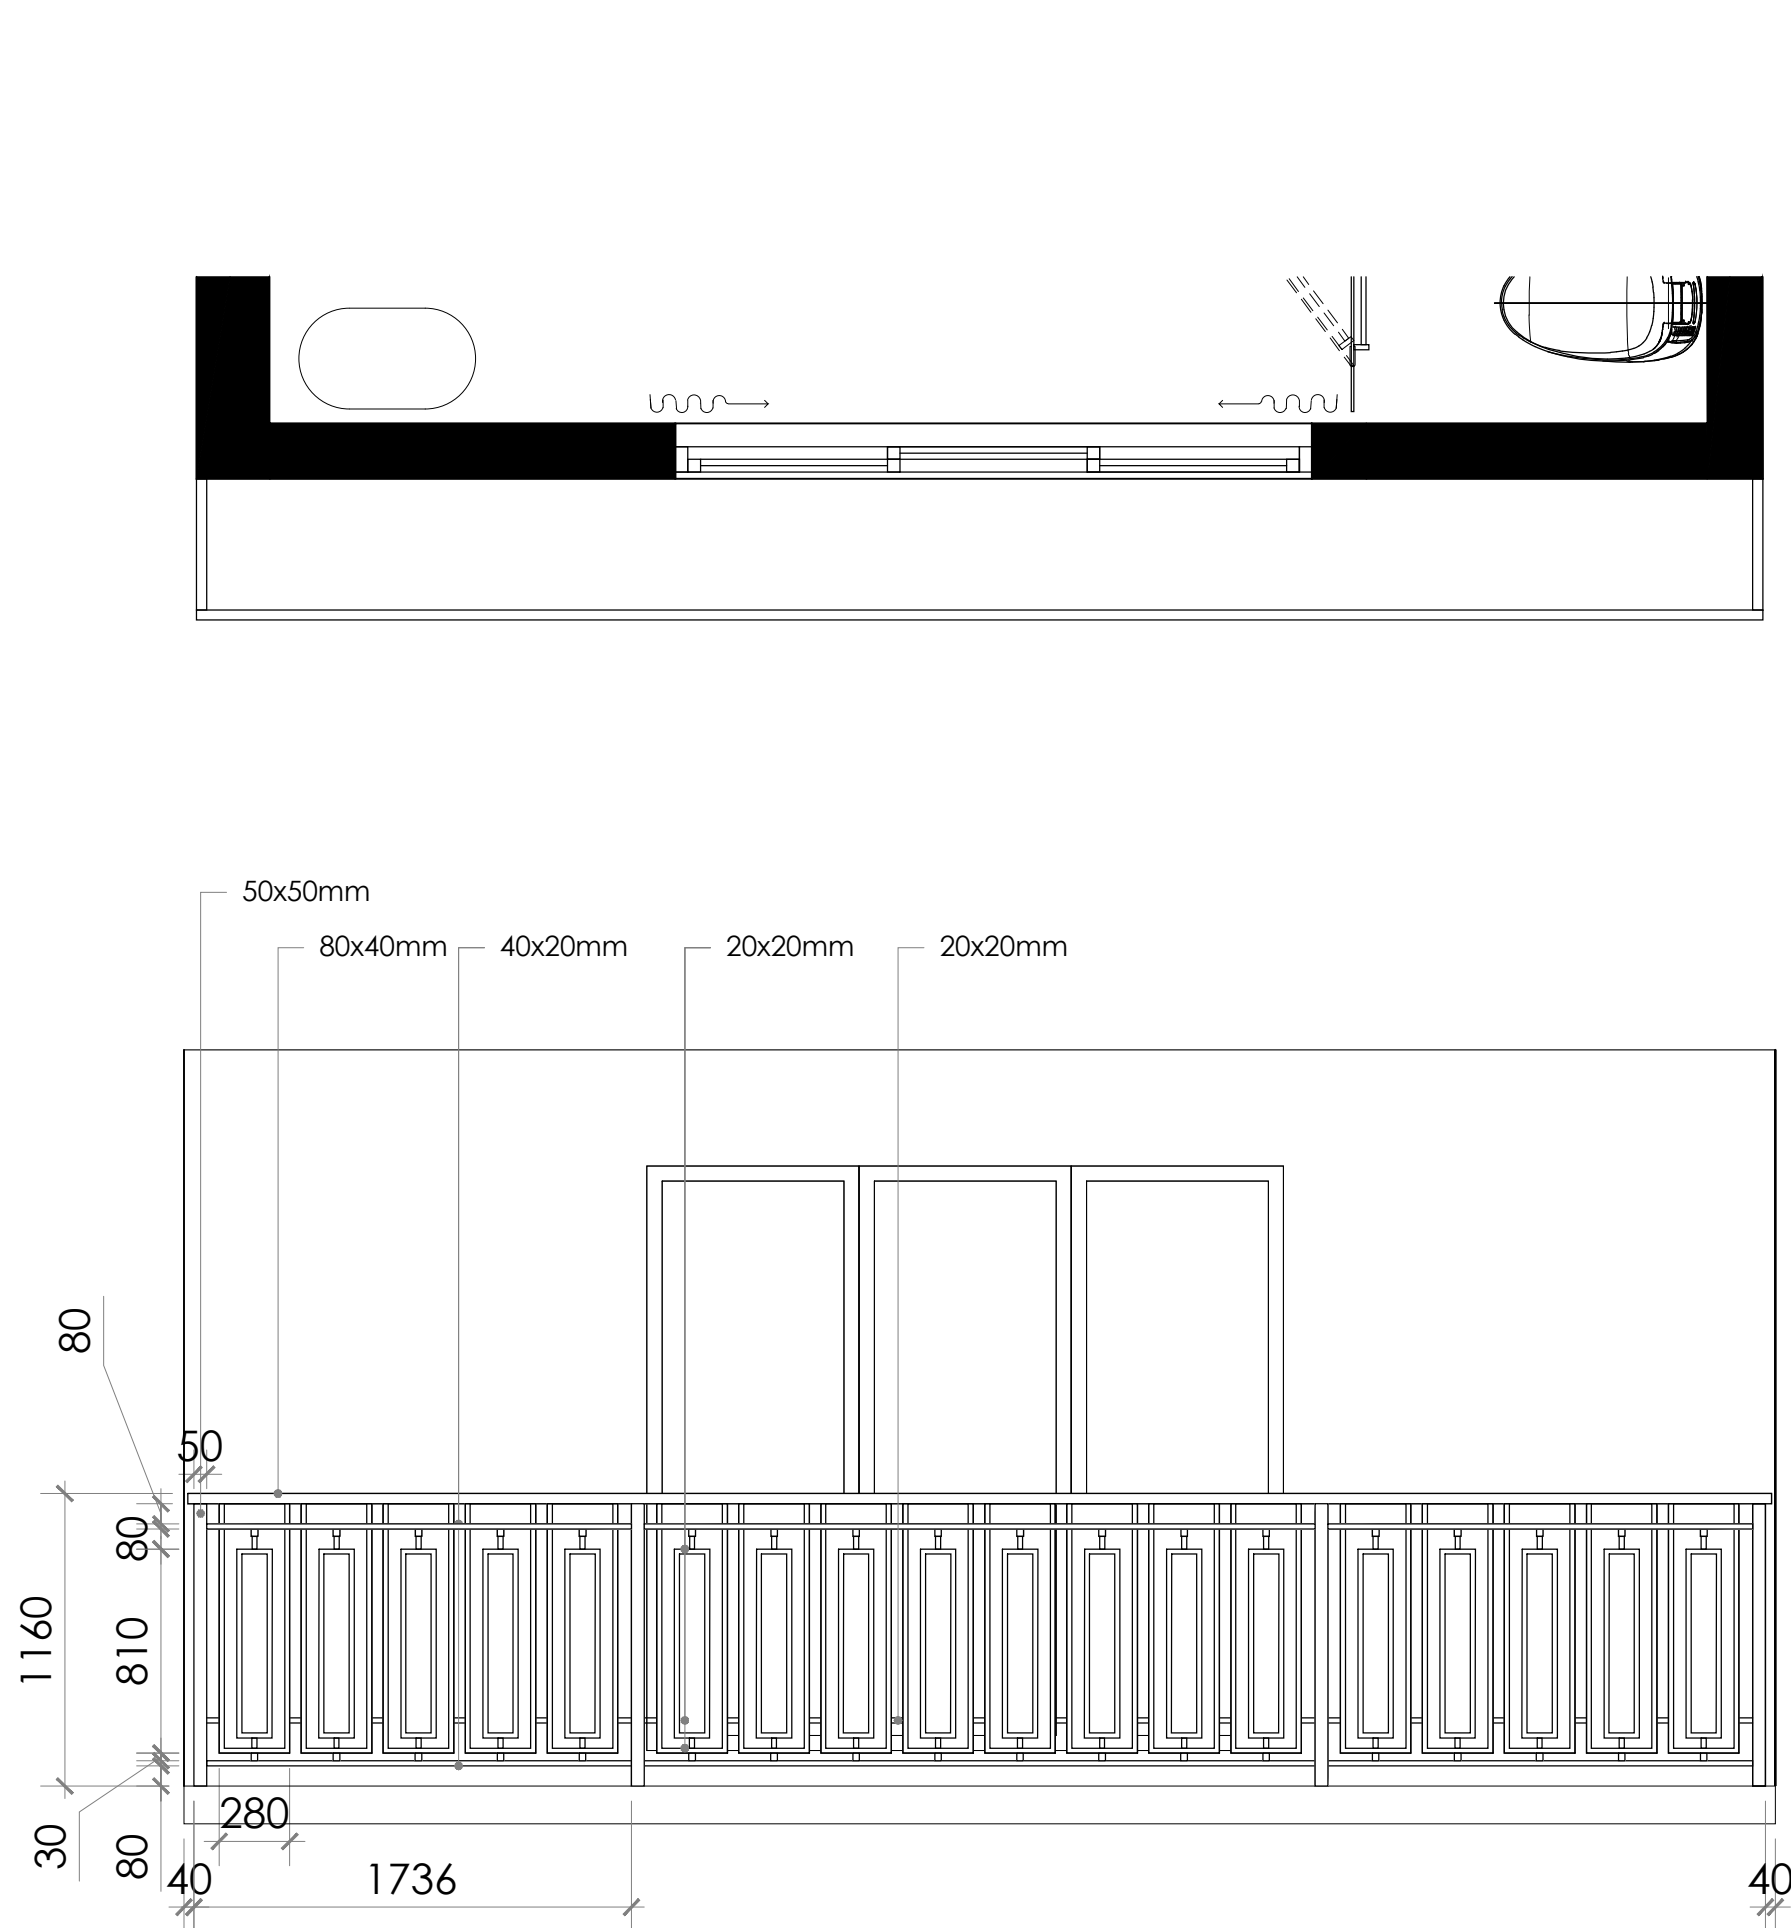

Revision

APPROVAL/核准

設計者:	建築師:
業主:	

備註:

a. 圖面標註尺寸僅供參考，施作均以現場放樣檢討之。
b. 圖面標註尺寸、材料及文字敘述因版本不同之差異，均以出圖章簽認日期之最近為準。
c. 電腦圖檔除由合約訂定外，均不得以任何方式外流。
d. 圖面所示均為本公司所擁有之智慧財產，切勿以任何方式複製修改。

M

MULA DECO

▲ 3F, N.26, Ln.290, Guangfu S. Rd., Taipei.
☎ 886-2-2546-3258
☎ 886-2-2546-3257
✉ Guido@muladeco.com



Project / 案名

天母葉公館

Sheet Title / 圖名

2F
立面圖

Date / 日期	Scale / 比例
8/10/2026	1/30CM
Designer / 設計	Approval / 核准
MONICA LIN	
Job No / 業務編號	Drawn By / 繪圖
00000	GUIDO
Dwg No.	Page No.
E-61	98

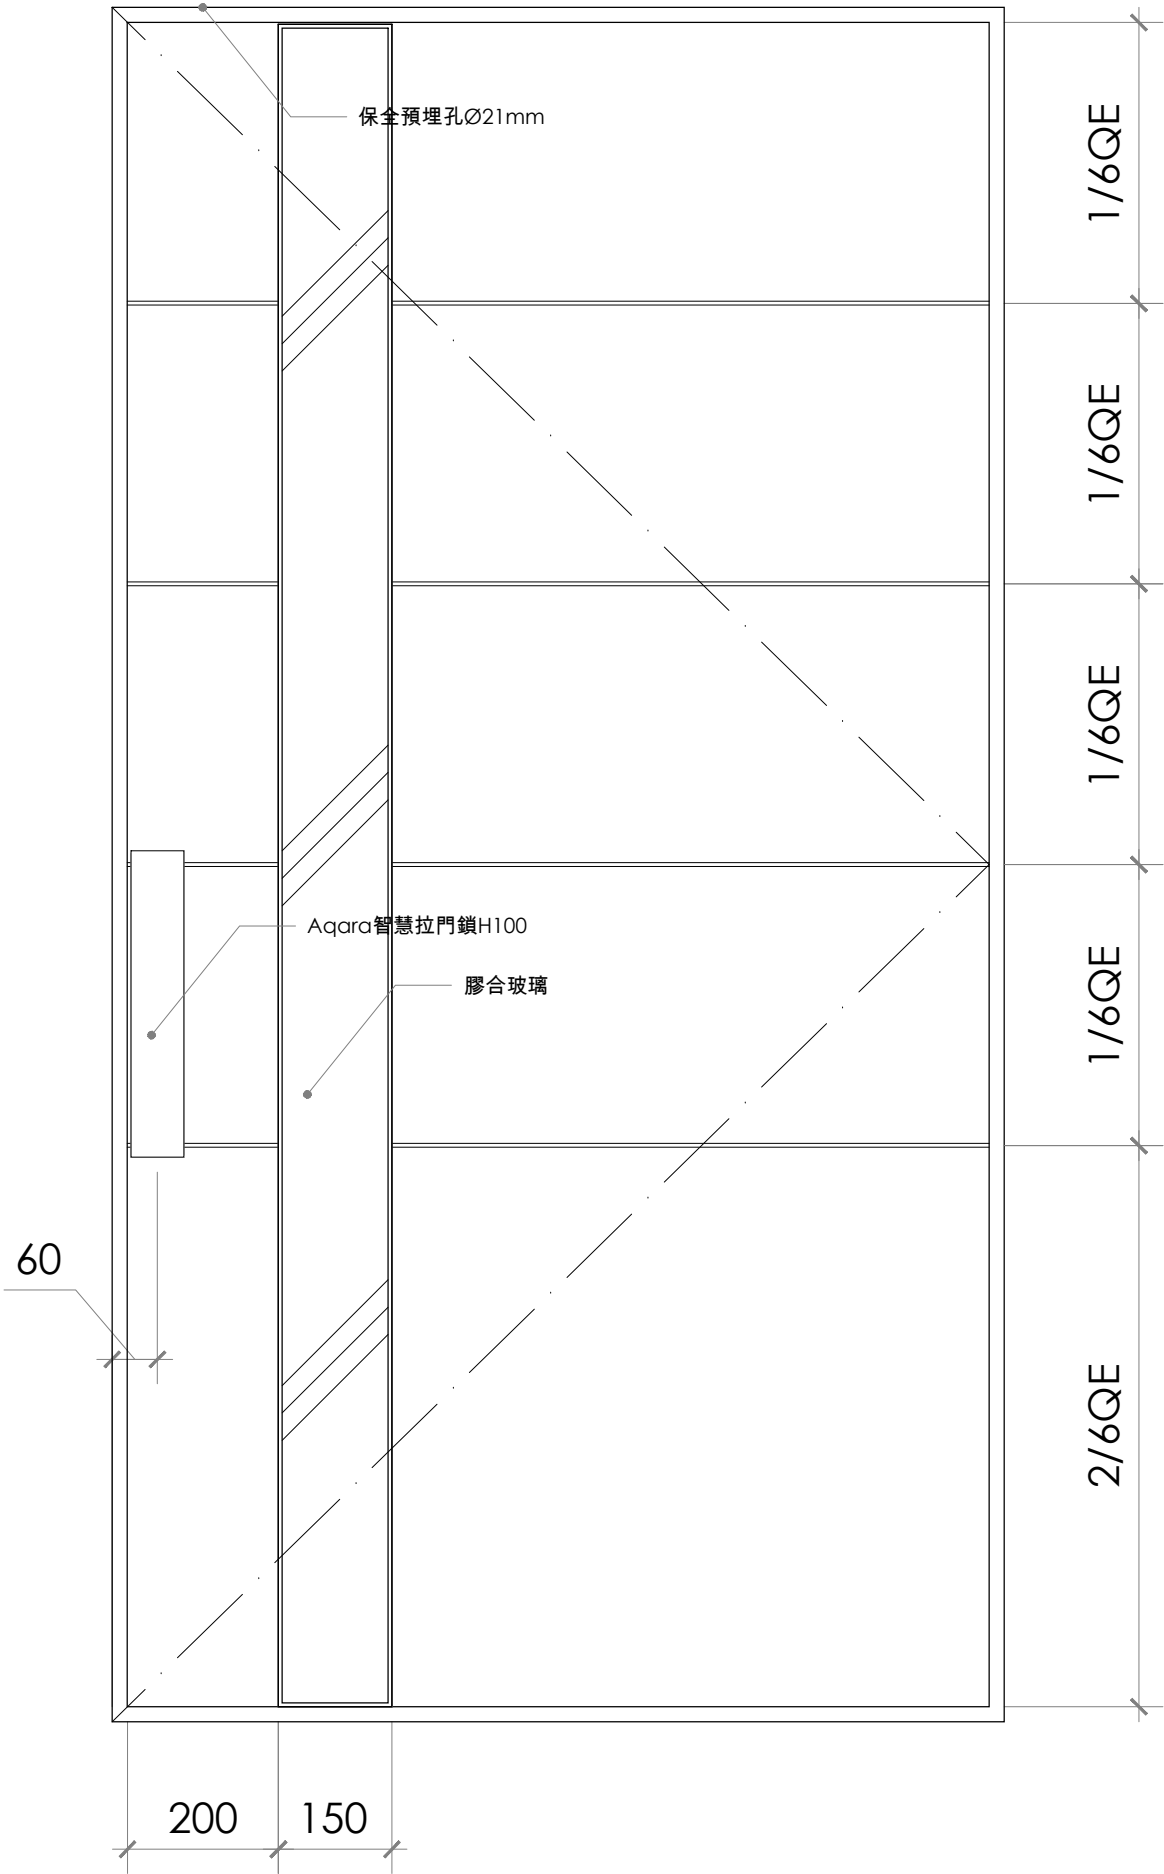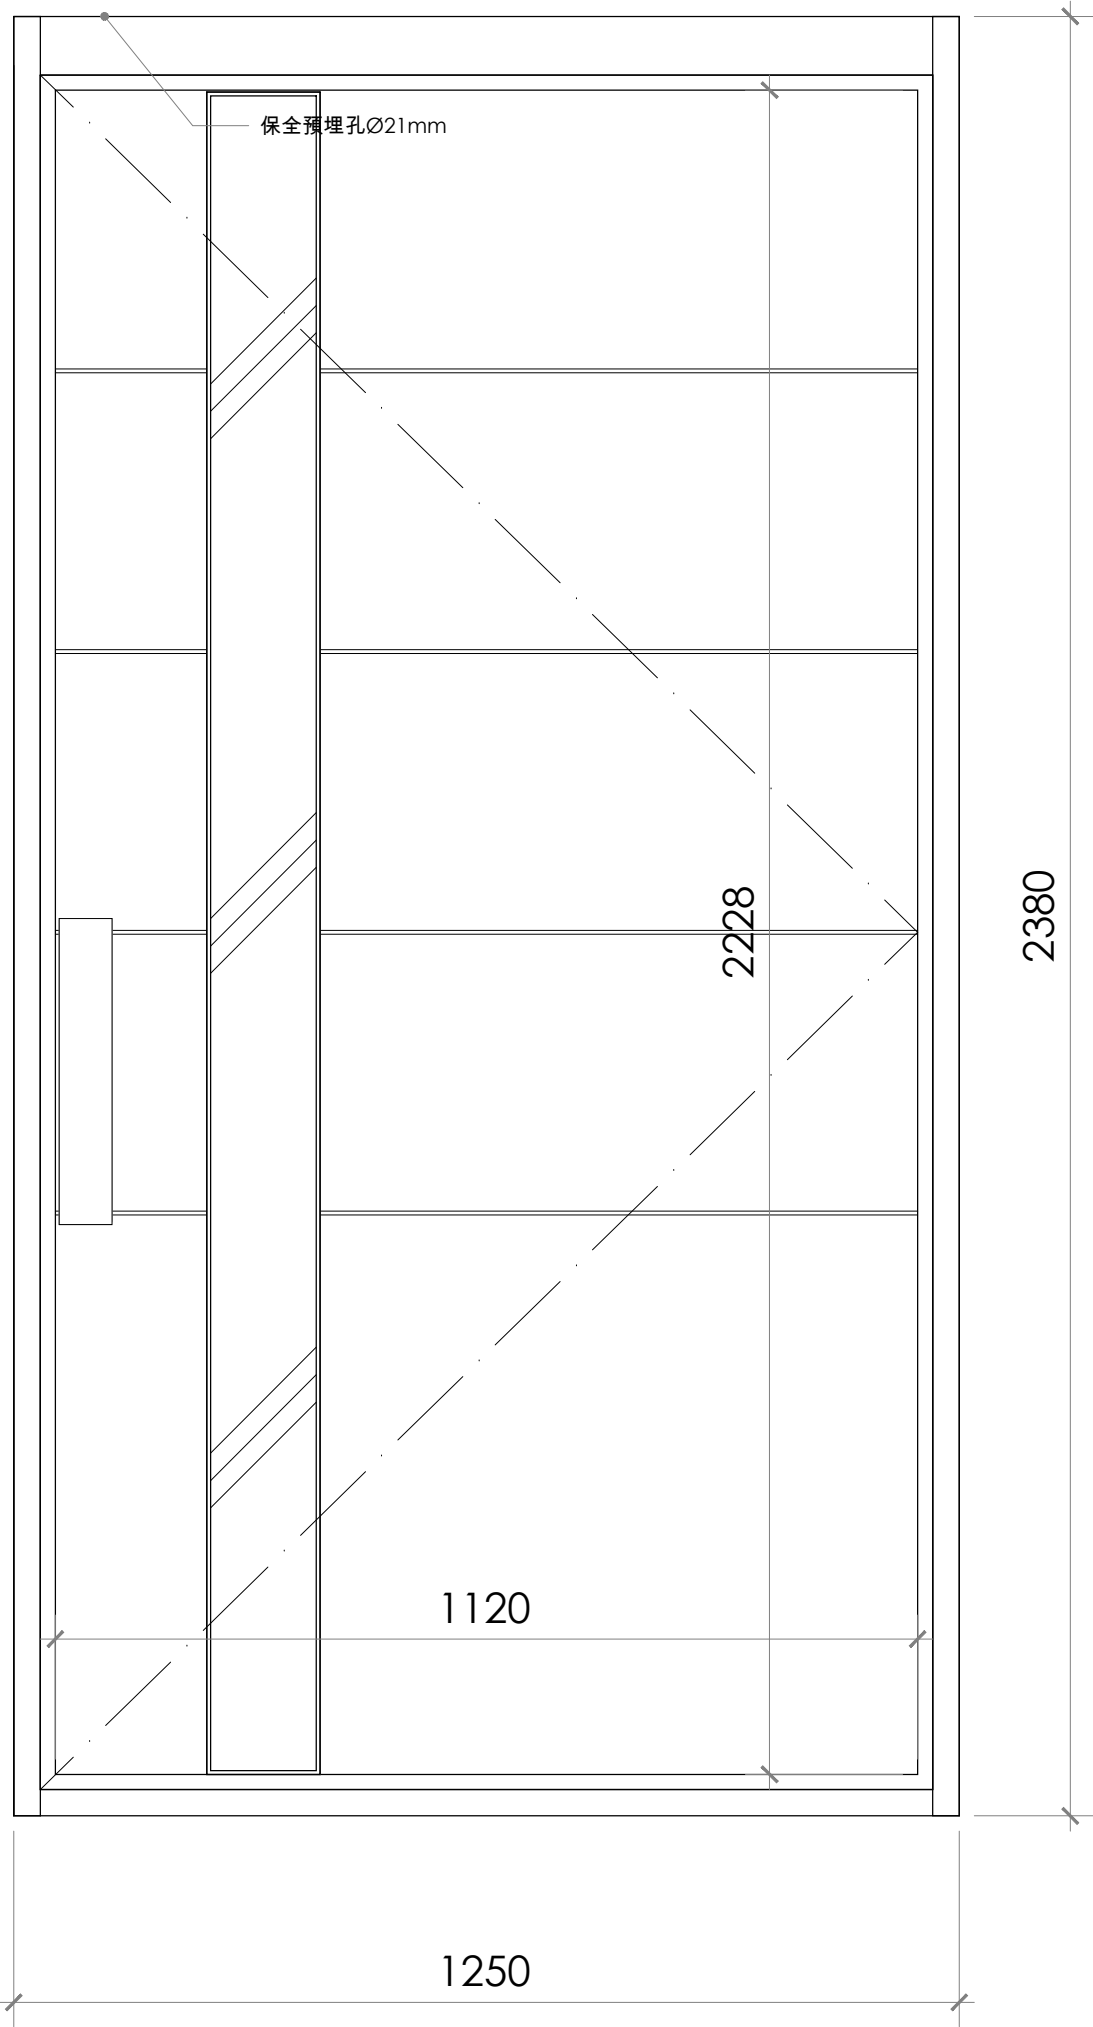

Revision	
APPROVAL / 核准	
設計者:	建築師:
業主:	

備註:
a. 圖面標註尺寸僅供參考，施作均以現場放樣檢討之。
b. 圖面標註尺寸、材料及文字敘述因版本不同之差異，均以出圖章簽認日期之最近為準。
c. 電腦圖檔除由合約訂定外，均不得以任何方式外流。
d. 圖面所示均為本公司所擁有之智慧財產，切勿以任何方式複製修改。



MULA DECO
A 3F, N.26, Ln.290, Guangfu S. Rd., Taipei.
T 886-2-2546-3258
F 886-2-2546-3257
E Guido@muladeco.com

Project / 案名





天母葉公館

Sheet Title / 圖名

1F

立面圖

Date / 日期	Scale / 比例
8/10/2026	1/30CM
Designer / 設計	Approval / 核准
MONICA LIN	
Job No / 業務編號	Drawn By / 繪圖
00000	GUIDO
Dwg No.	Page No.
DE-01	99

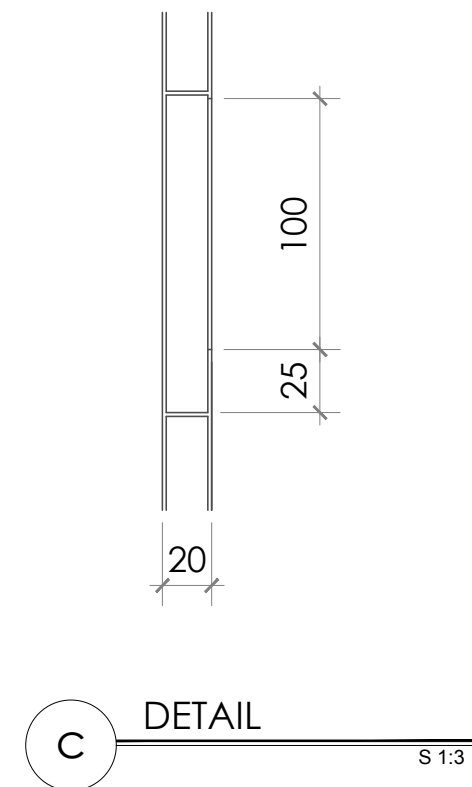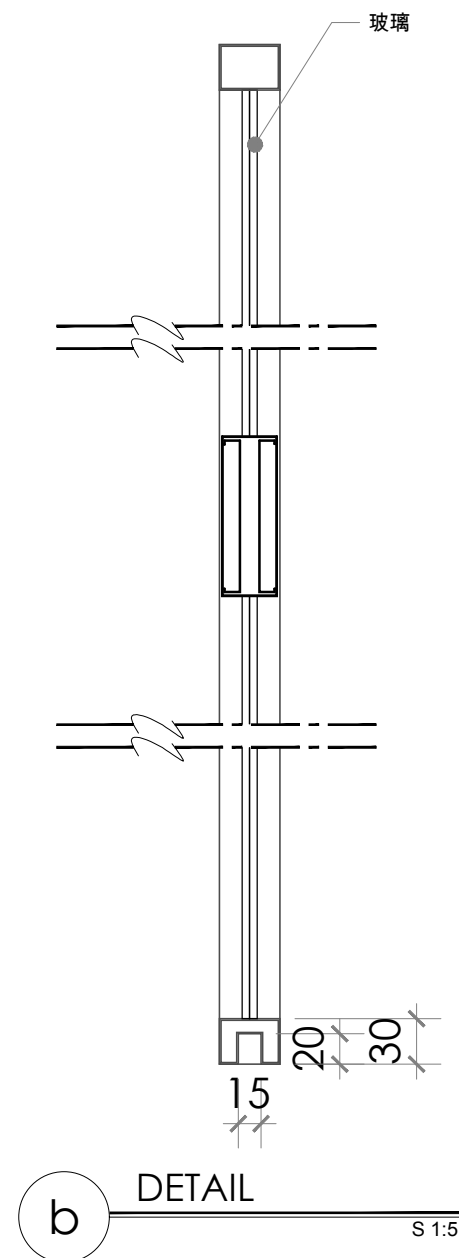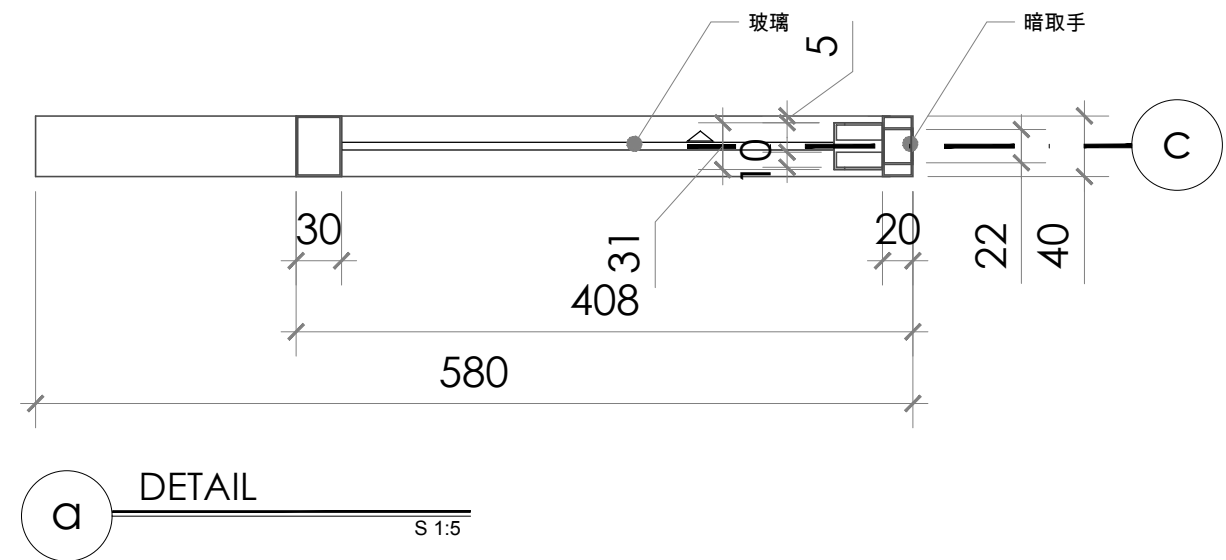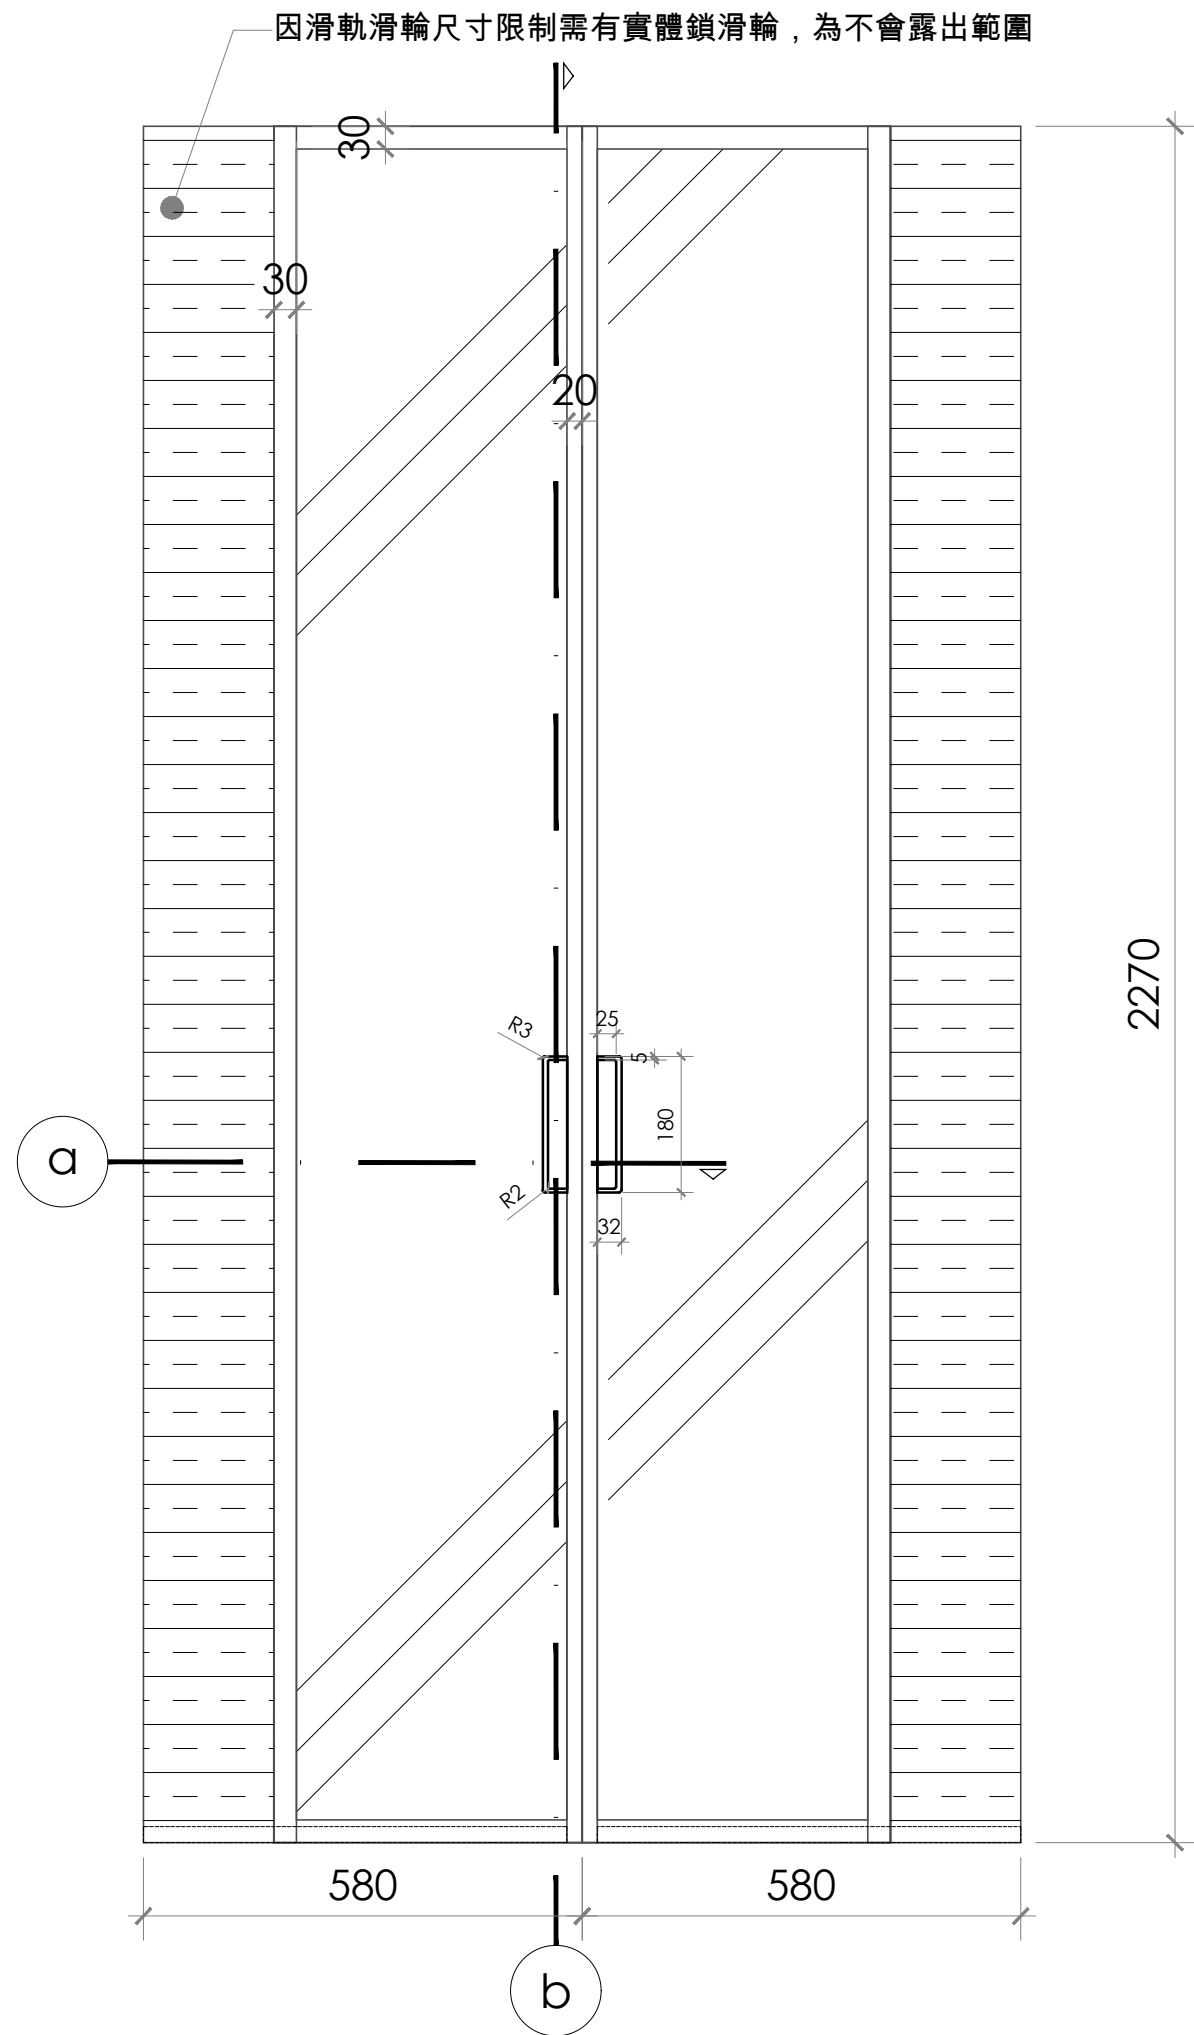

Revision

設計者:	建築師:
業主:	

APPROVAL/核准

備註:

a. 圖面標註尺寸僅供參考，施作均以現場放樣檢討之。

b. 圖面標註尺寸、材料及文字敘述因版本不同之差異，均以出圖章簽認日期之最近為準。

c. 電腦圖檔除由合約訂定外，均不得以任何方式外流。

d. 圖面所示均為本公司所擁有之智慧財產，切勿以任何方式複製修改。

M

MULA DECO

▲ 3F, N.26, Ln.290, Guangfu S. Rd., Taipei.
☎ 886-2-2546-3258
☎ 886-2-2546-3257
✉ Guido@muladeco.com

Project / 案名


天母葉公館

Sheet Title / 圖名

2F

立面圖

Date / 日期	Scale / 比例
8/10/2026	1/30CM
Designer / 設計	Approval / 核准
MONICA LIN	
Job No / 業務編號	Drawn By / 繪圖
00000	GUIDO
Dwg No.	Page No.
DE-02	100

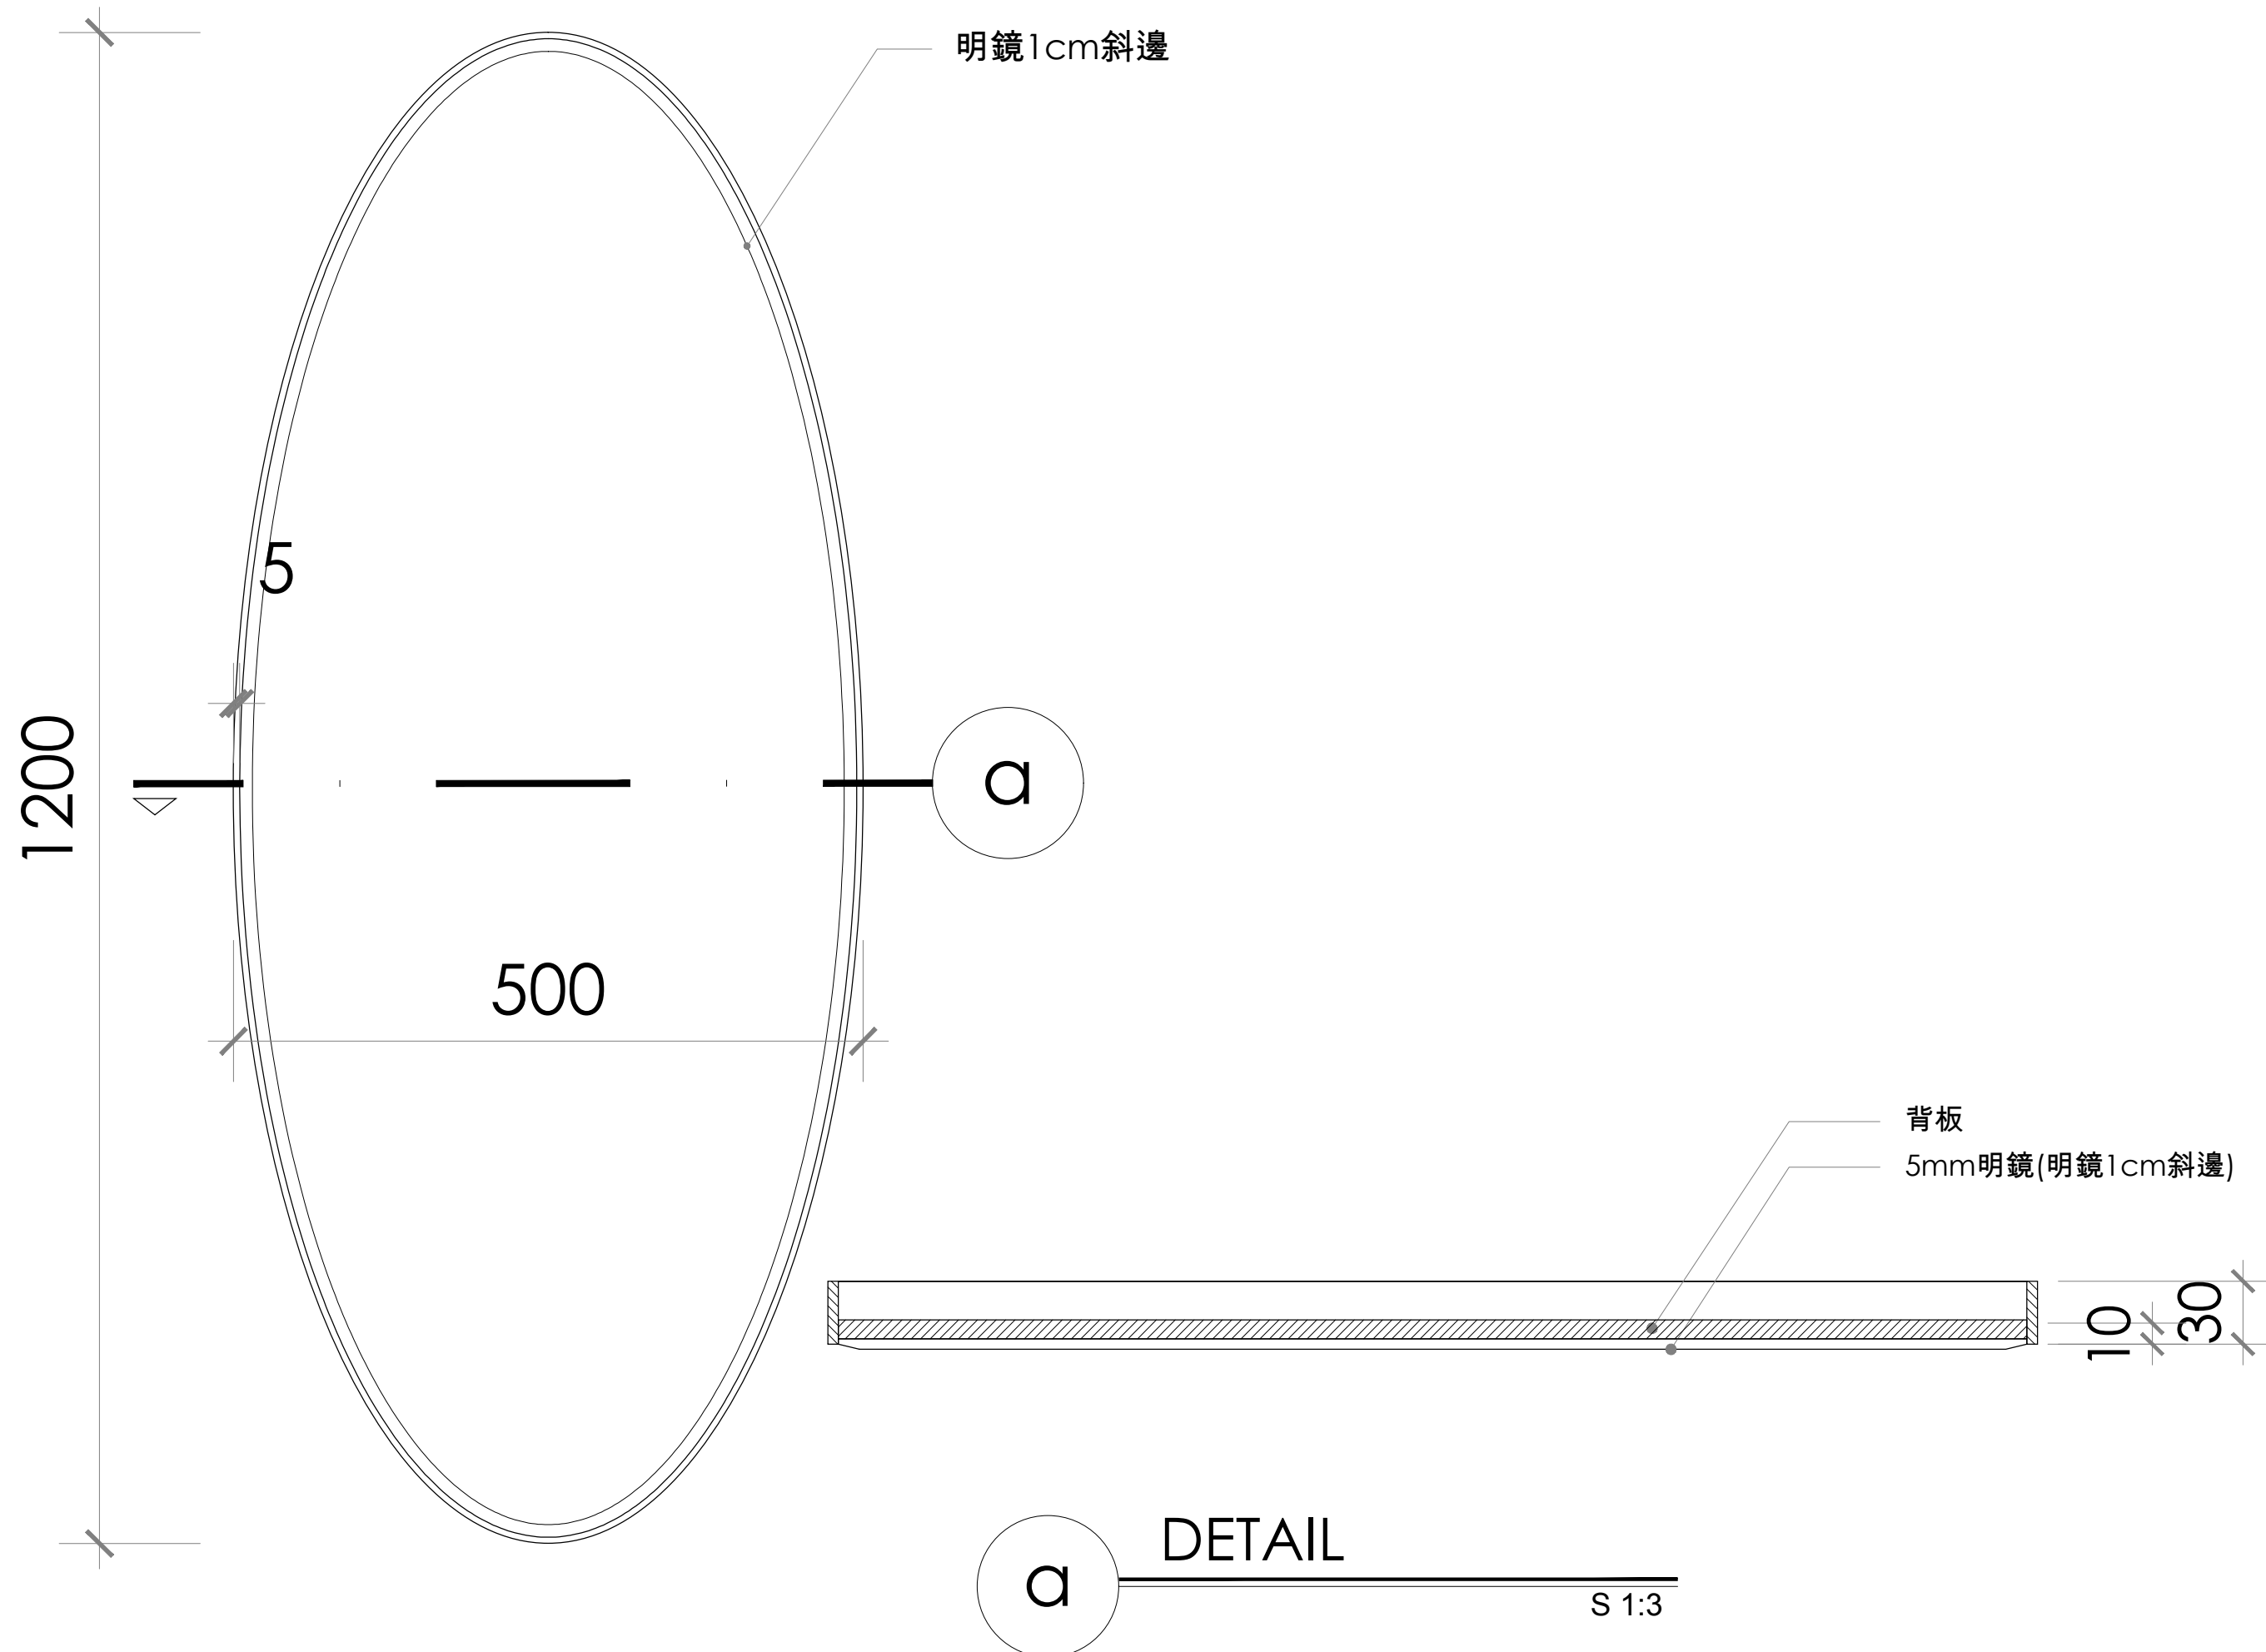[illegible]

備註:





- 圖面標註尺寸僅供參考，施作均以現場放樣檢討之。
- 圖面標註尺寸、材料及文字敘述因版本不同之差異，均以出圖章簽認日期之最近為準。
- 電腦圖檔除由合約訂定外，均不得以任何方式外流。
- 圖面所示均為本公司所擁有之智慧財產，切勿以任何方式複製修改。



MULA DECO

A 3F, N.26, Ln.290, Guangfu S. Rd., Taipei.
T 886-2-2546-3258
F 886-2-2546-3257
E Guido@mula deco.com

Project / 案名	
天母葉公館	
Sheet Title / 圖名	
2F	
立面圖	
Date / 日期	Scale / 比例
8/10/2026	1/5CM
Designer / 設計	Approval / 核准
MONICA LIN	
Job No / 業務編號	Drawn By / 繪圖
00000	GUIDO
Dwg No.	Page No.
DE-03	101

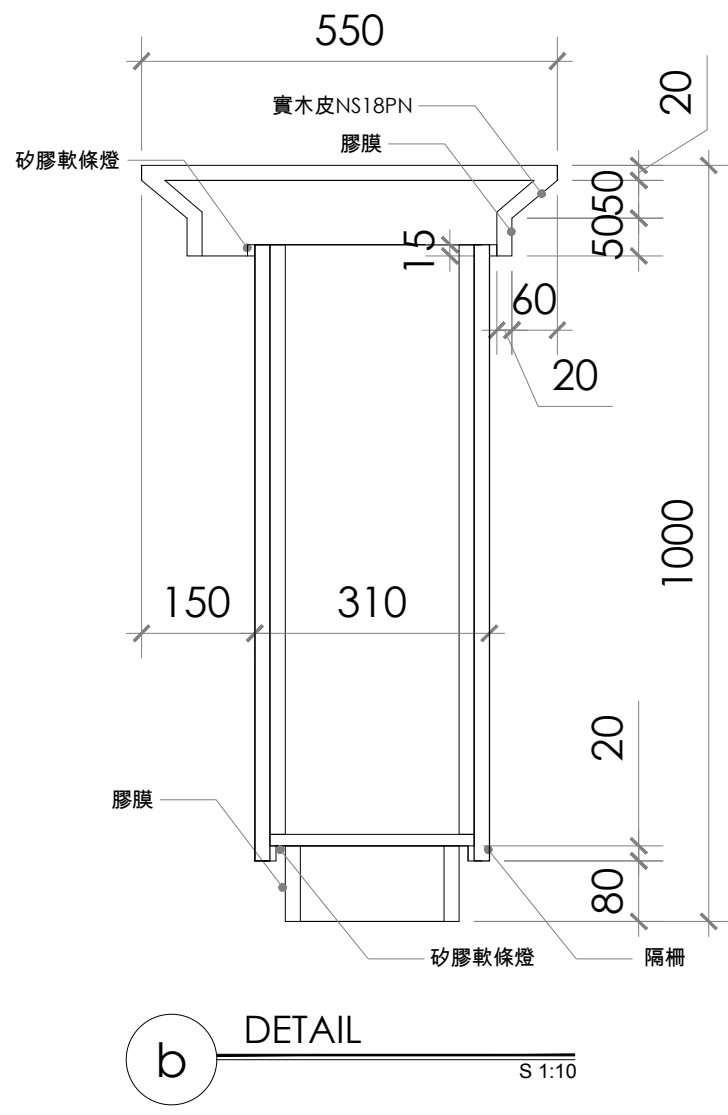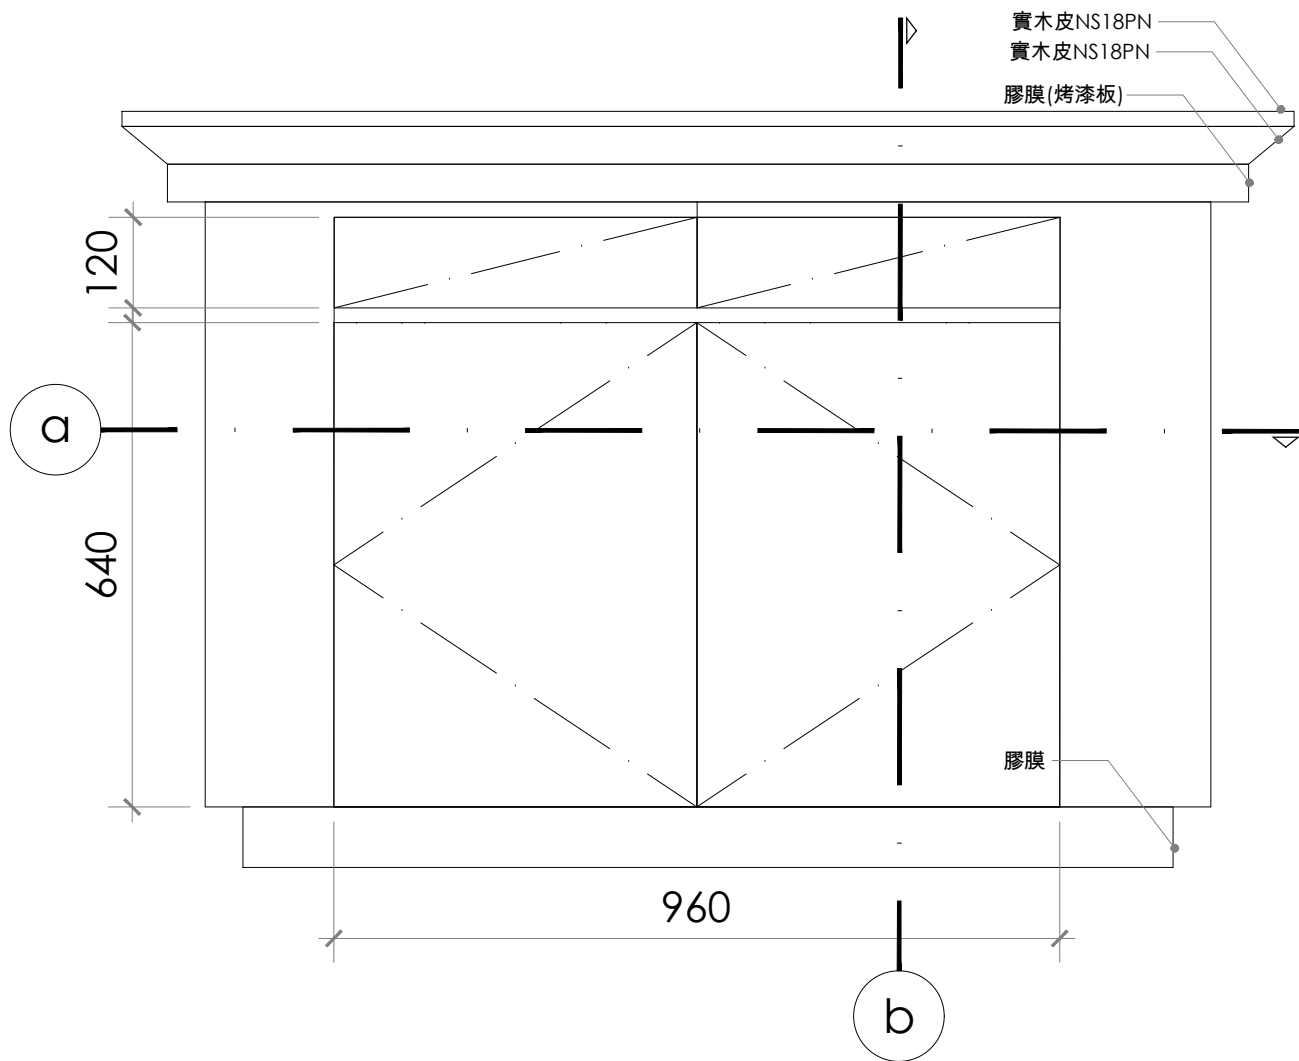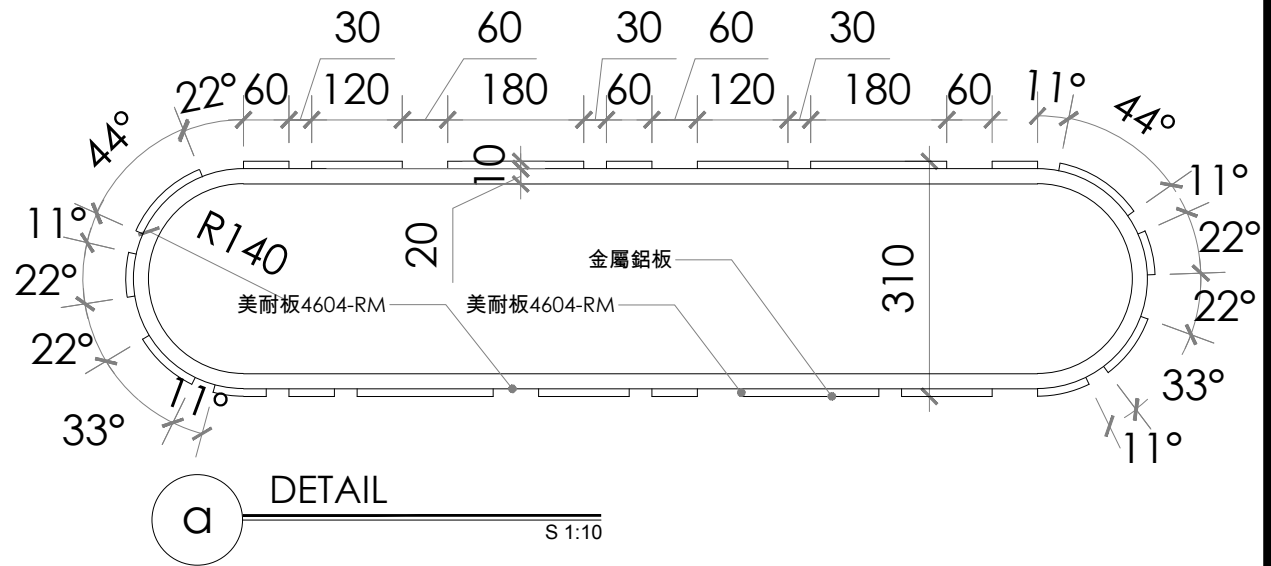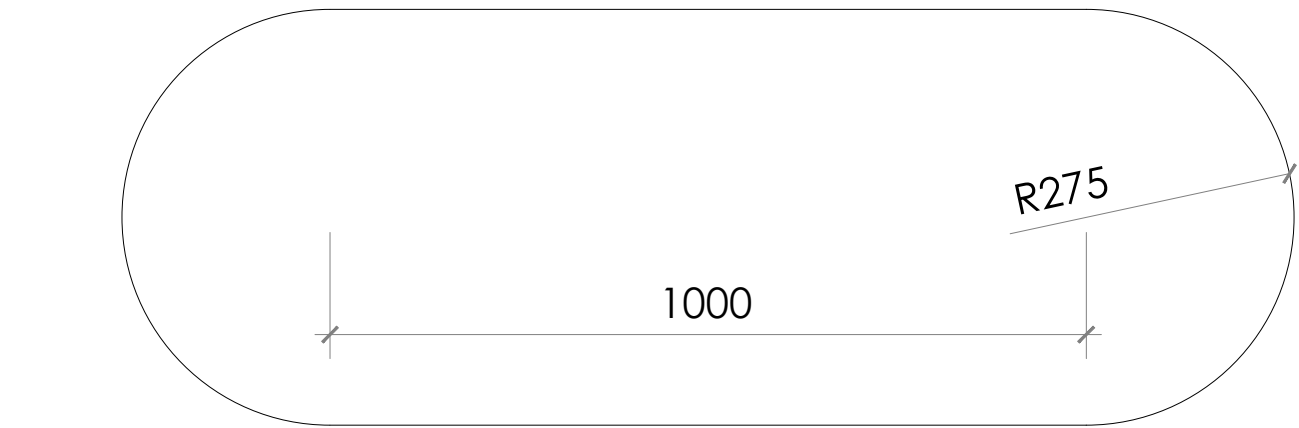

APPROVAL/核准

設計者:	建築師:
業主:	

備註:

- a. 圖面標註尺寸僅供參考，施作均以現場放樣檢討之。
b. 圖面標註尺寸、材料及文字敘述因版本不同之差異，均以出圖章簽認日期之最近為準。
c. 電腦圖檔除由合約訂定外，均不得以任何方式外流。
d. 圖面所示均為本公司所擁有之智慧財產，切勿以任何方式複製修改。



MULA DECO

▲ 3F, N.26, Ln.290, Guangfu S. Rd., Taipei.
☎ 886-2-2546-3258
☎ 886-2-2546-3257
✉ Guido@muladeco.com

Project / 案名




天母葉公館

Sheet Title / 圖名

1F

立面圖

Date / 日期	Scale / 比例
8/10/2026	1/10CM
Designer / 設計	Approval / 核准
MONICA LIN	
Job No / 業務編號	Drawn By / 繪圖
00000	GUIDO
Dwg No.	Page No.
DE-04	102

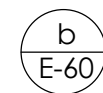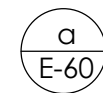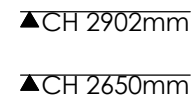

Dwg No.	Page No.
E-63	65