


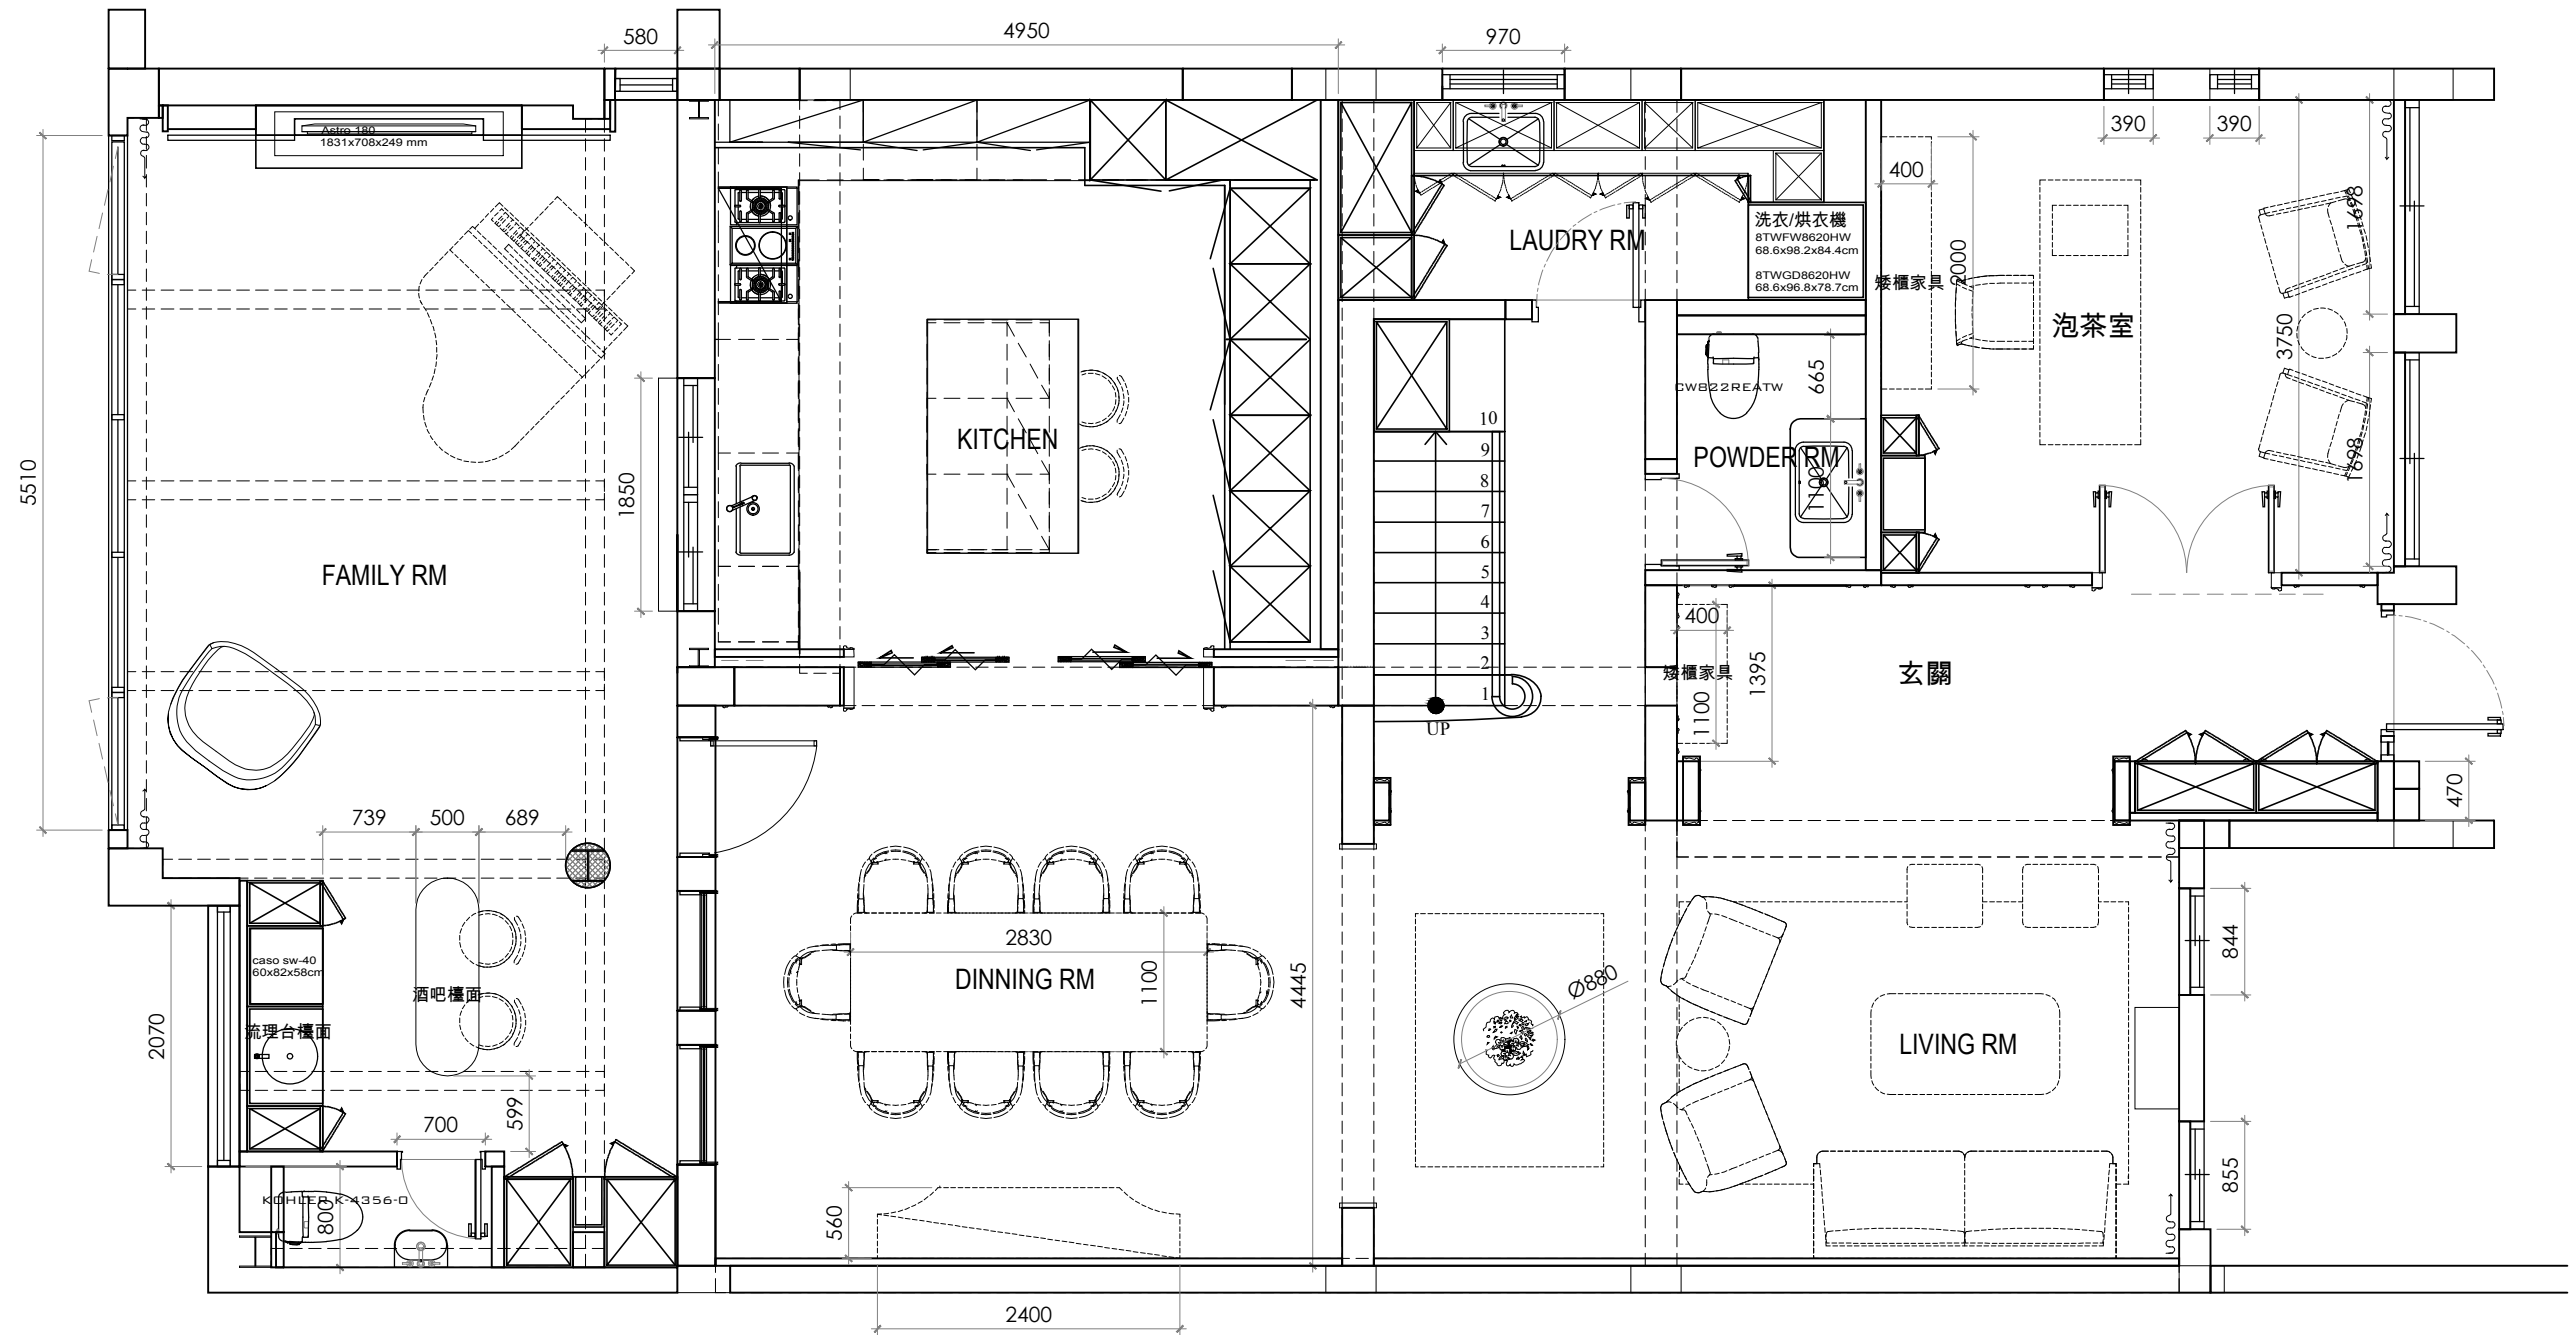

3F, N.26, Ln.290, Guangfu S. Rd., Taipei.
886-2-2546-3258
886-2-2546-3258
Guido@mula deco.com

備註:
a.圖面標註尺寸僅供參考，施作均以現場放樣檢封之。
b.圖面標註尺寸、材料與文字敘述因版本不同之差異，均以出圖章簽認日期之最近為準。
c.電腦圖檔係由合約訂定外，均不得以何方式外流。
d.圖面所承均為本公司所擁有之智慧財產，切勿以任何方式複製修改。

Revision		

Project /


天母葉公館


Job No /
00000
Scale /
1/60 mm


Date /	Approval /
8/10/2026	
Designer /	Drawn By /
Monica Lin	GUIDO

Sheet Title /
1F
平面配置圖

Dwg No.
P-01
Page No.
01

 牆 型 式	內 容	總 厚 度
	木作隔間牆	
	原有建築牆	154mm
	1/2B磚牆	120mm
	65mmC型骨架+單面(12mm石膏板+9mm矽酸鈣板),單面(12mm石膏板+9mm矽酸鈣板)	100mm
	65mmC型骨架+雙面15mm石膏板	95mm

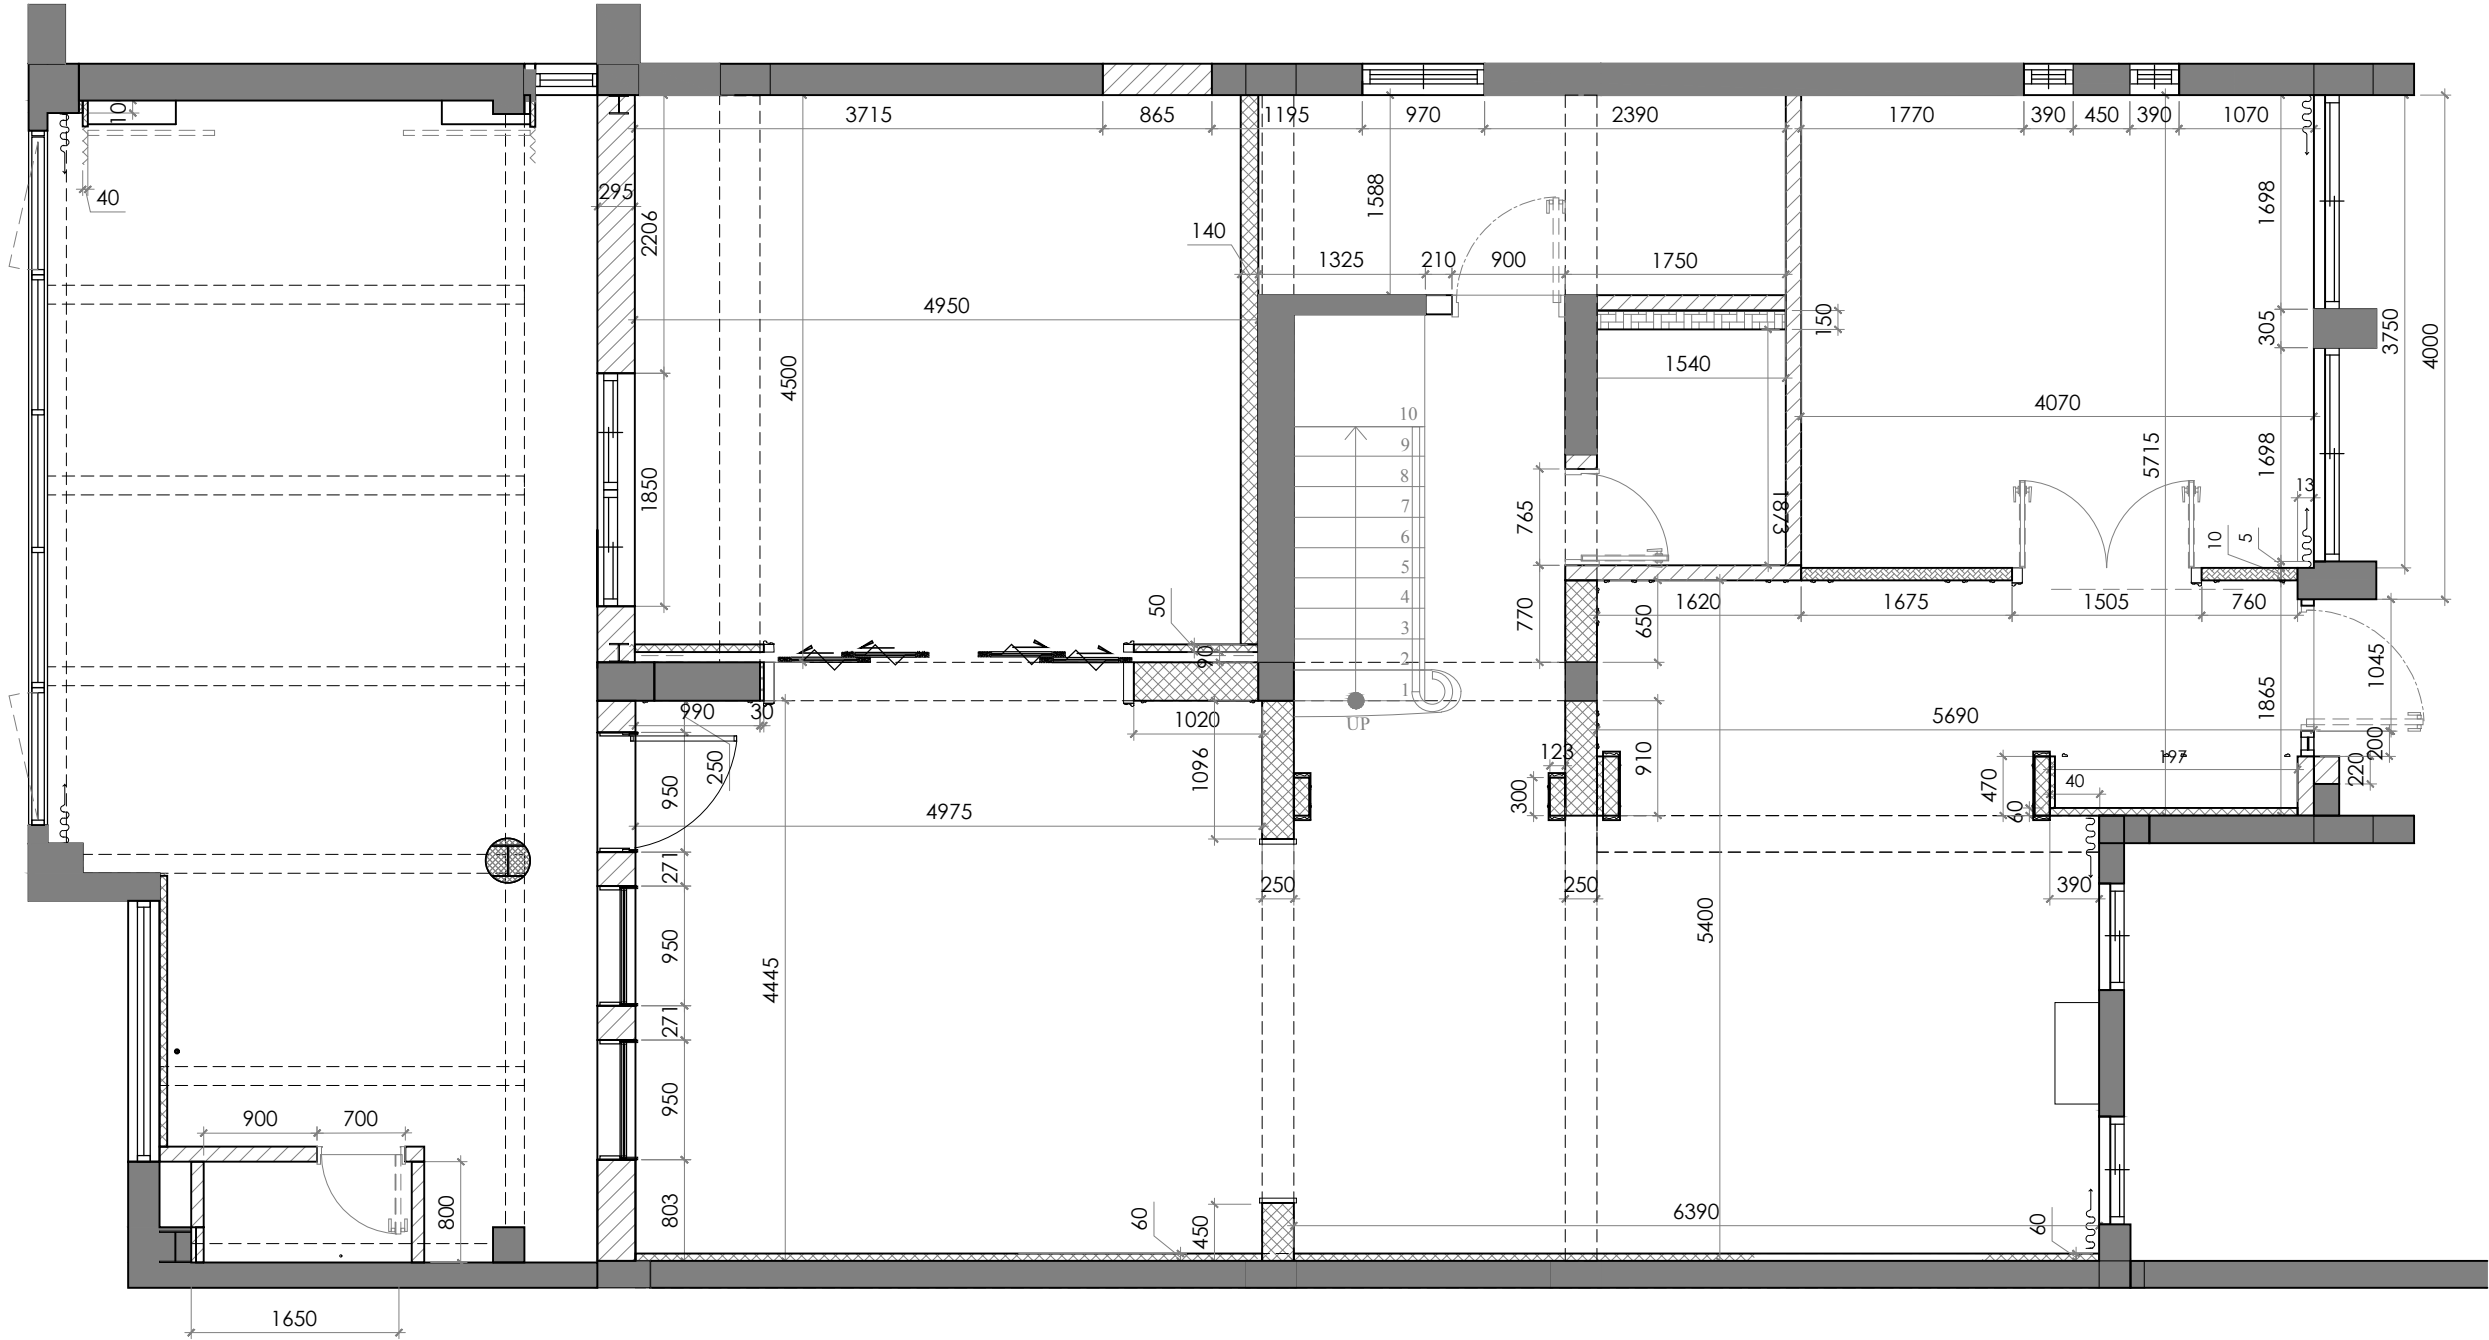

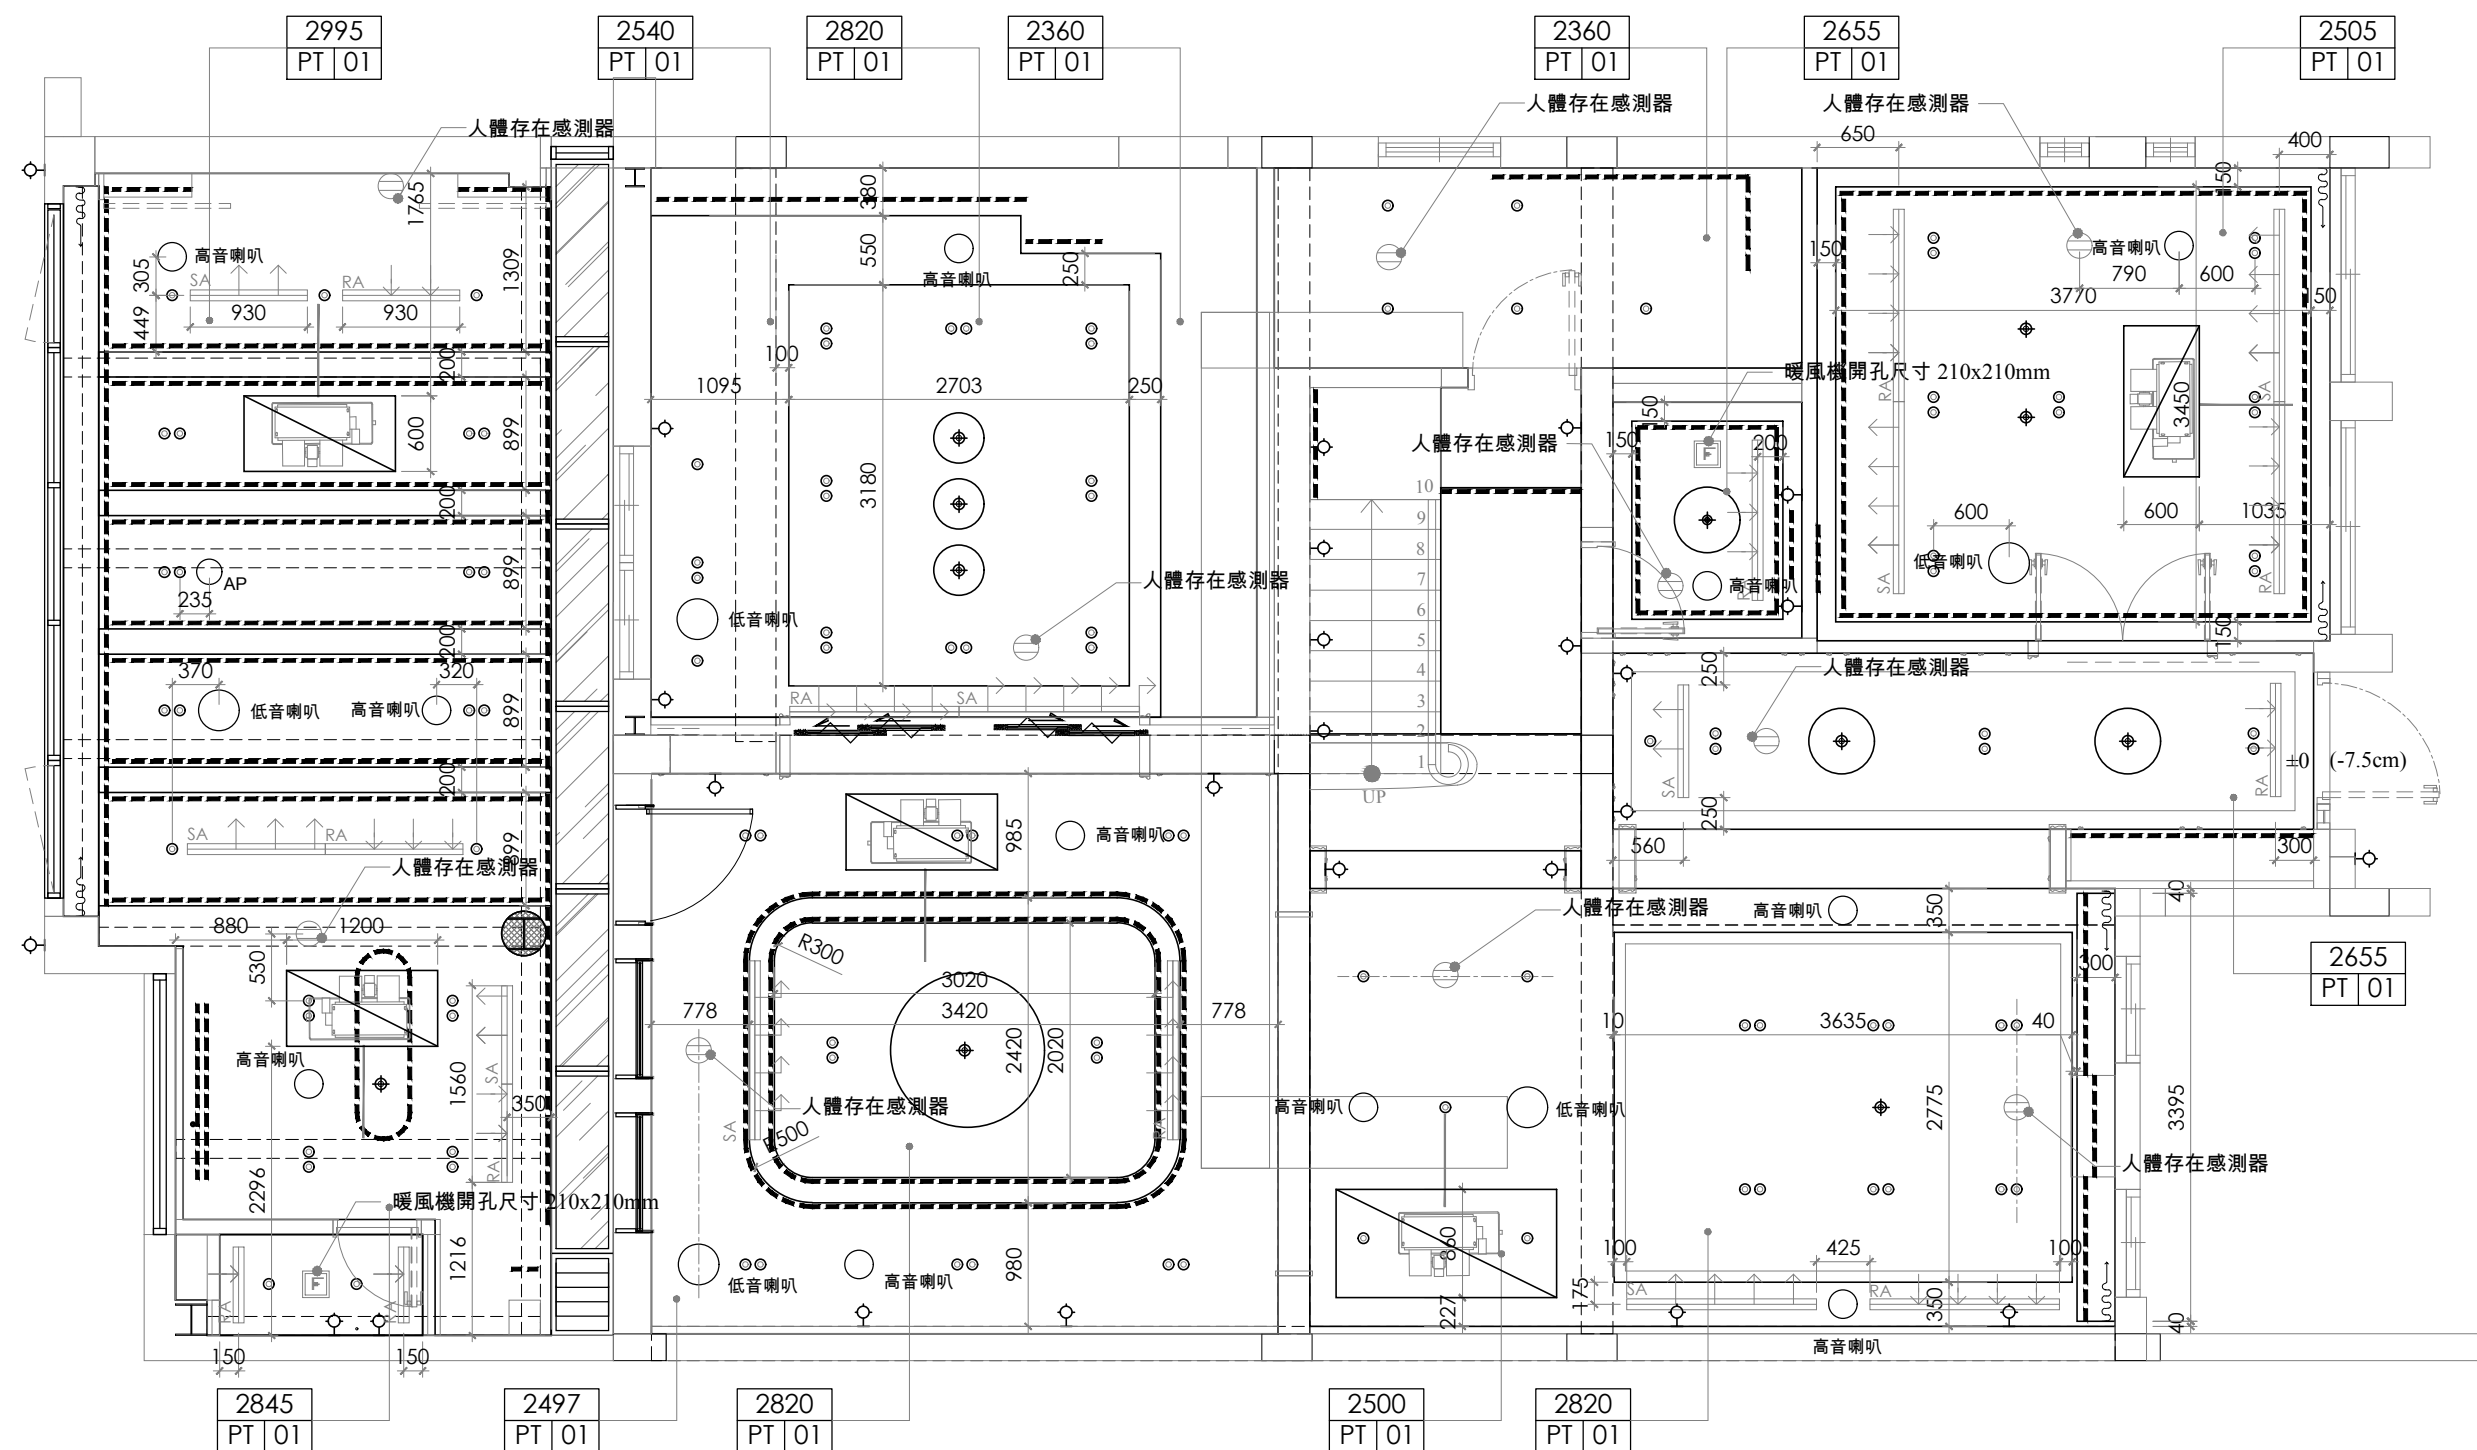

3F, N.26, Ln.290, Guangfu S. Rd., Taipei.
T 886-2-2546-3258
F 886-2-2546-3258
E Guido@mula deco.com

備註:
a.圖面標註尺寸僅供參考，施作均以現場放樣檢討之。
b.圖面標註尺寸、材料及文字敘述因版本不同之差異，均以出圖章後日期之最近為準。
c.電腦圖檔除由合約訂定外，均不得以何方式外洩。
d.圖面所示均為本公司所擁有之智慧財產，切勿以任何方式複製修改。

Revision	Project /


天母葉公館

Job No /
00000
Scale /
1/60 mm

Date /	Approval /
8/10/2026	
Designer /	Drawn By /
Monica Lin	GUIDO

Sheet Title /
1F
天花板造型尺寸圖

Dwg No.
P-03
Page No.
03

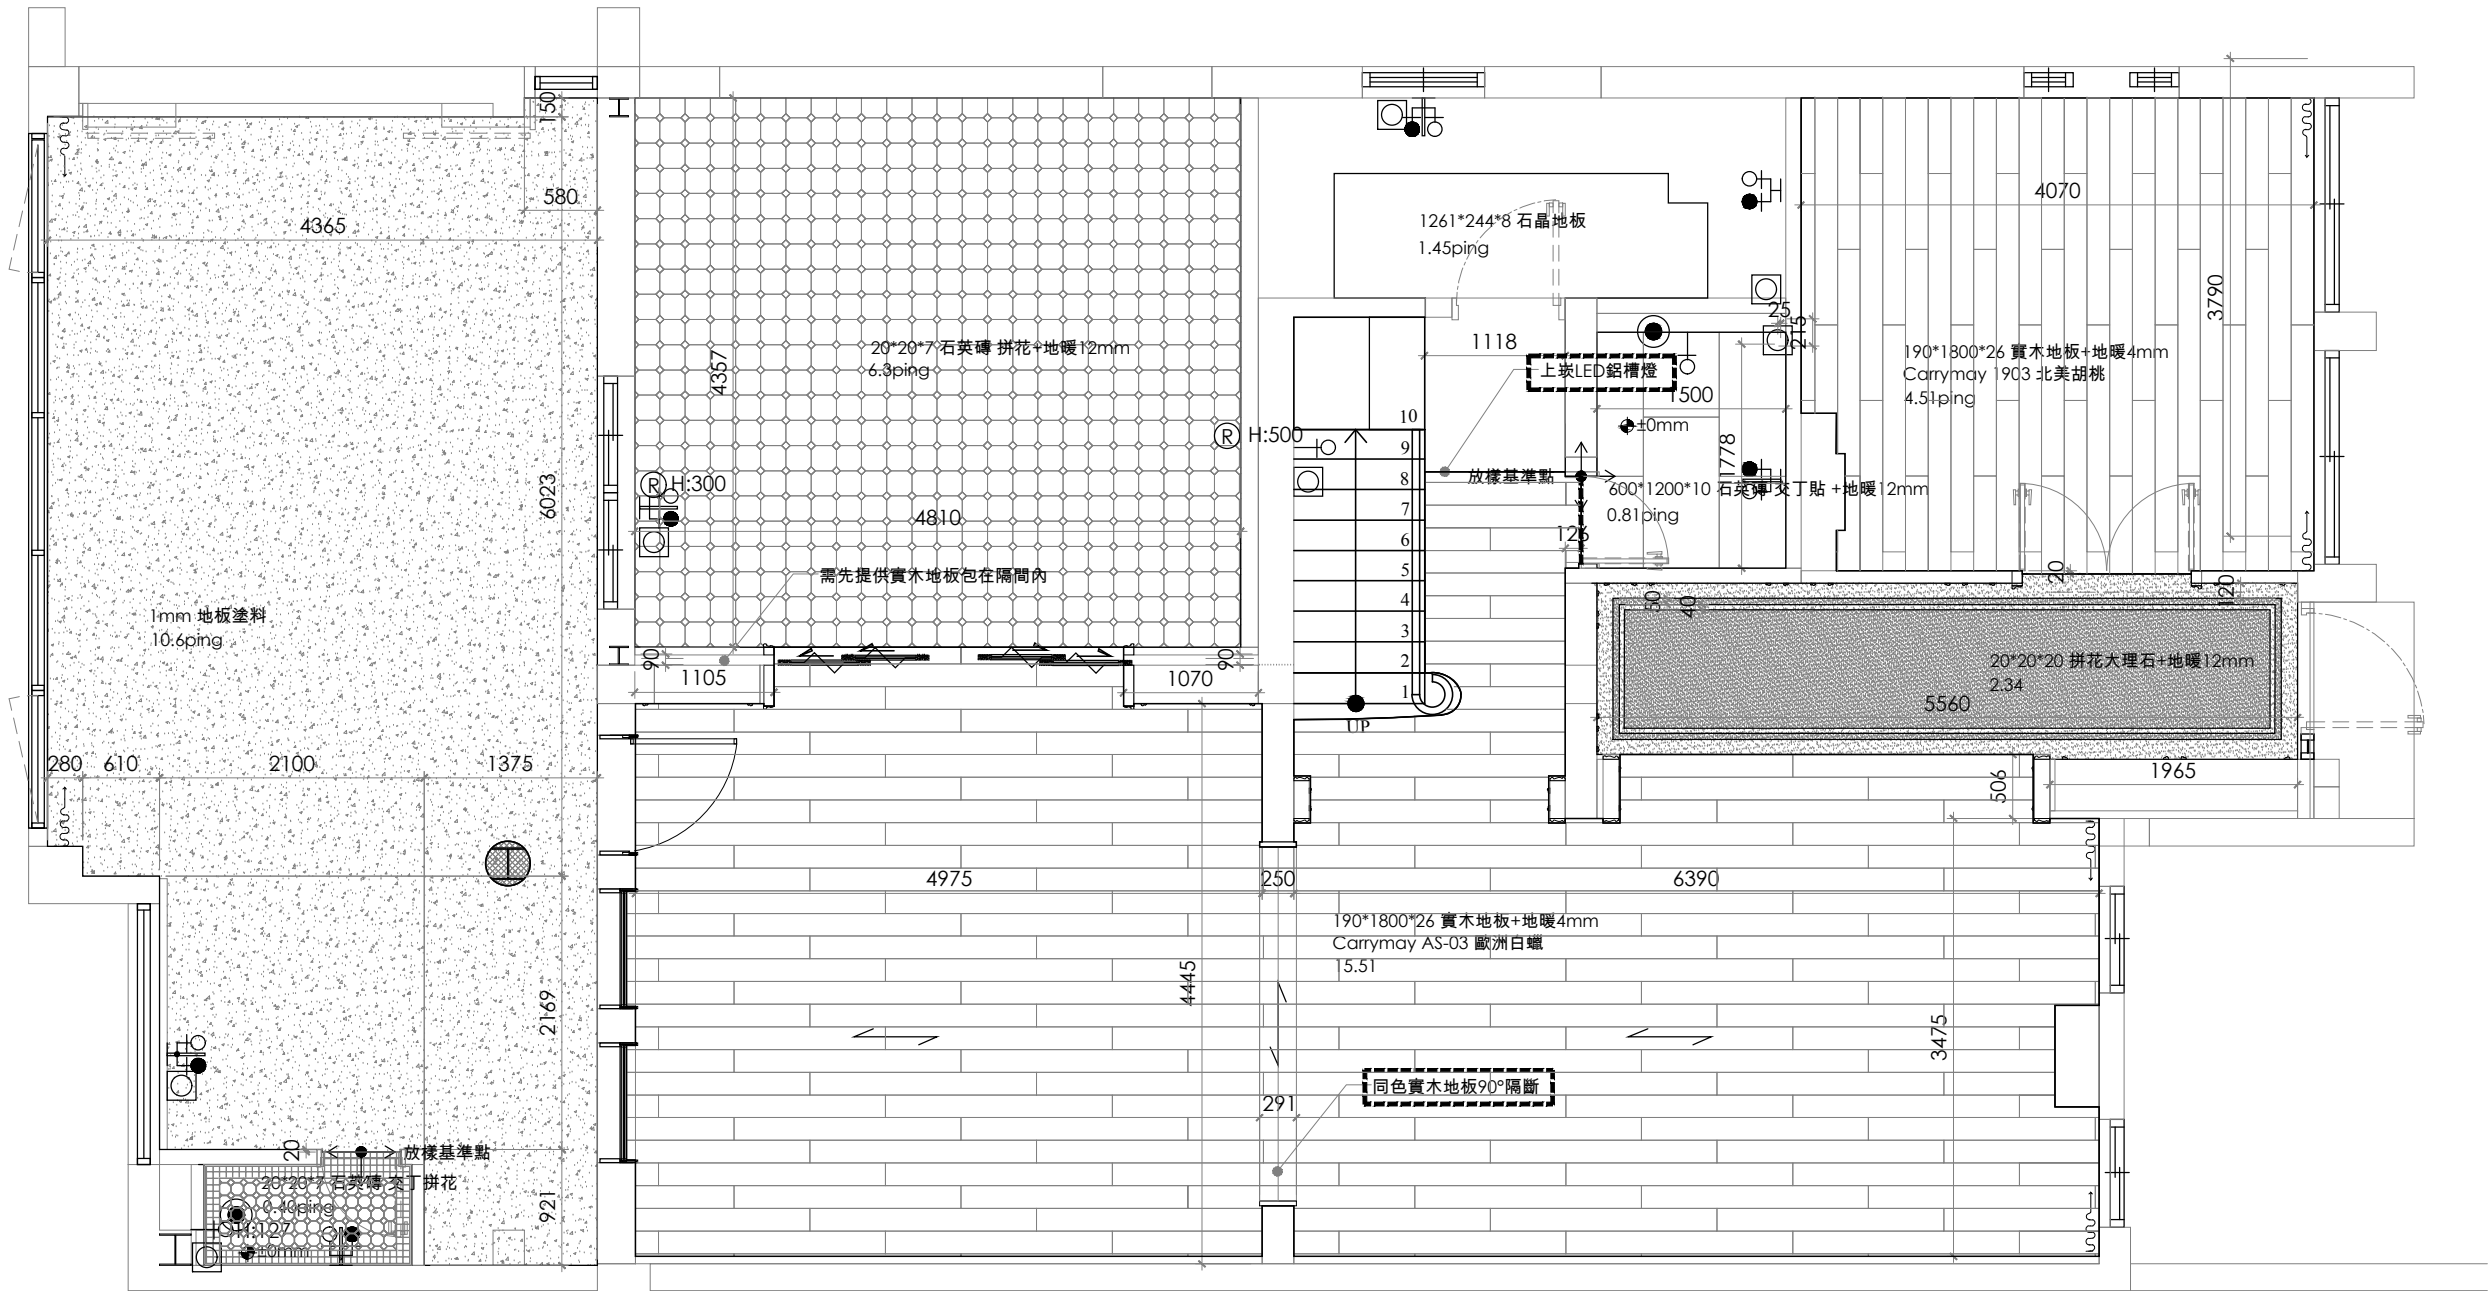

A 3F, N.26, Ln.290, Guangfu S. Rd., Taipei.
T 886-2-2546-3258
F 886-2-2546-3258
E Guido@mula deco.com

備註:
a.圖面標註尺寸僅供參考，施作均以現場放樣檢討之。
b.圖面標註尺寸、材料及文字敘述因版本不同之差異，均以出圖章簽認日期之最近為準。
c.電腦圖檔除由合約訂定外，均不得以何方式外流。
d.圖面所承均為本公司所擁有之智慧財產，切勿以任何方式複製修改。

Revision		

Project /

天母葉公館

Job No /
00000
Scale /
1/60 mm


Date /	Approval /
8/10/2026	
Designer /	Drawn By /
Monica Lin	GUIDO

Sheet Title /
1F
地坪材料尺寸圖

Dwg No.
P-04
Page No.
04


編號	圖示	說明	尺寸	光源	備註
L1	●	COB可調角度嵌燈	88mm Dia x H25mm	KW-303 / 8W / 3000k / 嵌孔75mm	80
L2	●	2線式停電照明嵌燈	105mm Dia x H55mm	FH- 849-1B / 5W / 3000k / 嵌孔93mm	
L3	●	3線式停電照明嵌燈	105mm Dia x H55mm	FH- 849-1B / 5W / 3000k / 嵌孔93mm	
L4	⊕	LED 吸頂燈		3000k	2
L5	●	舞光LED 邱比特軌道燈	W88mm x L115mm x H50mm	AE-B07 / 7W / 3000k / 24°	
L6	●	嵌入式感應式嵌燈	85mm Dia x H50mm	3000k / 嵌孔75mm	
L7	-----	LED軟條燈		3000k	
L8	-----	軌道燈軌道	W34mm x H20mm		
*燈具相關設備,需詳燈具規範最後確認。 *燈具供電皆為110V。					

編號	圖示	說明	尺寸	光源	備註
L9	●	COB小型可調角度嵌燈	63mm Dia x H72mm	3000k / 嵌孔55mm	3
L10	□	無邊框可調角LED單燈盒燈	W99mm x L99mm x H85mm	FH- 829-11C /10W /30° / 3000K	6
L11	▢	無邊框可調角LED雙燈盒燈	W99mm x L199mm x H85mm	FH- 829-12C /10W /30° / 3000K	
L12	— · — · —	磁吸式軌道燈			
L13	=====	防塵防濕T5燈具			
L14	●	上照LED埋地燈	42mm Dia. x H90mm	LED /3W /12° /12V /3000K / 700mA	10
DL-1	◆	吊燈			16
DL-2	♀	壁燈			31
*燈具相關設備,需詳燈具規範最後確認。 *燈具供電皆為110V。					

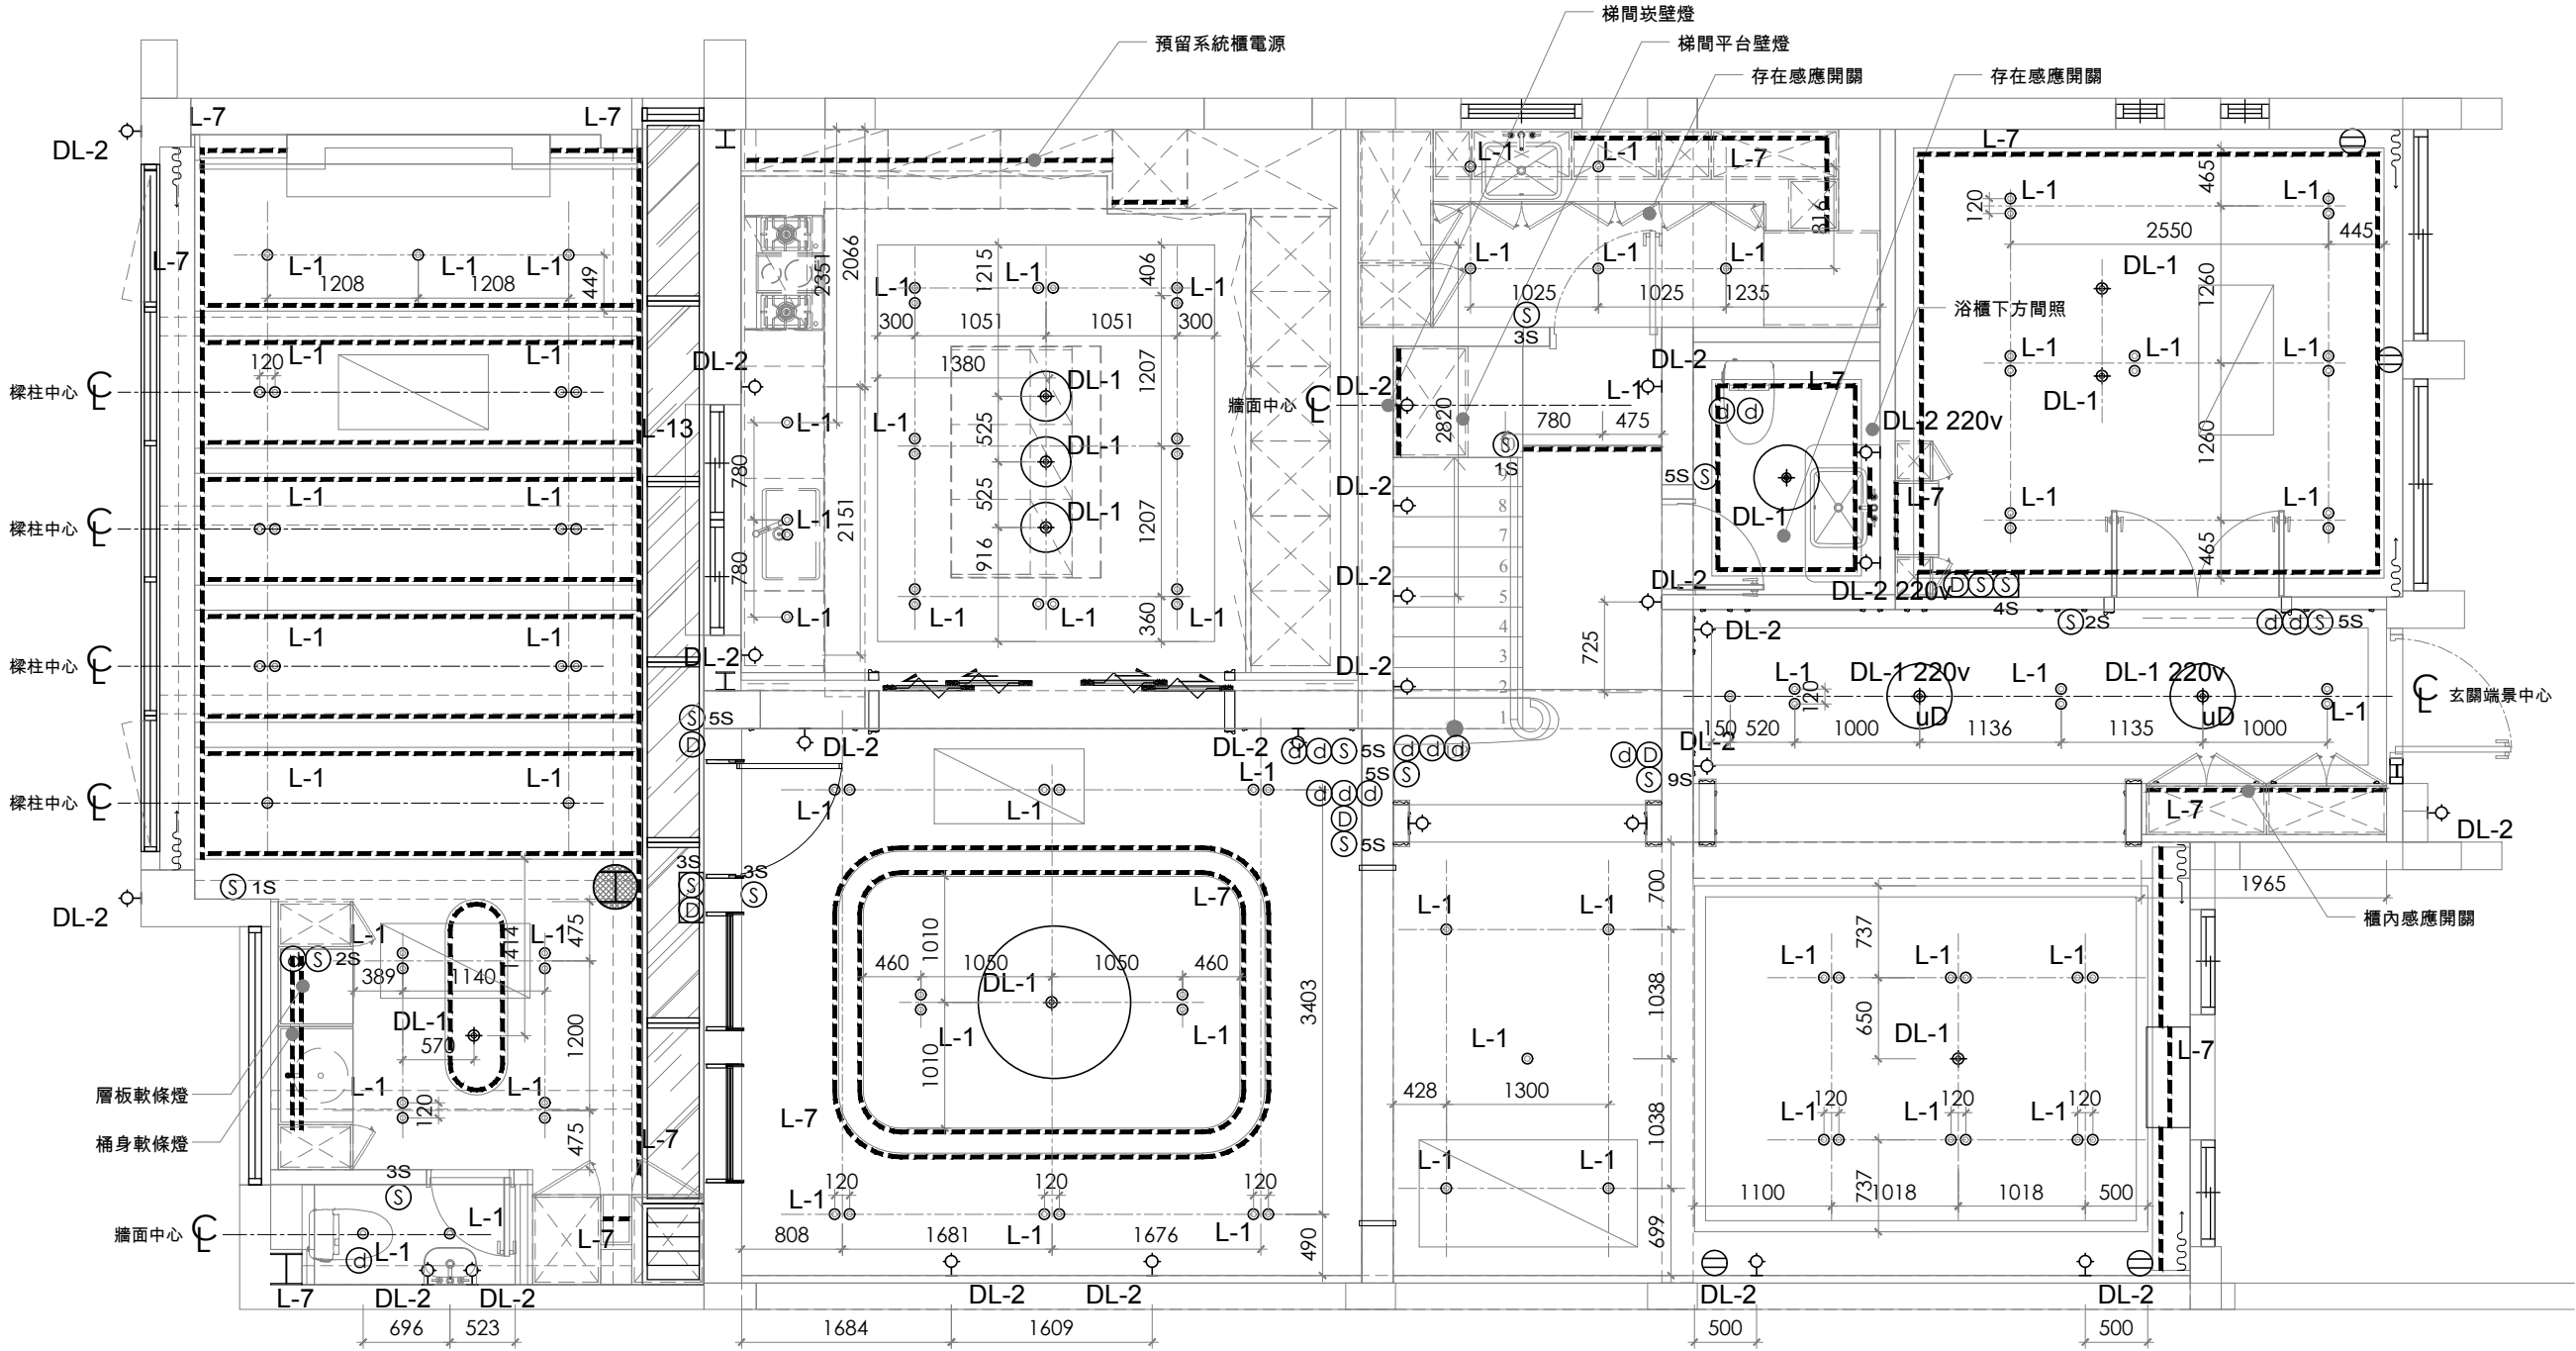


編號	圖示	說明	尺寸	光源	備註
L1	◦	COB可調角度嵌燈	88mm Dia x H25mm	KW-303 / 8W / 3000k / 嵌孔75mm	80
L2	●	2線式停電照明嵌燈	105mm Dia x H55mm	FH- 849-1B / 5W / 3000k / 嵌孔93mm	
L3	●	3線式停電照明嵌燈	105mm Dia x H55mm	FH- 849-1B / 5W / 3000k / 嵌孔93mm	
L4	⊕	LED 吸頂燈		3000k	2
L5	⊙	舞光LED 邱比特軌道燈	W88mm x L115mm x H50mm	AE-B07 / 7W / 3000k / 24°	
L6	⊙	嵌入式感應式嵌燈	85mm Dia x H50mm	3000k / 嵌孔75mm	
L7	-----	LED軟條燈		3000k	
L8	-----	軌道燈軌道	W34mm x H20mm		
*燈具相關設備,需詳燈具規範最後確認。 *燈具供電皆為110V。					

編號	圖示	說明	尺寸	光源	備註
L9	●	COB小型可調角度嵌燈	63mm Dia x H72mm	3000k / 嵌孔55mm	3
L10	□	無邊框可調角LED單燈盒燈	W99mm x L99mm x H85mm	FH- 829-11C /10W /30° / 3000K	6
L11	▣	無邊框可調角LED雙燈盒燈	W99mm x L199mm x H85mm	FH- 829-12C /10W /30° / 3000K	
L12	— · — · —	磁吸式軌道燈			
L13	▬	防塵防濕T5燈具			
L14	◦	上照LED埋地燈	42mm Dia. x H90mm	LED /3W /12° /12V /3000K / 700mA	10
DL-1	◆	吊燈			16
DL-2	♀	壁燈			31
*燈具相關設備,需詳燈具規範最後確認。 *燈具供電皆為110V。					

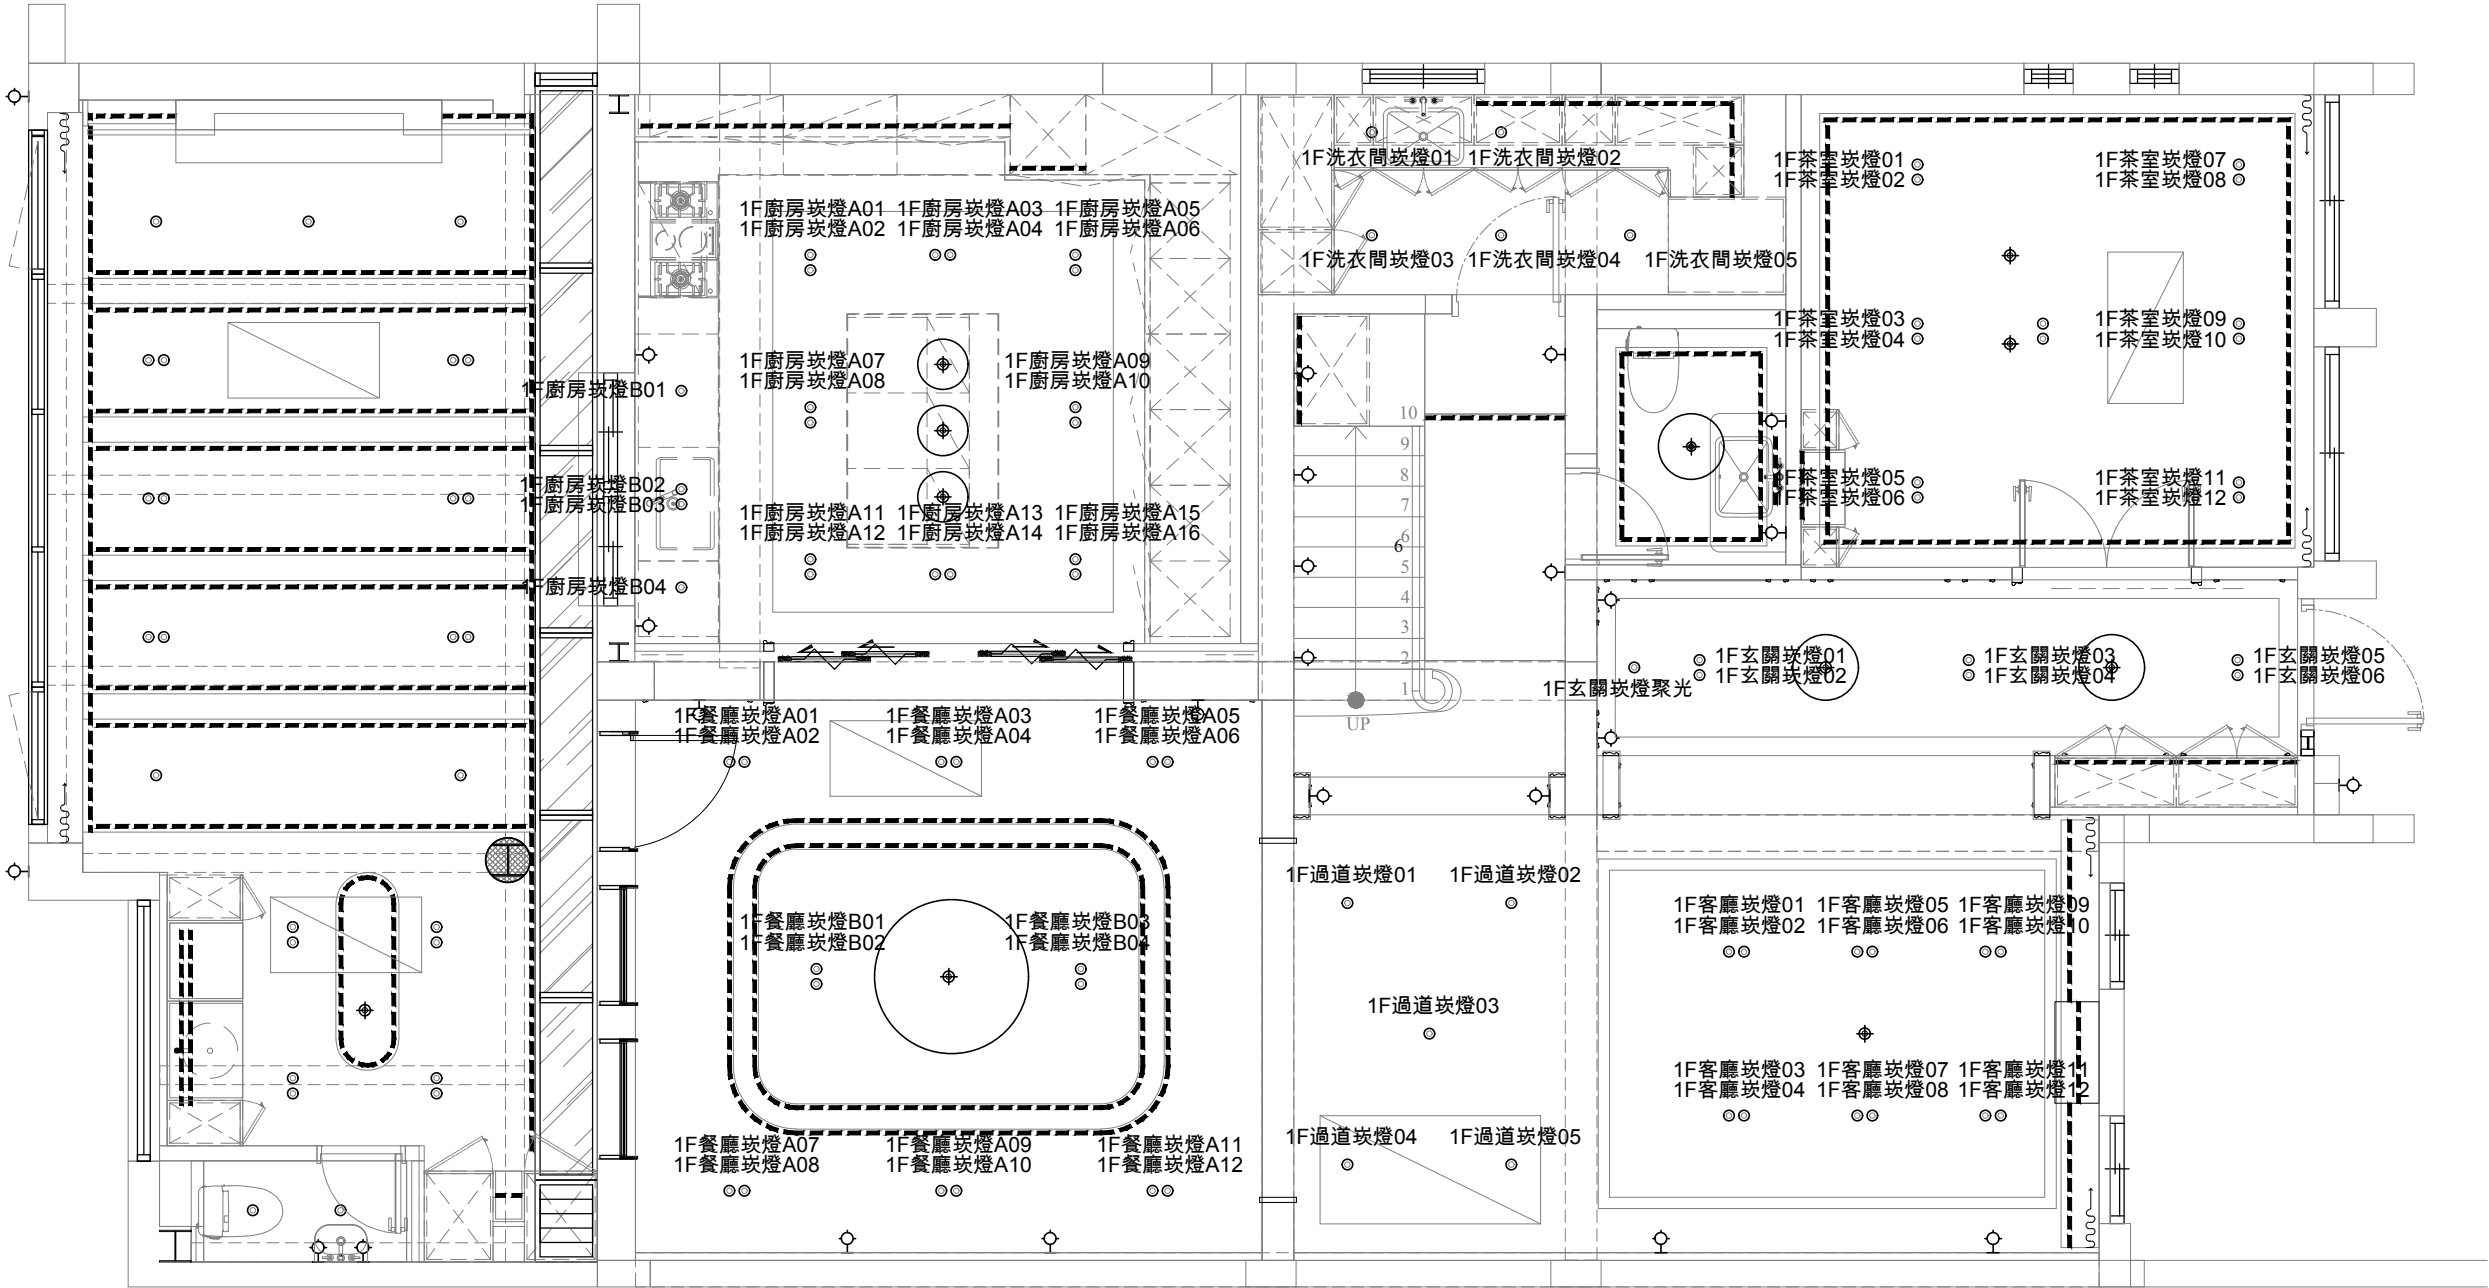


編號	圖示	說明	尺寸	光源	備註
L1	○	COB可調角度嵌燈	88mm Dia x H25mm	KW-303 / 8W / 3000k / 嵌孔75mm	80
L2	●	2線式停電照明嵌燈	105mm Dia x H55mm	FH- 849-1B / 5W / 3000k / 嵌孔93mm	
L3	●	3線式停電照明嵌燈	105mm Dia x H55mm	FH- 849-1B / 5W / 3000k / 嵌孔93mm	
L4	⊕	LED 吸頂燈		3000k	2
L5	⦿	舞光LED 邱比特軌道燈	W88mm x L115mm x H50mm	AE-B07 / 7W / 3000k / 24°	
L6	⦿	嵌入式感應式嵌燈	85mm Dia x H50mm	3000k / 嵌孔75mm	
L7	-----	LED軟條燈		3000k	
L8	-----	軌道燈軌道	W34mm x H20mm		
*燈具相關設備,需詳燈具規範最後確認。 *燈具供電皆為110V.					


編號	圖示	說明	尺寸	光源	備註
L9	●	COB小型可調角度嵌燈	63mm Dia x H72mm	3000k / 嵌孔55mm	3
L10	□	無邊框可調角LED單燈盒燈	W99mm x L99mm x H85mm	FH- 829-11C /10W /30° / 3000K	6
L11	▣	無邊框可調角LED雙燈盒燈	W99mm x L199mm x H85mm	FH- 829-12C /10W /30° / 3000K	
L12	— · — · —	磁吸式軌道燈			
L13	=====	防塵防濕T5燈具			
L14	◦	上照LED埋地燈	42mm Dia. x H90mm	LED /3W /12° /12V /3000K / 700mA	10
DL-1	◆	吊燈			16
DL-2	♀	壁燈			31
*燈具相關設備,需詳燈具規範最後確認。 *燈具供電皆為110V.					

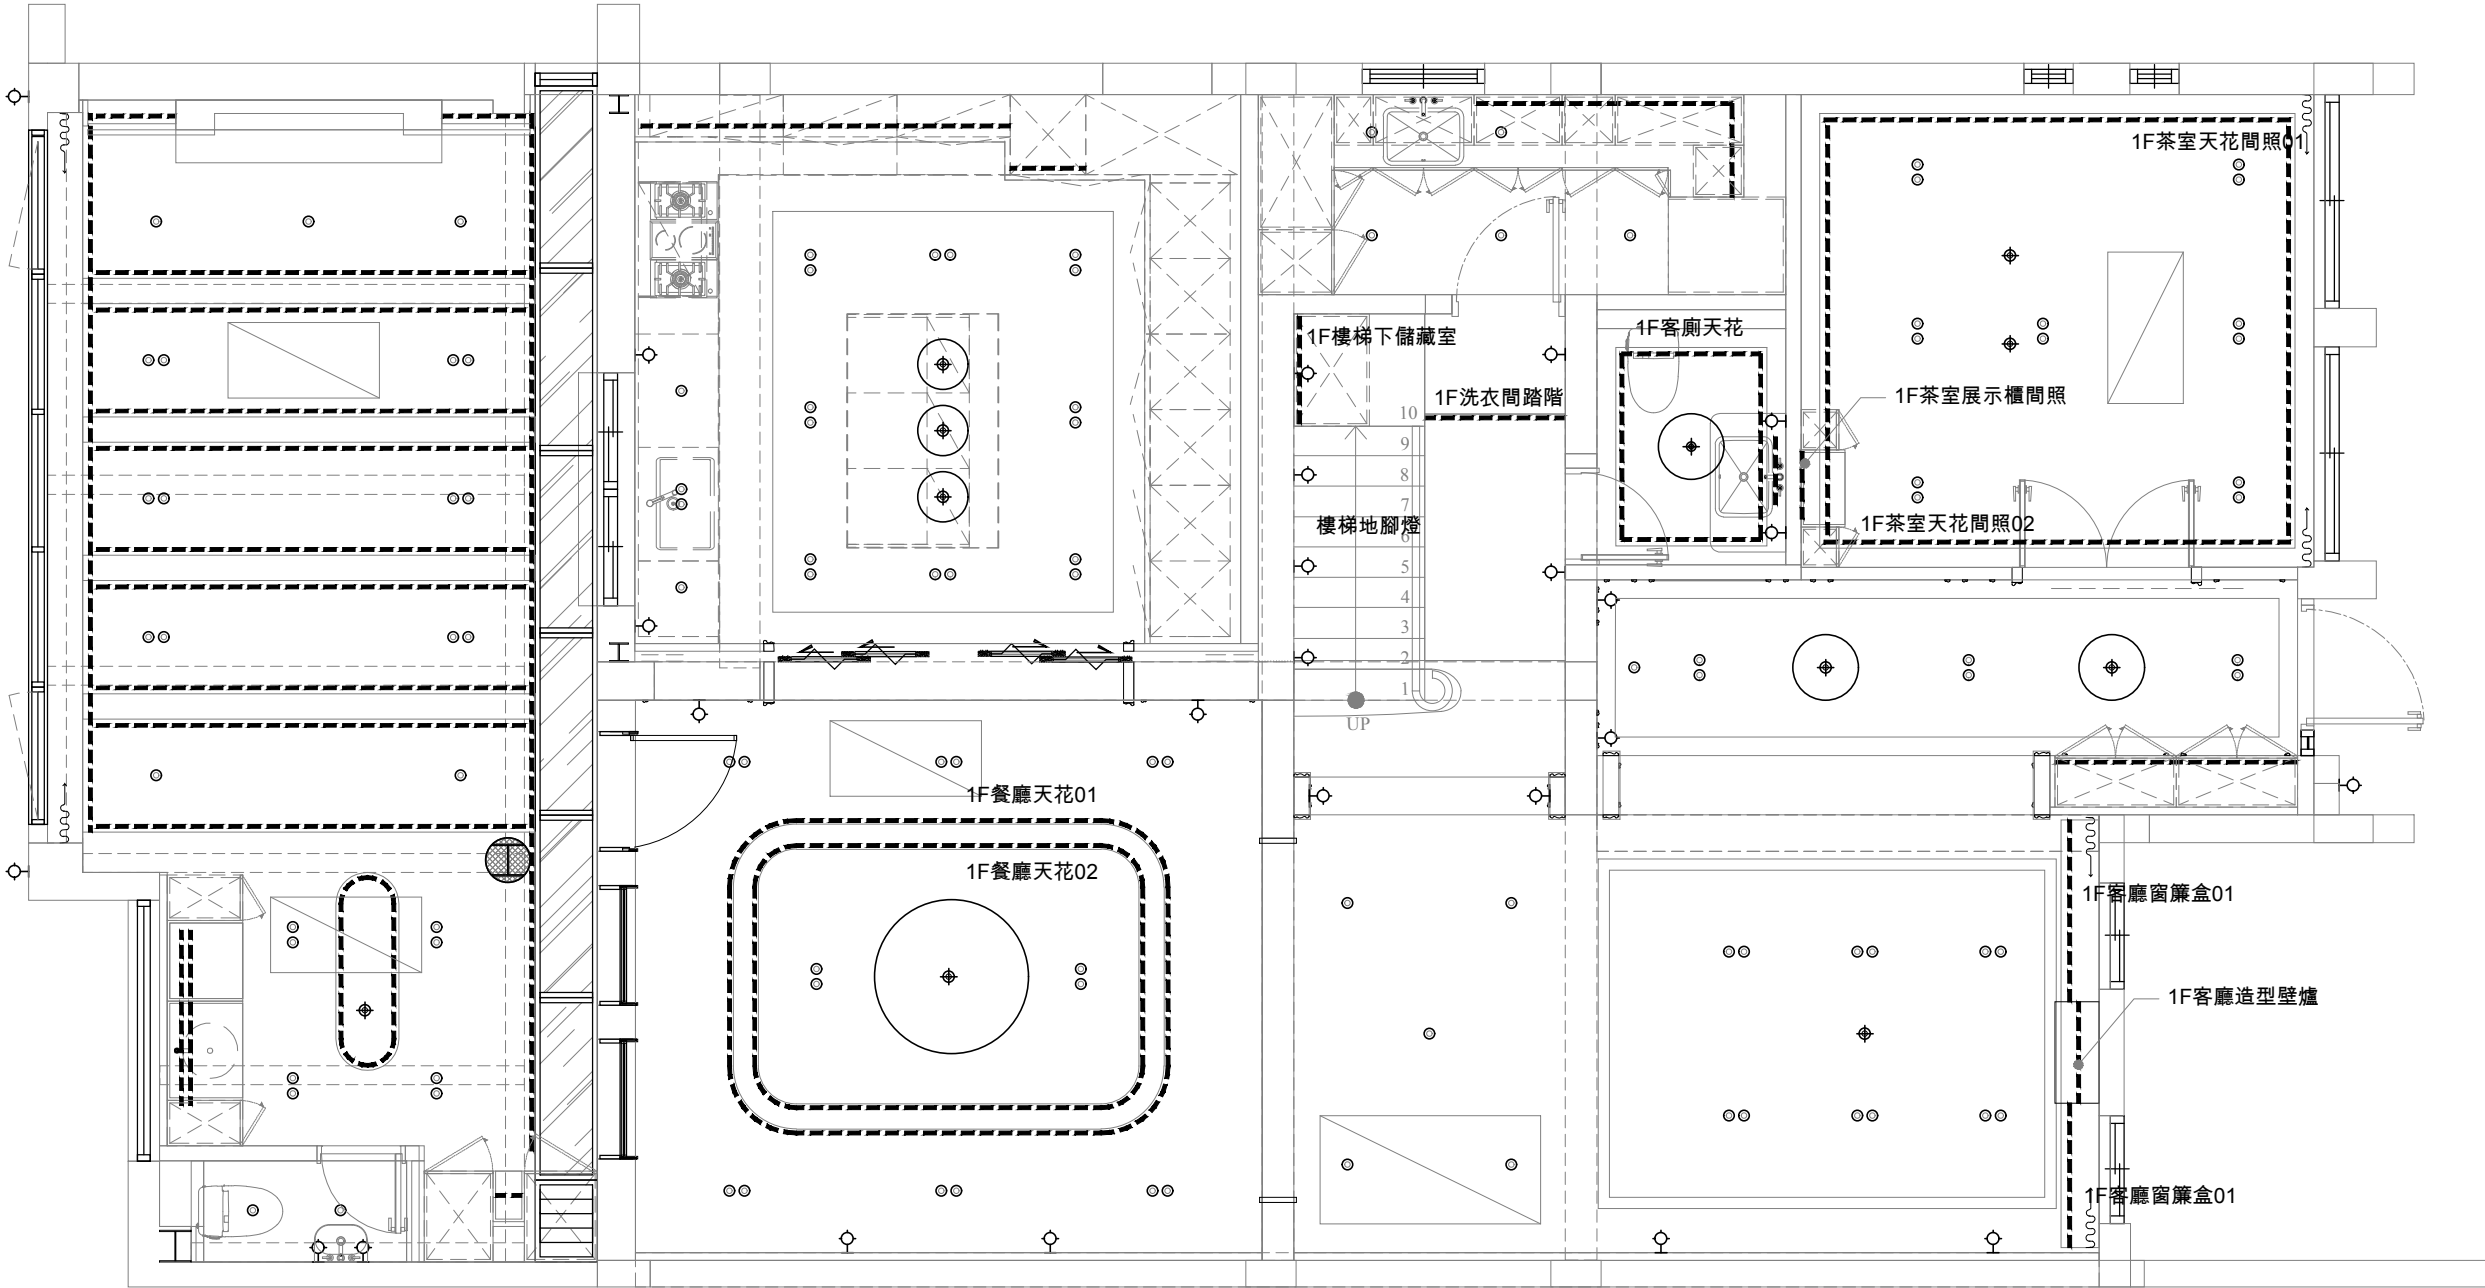


弱電設備圖例說明								
圖例	說 明	數 量	圖例	說 明	數 量	圖例	說 明	數 量
⊖	插座(110V雙插座)	62	Ⓢ	資訊插座	22	Ⓜ	HDMI插座	2
⊖	插座(220V雙插座)	4	Ⓢ	燈具開關	26	BT	對講機	1
Ⓜ	地板插座(110V雙插座)	1	Ⓢ	調光開關	11	ID	門禁刷卡器	2
Ⓜ	不斷電插座(110V雙插座)		Ⓢ	機械式調光開關		■	配電盤	2
Ⓢ	獨立電源	28	AL	音響出線	15	AL	音響地面出線	
①	電話插座	2	Ⓢ	電源出線口	55	A	空調開關	5
☒	智能控制面板		■	地板電源出線	12	Ⓢ	除濕機開關	1
TV	電視插座		Ⓢ	暖風機開關	2	FH	地暖控制面板	6
備註		1.插座、燈具出線口詳細位置尺寸、高度詳裝修圖。 2.所有壁面插座,除特別標示高度者之外,中心點一律離地完成面+300AFF。 3.所有壁面開關,除特別標示高度者之外,中心點一律離地完成面+1200AFF。 4.所有配管、線均由平頂天花配置。 5.影音視聽系統所需弱電設備,由影音視聽系統廠商規劃後,提供圖面予業主審核。						

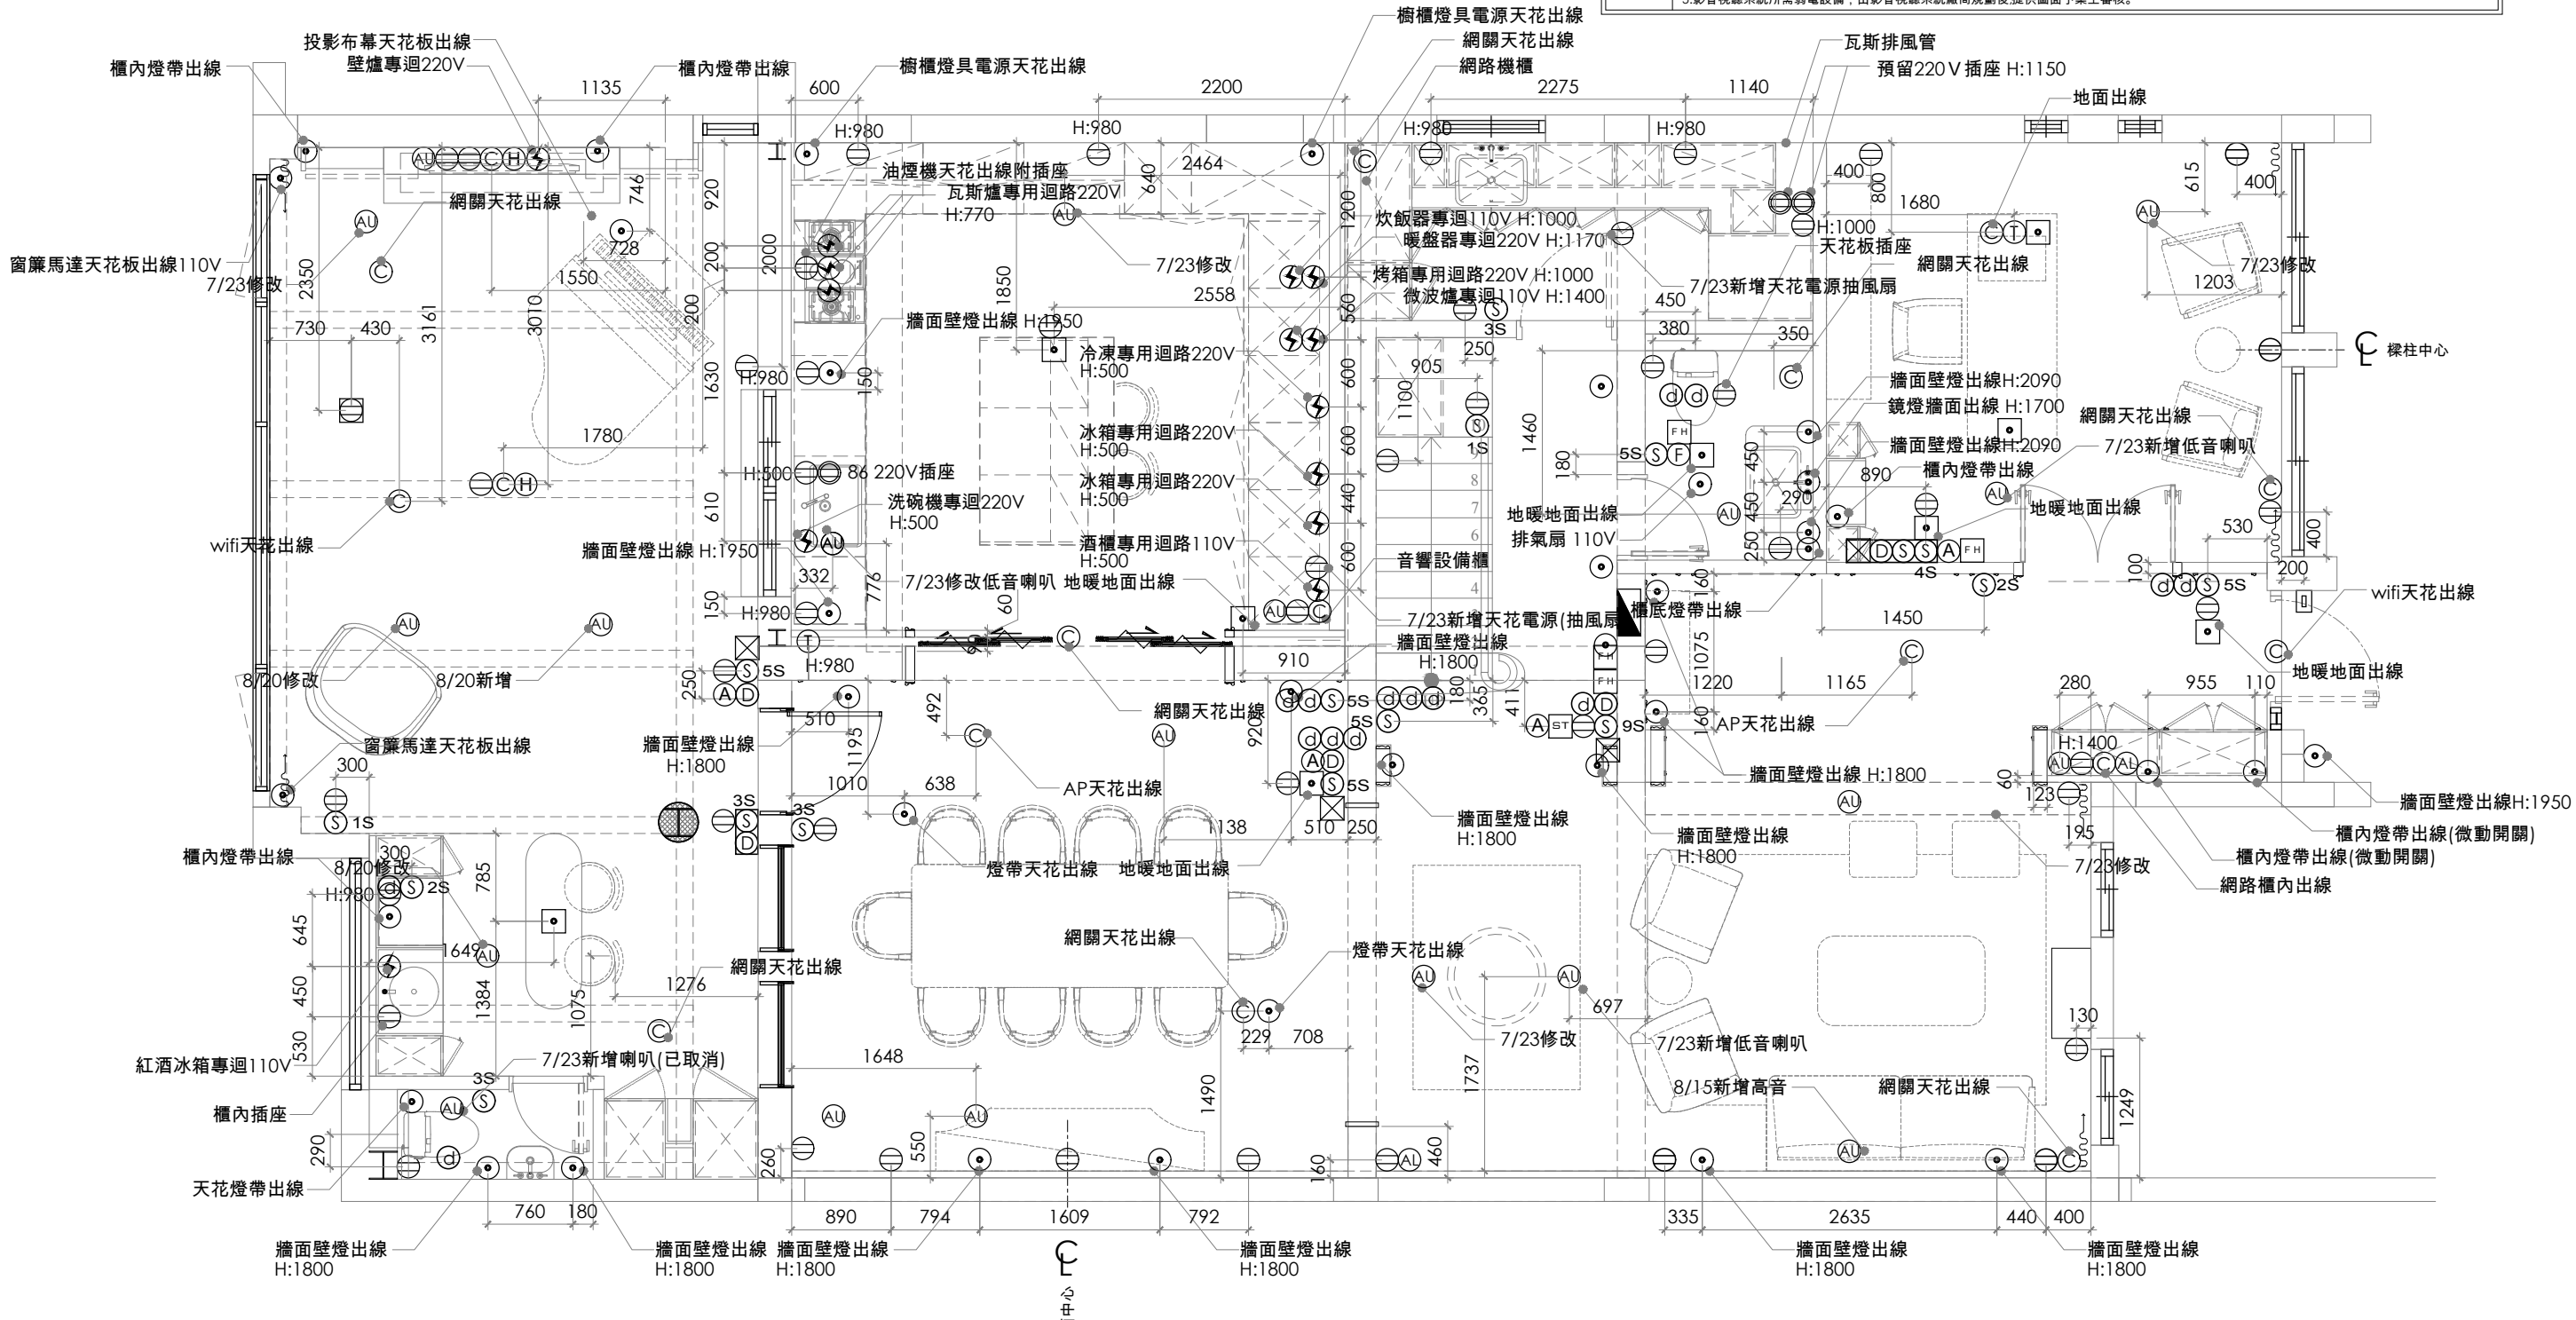


空調設備圖例說明			
圖 例	說 明	圖 例	說 明
	側吹出風口		出風口
	側吹回風口		吊隱式除濕主機
	下吹出風口		五合一暖風機
	下吹回風口		全熱交換器
	空調維修孔		

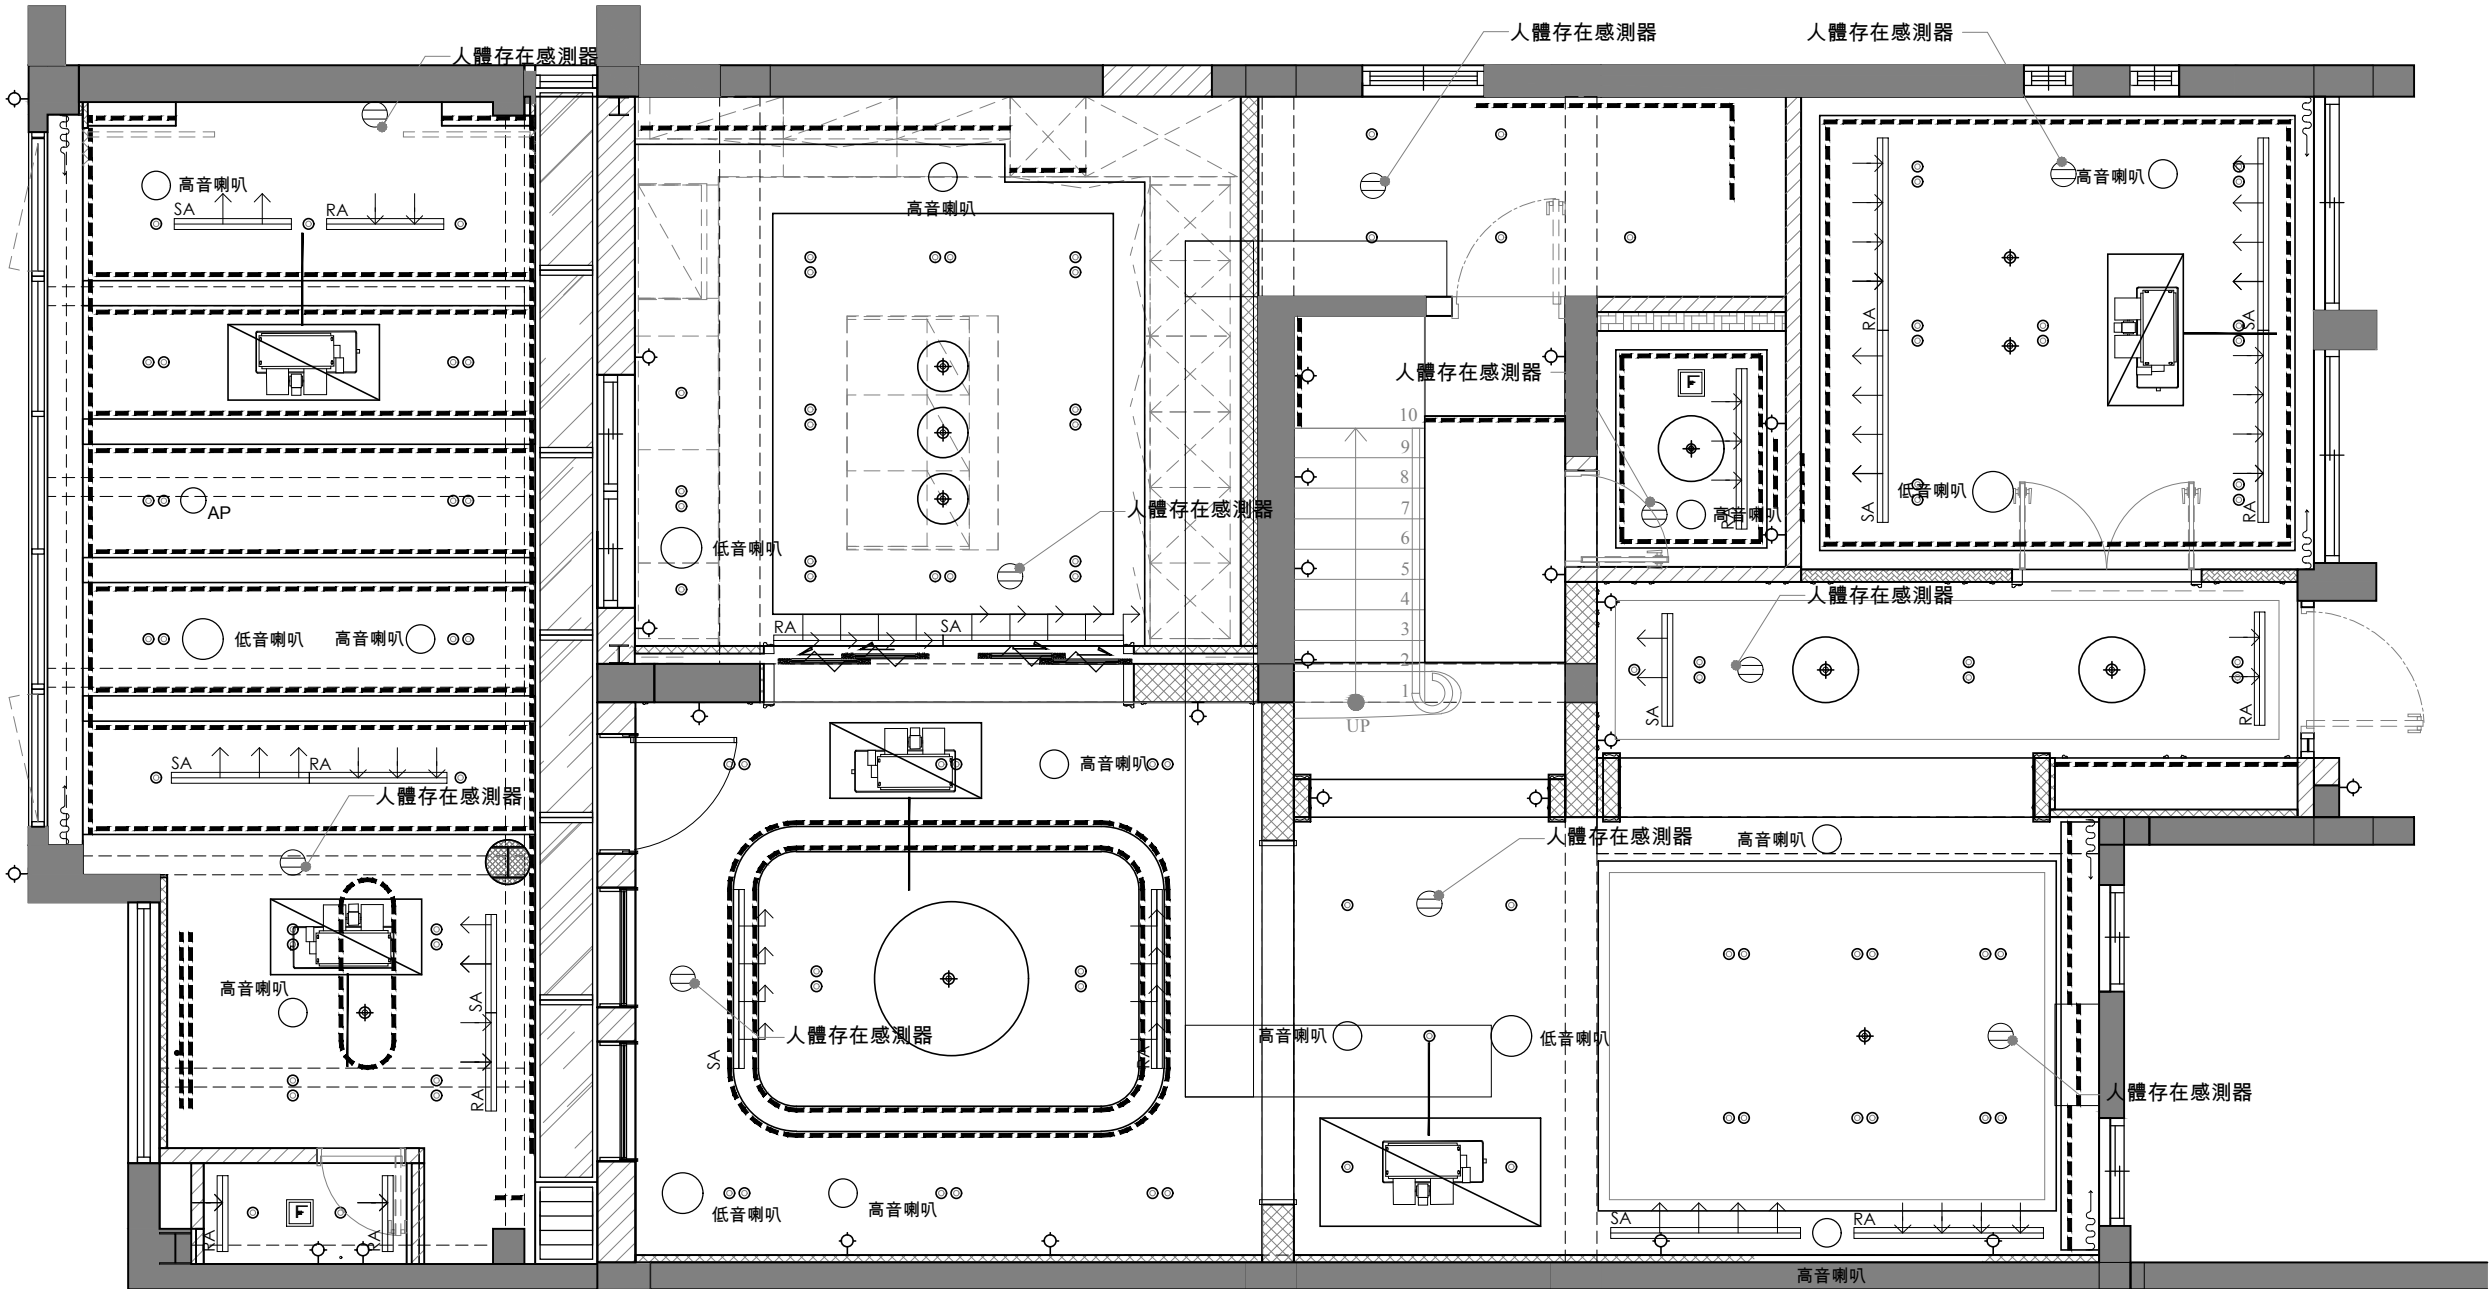

給排水設備圖例說明表			
圖例	說 明	規格	高度
—○	壁面冷給水		
—●	壁面熱給水		
H○●	壁面冷熱給水		
H○●	壁面冷熱給水及排水		
□	地板排水口		
●	糞管		
Ⓡ	RO進水管		
備註	1.淋浴間,蓮蓬頭出水口+2100AFF。 2.淋浴間,蓮蓬頭出水口+2100AFF		

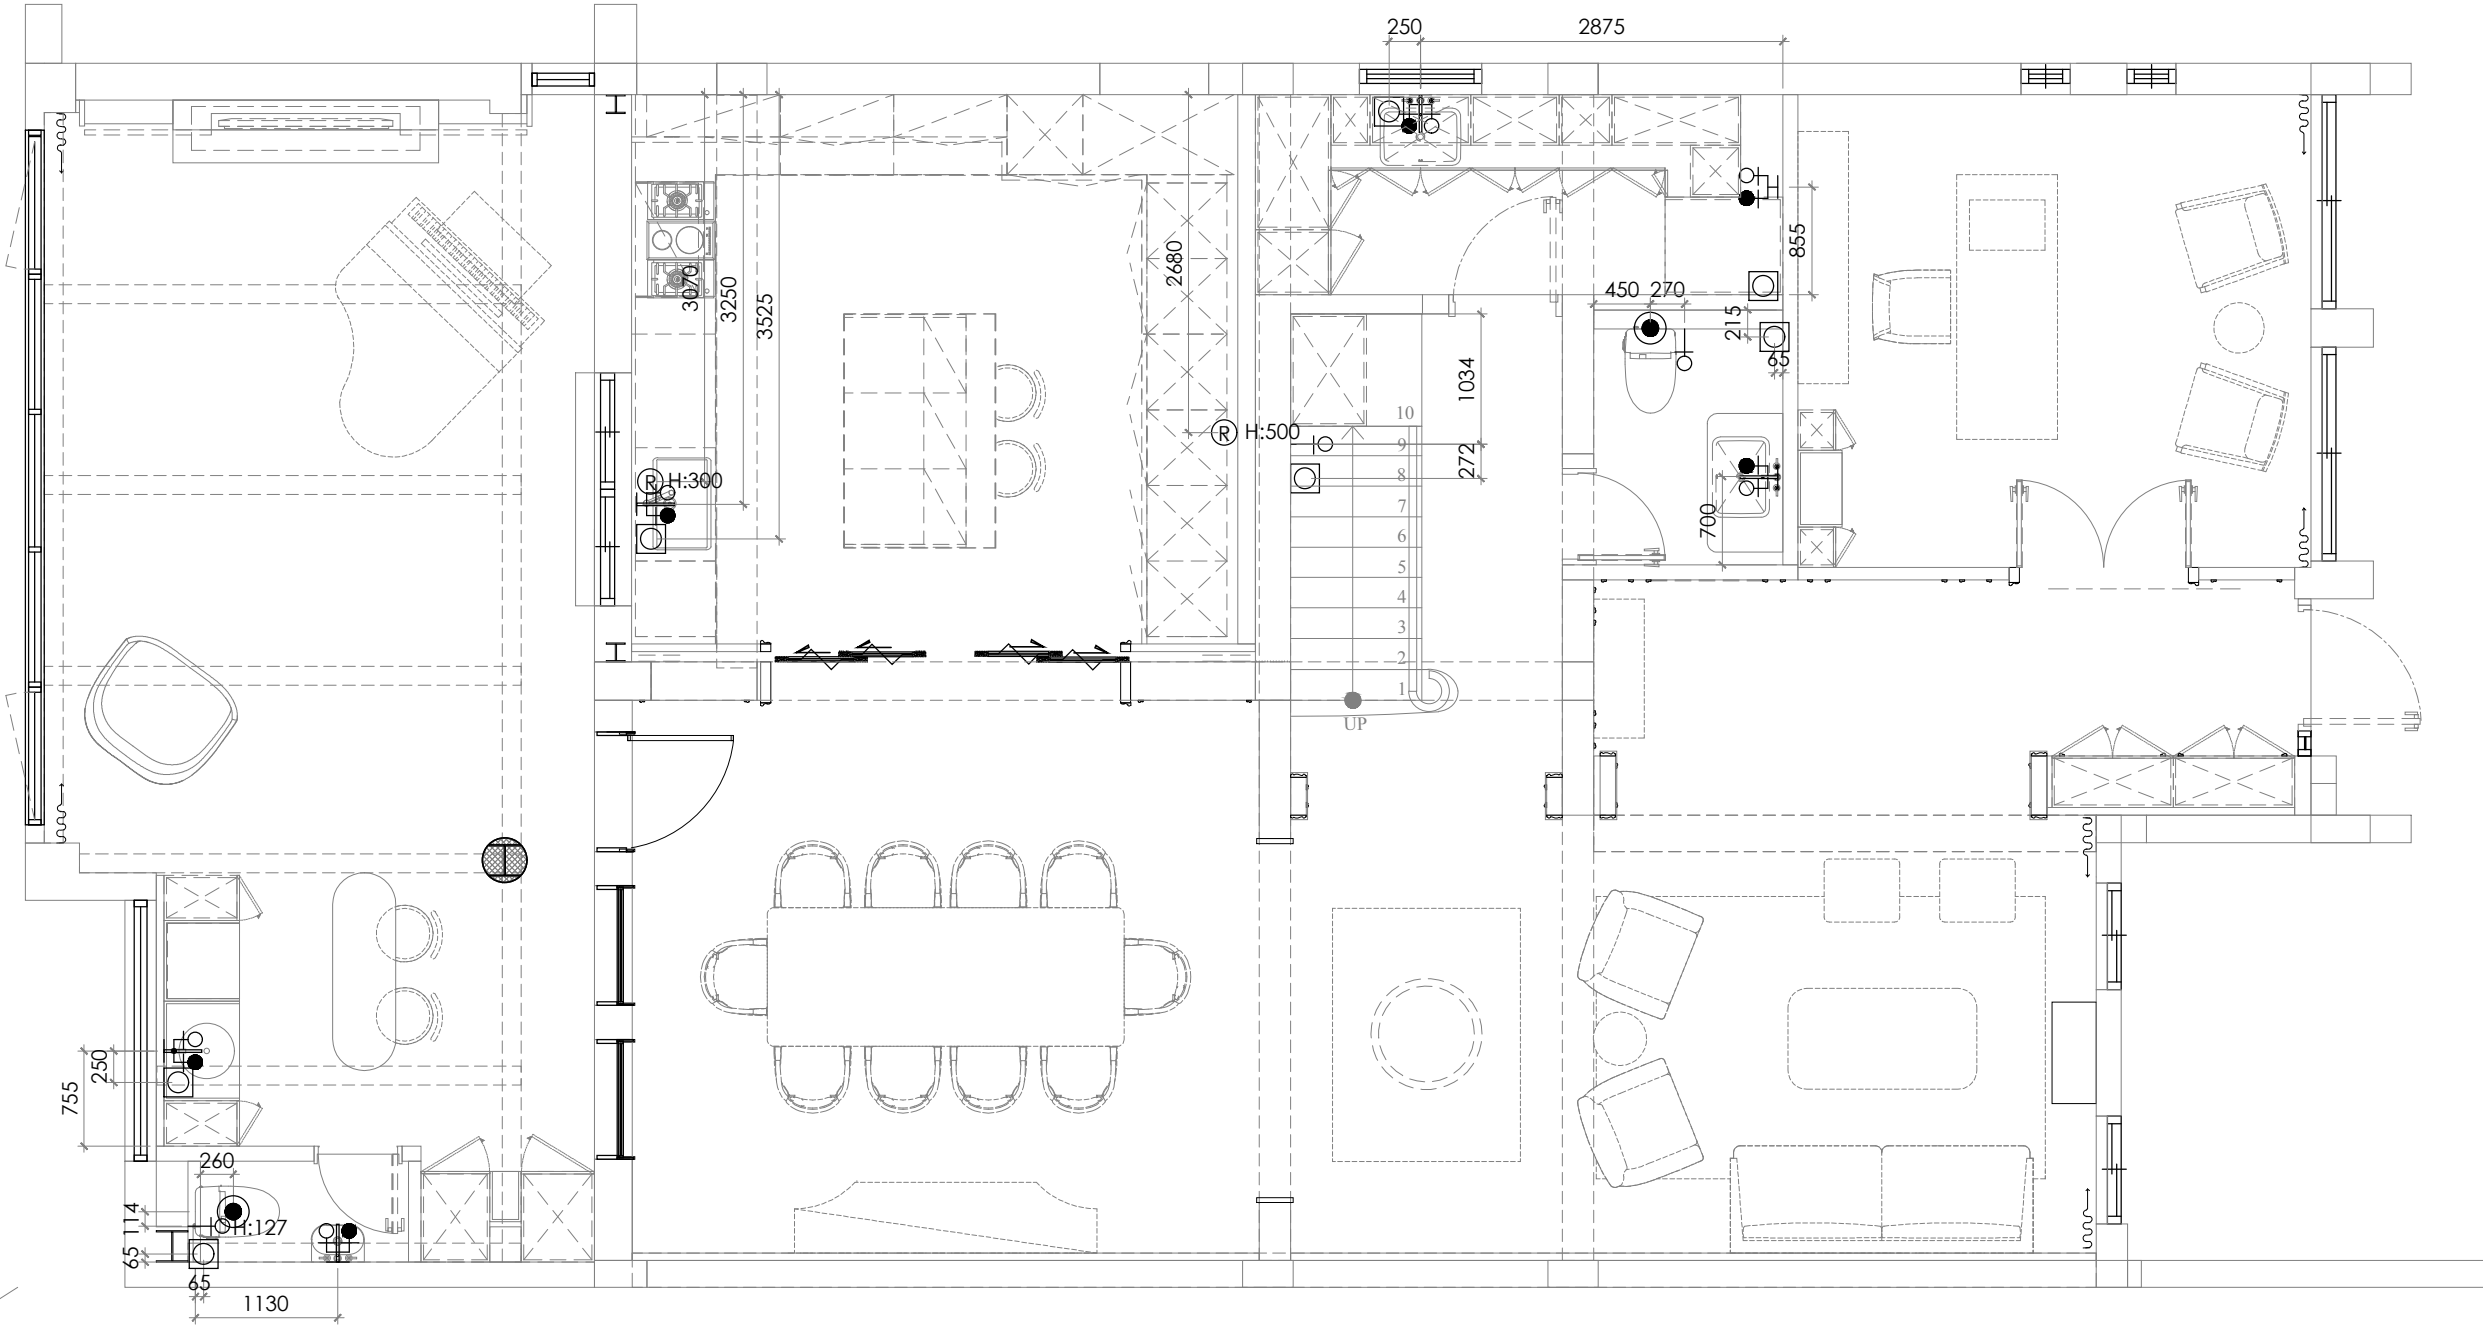

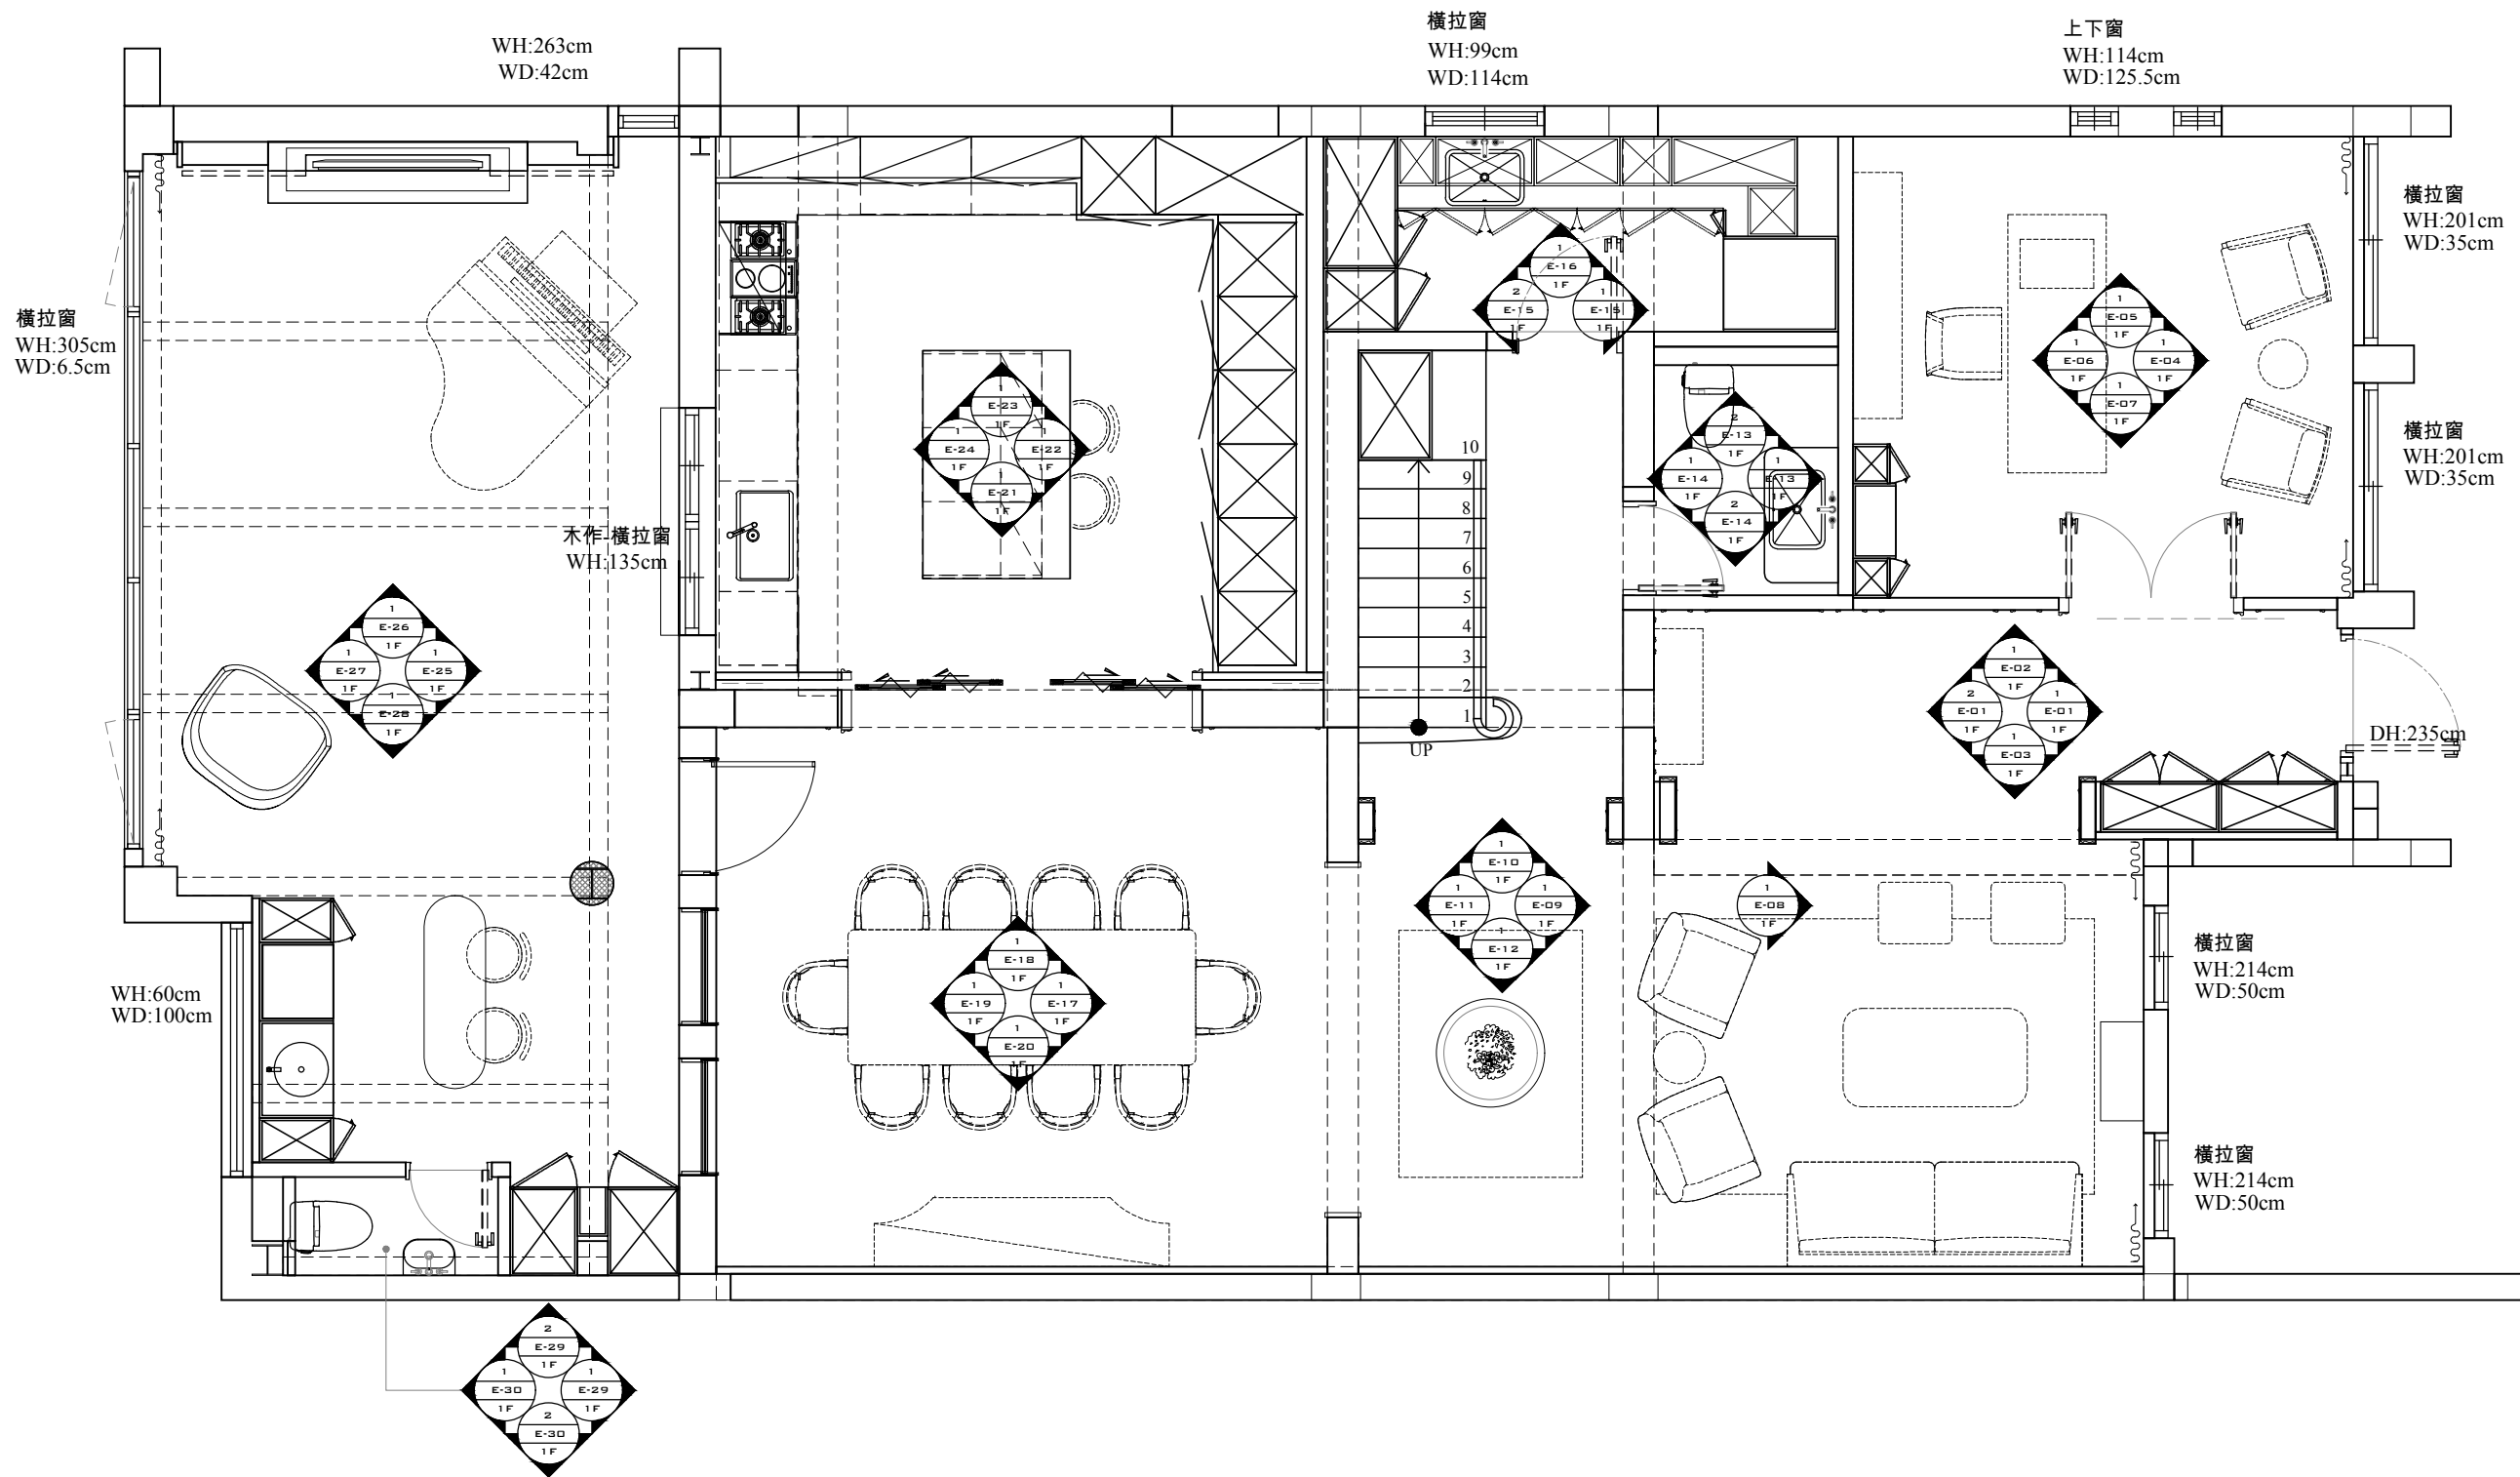

A 3F, N.26, Ln.290, Guangfu S. Rd., Taipei.
T 886-2-2546-3258
F 886-2-2546-3258
E Guido@mula deco.com

備註:
a.圖面標註尺寸僅供參考, 施作均以現場放樣檢討之。
b.圖面標註尺寸、材料與文字敘述因版本不同之差異, 均以出圖章簽認日期之最近為準。
c.電腦圖檔係由合約訂定外, 均不得以何方式外流。
d.圖面所承均為本公司所擁有之智慧財產, 切勿以任何方式複製修改。

Revision		

Project /


天母葉公館


Job No /
00000
Scale /
1/60 mm

Date /	Approval /
8/10/2026	
Designer /	Drawn By /
Monica Lin	GUIDO

Sheet Title /
1F
立面及門編索引圖

Dwg No.
P-10
Page No.
13

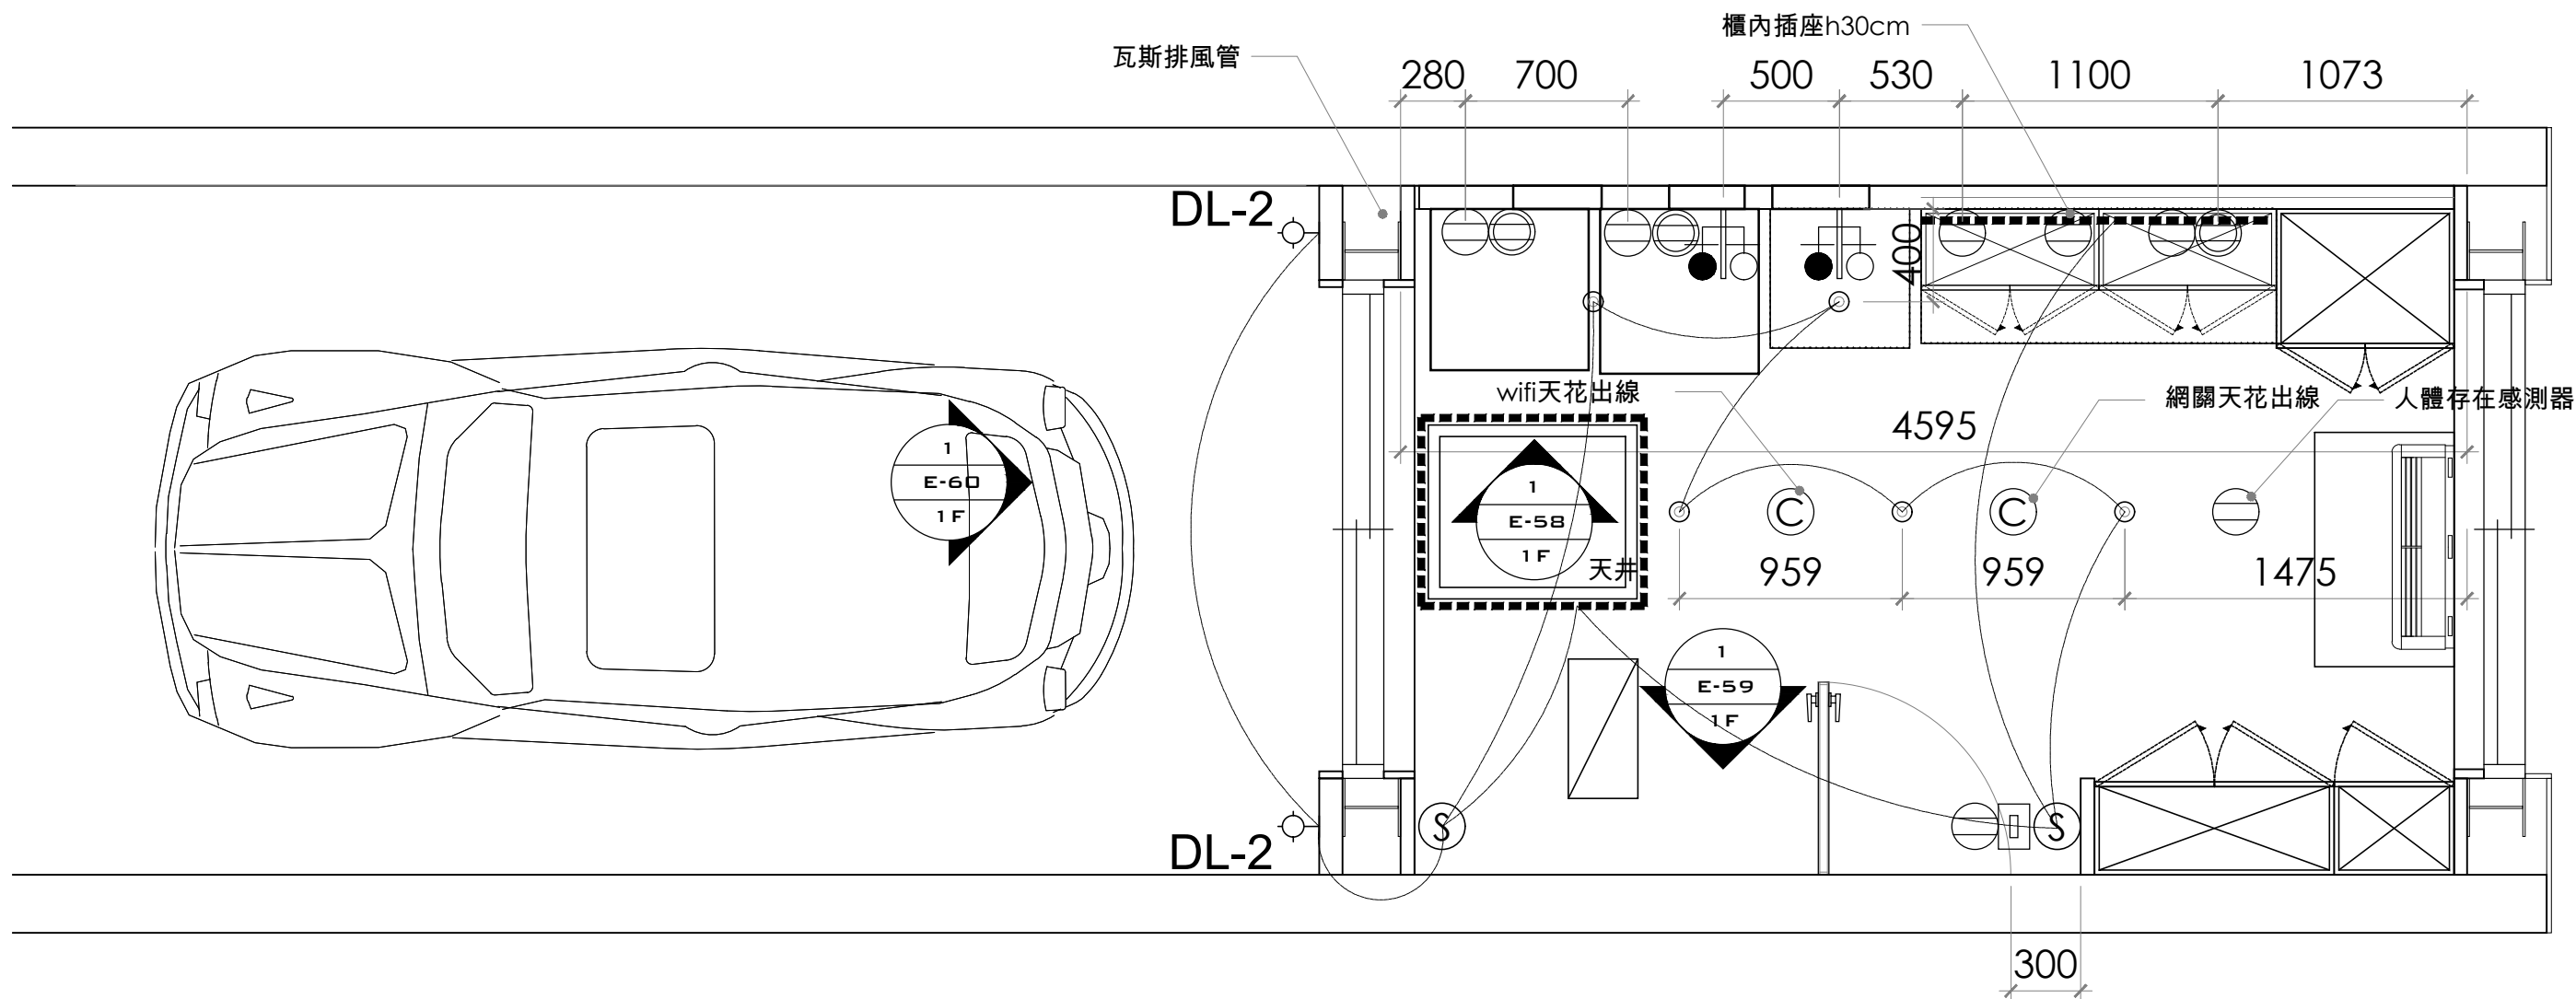

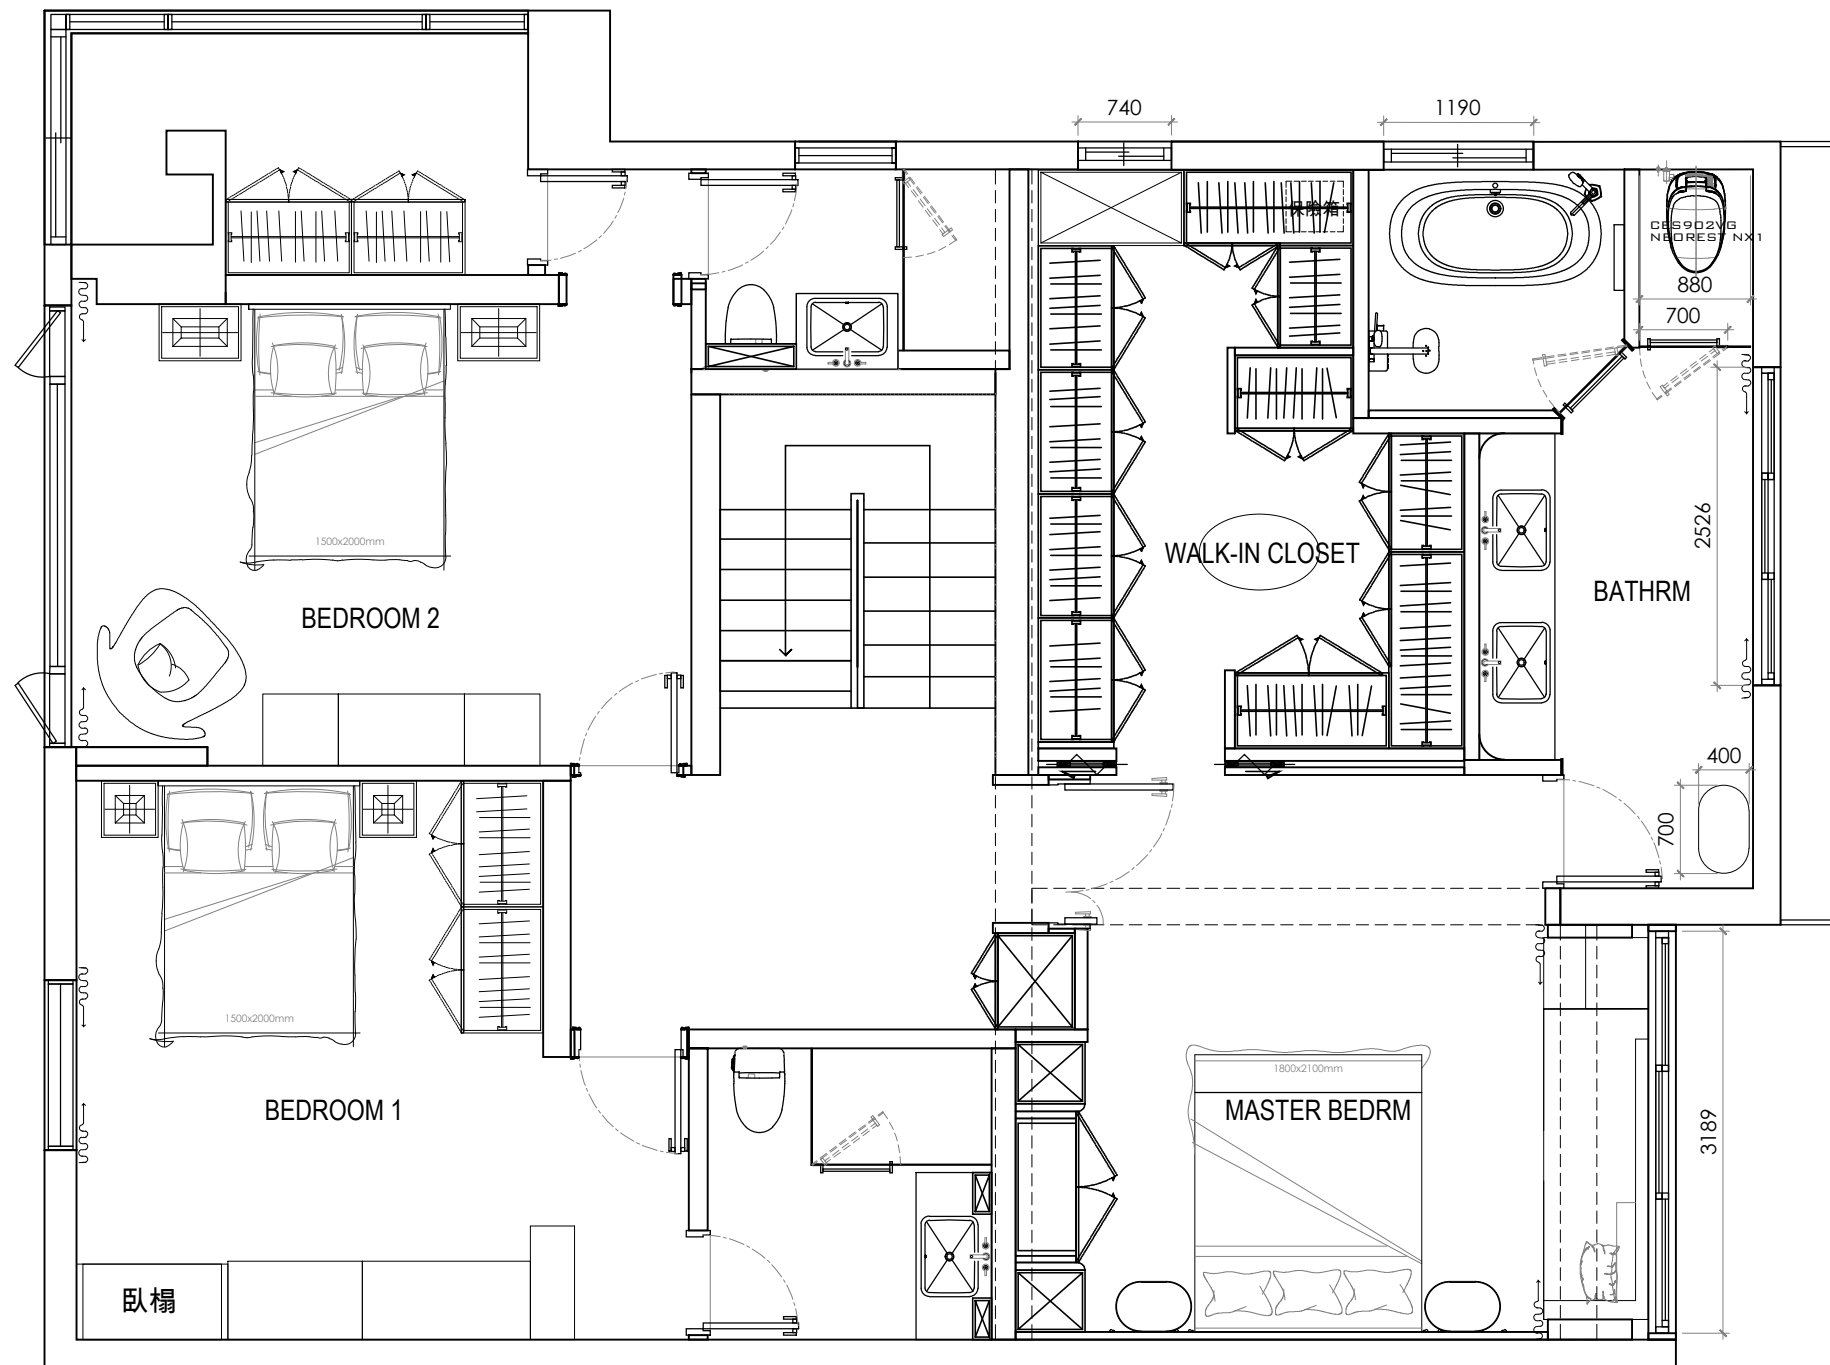

A 3F, N.26, Ln.290, Guangfu S. Rd., Taipei.
T 886-2-2546-3258
F 886-2-2546-3258
E Guido@mula deco.com

備註:
a.圖面標註尺寸僅供參考，施作均以現場放樣檢討之。
b.圖面標註尺寸、材料與文字敘述因版本不同之差異，均以出圖章後日期之最近為準。
c.電腦圖檔除由合約訂定外，均不得以何方式外流。
d.圖面所承均為本公司所擁有之智慧財產，切勿以任何方式複製修改。

Revision		

Project /

天母葉公館


Job No /
00000
Scale /
1/60 mm


Date /	Approval /
8/10/2026	
Designer /	Drawn By /
Monica Lin	GUIDO


Sheet Title /
2F
平面配置圖

Dwg No.
P-11
Page No.
15

牆 型 式	內 容	總 厚 度
	木作隔間牆	
	原有建築牆	154mm
	1/2B磚牆	120mm
	65mmC型骨架+單面(12mm石膏板+9mm矽酸鈣板)，單面(12mm石膏板+9mm矽酸鈣板)	100mm
	65mmC型骨架+雙面15mm石膏板	95mm

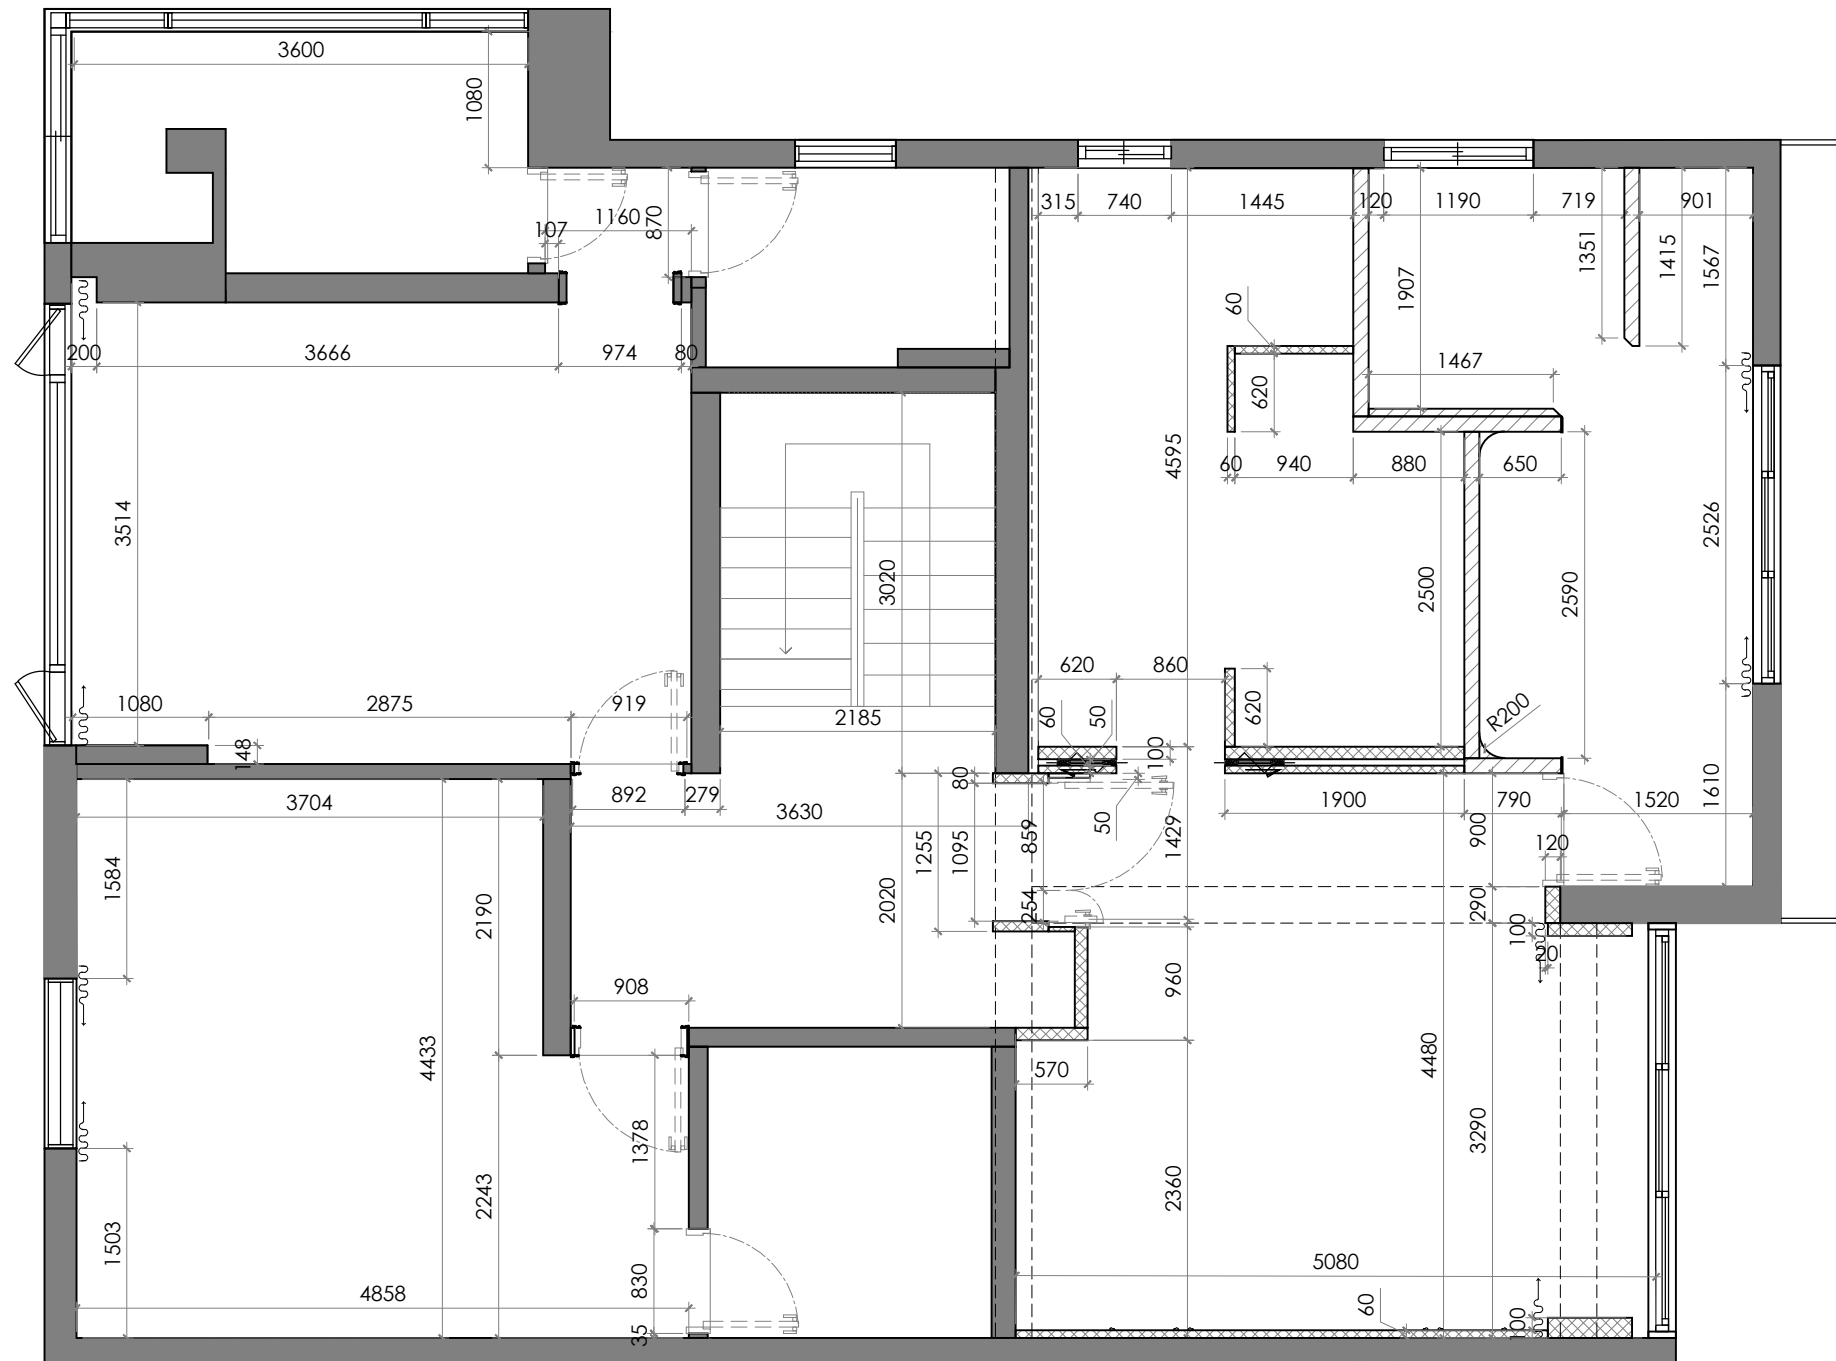

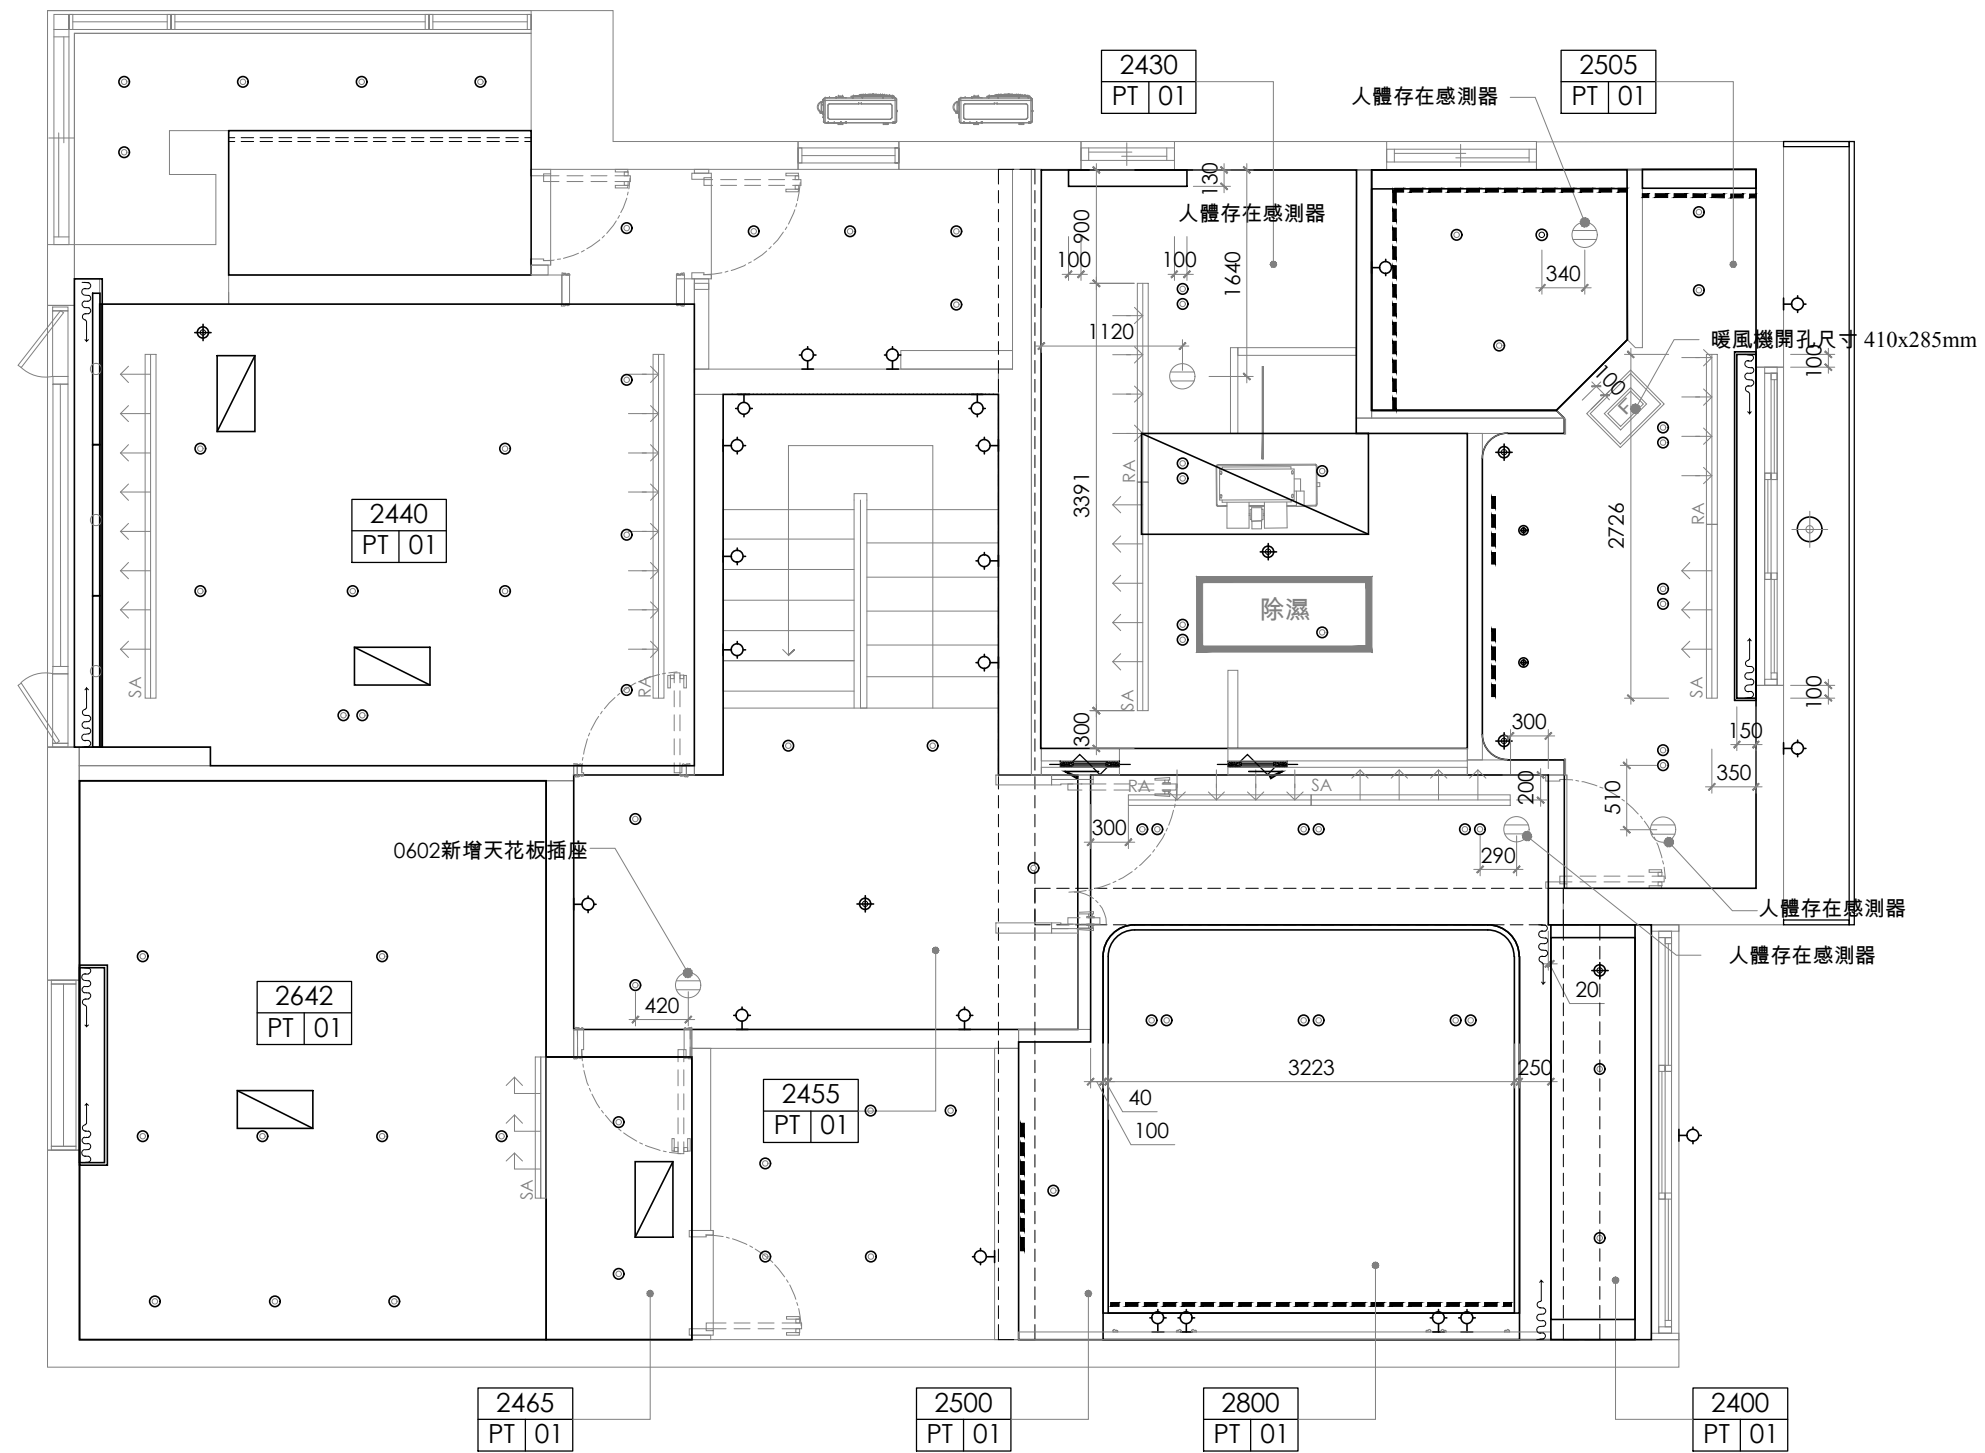

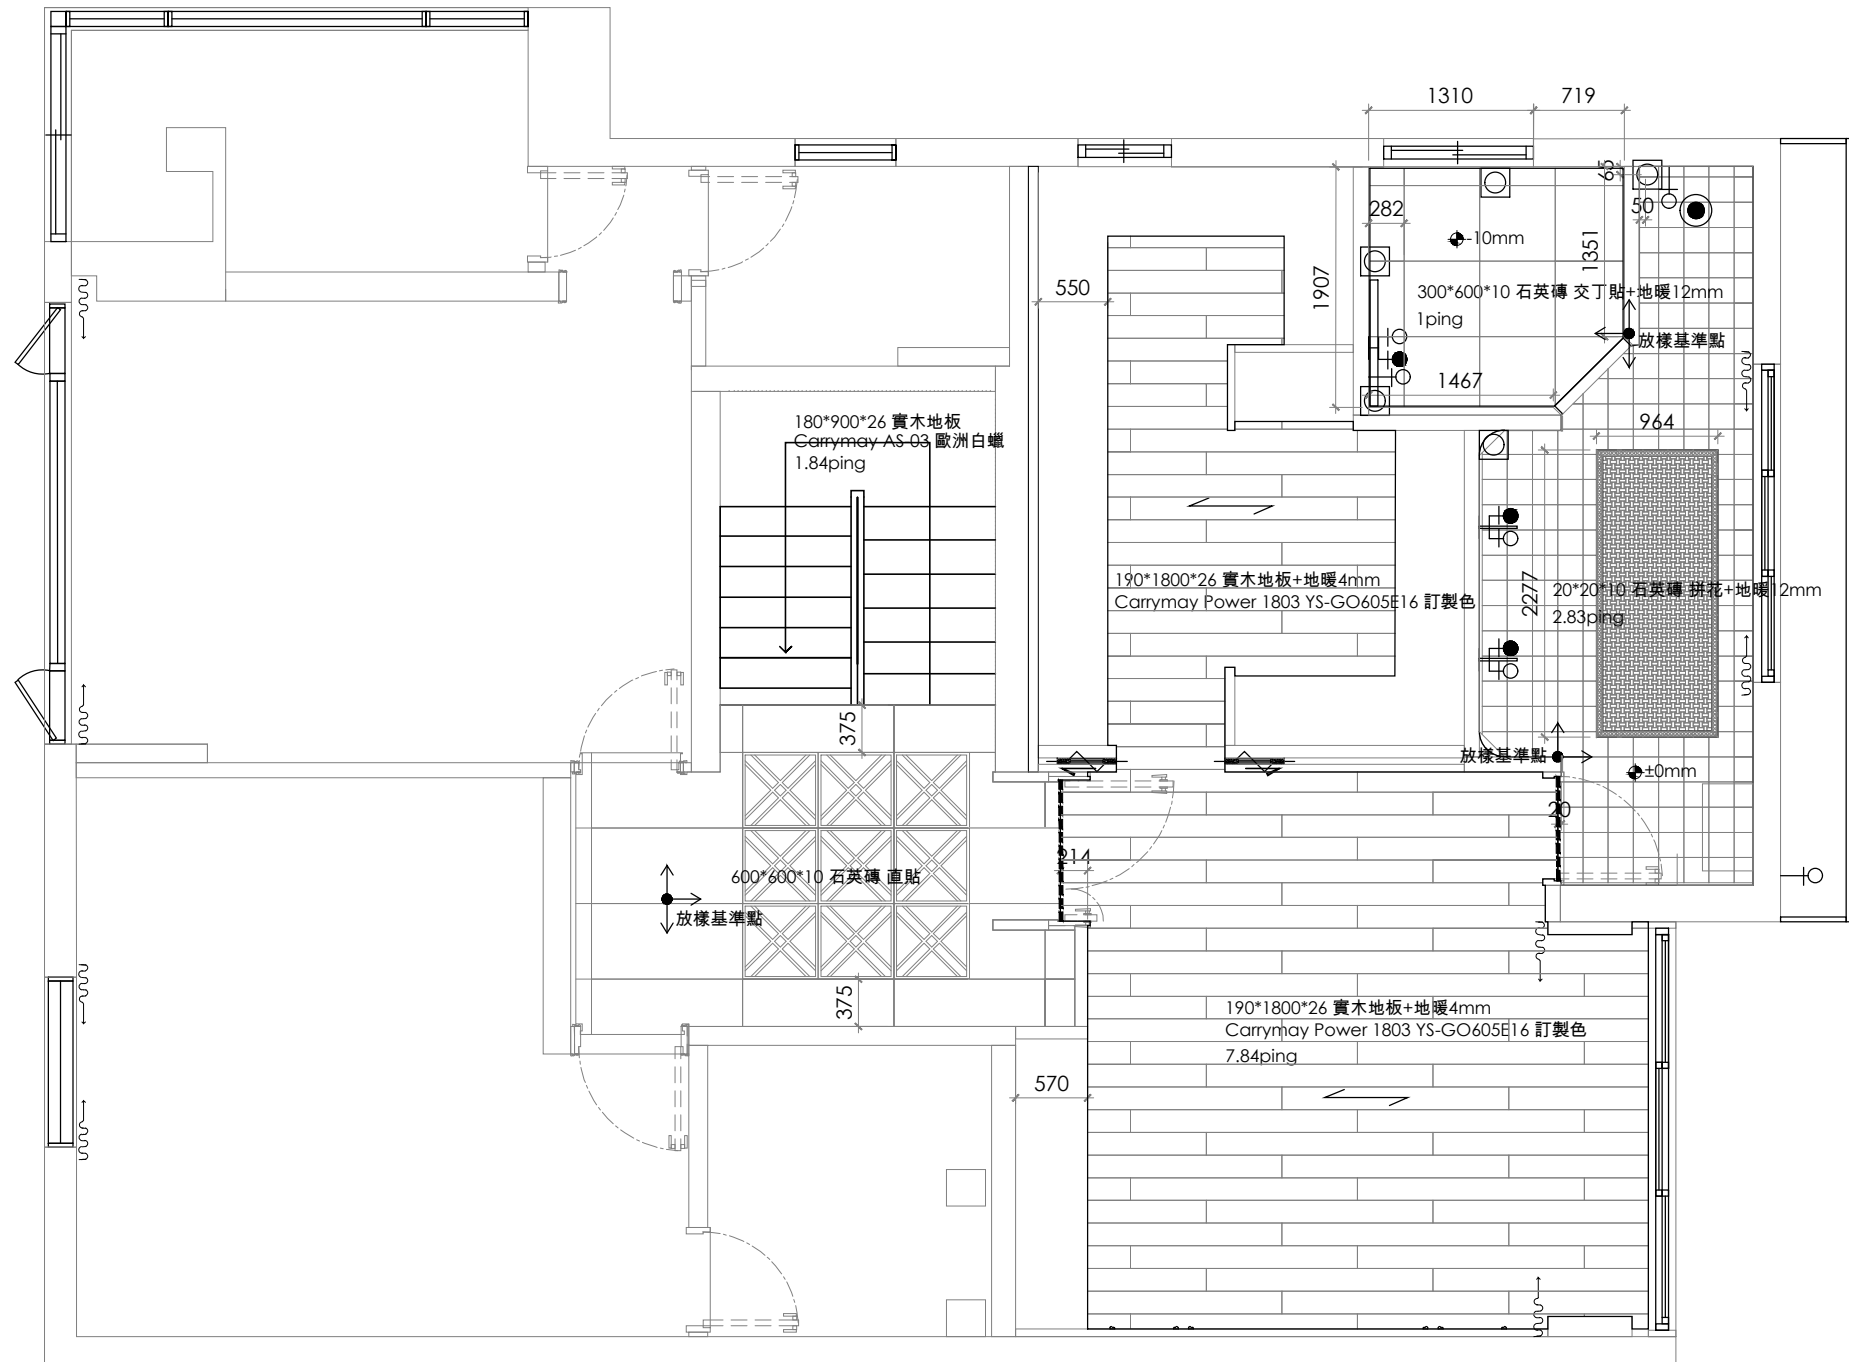

A 3F, N.26, Ln.290, Guangfu S. Rd., Taipei.
T 886-2-2546-3258
F 886-2-2546-3258
E Guido@mula deco.com

備註:
a.圖面標註尺寸僅供參考，施作均以現場放樣檢討之。
b.圖面標註尺寸、材料與文字敘述因版本不同之差異，均以出圖章後日期之最近為準。
c.電腦圖檔除由合約訂定外，均不得以何方式外流。
d.圖面所承均為本公司所擁有之智慧財產，切勿以任何方式複製修改。

Revision		

Project /

天母葉公館

Job No /

00000

Scale /

1/60 mm

Date /

8/10/2026

Designer /

Monica Lin

Approval /

Drawn By /

GUIDO

Sheet Title /

2F

地坪材料尺寸圖

Dwg No.


P-14

Page No.

18


編號	圖示	說明	尺寸	光源	備註
L1	●	COB可調角度嵌燈	88mm Dia x H25mm	KW-303 / 8W / 3000k / 嵌孔75mm	80
L2	●	2線式停電照明嵌燈	105mm Dia x H55mm	FH- 849-1B / 5W / 3000k / 嵌孔93mm	
L3	●	3線式停電照明嵌燈	105mm Dia x H55mm	FH- 849-1B / 5W / 3000k / 嵌孔93mm	
L4	⊕	LED 吸頂燈		3000k	2
L5	●	舞光LED 邱比特軌道燈	W88mm x L115mm x H50mm	AE-B07 / 7W / 3000k / 24°	
L6	●	嵌入式感應式嵌燈	85mm Dia x H50mm	3000k / 嵌孔75mm	
L7	-----	LED軟條燈		3000k	
L8	=====	軌道燈軌道	W34mm x H20mm		
*燈具相關設備,需詳燈具規範最後確認。 *燈具供電皆為110V。					

編號	圖示	說明	尺寸	光源	備註
L9	●	COB小型可調角度嵌燈	63mm Dia x H72mm	3000k / 嵌孔55mm	3
L10	□	無邊框可調角LED單燈盒燈	W99mm x L99mm x H85mm	FH- 829-11C /10W /30° / 3000K	6
L11	▣	無邊框可調角LED雙燈盒燈	W99mm x L199mm x H85mm	FH- 829-12C /10W /30° / 3000K	
L12	— · — · —	磁吸式軌道燈			
L13	=====	防塵防濕T5燈具			
L14	●	上照LED埋地燈	42mm Dia. x H90mm	LED /3W /12° /12V /3000K / 700mA	10
DL-1	◆	吊燈			16
DL-2	♀	壁燈			31
*燈具相關設備,需詳燈具規範最後確認。 *燈具供電皆為110V。					

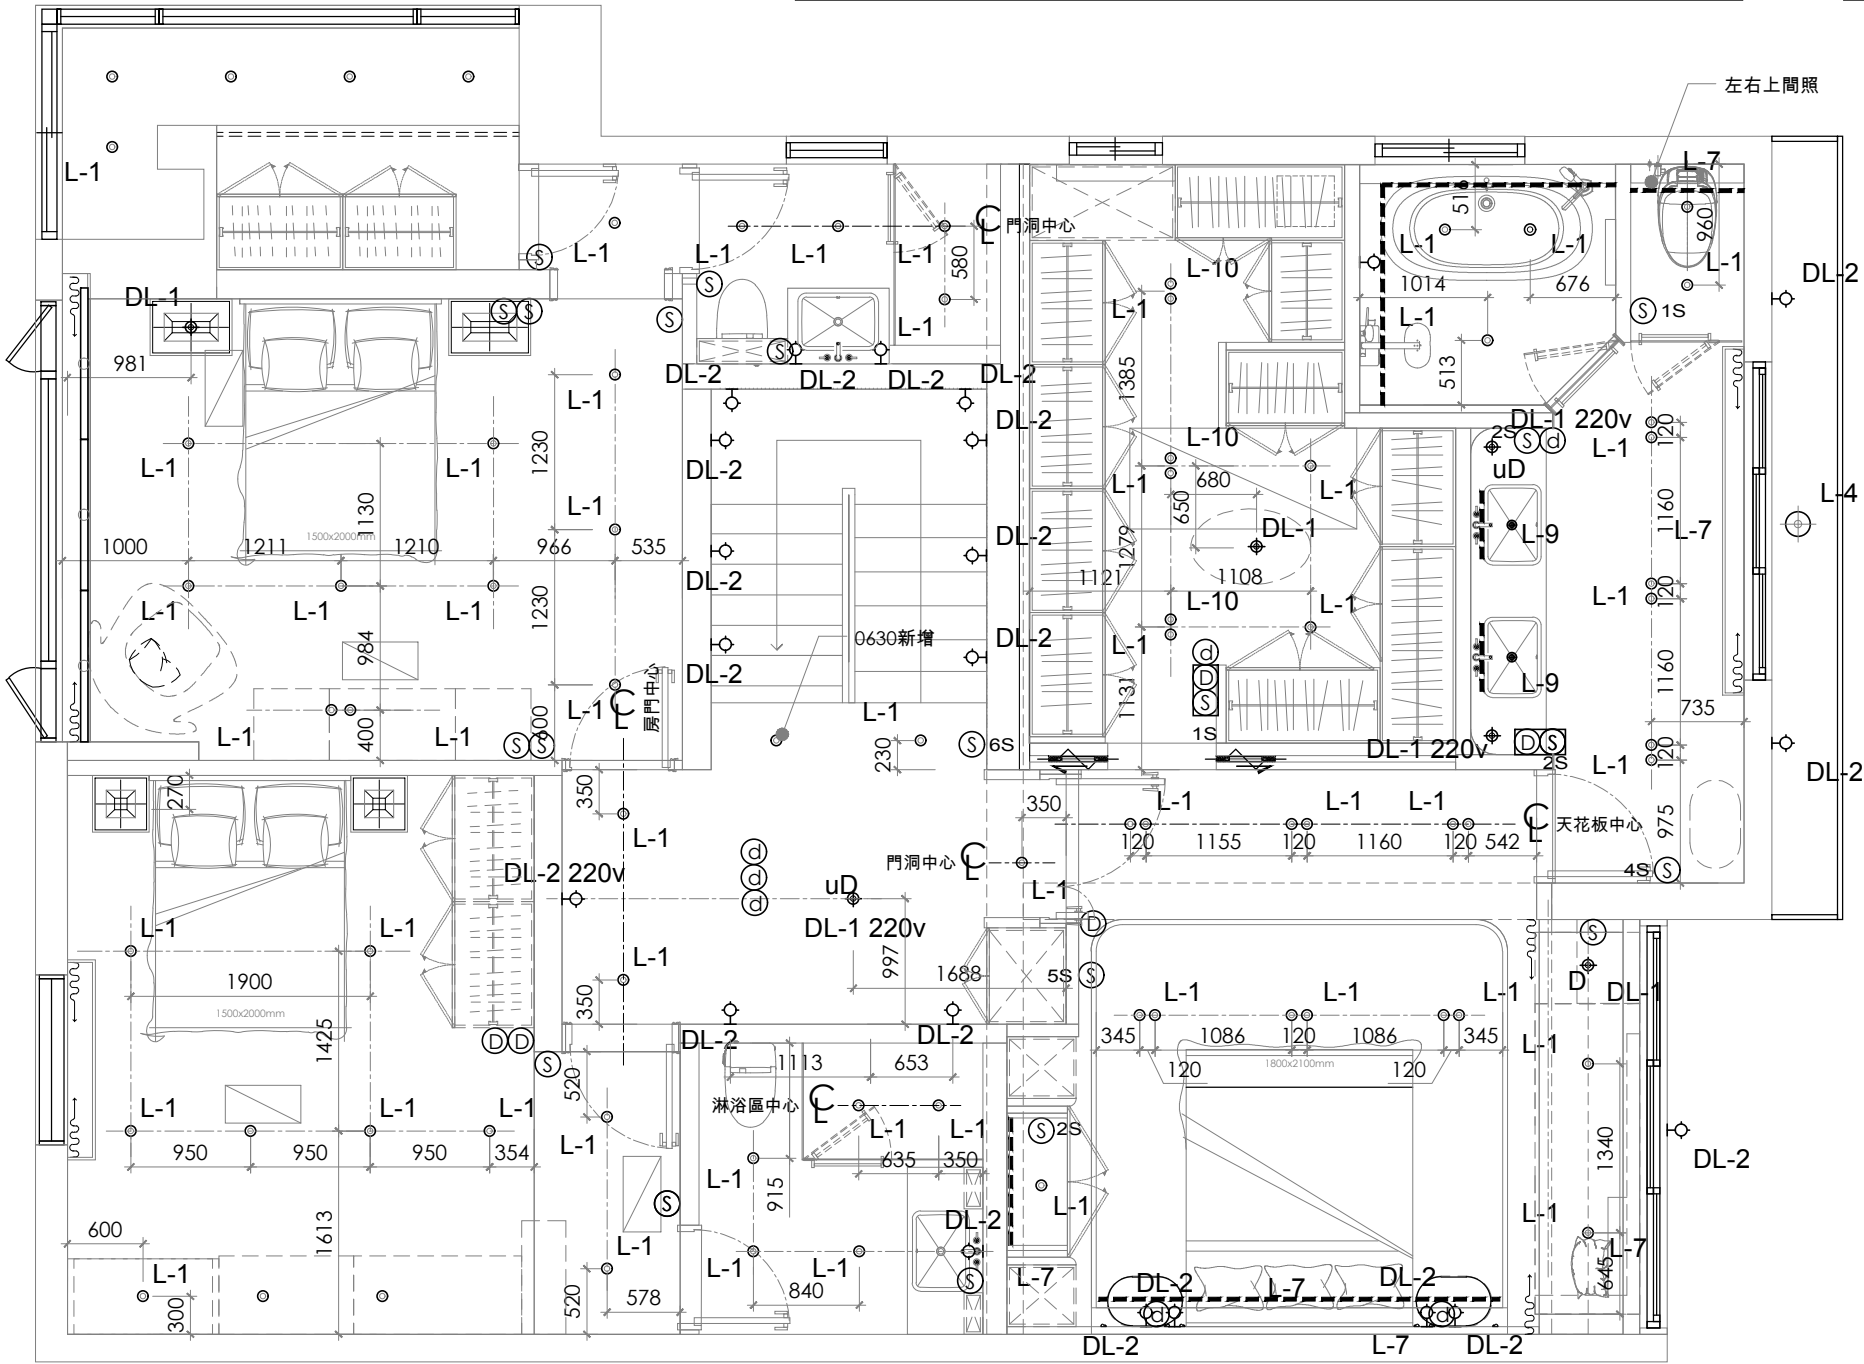


編號	圖示	說明	尺寸	光源	備註
L1	●	COB可調角度嵌燈	88mm Dia x H25mm	KW-303 / 8W / 3000k / 嵌孔75mm	80
L2	●	2線式停電照明嵌燈	105mm Dia x H55mm	FH- 849-1B / 5W / 3000k / 嵌孔93mm	
L3	●	3線式停電照明嵌燈	105mm Dia x H55mm	FH- 849-1B / 5W / 3000k / 嵌孔93mm	
L4	⊕	LED 吸頂燈		3000k	2
L5	●	舞光LED 邱比特軌道燈	W88mm x L115mm x H50mm	AE-B07 / 7W / 3000k / 24°	
L6	●	嵌入式感應式嵌燈	85mm Dia x H50mm	3000k / 嵌孔75mm	
L7	-----	LED軟條燈		3000k	
L8	=====	軌道燈軌道	W34mm x H20mm		
*燈具相關設備,需詳燈具規範最後確認。 *燈具供電皆為110V.					

編號	圖示	說明	尺寸	光源	備註
L9	●	COB小型可調角度嵌燈	63mm Dia x H72mm	3000k / 嵌孔55mm	3
L10	□	無邊框可調角LED單燈盒燈	W99mm x L99mm x H85mm	FH- 829-11C /10W /30° / 3000K	6
L11	▣	無邊框可調角LED雙燈盒燈	W99mm x L199mm x H85mm	FH- 829-12C /10W /30° / 3000K	
L12	— · — · —	磁吸式軌道燈			
L13	=====	防塵防濕T5燈具			
L14	●	上照LED埋地燈	42mm Dia. x H90mm	LED /3W /12° /12V /3000K / 700mA	10
DL-1	◆	吊燈			16
DL-2	♀	壁燈			31
*燈具相關設備,需詳燈具規範最後確認。 *燈具供電皆為110V.					

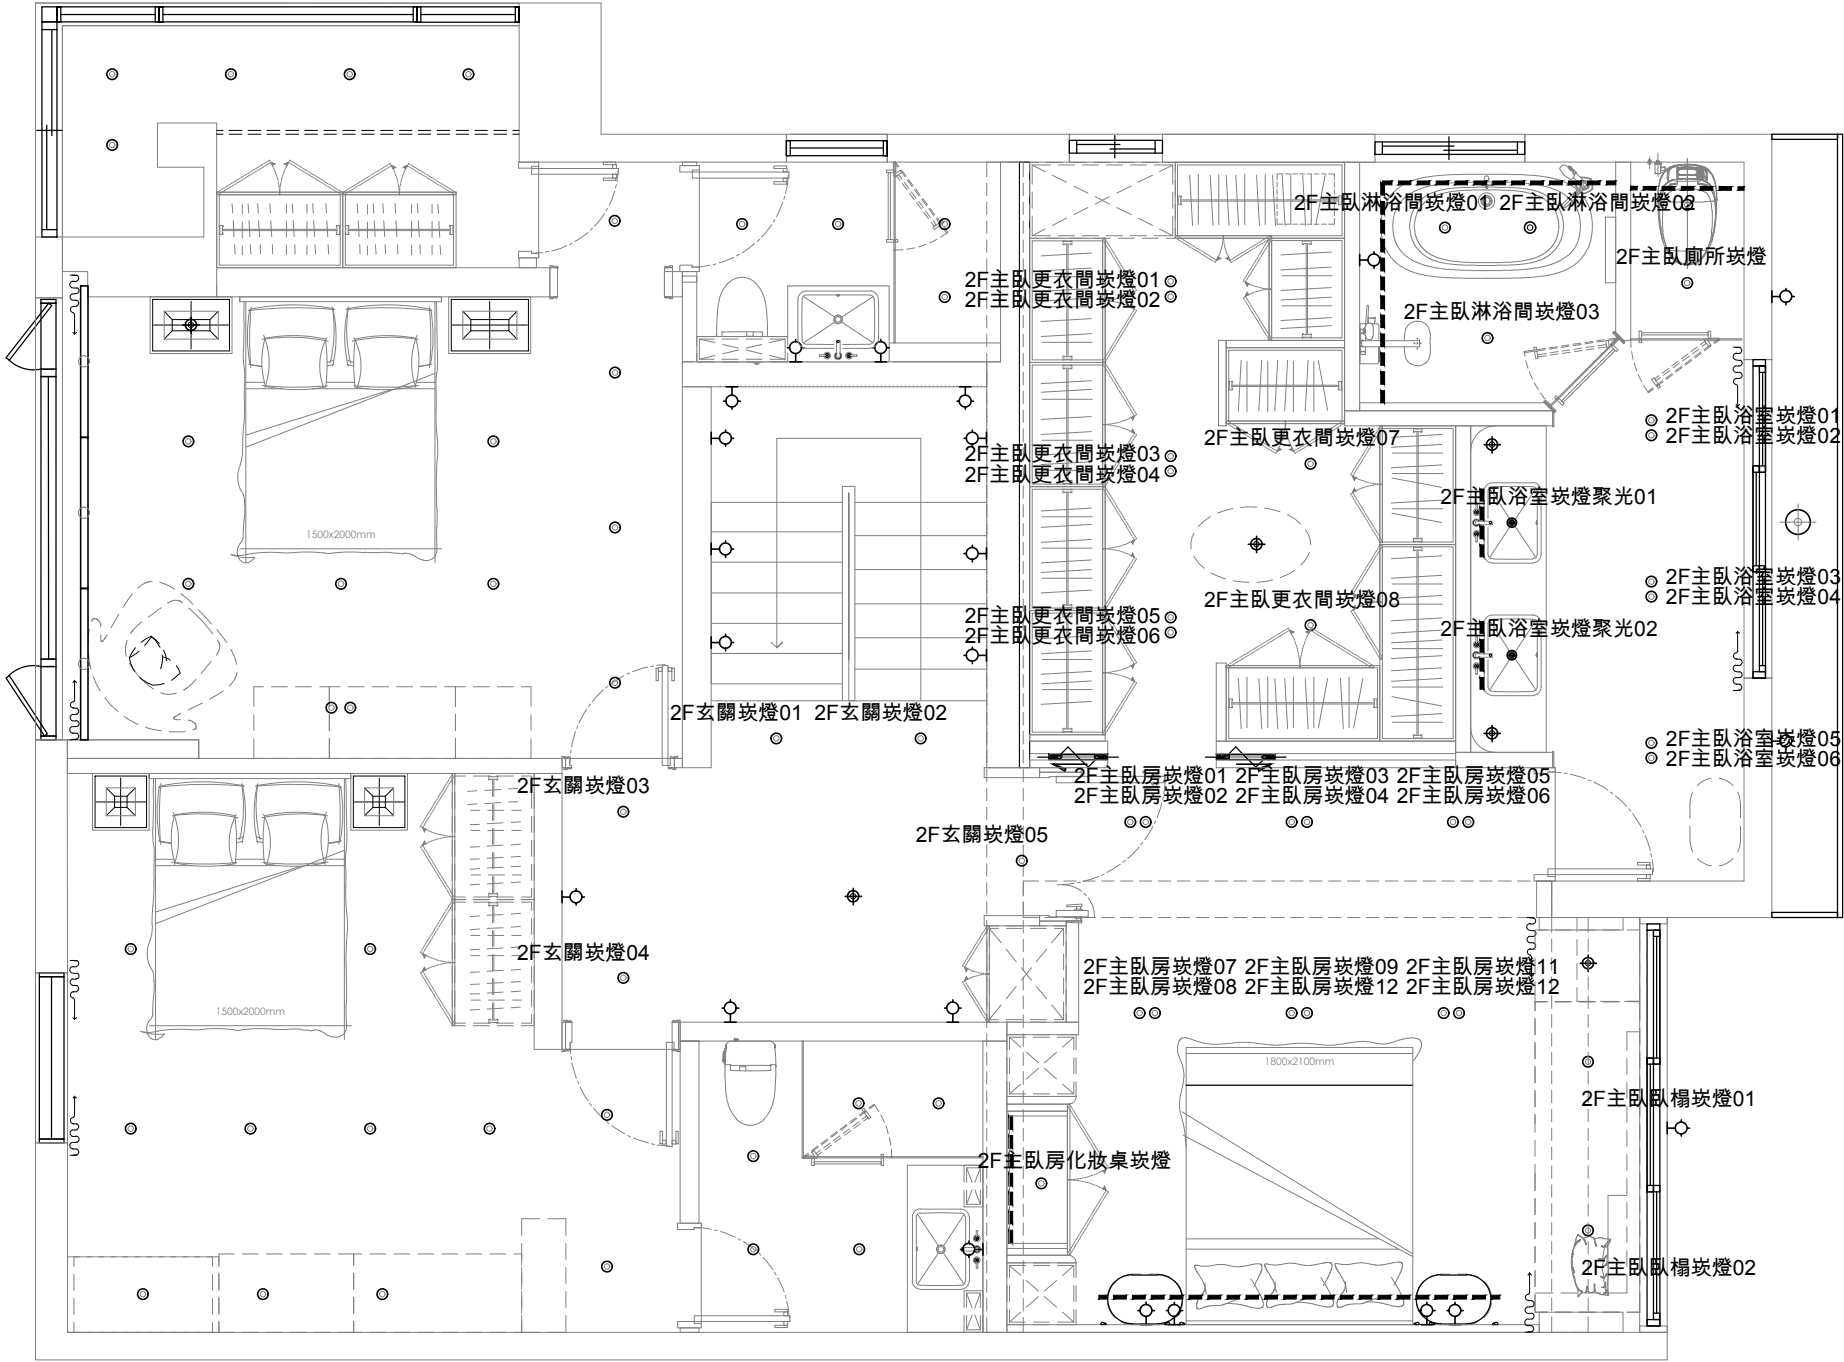


編號	圖示	說明	尺寸	光源	備註
L1	●	COB可調角度嵌燈	88mm Dia x H25mm	KW-303 / 8W / 3000k / 嵌孔75mm	80
L2	●	2線式停電照明嵌燈	105mm Dia x H55mm	FH- 849-1B / 5W / 3000k / 嵌孔93mm	
L3	●	3線式停電照明嵌燈	105mm Dia x H55mm	FH- 849-1B / 5W / 3000k / 嵌孔93mm	
L4	⊕	LED 吸頂燈		3000k	2
L5	●	舞光LED 邱比特軌道燈	W88mm x L115mm x H50mm	AE-B07 / 7W / 3000k / 24°	
L6	●	嵌入式感應式嵌燈	85mm Dia x H50mm	3000k / 嵌孔75mm	
L7	-----	LED軟條燈		3000k	
L8	=====	軌道燈軌道	W34mm x H20mm		
*燈具相關設備,需詳燈具規範最後確認。 *燈具供電皆為110V.					

編號	圖示	說明	尺寸	光源	備註
L9	●	COB小型可調角度嵌燈	63mm Dia x H72mm	3000k / 嵌孔55mm	3
L10	□	無邊框可調角LED單燈盒燈	W99mm x L99mm x H85mm	FH- 829-11C /10W /30° / 3000K	6
L11	▣	無邊框可調角LED雙燈盒燈	W99mm x L199mm x H85mm	FH- 829-12C /10W /30° / 3000K	
L12	— · — · —	磁吸式軌道燈			
L13	=====	防塵防濕T5燈具			
L14	◦	上照LED埋地燈	42mm Dia. x H90mm	LED /3W /12° /12V /3000K / 700mA	10
DL-1	◆	吊燈			16
DL-2	♀	壁燈			31
*燈具相關設備,需詳燈具規範最後確認。 *燈具供電皆為110V.					

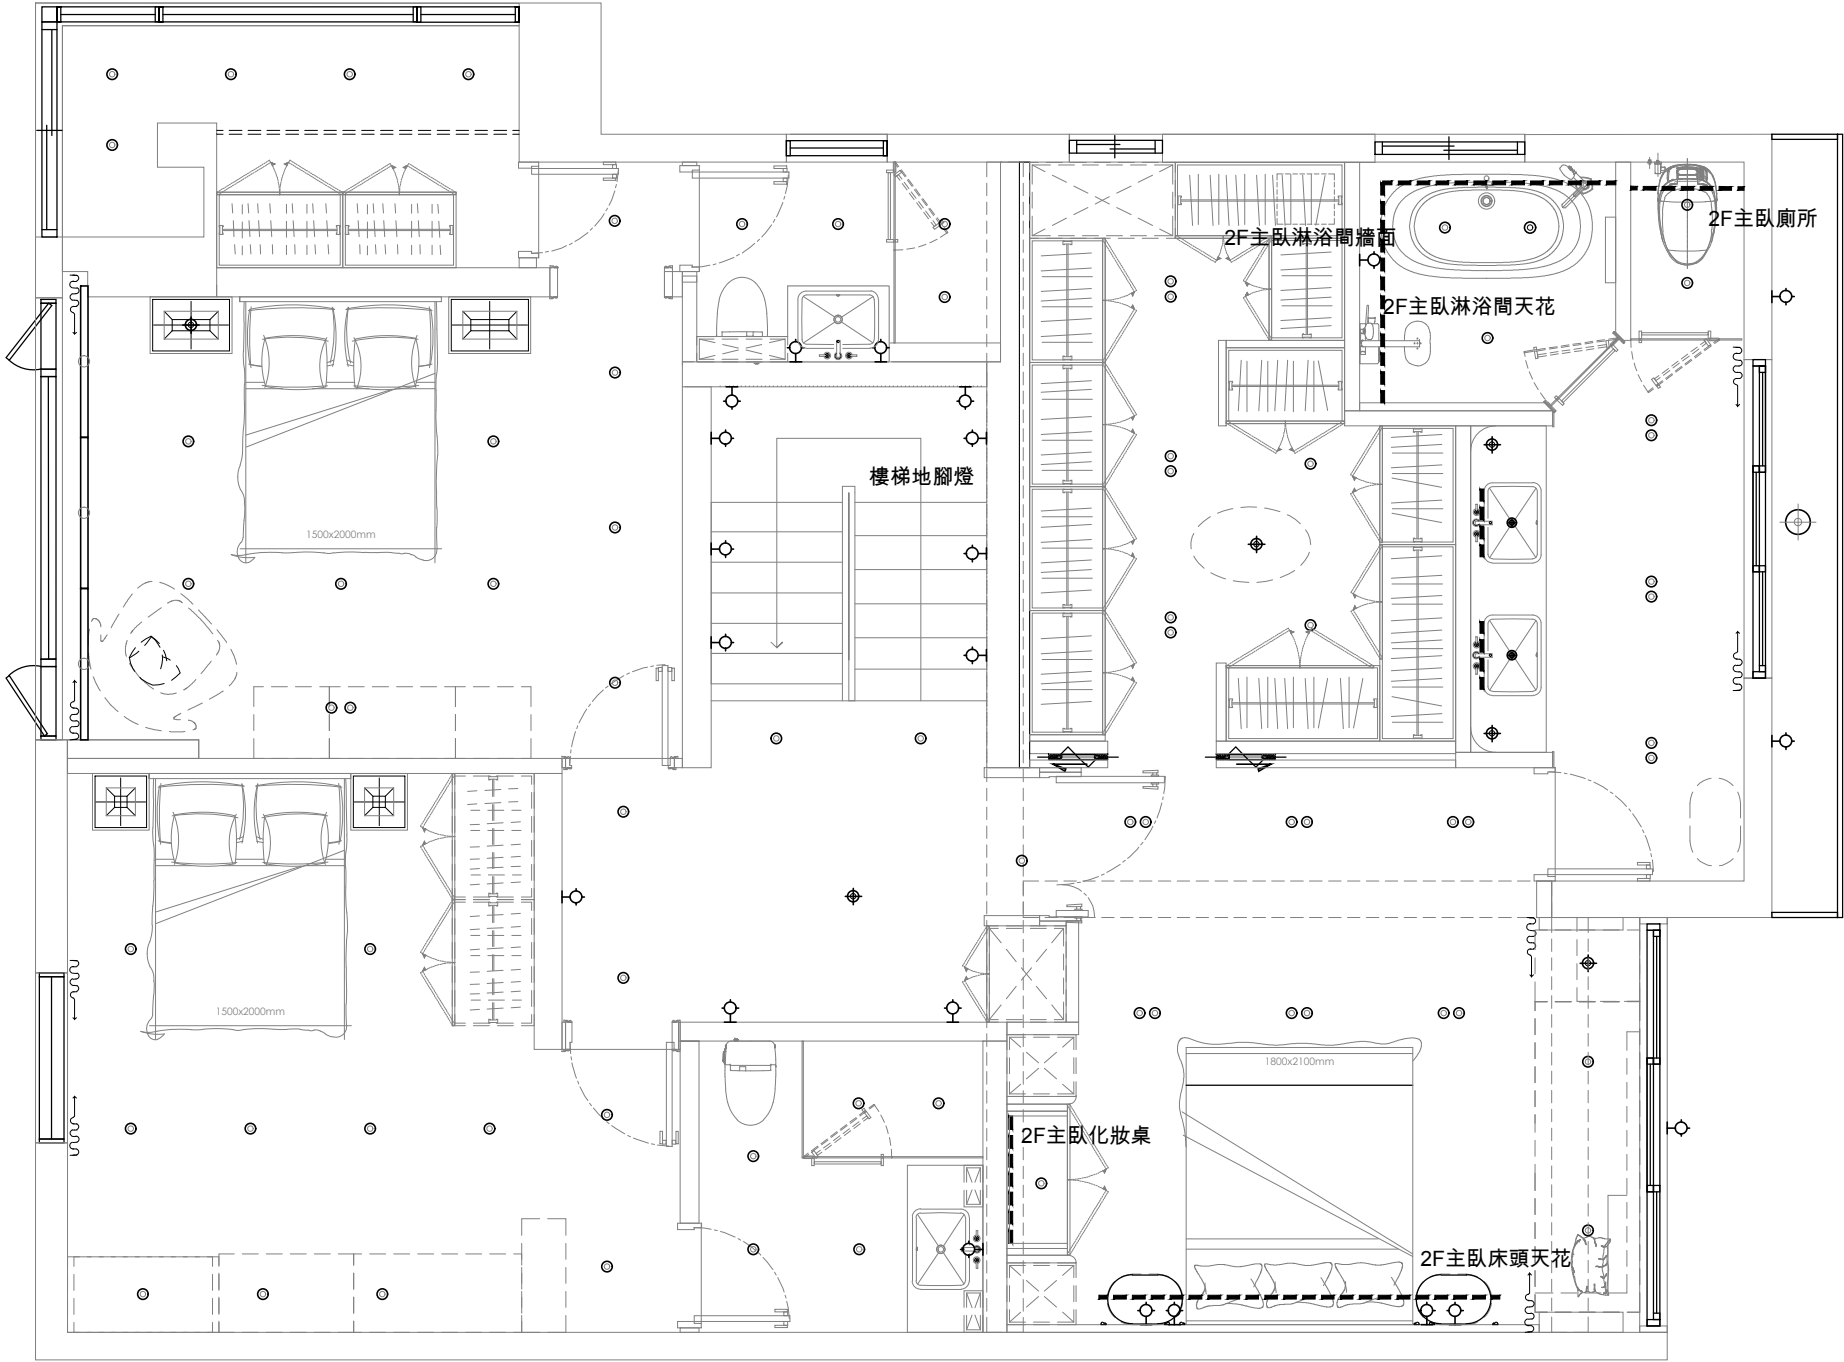


編號	圖示	說明	尺寸	光源	備註
L1	●	COB可調角度嵌燈	88mm Dia x H25mm	KW-303 / 8W / 3000k / 嵌孔75mm	80
L2	●	2線式停電照明嵌燈	105mm Dia x H55mm	FH- 849-1B / 5W / 3000k / 嵌孔93mm	
L3	●	3線式停電照明嵌燈	105mm Dia x H55mm	FH- 849-1B / 5W / 3000k / 嵌孔93mm	
L4	⊕	LED 吸頂燈		3000k	2
L5	●	舞光LED 邱比特軌道燈	W88mm x L115mm x H50mm	AE-B07 / 7W / 3000k / 24°	
L6	●	嵌入式感應式嵌燈	85mm Dia x H50mm	3000k / 嵌孔75mm	
L7	-----	LED軟條燈		3000k	
L8	=====	軌道燈軌道	W34mm x H20mm		
*燈具相關設備,需詳燈具規範最後確認。 *燈具供電皆為110V。					


編號	圖示	說明	尺寸	光源	備註
L9	●	COB小型可調角度嵌燈	63mm Dia x H72mm	3000k / 嵌孔55mm	3
L10	▣	無邊框可調角LED單燈盒燈	W99mm x L99mm x H85mm	FH- 829-11C /10W /30° / 3000K	6
L11	▣	無邊框可調角LED雙燈盒燈	W99mm x L199mm x H85mm	FH- 829-12C /10W /30° / 3000K	
L12	— · — · —	磁吸式軌道燈			
L13	=====	防塵防濕T5燈具			
L14	●	上照LED埋地燈	42mm Dia. x H90mm	LED /3W /12° /12V /3000K / 700mA	10
DL-1	◆	吊燈			16
DL-2	◇	壁燈			31
*燈具相關設備,需詳燈具規範最後確認。 *燈具供電皆為110V。					

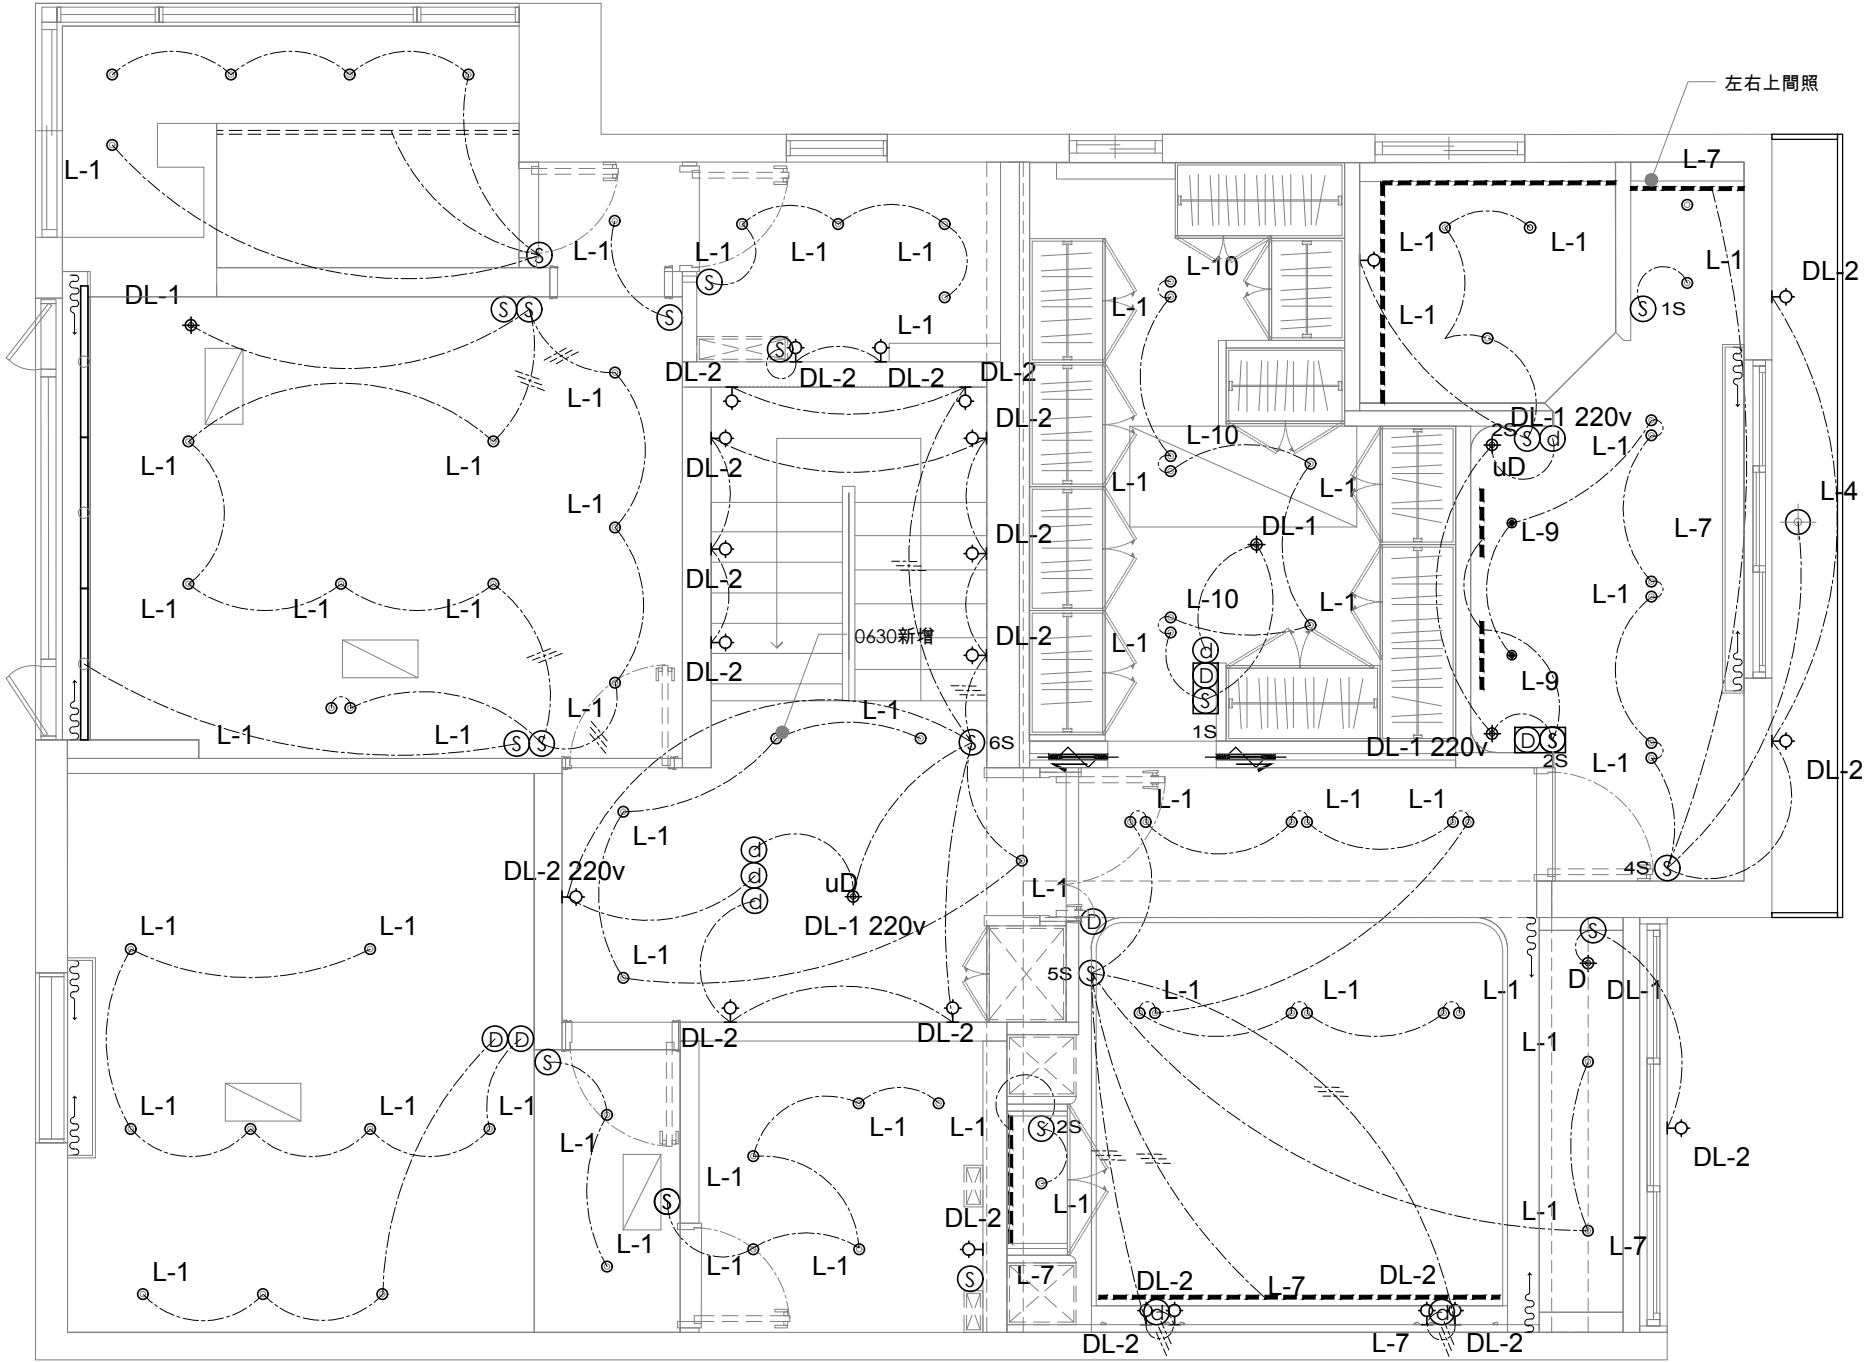


空調設備圖例說明			
圖 例	說 明	圖 例	說 明
	側吹出風口		出風口
	側吹回風口		吊隱式除濕主機
	下吹出風口		五合一暖風機
	下吹回風口		全熱交換器
	空調維修孔		

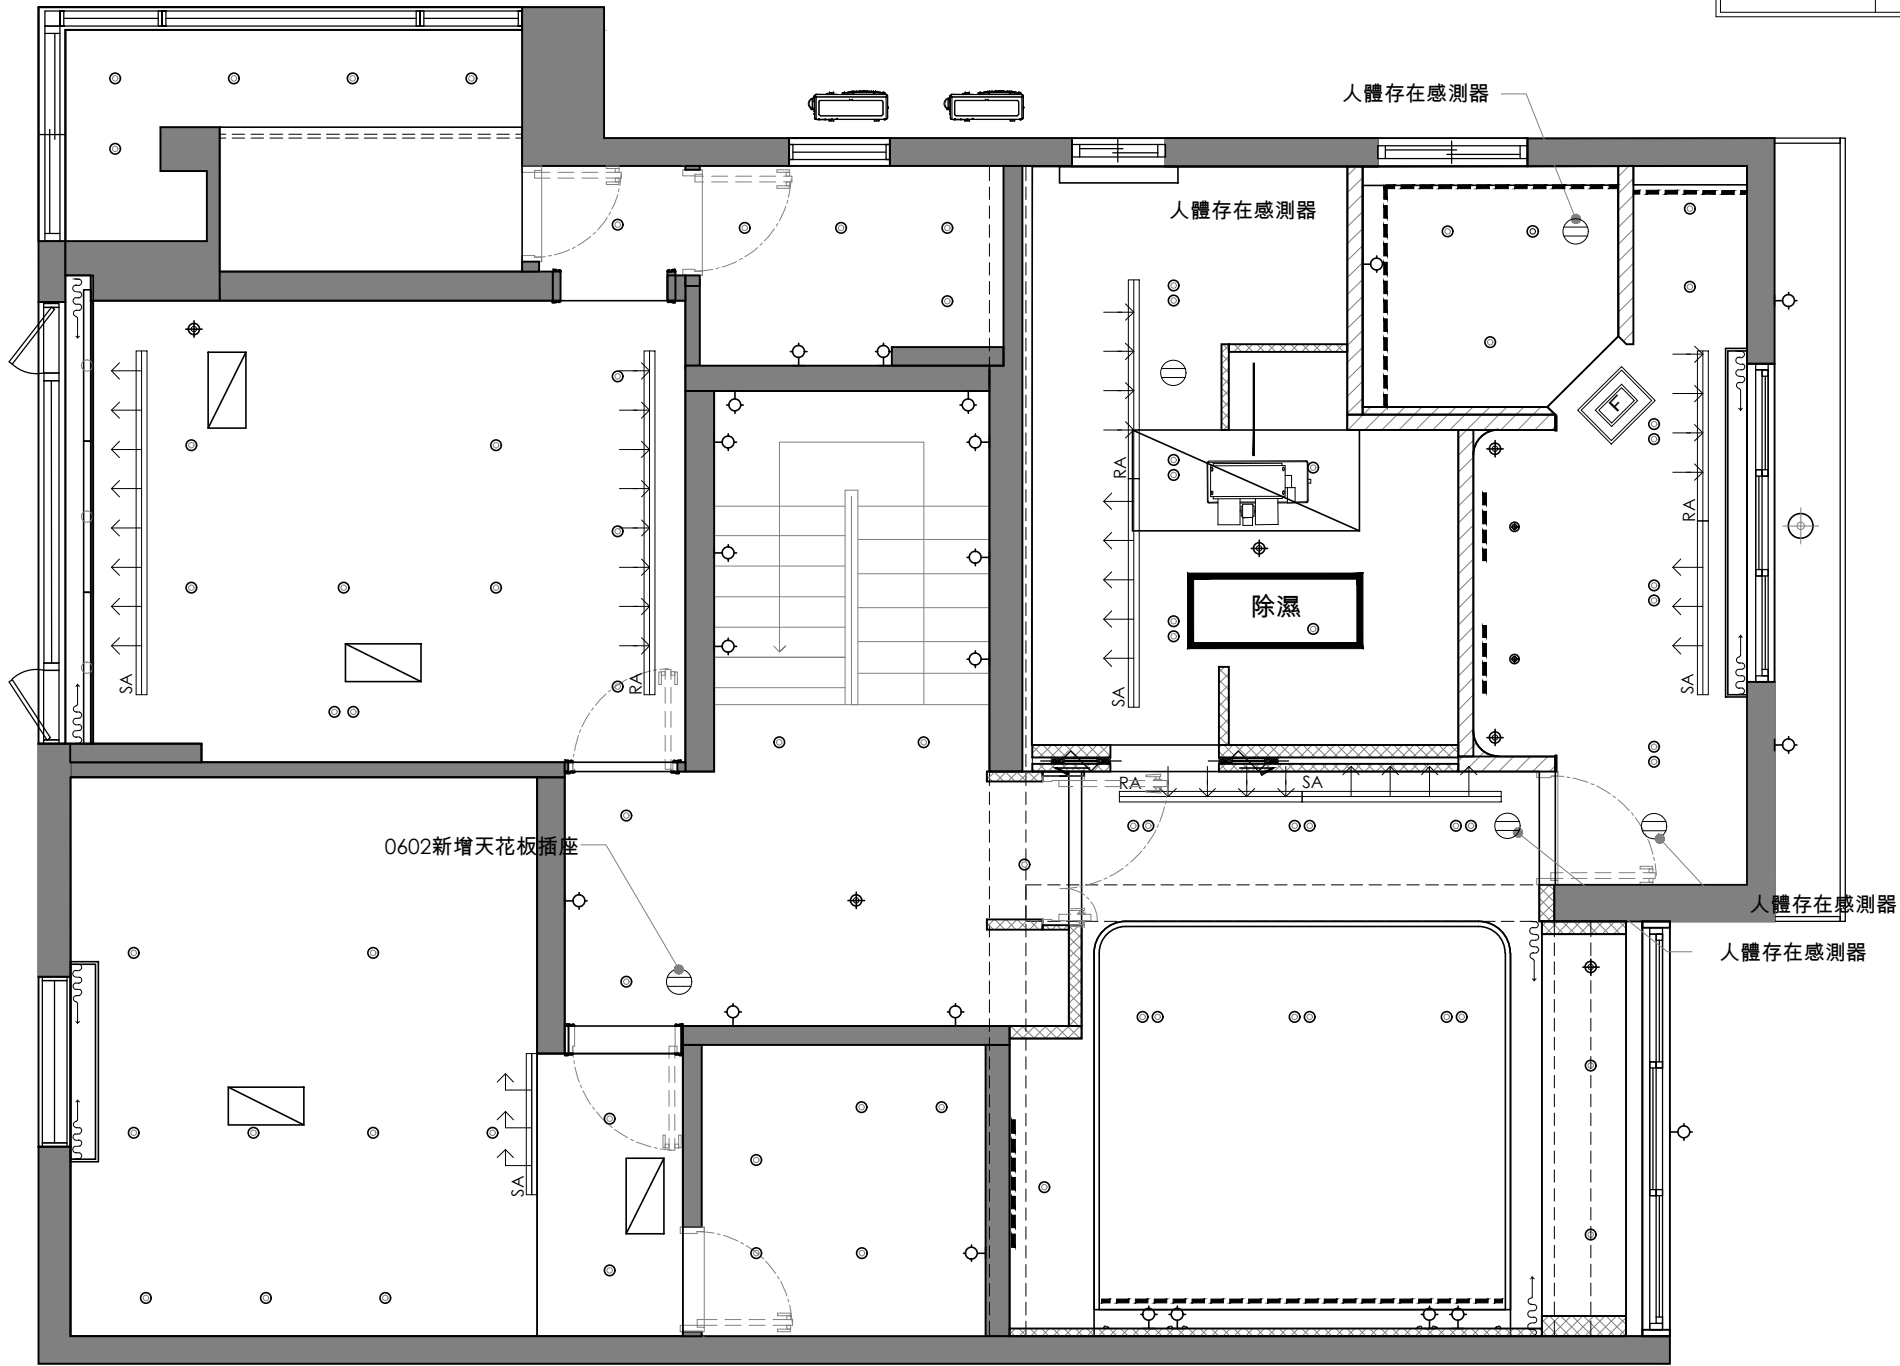

給排水設備圖例說明表			
圖例	說 明	規格	高度
—○	壁面冷給水		
—●	壁面熱給水		
H○●	壁面冷熱給水		
H○●	壁面冷熱給水及排水		
□	地板排水口		
●	糞管		
⊗	RO進水管		
備註	1.淋浴間,蓮蓬頭出水口+2100AFF。 2.淋浴間,蓮蓬頭出水口+2100AFF		

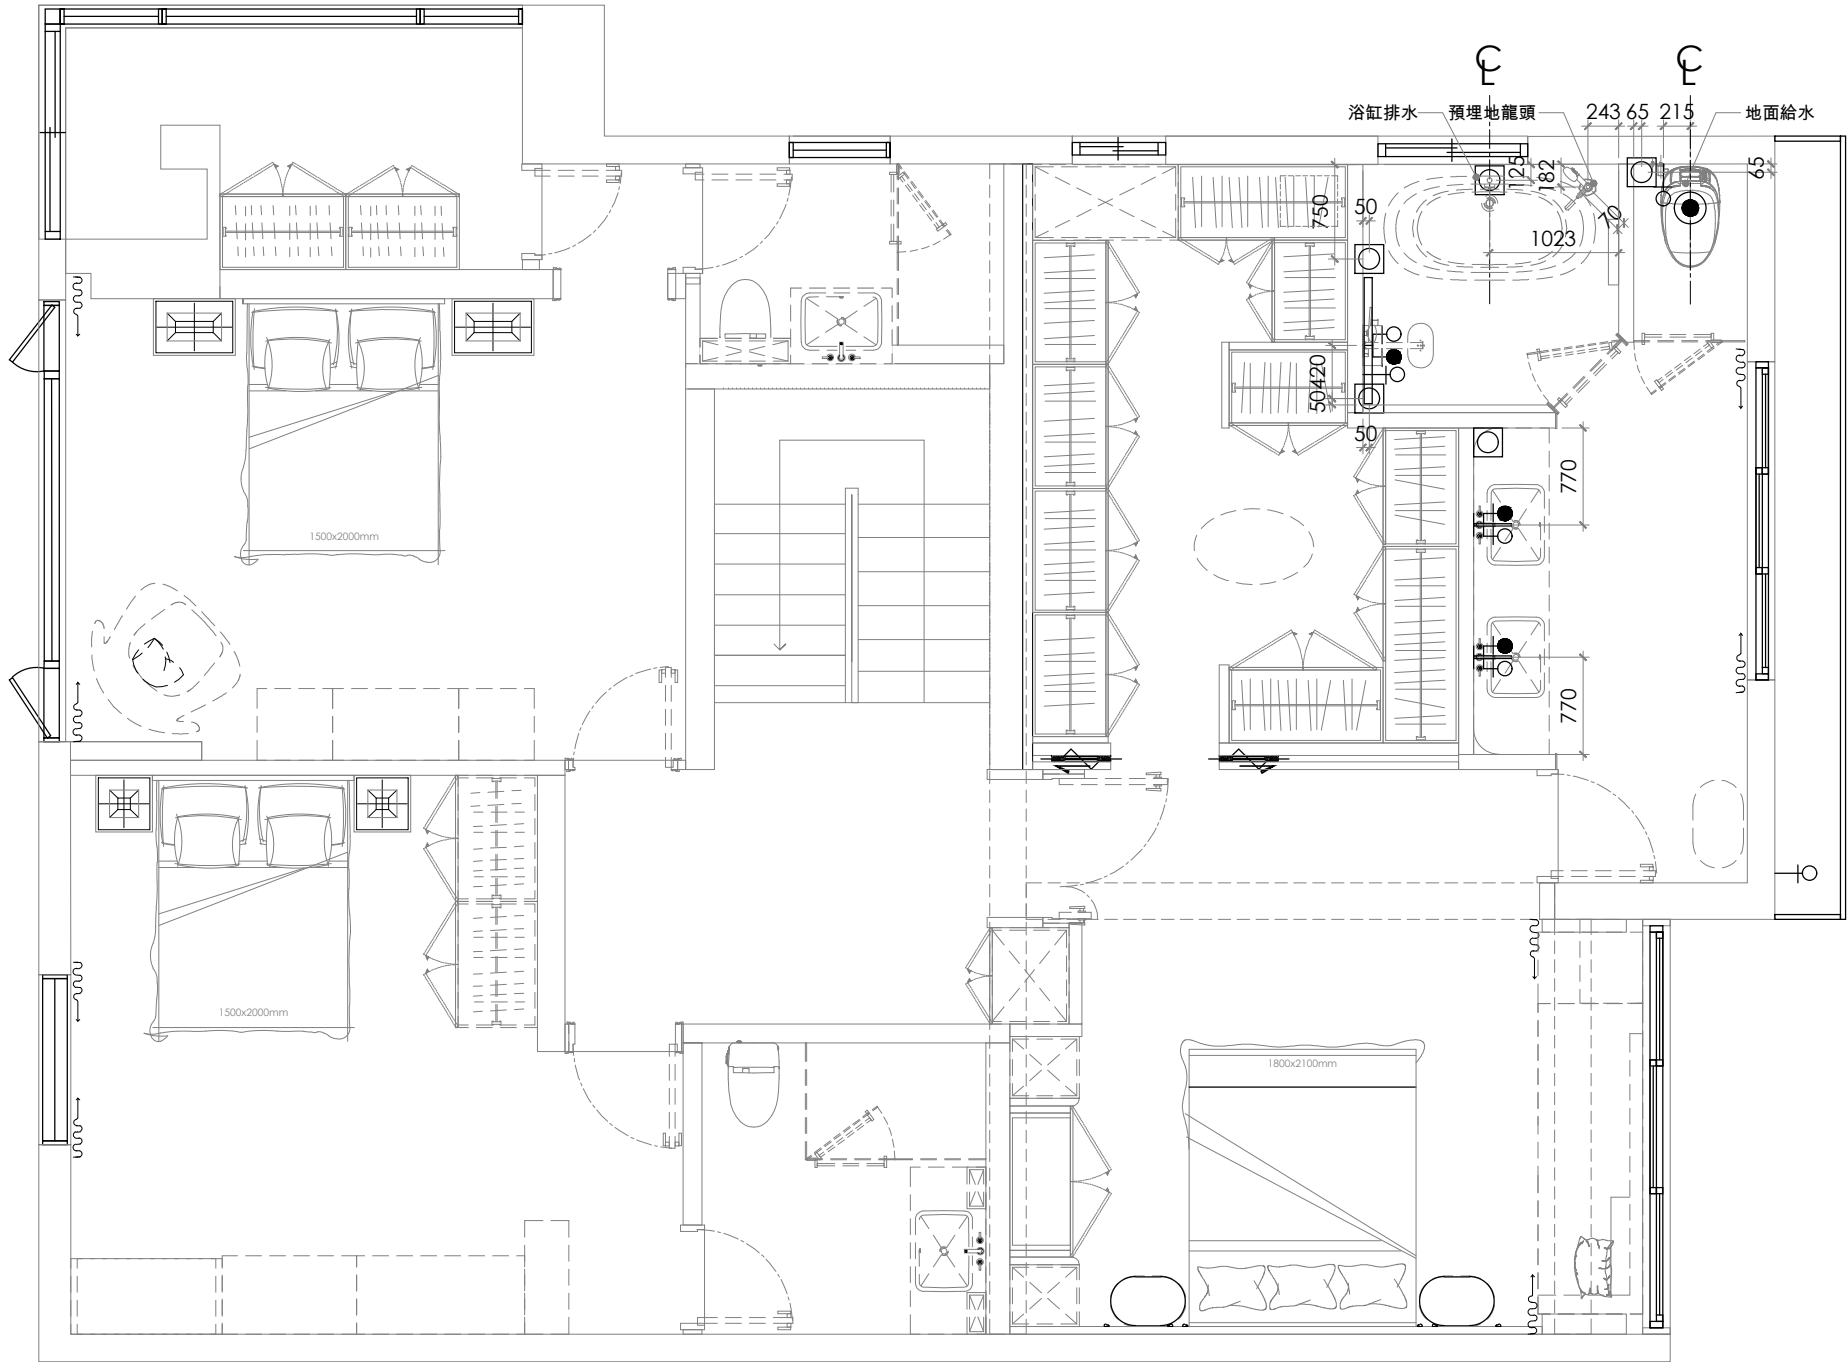

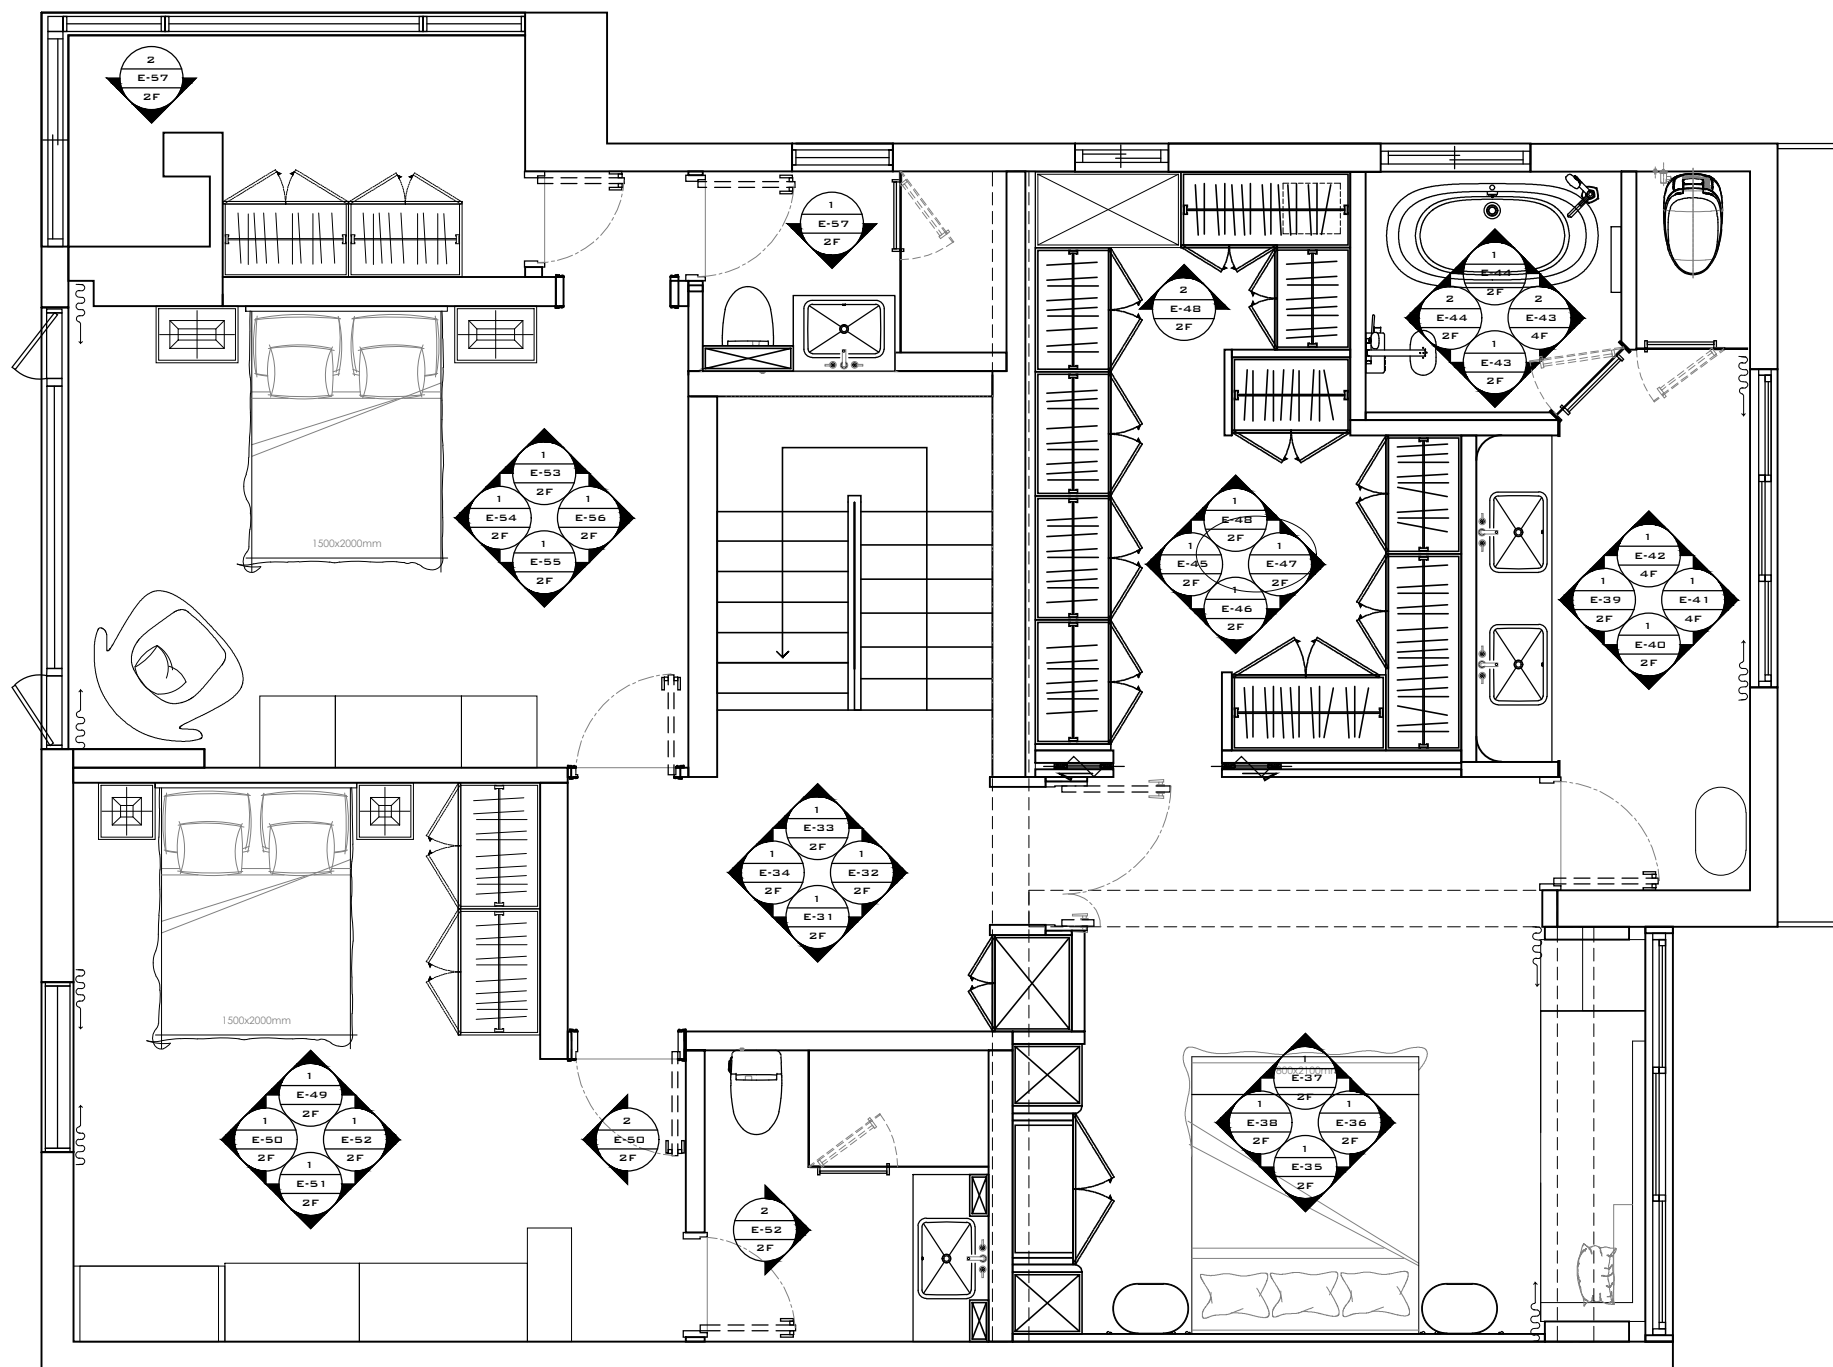

A 3F, N.26, Ln.290, Guangfu S. Rd., Taipei.
T 886-2-2546-3258
F 886-2-2546-3258
E Guido@mula deco.com

備註:
a.圖面標註尺寸僅供參考，施作均以現場放樣檢核之。
b.圖面標註尺寸、材料與文字敘述因版本不同之差異，均以出圖章簽認日期之最近為準。
c.電腦圖檔標除由合約訂定外，均不得以何方式外流。
d.圖面所承均為本公司所擁有之智慧財產，切勿以任何方式複製修改。

Revision		

Project /

天母葉公館

Job No /
00000
Scale /
1/60 mm

Date /	Approval /
8/10/2026	
Designer /	Drawn By /
Monica Lin	GUIDO

Sheet Title /
2F
立面及門編索引圖

Dwg No.
P-20
Page No.
26

